

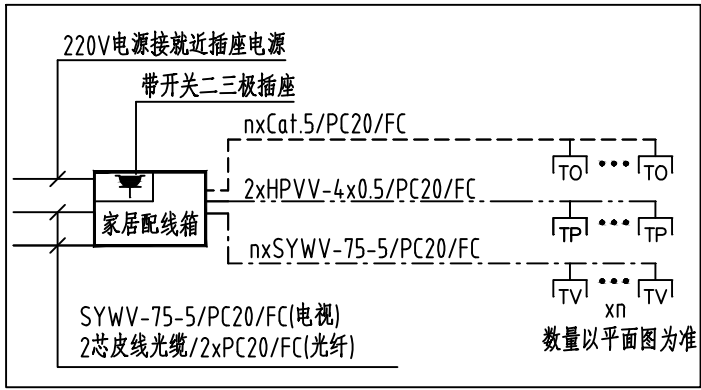


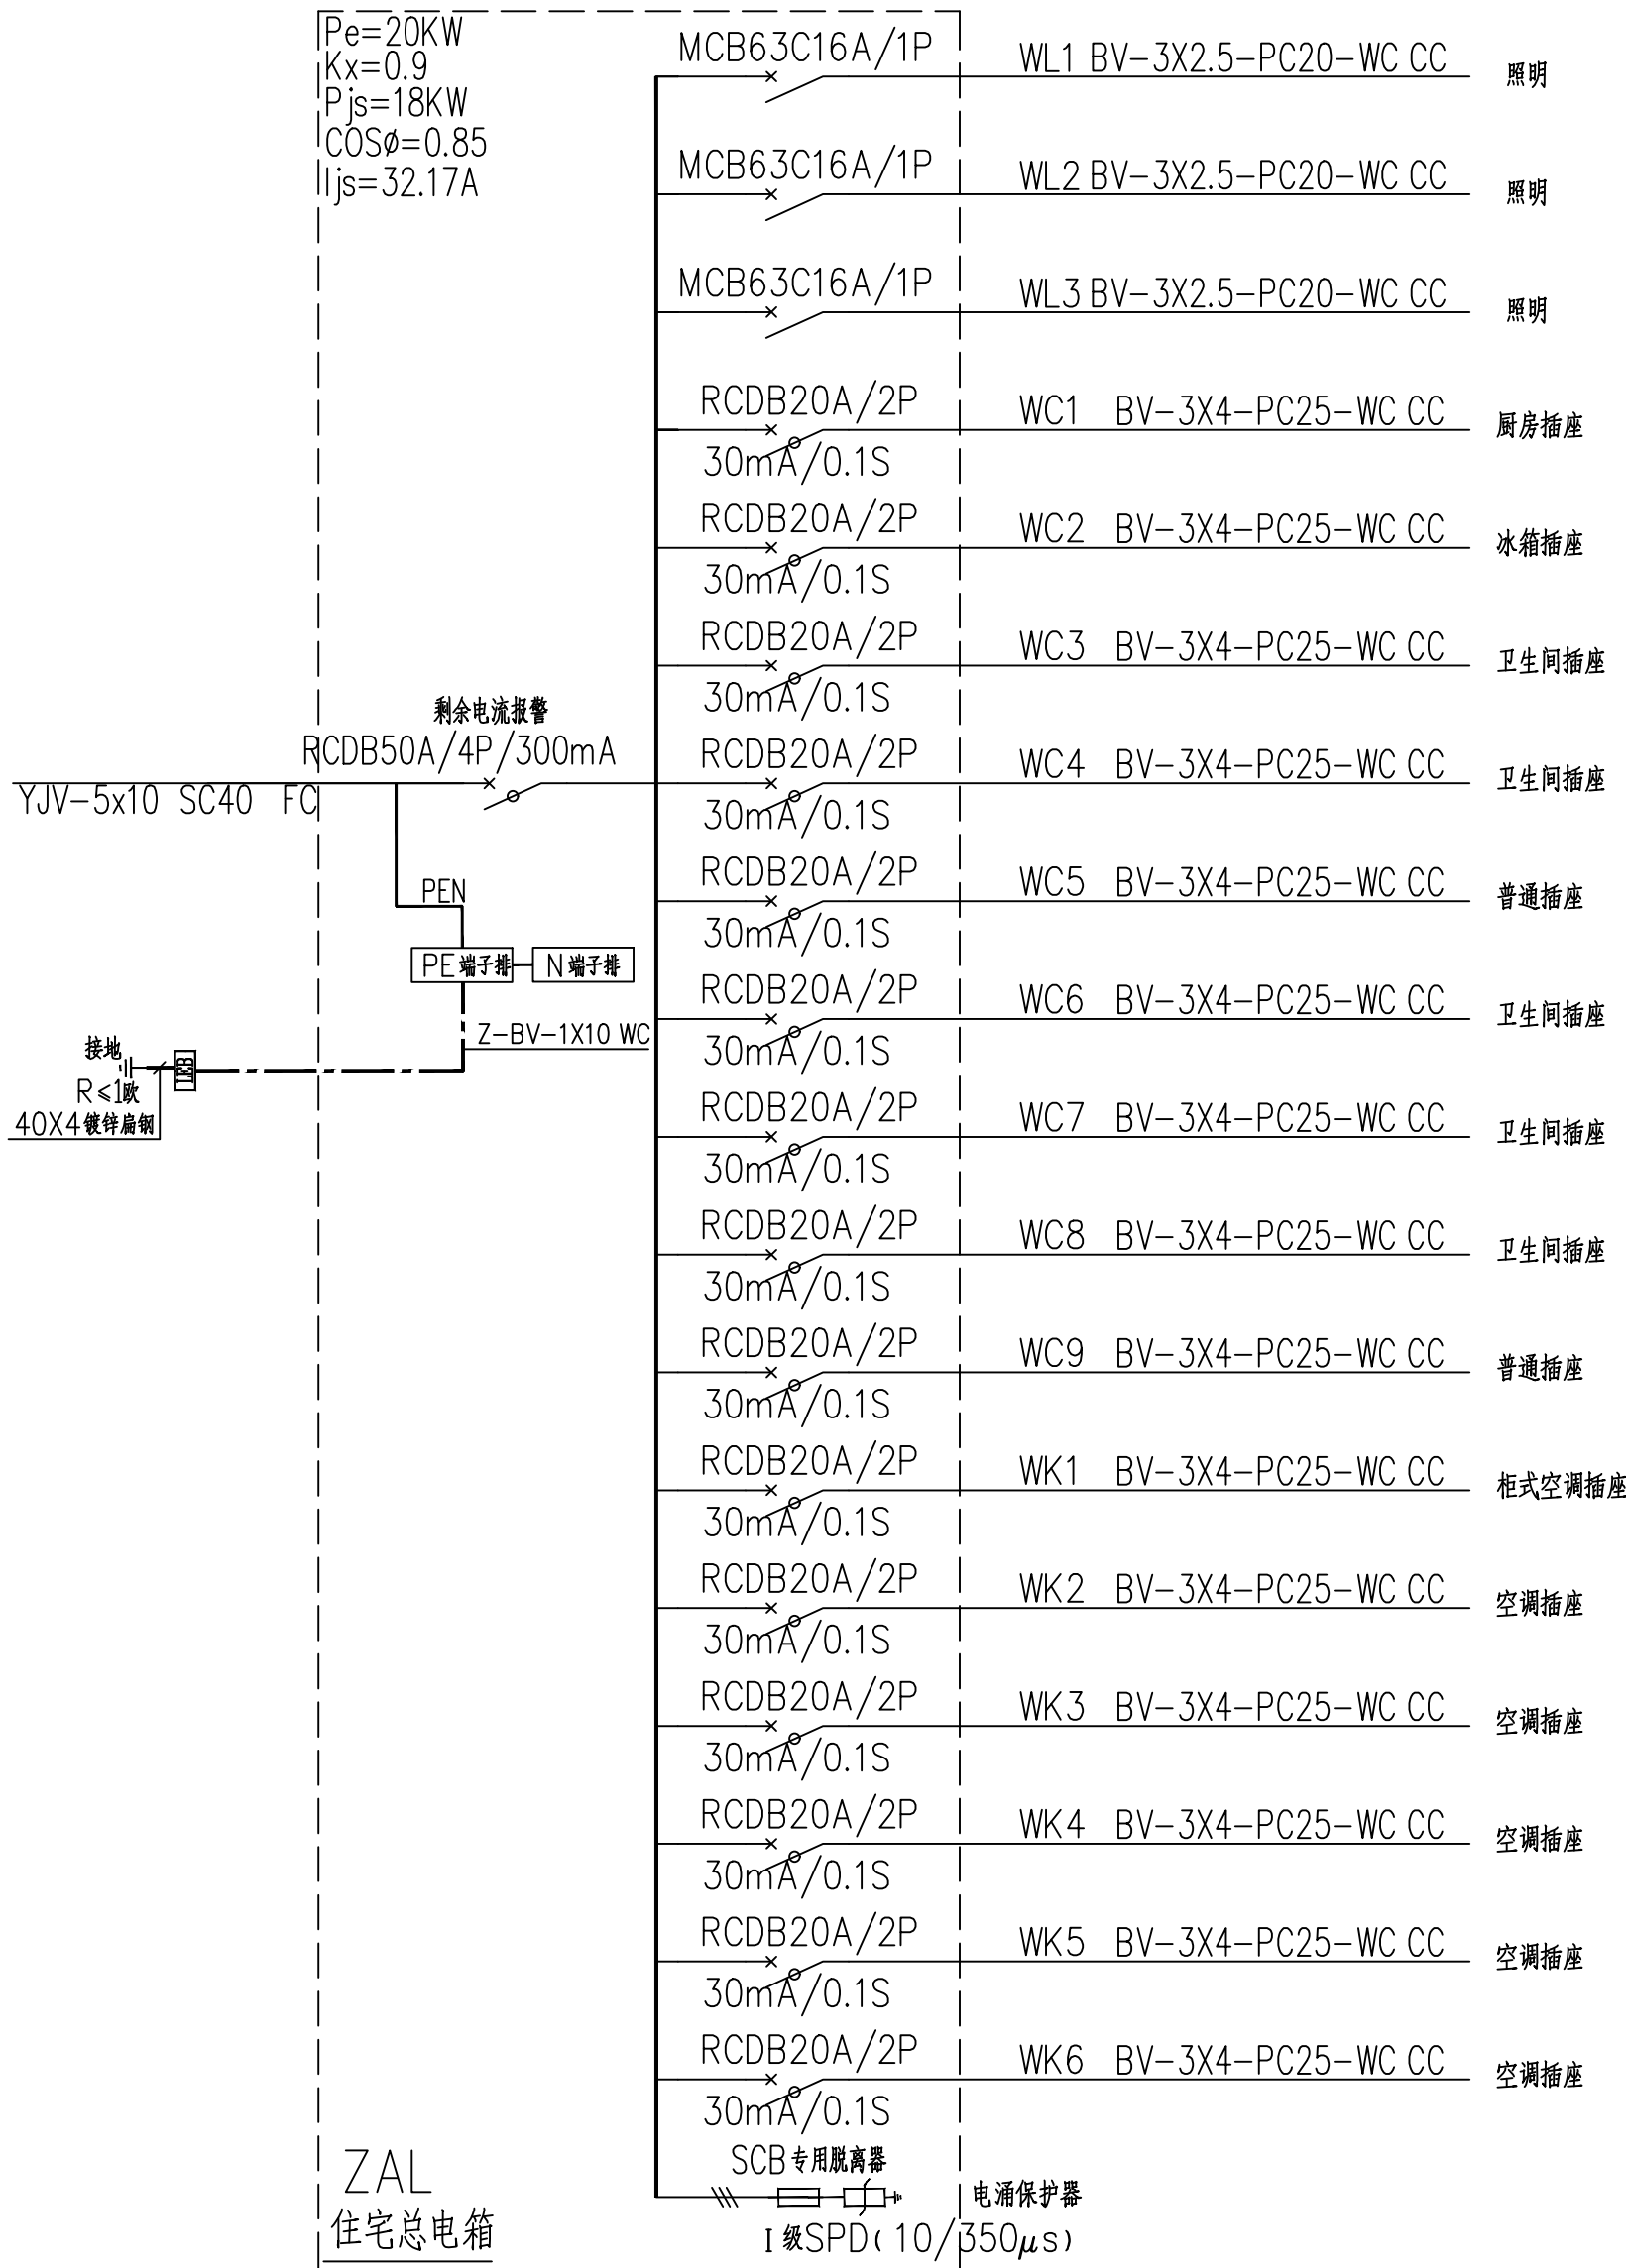

家居配电箱接线示意图

注：家居配电箱的电源插座采取隔离措施。

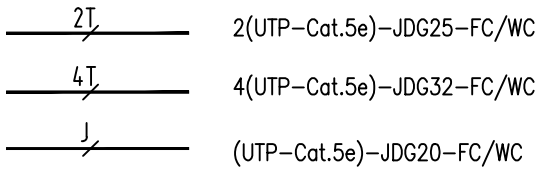

电话通信、网络通信、有线电视三网合一系统

设计依据：《住宅区和住宅建筑内光纤到户通信设施工程设计规范》GB50846-2012

《住宅小区及商住楼通信设施建设标准》DBJ 43/003-2012

- 1、本工程弱电系统采用FTTH（光纤到户）的方式，实现三网合一。
- 2、本工程弱电设备间设于一层，弱电机房大小按满足4家运营商同时接入进行预留。机房内机柜和箱体由各自运营商负责设计安装。
- 3、在本建筑物一设置无跳接光缆交接箱，箱内设置光分路器，通过24或48芯单模光纤，接至楼层竖井内的光分纤箱。每个光缆交接箱配线户数不超过三百户。
- 4、光分纤箱至住户家庭信息箱的线缆应一次布放到位，每户按两条单芯蝶形光缆和一条SYWV-75-5同轴电缆进行配置。
- 5、家庭信息箱内应设置两个AC220V的电源插座，插座引自就近的照明回路。箱体内应提供电话、数据、有线电视等网络综合接线模块。强弱电之间应有安全隔离措施。家庭信息箱底边距地0.4m安装。
- 6、每户在起居室和主卧室各设置一个电视插座，用户电视插座暗装，底边距地0.4m。支线电缆选用SYWV-75-5,穿PVC20管沿墙及楼板暗敷。起居室、主卧和书房（次卧）各设置一个网络插座，网络插座选用RJ45超五类型，与网线匹配，插座暗装，底边距地0.4m。其中起居室和主卧的网络插座设于电视机插座旁。网络采用超五类对绞线,穿PVC20管沿墙及楼板暗敷。起居室和主卧各设置一个电话插座，电话插座暗装，底边距地0.4m。电话采用4对对绞线，穿PVC20管沿墙及楼板暗敷。
- 7、高层住宅楼配线应采用竖井上升方式，按照16户为最大容量考虑，分层设置壁挂式单元配电箱。
- 8、所有箱体及金属导管都应可靠接地。