


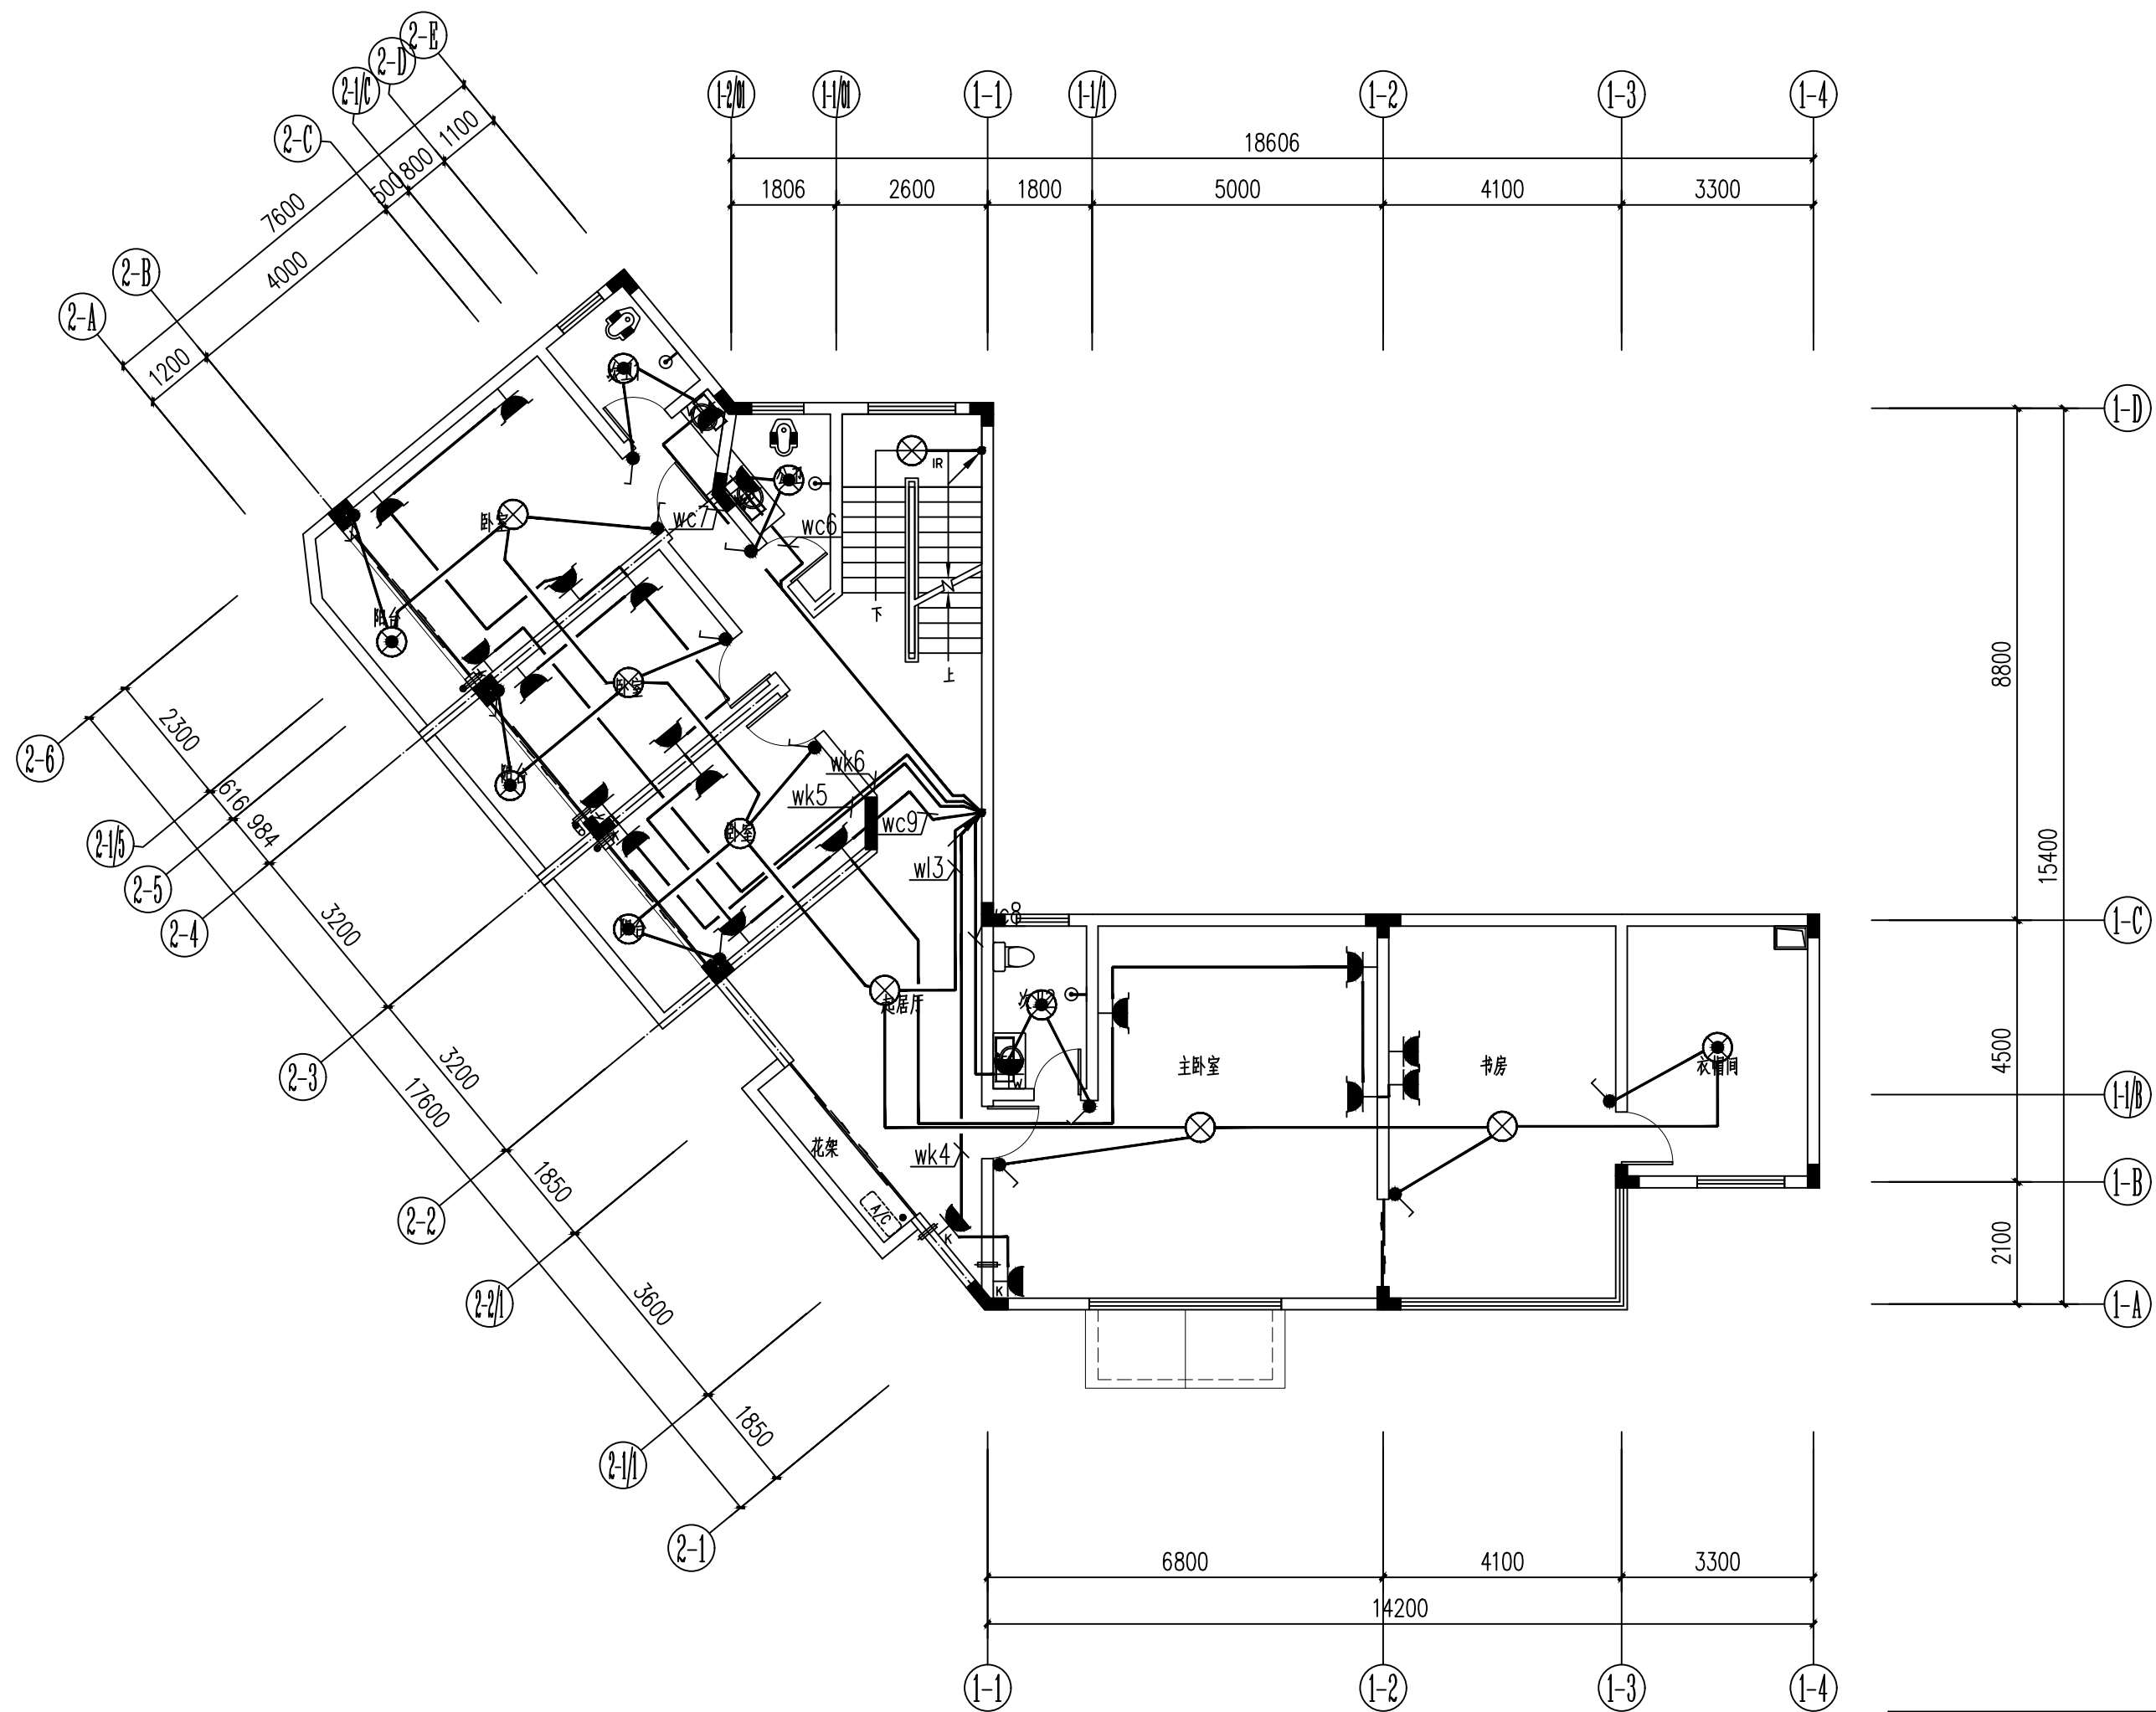

二层强电平面图 1:100

二层强电平面图