


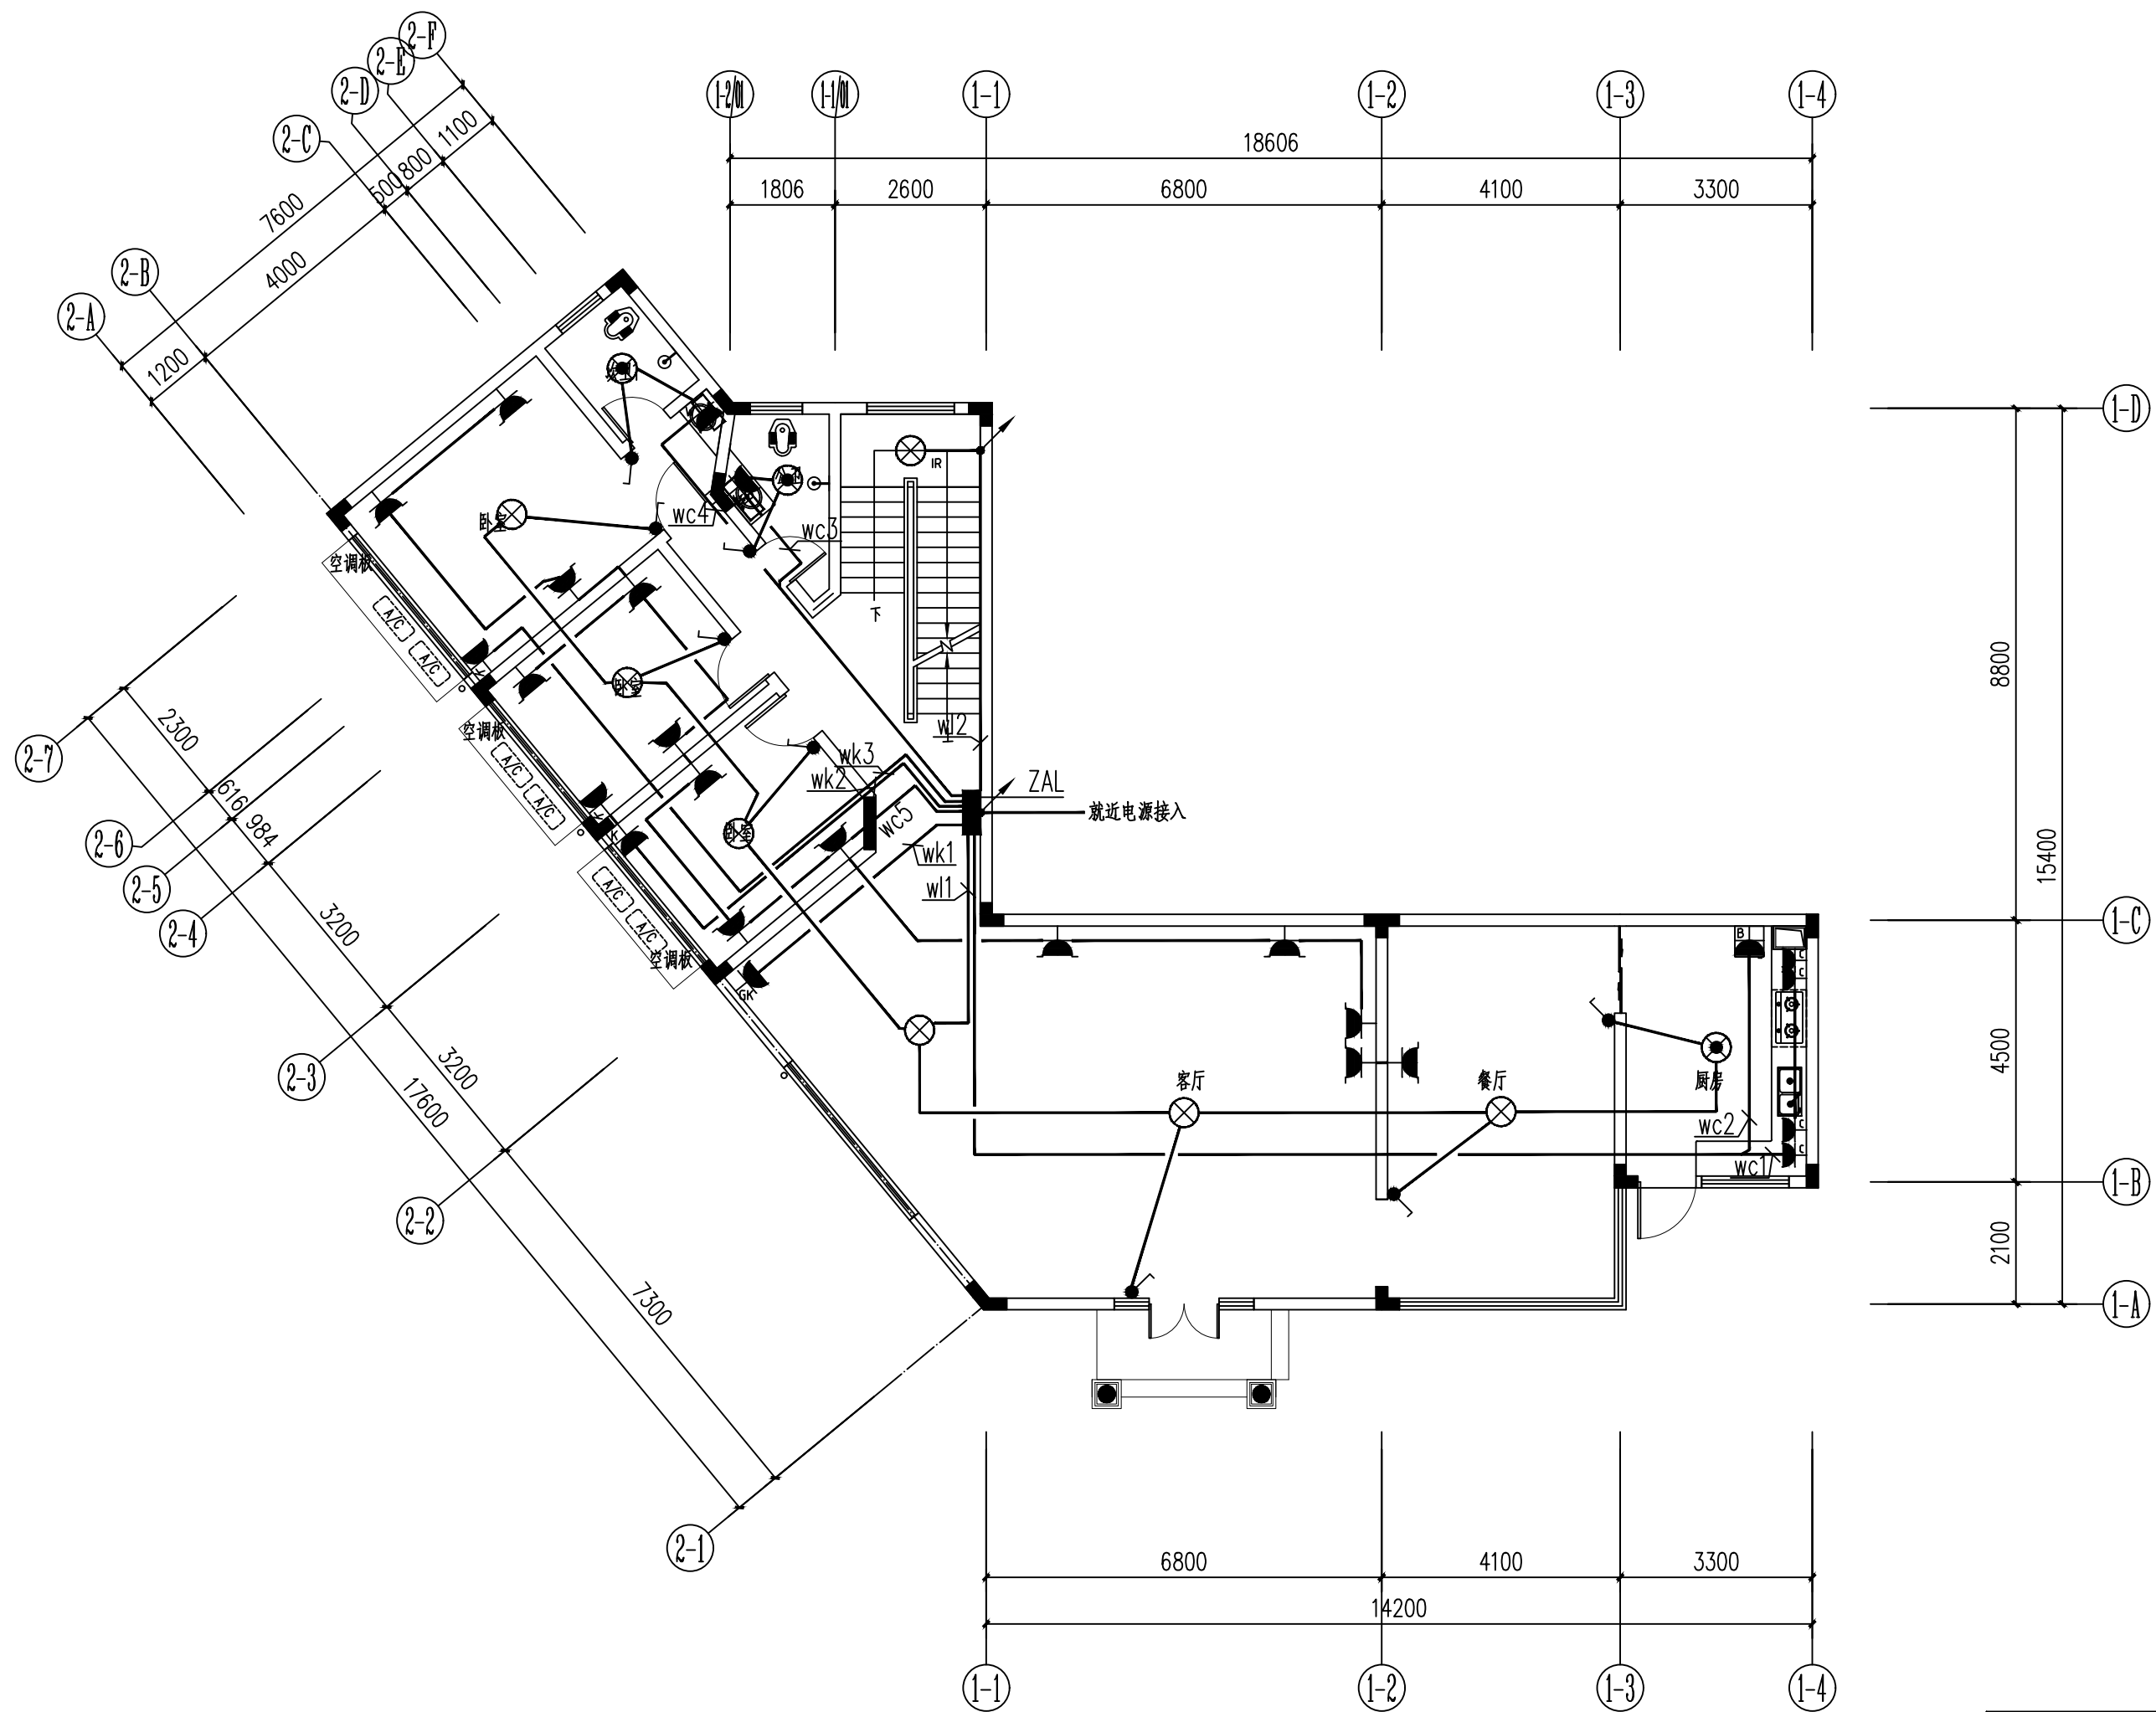

一层强电平面图 1:100

一层强电平面图