

建设单位/CLIENT:


麻阳苗族自治县远桥房地产开发有限公司

项目名称/PROJECT:
远程国际

子项目名称/SUB-PROJECT:

远程国际


区位图/REGIONAL LOCATION MAP :

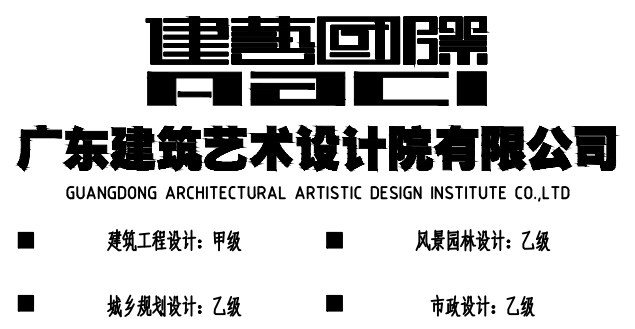

图纸名称/TITLE:

负一层平面图

项目名称/PROJECT: 远程国际

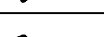设计 DESIGNED	古新辉	
校对 CHECKED	吴新红	
专业负责人 CHIEF	吴志刚	
项目负责人 PROJECT CHIEF	吴志刚	
审核 IDENTIFIED	黄履优	
审定 APPROVED	李 坚	

业务号/JOB NO.

设计阶段/STATUS: 施工图

专业/DISCIPLINE: 建施

比例/ SCALE:	1: 100	规格/ SIZE:	A1
---------------	--------	--------------	----


出图日期/DATE: 2021.06

图号/DRAWING NO. JS-13

版次 NO.	修改内容 DESCRIPTION	日期 DATE

条形码/BARCODE:

版权所有，不得复制、套用。
ALL RIGHTS RESERVED, DON' T COPIED, REPRODUCED.

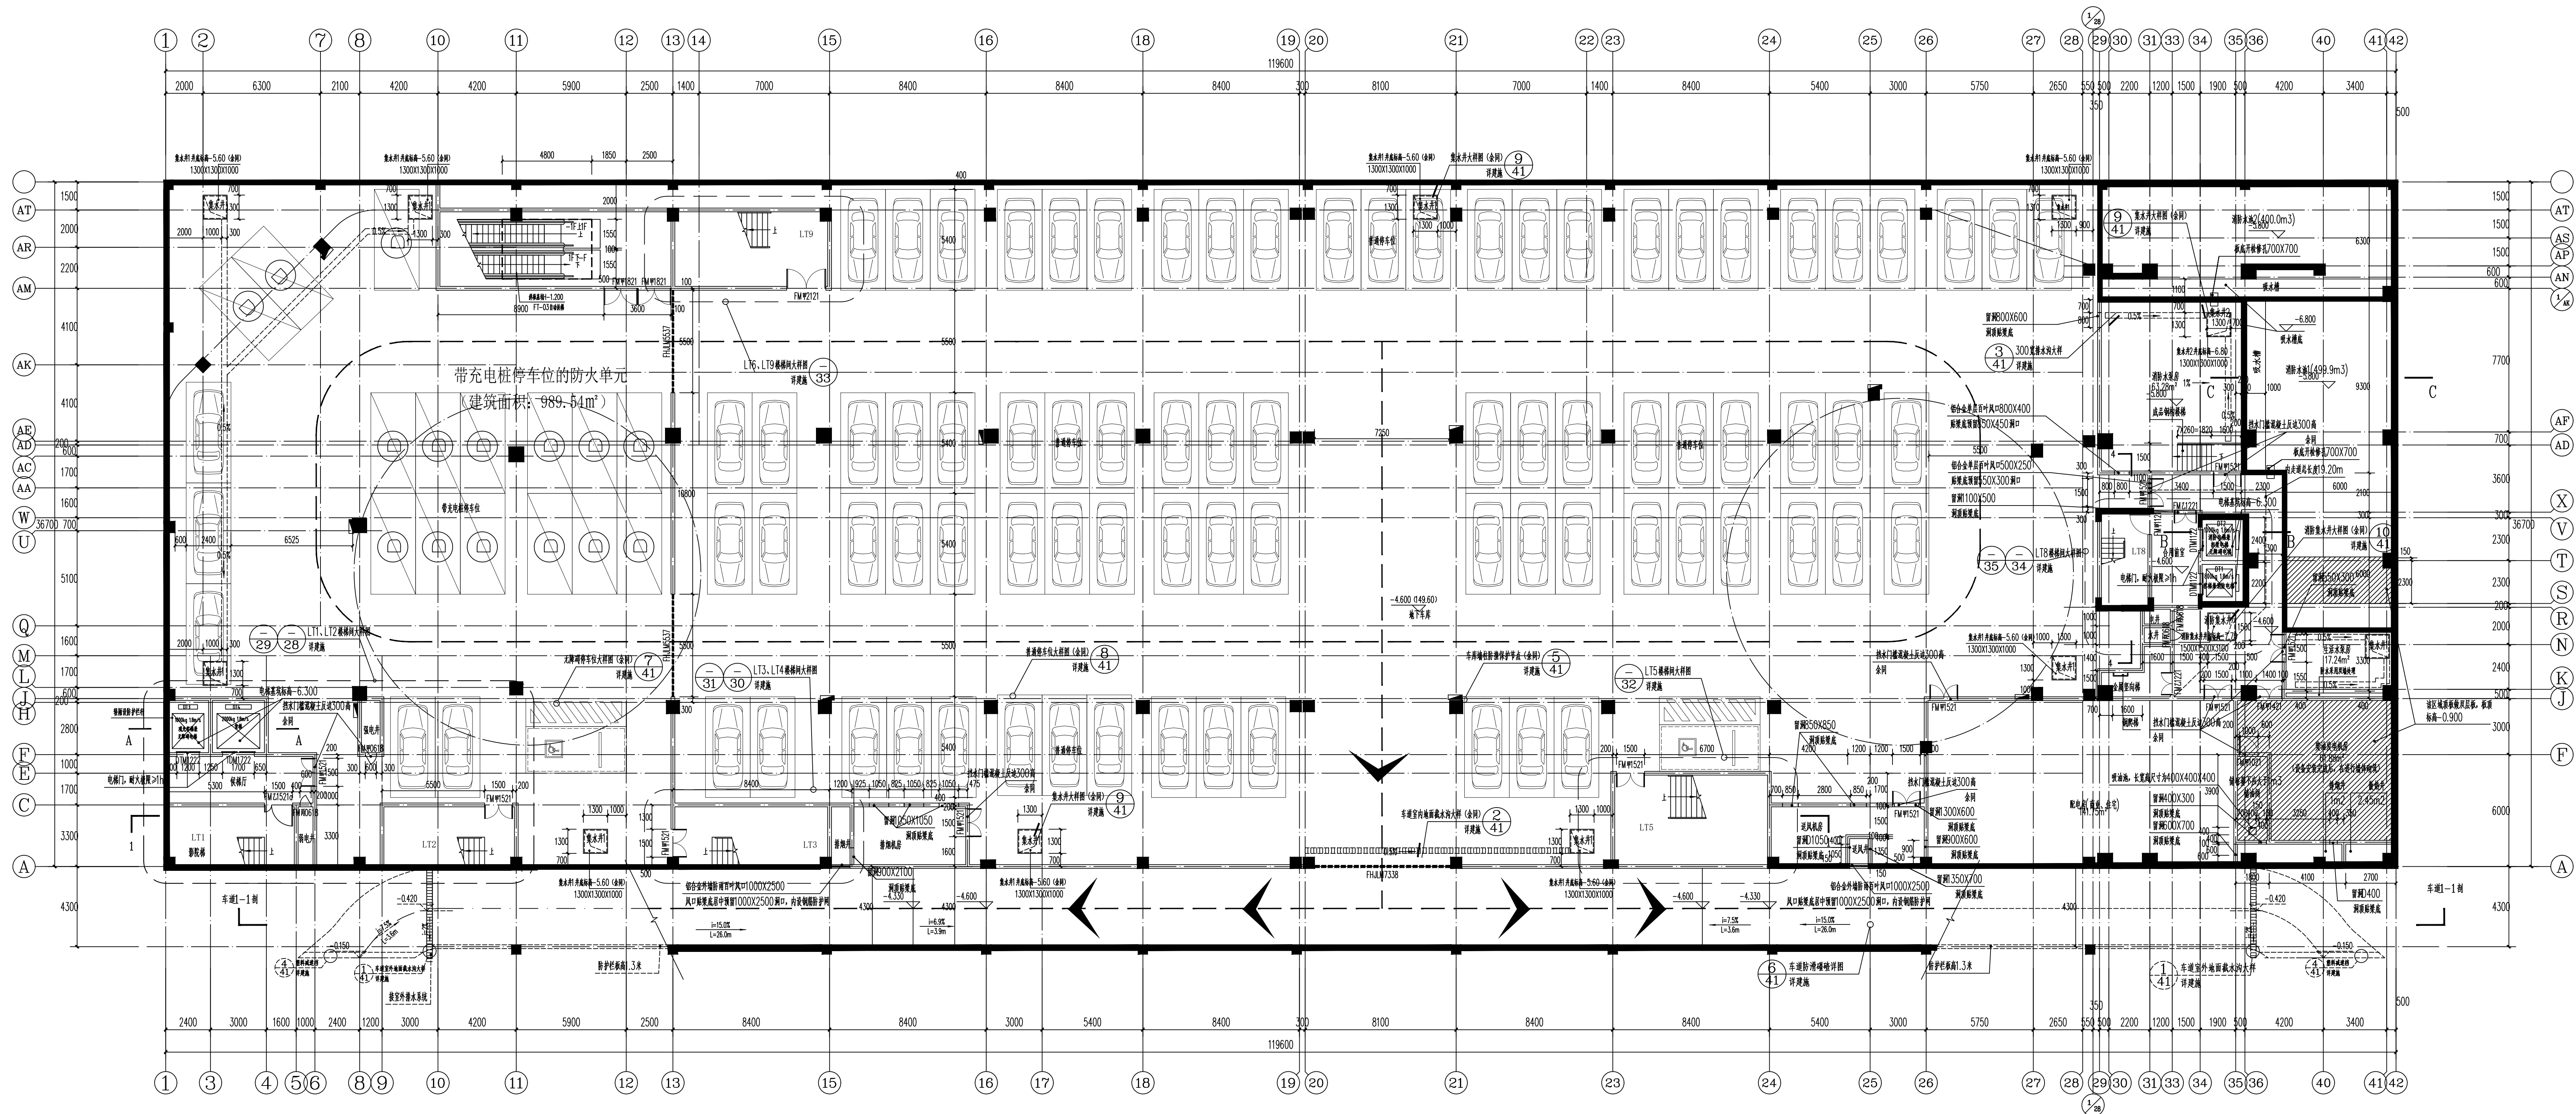

负一层平面图 1:150


本层建筑面积: 4663.04m²

停车位：总计100个，其中含带充电桩车位15个，无障碍车位2个，普通车位83个

图例：

普通车位:

带充电桩车

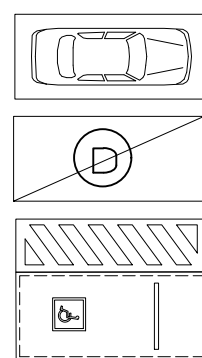

消防示意图例

S	合用前室及前室
T	疏散楼梯
ST	金属竖梯
D	客梯、货梯
FT	自动扶梯
XD	消防电梯
➡	安全出口


车位图例

	帶充电桩车位
	普通车位
	无障碍车位

注:防火分区间均采用防火墙分隔
防火墙上所开门窗均为甲级防火门窗
所有直接开向车库的门均为甲级防火门

负一层防火分区示意图 1:500

注：地下车库设置自动喷淋灭火系统
负一层设2个防火分区，其中两个防火分区一还有一个带充电设施的防火单元，每个防火分区（防火单元）均设有2个以上的安全出口。
防火分区的普通车库区设有3个安全出口，防火分区内最远点至最近安全出口的距离为49.5m（ $\leq 60m$ ），满足规范要求。
防火分区一内带充电设施的防火单元有2个安全出口，防火分区内最远点至最近安全出口的距离为40.6m（ $\leq 60m$ ），满足规范要求。
防火分区二有2个安全出口，其中一个为金属竖梯，房间内最远点至最近安全出口的距离为11.3m（ $\leq 27.5m$ ），满足规范要求。
最远疏散门至最近安全出口的距离为6.4m（ $\leq 50m$ ），满足规范要求。

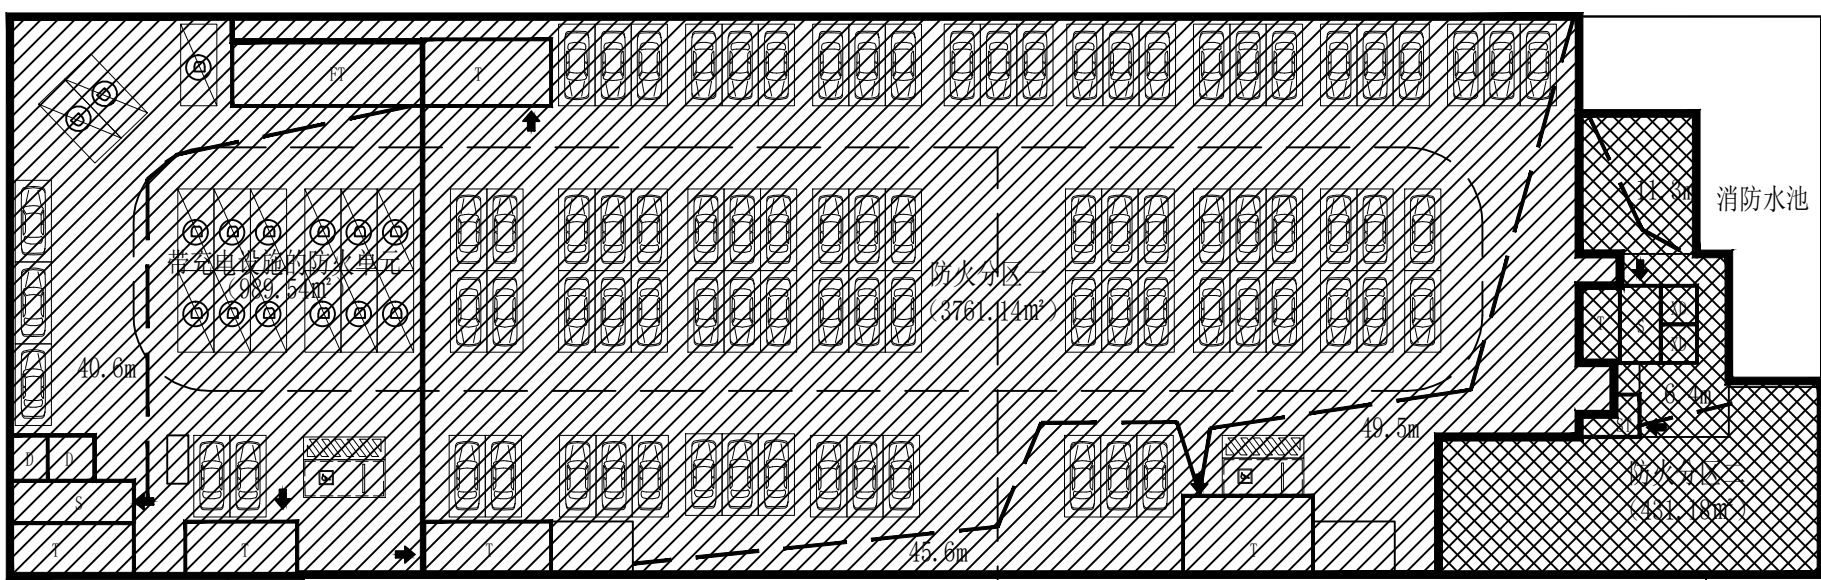

注明:

- | | |
|---|--|
| <p>地下车库标高使用绝对标高。</p> <p>4. 本车库中风机设备房等设备安装用房中防火门在设备安装完毕土建施工预留洞口等设备安装完后再次安装防火门。有风贯穿穿墙位, 预留顶下1m高洞洞, 待风贯穿安装完后砌筑。</p> <p>5. 本地下车库中钢筋混凝土柱、柱及其专业管道预埋尺寸按相关专业施工图纸施工。</p> <p>地下车库墙柱预埋与相关专业配合。</p> <p>6. 本地下车库中未及标注的门窗尺寸(核心筒及楼梯间内除外)均为100/200宽或中窗。</p> <p>7. 本地下车库防火卷帘门采用耐火面提升耐火极限满足条件, 且耐火极限不低于3.0小时的甲级钢卷防火卷帘门, 尺寸详门窗表。</p> <p>8. 本地下车库中除钢筋混凝土梁外, 其余墙柱均采用200厚页岩多孔砖, 框柱框中或混凝土柱或混凝土梁。框柱中或混凝土柱或混凝土梁。</p> <p>9. 楼梯平台及楼面见各单元楼梯间平面图及剖面图。</p> <p>10. 集水坑、排水沟在各单位内任意位置, 其定位及做法详附图。防水做法按节点最大标高。宽300mm, 坡度点距150mm, 水系室内地面均向排水沟找坡1%。排水沟向集水坑找坡0.5%。</p> <p>11. 集水坑及屋面排水详图, 排水沟做法详附图, 盖板为铸钢盖板。</p> <p>12. 所有车道旁车位均设置防撞设施, 车位下方设置防撞设施, 位置同附图。</p> | <p>11. 地下室防水构造</p> <p>施工防水构造10J301 $\frac{1}{42}$</p> <p>后浇带防水构造10J301 $\frac{1}{49}$</p> <p>基础逆坡防水构造10J301 $\frac{1}{27}$ $\frac{1}{27}$ $\frac{1}{27}$</p> <p>坑槽防水构造10J301 $\frac{1}{41}$</p> <p>框头防水构造10J301 $\frac{1}{59}$</p> <p>12. 风机基础采用C20砼垫层, 垫层高度为150。</p> <p>13. 设备用房采用耐火极限不低于1.50h的不燃性板或防火隔墙或耐火极限不低于1.50h的防火卷帘。</p> <p>14. 储油间的油桶应密封且应设置通向室外的通气孔, 通气管应设置带阻火器的呼吸阀。</p> <p>油桶的下方应设置防止油品流出的设施。</p> <p>15. 地下室标高-6.600相当与绝对标高为14.9.60</p> <p>16. 管道井及设备安装间防水做法, 门为防水300C20混凝土门。</p> <p>17. 成品管井。</p> |
|---|--|