


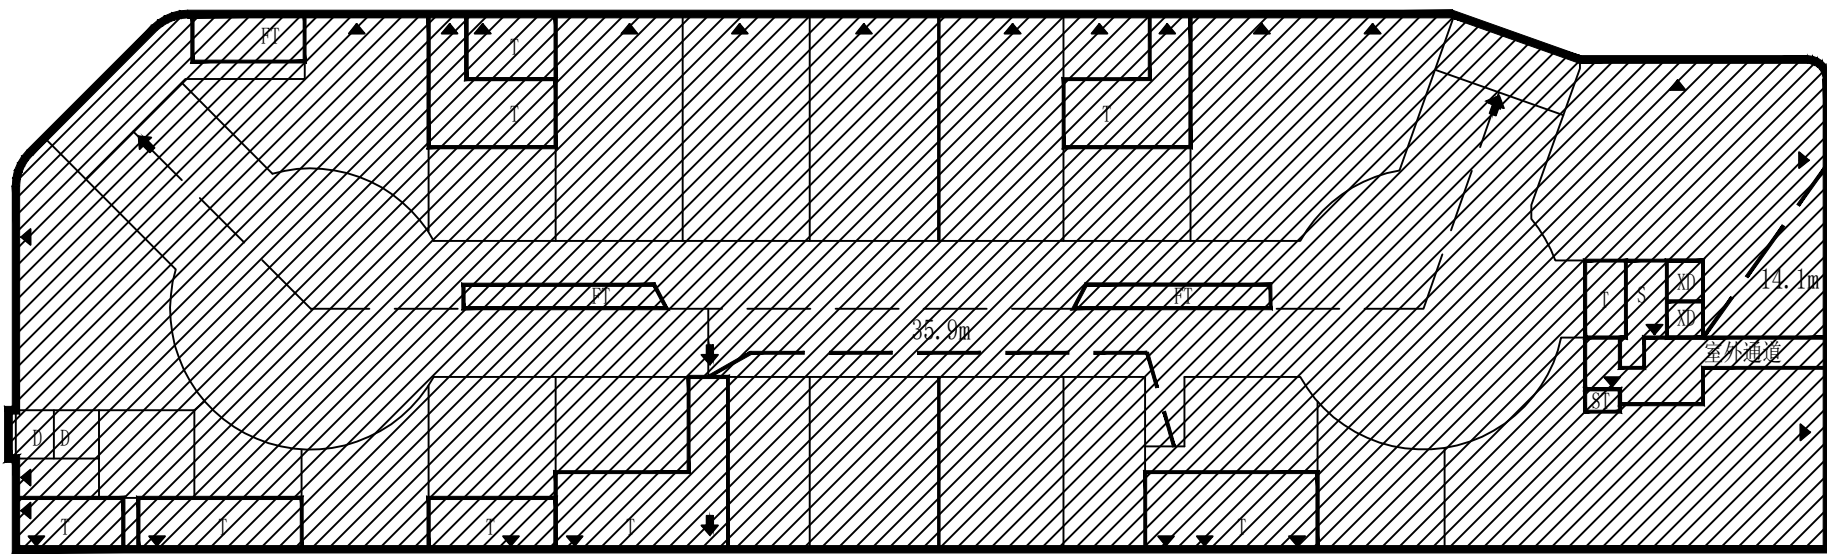

一层防火分区示意图 1:500


注：一层商场设置自动喷淋灭火系统
 本层为一个防火分区，防火分区面积为4129.28㎡，共有3个安全出口。
 房层内最远点至最近安全出口的距离为14.1m≤27.5m，最远疏散门至最近安全出口的距离为35.9m(≤37.5m)，满足规范要求。
 本层需要的疏散宽度为3692.11X0.43X1/100=15.87m(计算疏散宽度的面积是减掉一层所有楼梯间面积后的净面积)
 本层设计的疏散宽度为7.2X2+2.4=16.80m，满足规范要求。

一层平面图 1:150

本层建筑面积: 4129.28m²
总建筑面积: 22985.06m²
计容总建筑面积: 18157.36m²
不计容总建筑面积: 4827.70m²

图例

 灰砂加气混凝土砌块 (商铺隔墙)
 消火栓

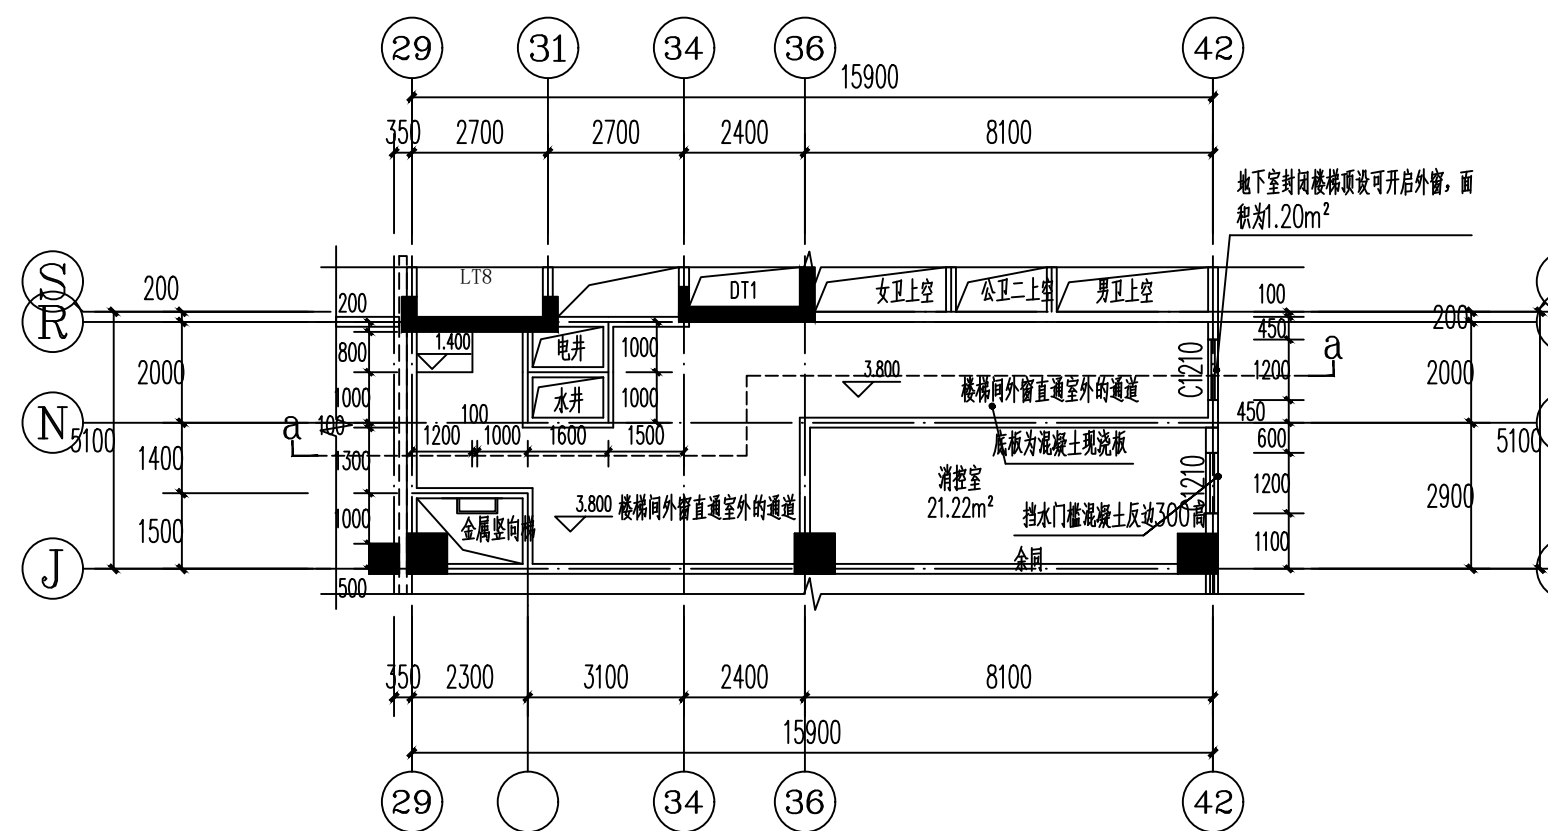

室外通道夹层平面图 1:150 注: a-a剖面图详IS-25

注明：

- 柱、柱位置尺寸详见详图。
- 除图中注明者外，门窗窗洞口的墙垛均为100mm或平柱、墙垛、墙中安装。
- 本工程所有外墙厚度均为240厚钢筋混凝土压加气混凝土砌块，墙垛墙体外侧均为100厚，内侧均为140厚。
商榷墙垛墙体外侧注明均为100厚灰砂加气混凝土砌块，其余墙垛均为200厚烧结实心多孔砖。
- 门窗台高小于900mm时，作防护栏杆具体做法详见11ZJ3401《建筑工程施工工艺安全操作规程》，防止人员坠落。
- 各种设备布置、管径、管进及埋设等具体做法应同时参照及配合专业图纸，以免遗漏。
- 本楼设自动喷淋灭火系统，消防栓位置见详图。
- 管道井及设备用房除防水进水的房间，下方应设300高C20混凝土盖板，厚度同楼板。
- 除室外外，卫生间明楼地面标高均 ± 0.05 ；卫生间坐便器安装标高均为 ± 0.03 ，以 ± 1.2 楼面标高，（H为楼面标高），详见卫生间大图。
- 所有外墙外窗、更衣室窗玻璃为磨砂玻璃。
- 外墙窗洞与卫生间完成面相应标高或新面 ± 0.05 ，并应有预埋过梁，具体详见11ZJ11-A-4图。
- 外墙窗洞预埋11ZJ111-A-26，内窗洞预埋11ZJ111-A-7-4-9，地面标高预埋11ZJ111-A-7-2，楼面标高预埋11ZJ111-A-8-1-8。
- 人行出入口及疏散门为2个主入口的钢结构玻璃门，其他地方设置双开120°钢化玻璃门玻璃厚0.76mm厚钢化玻璃夹胶玻璃。
- 3-3疏散楼梯间门为玻璃门宽 ≥ 1.0 m $\times 1.0$ m，下楼梯室的地面不 ≤ 1.2 m，门洞尺寸 ≥ 2.0 m，门扇扇面玻璃，并拉直可在室外最认可的扇面长度，详见平面、立面图。
- 电梯轿厢门套高1000 $\times 2200$ ，轿厢门洞700 $\times 2200$ 均同大照壁不宜低 ≥ 1.0 m，轿梯、扶梯梯高 ≥ 1.700 。D3观光电梯轿厢内设防护栏杆。
- 玻璃幕墙自外墙、幕墙三层的设置可另加幕墙总高 ≥ 2 m，开窗面积不大于 $\frac{1}{3}$ 。
- 玻璃幕墙玻璃与幕墙以及幕墙板的嵌缝均采用硅酮耐候密封胶。
- 楼层门套高度在门套洞口顶部为300mm，门洞高度 ≥ 2.0 m，在幕墙洞口侧做嵌边，垂直高度为300mm嵌边高度。
- 公共楼梯、电梯梯井净宽 ≥ 2 m时，必须采取防止少年儿童攀爬的措施，住宅建筑、电梯井净宽 ≥ 1.1 m时，必须采取防止儿童攀爬的措施。
- 图中设备管道间尺寸及设备布置专业图纸冲突时以专业图纸为准。

建设单位/CLIENT:

麻阳苗族自治县远桥房地产开发有限公司

项目名称/PROJECT:

远程国际

子项目名称/SUB-PROJECT:

远程国际

区位图/REGIONAL LOCATION MAP :



图纸名称/TITLE:

一层平面图

项目名称/PROJECT:

远程国际

设计 DESIGNED	古新辉	
校对 CHECKED	吴新红	
专业负责人 CHIEF	吴志刚	
项目负责人 PROJECT CHIEF	吴志刚	
审核 IDENTIFIED	黄履优	
审定 APPROVED	李 坚	

业务号/JOB NO.

设计阶段/STATUS: 施工图

专业/DISCIPLINE: 建施

比例/ SCALE:	1: 100
---------------	--------

出图日期/DATE: 2021.06

图号/DRAWING NO. JS-14

版次 NO.	修改内容 DESCRIPTION	日期 DATE

条形码/BARCODE:

版权所有，不得复制、套用。
ALL RIGHTS RESERVED, DON'T COPIED, REPRODUCED.