

建设单位/CLIENT:

麻阳苗族自治县远桥房地产开发有限公司

项目名称/PROJECT:

远程国际

子项目名称/SUB-PROJECT:

远程国际

区位图/REGIONAL LOCATION MAP :

广东建筑艺术设计院有限公司
GUANGDONG ARCHITECTURAL ARTISTIC DESIGN INSTITUTE CO.,LTD

■ 规划工程设计：甲级 ■ 风景园林设计：乙级

■ 城乡规划设计：乙级 ■ 市政设计：乙级

图纸名称/TITLE:

商业屋顶平面图
商业屋顶构件平面图

项目名称/PROJECT:

远程国际

NAME		NO.
------	--	-----

DESIGNED		
----------	--	---

CHECKED	大新江	美打只
---------	-----	-----

专业负责人 CHIEF	吴志刚	吴志刚
----------------	-----	-----

项目负责人 PROJECT CHIEF	吴志刚	吴志刚
------------------------	-----	-----

审核 IDENTIFIED	黄履优	
------------------	-----	---

审定
APPROVED

李 坚



业务号/JOB NO.

设计阶段/STATUS: 施工图

专业 / DISCIPLINE: 建筑

比例/		规格/	
-----	--	-----	--

SCALE.		SIZE.	
--------	--	-------	--

图 97 DRAWING NO. 35 10


版次 NO.	修改内容 DESCRIPTION	日期 DATE
-----------	---------------------	------------

[illegible][illegible]

条形码/BARCODE:

版权所有 不得复制 李田

ALL RIGHTS RESERVED, DON'T COPY, REPRODUCED.

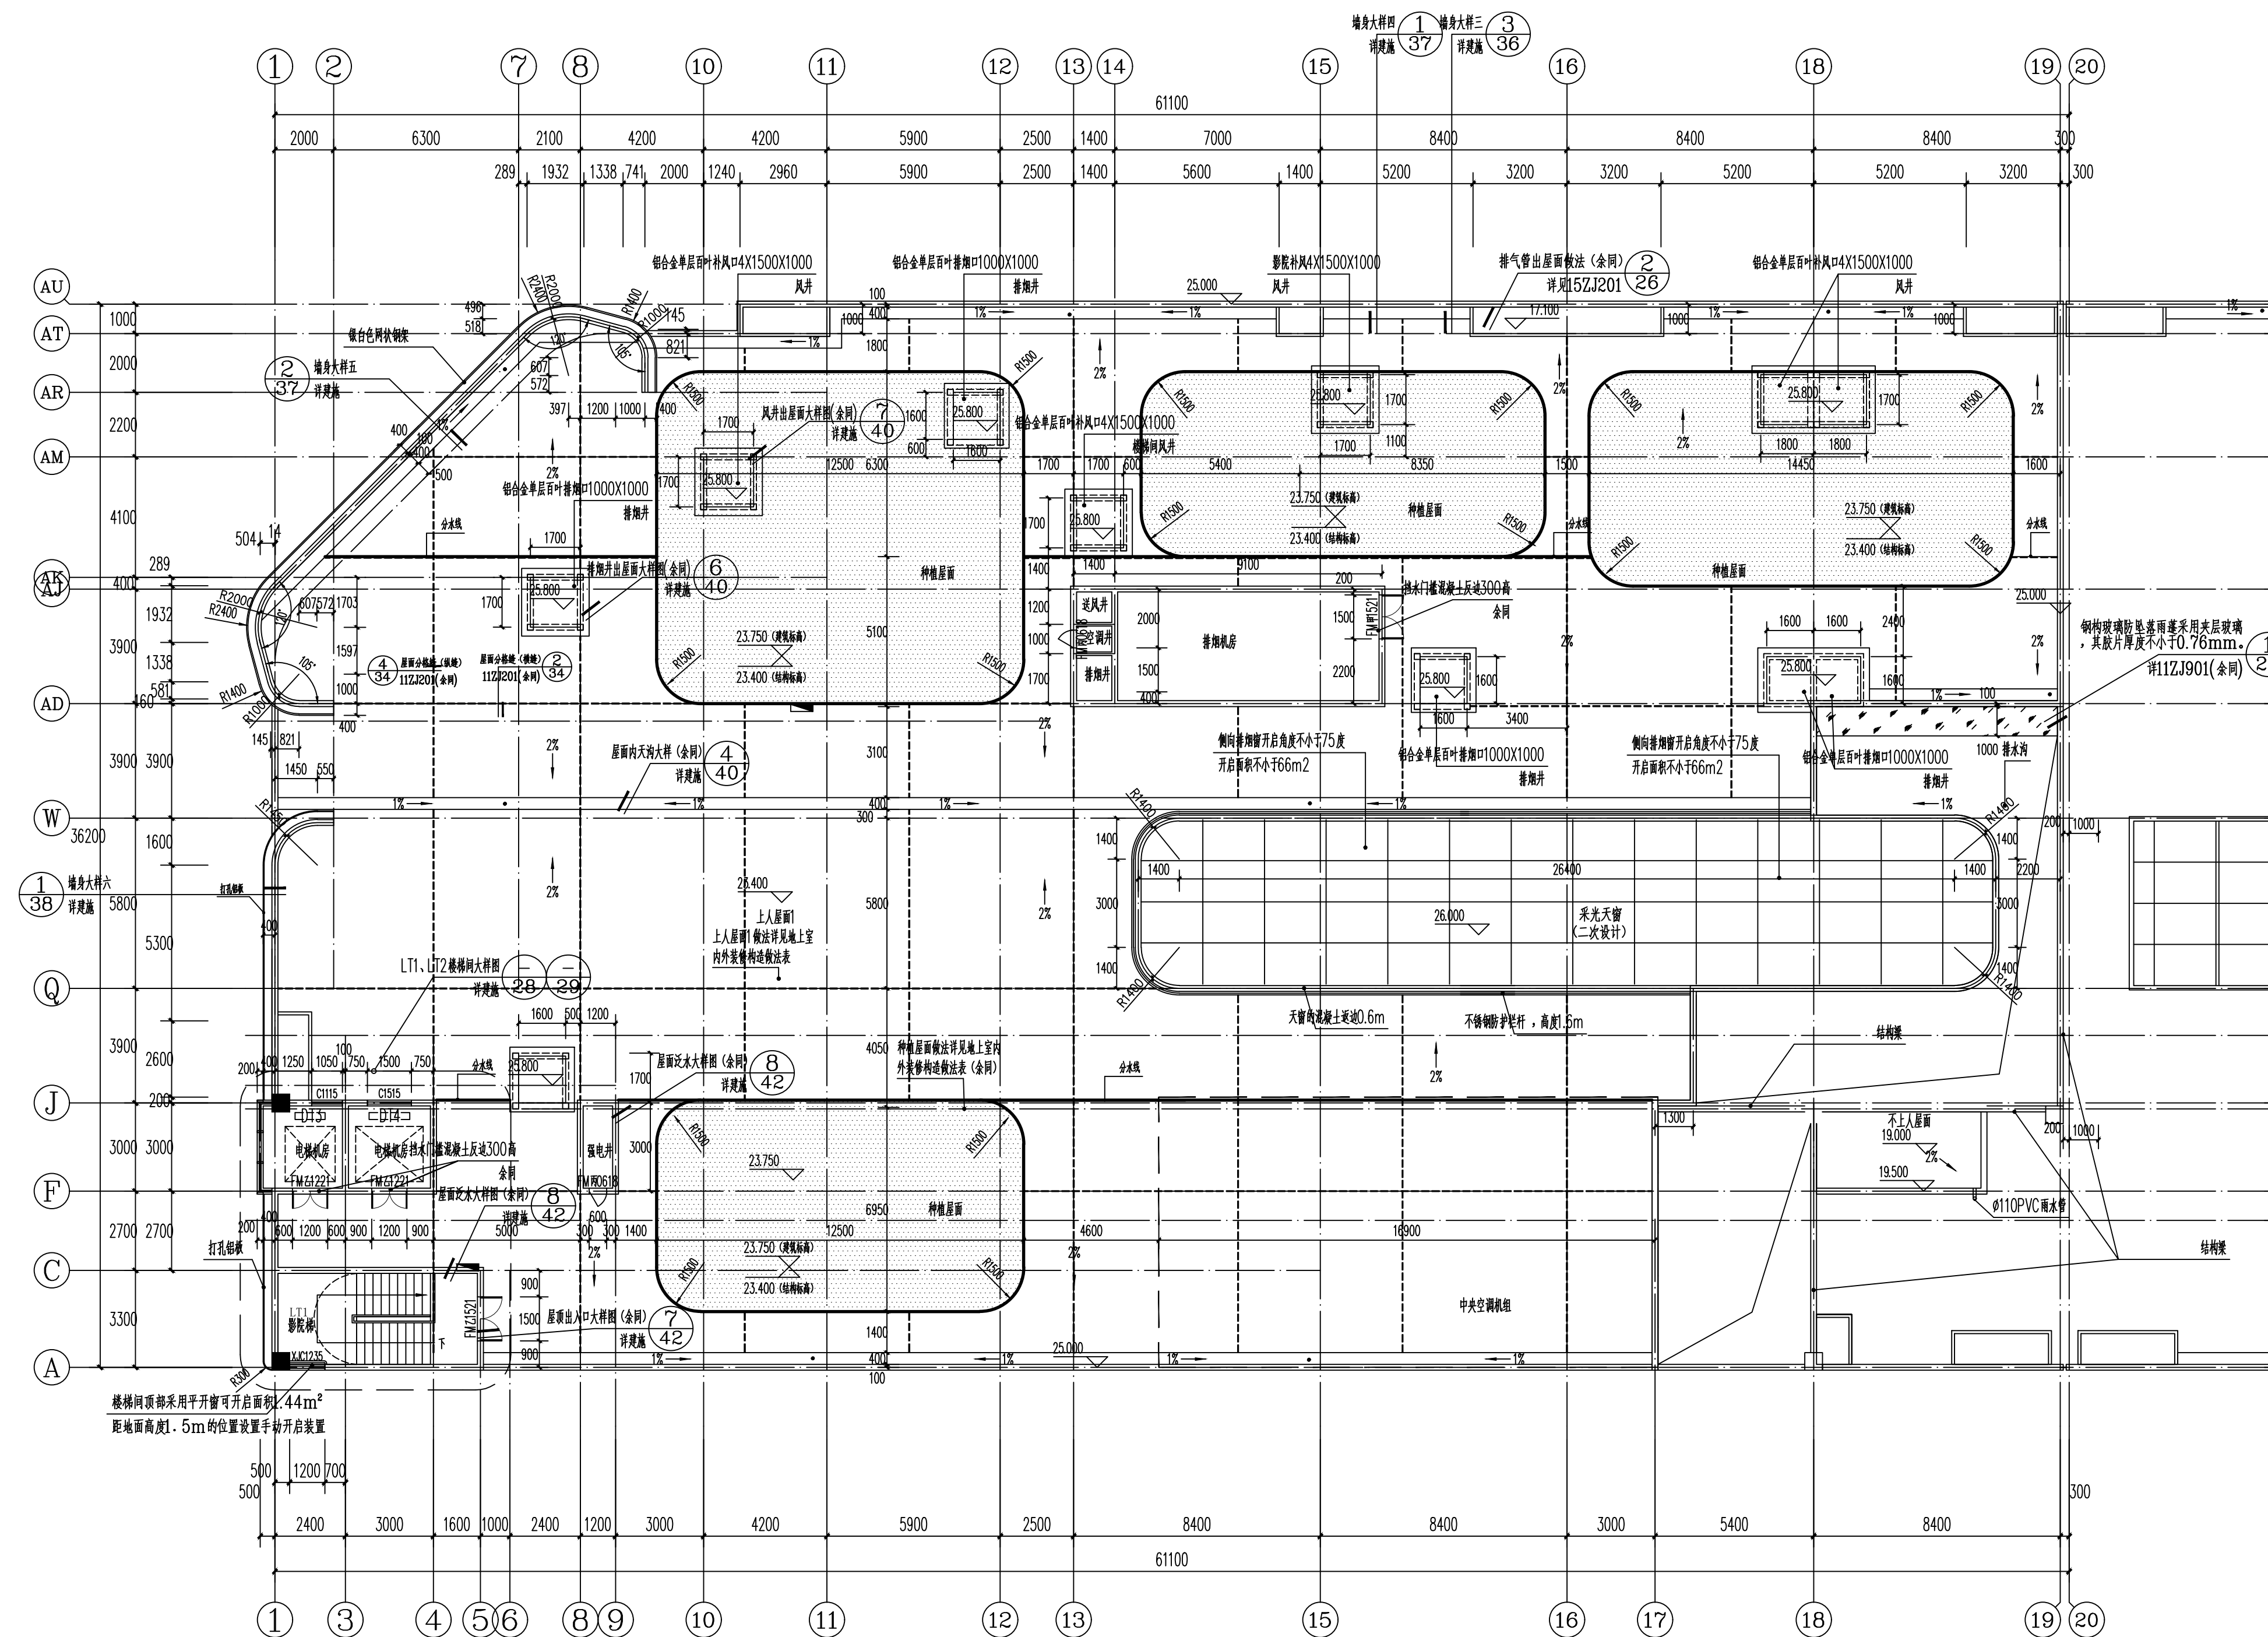


商业屋顶平面图 1:150

本层建筑面积: 82.85m²

图例

 消火栓

注：1、保温材料为：难燃橡塑保温板聚苯板
防水材料为：4.0厚单组份聚氨酯防水涂料+3厚自粘聚合物改性沥青防水卷材
种植屋面做法详见种植地上室内外装饰装修做法表
种植屋面②做法详见种植地上室内外装饰装修做法表
非上人屋面做法详见15ZJ001-122~105
屋面分格缝做法详见15ZJ201③④⑤⑥⑦⑧⑨⑩⑪⑫⑬⑭⑮⑯⑰⑱⑲⑳㉑㉒㉓㉔㉕
屋面亮油做法详见11ZJ111④⑤⑥⑦⑧⑨⑩⑪⑫⑬⑭⑮⑯⑰⑱⑲⑳㉑㉒㉓㉔㉕
2、小屋面至屋顶大屋面的雨水管下穿屋面做法，做法详见15ZJ201①
3、屋面排水110UPVC雨水管，做法详见115ZJ201①
4、檐口、屋面女儿墙做法详见17J301①②③④⑤⑥⑦⑧⑨⑩⑪⑫⑬⑭⑮⑯⑰⑱⑲⑳㉑㉒㉓㉔㉕
5、透气管屋面做法详见15ZJ201①②③④⑤⑥⑦⑧⑨⑩⑪⑫⑬⑭⑮⑯⑰⑱⑲⑳㉑㉒㉓㉔㉕

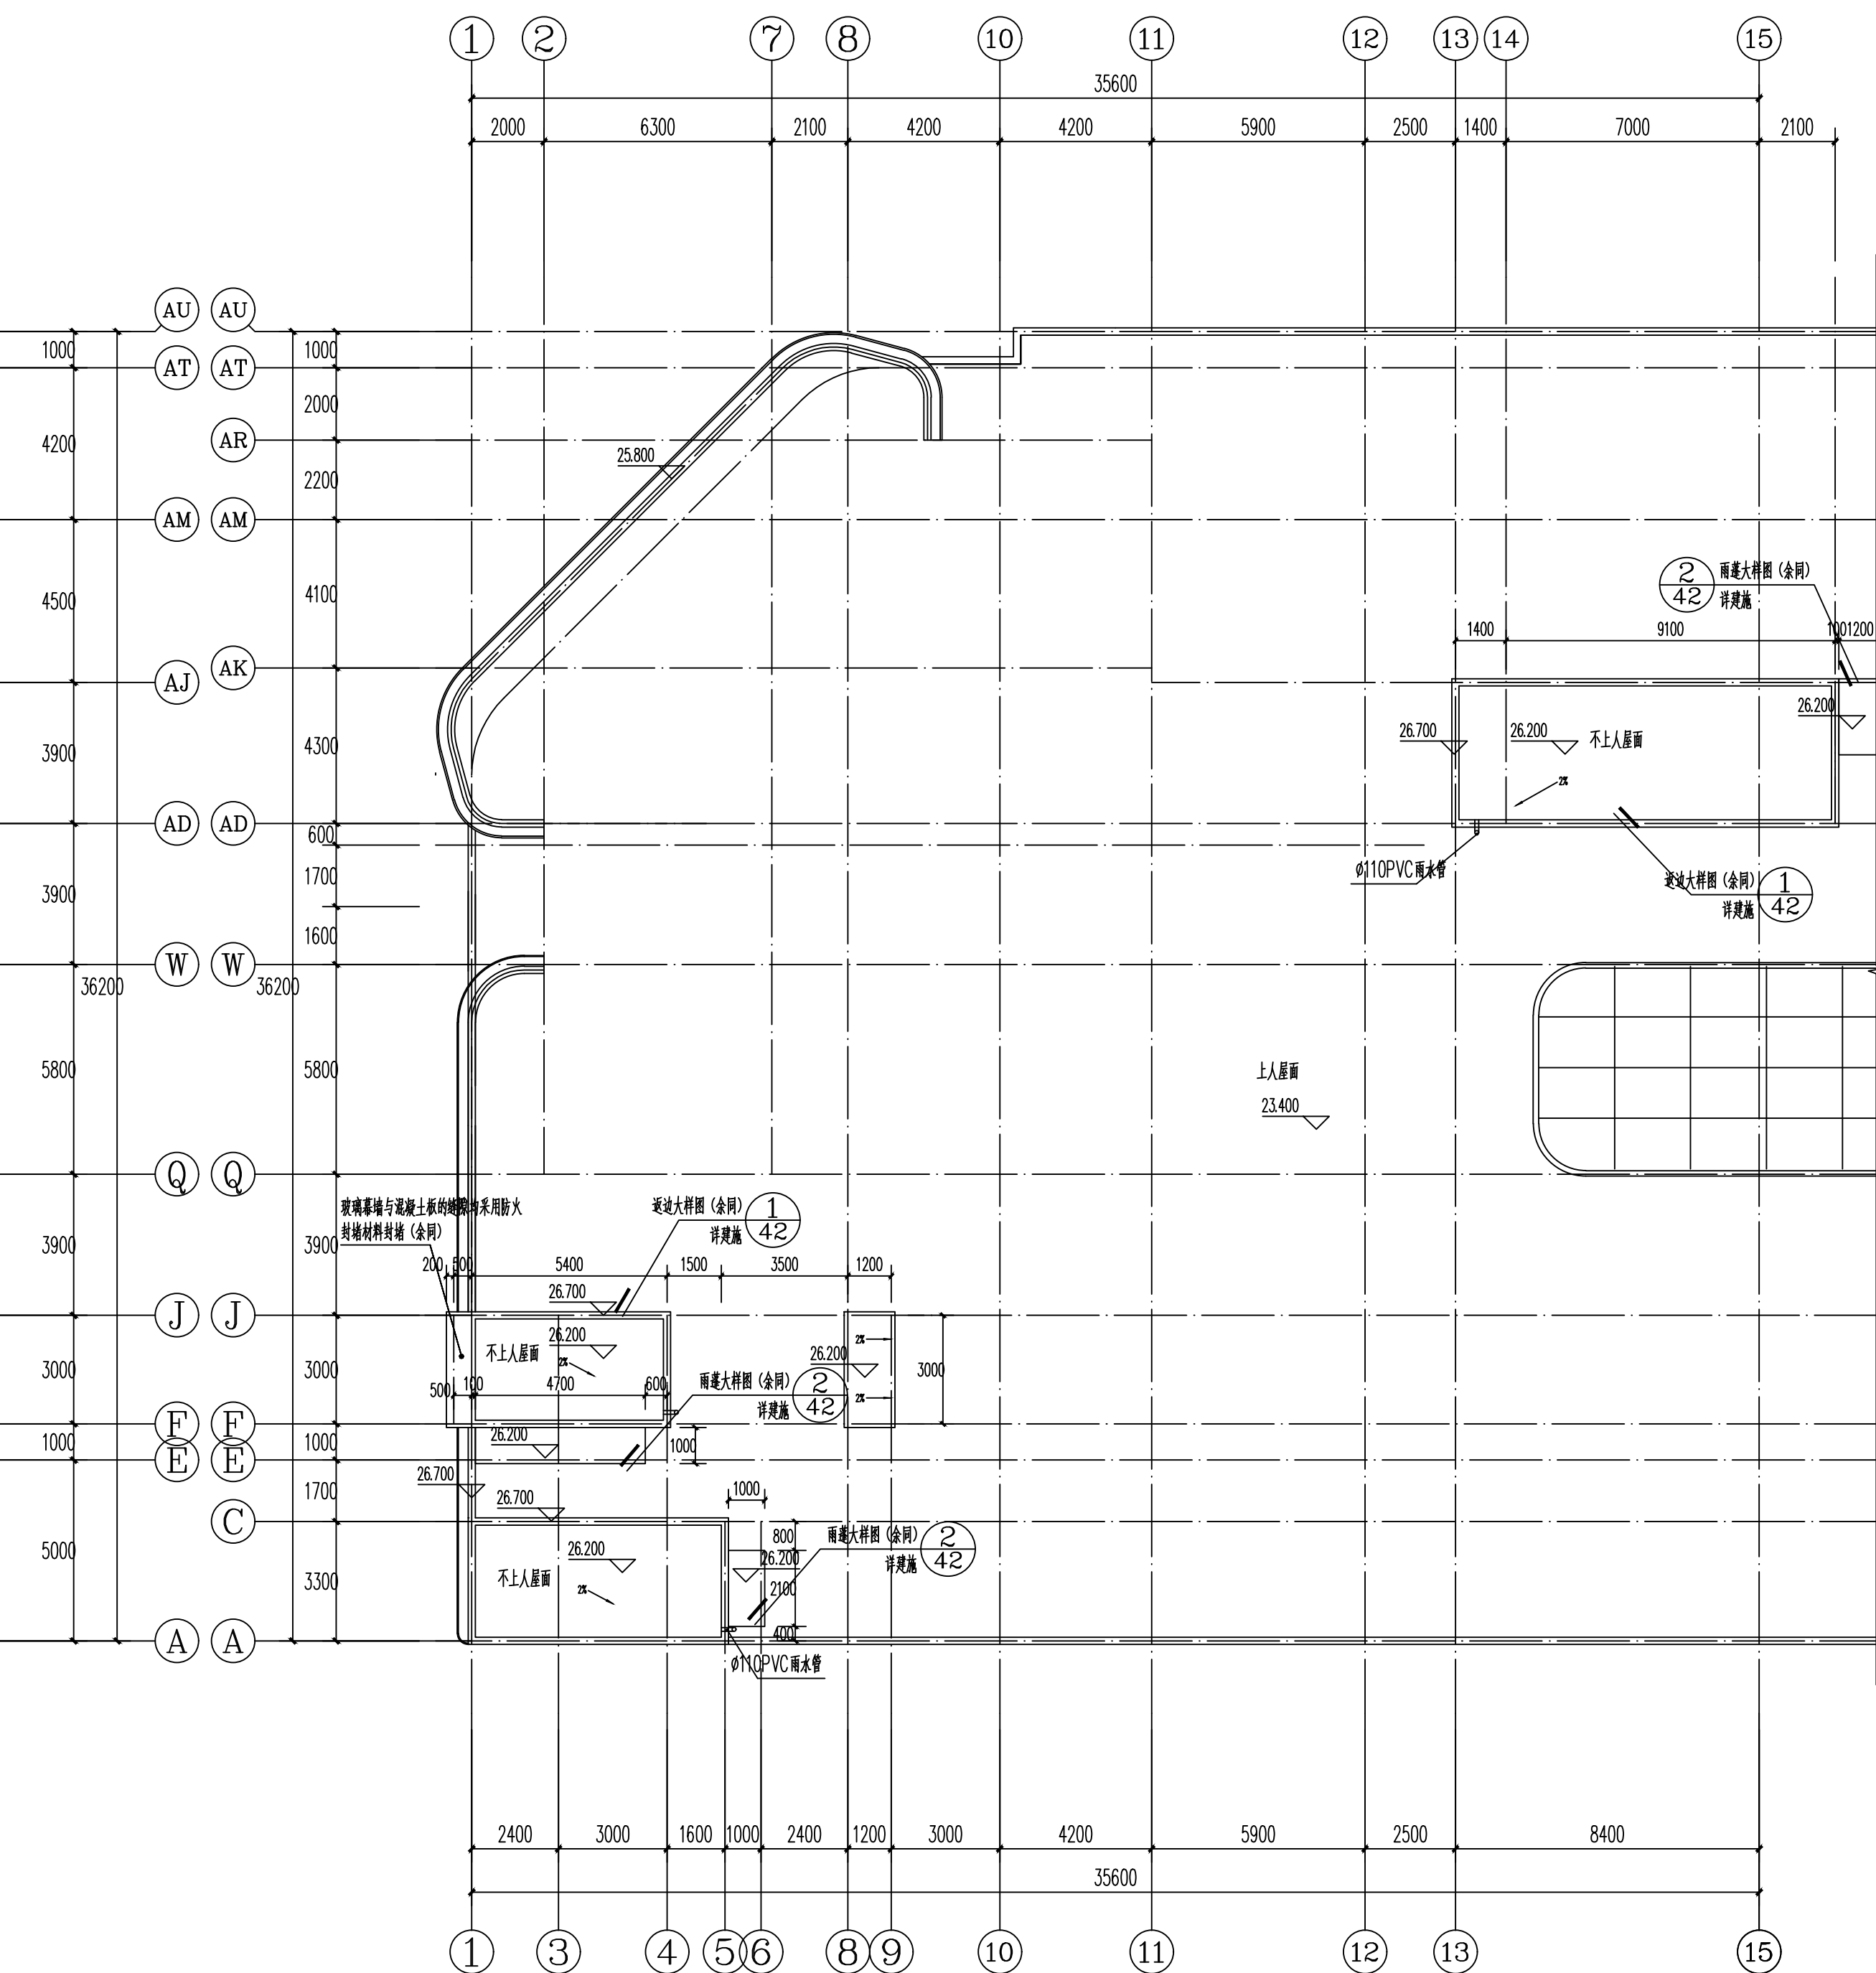

商业屋顶构件平面图 1:100