
 
 
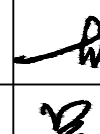
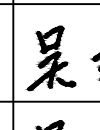
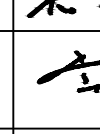
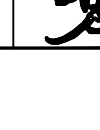
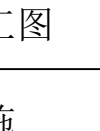


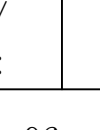

建设单位/CLIENT:				麻阳苗族自治县远桥房地产开发有限公司			
项目名称/PROJECT:				远程国际			
子项目名称/SUB-PROJECT:				远程国际			
区位图/REGIONAL LOCATION MAP :							
 广东建筑艺术设计院有限公司 GUANGDONG ARCHITECTURAL ARTISTIC DESIGN INSTITUTE CO.,LTD ■ 建筑方案设计: 李坚 ■ 方案深化设计: 乙级 ■ 城乡规划设计: 乙级 ■ 市政设计: 乙级							
图纸名称/TITLE:							
LT1、LT2楼梯间大样图一							
项目名称/PROJECT:							
远程国际							
设计 DESIGNED		古新辉					
校对 CHECKED		吴新红					
专业负责人 CHIEF		吴志刚					
项目负责人 PROJECT CHIEF		吴志刚					
审核 IDENTIFIED		黄履优					
审定 APPROVED		李 坚					
业务号/JOB NO.							
设计阶段/STATUS: 施工图							
专业/DISCIPLINE: 建筑							
比例/ SCALE:		1: 100		规格/ SIZE:		A1	
出图日期/DATE: 2021.06							
图号/DRAWING NO. JS- 28							
版次 NO.		修改内容 DESCRIPTION				日期 DATE	
条形码/BARCODE:							
版权所有，不得复制、套用。 ALL RIGHTS RESERVED, DON'T COPIED, REPRODUCED.							