

建设单位/CLIENT:
麻阳苗族自治县远桥房地产开发有限公司

项目名称/PROJECT:
远程国际

子项目名称/SUB-PROJECT:
远程国际

区位图/REGIONAL LOCATION MAP :

建艺国际
广东建筑艺术设计院有限公司
GUANGDONG ARCHITECTURAL ARTISTIC DESIGN INSTITUTE CO.,LTD

■ 建筑方案设计: 甲级

■ 风景园林设计: 乙级

■ 城乡规划设计: 乙级

■ 市政设计: 乙级

图纸名称/TITLE:
①~⑩轴立面图
⑩~①轴立面图

项目名称/PROJECT:
远程国际

设计 DESIGNED	古新辉	
校对 CHECKED	吴新红	
专业负责人 CHIEF	吴志刚	
项目负责人 PROJECT CHIEF	吴志刚	
审核 IDENTIFIED	黄履优	
审定 APPROVED	李 坚	

业务号/JOB NO.

设计阶段/STATUS: 施工图

专业/DISCIPLINE: 建筑

比例/ SCALE:	1: 100	规格/ SIZE:	A1
---------------	--------	--------------	----


出图日期/DATE: 2021. 06

图号/DRAWING NO. JS- 23

版次 NO.	修改内容 DESCRIPTION	日期 DATE


条形码/BARCODE:

版权所有，不得复制、套用。
ALL RIGHTS RESERVED, DON'T COPIED, REPRODUCED.

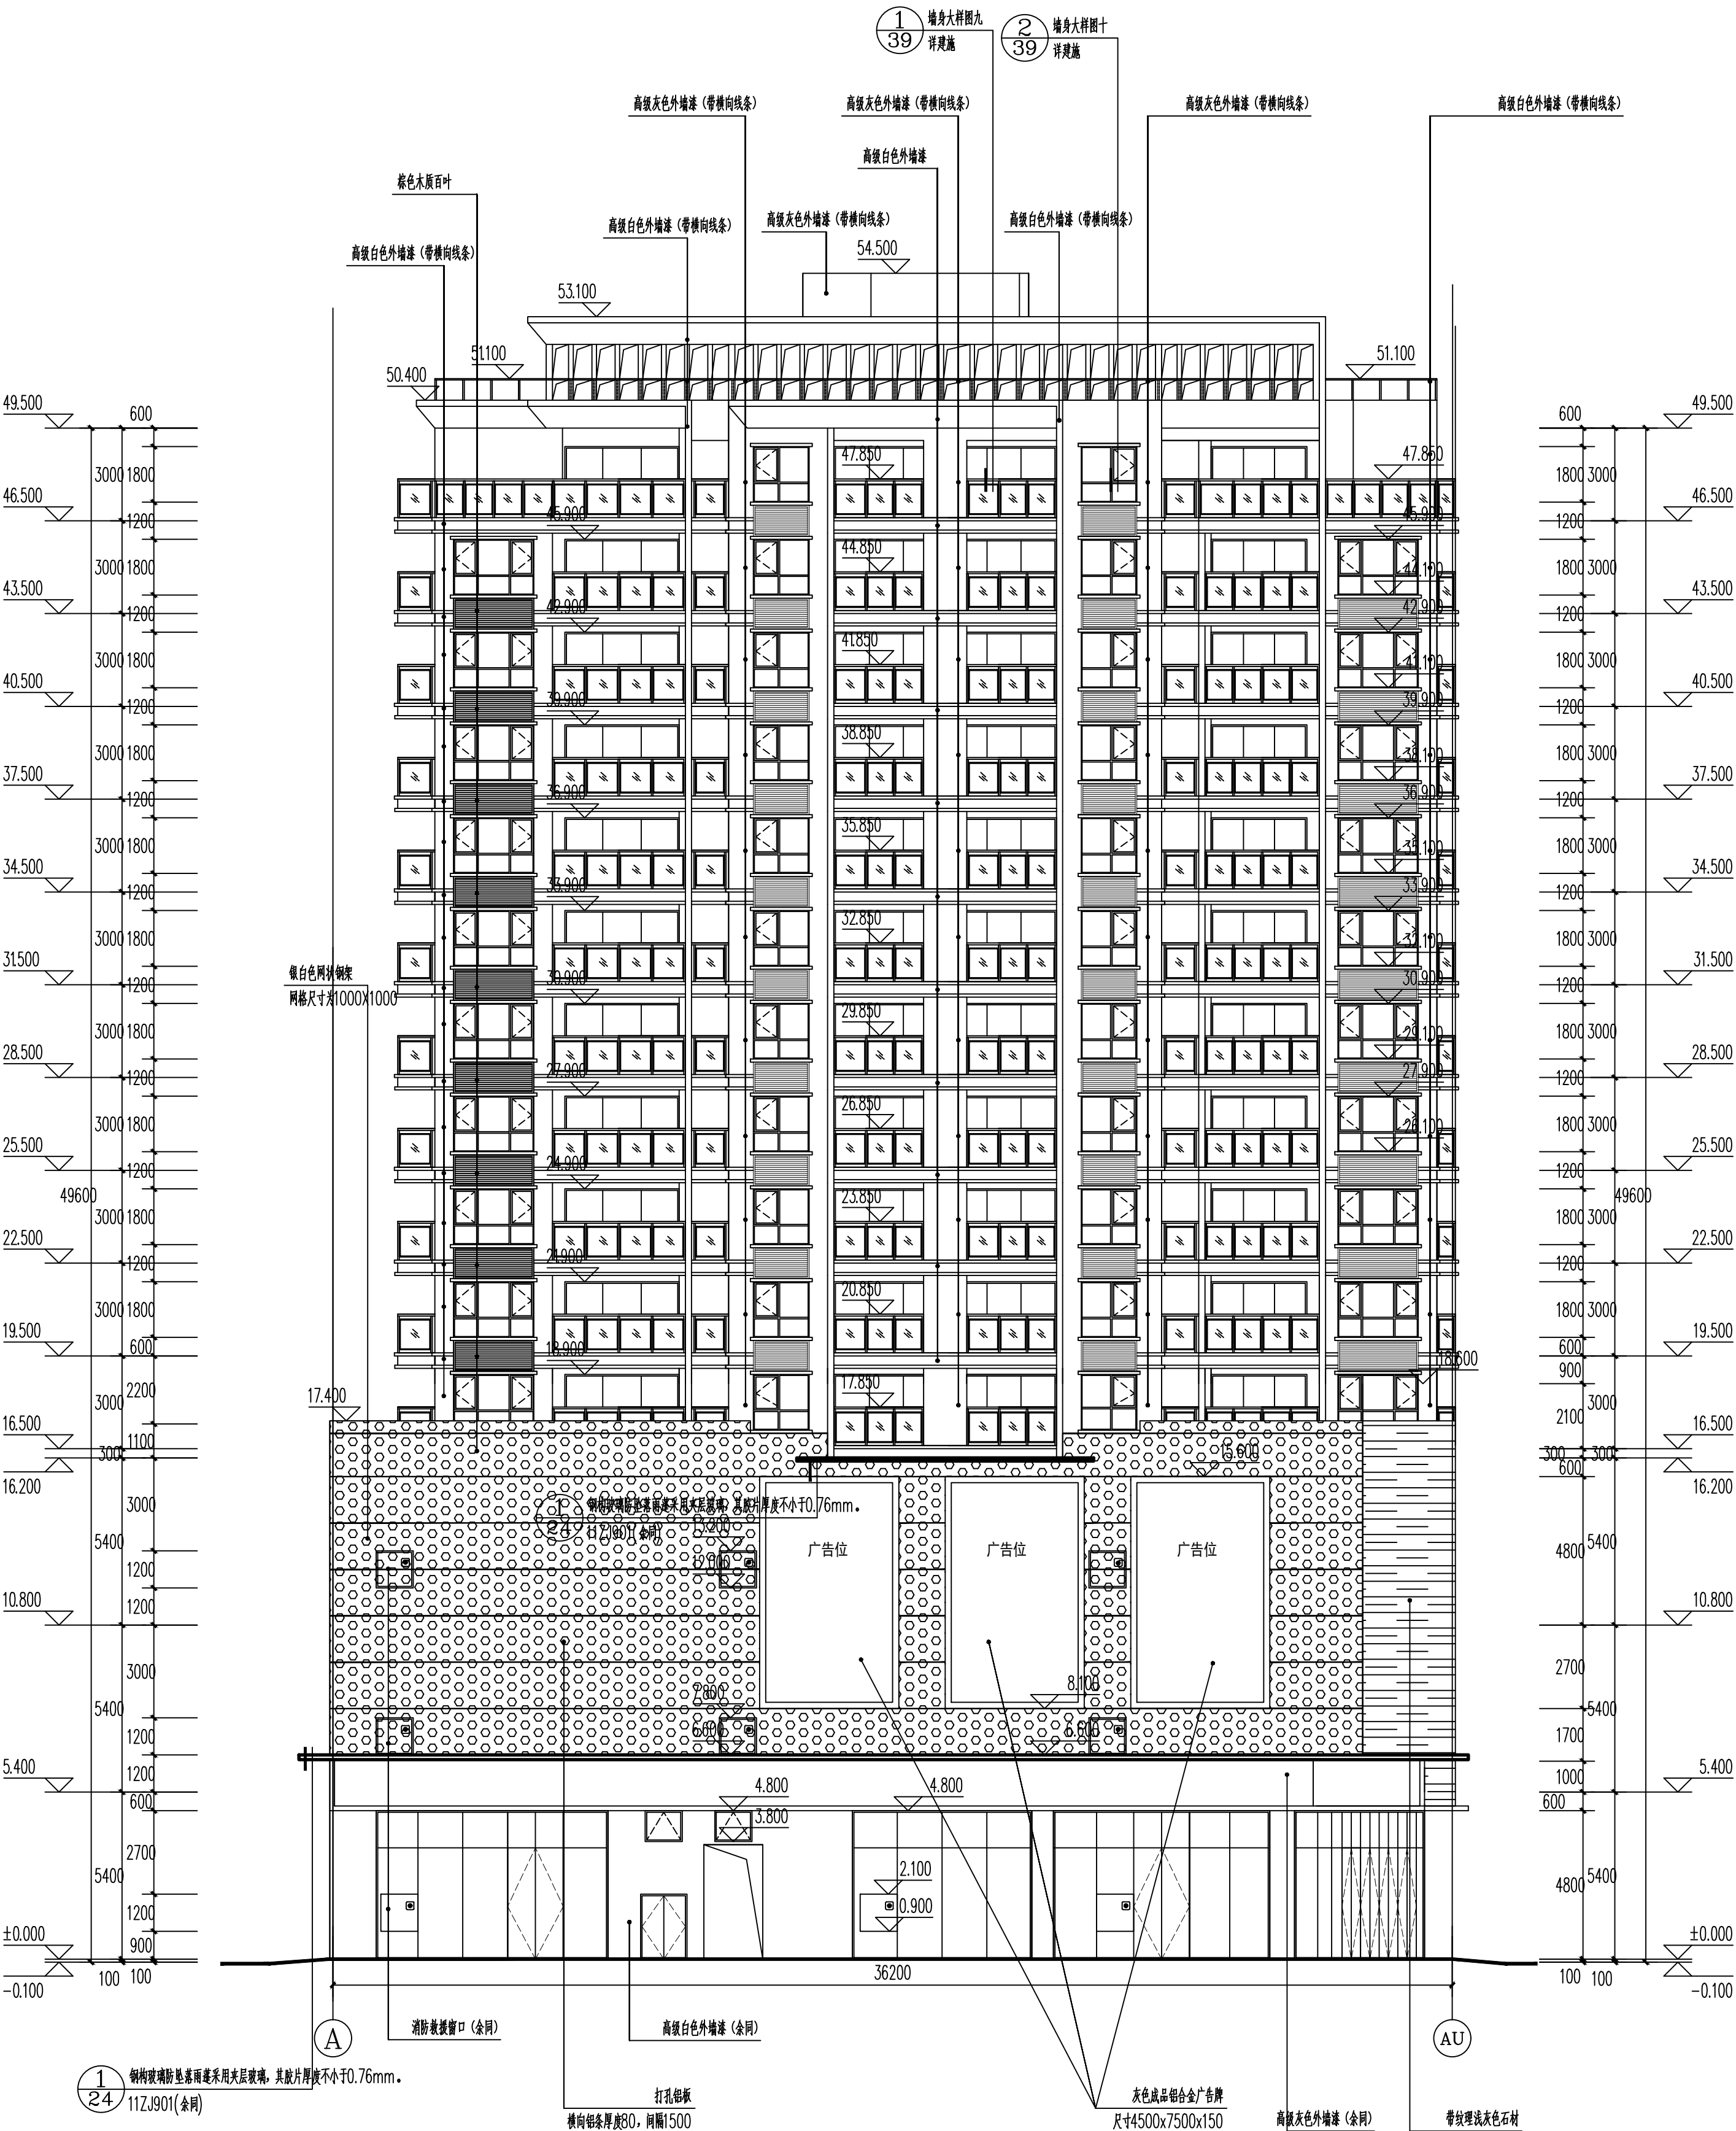

①~⑩轴立面图 1:150

注: 1、消防疏散窗口 (不小于1.0mX1.0m, 窗台宽不小于1.2m, 玻璃采用钢化玻璃)

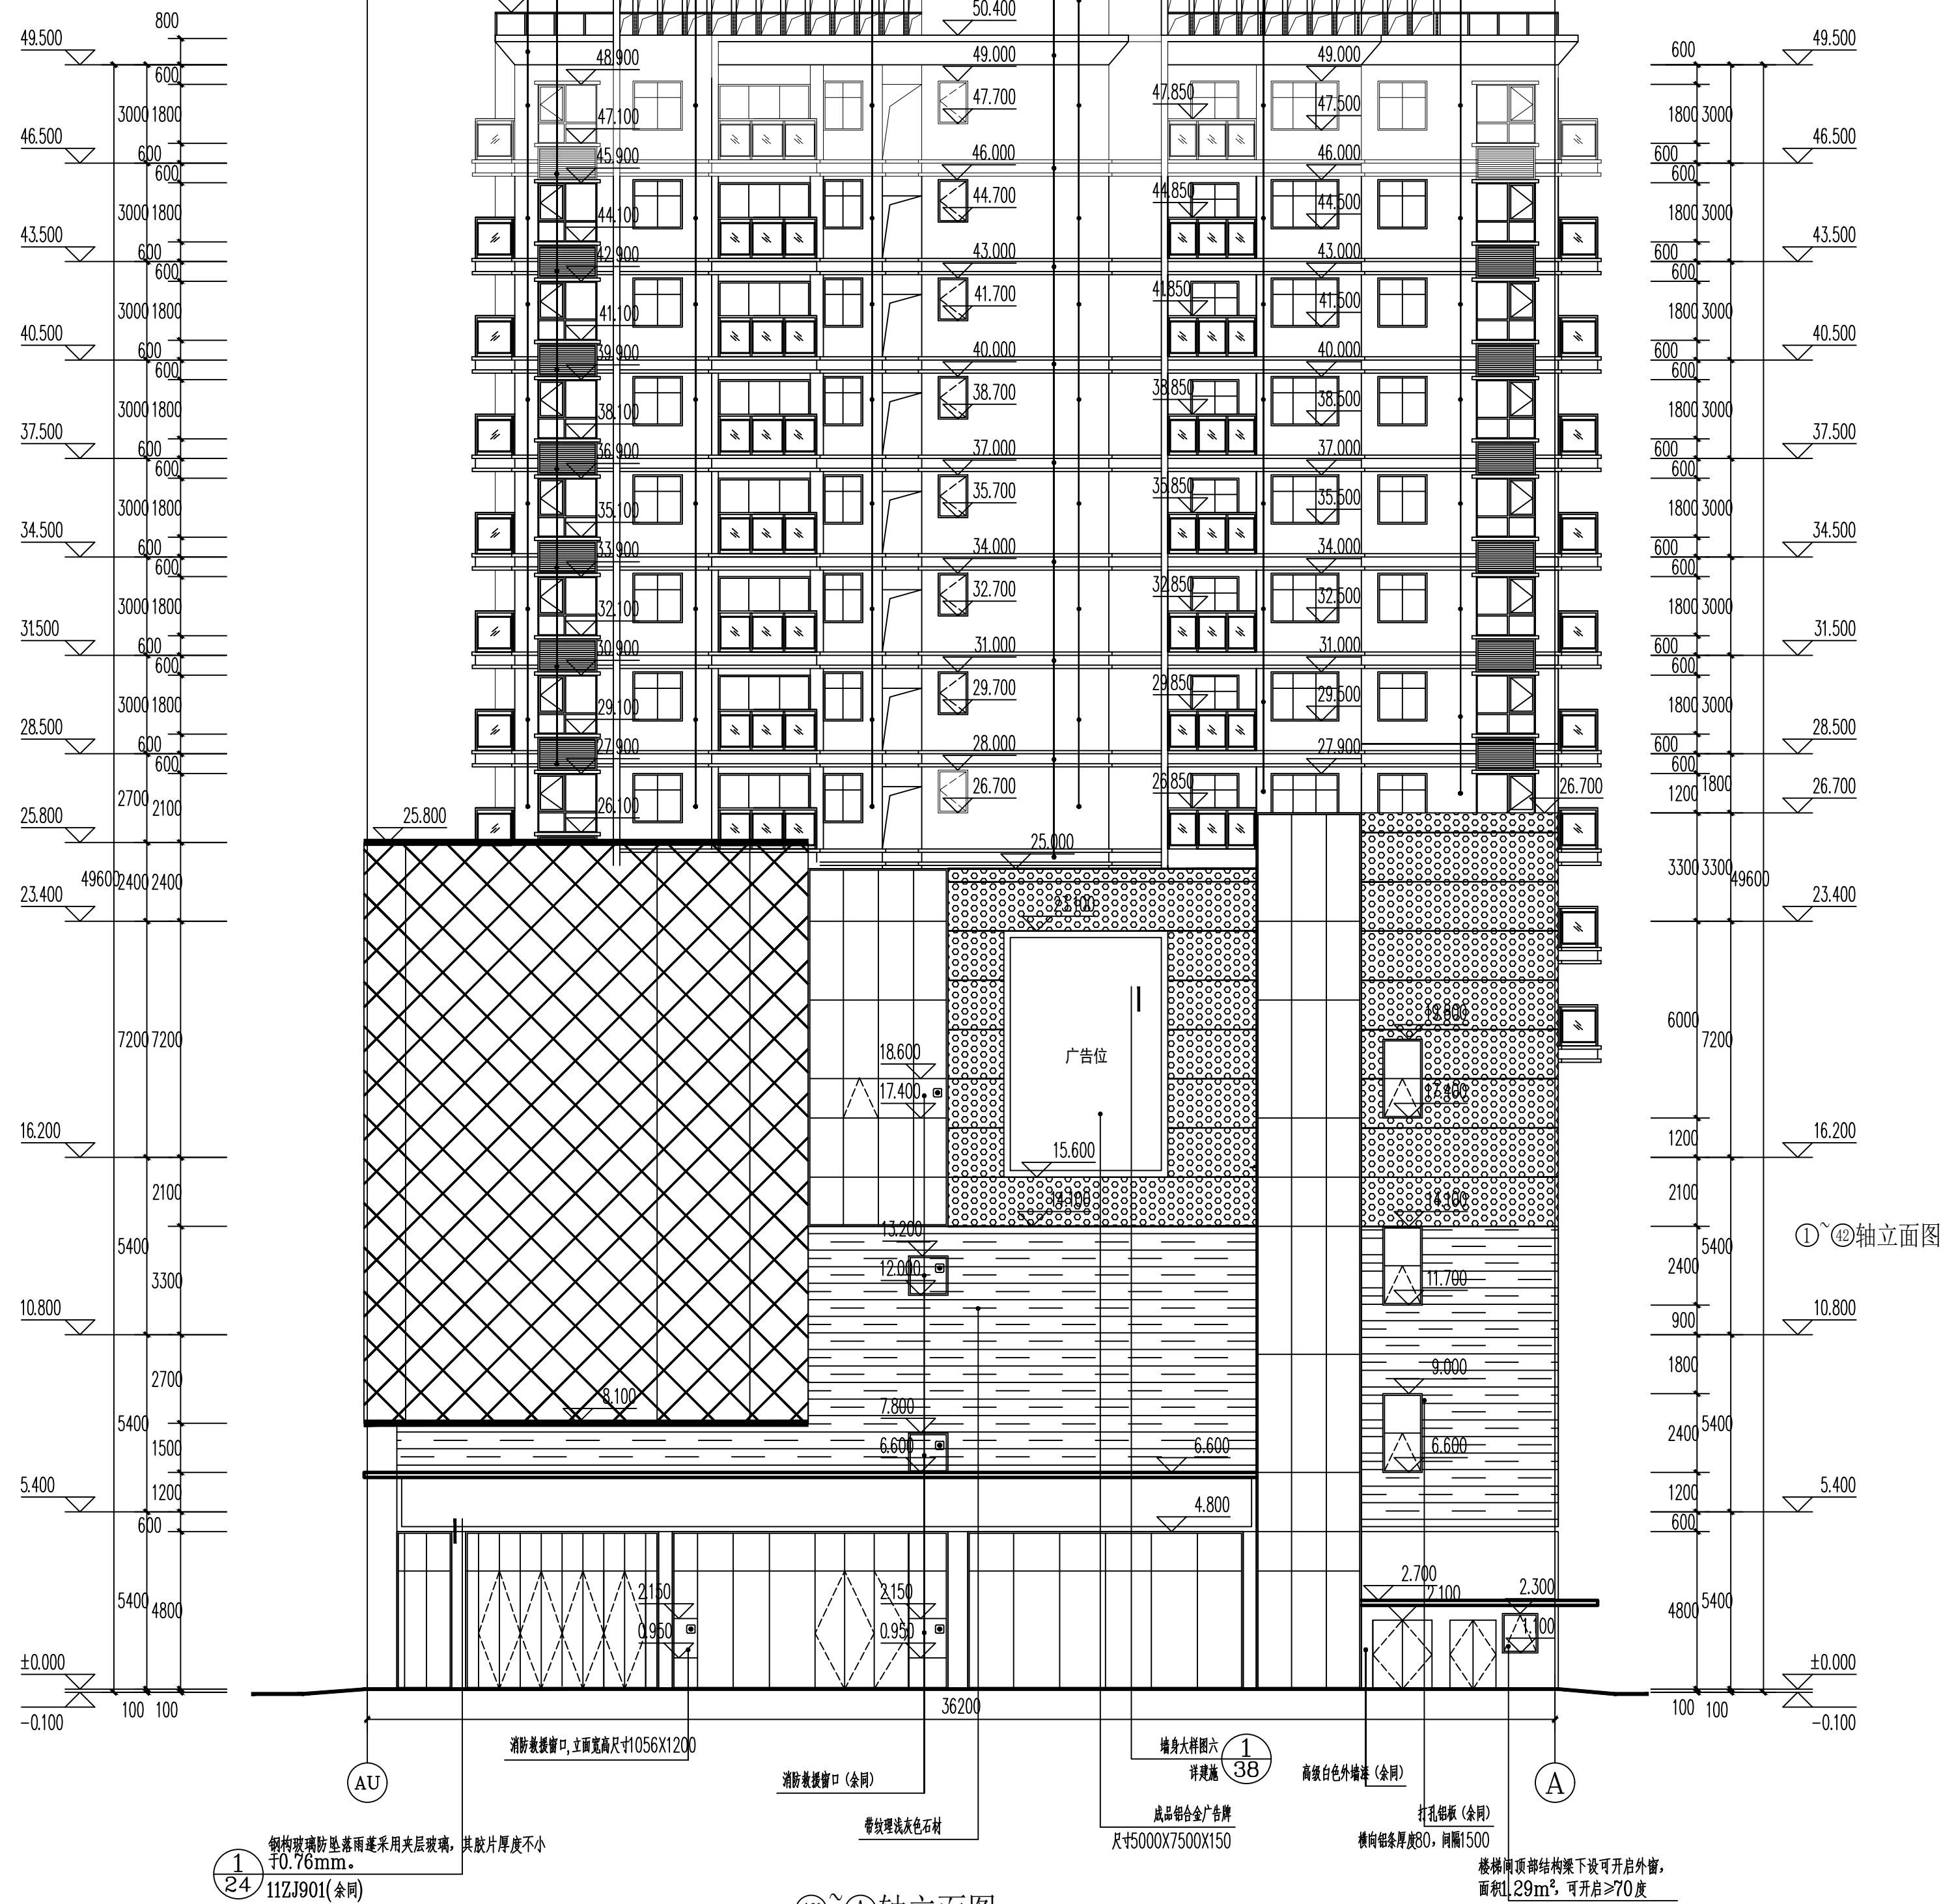

⑩~①轴立面图 1:150

注: 1、消防疏散窗口 (不小于1.0mX1.0m, 窗台宽不小于1.2m, 玻璃采用钢化玻璃)