

建设单位/CLIENT:
麻阳苗族自治县远桥房地产开发有限公司

项目名称/PROJECT:
远程国际

子项目名称/SUB-PROJECT:
远程国际

区位图/REGIONAL LOCATION MAP :

远桥国际

广东建筑艺术设计院有限公司

GUANGDONG ARCHITECTURAL ARTISTIC DESIGN INSTITUTE CO.,LTD

■ 建筑方案设计: 甲级 ■ 风景园林设计: 乙级

■ 城乡规划设计: 乙级 ■ 市政设计: 乙级

图纸名称/TITLE:
2-2剖面图、4-4剖面图
A-A断面图、B-B断面图

项目名称/PROJECT:
远程国际

设计 DESIGNED	古新辉	
校对 CHECKED	吴新红	
专业负责人 CHIEF	吴志刚	
项目负责人 PROJECT CHIEF	吴志刚	
审核 IDENTIFIED	黄履优	
审定 APPROVED	李 坚	

业务号/JOB NO.

设计阶段/STATUS: 施工图

专业/DISCIPLINE: 建筑

比例/
SCALE:

1: 100	规格/ SIZE:	A1
--------	--------------	----


出图日期/DATE: 2021. 06

图号/DRAWING NO. JS-26

版次 NO.	修改内容 DESCRIPTION	日期 DATE

条形码/BARCODE:

版权所有，不得复制、套用。
ALL RIGHTS RESERVED, DON'T COPIED, REPRODUCED.

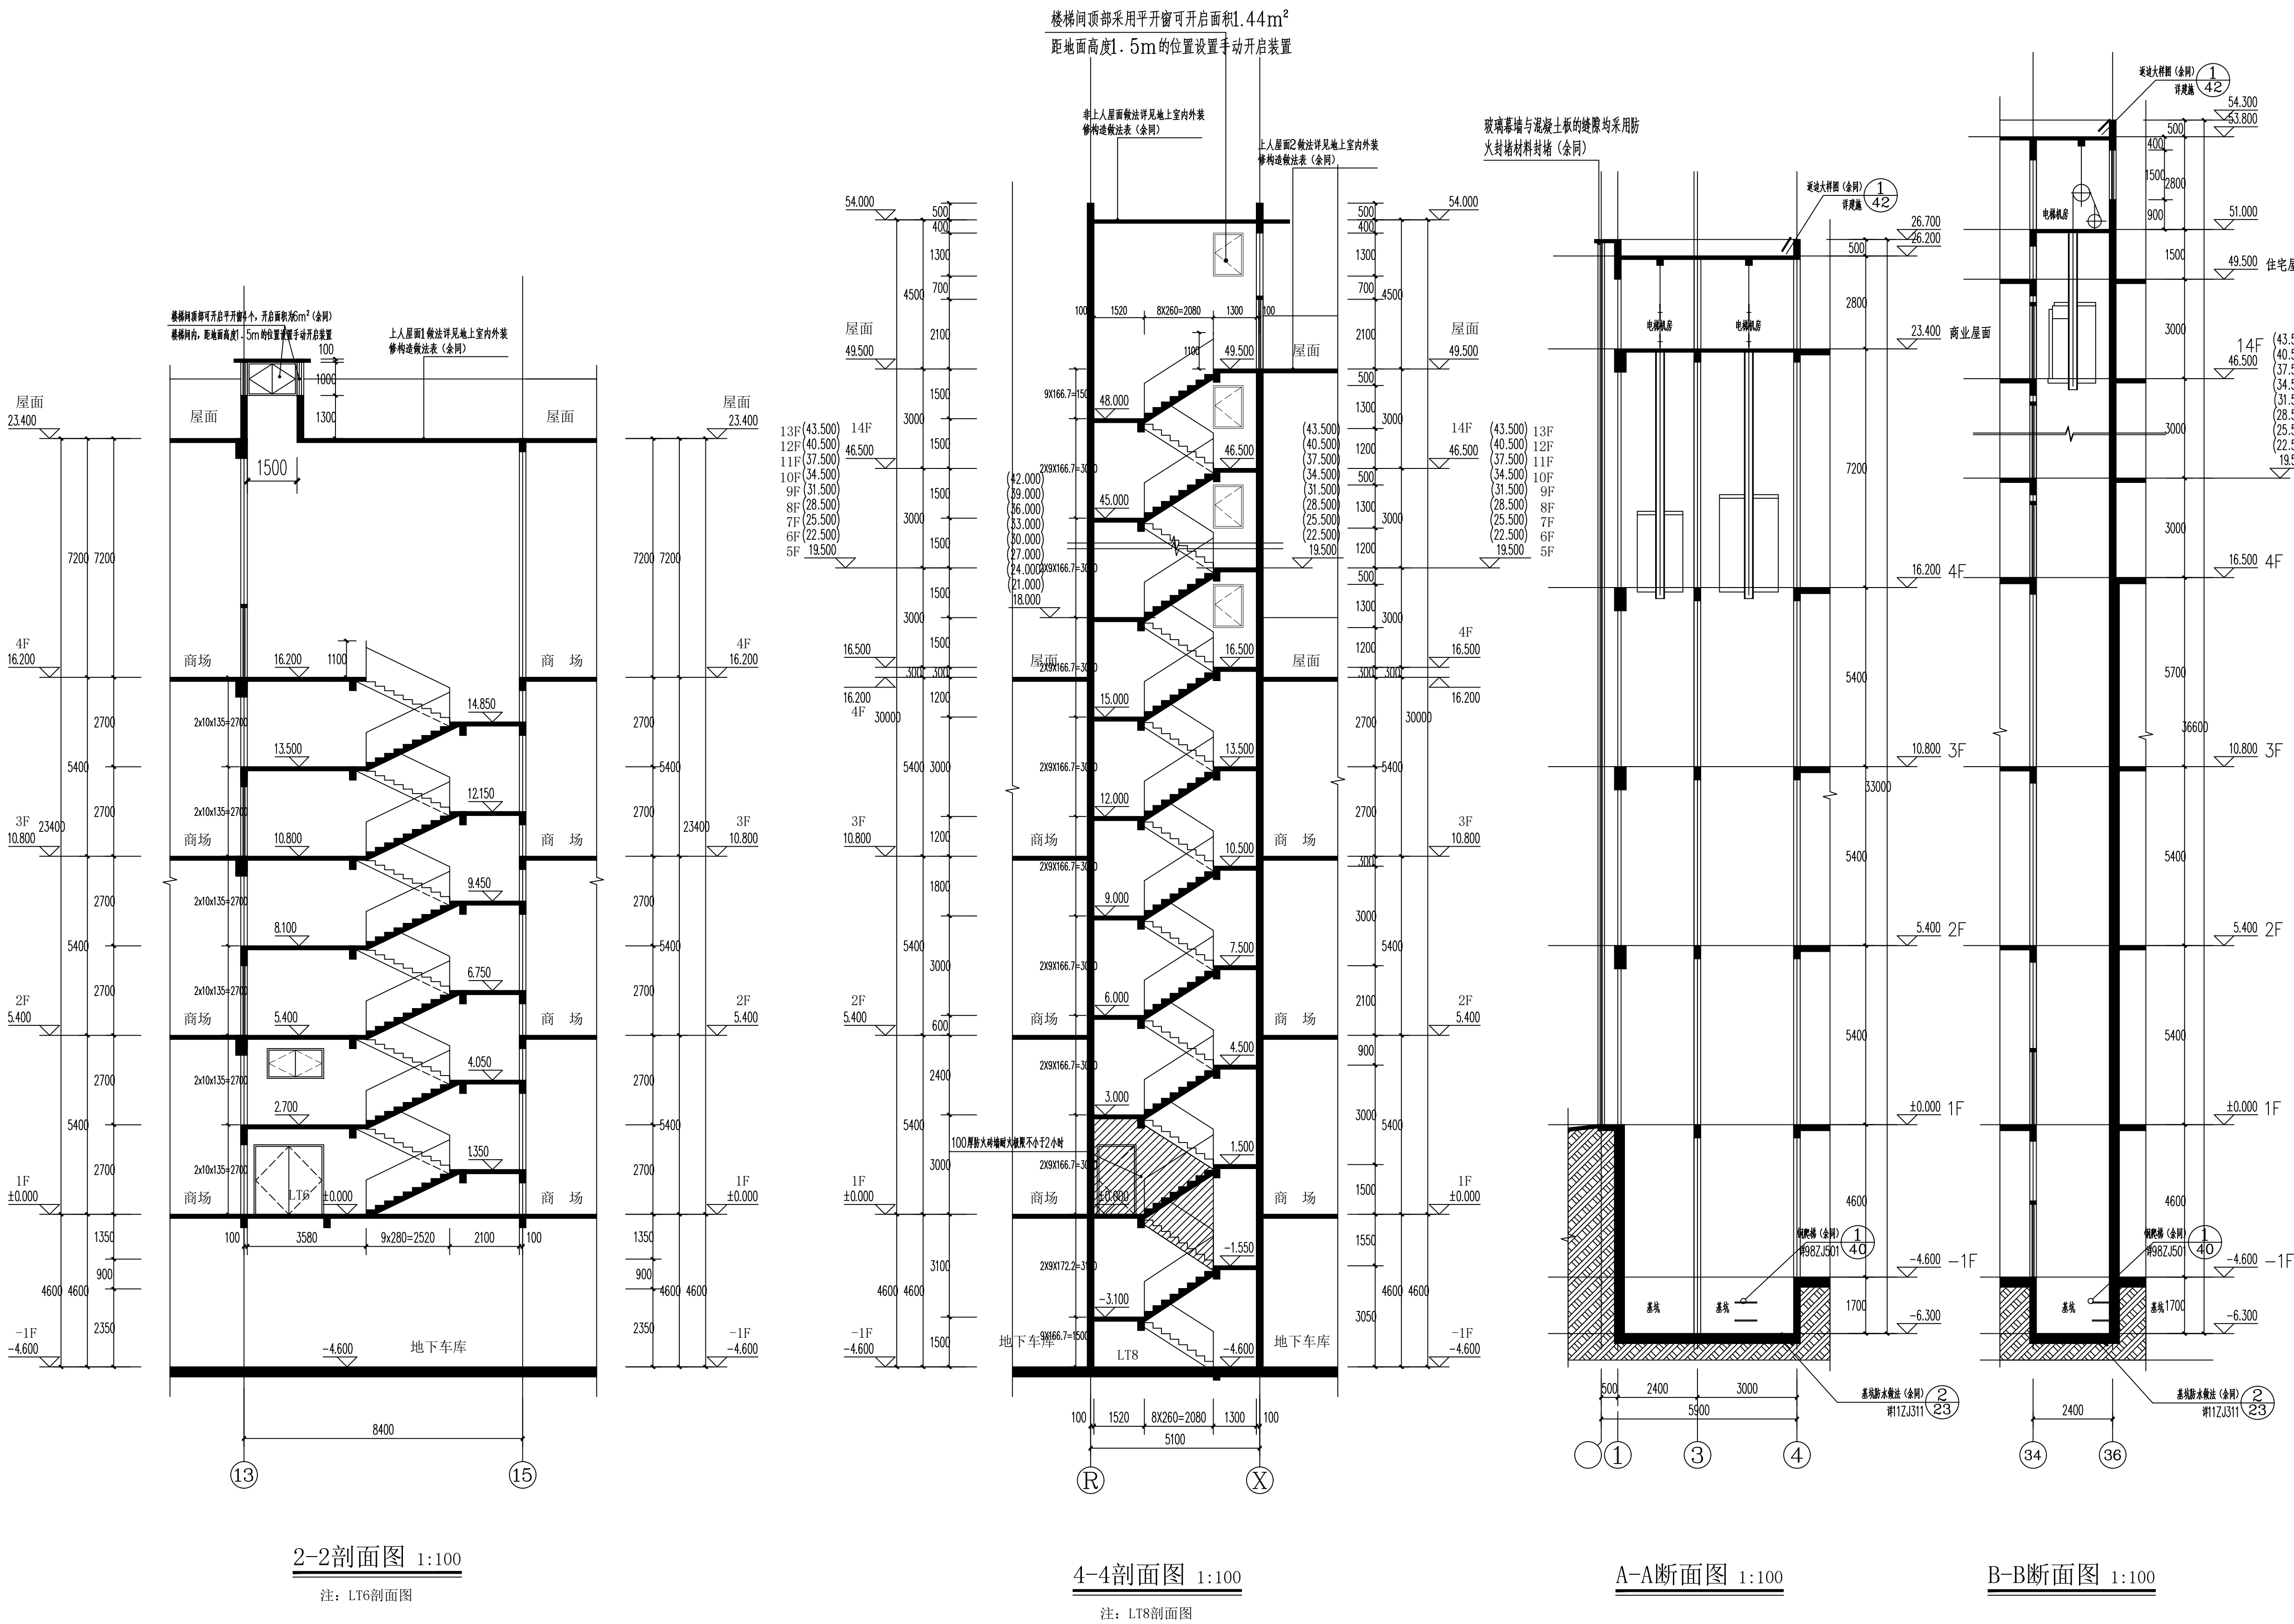

- 本工程楼梯踏步高、宽、步数及平台宽度等详楼梯大样。楼梯栏杆采用不锈钢栏杆900高, 详11ZJ401-13-W扶手详11ZJ401-37-16, (注: 当扶手水平长度大于0.5m时, 栏杆净高不低于1100)。
- 起步详11ZJ40138-6; 扶手与填充墙连接详11ZJ401-42-5, 防滑详05ZJ401-39-6
- 梯井大于110, 均做防坠网处理。