




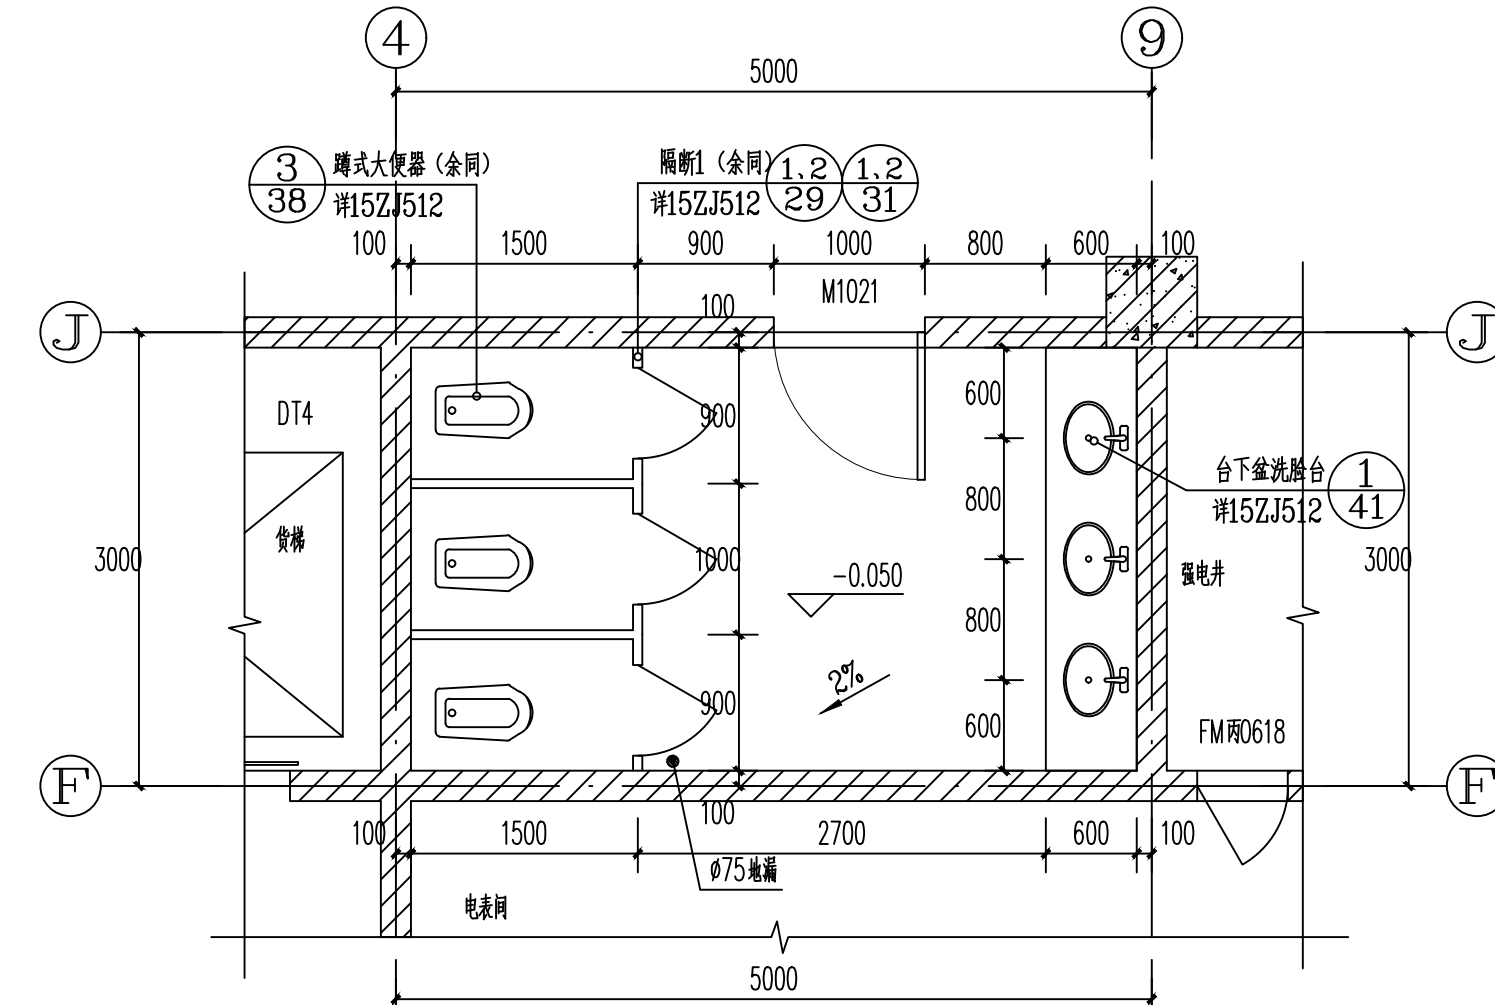


① 公卫一大样图 1:50

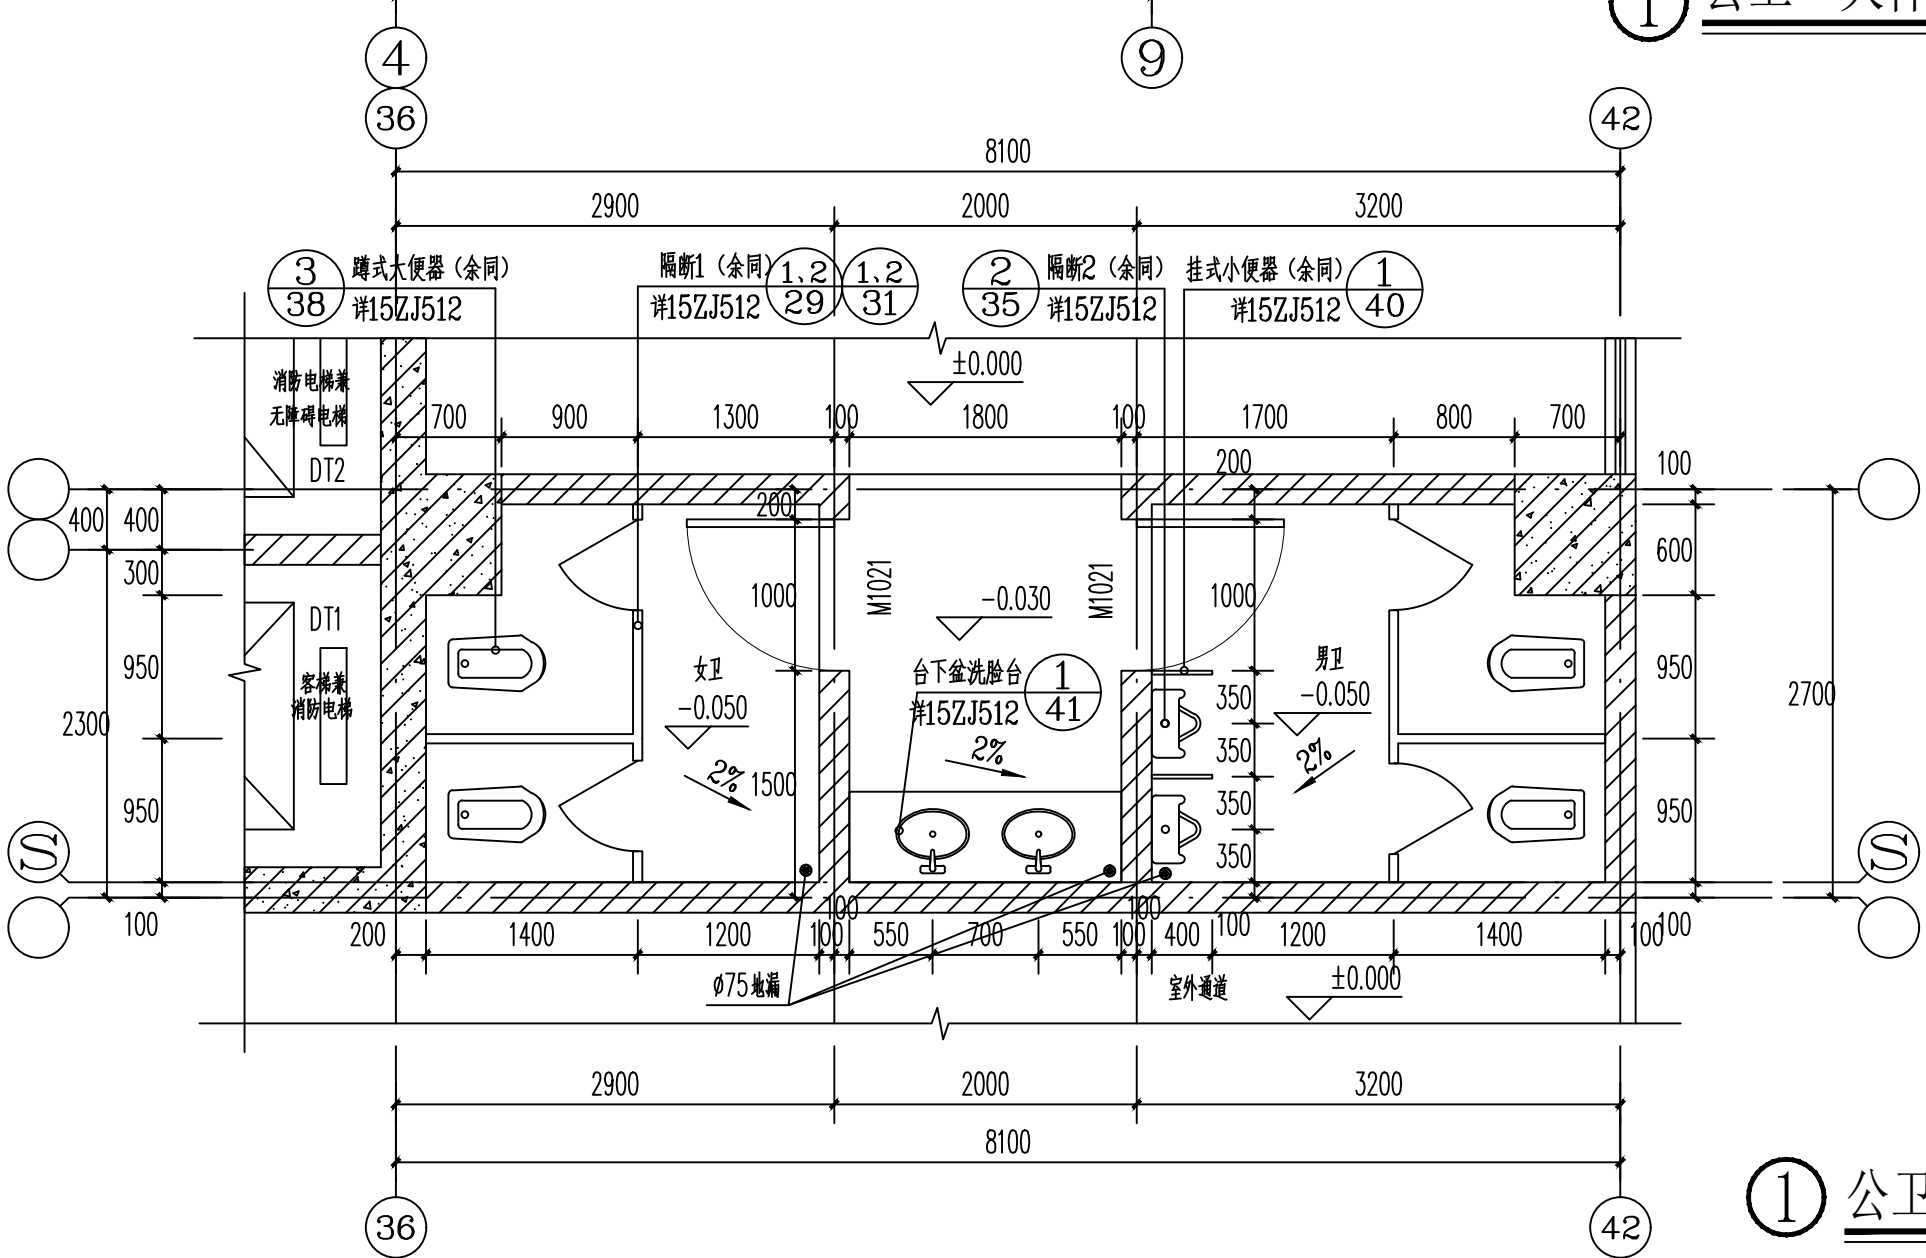


① 公卫二大样图 1:50

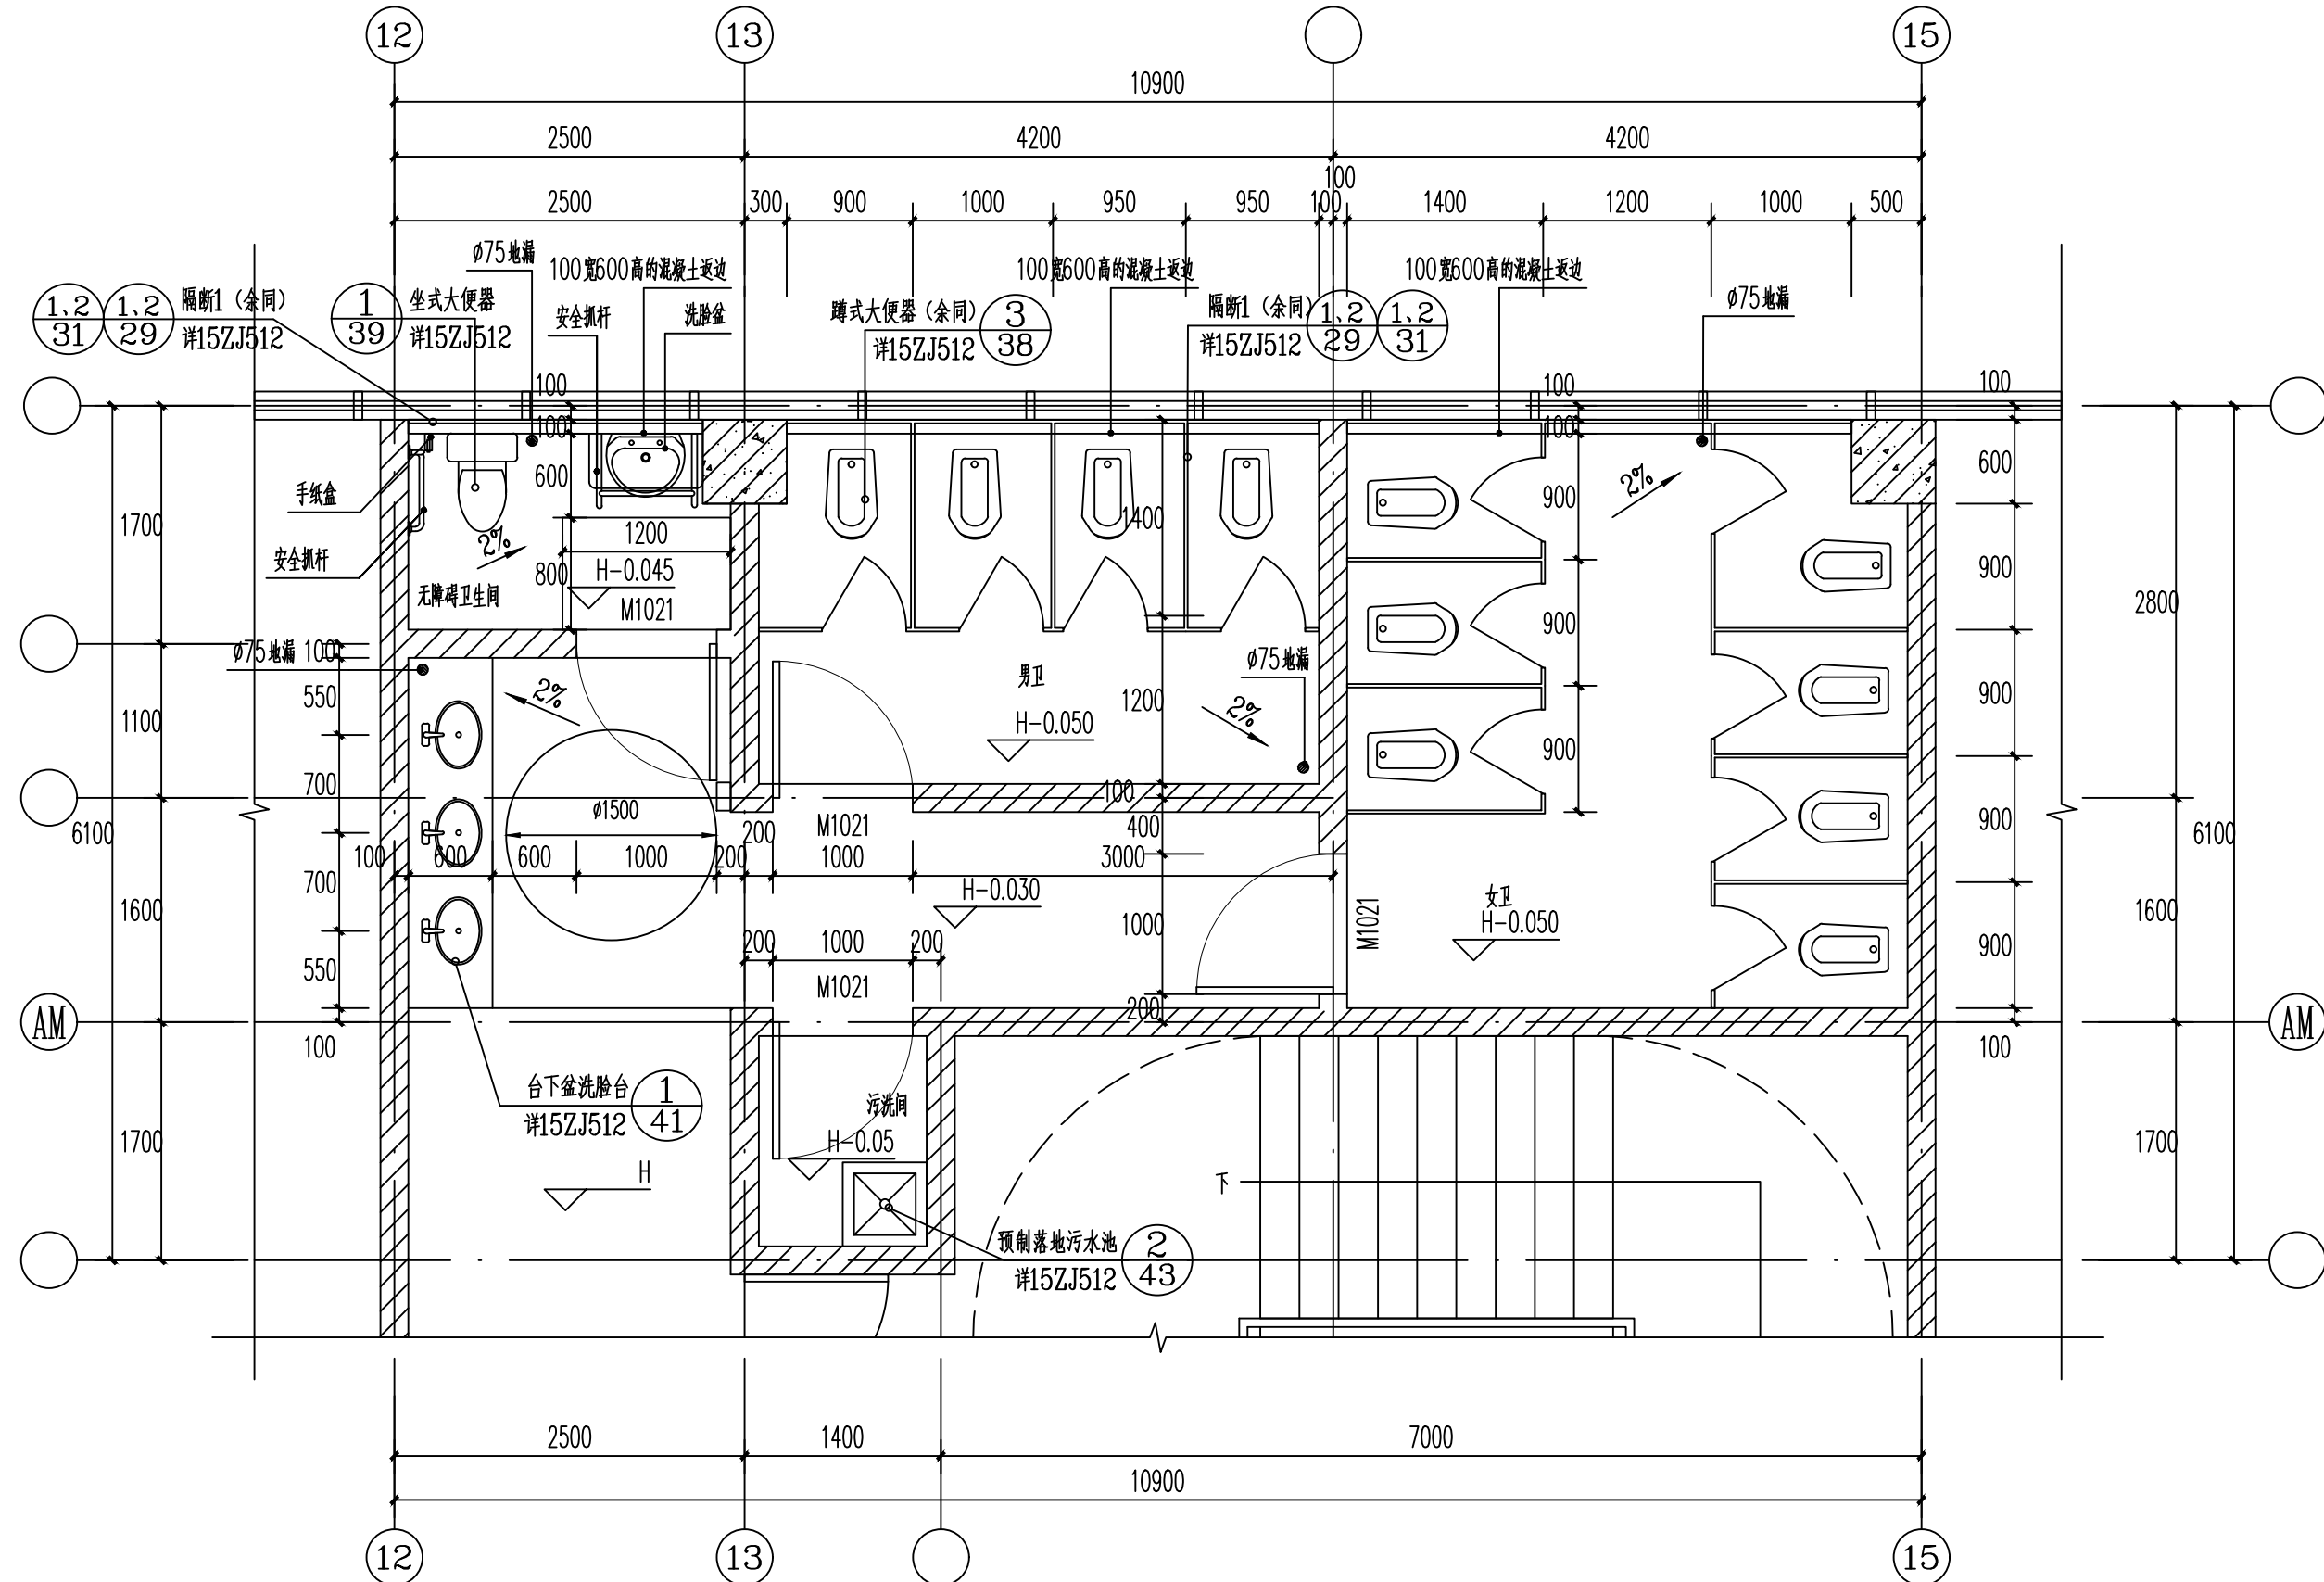


④ 公卫四大样图 1:50

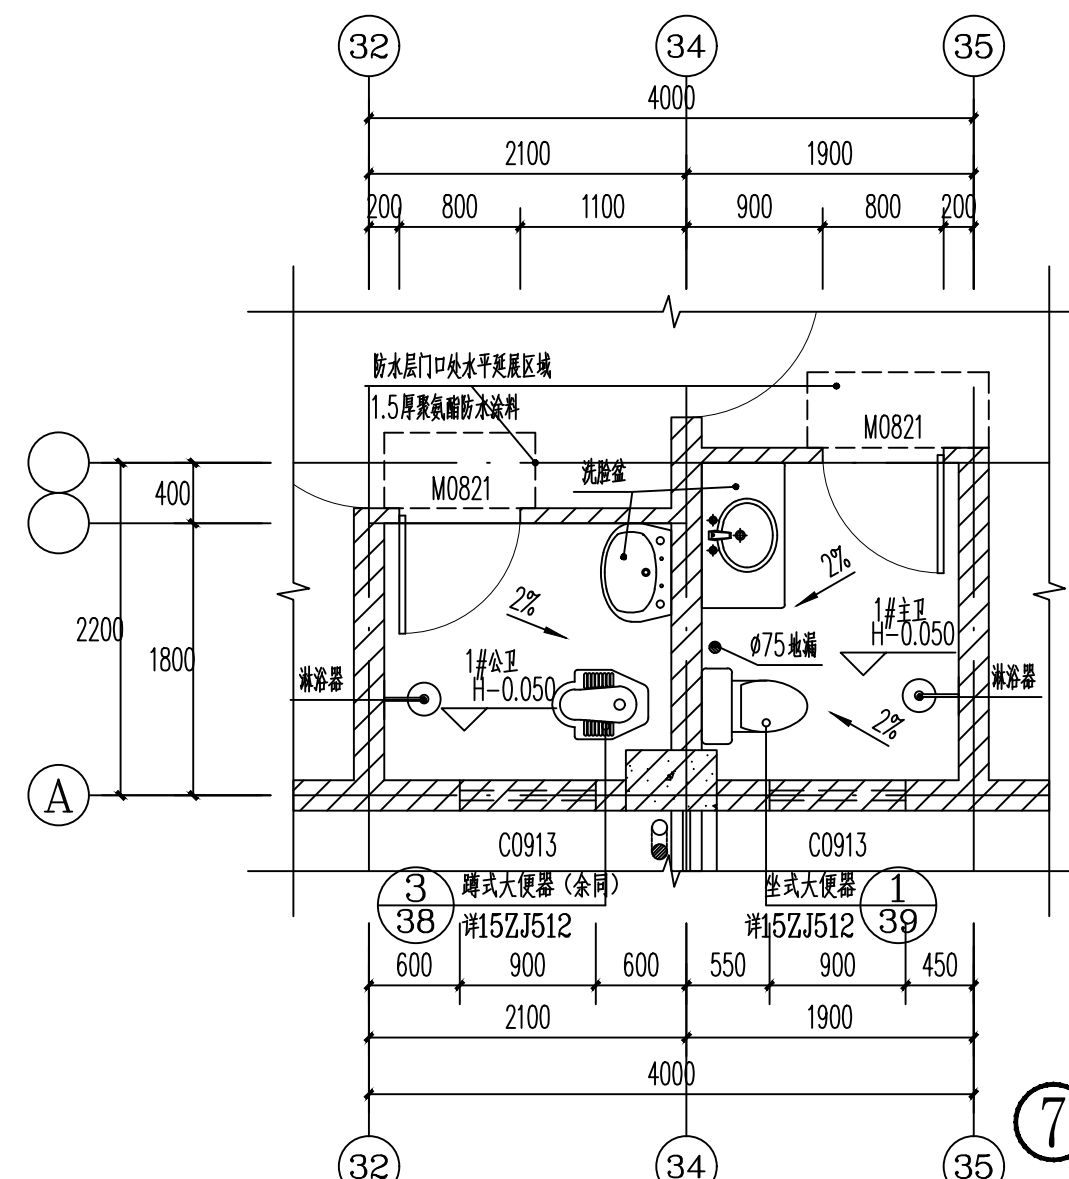


⑦ 1#公卫、1#主卫大样图 1:50

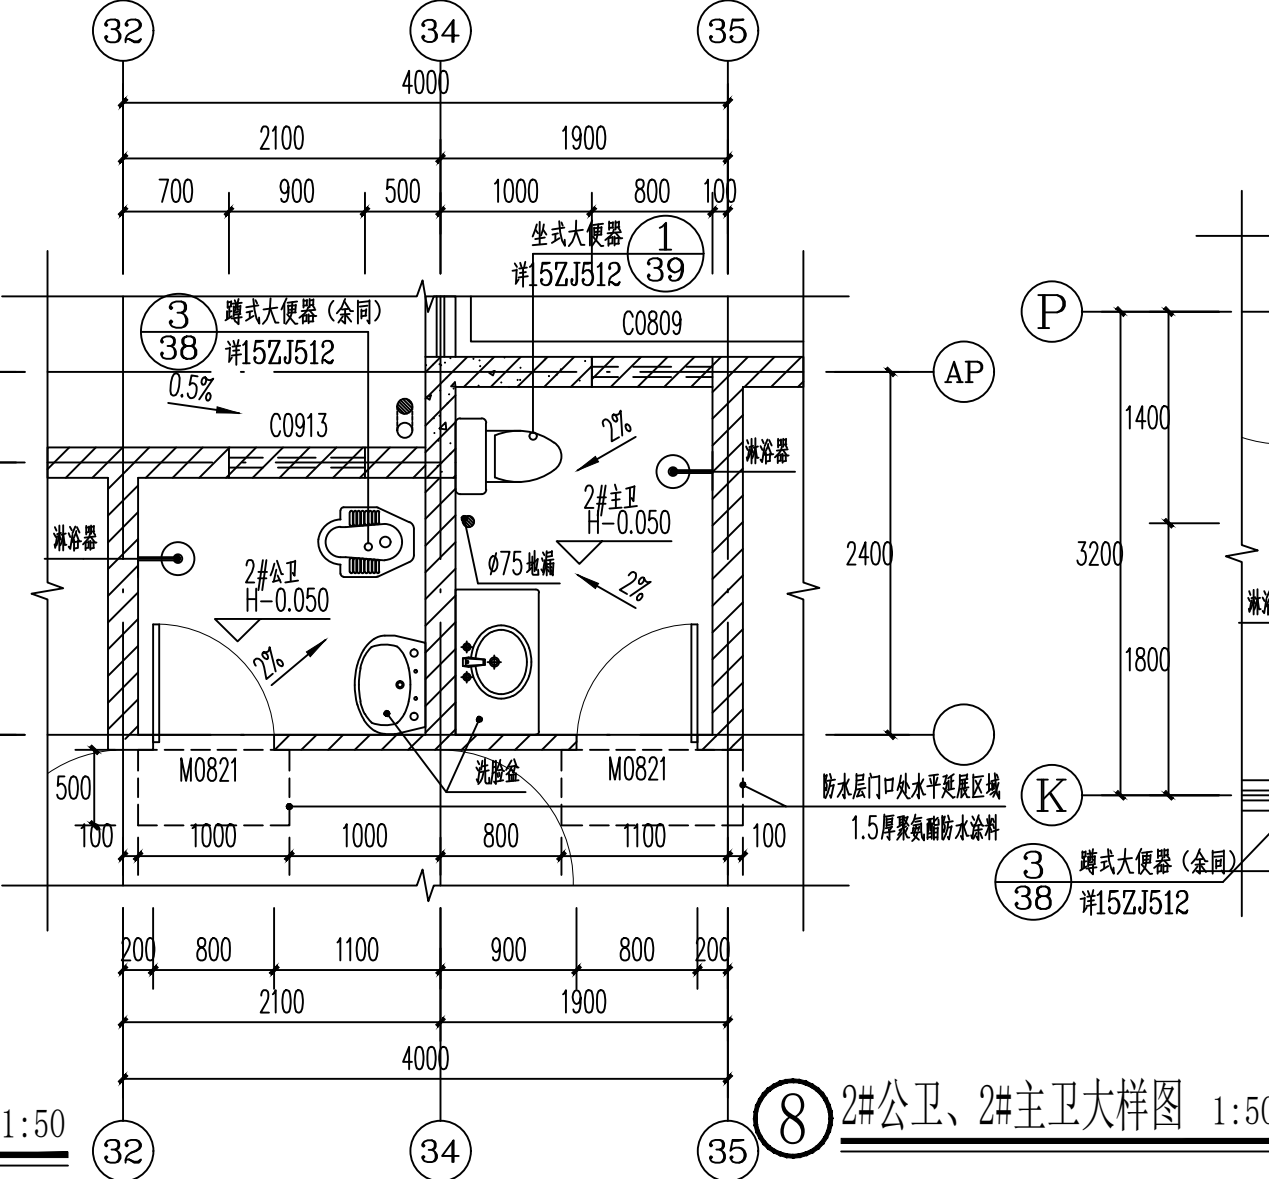


⑧ 2#公卫、2#主卫大样图 1:50

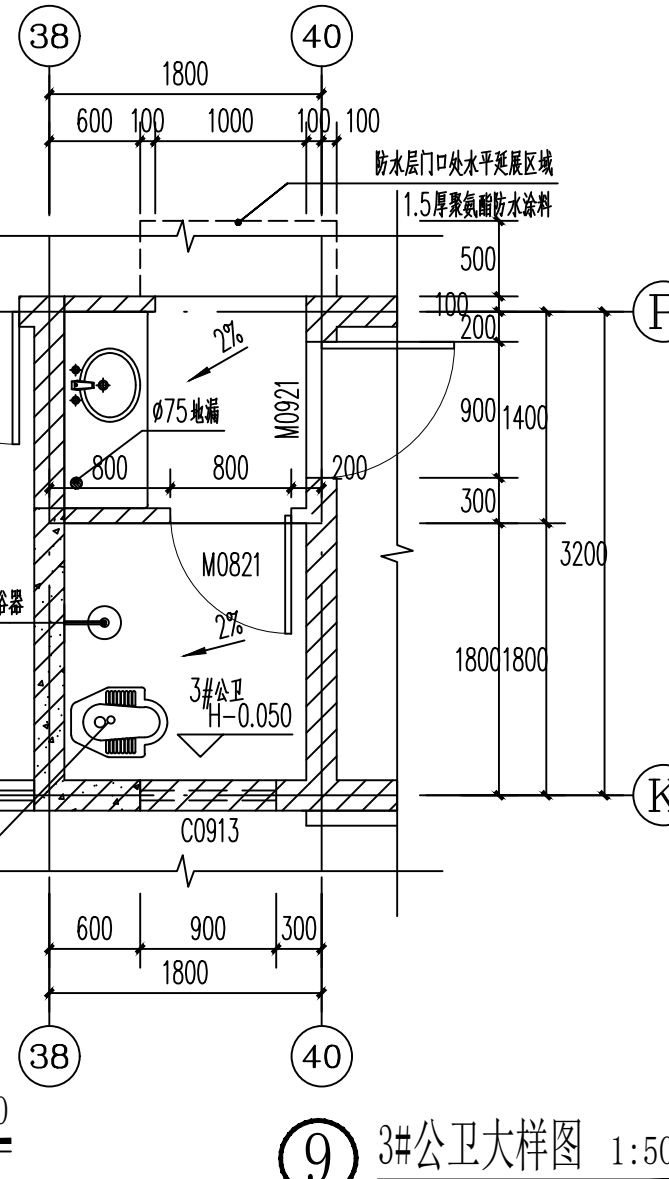


⑨ 3#公卫大样图 1:50

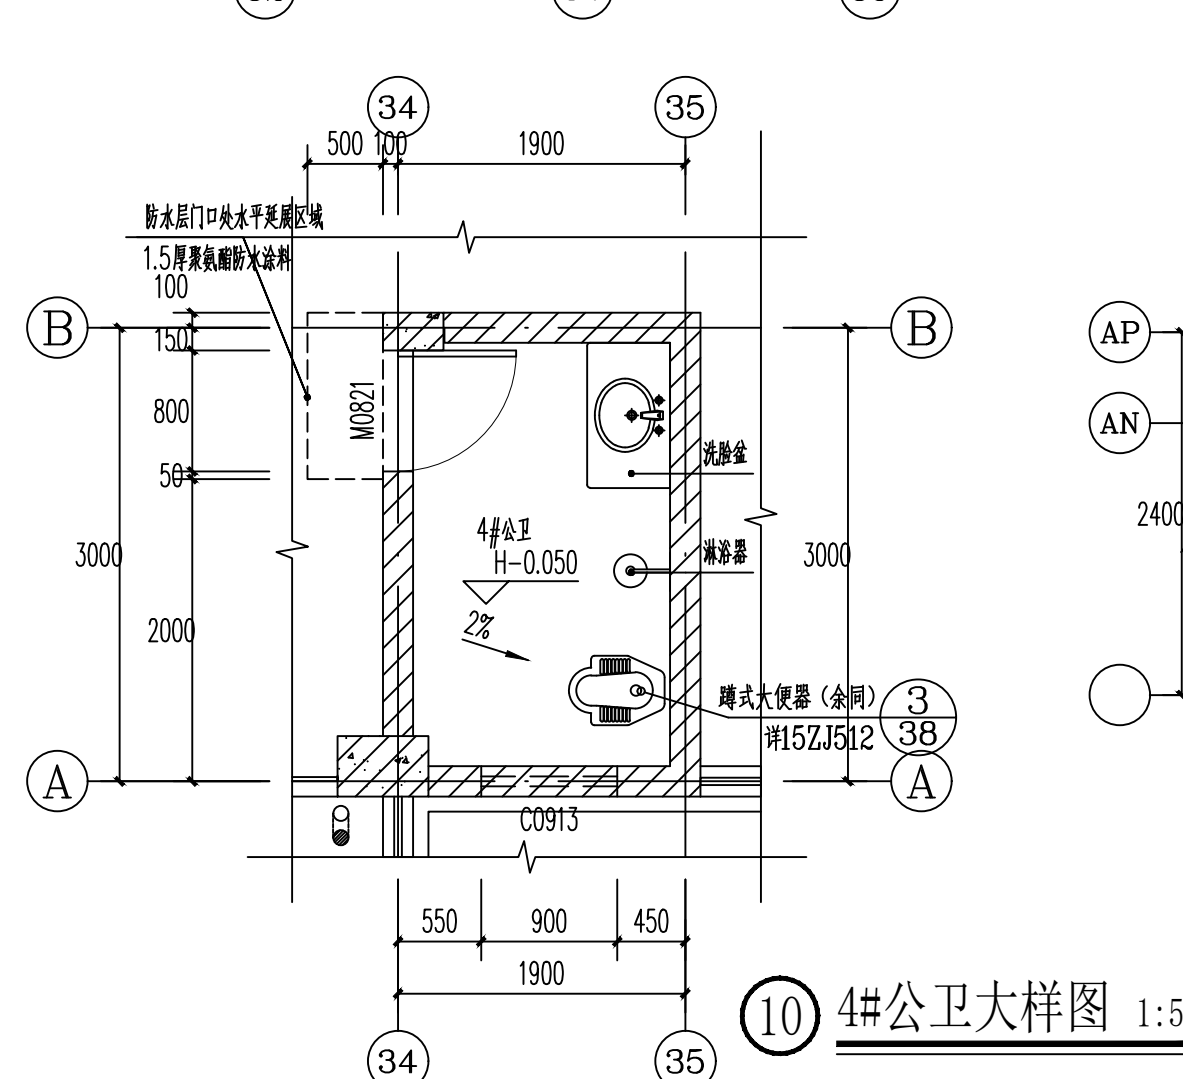


⑩ 4#公卫大样图 1:50

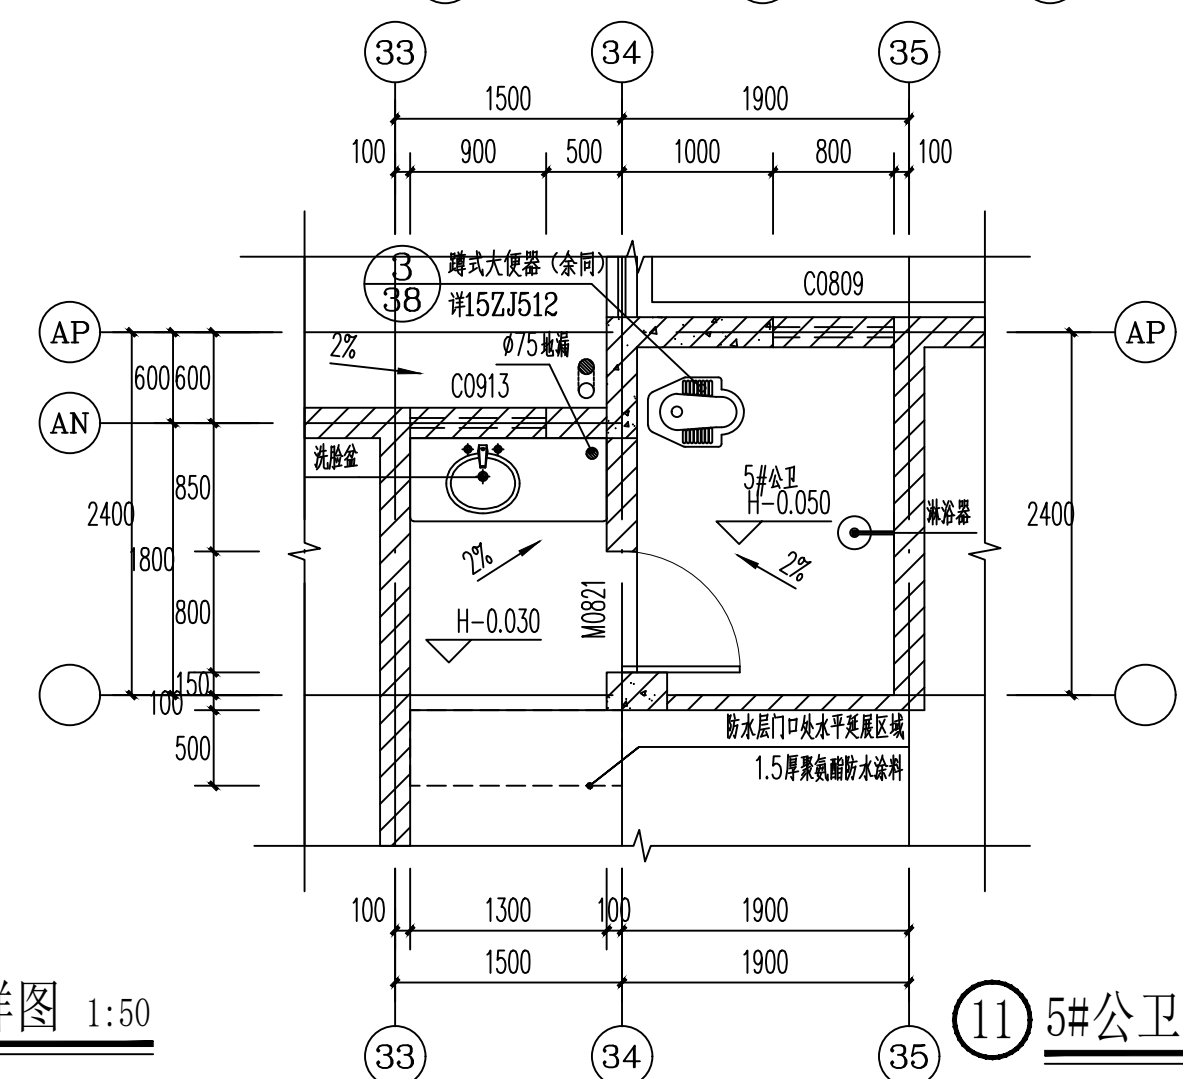


⑪ 5#公卫大样图 1:50

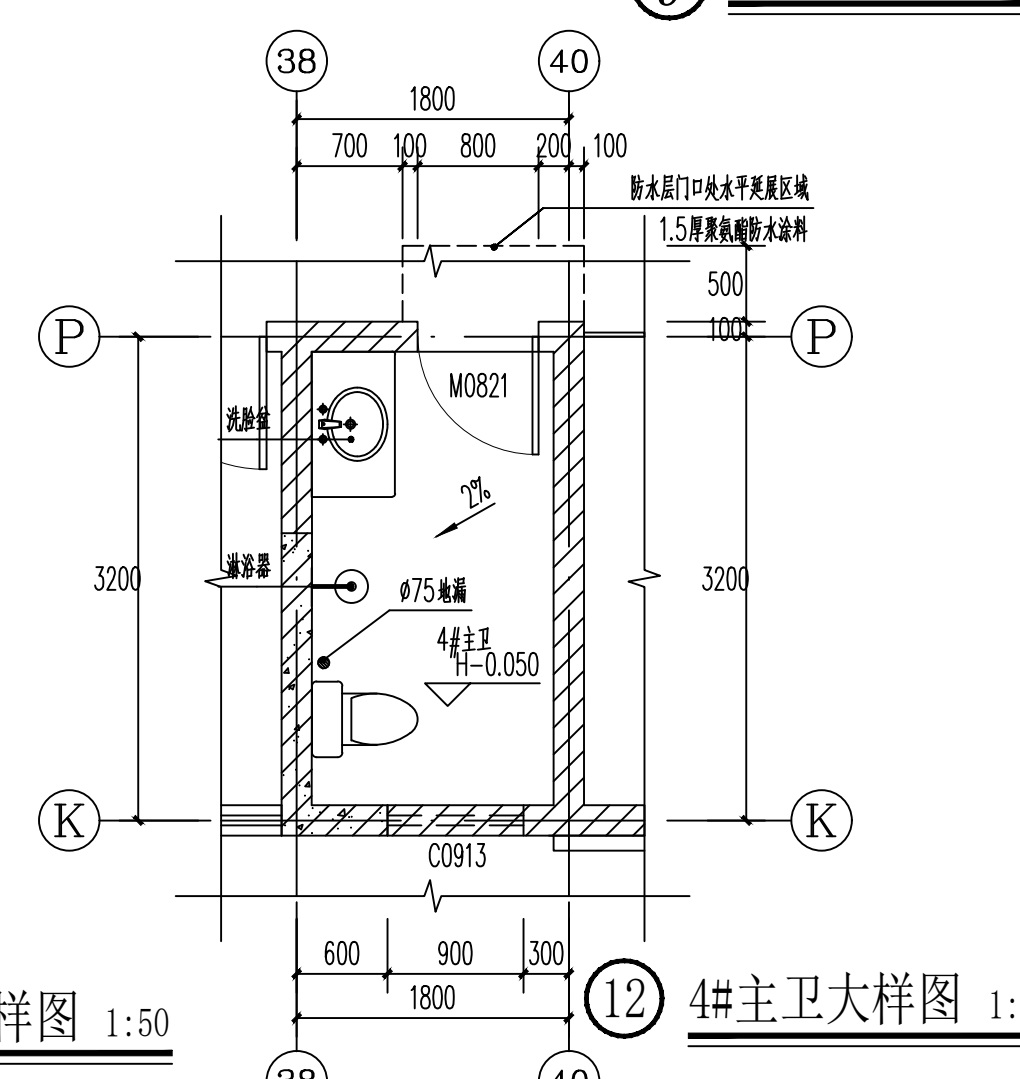


⑫ 4#主卫大样图 1:50

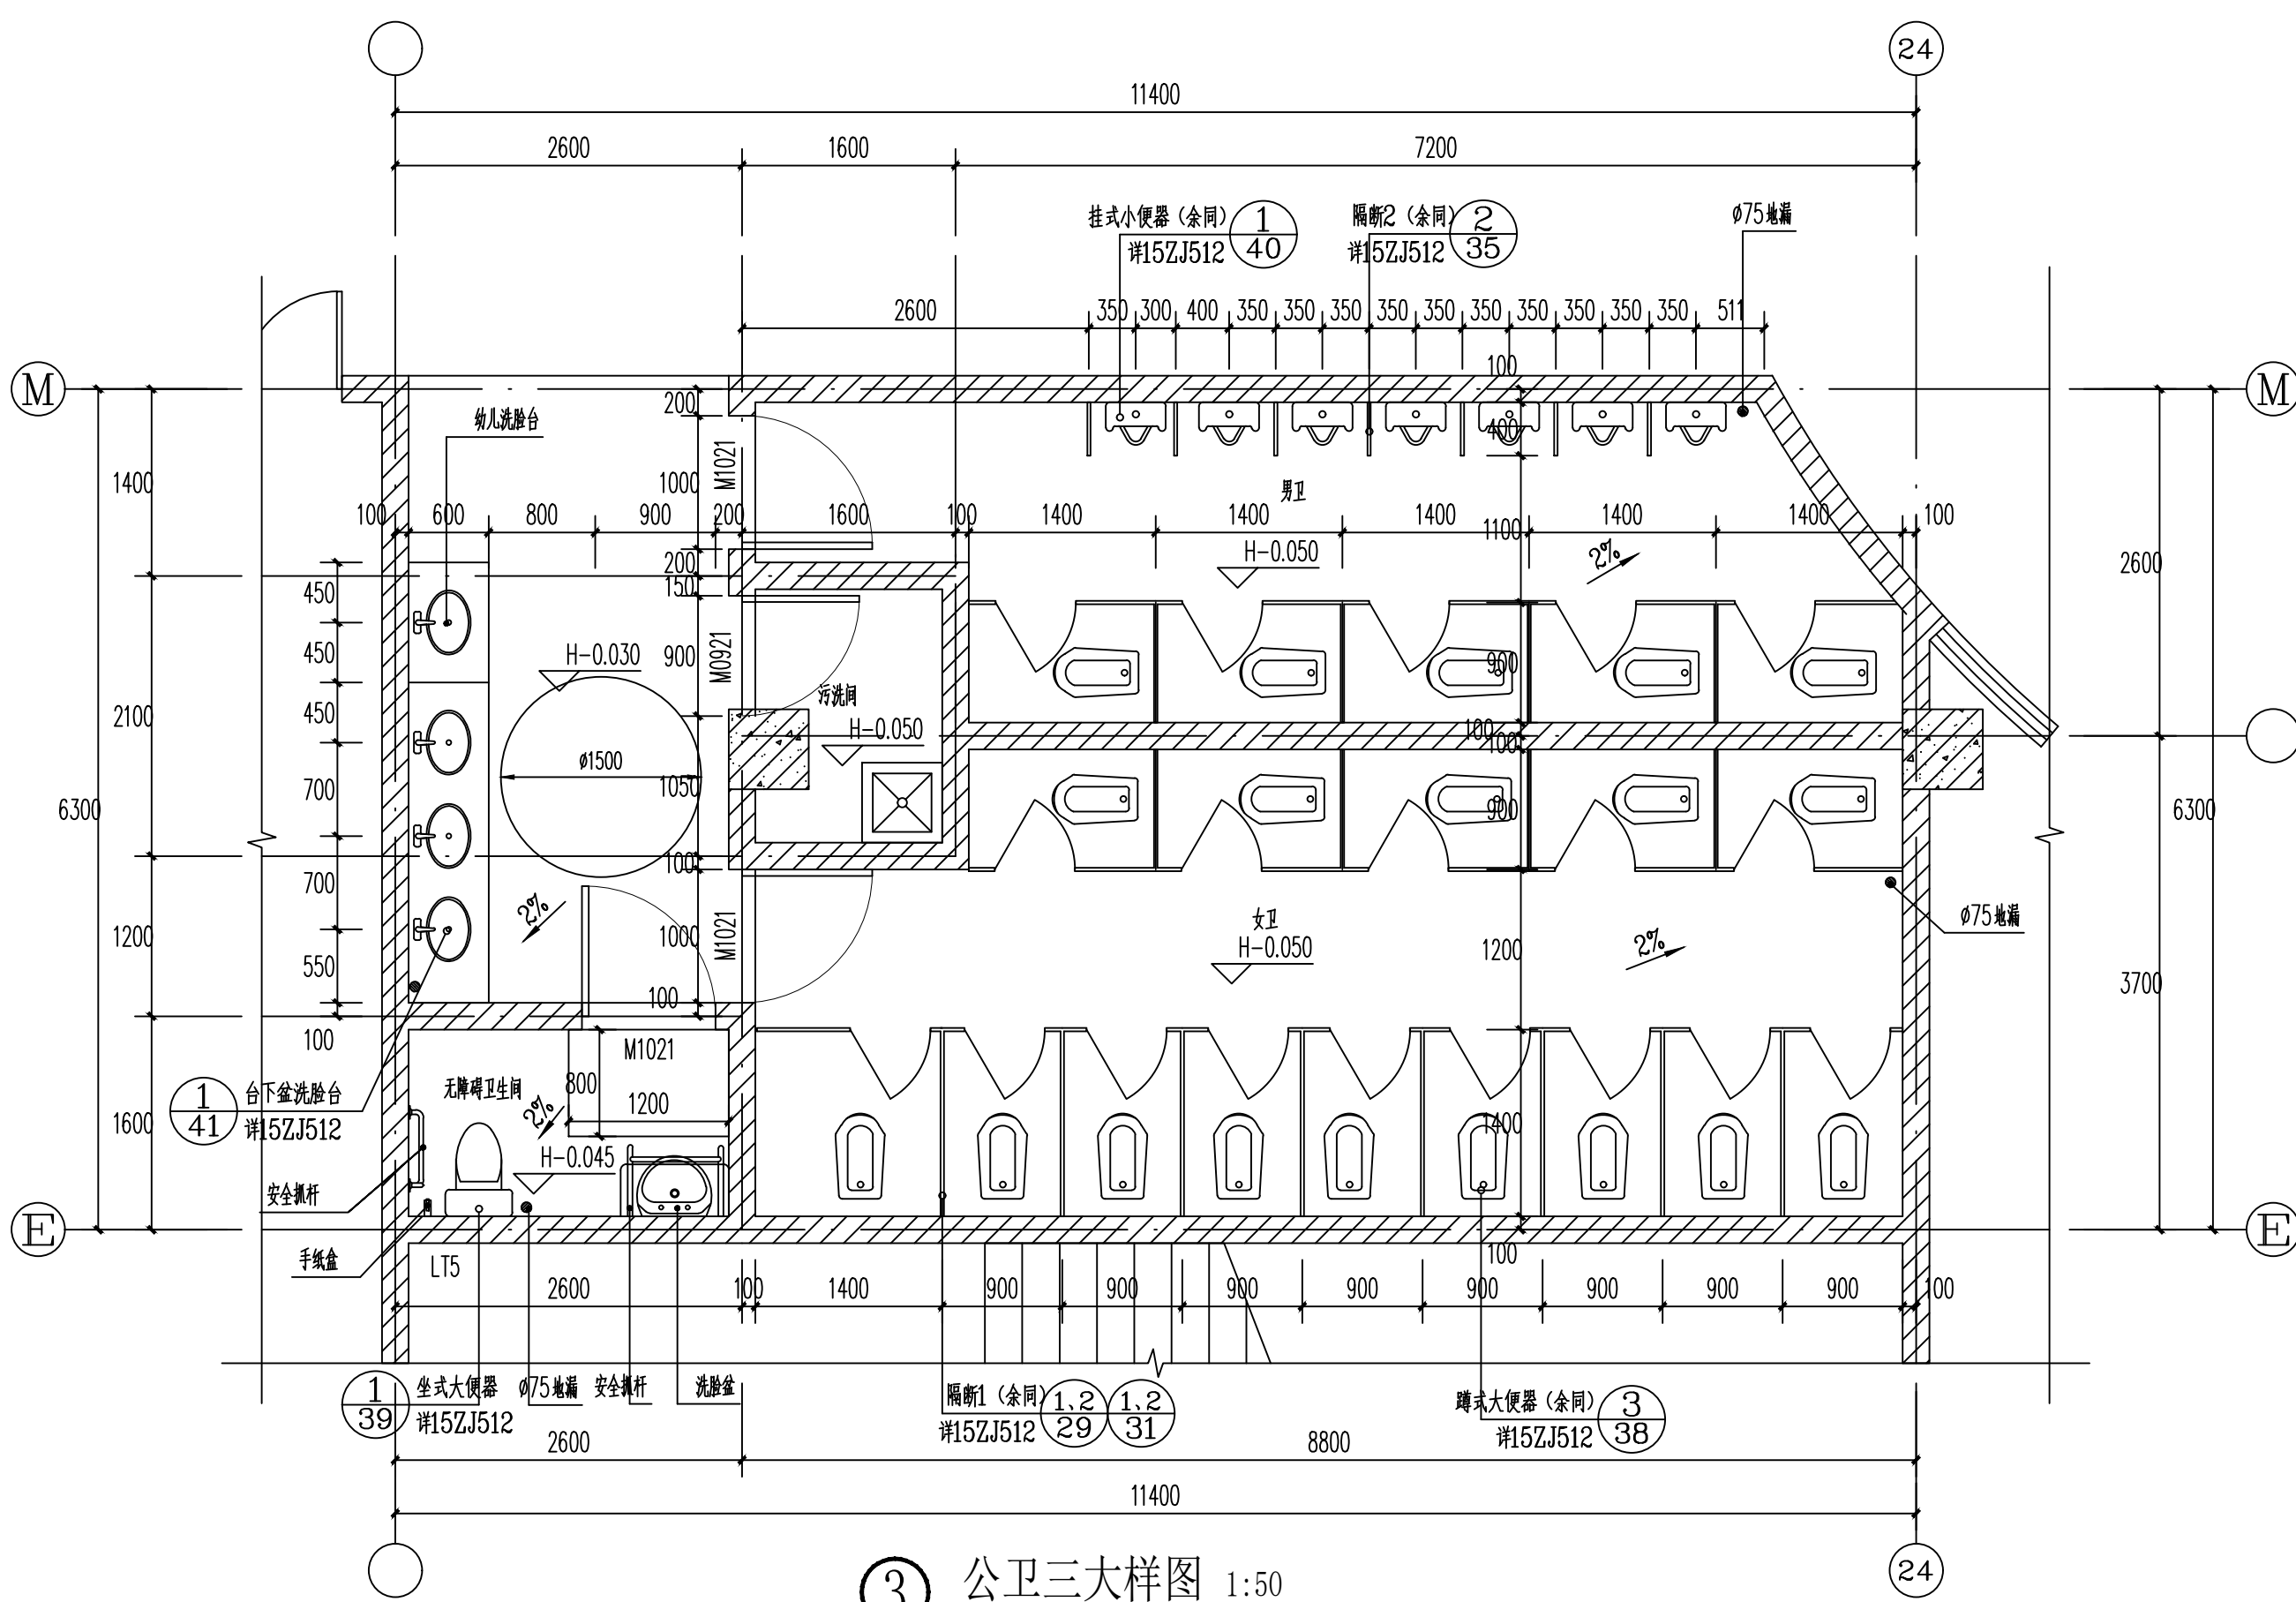

③ 公卫三大样图 1:50

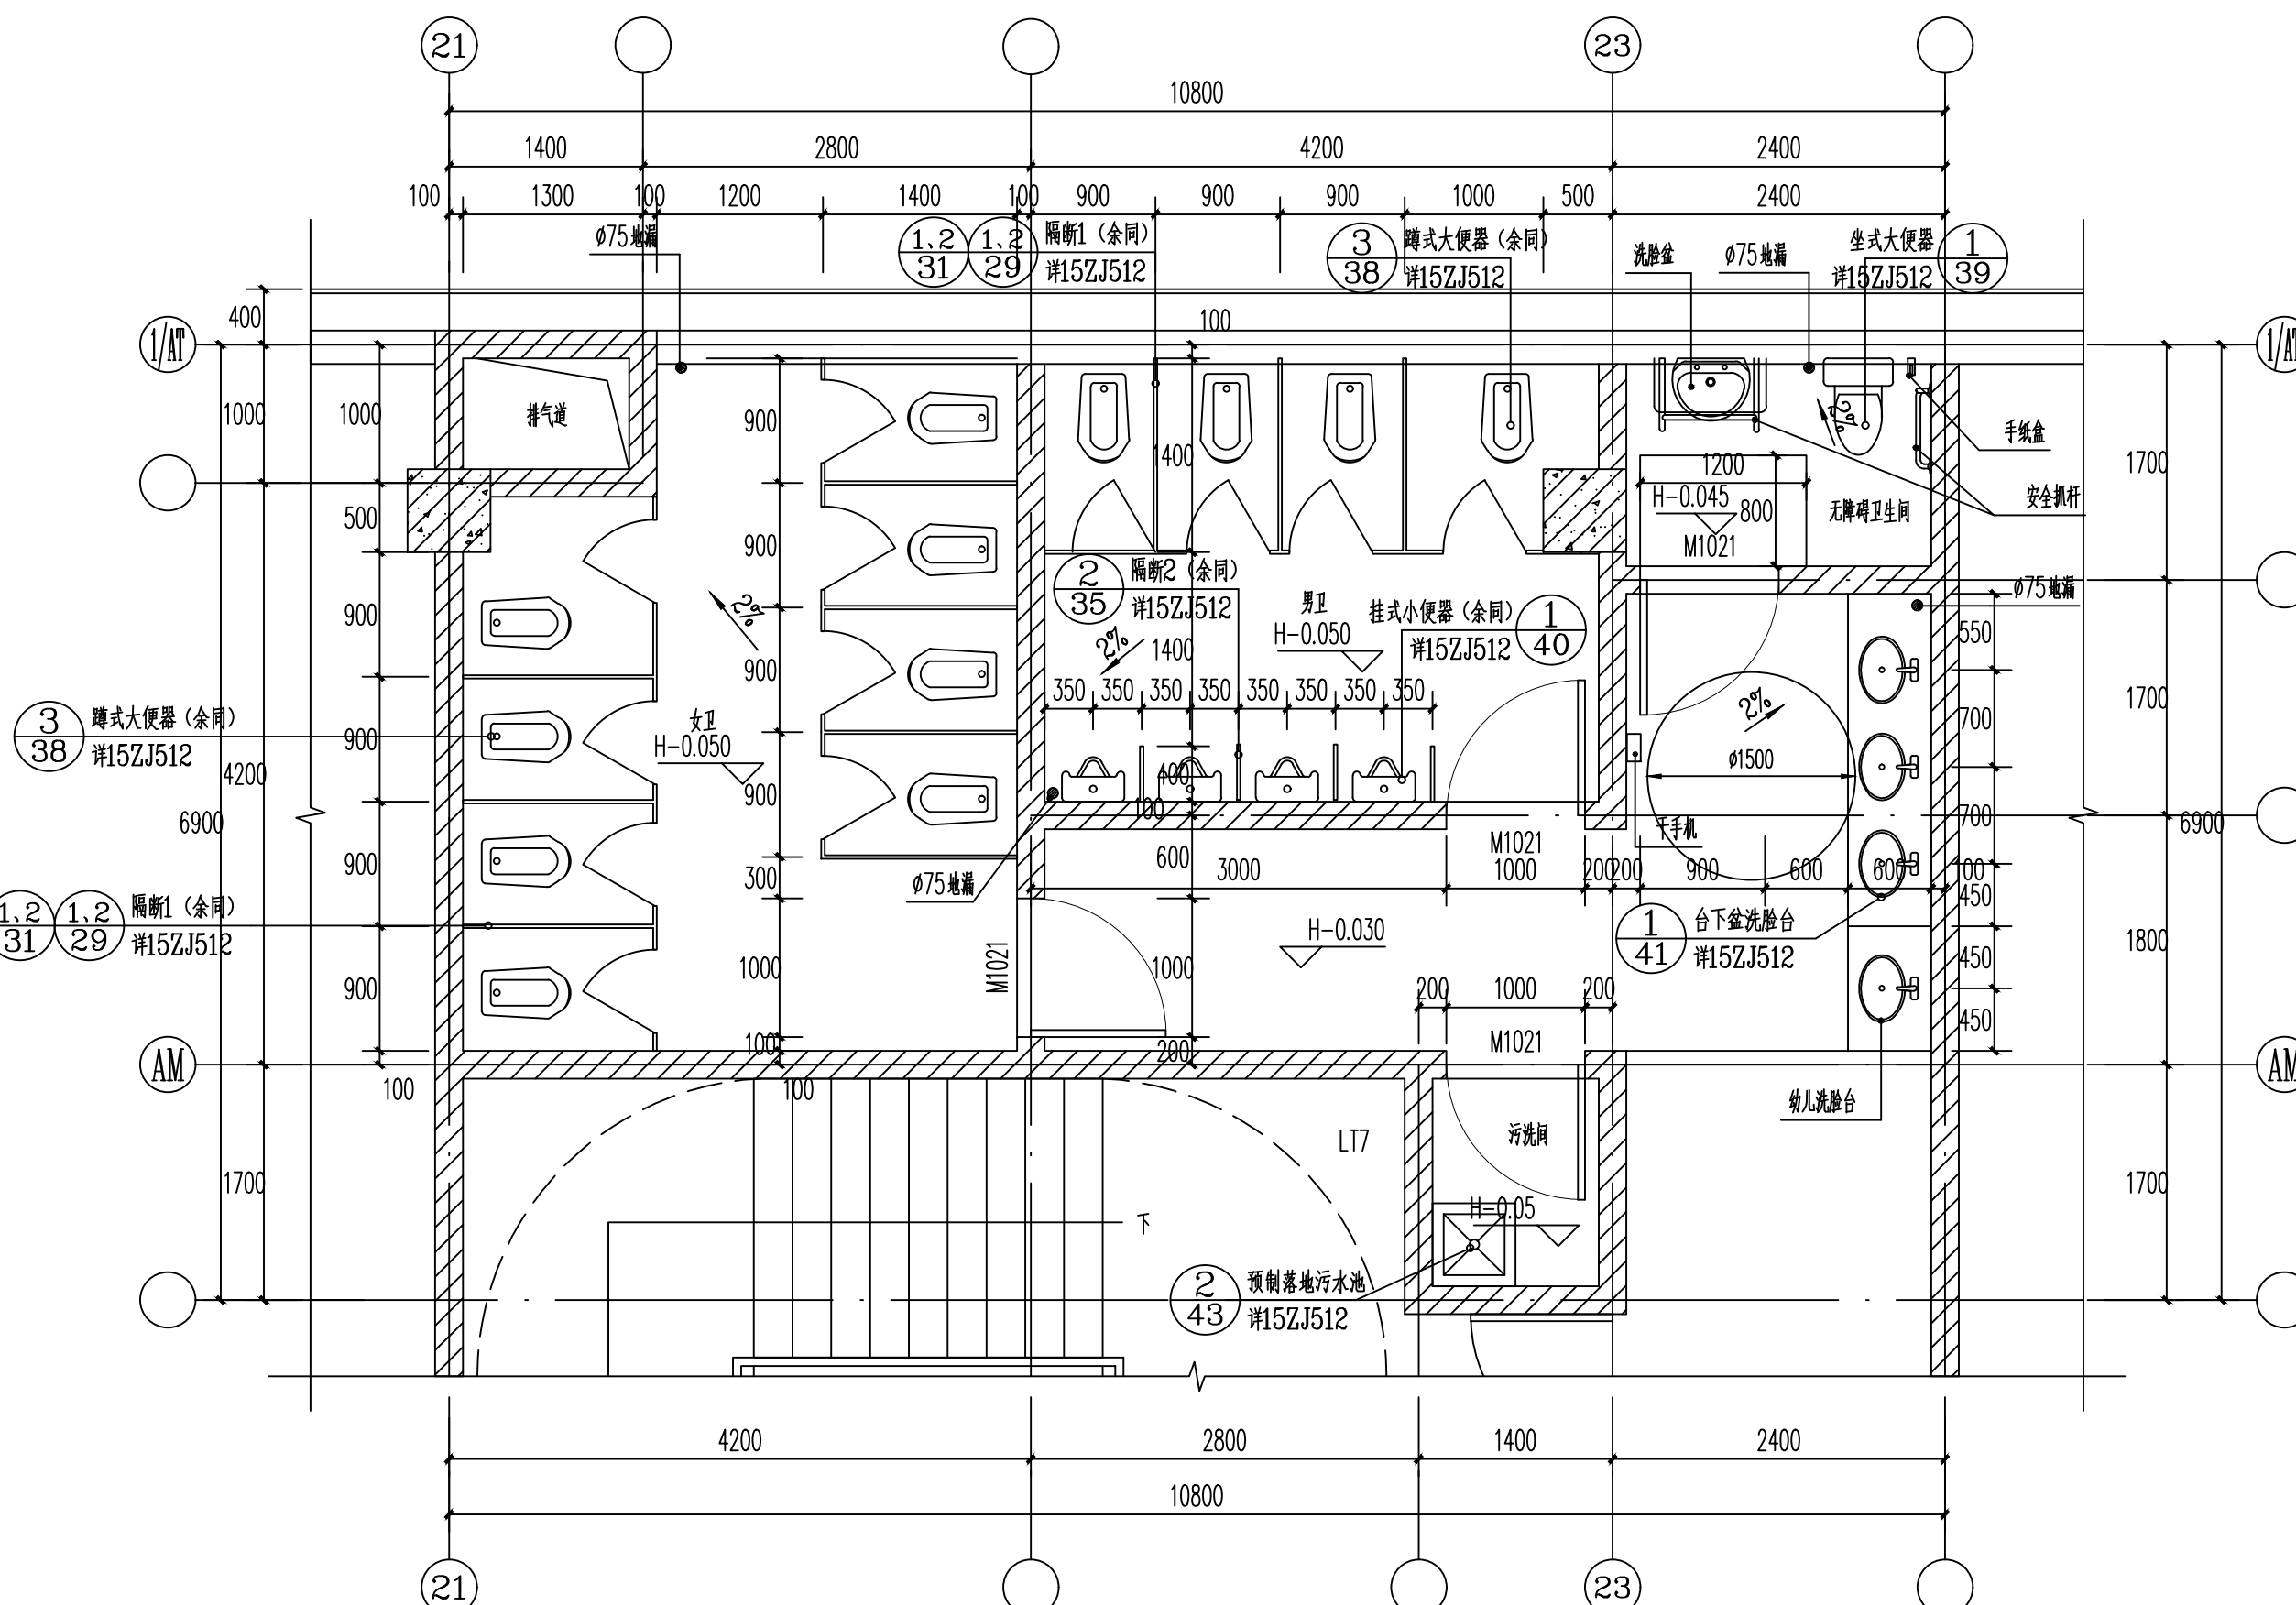

⑤ 公卫五大样图 1:50

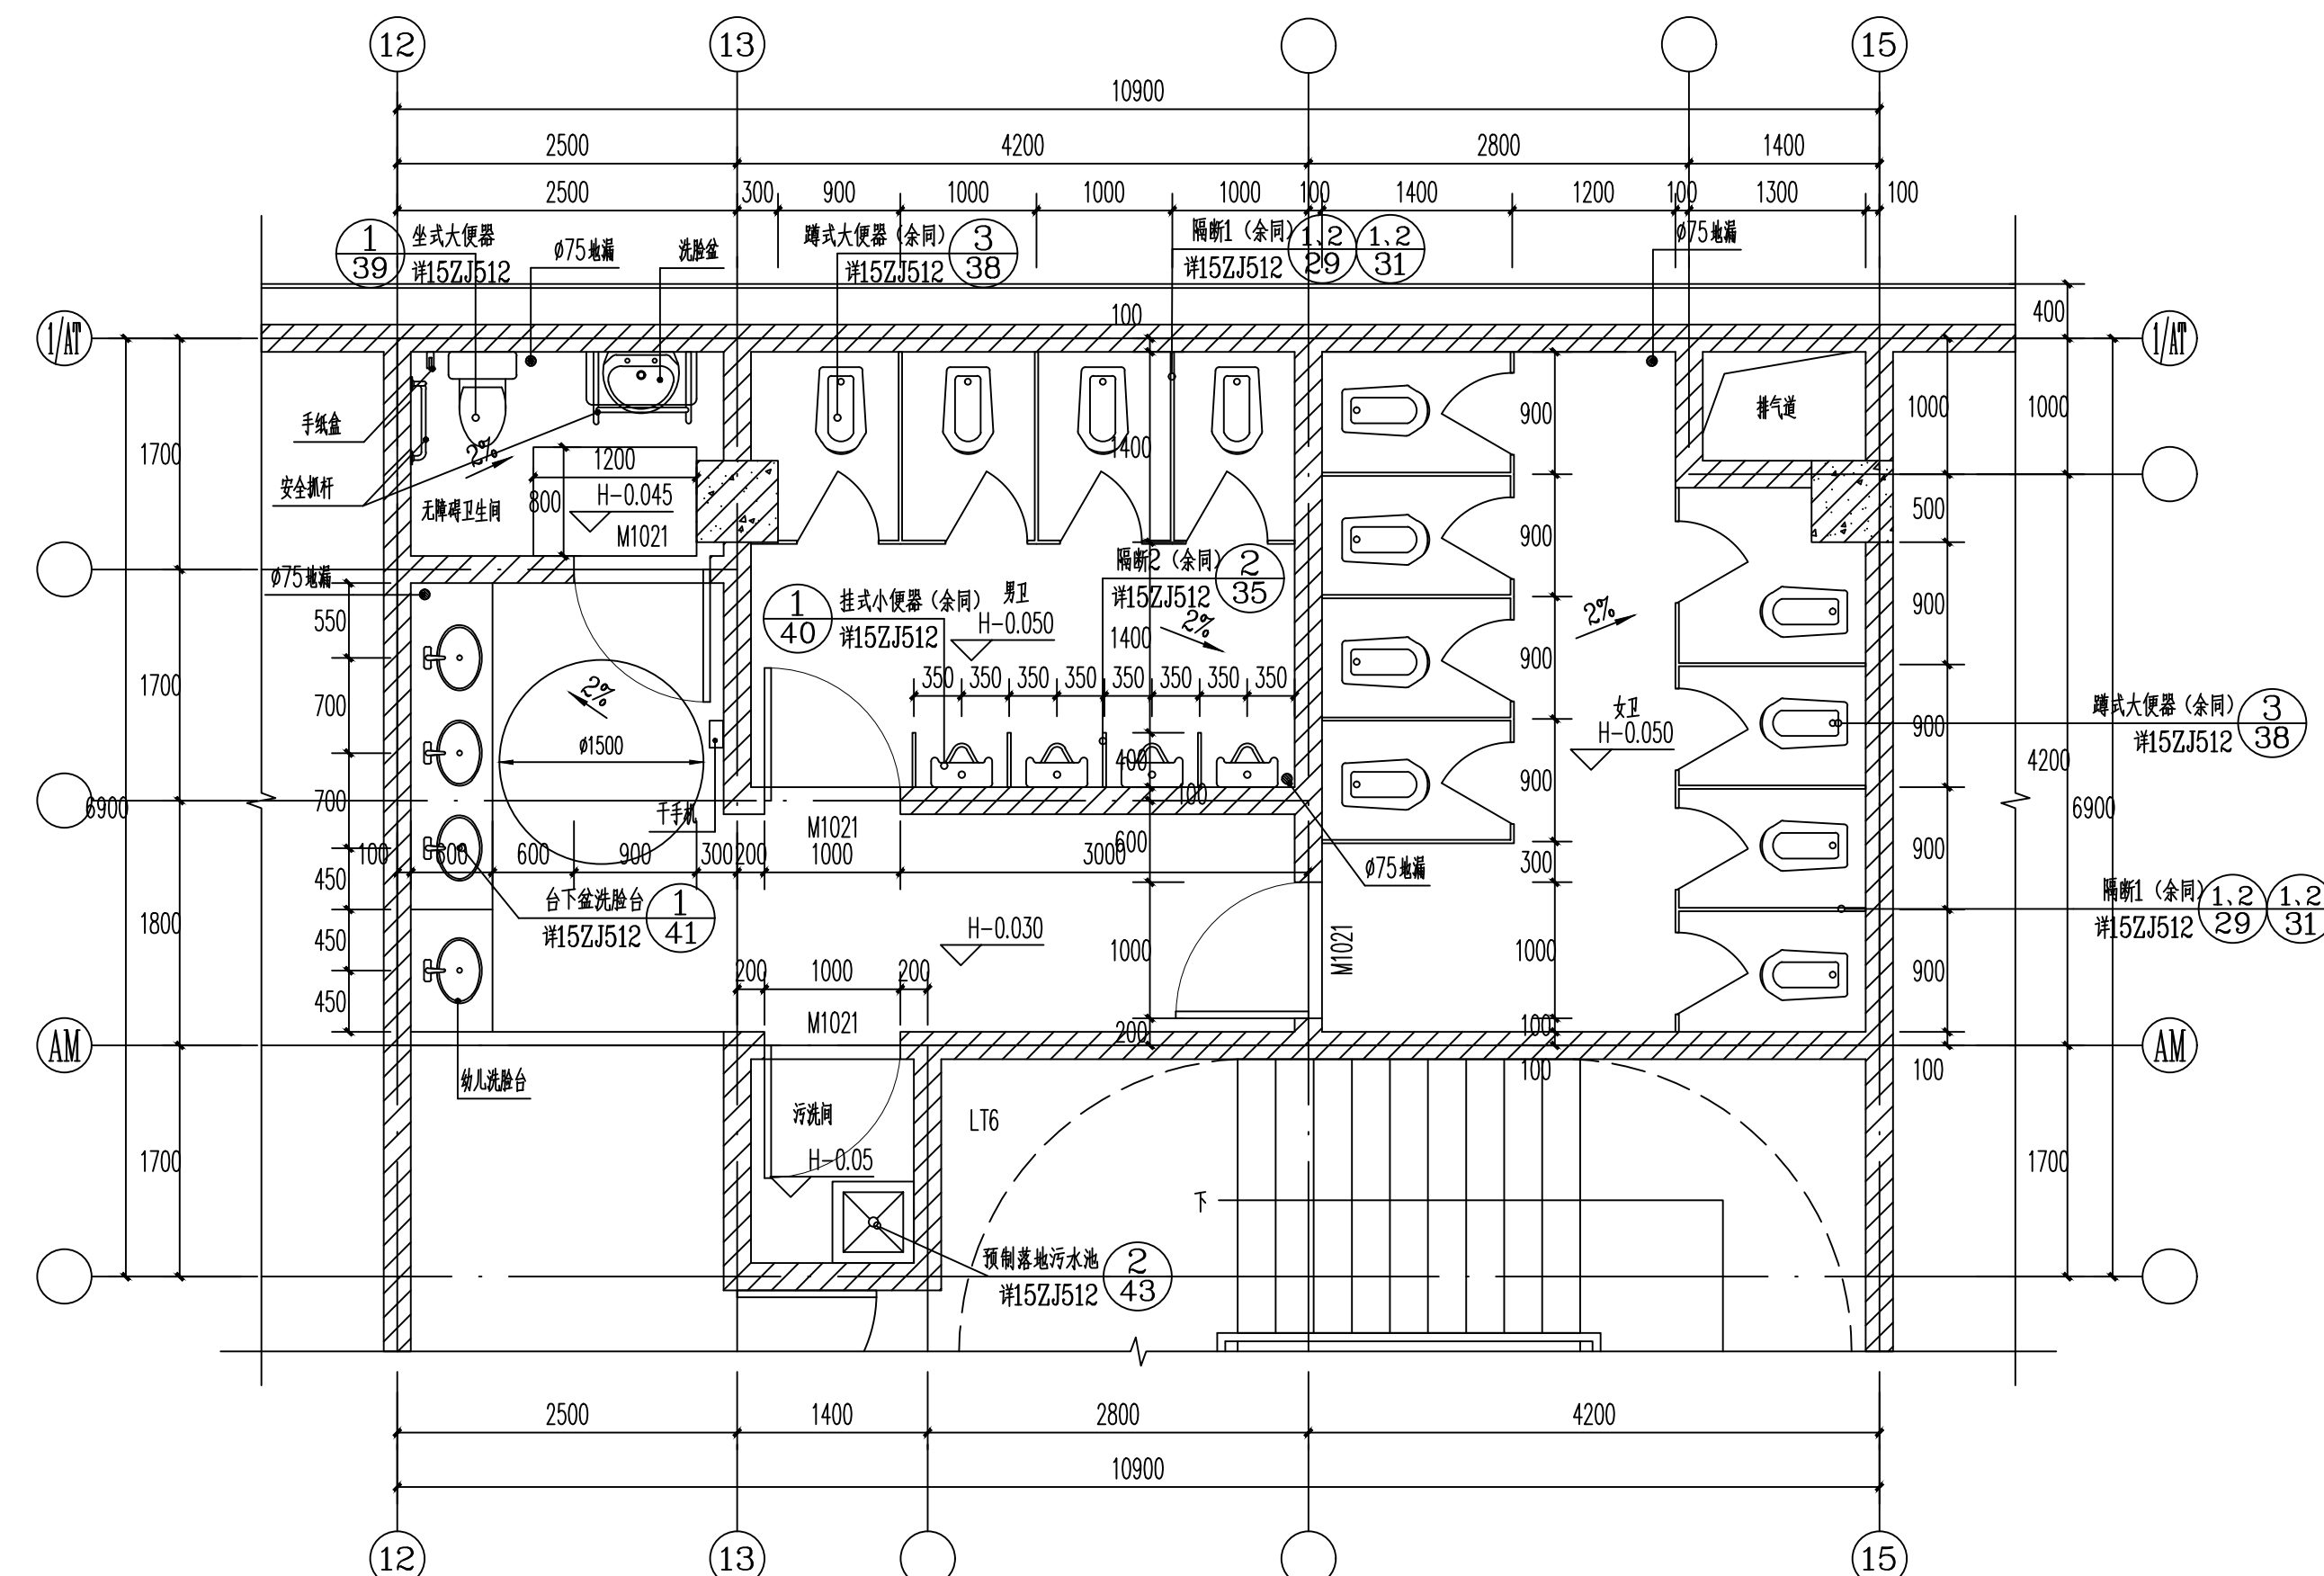

⑥ 公卫六大样图 1:50

建设单位/CLIENT: 麻阳苗族自治县远桥房地产开发有限公司		
项目名称/PROJECT: 远桥国际		
子项目名称/SUB-PROJECT: 远桥国际		
区位图/REGIONAL LOCATION MAP :		
广东建筑艺术设计院有限公司 GUANGDONG ARCHITECTURAL ARTISTIC DESIGN INSTITUTE CO.,LTD ■ 建筑方案设计: 甲级 ■ 风景园林设计: 乙级 ■ 城乡规划设计: 乙级 ■ 市政工程设计: 乙级		
图纸名称/TITLE: 卫生间大样图		
项目名称/PROJECT: 远桥国际		
设计 DESIGNED	古新辉	
校对 CHECKED	吴新红	
专业负责人 CHIEF	吴志刚	
项目负责人 PROJECT CHIEF	吴志刚	
审核 IDENTIFIED	黄展优	
审定 APPROVED	李 坚	
业务号/JOB NO.		
设计阶段/STATUS: 施工图		
专业/DISCIPLINE: 建筑		
比例/ SCALE:	1: 100	规格/ SIZE: A1
出图日期/DATE: 2021.06		
图号/DRAWING NO. JS-27		
版次 NO.	修改内容 DESCRIPTION	日期 DATE
条形码/BARCODE:		
版权所有, 不得复制、套用。 ALL RIGHTS RESERVED, DON'T COPIED, REPRODUCED.		