


LT5楼梯间负一层平面图 1:50

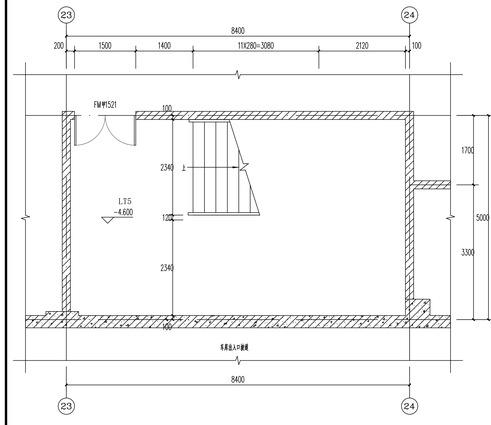


LT5楼梯间H=-2.700处平面图 1:50




LT5楼梯间一层平面图 1:50

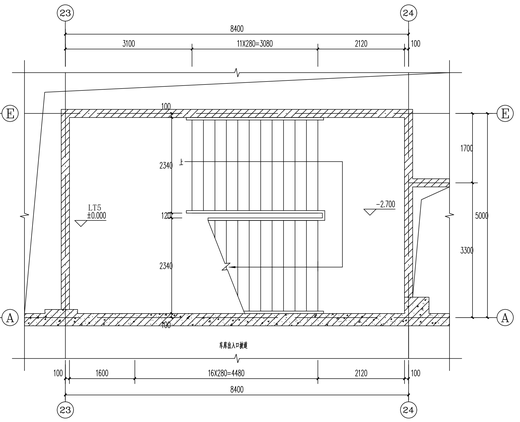


LT5楼梯间H=2.600平面图 1:50

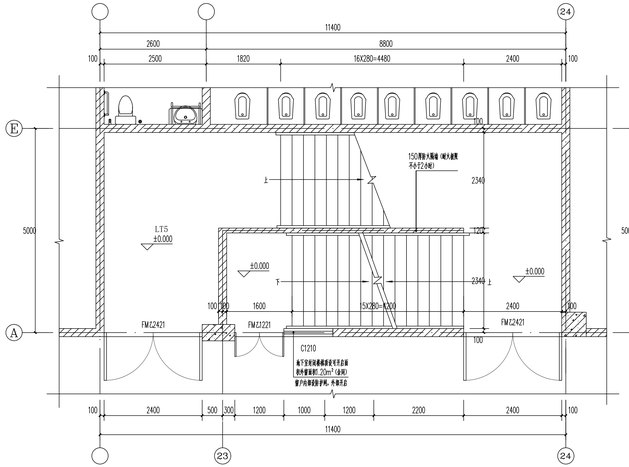


LT5楼梯间二层平面图 1:50

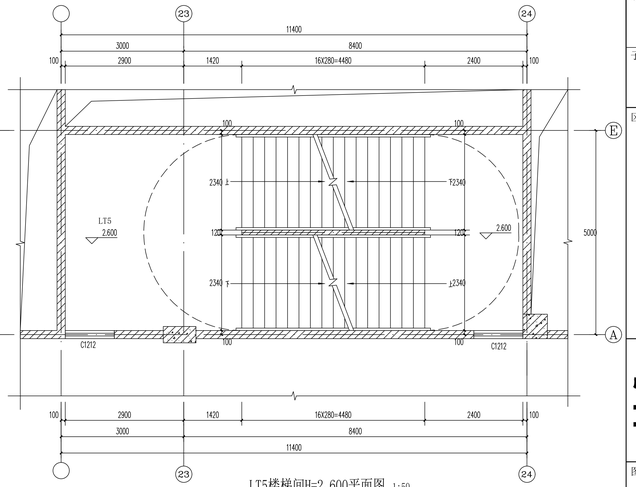


LT5楼梯间H=8.100处平面图 1:50

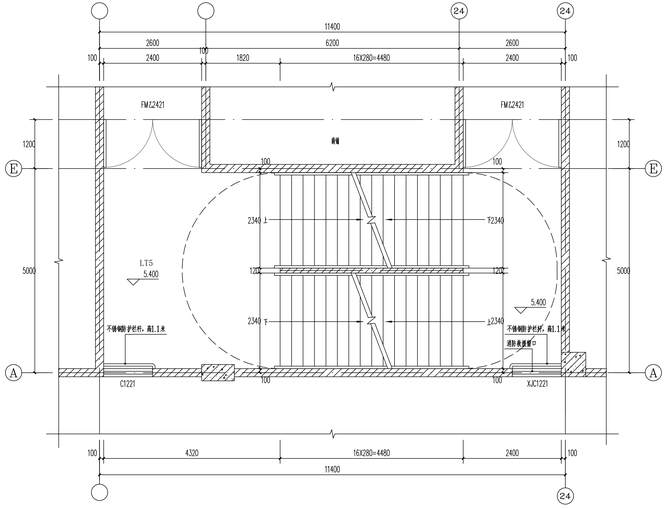


LT5楼梯间三层平面图 1:50

建设单位/CLIENT:

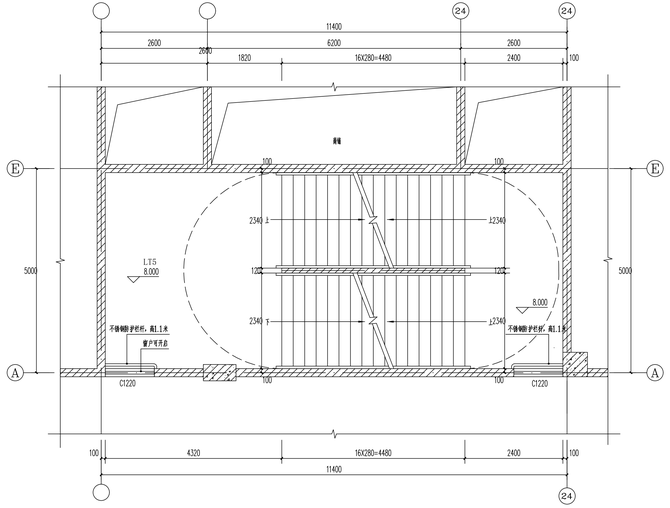麻阳苗族自治县远桥房地产开发有限公司

项目名称/PROJECT:

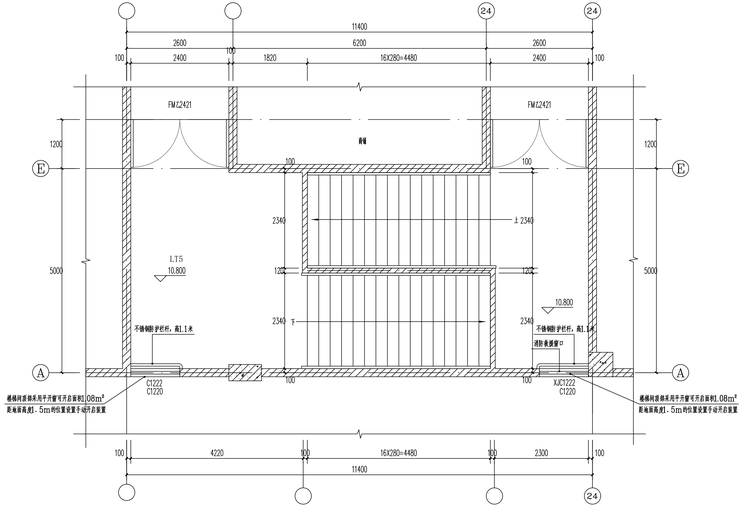远程国际

子项目名称/SUB-PROJECT:

远程国际

区位图/REGIONAL LOCATION MAP :


广东建筑艺术设计院有限公司
GUANGDONG ARCHITECTURAL ARTISTIC DESIGN INSTITUTE CO.,LTD
■ 建筑工程设计，甲级 ■ 风景园林设计，乙级
■ 城乡规划设计，乙级 ■ 市政设计，乙级


图纸名称/TITLE:

LT5楼梯间大样图

项目名称/PROJECT:

远程国际

| | | |
|---|---|---|
| 设计 DESIGNED | 古新辉 | |
| 校对 CHECKED | 吴新红 | |
| 专业负责人 CHIEF | 吴志刚 | |
| 项目负责人 PROJECT CHIEF | 吴志刚 | |
| 审核 IDENTIFIED | 黄视优 | |
| 审定 APPROVED | 李 坚 | |

业务号/JOB NO.

设计阶段/STATUS: 施工图

专业/DISCIPLINE: 建施

| 比例/SCALE: | 1：100 | 规格/SIZE: | A1 |
|---|---|---|---|

出图日期/DATE: 2021.06

图号/DRAWING NO. JS-32

| 版次 NO. | 修改内容 DESCRIPTION | 日期 DATE |
|---|---|---|
| | | |
| | | |

条形码/BARCODE:


版权所有，不得复制、套用。
ALL RIGHTS RESERVED, DON'T COPIED, REPRODUCED.