




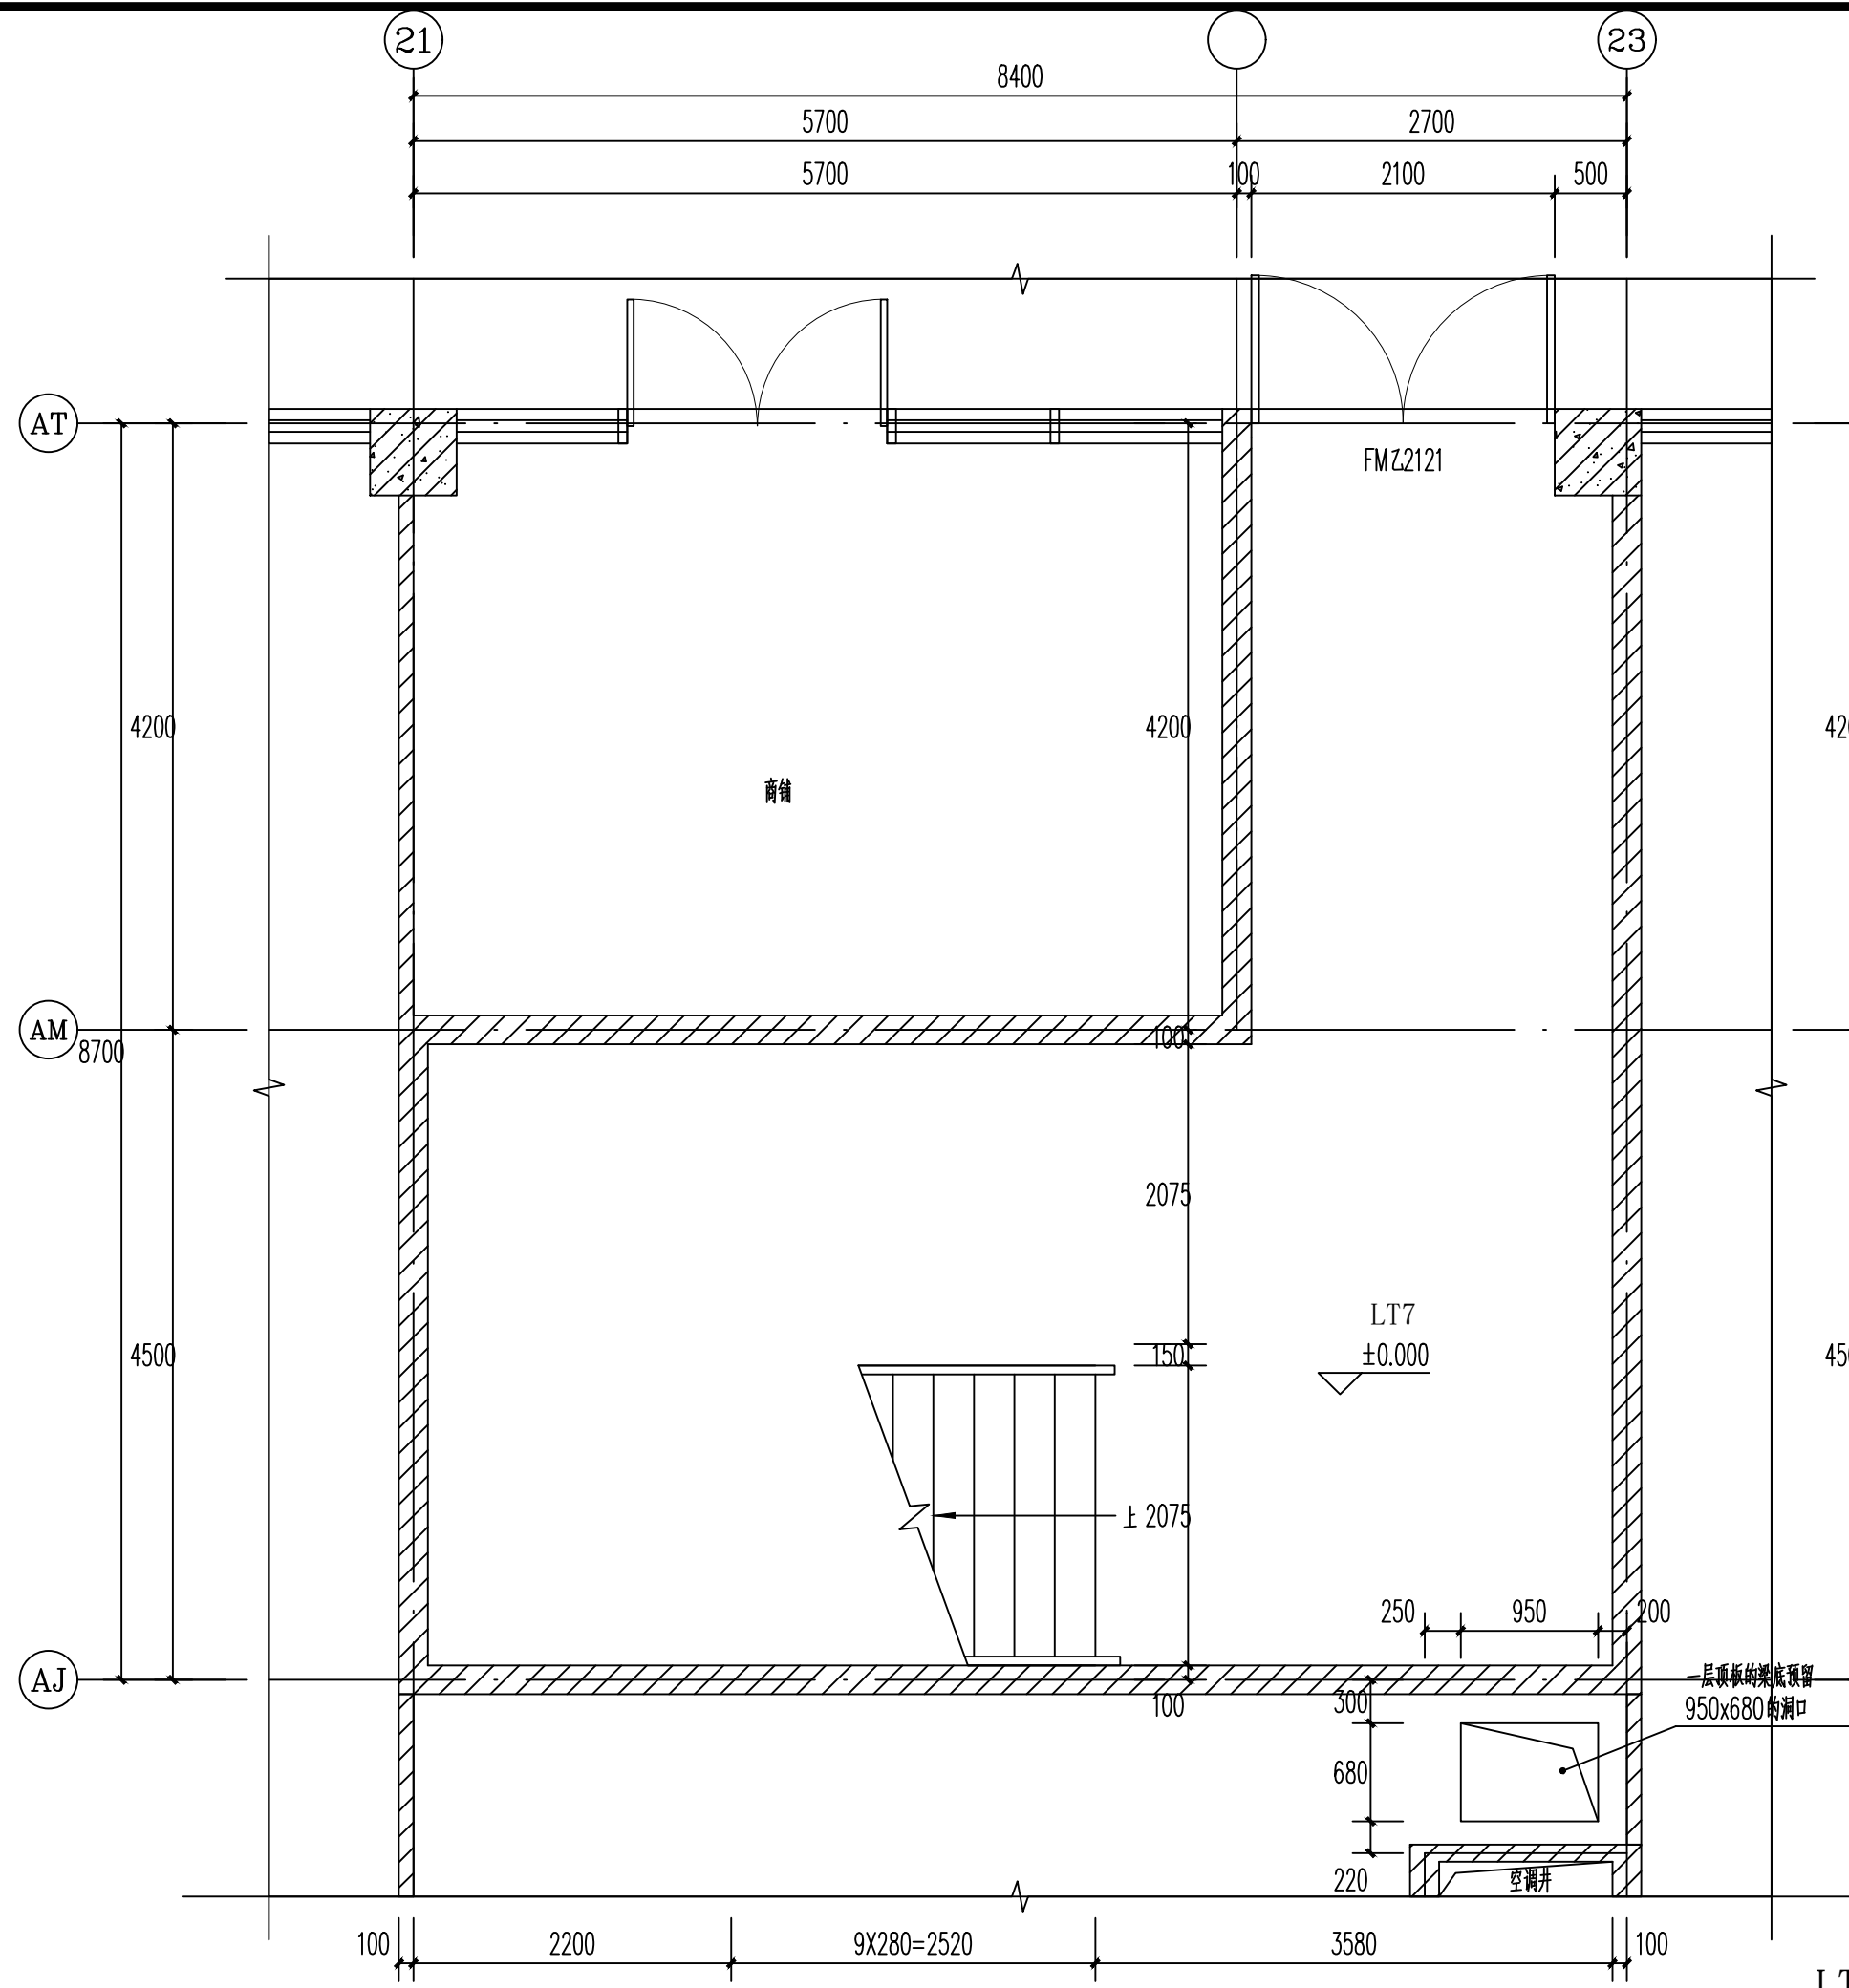


LT7楼梯间一层平面图 1:50

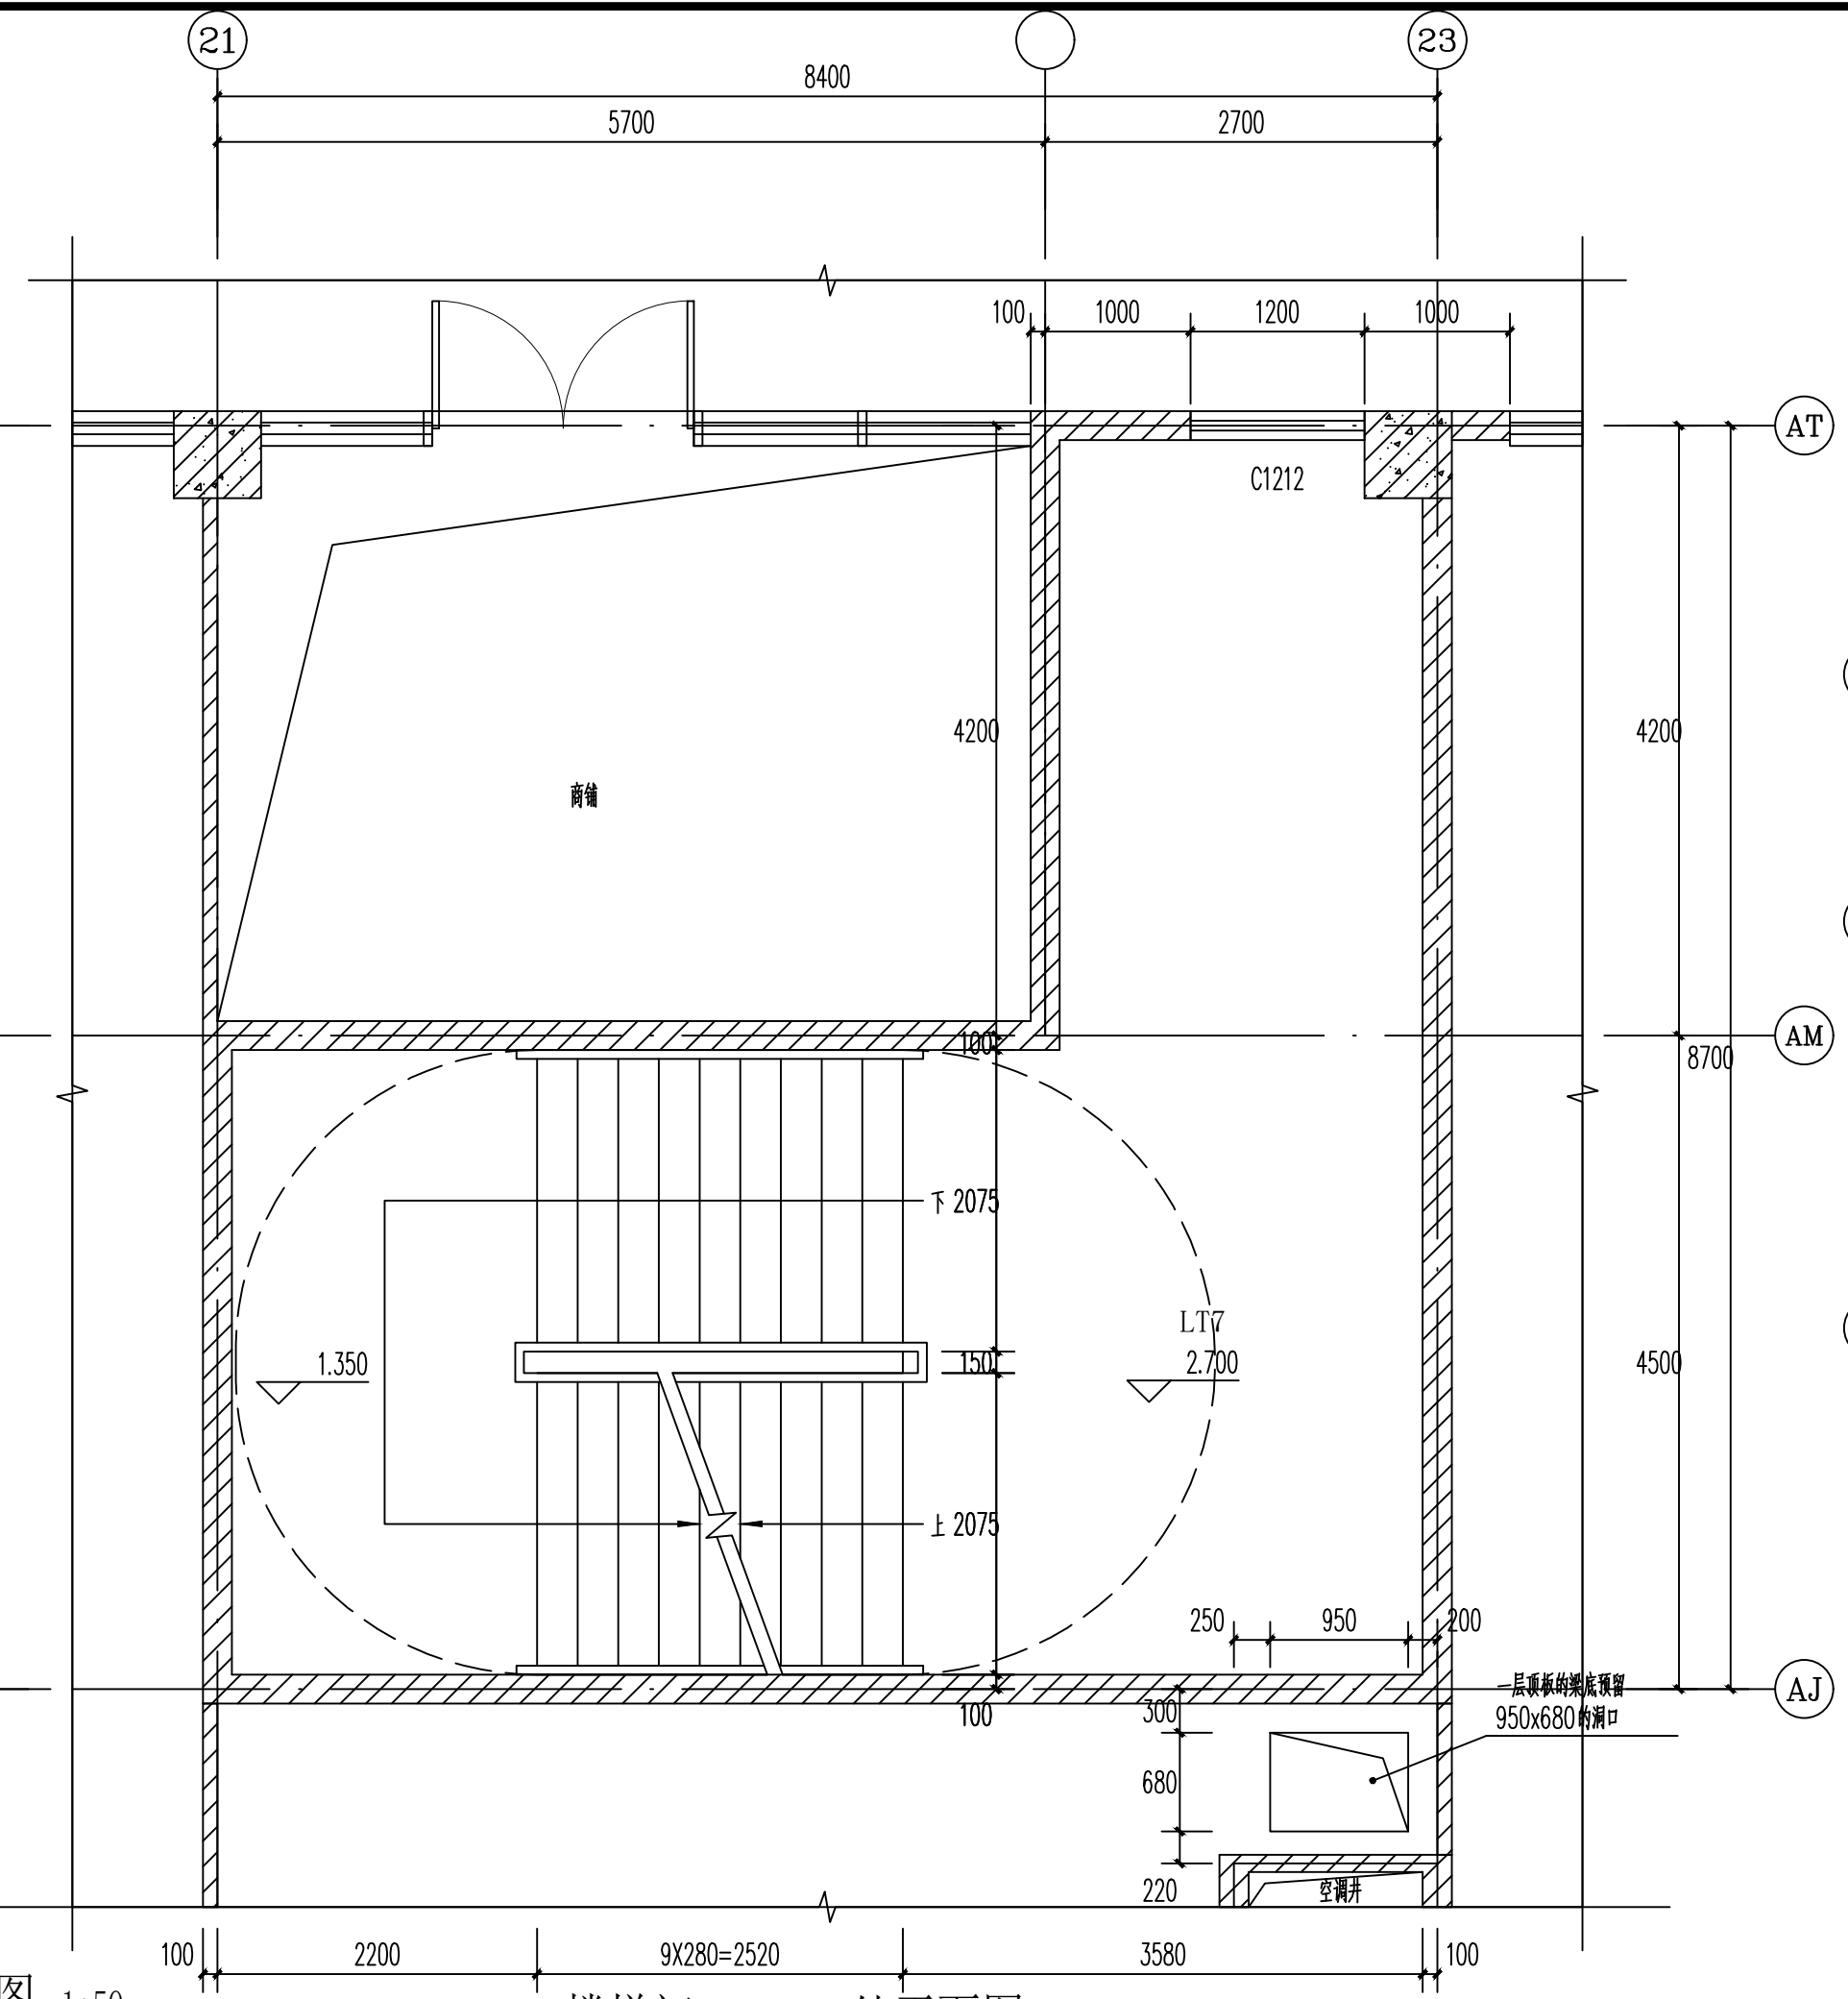


LT7楼梯间H=2.700处平面图 1:50

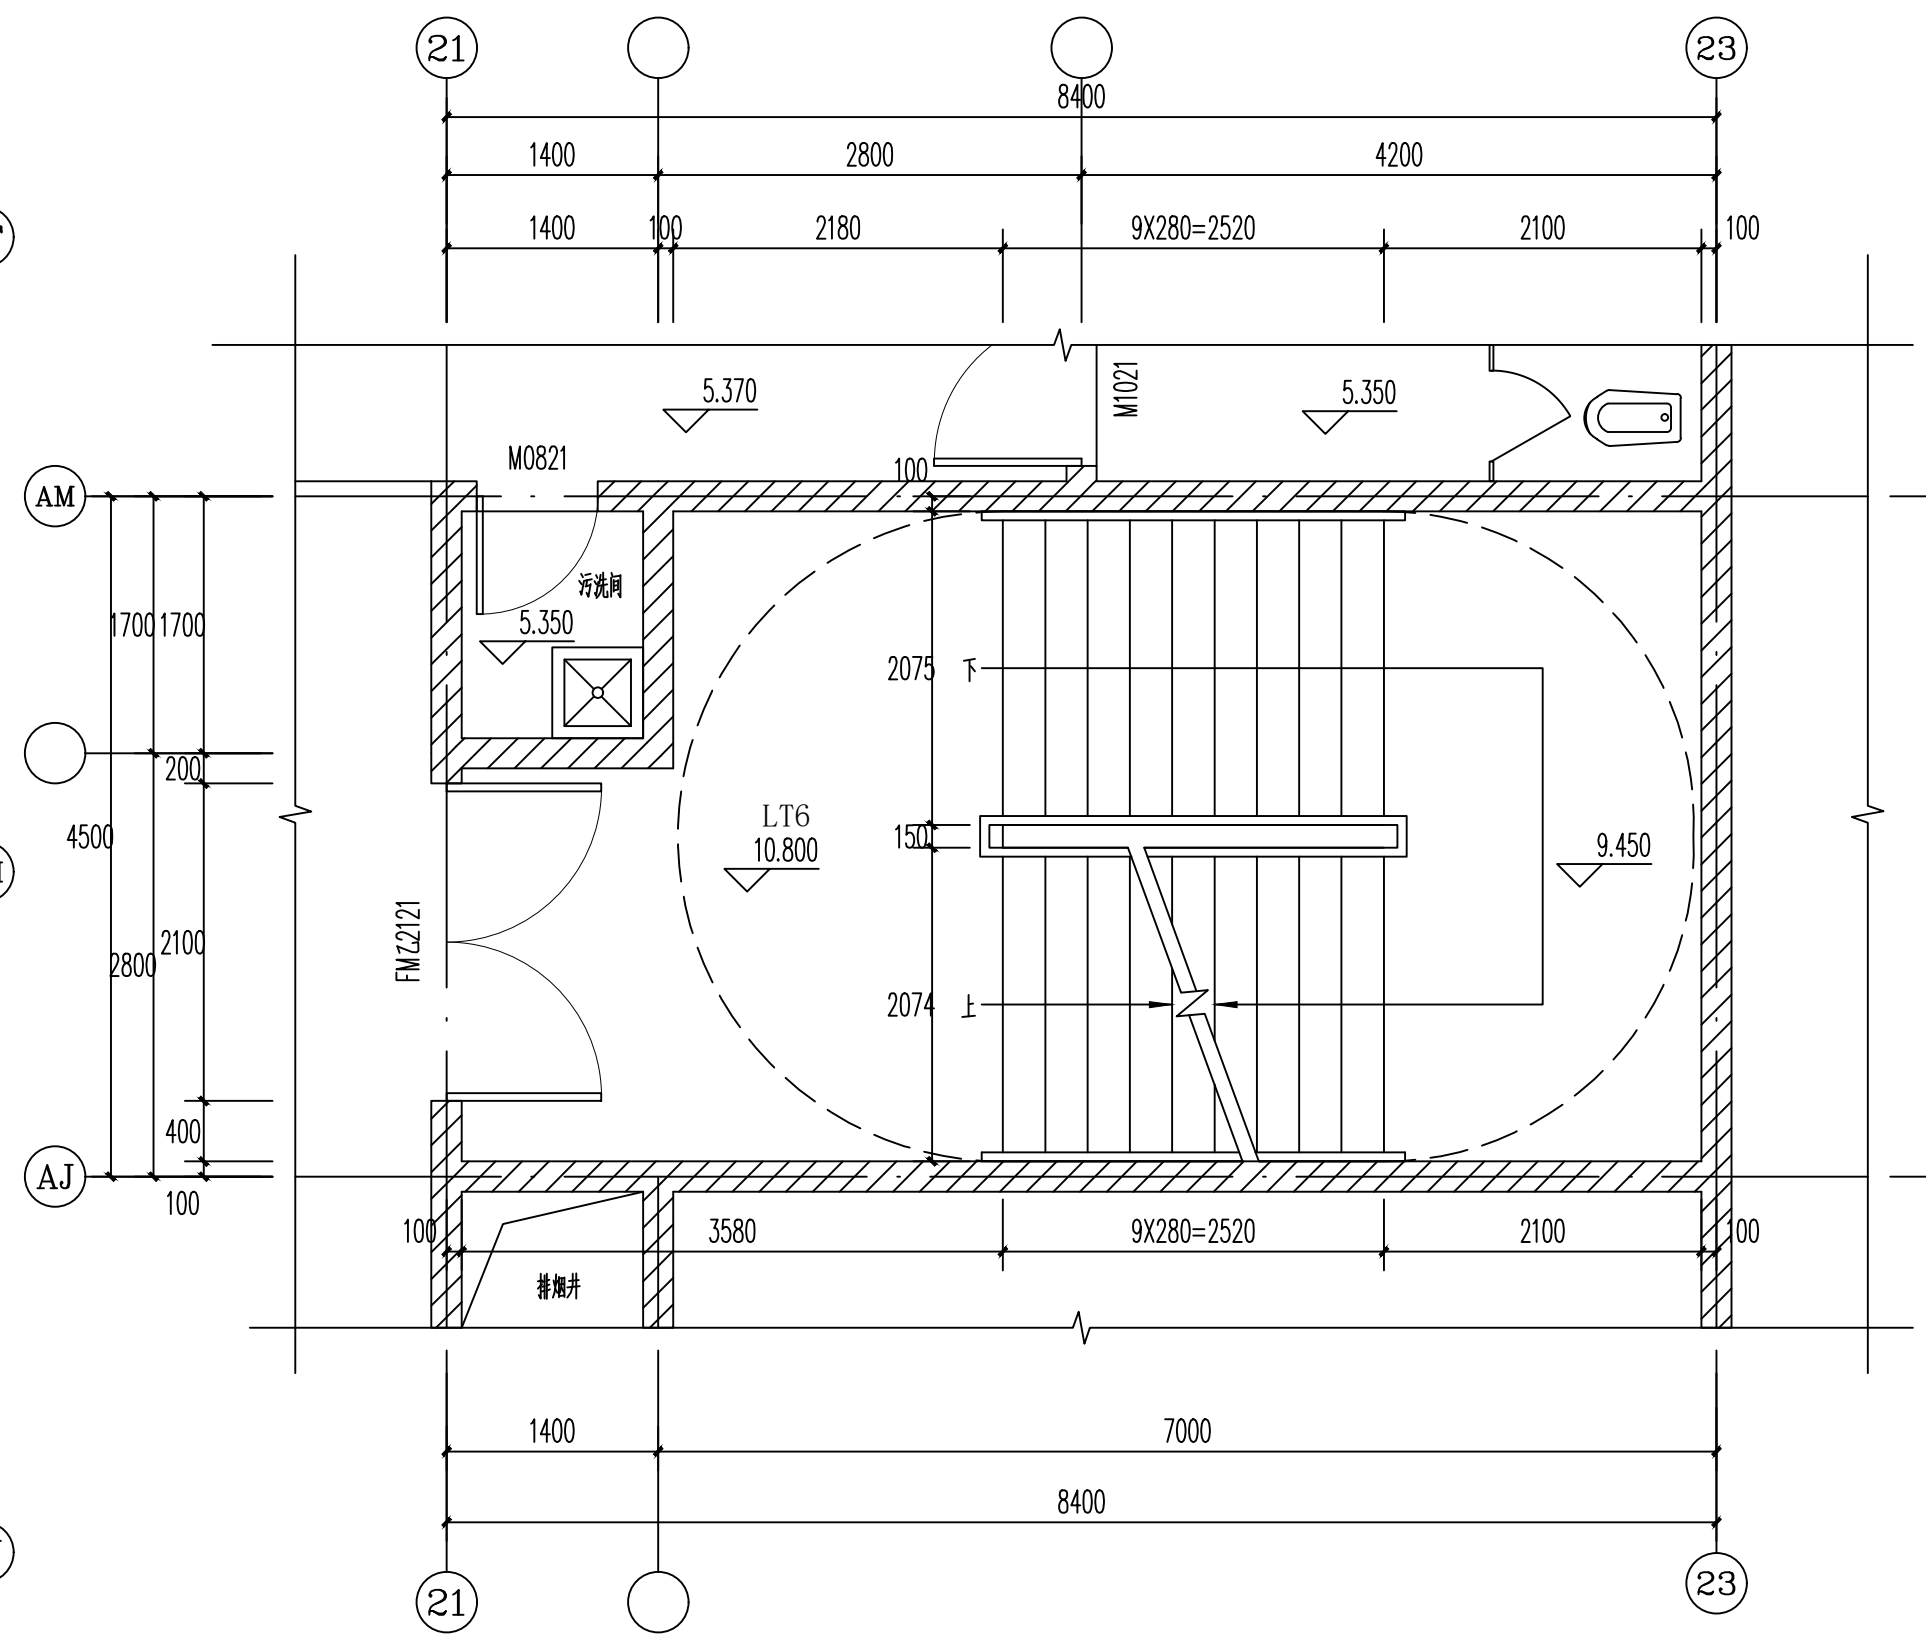

LT7楼梯间二层平面图 1:50

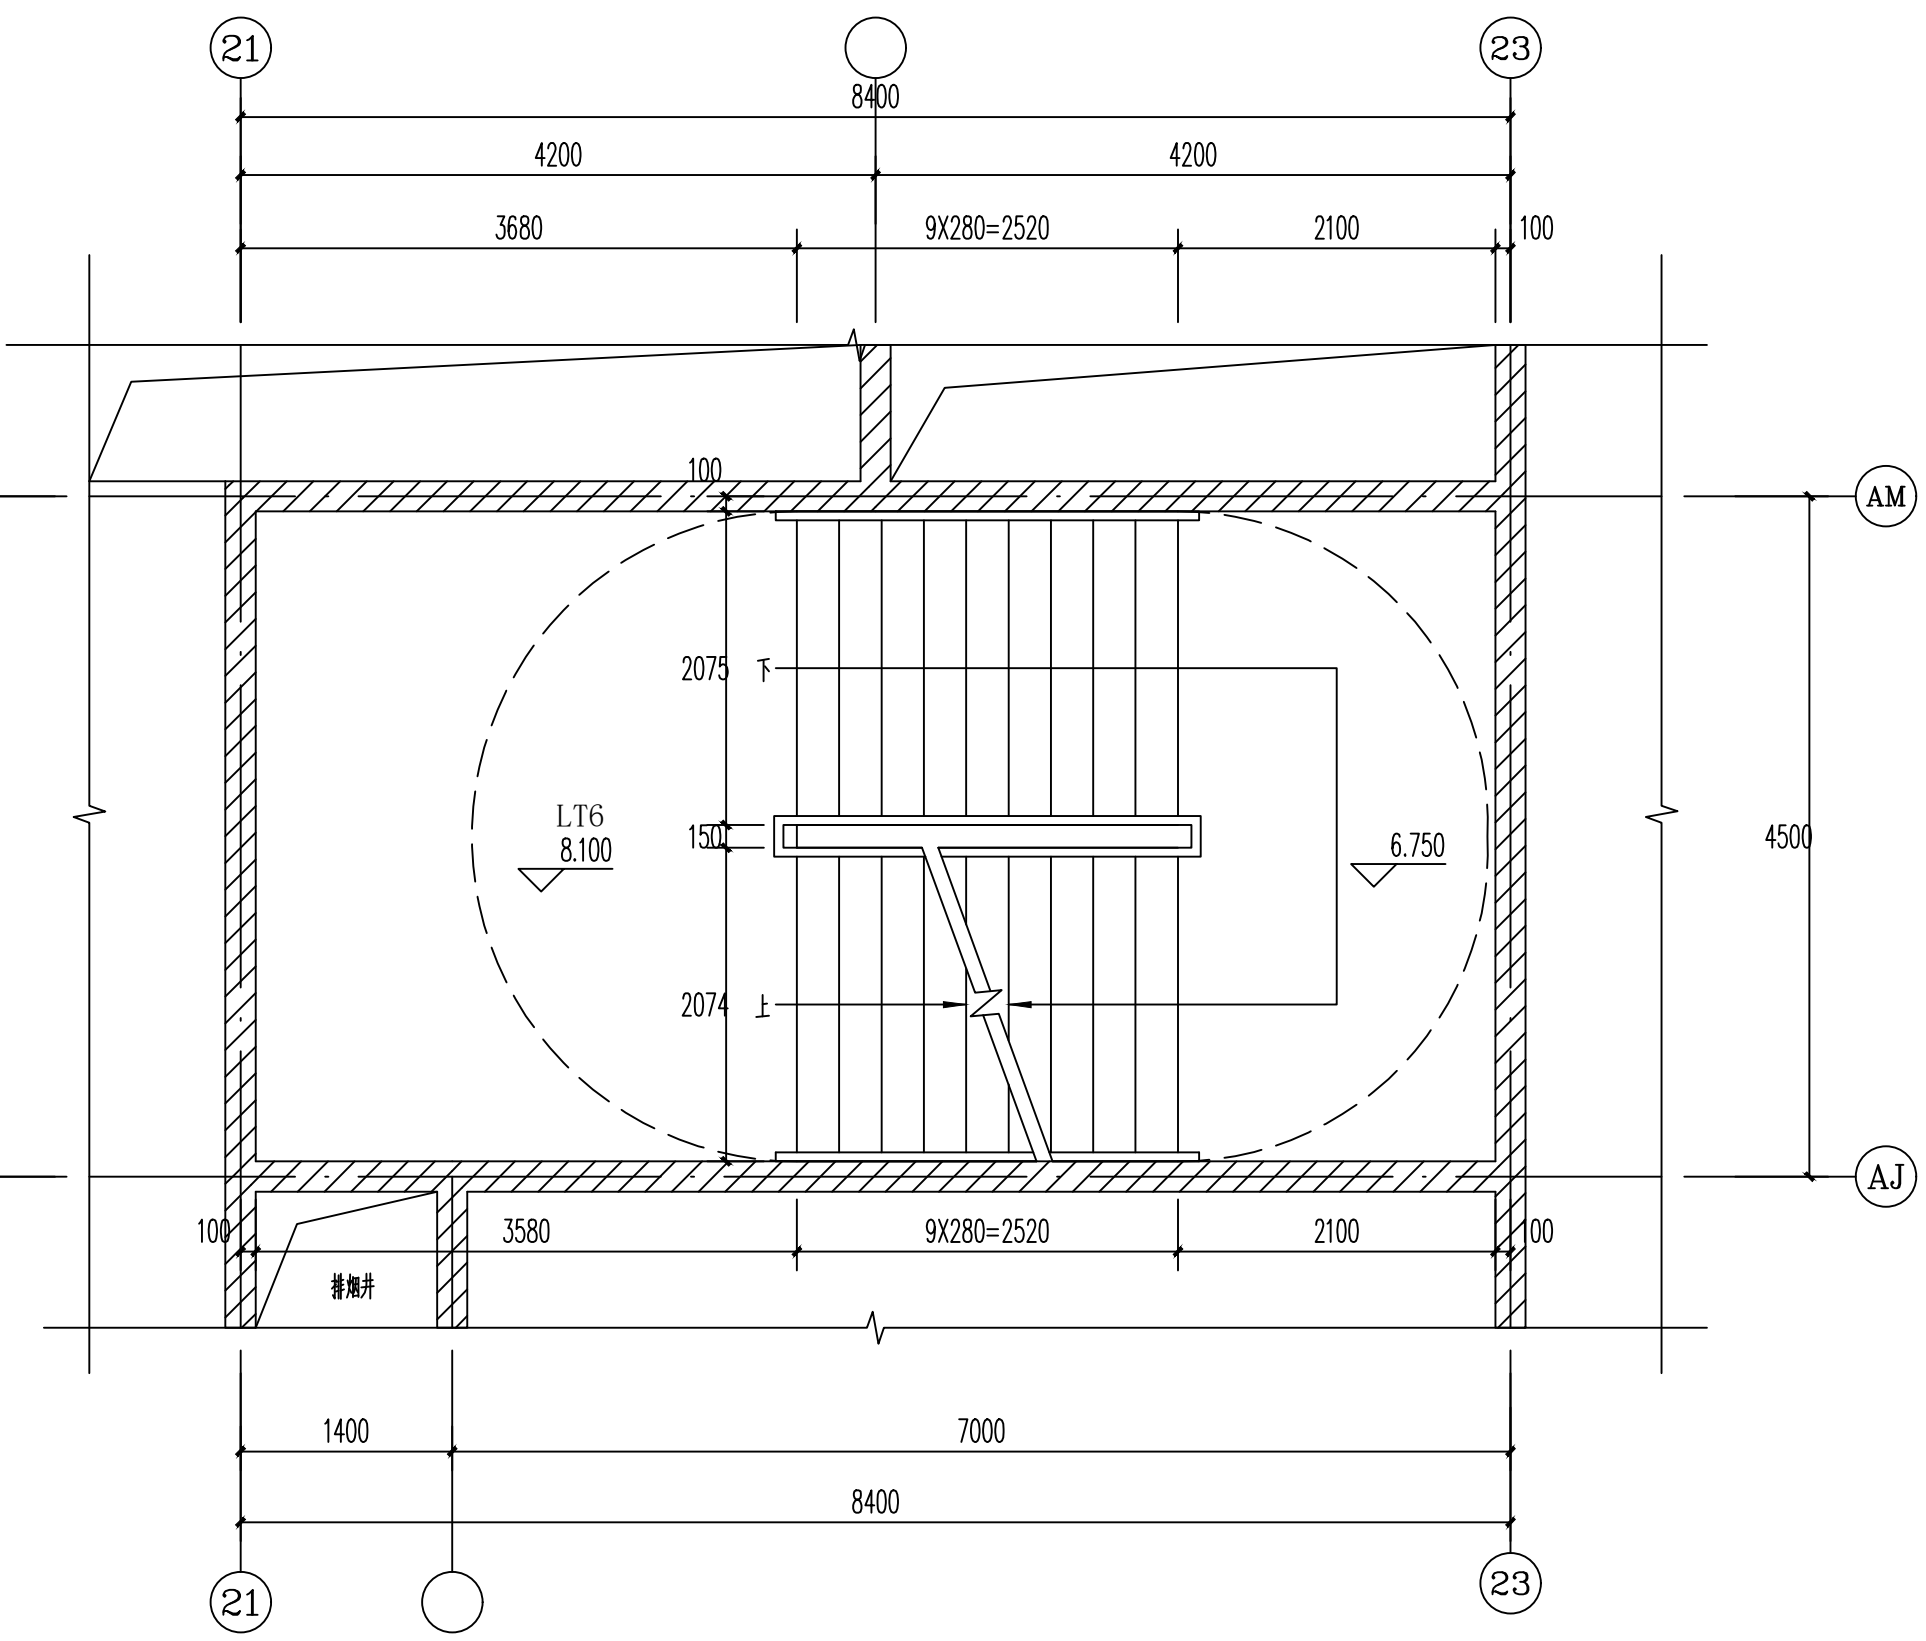


LT7楼梯间H=8.100处平面图 1:50

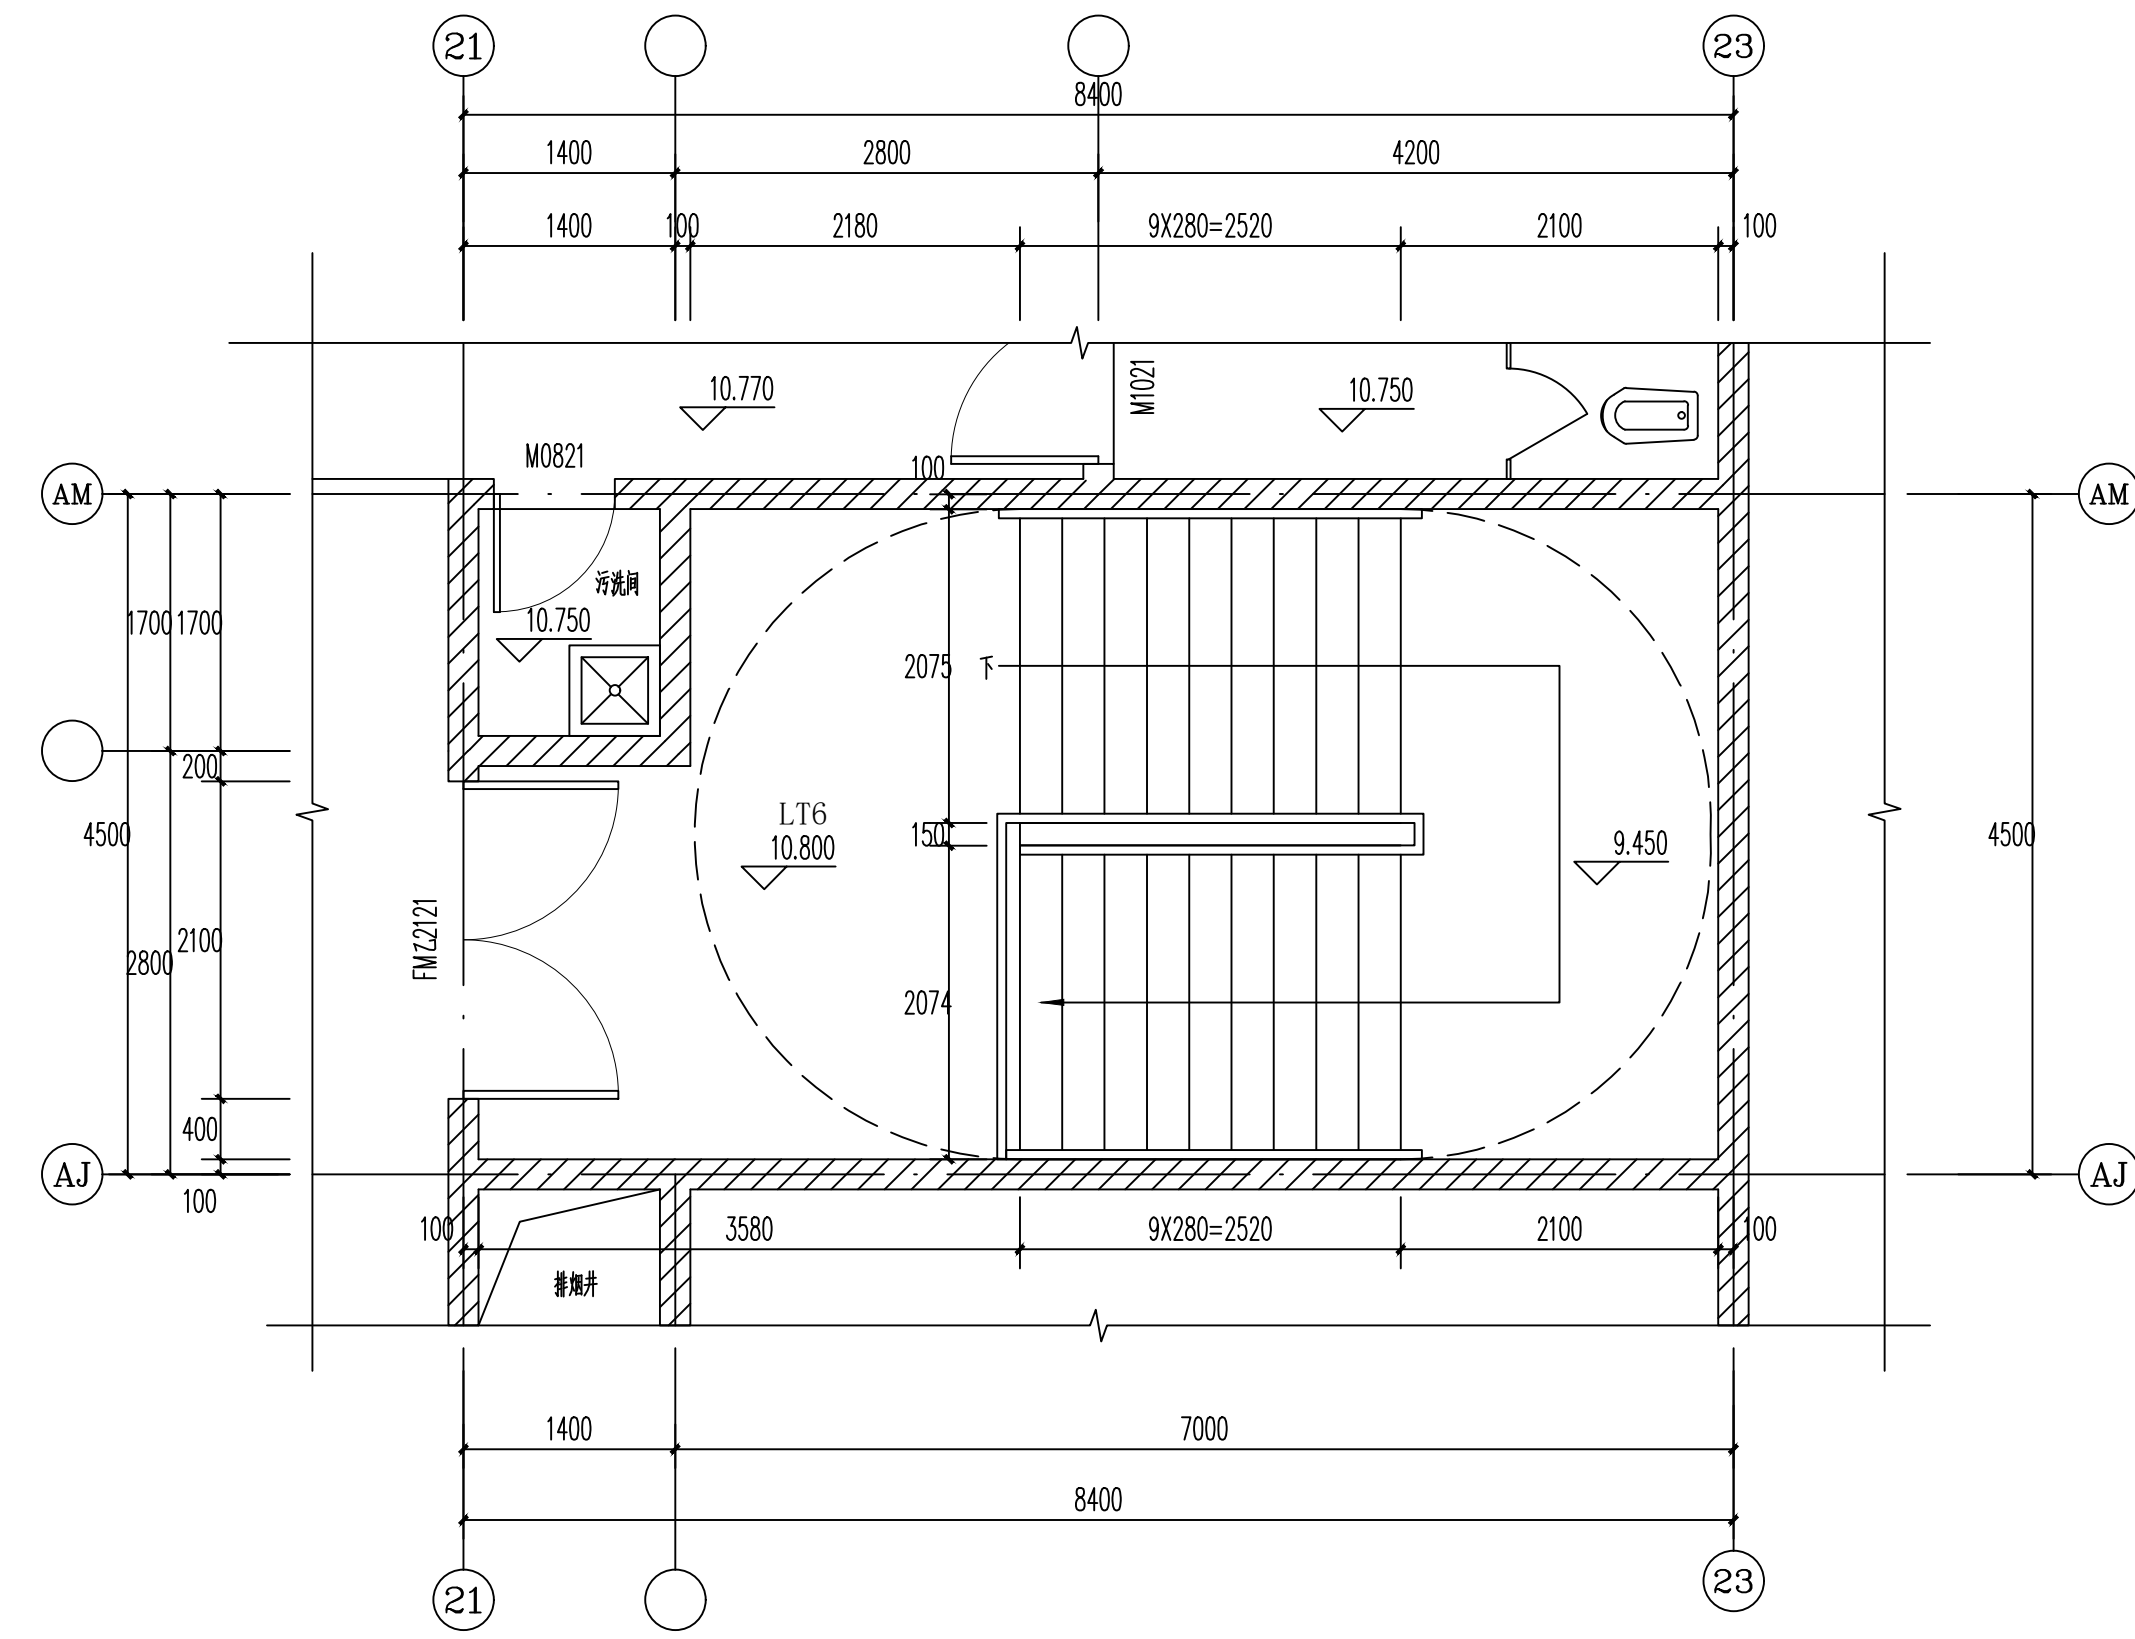


LT7楼梯间三层平面图 1:50

LT7楼梯间屋顶风井平面图详JS-28

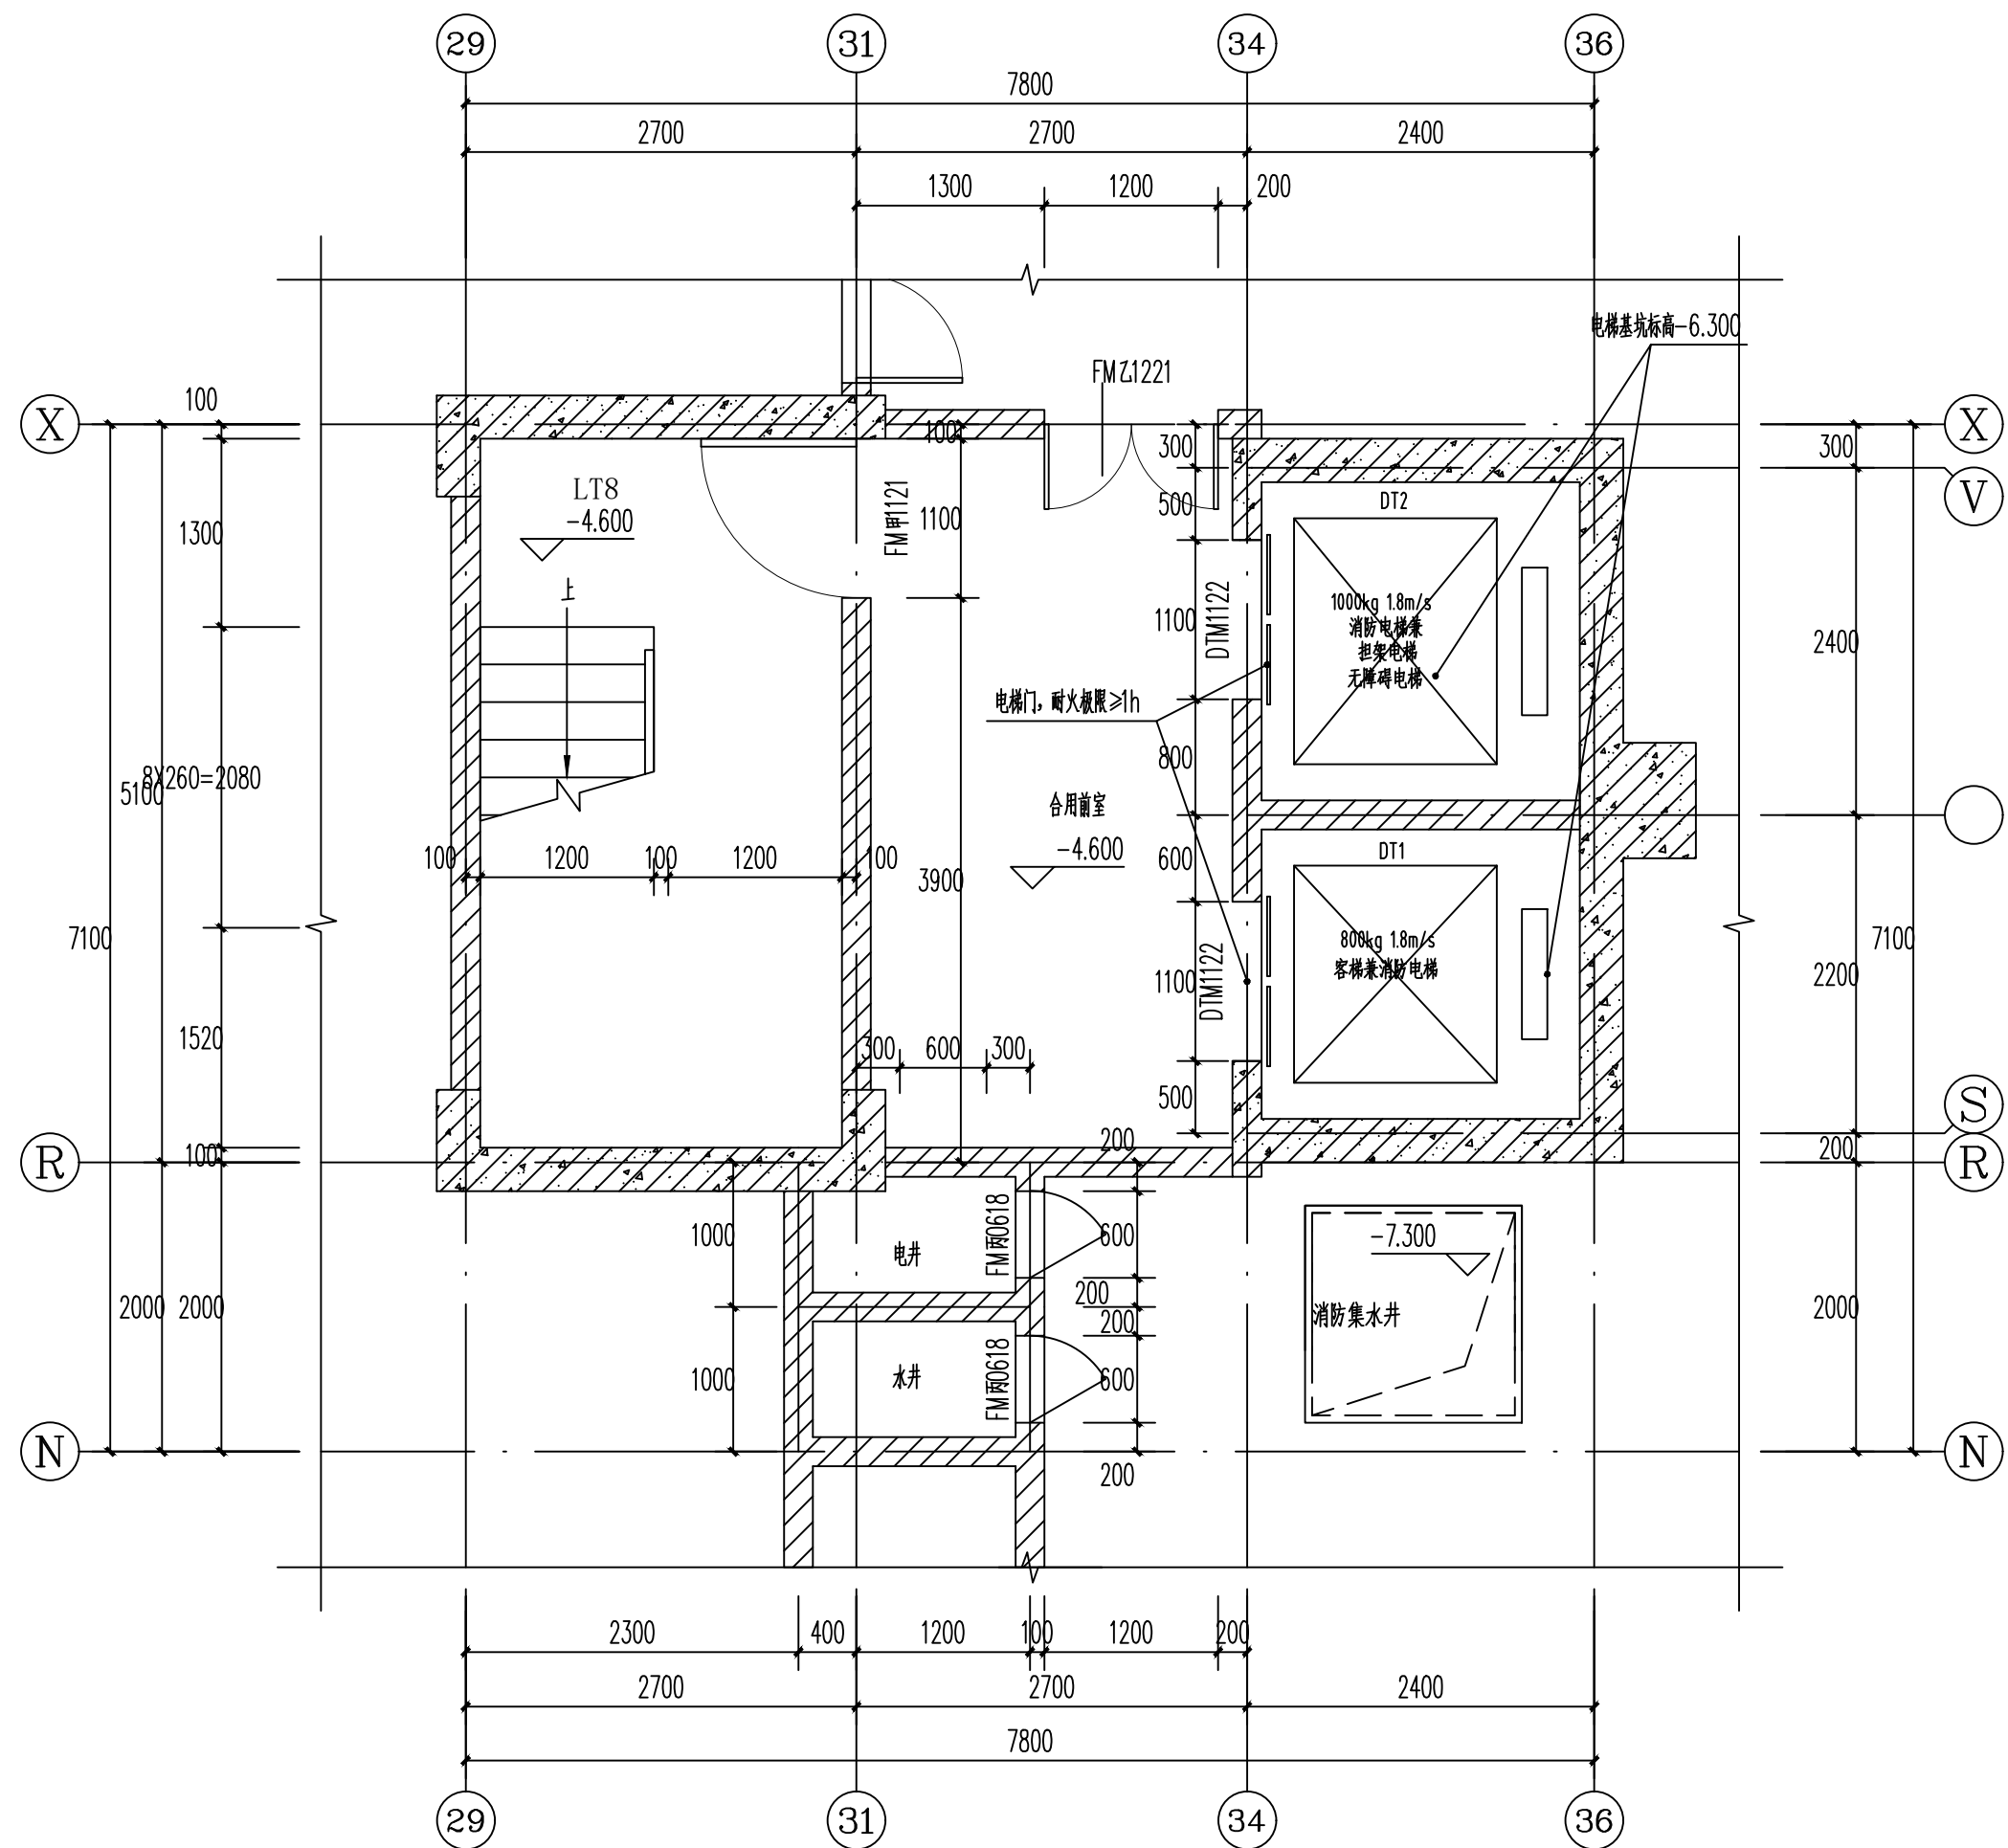

LT8楼梯间负一层平面图 1:50

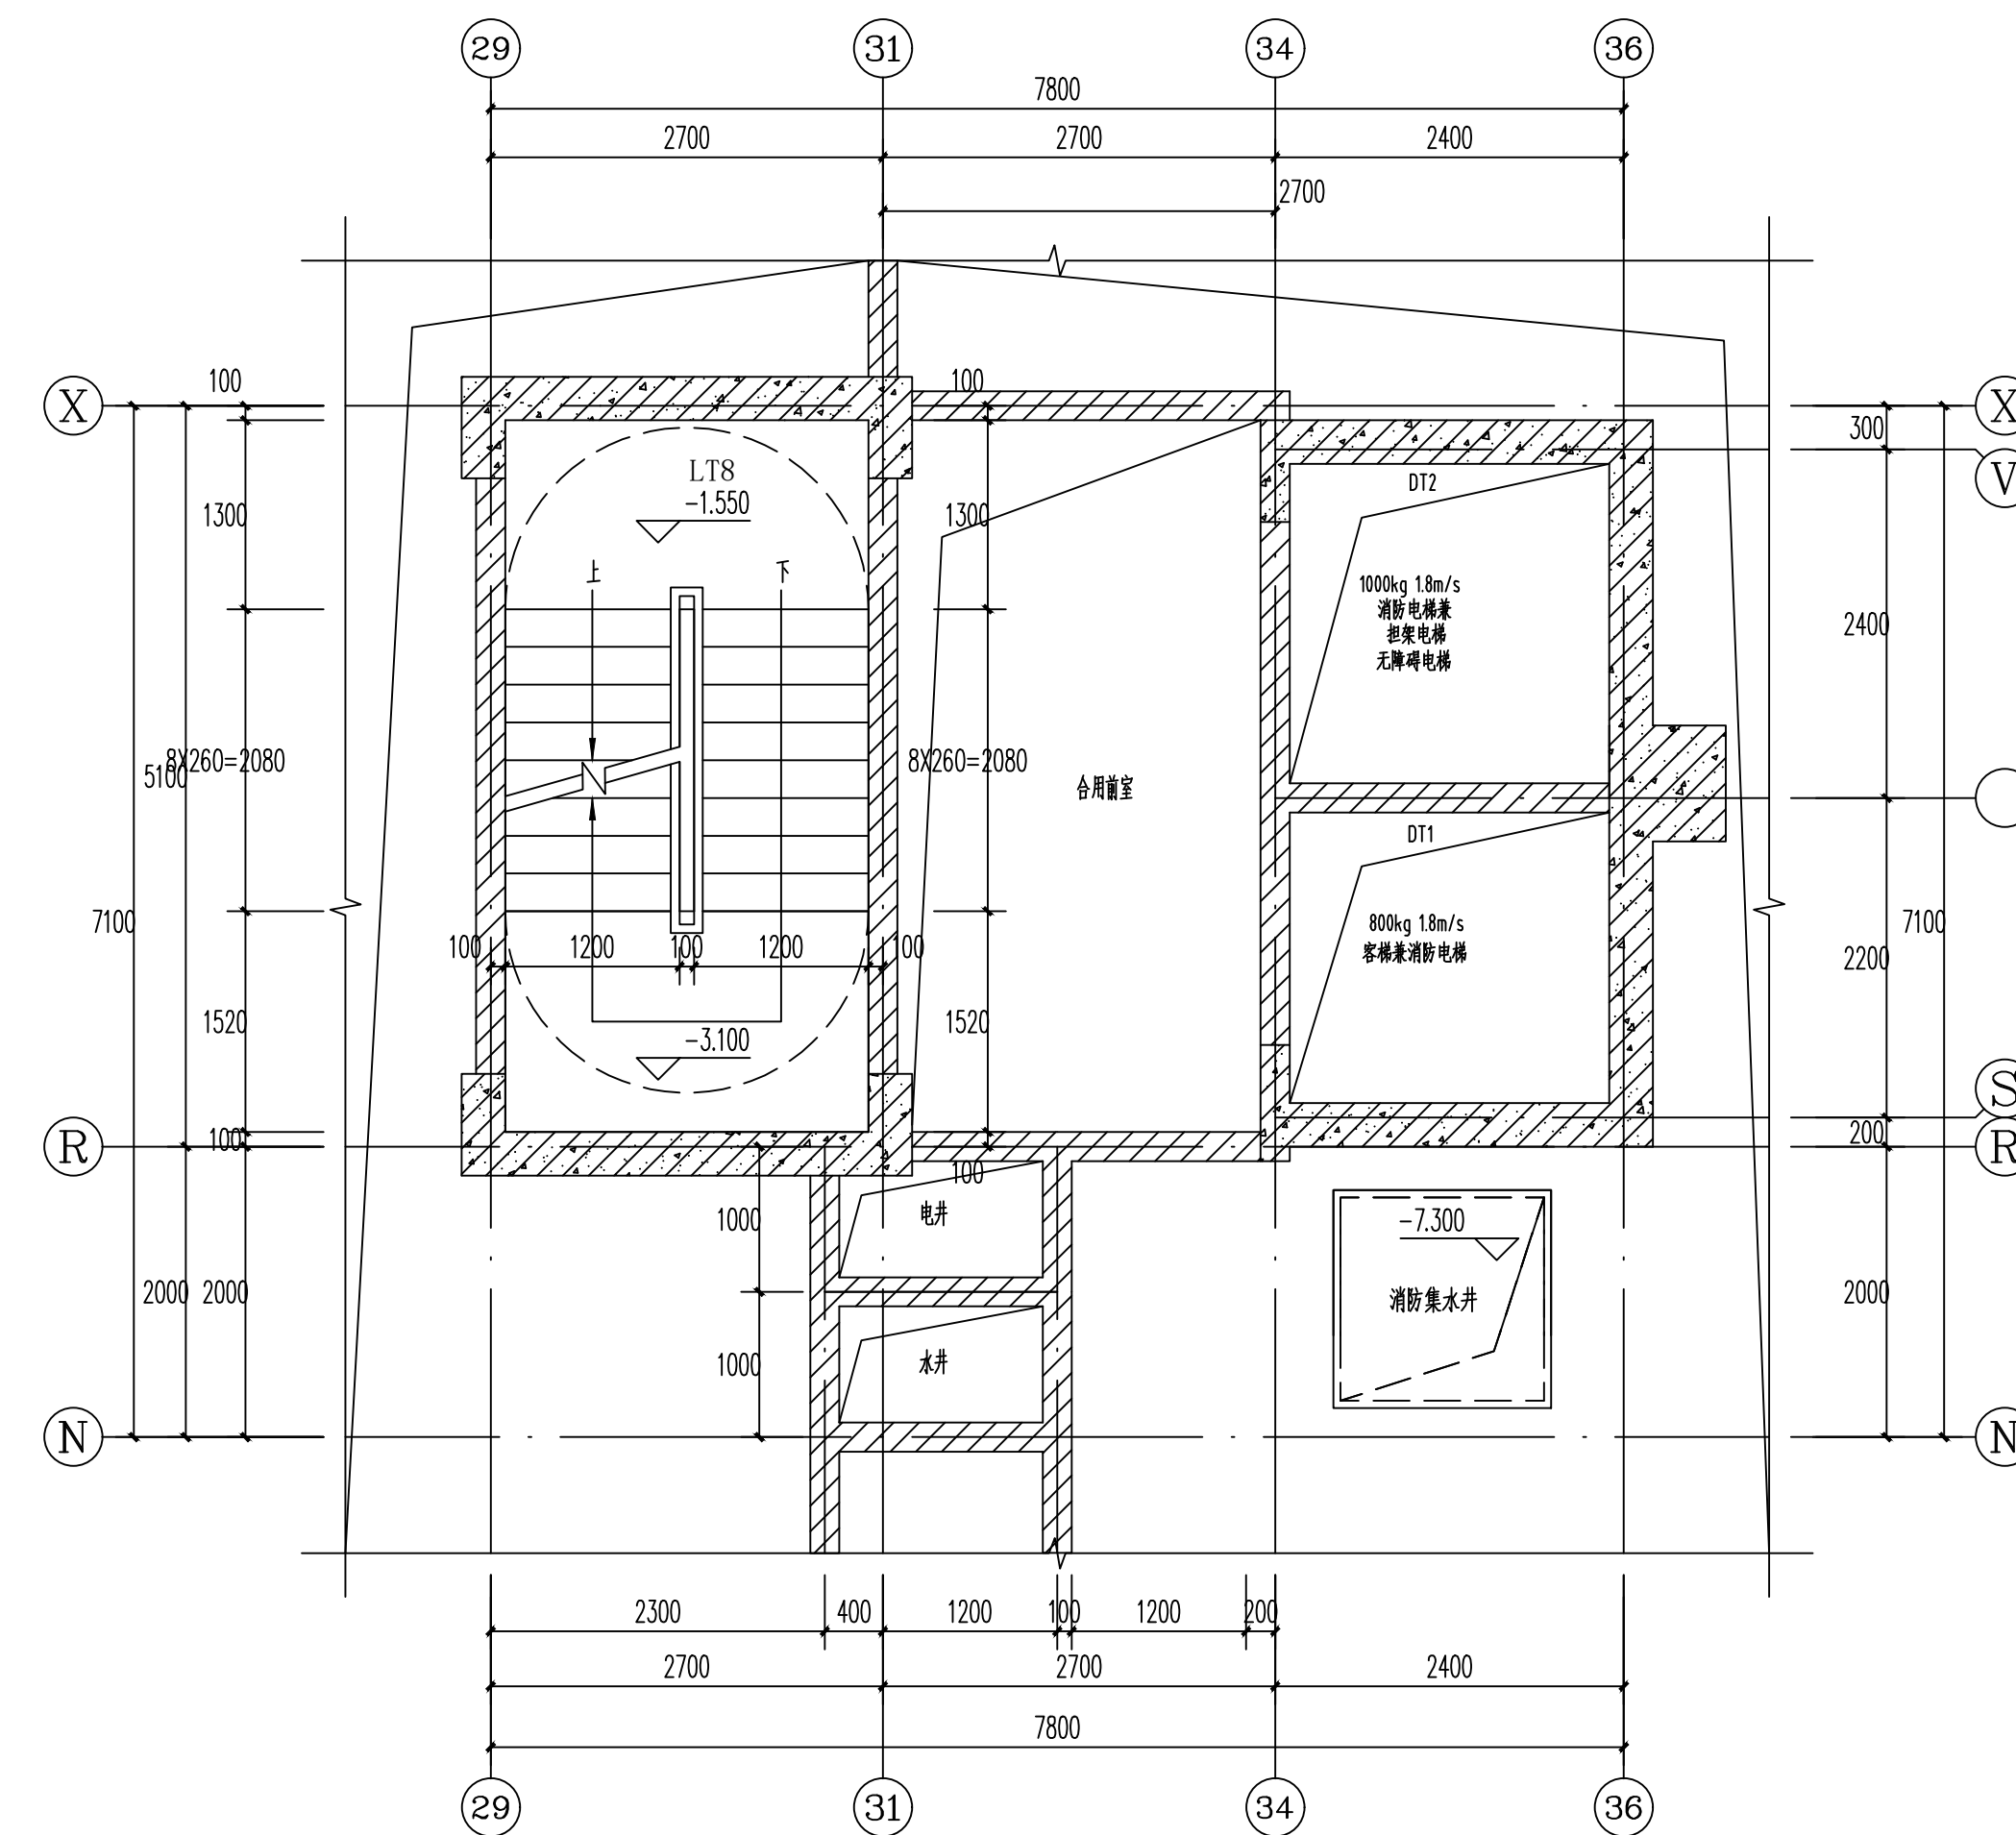

LT8楼梯间H=-1.550处平面图 1:50

|                                                                                     |
|-------------------------------------------------------------------------------------|
| 建设单位/CLIENT:                                                                        |
| 麻阳苗族自治县远桥房地产开发有限公司                                                                  |
| 项目名称/PROJECT:                                                                       |
| 远程国际                                                                                |
| 子项目名称/SUB-PROJECT:                                                                  |
| 远程国际                                                                                |
| 区位图/REGIONAL LOCATION MAP :                                                         |
|  |
| 图纸名称/TITLE:                                                                         |
| LT7楼梯间大样图                                                                           |
| LT8楼梯间大样图一                                                                          |

|                                                                  |
|------------------------------------------------------------------|
| 项目名称/PROJECT:                                                    |
| 远程国际                                                             |
| 设计<br>DESIGNED                                                   |
| 校对<br>CHECKED                                                    |
| 专业负责人<br>CHIEF                                                   |
| 项目负责人<br>PROJECT CHIEF                                           |
| 审核<br>IDENTIFIED                                                 |
| 审定<br>APPROVED                                                   |
| 业务号/JOB NO.                                                      |
| 设计阶段/STATUS: 施工图                                                 |
| 专业/DISCIPLINE: 建筑                                                |
| 比例/<br>SCALE:                                                    |
| 1: 100                                                           |
| 规格/<br>SIZE:                                                     |
| A1                                                               |
| 出图日期/DATE: 2021.06                                               |
| 图号/DRAWING NO. JS-34                                             |
| 版次<br>NO.                                                        |
| 修改内容<br>DESCRIPTION                                              |
| 日期<br>DATE                                                       |
| 条形码/BARCODE:                                                     |
| 版权所有, 不得复制、套用。<br>ALL RIGHTS RESERVED, DON'T COPIED, REPRODUCED. |