




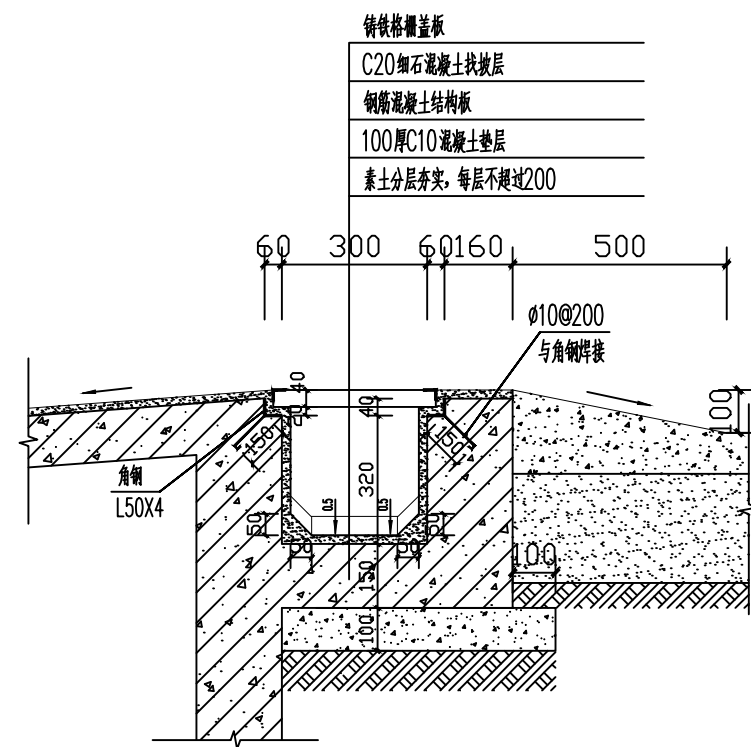


① 车道室外地面截水沟大样 1:25

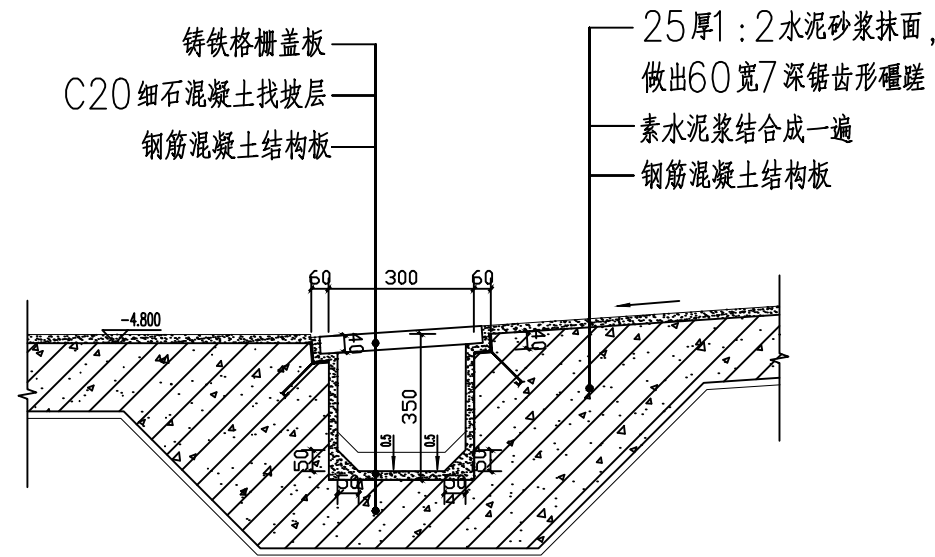


② 车道室内地面截水沟大样 1:25

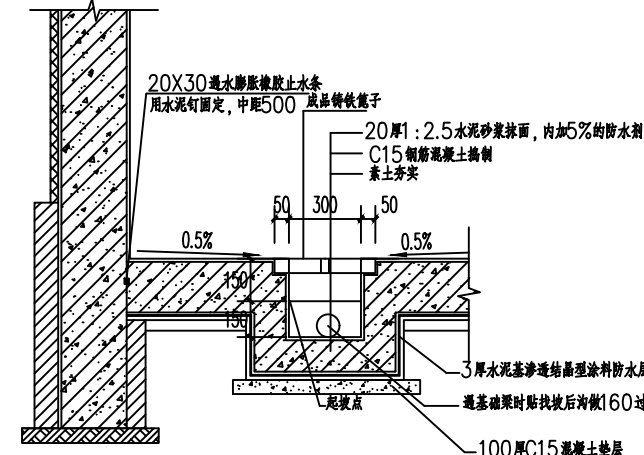


③ 300宽排水沟大样 1:25

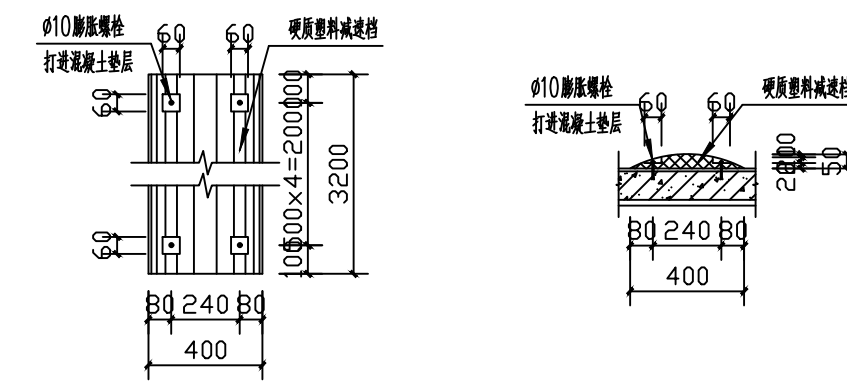


④ 塑料减速档 1:25

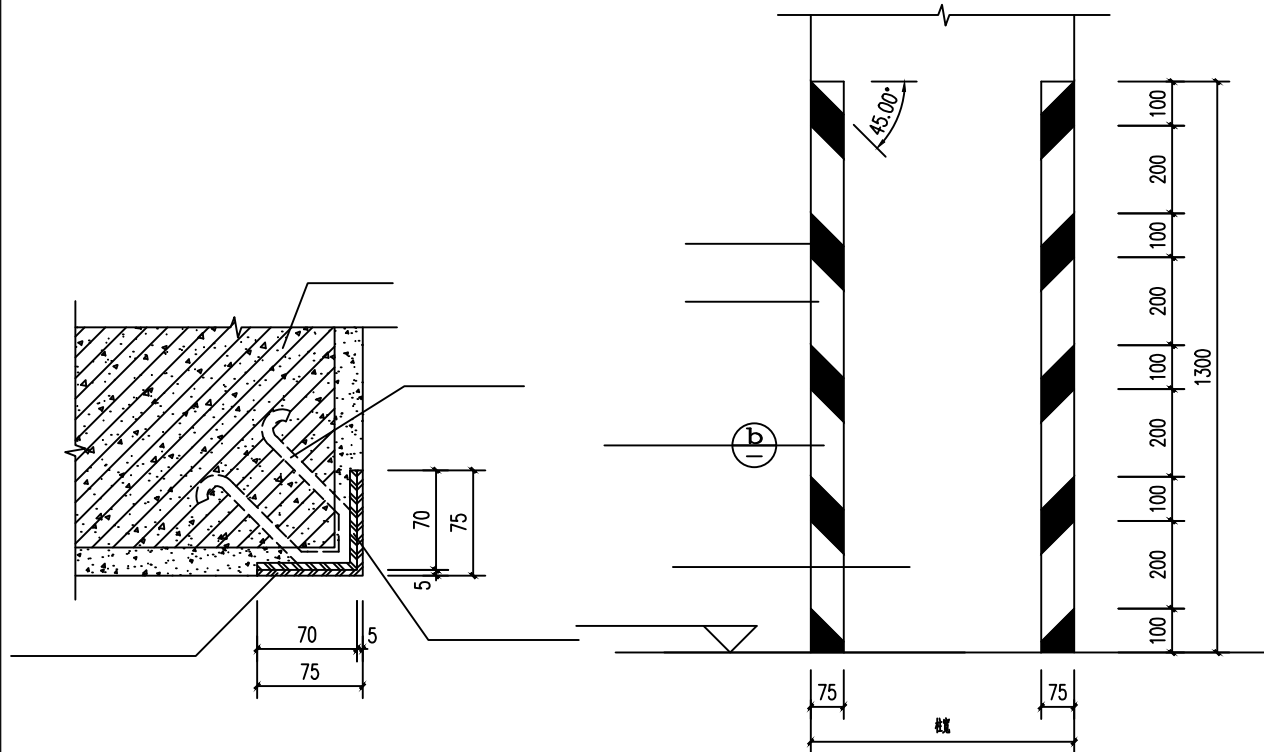

⑤ 车库墙柱防撞保护节点 1:5

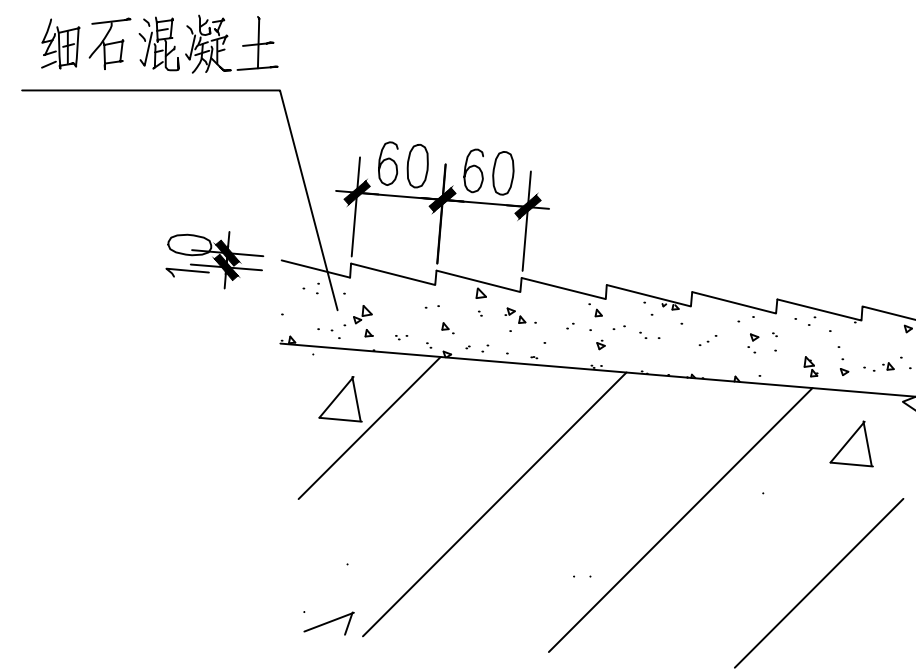


⑥ 车道防滑礅碯详图 1:5

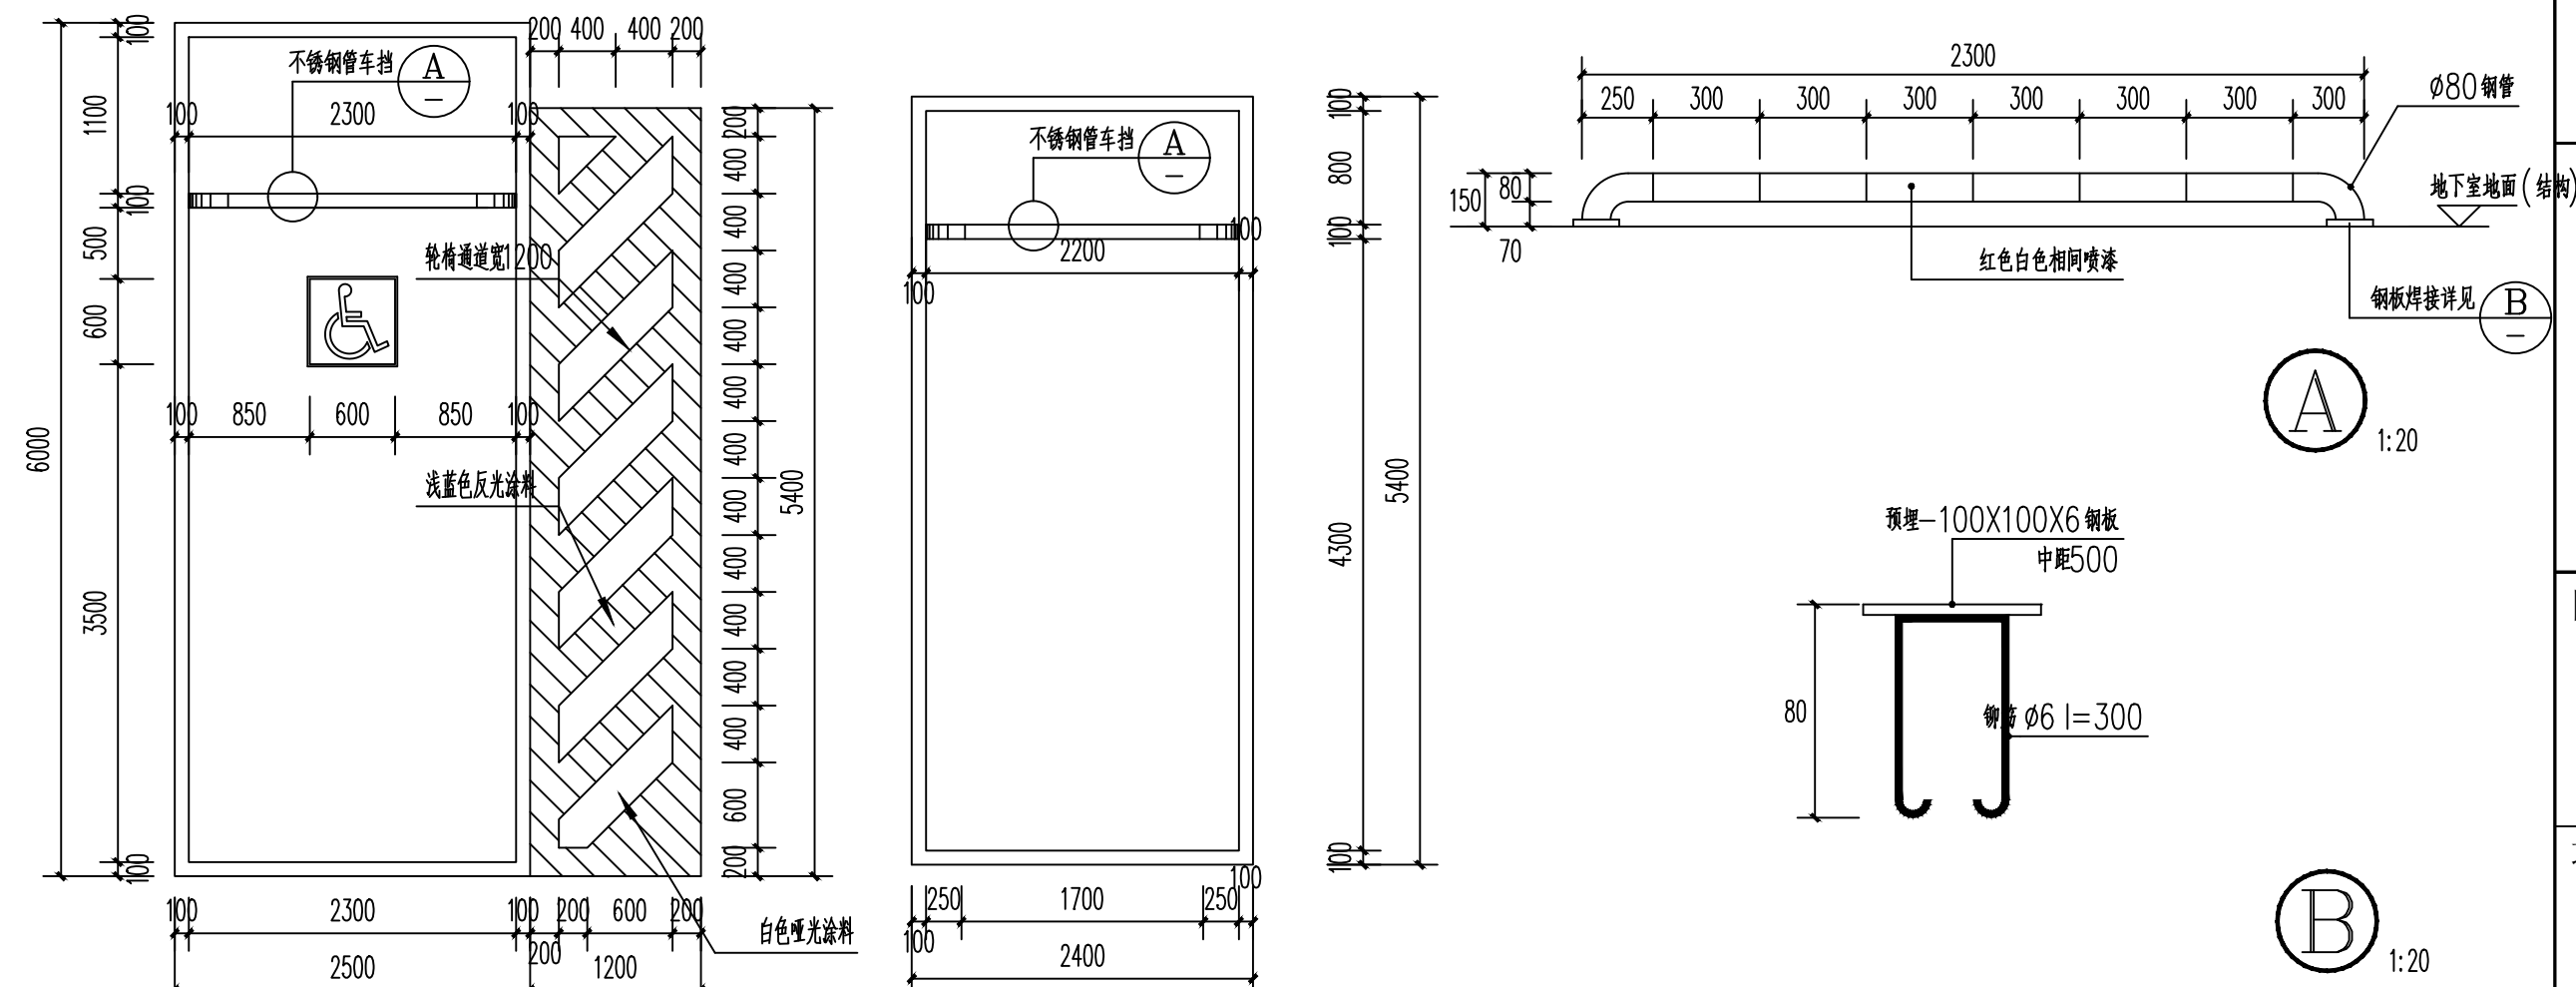


⑦ 无障碍停车位 1:50

⑧普通停车位 1:50

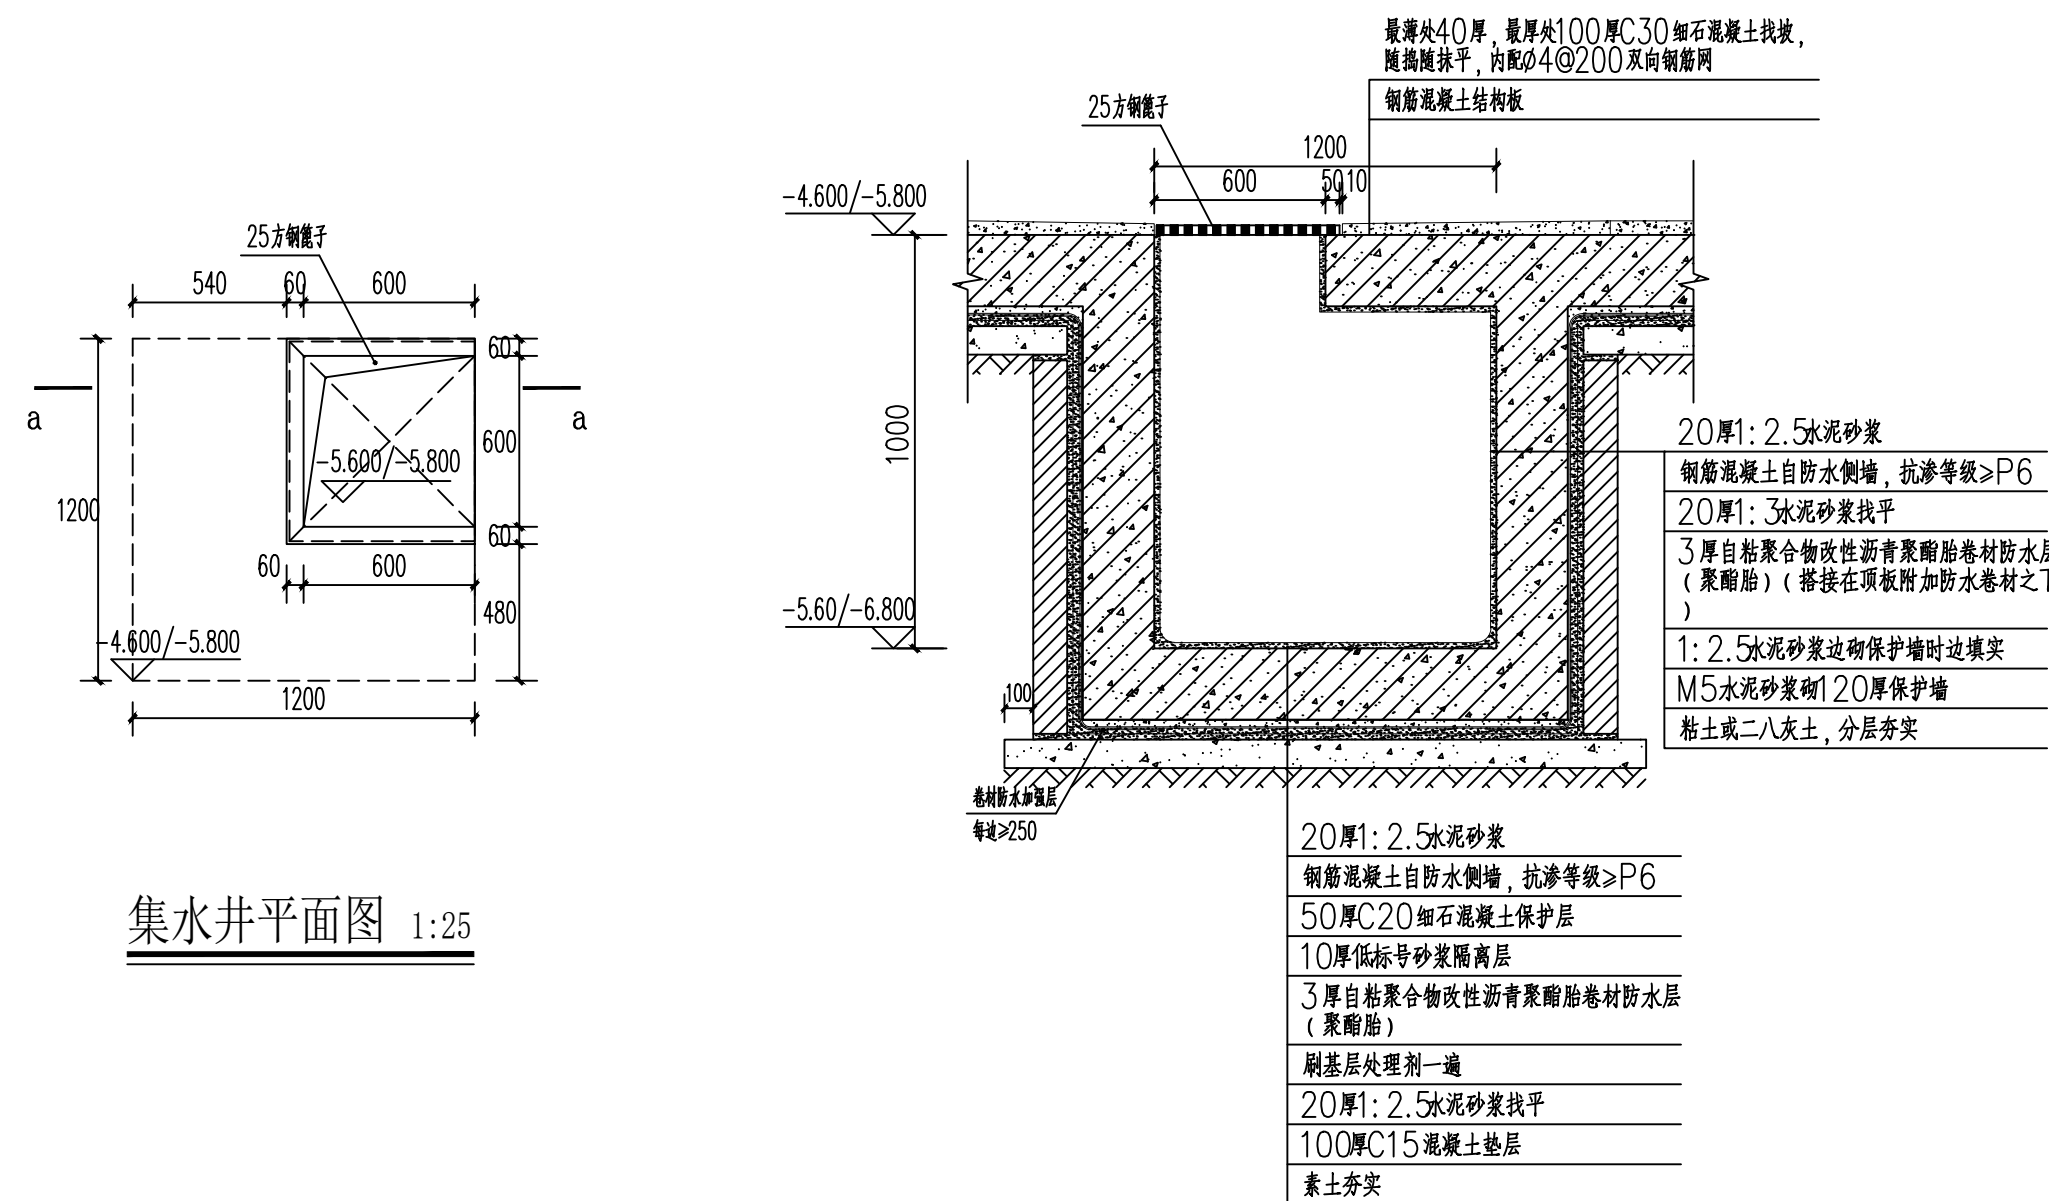

⑨ 集水井大样图 1:25

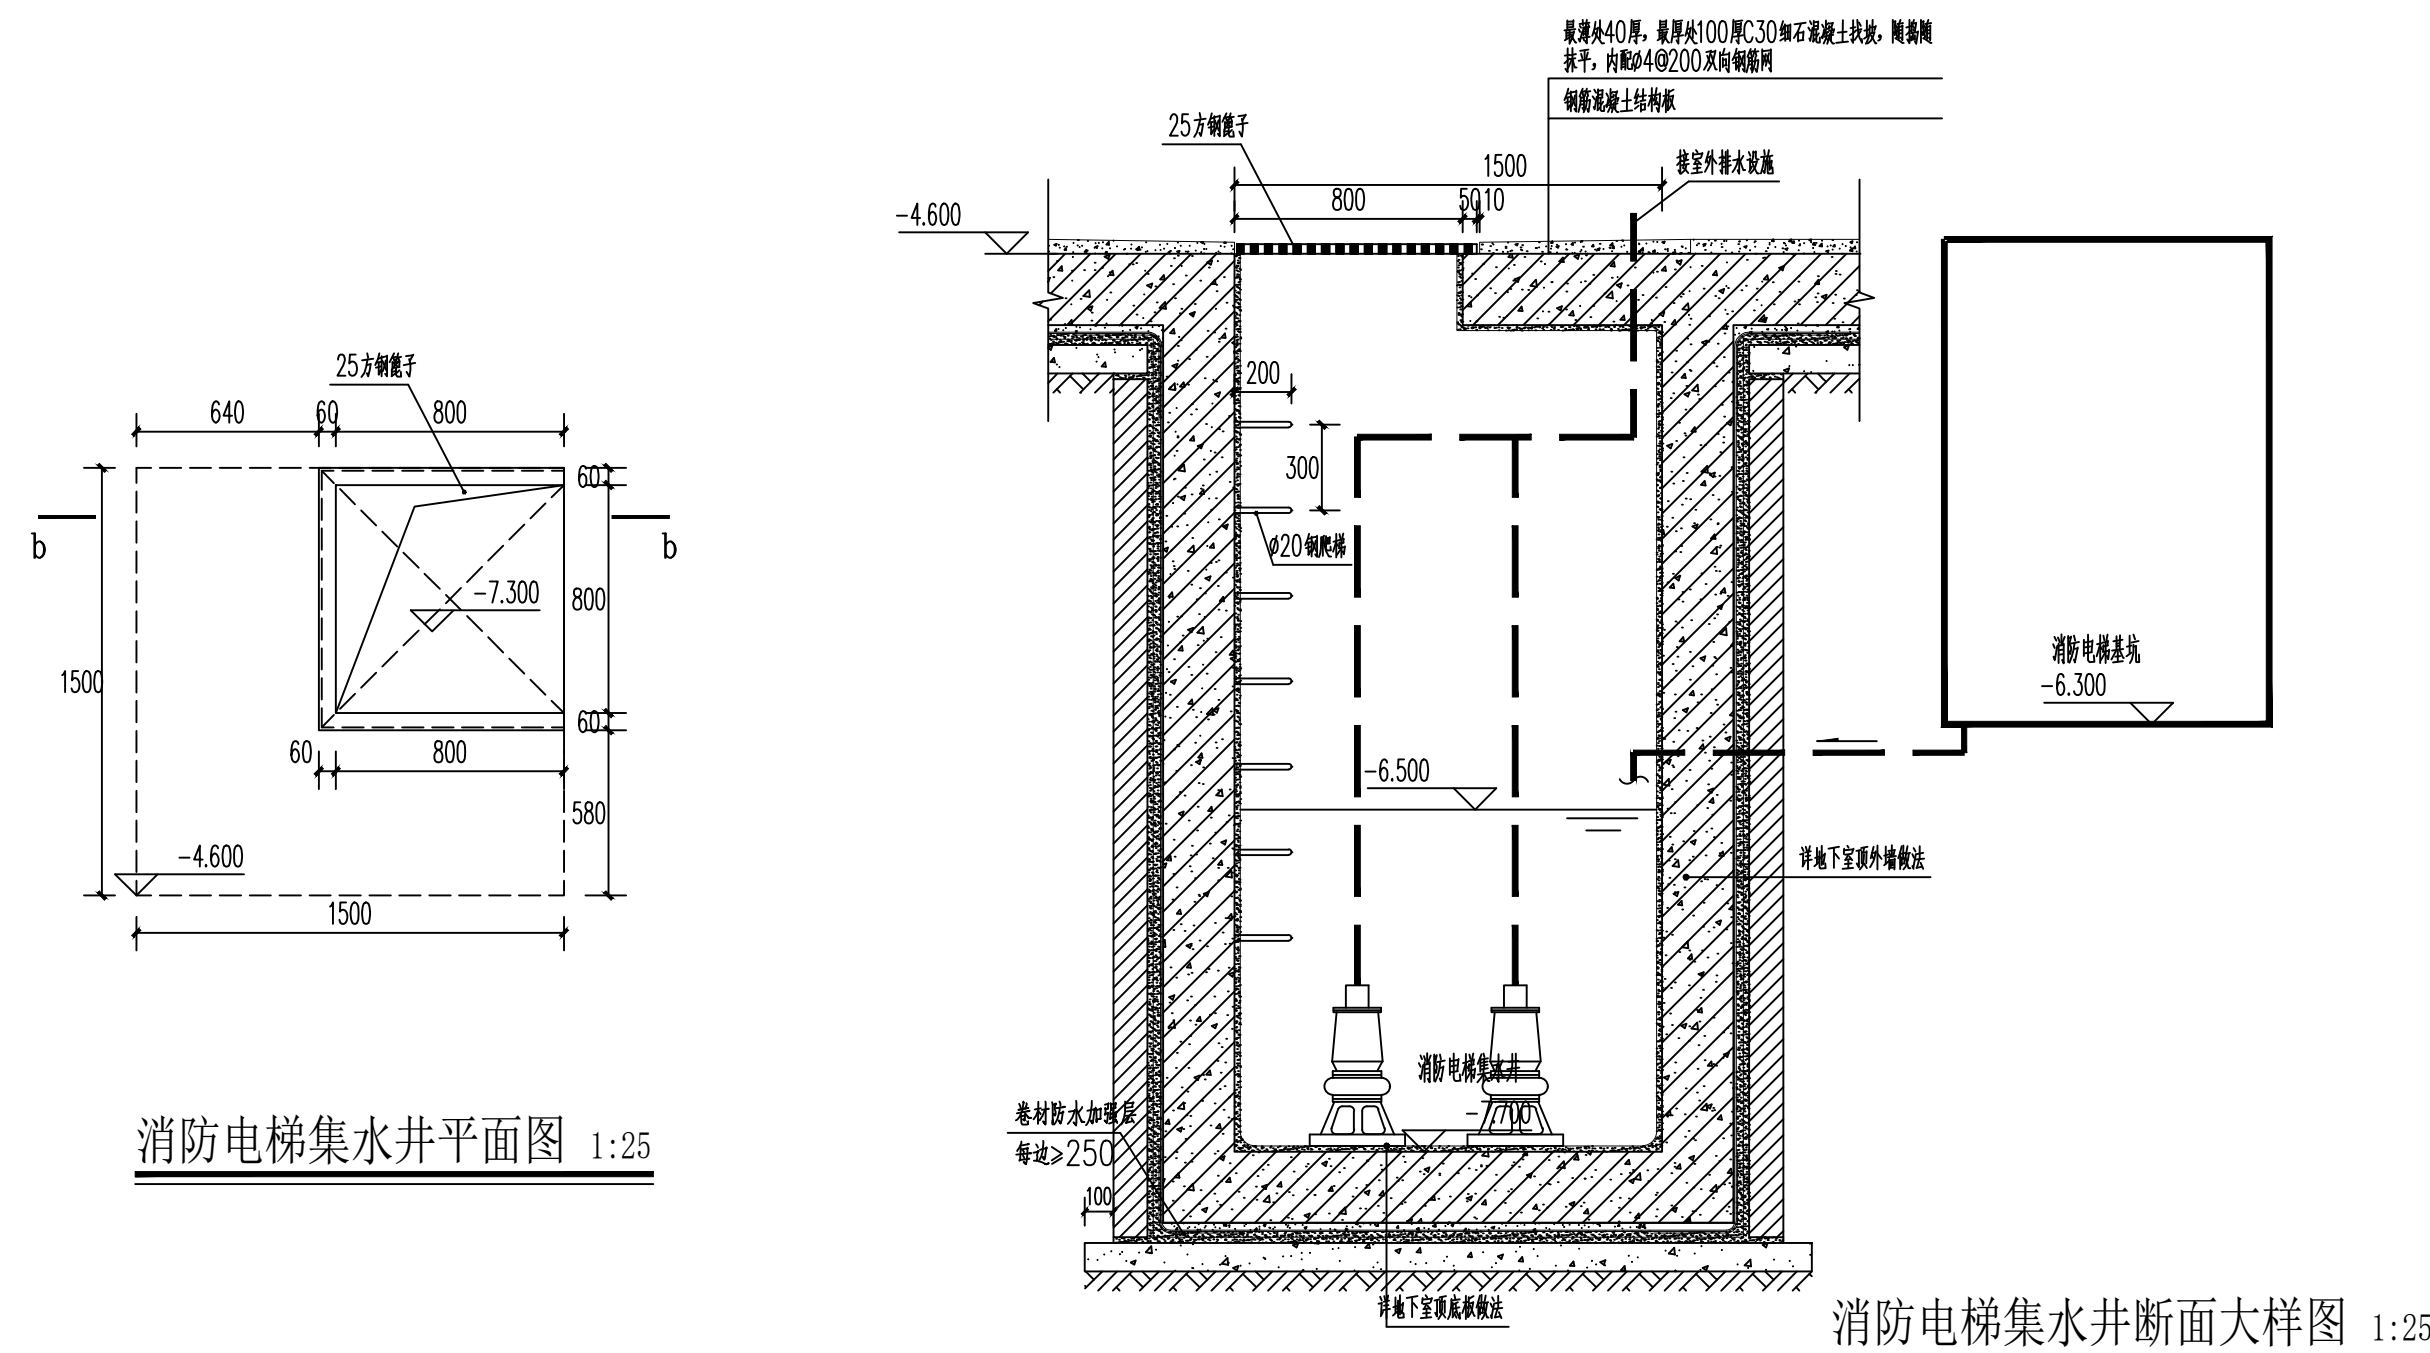

⑩消防电梯集水井大样图 1:25

建设单位/CLIENT:

麻阳苗族自治县远桥房地产开发有限公司

|                       |
|-----------------------|
| 项目名称/PROJECT:<br>远程国际 |
|-----------------------|

|                    |
|--------------------|
| 子项目名称/SUB-PROJECT: |
| 远程国际               |

区位图/REGIONAL LOCATION MAP :

|                               |
|-------------------------------|
| 图纸名称/TITLE:<br><br><br>节点大样图二 |
|-------------------------------|

|               |      |
|---------------|------|
| 项目名称/PROJECT: | 远程国际 |
|---------------|------|

|                        |     |                                                                                       |
|------------------------|-----|---------------------------------------------------------------------------------------|
| 设计<br>DESIGNED         | 古新辉 |  |
| 校对<br>CHECKED          | 吴新红 |  |
| 专业负责人<br>CHIEF         | 吴志刚 |  |
| 项目负责人<br>PROJECT CHIEF | 吴志刚 |  |
| 审核<br>IDENTIFIED       | 黄履优 |  |
| 审定<br>APPROVED         | 李 坚 |  |

业务号/JOB NO.

设计阶段/STATUS: 施工图

专业/DISCIPLINE: 建施

|               |        |              |    |
|---------------|--------|--------------|----|
| 比例/<br>SCALE: | 1: 100 | 规格/<br>SIZE: | A1 |
|---------------|--------|--------------|----|

|            |         |
|------------|---------|
| 出图日期/DATE: | 2021.06 |
|------------|---------|

图号/DRAWING NO. JS-41

| 版次<br>NO. | 修改内容<br>DESCRIPTION | 日期<br>DATE |
|-----------|---------------------|------------|
|           |                     |            |
|           |                     |            |

条形码/BARCODE:

版权所有，不得复制、套用。  
ALL RIGHTS RESERVED, DON'T COPIED, REPRODUCED.