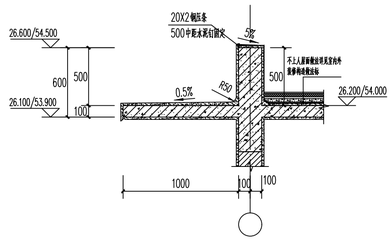
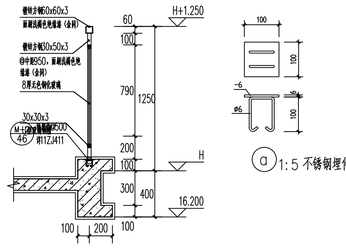


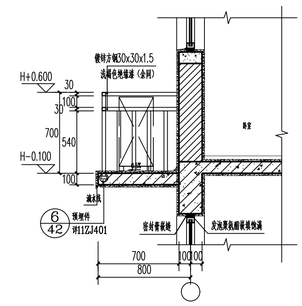

① 返边大样图 1:25



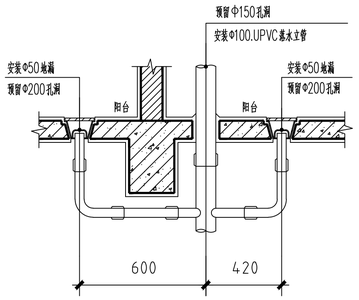

② 雨蓬大样图 1:25



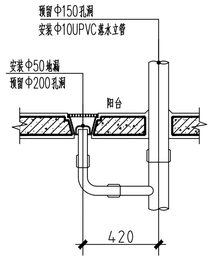

③ 阳台栏杆大样图 1:25



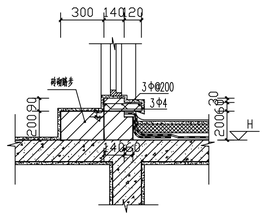

④ 空调板大样图 1:25



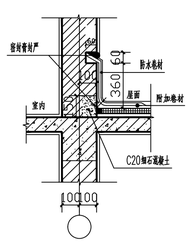

⑤ 双阳台排水大样图 1:25



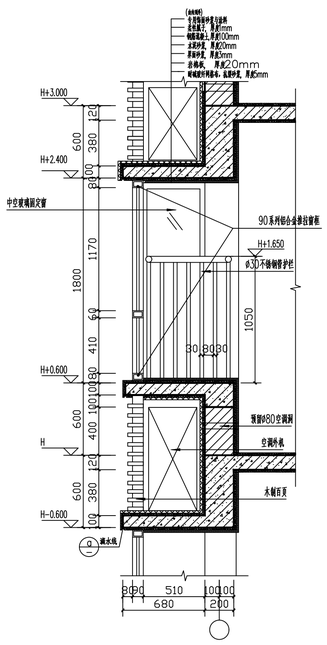

⑥ 单阳台排水大样图 1:25



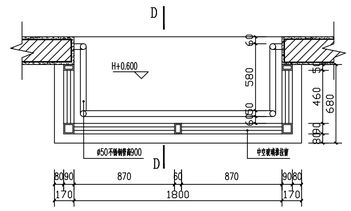

⑦ 屋顶出入口大样图 1:25



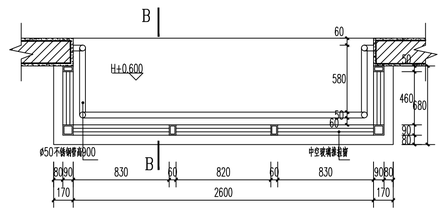

⑧ 屋面泛水大样图 1:25



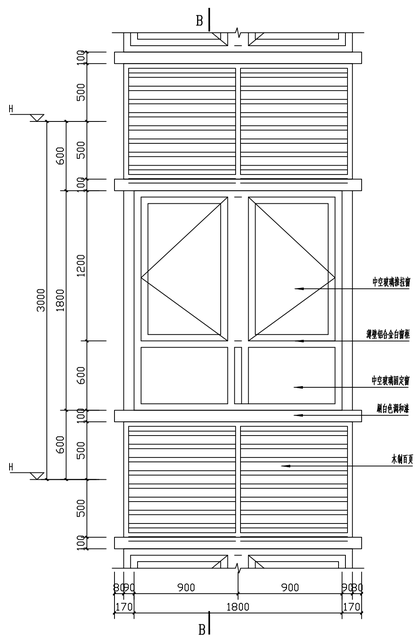

B-B剖面图 1:20




TC1平面图 1:20

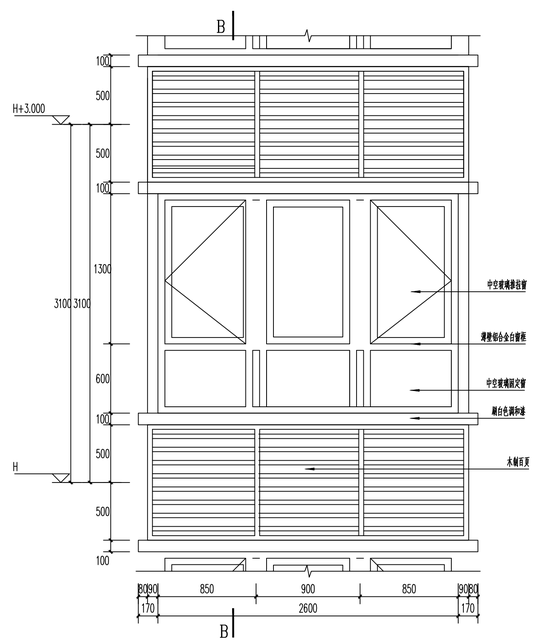



TC2平面图 1:20




TC1立面 1:20

⑨ TC1大样图 1:20




TC2立面 1:20

⑩ TC2大样图 1:20

注：所有凸窗设置百叶帘遮阳系统，详11ZJ903 1/38

建设单位/CLIENT:

麻阳苗族自治县远桥房地产开发有限公司

项目名称/PROJECT:

远程国际

子项目名称/SUB-PROJECT:

远程国际

区位图/REGIONAL LOCATION MAP :

广东建筑艺术设计院有限公司
GUANGDONG ARCHITECTURAL ARTISTIC DESIGN INSTITUTE CO.,LTD

■ 建筑工程设计：甲级 ■ 风景园林设计：乙级
■ 城乡规划设计：乙级 ■ 市政设计：乙级

图纸名称/TITLE:

节点大样图三

项目名称/PROJECT:

远程国际

| | | |
|---|---|---|
| 设计 DESIGNED | 古新辉 | |
| 校对 CHECKED | 吴新红 | |
| 专业负责人 CHIEF | 吴志刚 | |
| 项目负责人 PROJECT CHIEF | 吴志刚 | |
| 审核 IDENTIFIED | 黄履优 | |
| 审定 APPROVED | 李 坚 | |

业务号/JOB NO.

设计阶段/STATUS: 施工图

专业/DISCIPLINE: 建施

| 比例/SCALE: | 1：100 | 规格/SIZE: | A1 |
|---|---|---|---|

出图日期/DATE: 2021.06

图号/DRAWING NO. JS-42

| 版次 NO. | 修改内容 DESCRIPTION | 日期 DATE |
|---|---|---|
| | | |
| | | |

条形码/BARCODE:

版权所有，不得复制、套用。
ALL RIGHTS RESERVED,DON'T COPIED,REPRODUCED.