
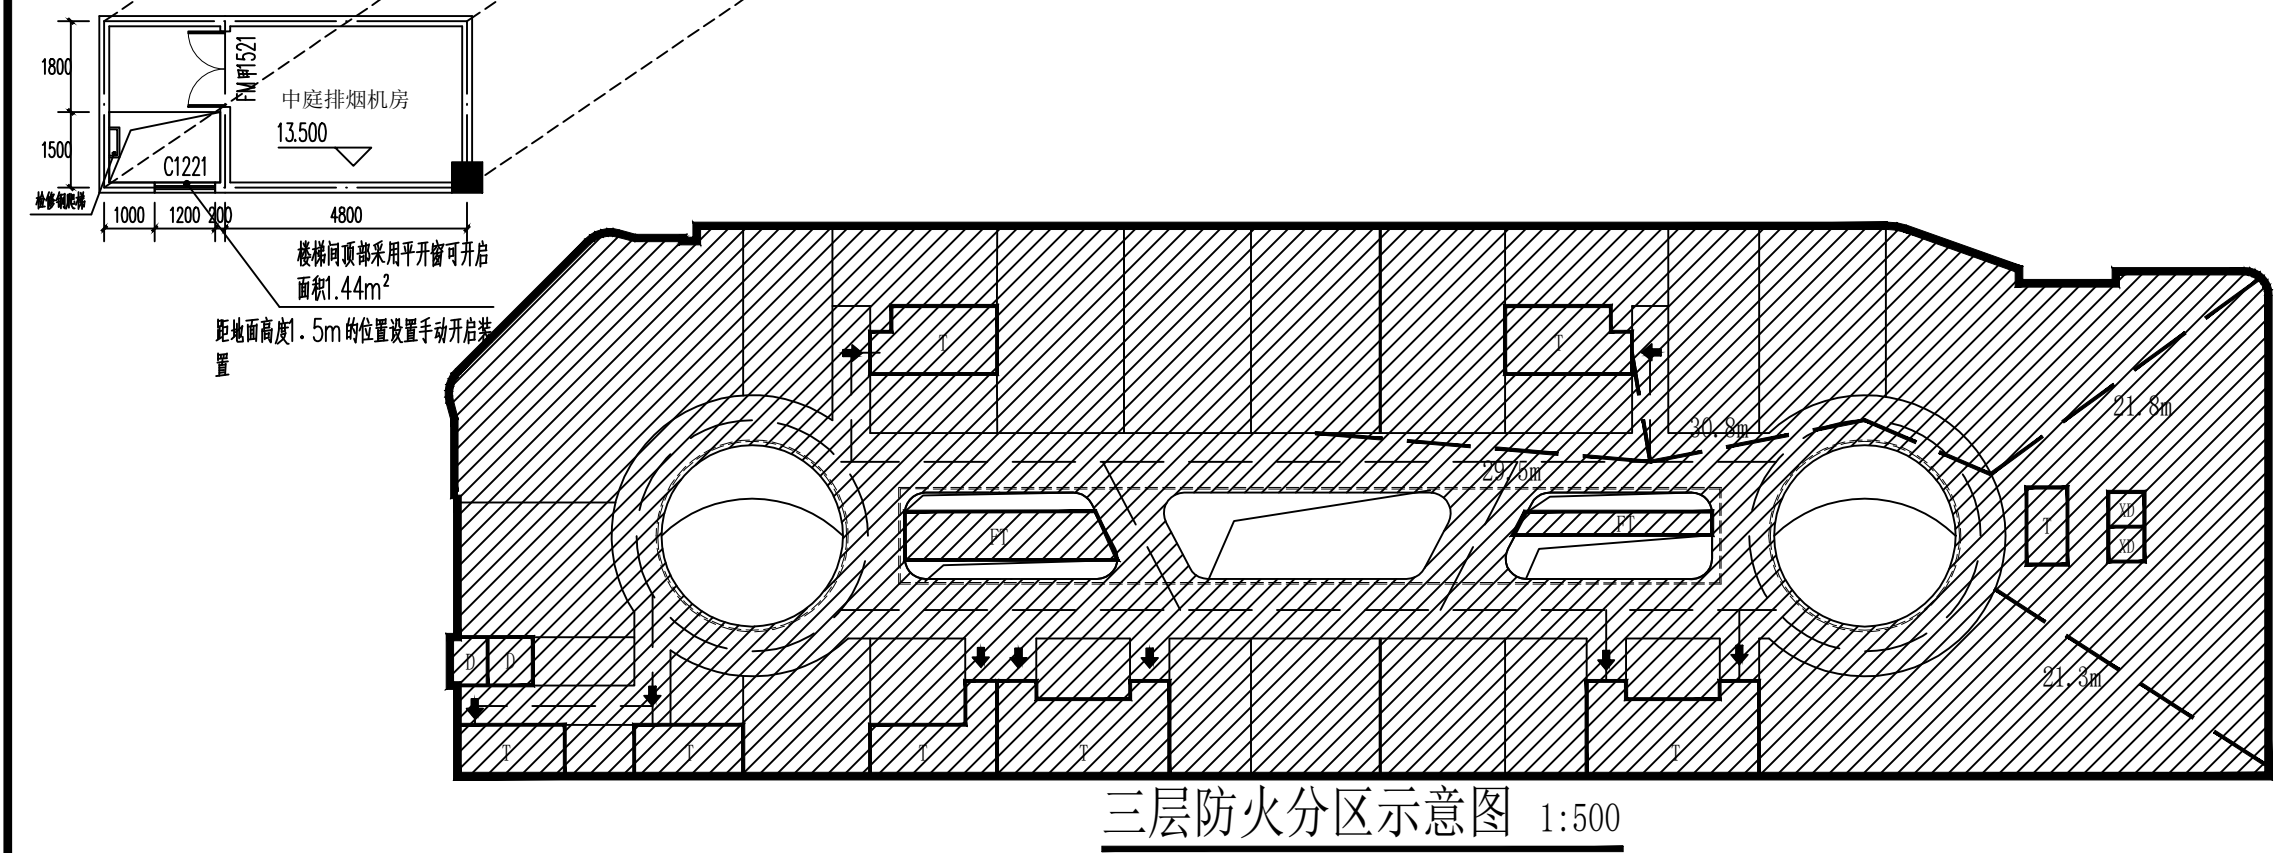


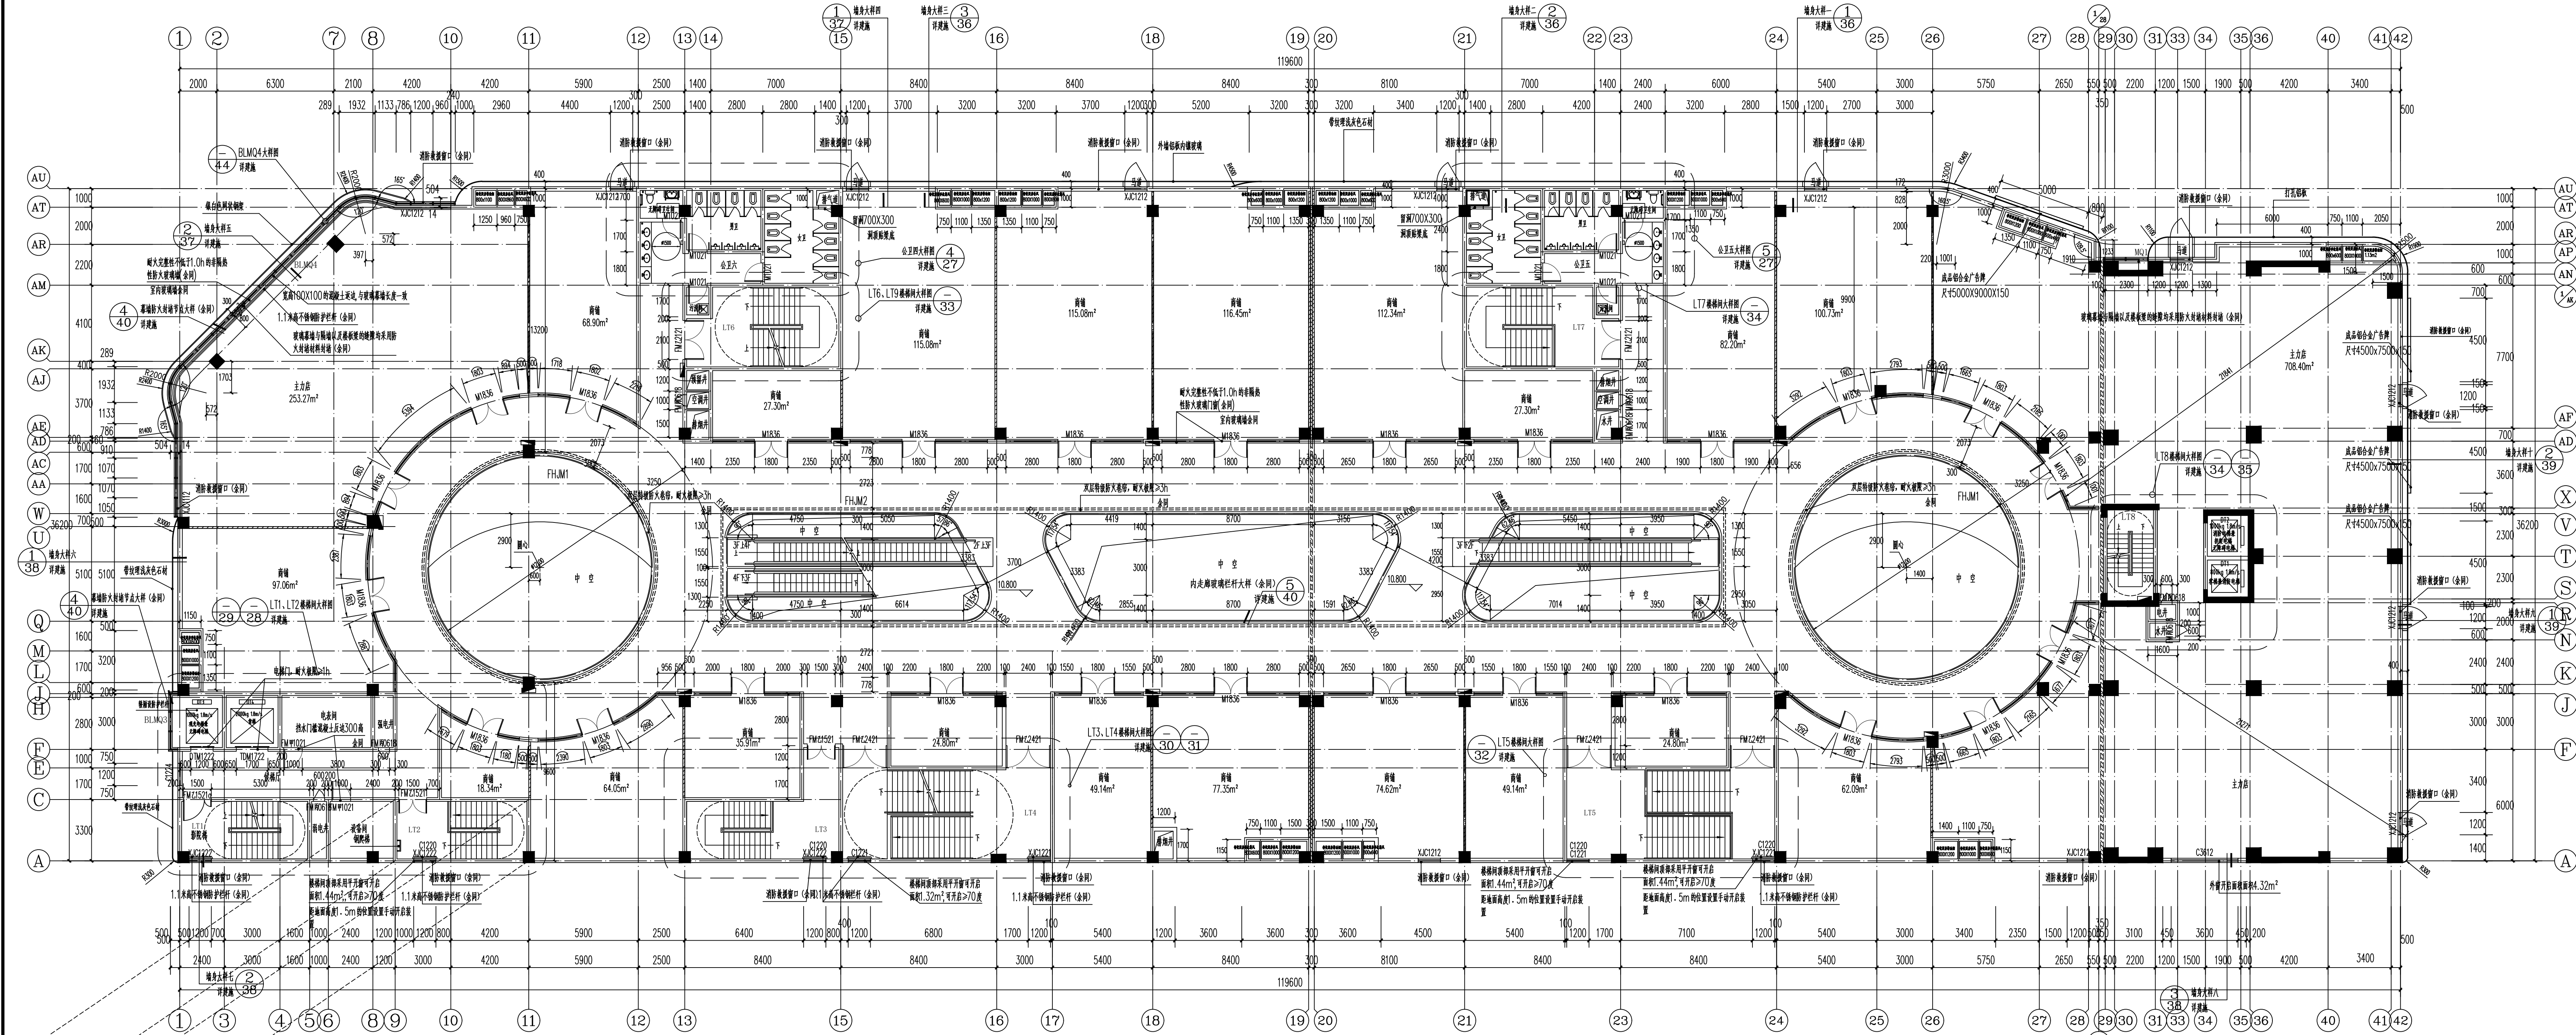

消防示意图例	
S	合用前室及前室
T	疏散楼梯
ST	金属竖梯
D	客梯、货梯
FT	自动扶梯
XD	消防电梯
➡	安全出口

注：三层商场设置自动喷淋灭火系统
本层为一个防火分区，防火分区面积为3837.23㎡，共有9个疏散楼梯，9个安全出口，其中LT1楼梯间为影院独有楼梯间。
房间内最远点至最近安全出口的距离为21.8m(≤27.5m)，最近疏散门至最近安全出口的距离为30.8m(≤37.5m)，满足规范要求。
本层需要的疏散宽度为3809.22X0.39X1/100=14.86m(计算疏散宽度的面积是减掉本层住宅楼梯间、消防电梯间面积的净面积)
本层设计的疏散宽度为2X1.475+2.325X2+2.34X2+2X2.075=16.43m，满足规范要求。

三层平面图 1:150

本层建筑面积：3837.23㎡

图例

- 灰砂加气混凝土砌块（商铺隔墙）
- 消火栓

- 注：
- 柱布置尺寸详结构图。
 - 除图中除注明者外，门窗洞口的墙体均为100mm厚平墙，墙、柱中安装。
 - 本工程所有外墙厚度均为240mm厚粉煤灰蒸压加气混凝土砌块，墙体轴线两侧100mm，内侧140mm。商铺隔墙除特殊注明外均为100mm厚灰砂加气混凝土砌块，其余墙体均为200mm厚烧结页岩多孔砖。
 - 凡窗台高小于900mm时，作防护栏杆具体做法详见1Z J401。玻璃幕墙作符合安全防护要求，以防止人攀爬。
 - 各种设备管道、穿墙孔、管井及附件等具体做法详同时对照各专业图纸，以免遗漏。
 - 本建筑设自动喷淋灭火系统，消火栓位置见水池。
 - 管进井及设备间防水溢进房间，门下方设300mm宽C20混凝土门槛，宽度同墙厚。
 - 除注明外，卫生间楼面标高均为+0.05；卫生间前室楼面标高均为+0.03，以=1%坡度向地漏，（H为楼面标高），详见卫生间大样图。
 - 所有室外卫生间、更衣室窗玻璃为磨砂玻璃。
 - 无障卫生间完成地面比相应楼面完成面低5mm，，并应有坡度坡，具体详见卫生间详图。
 - 外墙变形缝缝1Z J111-(A-2)-26，内墙及顶棚变形缝缝1Z J111-(A-4)-9，地面变形缝缝1Z J111-(A-7)-2，楼面变形缝缝1Z J111-(A-8)-1。
 - 人行安全出入口除T2个出入口的钢化玻璃门外，其他地方设置外挑2m钢化玻璃雨篷，0.76mm厚双层钢化夹层玻璃。
 - 消防疏散出口的净宽均不小于1.0mX1.0m，下脚距地面不大于1.2m，间距不大于2m，采用钢化玻璃，并应设置在室外易于识别的明显标志，详见平面、立面图。
 - 电梯层门客梯(洞口100X2200)，货梯(洞口700X2200)的耐火极限不应低于1.0h，客梯、货梯基台-1.700，D3观光电梯轿厢内应设防护栏。
 - 楼梯间自然通风，每五层内设置可开启外窗总面积≥2㎡，开窗间隔不大于三层。
 - 各层玻璃幕墙与隔墙以及楼板的墙体均采用防火封堵材料封堵。
 - 楼层之间竖向的门窗洞口间距≥800mm，间距不够的，在楼层外墙做进深，进深高度≥800mm高。
 - 公共建筑，当楼梯净宽大于0.2m时，必须采取防止少年儿童攀爬的措施；住宅建筑，楼梯净宽大于0.11m时，必须采取防止少年儿童攀爬的措施。
 - 图中设备预留尺寸及位置与设备专业图纸冲突时及时通知设计院。

建设单位/CLIENT:
麻阳苗族自治县远桥房地产开发有限公司

项目名称/PROJECT:
远程国际

子项目名称/SUB-PROJECT:
远程国际

区位图/REGIONAL LOCATION MAP :

建图国际
广东建筑艺术设计院有限公司
GUANGDONG ARCHITECTURAL ARTISTIC DESIGN INSTITUTE CO.,LTD

■ 建筑方案设计：甲级
■ 建筑结构设计：乙级
■ 装修设计：乙级
■ 幕墙设计：乙级

图纸名称/TITLE:
三层平面图

项目名称/PROJECT:
远程国际

设计 DESIGNED	古新辉	陈辉
校对 CHECKED	吴新红	吴新红
专业负责人 CHIEF	吴志刚	吴志刚
项目负责人 PROJECT CHIEF	吴志刚	吴志刚
审核 IDENTIFIED	黄履优	黄履优
审定 APPROVED	李 坚	李 坚

业务号/JOB NO.

设计阶段/STATUS: 施工图

专业/DISCIPLINE:	建筑		
比例/ SCALE:	1: 100	规格/ SIZE:	A1

出图日期/DATE: 2021. 06

图号/DRAWING NO. JS-16

版次 NO.	修改内容 DESCRIPTION	日期 DATE

条形码/BARCODE:

版权所有，不得复制或套用。
ALL RIGHTS RESERVED, DON'T COPIED, REPRODUCED.