





建设单位/CLIENT:			麻阳苗族自治县远桥房地产开发有限公司		
项目名称/PROJECT:			远程国际		
子项目名称/SUB-PROJECT:			远程国际		
区位图/REGIONAL LOCATION MAP:					
图纸名称/TITLE:			LT1、LT2楼梯间大样图一		
项目名称/PROJECT:			远程国际		
设计 DESIGNED	古新辉		校对 CHECKED	吴新红	
专业负责人 CHIEF	吴志刚		项目负责 PROJECT CHIEF	吴志刚	
审核 IDENTIFIED	黄履优		审定 APPROVED	李 坚	
业务号/JOB NO.			设计阶段/STATUS: 施工图		
专业/DISCIPLINE: 建筑			比例/ SCALE: 1: 100	规格/ SIZE: A1	
出图日期/DATE: 2021.06			图号/DRAWING NO. JS- 28		
版次 NO.	修改内容 DESCRIPTION	日期 DATE			
条形码/BARCODE:					
版权所有，不得复制、套用。 ALL RIGHTS RESERVED, DON'T COPIED, REPRODUCED.					