

建设单位/CLIENT:
麻阳苗族自治县远桥房地产开发有限公司

项目名称/PROJECT:
远程国际

子项目名称/SUB-PROJECT:
远程国际

区位图/REGIONAL LOCATION MAP :

建图国际

广东建筑艺术设计院有限公司

GUANGDONG ARCHITECTURAL ARTISTIC DESIGN INSTITUTE CO.,LTD

■ 建筑方案设计: 甲级

■ 风景园林设计: 乙级

■ 城乡规划设计: 乙级

■ 市政设计: 乙级

图纸名称/TITLE:
①~④轴立面图

项目名称/PROJECT:
远程国际

设计 DESIGNED	古新辉	设计人
校对 CHECKED	吴新红	校对
专业负责人 CHIEF	吴志刚	专业负责人
项目负责人 PROJECT CHIEF	吴志刚	项目负责人
审核 IDENTIFIED	黄履优	审核
审定 APPROVED	李 坚	审定

业务号/JOB NO.

设计阶段/STATUS: 施工图

专业/DISCIPLINE: 建筑

比例/
SCALE: 1: 100 规格/
SIZE: A1


出图日期/DATE: 2021. 06

图号/DRAWING NO. JS-22

版次 NO.	修改内容 DESCRIPTION	日期 DATE

条形码/BARCODE:

版权所有，不得复制、套用。
ALL RIGHTS RESERVED, DON'T COPIED, REPRODUCED.

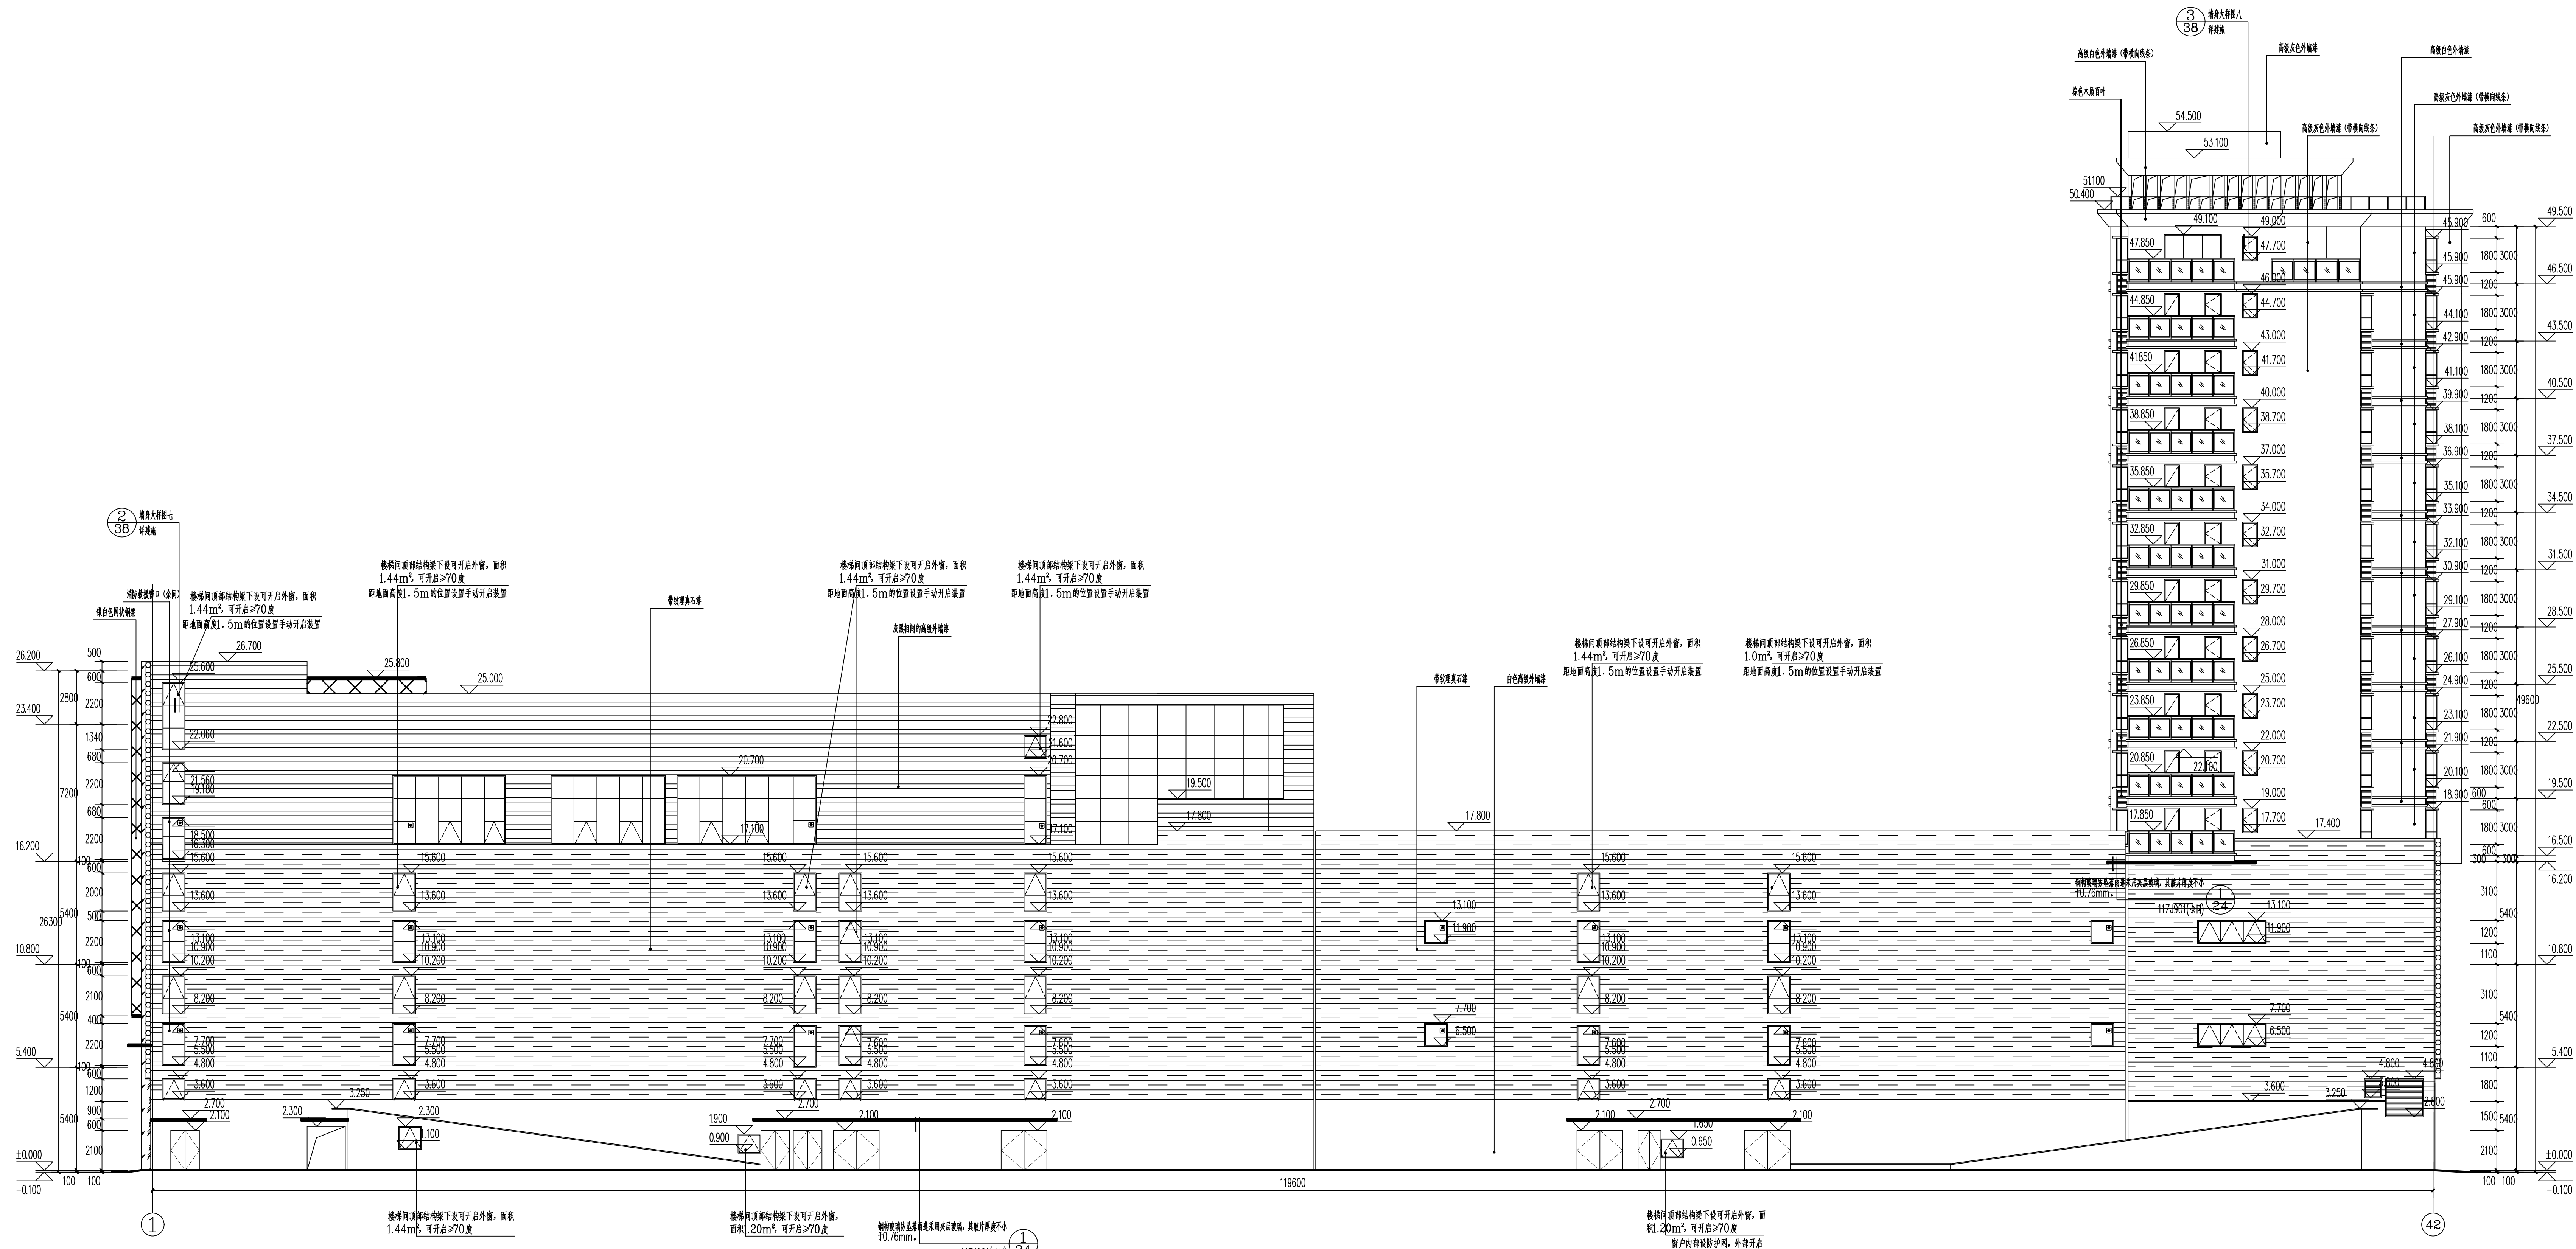

①~④轴立面图 1:150

注: 1、楼梯间洞口 (不小于1.0mX1.0m,
窗台高不小于1.2m, 玻璃采用钢化玻璃)