

建设单位/CLIENT:
麻阳苗族自治县远桥房地产开发有限公司

项目名称/PROJECT:
远程国际

子项目名称/SUB-PROJECT:
远程国际

区位图/REGIONAL LOCATION MAP :

售楼部

广东建筑艺术设计院有限公司

GUANGDONG ARCHITECTURAL ARTISTIC DESIGN INSTITUTE CO.,LTD

■ 建筑方案设计: 甲级 ■ 风景园林设计: 乙级

■ 施工图设计: 乙级 ■ 市政设计: 乙级

图纸名称/TITLE:
1-1剖面图

项目名称/PROJECT:
远程国际

设计 DESIGNED	古新辉	
校对 CHECKED	吴新红	
专业负责人 CHIEF	吴志刚	
项目负责人 PROJECT CHIEF	吴志刚	
审核 IDENTIFIED	黄展优	
审定 APPROVED	李 坚	

业务号/JOB NO.

设计阶段/STATUS: 施工图

专业/DISCIPLINE: 建筑

比例/ SCALE:	1: 100	规格/ SIZE:	A1
---------------	--------	--------------	----


出图日期/DATE: 2021. 06

图号/DRAWING NO. JS-24

版次 NO.	修改内容 DESCRIPTION	日期 DATE

条形码/BARCODE:

版权所有, 不得复制、套用。
ALL RIGHTS RESERVED, DON'T COPIED, REPRODUCED.

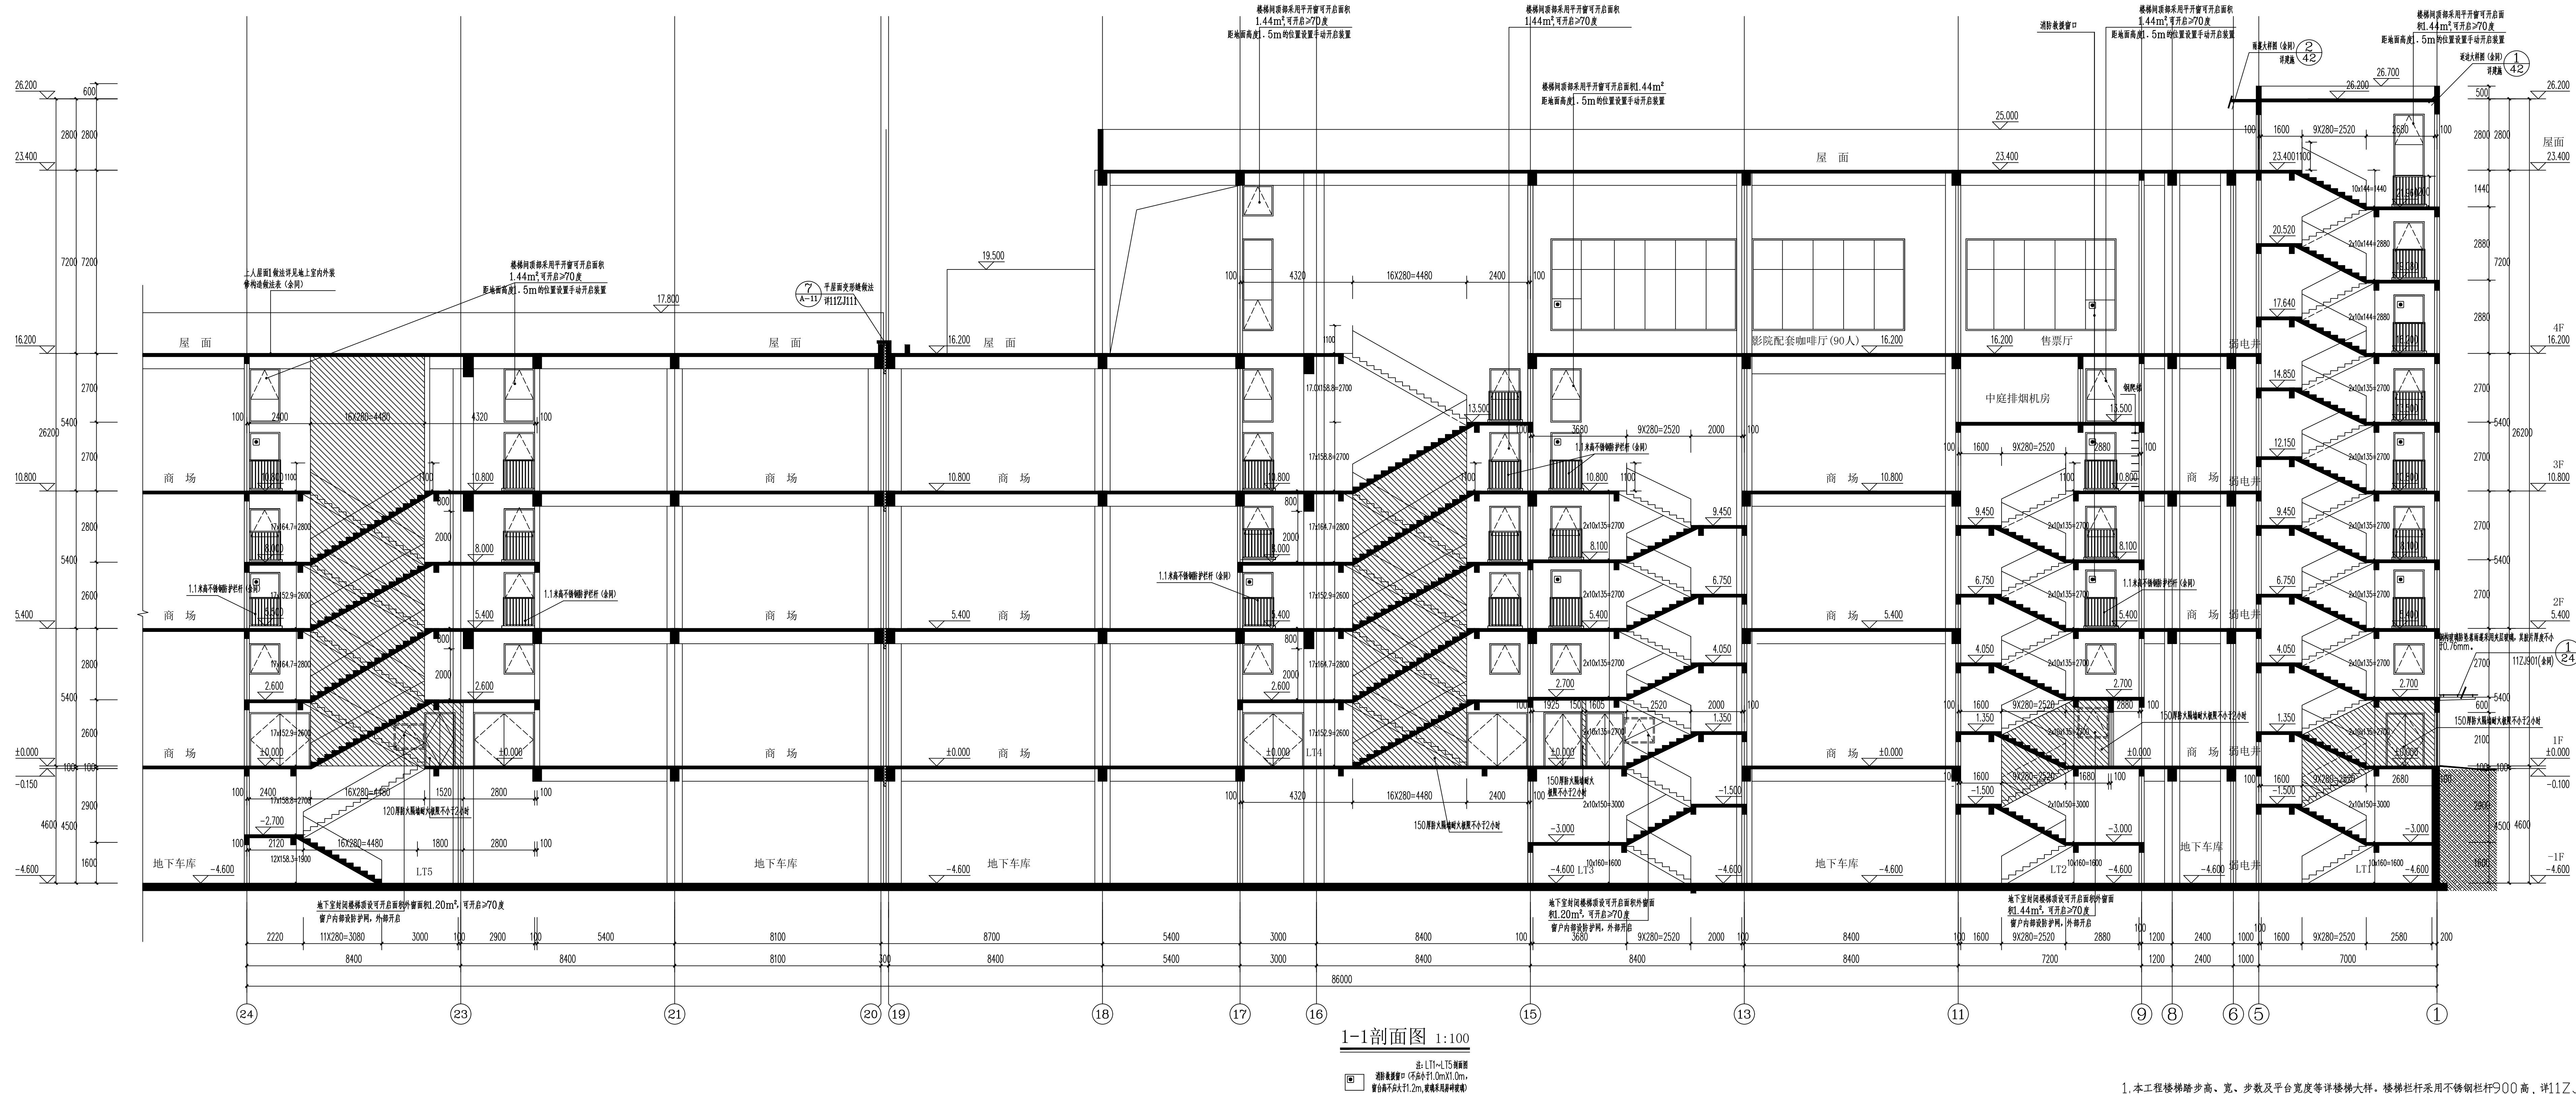

1.本工程楼梯踏步高、宽、步数及平台宽度等详楼梯大样。楼梯栏杆采用不锈钢栏杆900高,详11ZJ401-13-W扶手详11ZJ401-37-16。(注:当扶手水平长度大于0.5m时,栏杆净高不低于1100)。

2.起步详11ZJ40138-6;扶手与填充墙连接详11ZJ401-42-5,防滑详05ZJ401-39-6

3.梯井大于110,均做防坠网处理。

4.凡窗台小于900mm时,作防护栏杆具体做法详11ZJ401-43-1。栏杆制作要符合安全防护要求,以防止人攀爬。