




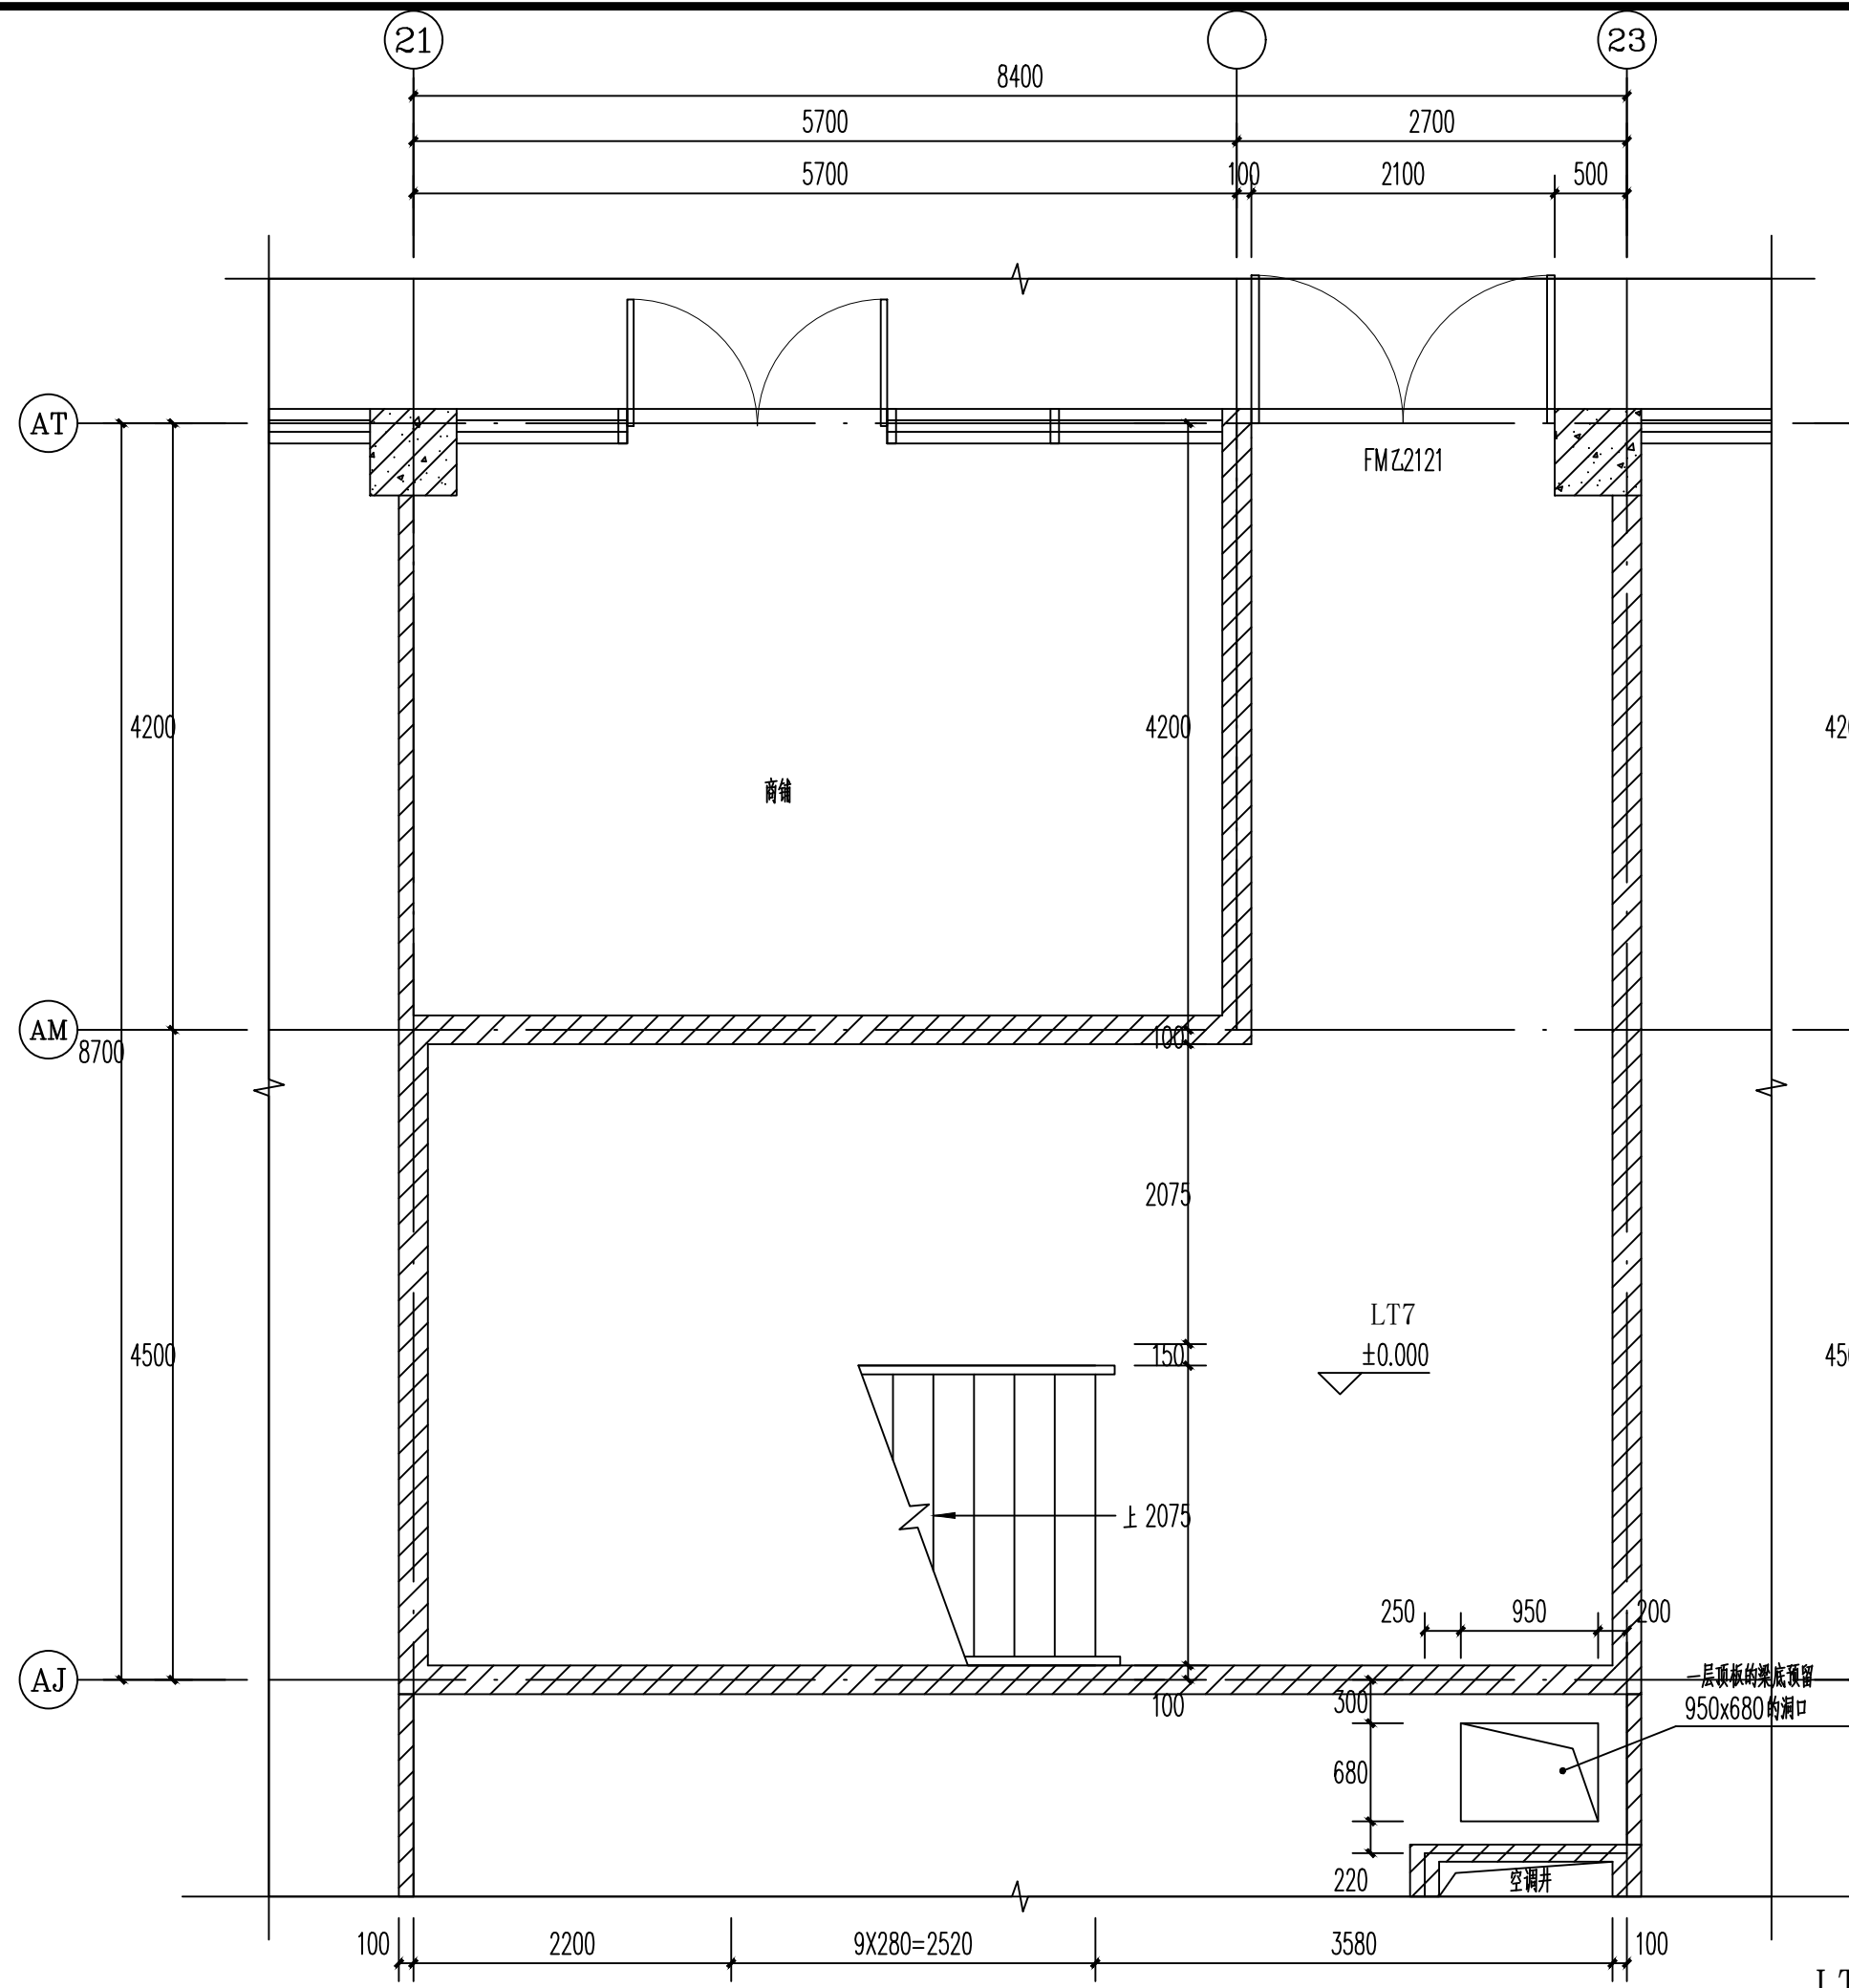


LT7楼梯间一层平面图 1:50

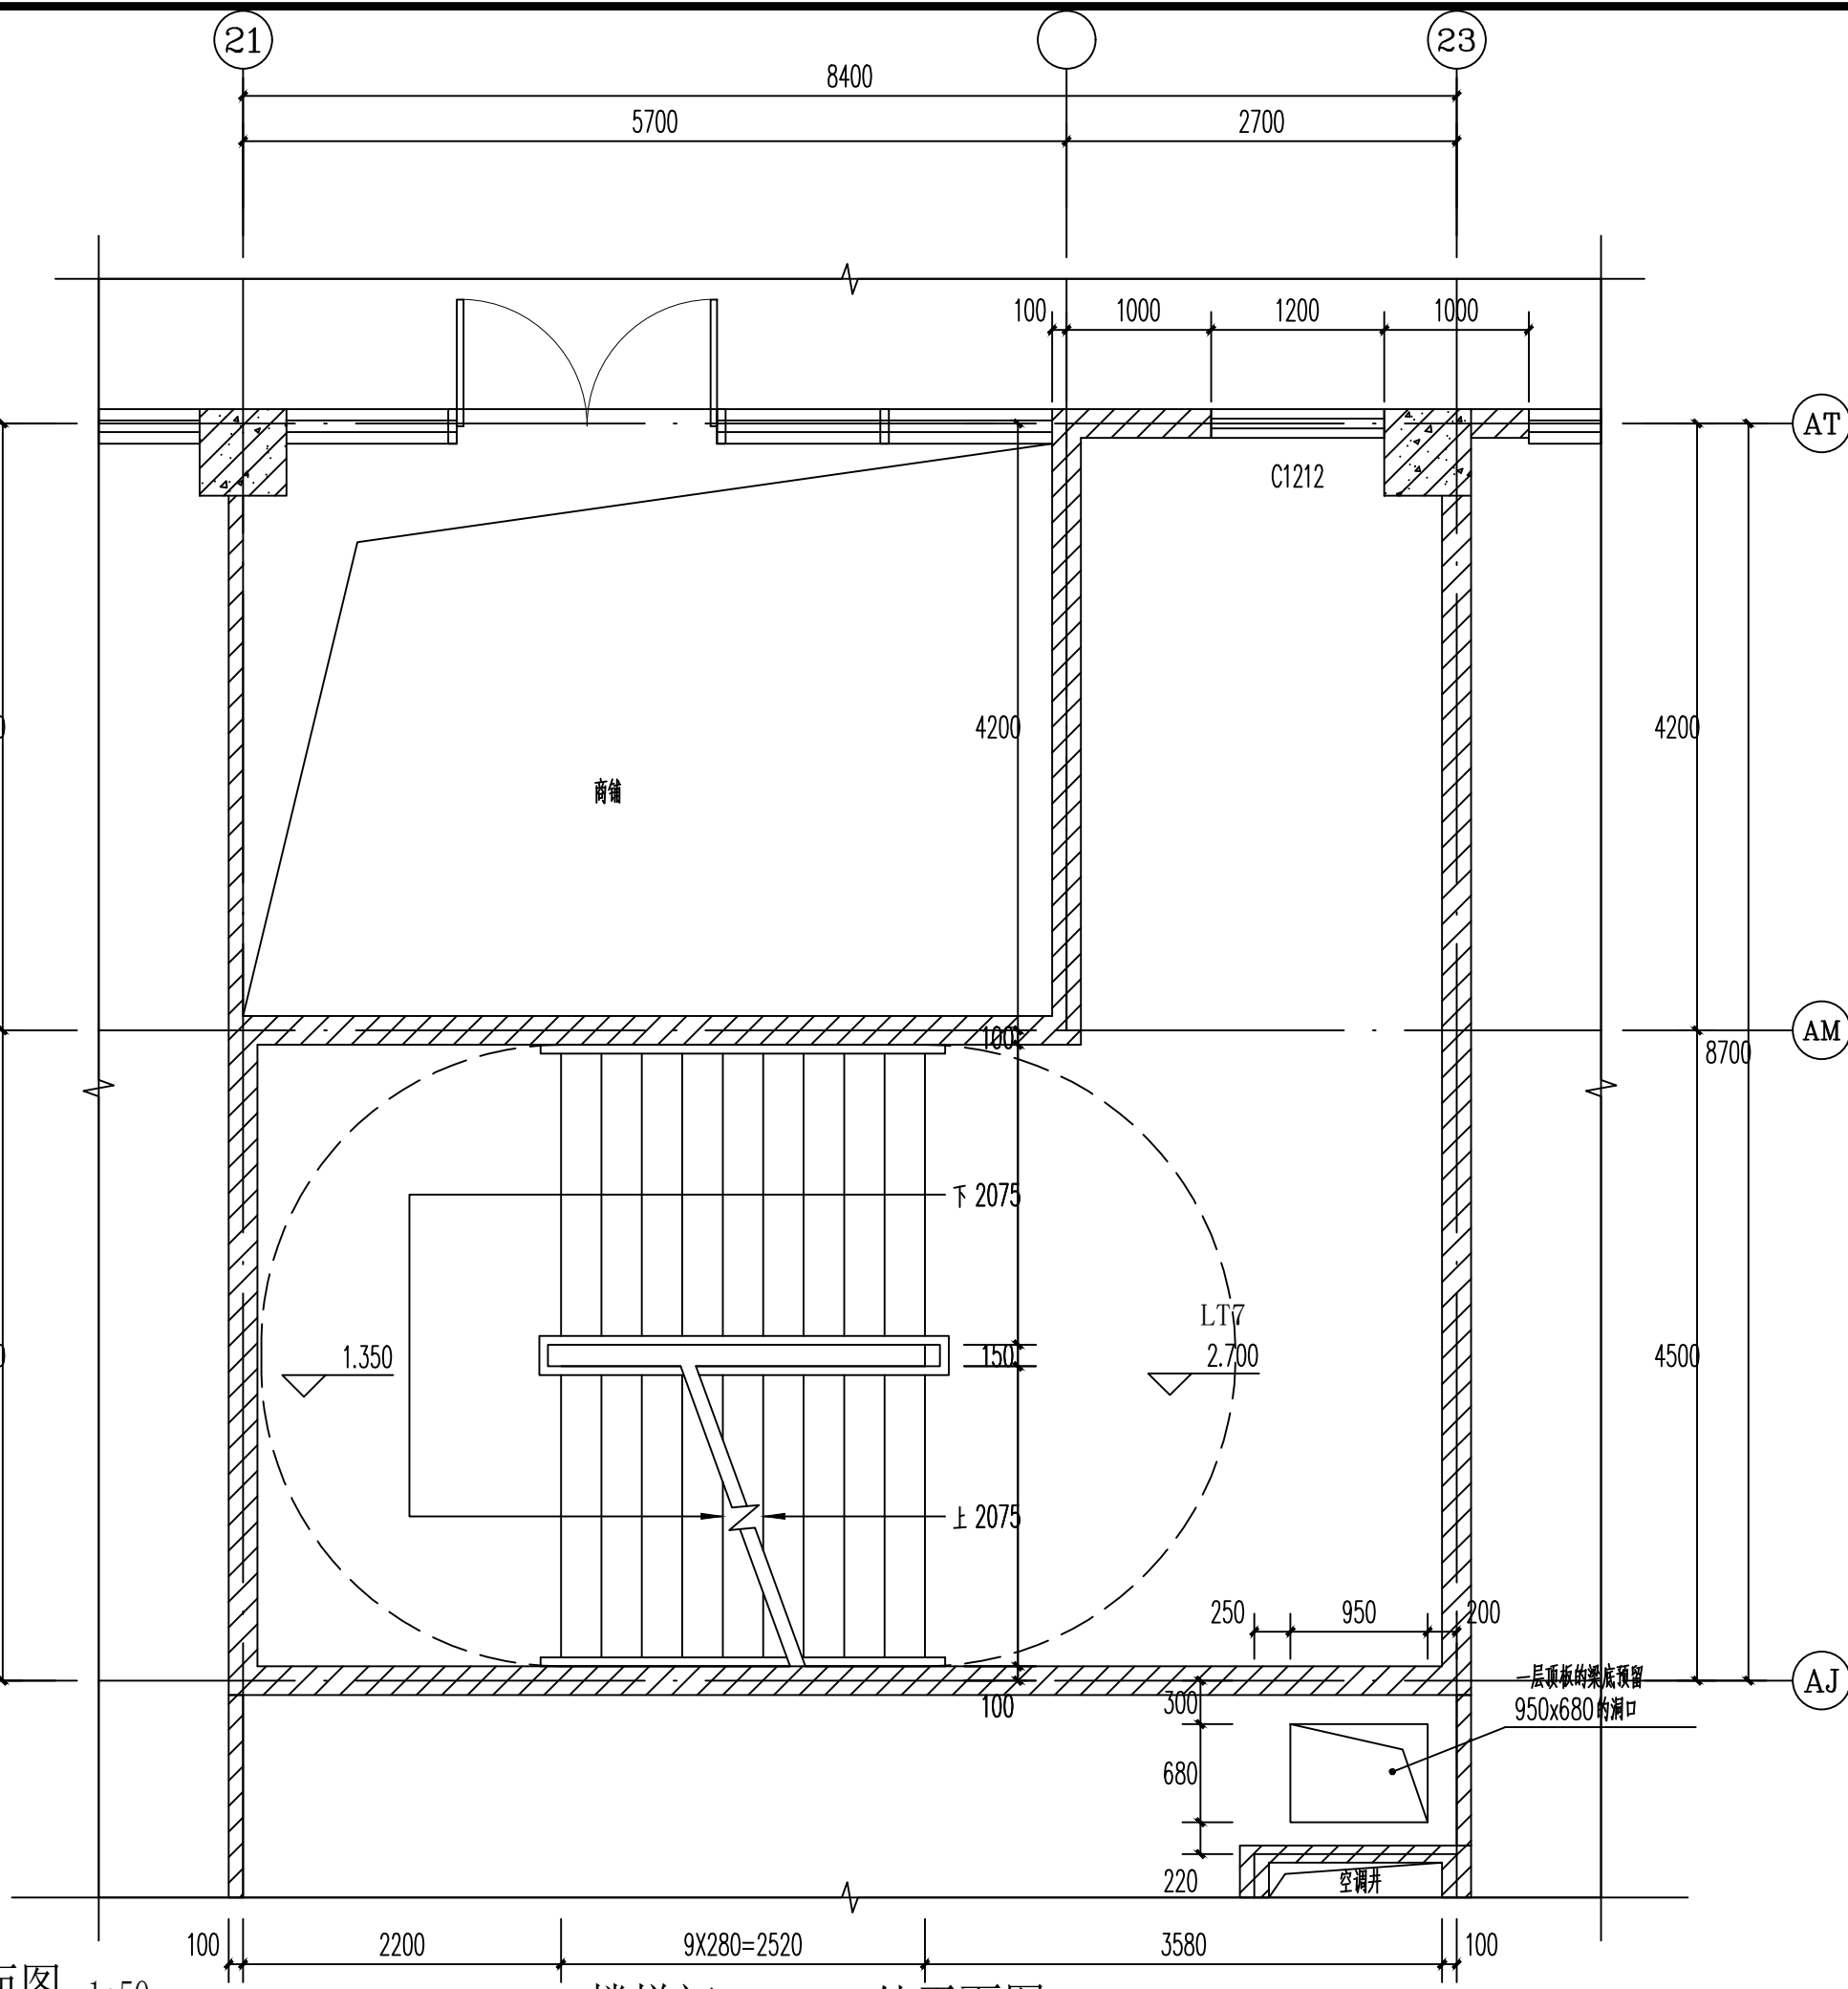


LT7楼梯间H=2.700处平面图 1:50

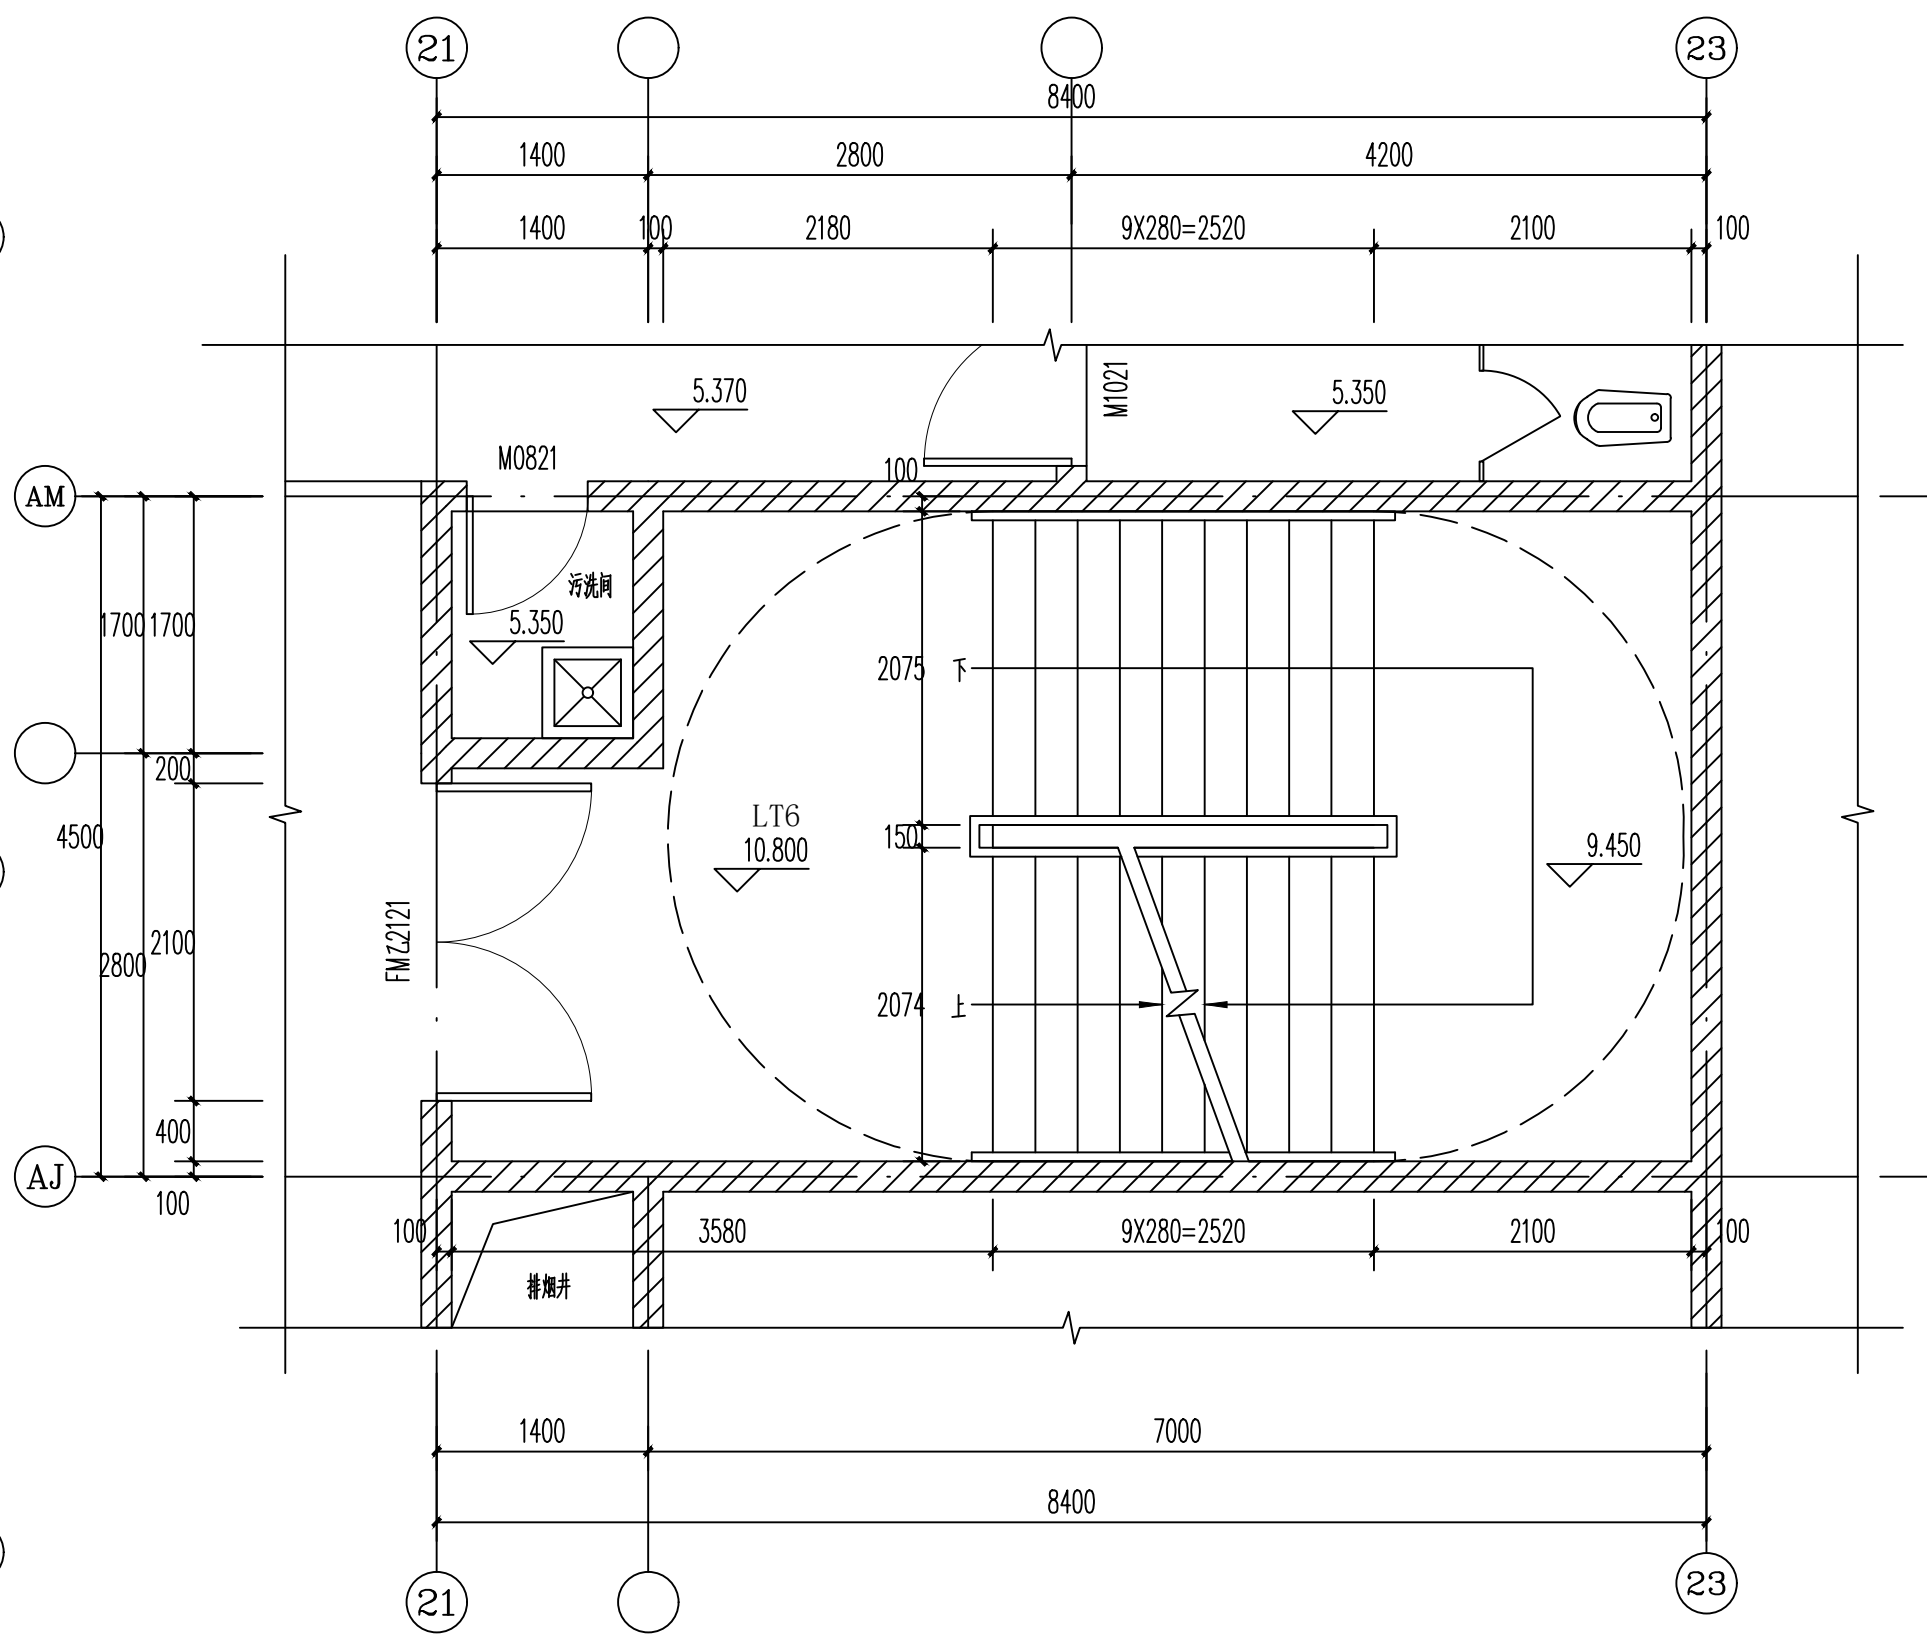

LT7楼梯间二层平面图 1:50

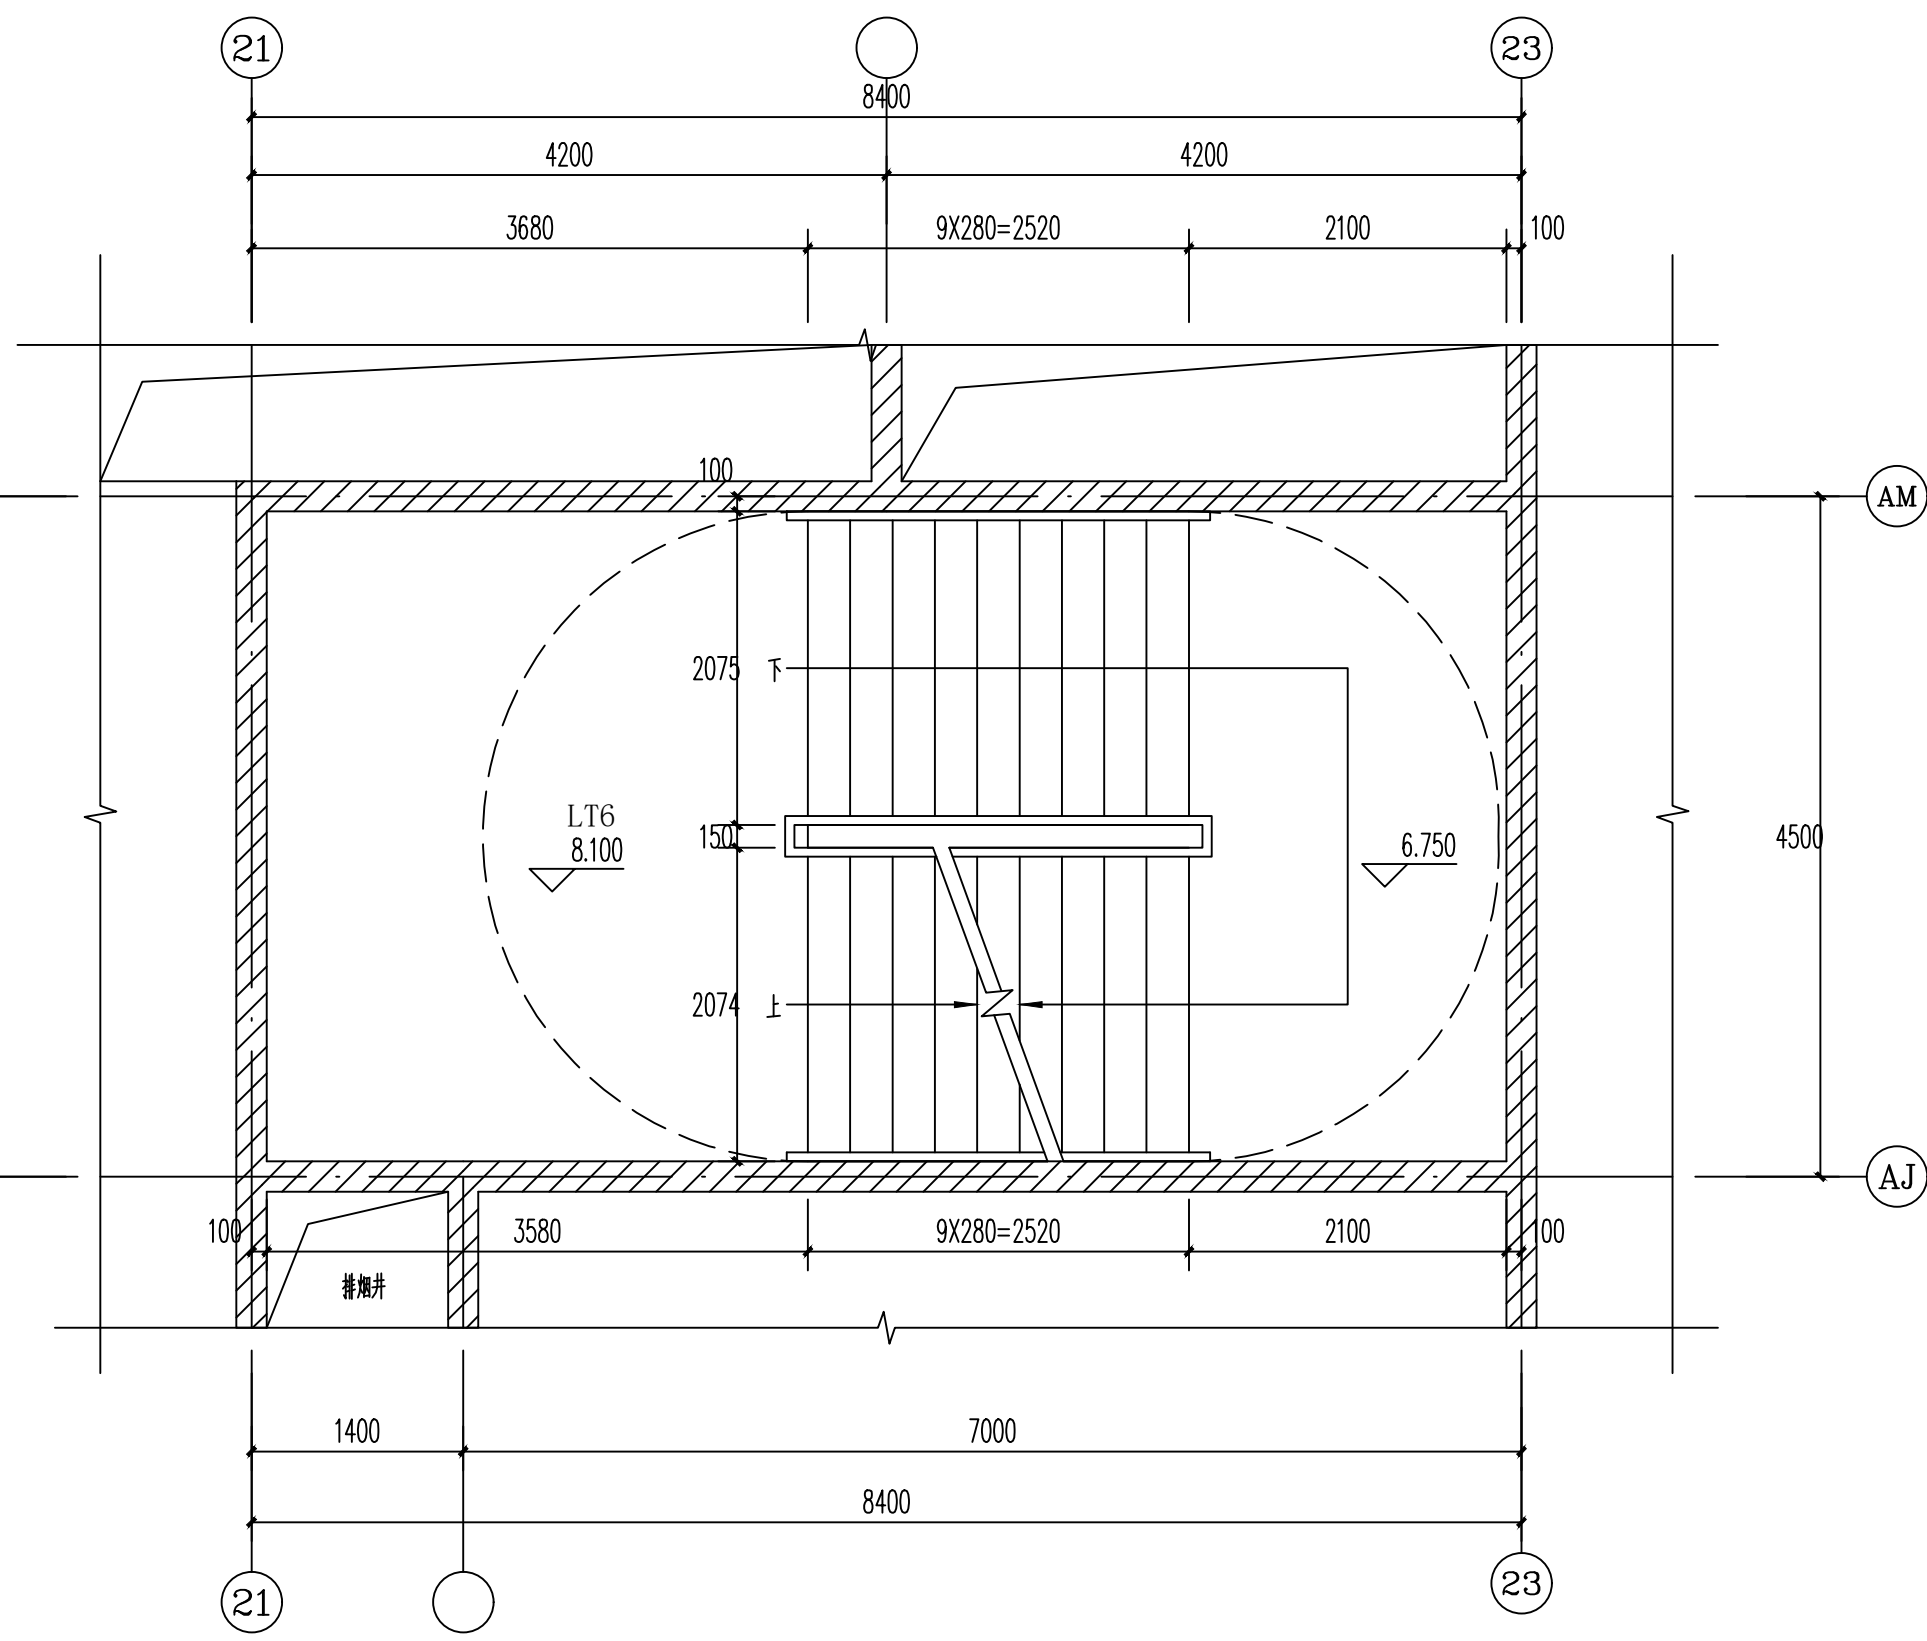


LT7楼梯间H=8.100处平面图 1:50

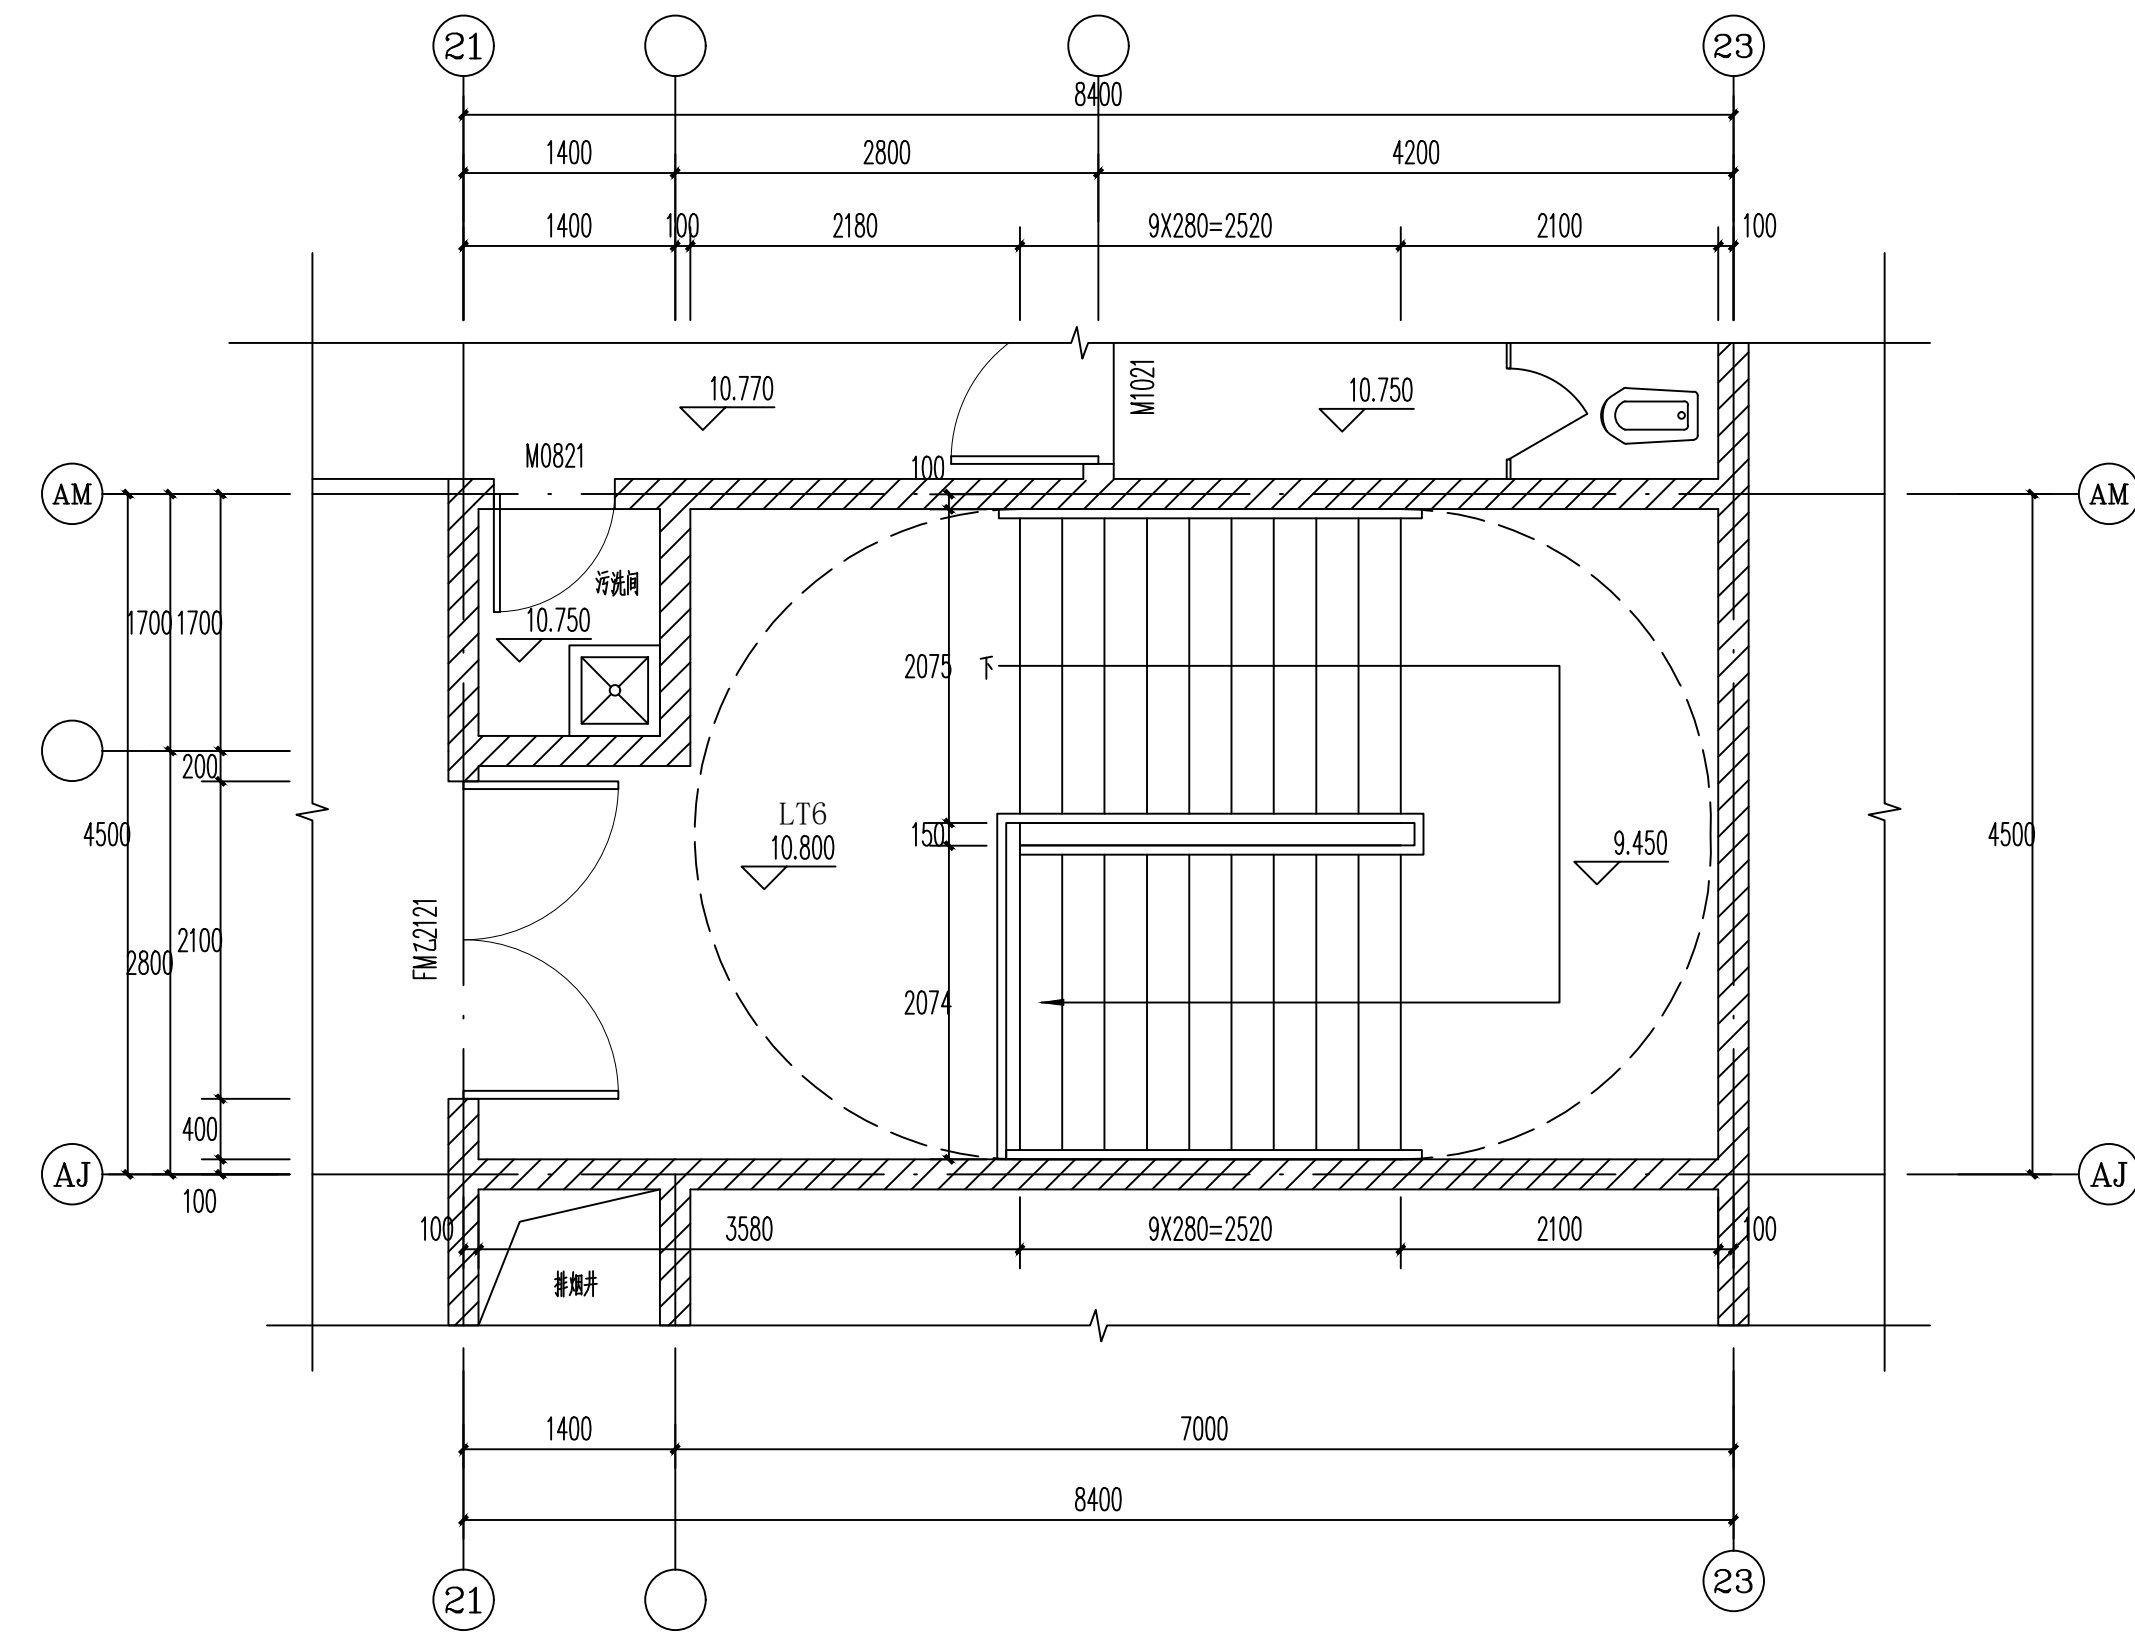


LT7楼梯间三层平面图 1:50

LT7楼梯间屋顶风井平面图详JS-28

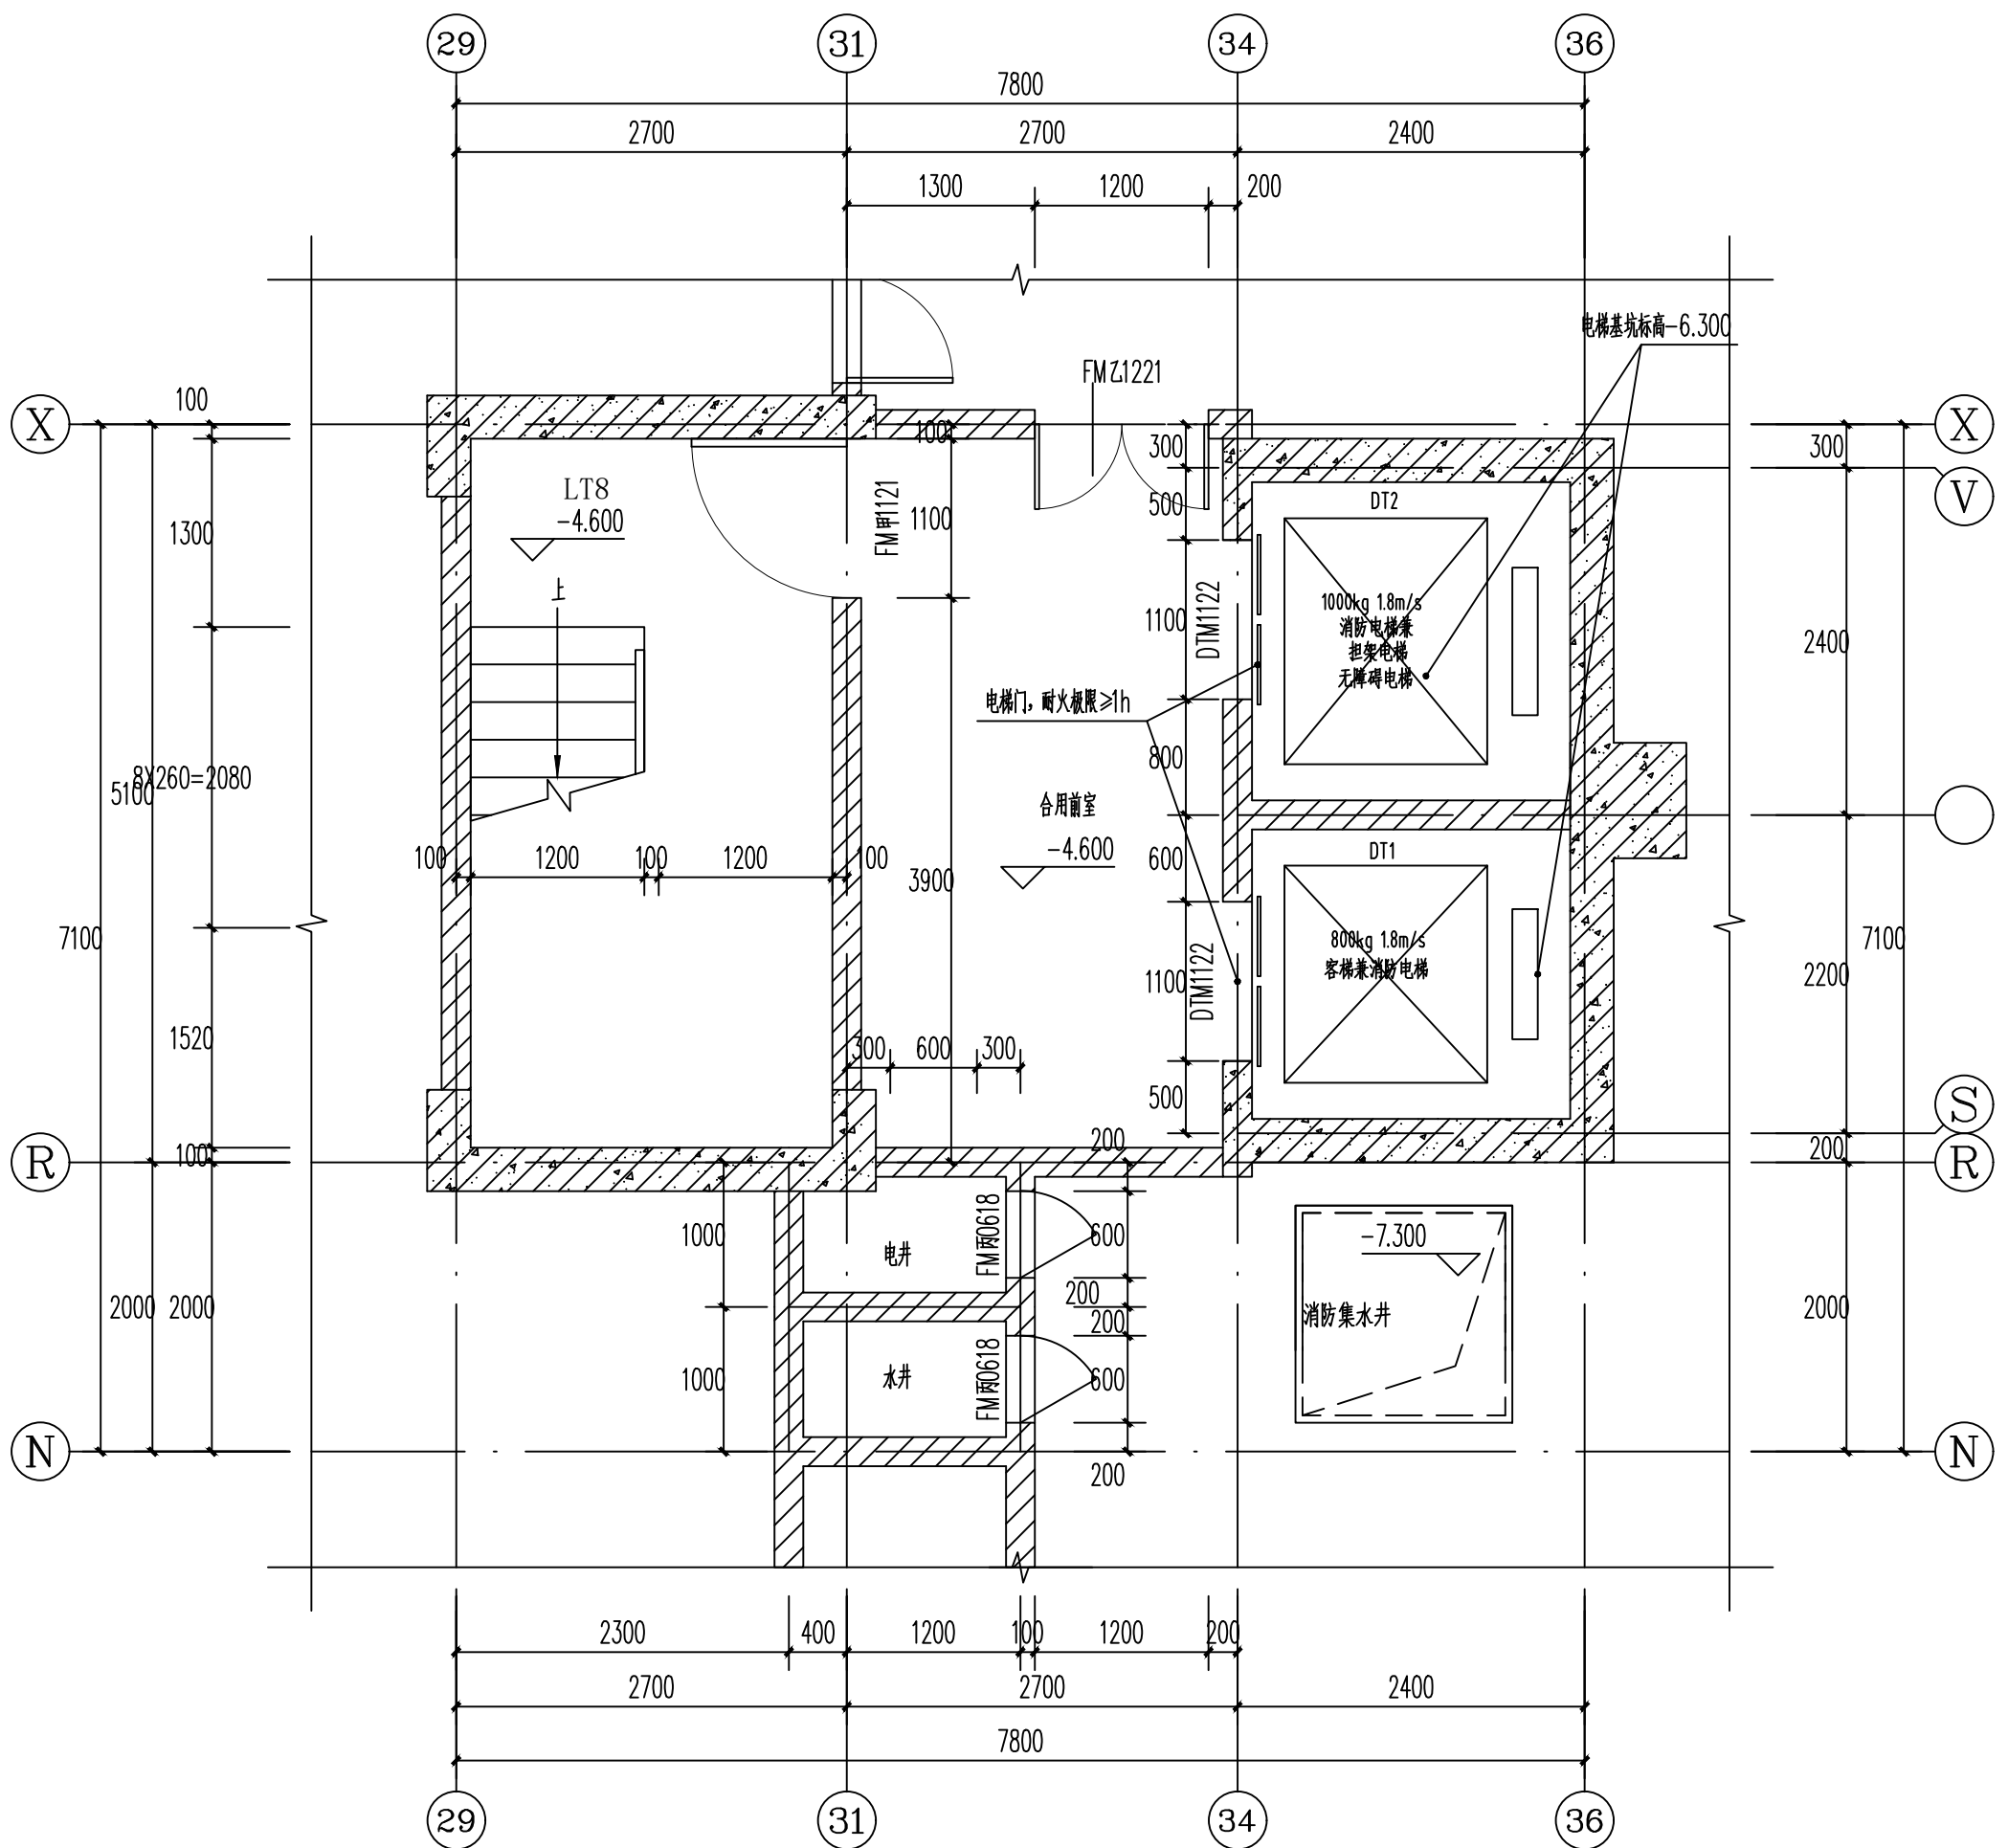

LT8楼梯间负一层平面图 1:50

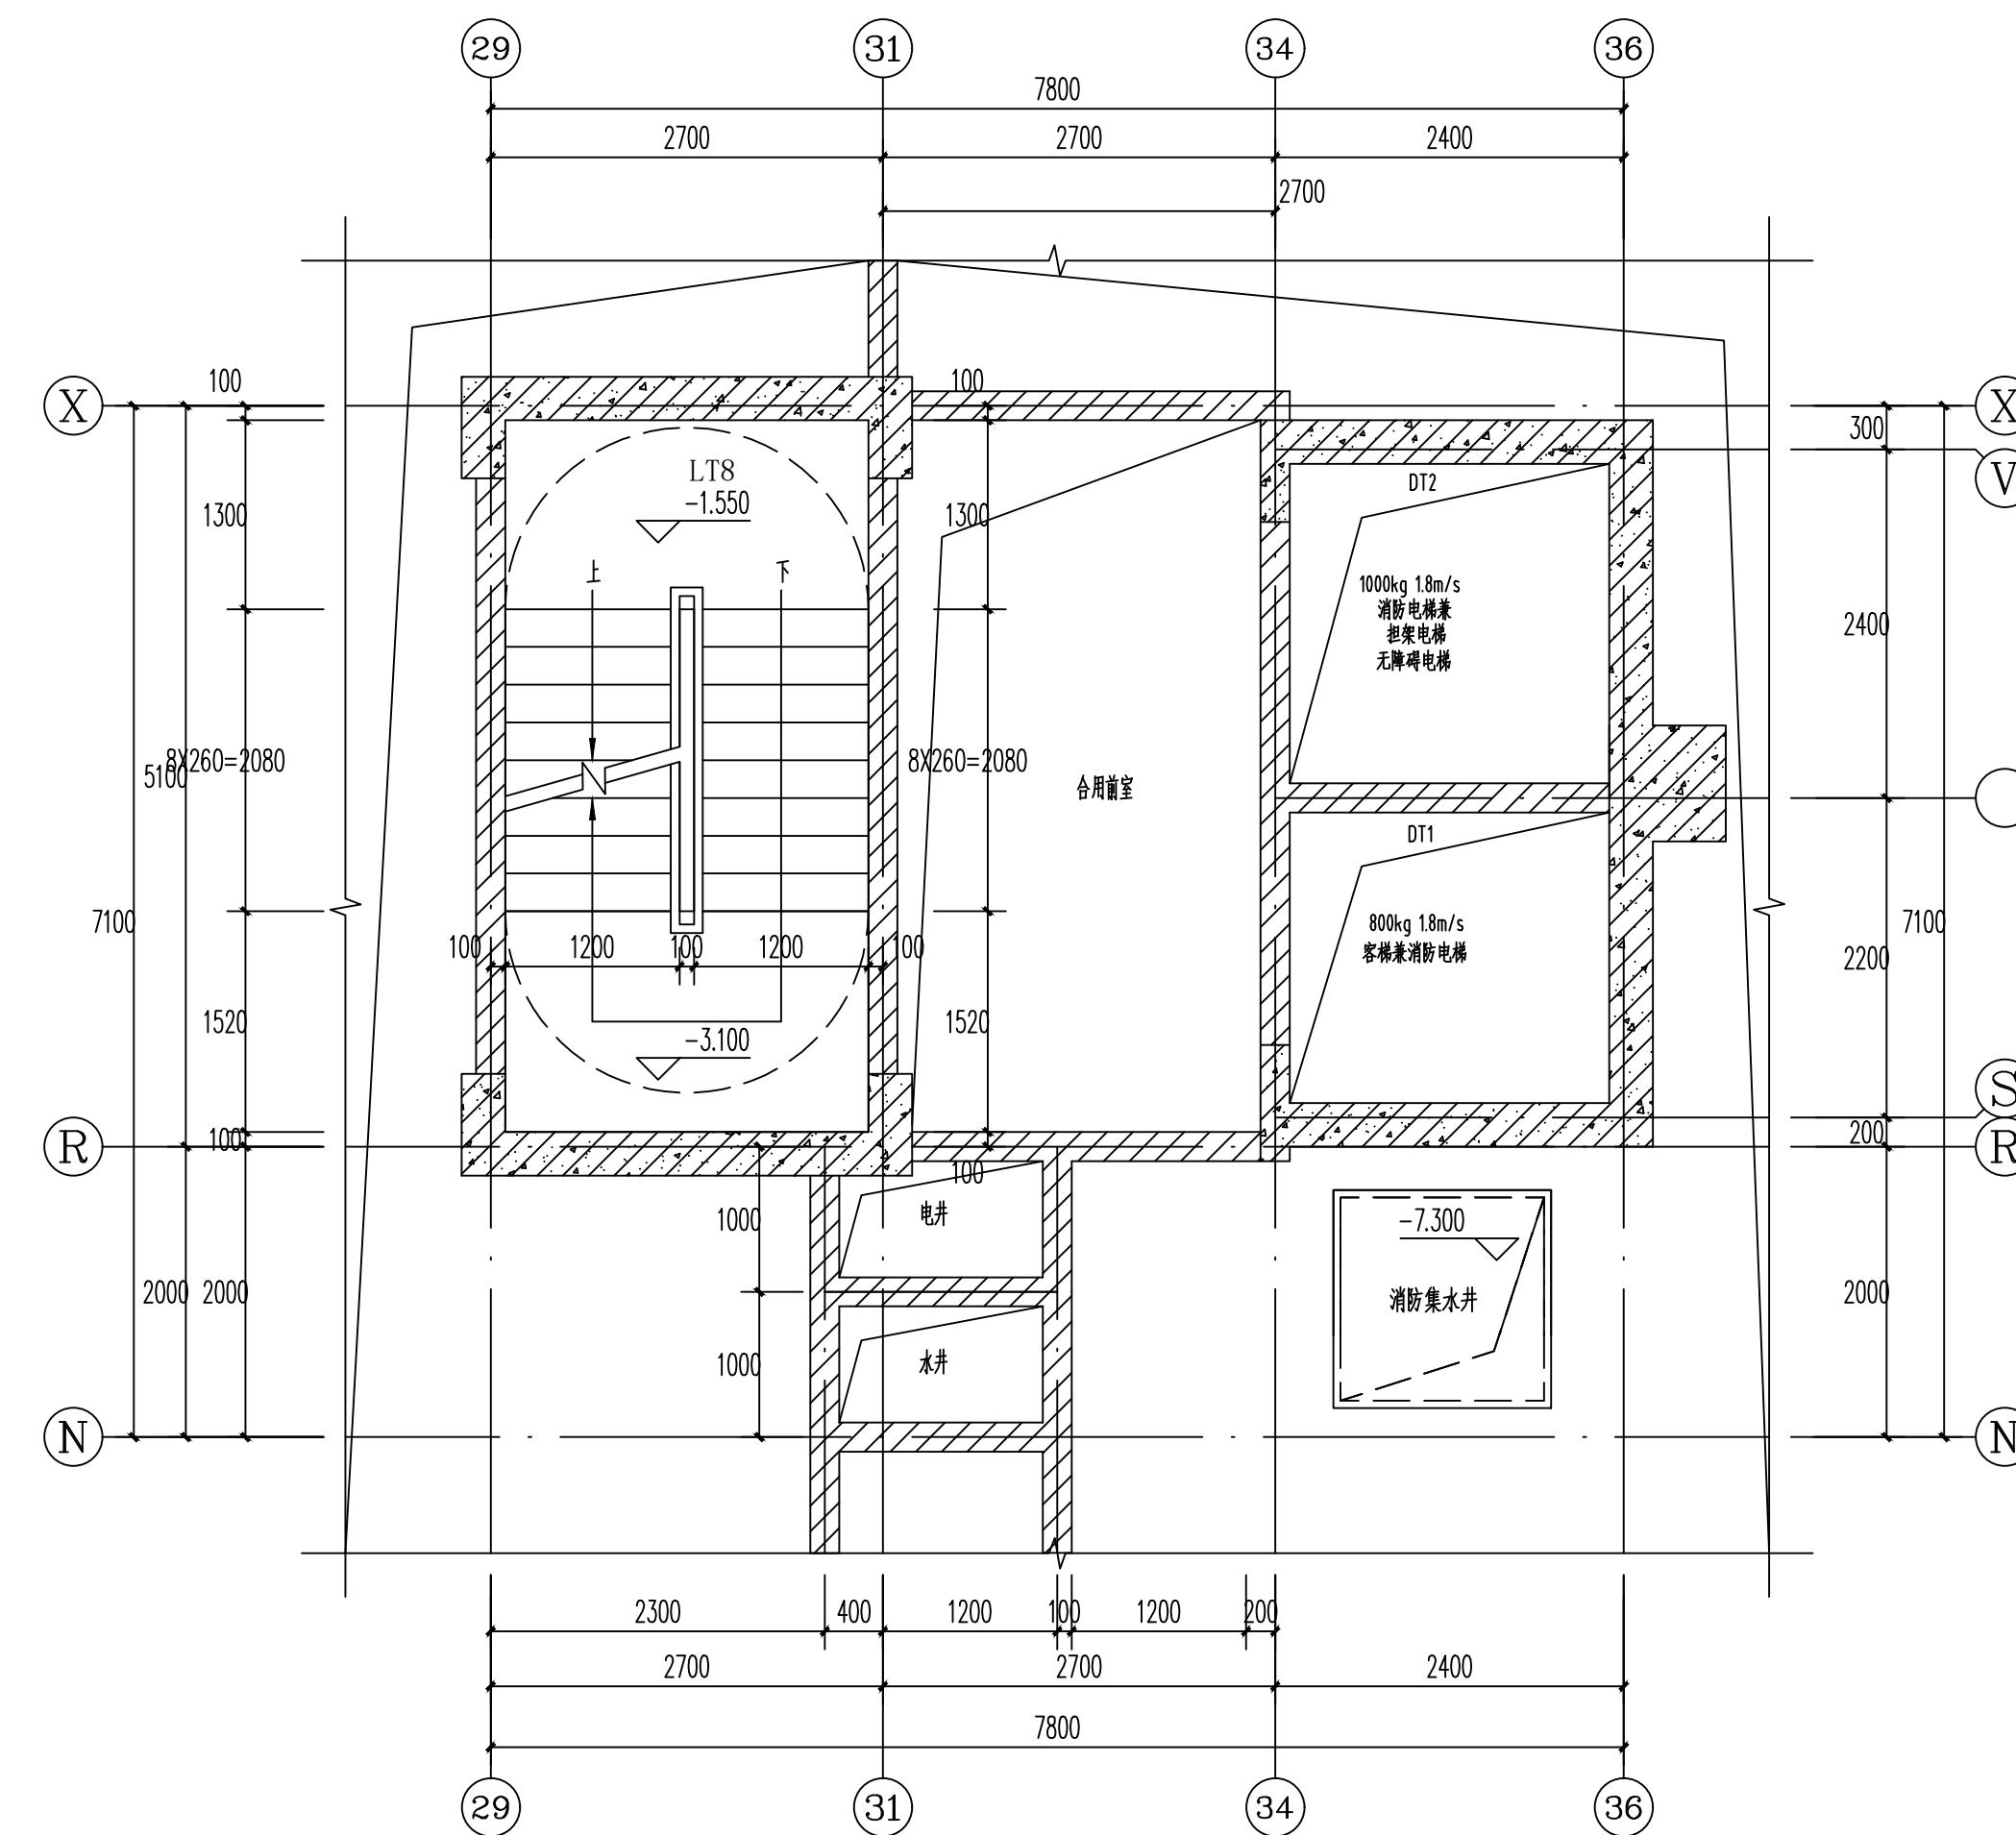

LT8楼梯间H=-1.550处平面图 1:50

建设单位/CLIENT:		
麻阳苗族自治县远桥房地产开发有限公司		
项目名称/PROJECT:		
远程国际		
子项目名称/SUB-PROJECT:		
远程国际		
区位图/REGIONAL LOCATION MAP :		
售楼部 广东建筑艺术设计院有限公司 GUANGDONG ARCHITECTURAL ARTISTIC DESIGN INSTITUTE CO.,LTD ■ 建筑方案设计: 甲级 ■ 风景园林设计: 乙级 ■ 城乡规划设计: 乙级 ■ 市政工程设计: 乙级		
图纸名称/TITLE:		
LT7楼梯间大样图		
LT8楼梯间大样图一		

项目名称/PROJECT:		
远程国际		
设计	古新辉	古新辉
DESIGNED		
校对	吴新红	吴新红
CHECKED		
专业负责人	吴志刚	吴志刚
CHIEF		
项目负责人	吴志刚	吴志刚
PROJECT CHIEF		
审核	黄展优	黄展优
IDENTIFIED		
审定	李 坚	李 坚
APPROVED		
业务号/JOB NO.		
设计阶段/STATUS: 施工图		
专业/DISCIPLINE: 建筑		
比例/SCALE:	1: 100	规格/SIZE: A1
出图日期/DATE: 2021. 06		
图号/DRAWING NO. JS-34		
版次NO.	修改内容DESCRIPTION	日期DATE
条形码/BARCODE:		
版权所有, 不得复制、套用。 ALL RIGHTS RESERVED, DON'T COPIED, REPRODUCED.		