




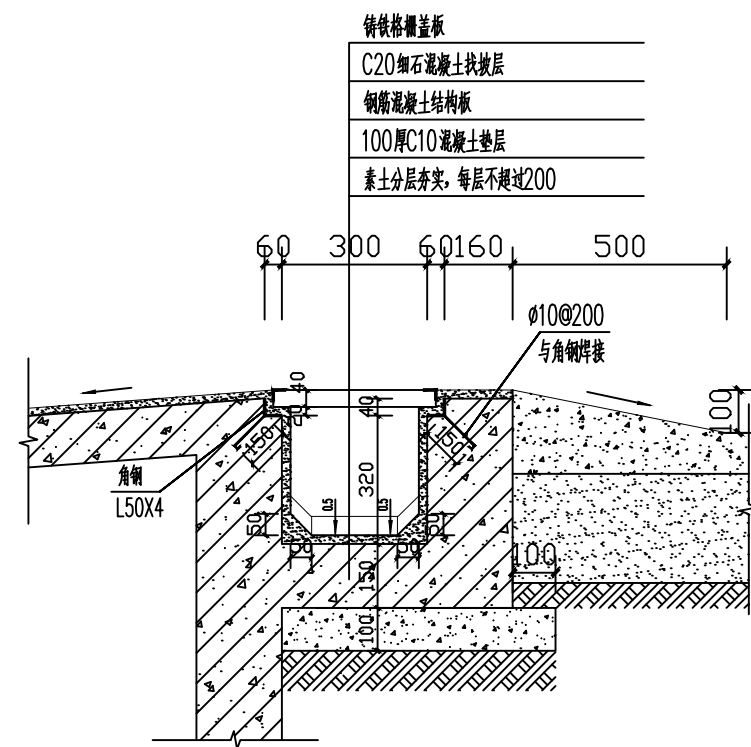


① 车道室外地面截水沟大样 1:25

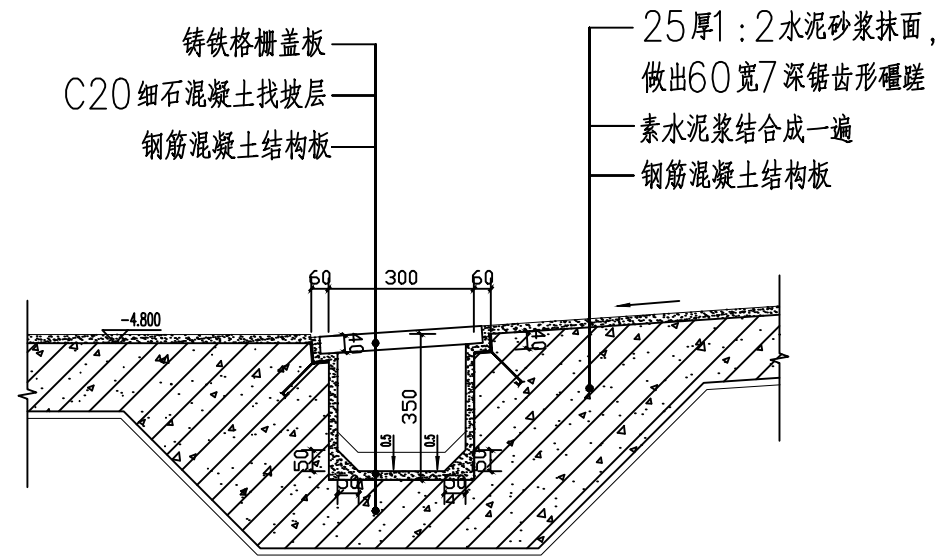


② 车道室内地面截水沟大样 1:25

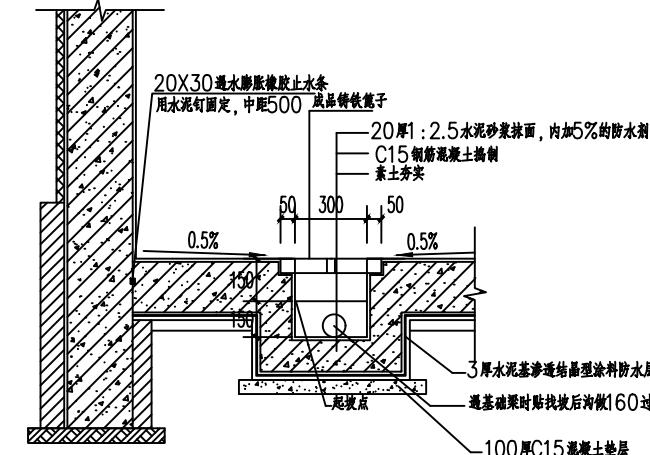


③ 300宽排水沟大样 1:25

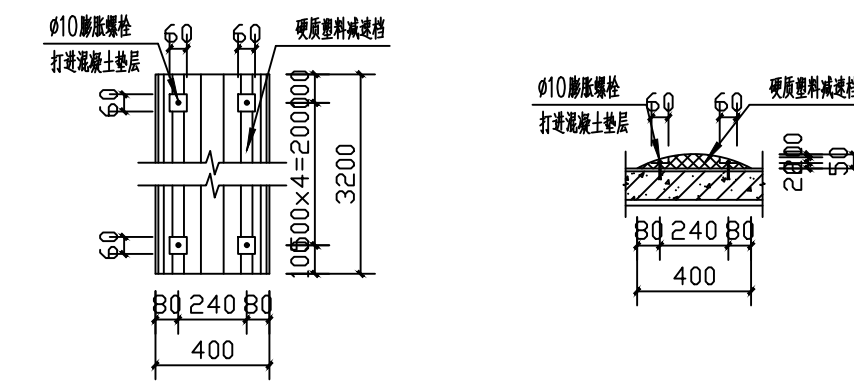


④ 塑料減速檔 1:25

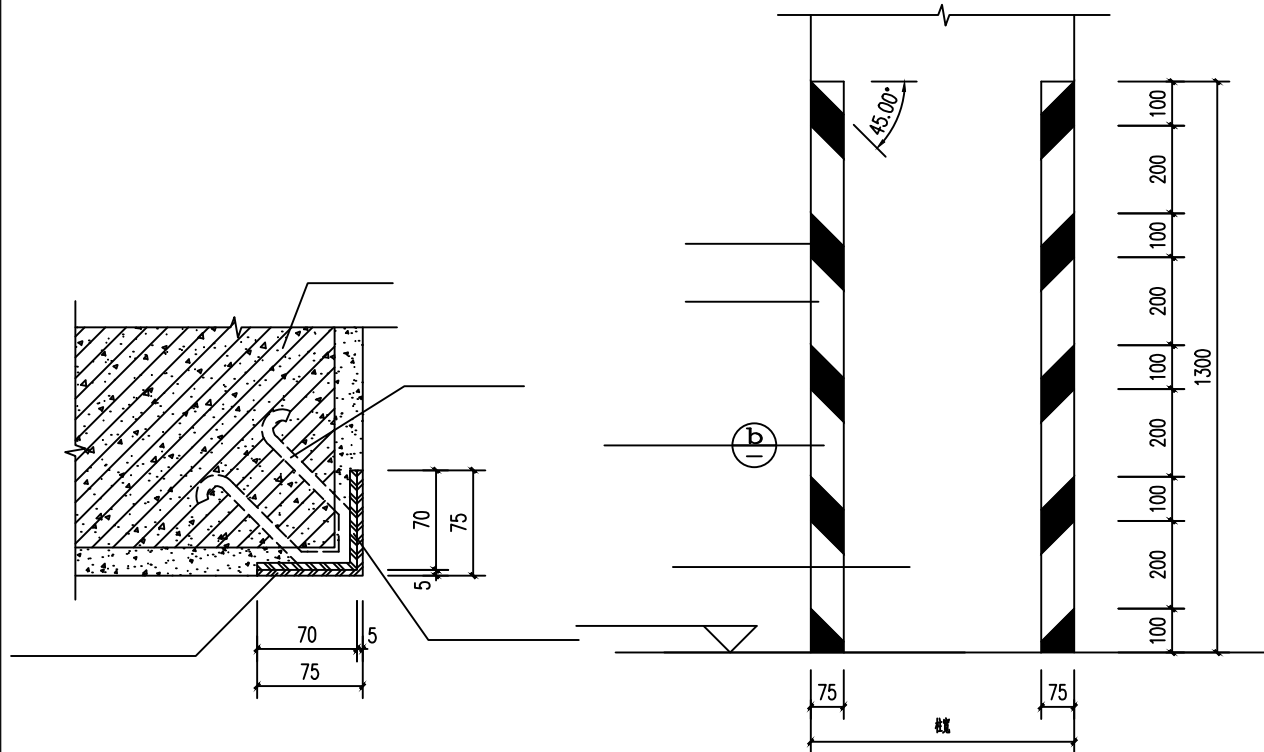

⑤ 车库墙柱防撞保护节点 1:5

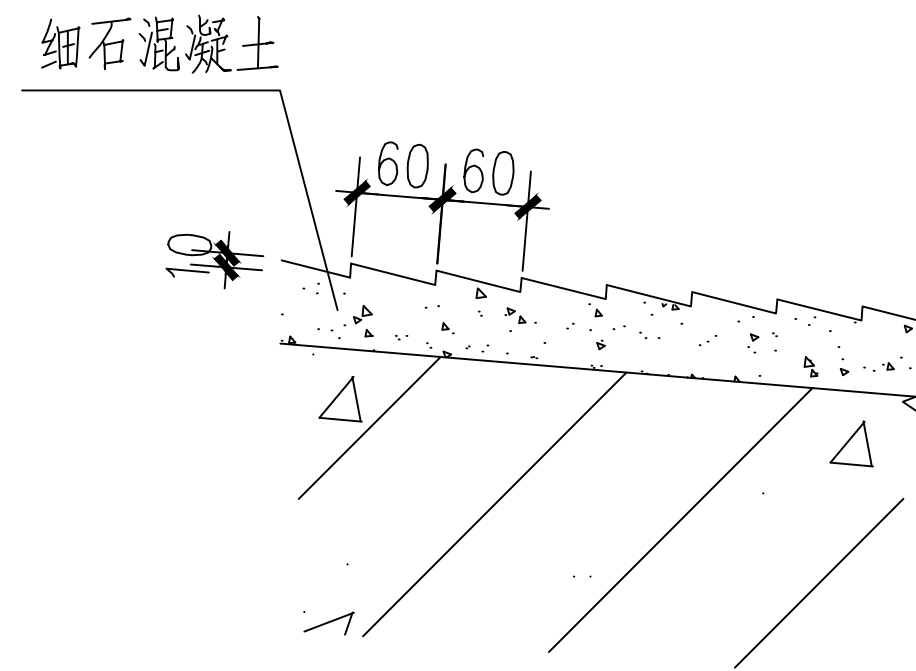


⑥ 车道防滑礞碯详图 1:5

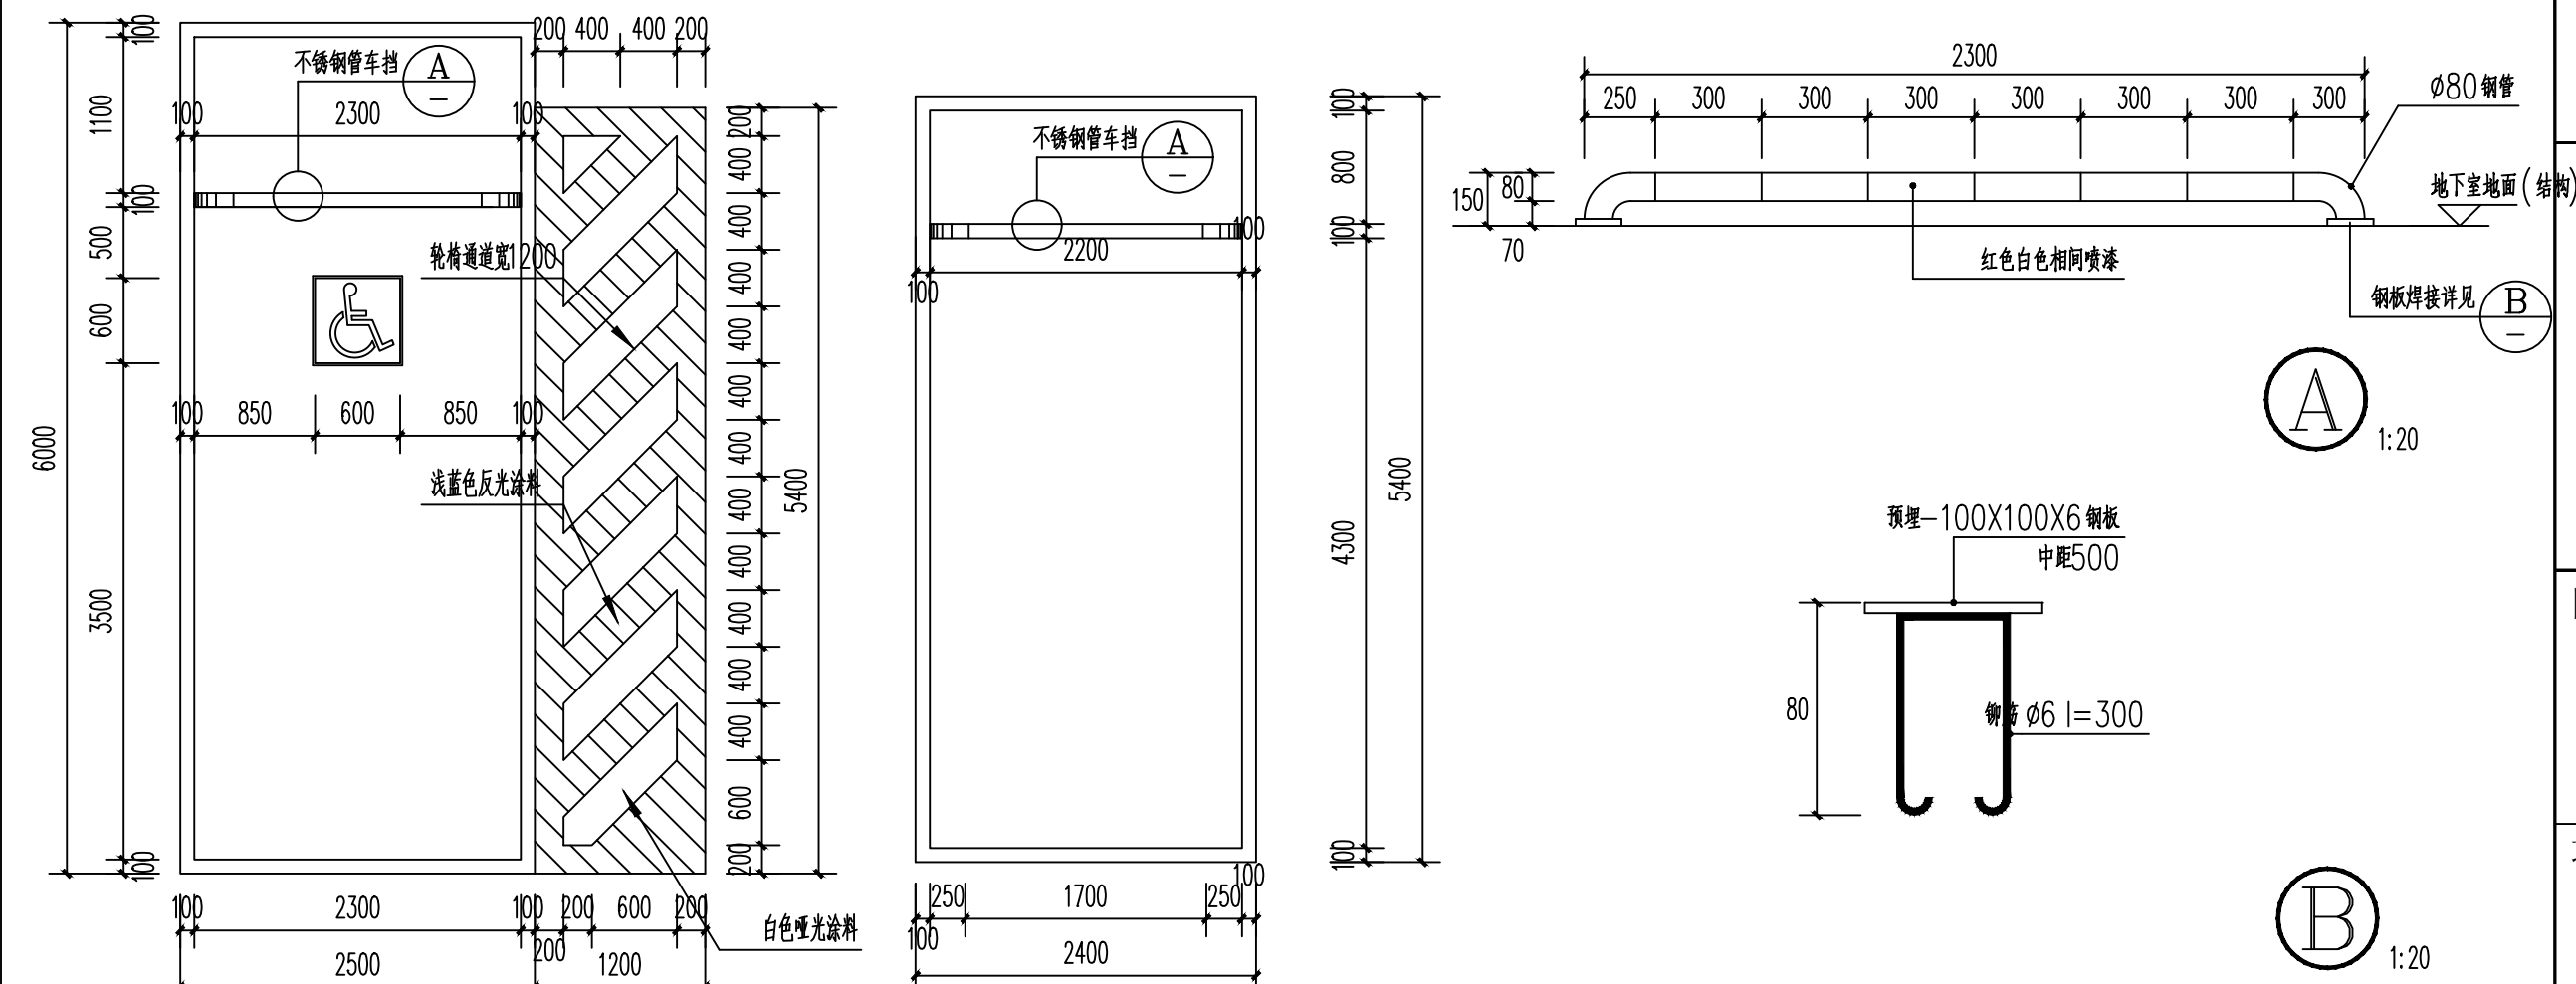


⑦ 无障碍停车位 1:50

⑧普通停车位 1:50

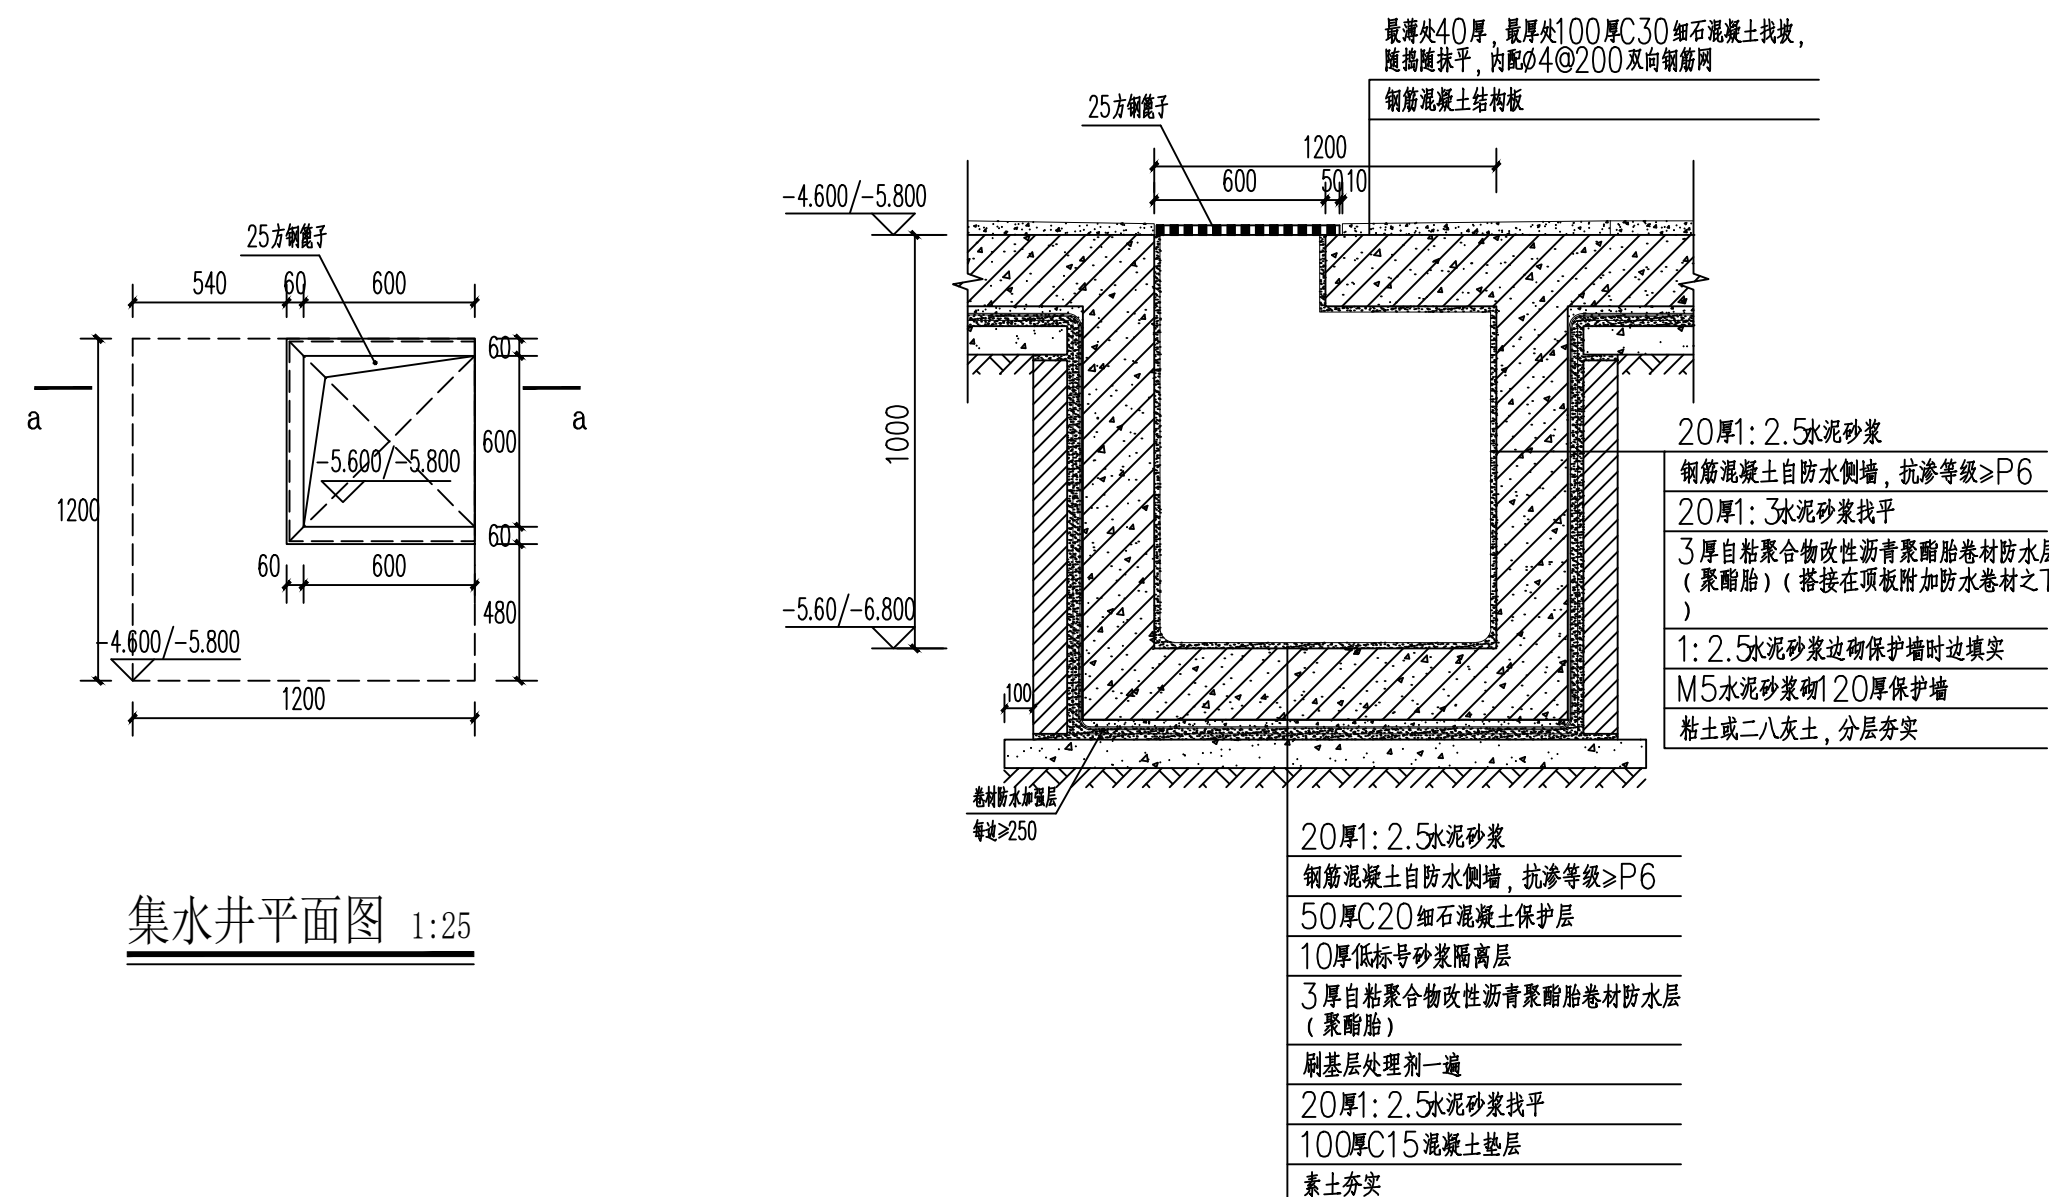

⑨ 集水井大样图 1:25

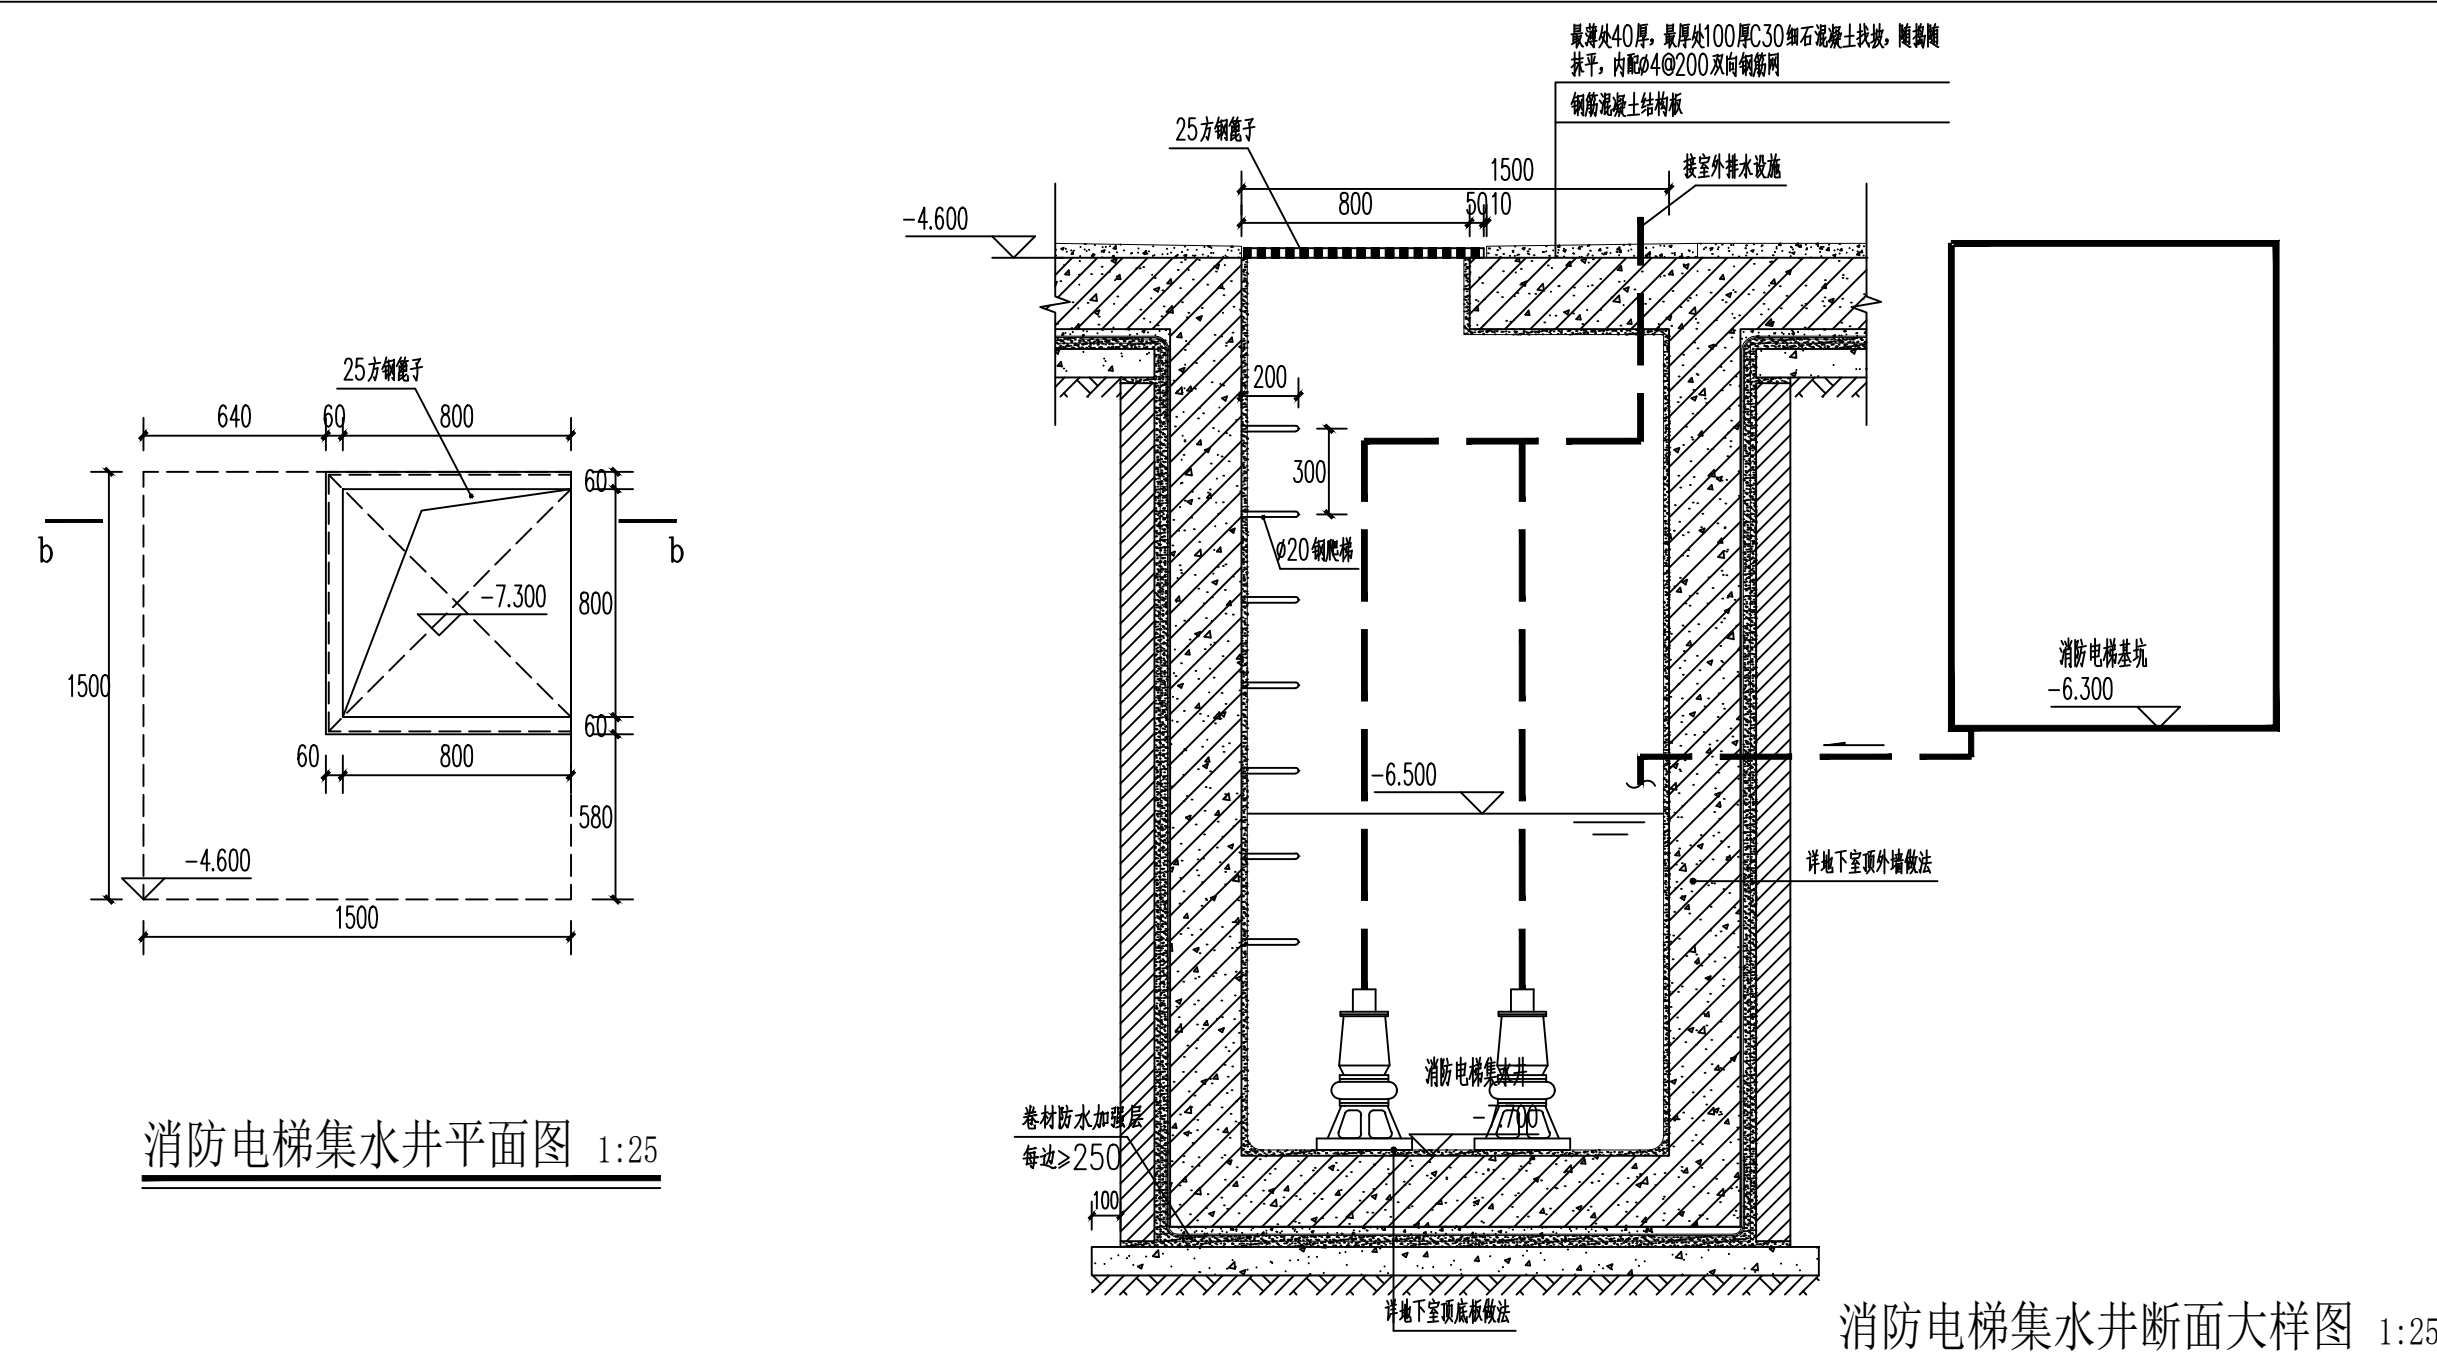

⑩消防电梯集水井大样图 1:25