




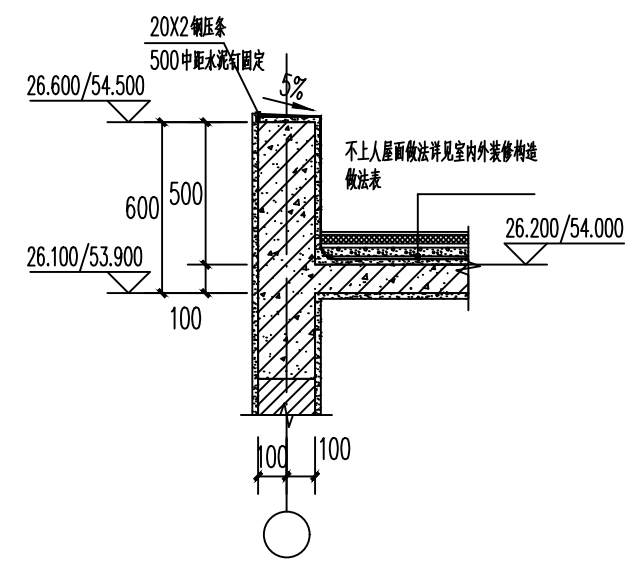


① 返边大样图 1:25

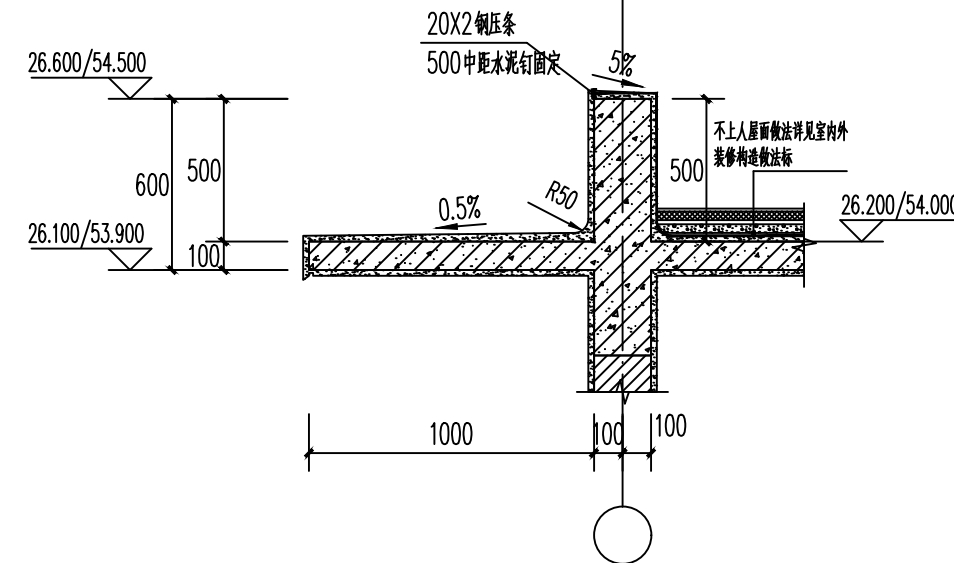


② 雨蓬大样图 1:25

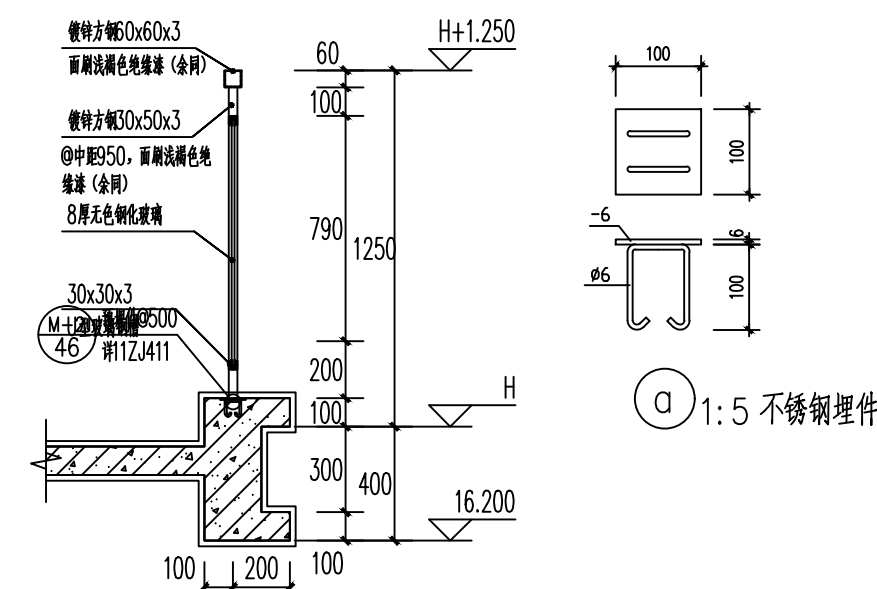


③ 阳台栏杆大样图 1:25

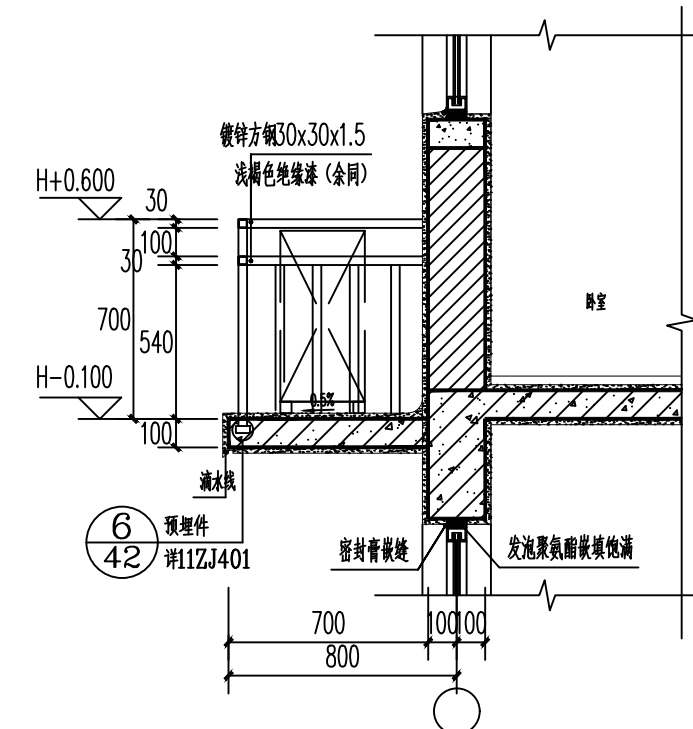


④ 空调板大样图 1:25

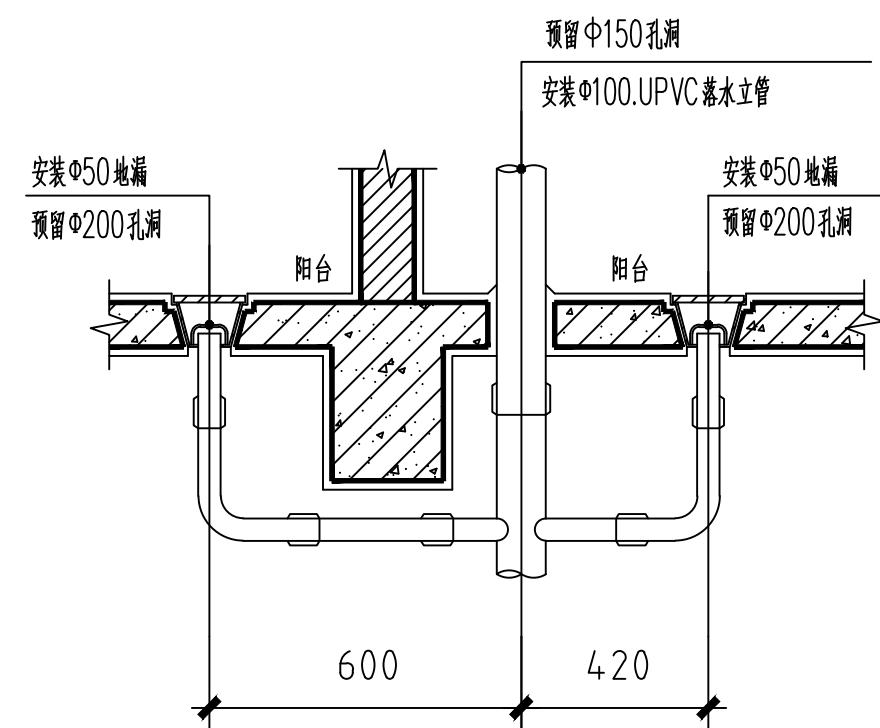


⑤ 双阳台排水大样图 1:25

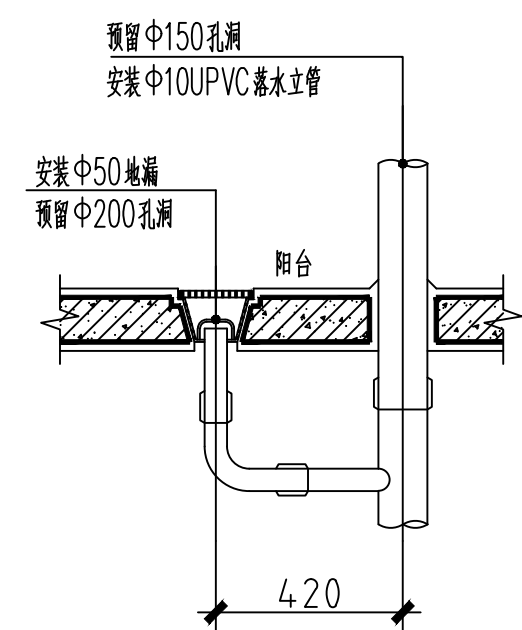


⑥单阳台排水大样图 1:25

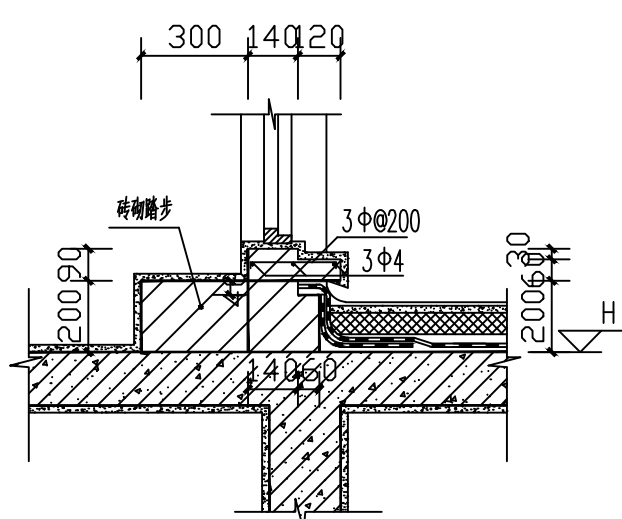


⑦ 屋顶出入口大样图 1:25

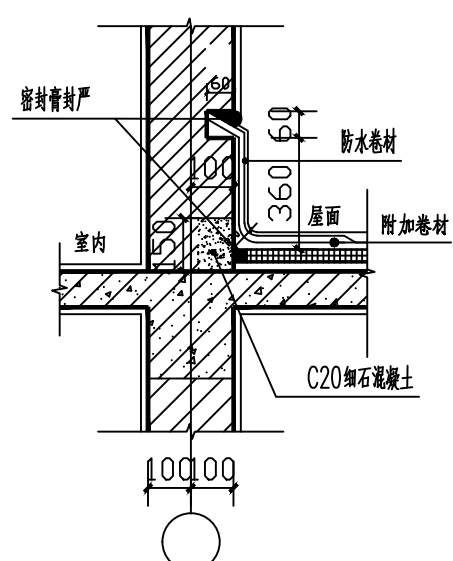


⑧ 屋面泛水大样图 1:25

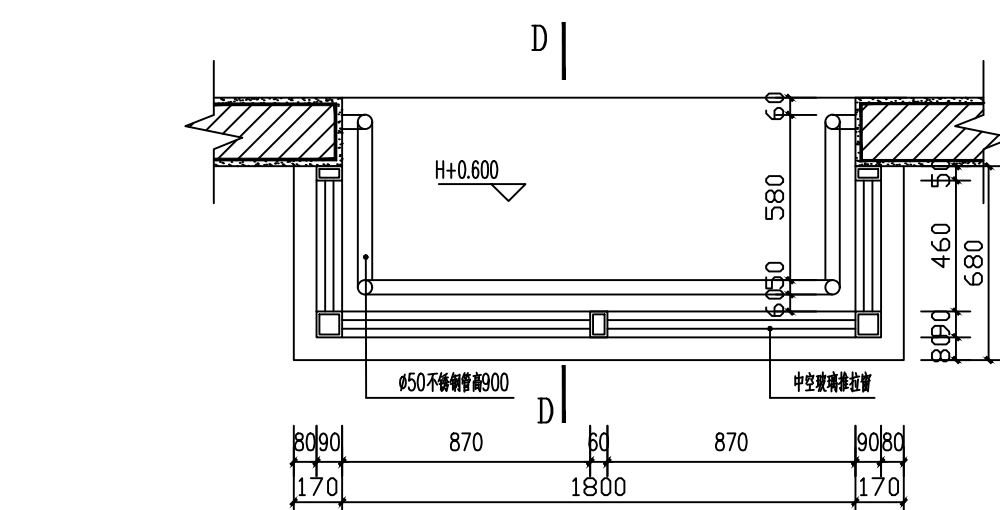

TC1平面图 1:20

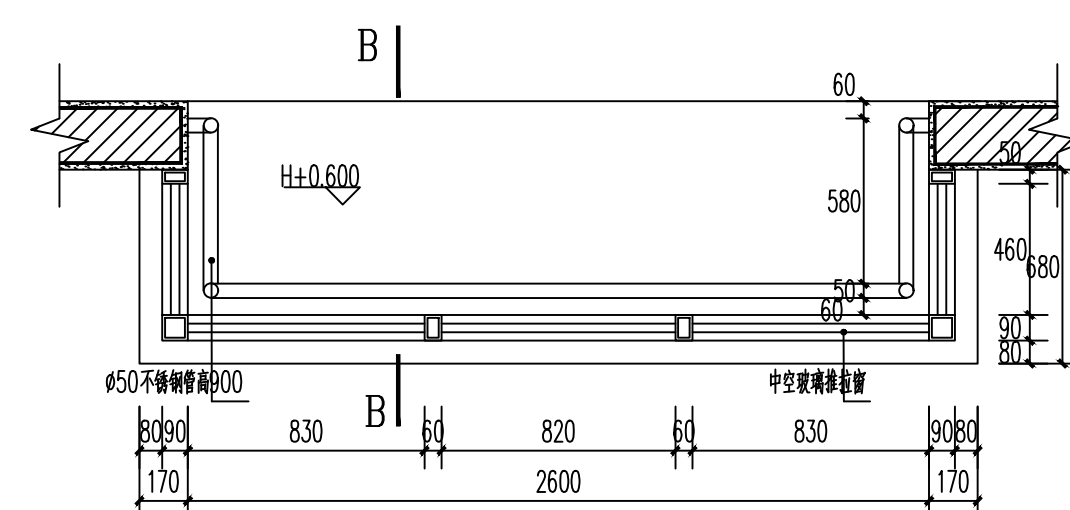


TC2平面图 1:20

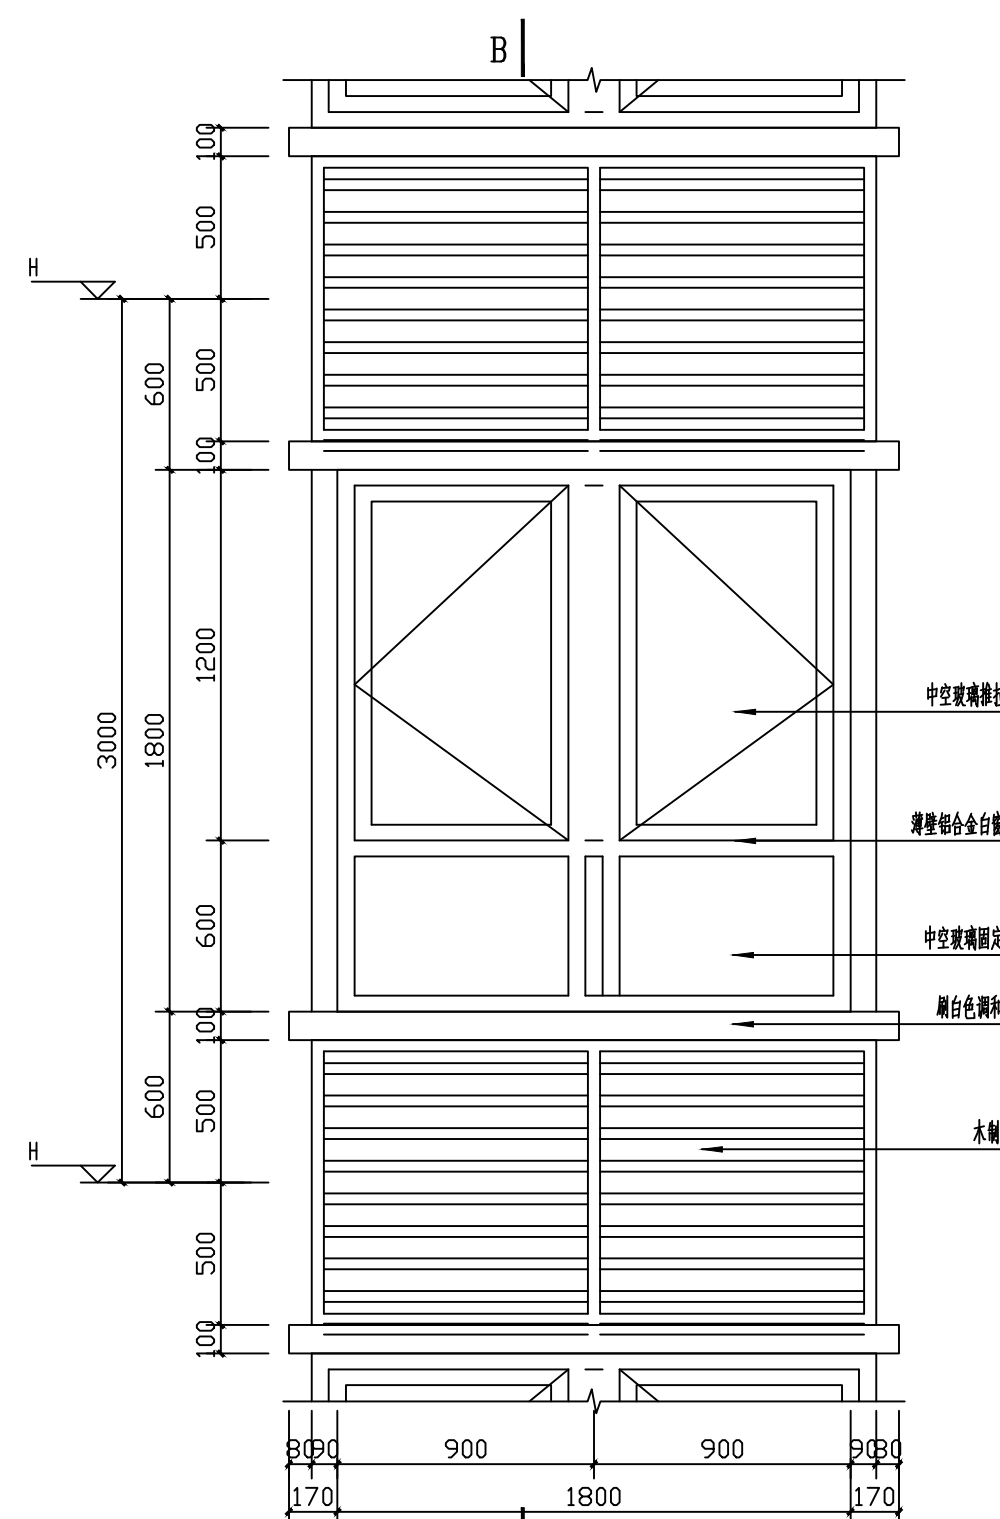

TC1立面 1:20



注: 所有凸窗设置百叶帘遮阳系统, 详11ZJ903(1/38)

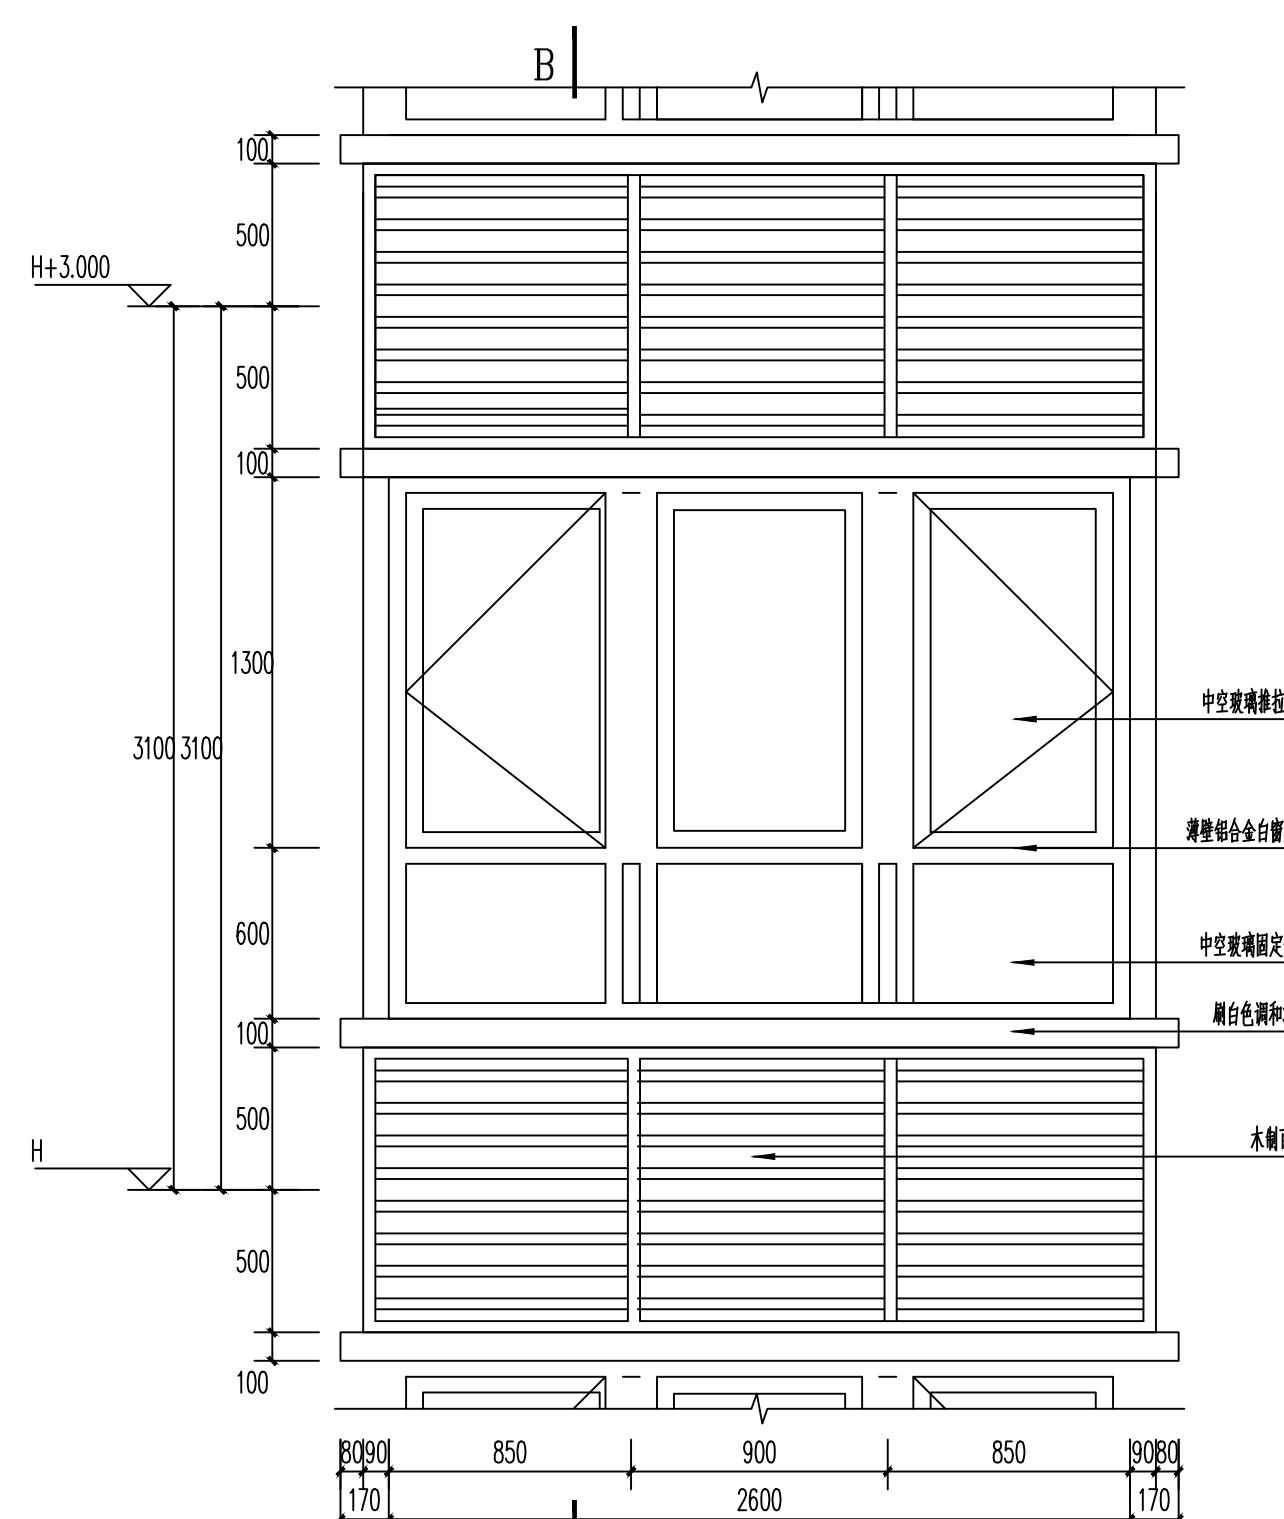

TC2立面 1:20



建设单位/CLIENT:

麻阳苗族自治县远桥房地产开发有限公司

项目名称/PROJECT:

远程国际

子项目名称/SUB-PROJECT:

远程国际

区位图/REGIONAL LOCATION MAP :



图纸名称/TITLE:

节点大样图三

项目名称/PROJECT:

远程国际

设计 DESIGNED	古新辉	
校对 CHECKED	吴新红	
专业负责人 CHIEF	吴志刚	
项目负责人 PROJECT CHIEF	吴志刚	
审核 IDENTIFIED	黄履优	
审定 APPROVED	李 坚	

业务号/JOB NO.

设计阶段/STATUS: 施工图

专业/DISCIPLINE: 建施

比例/ SCALE:	1: 100	规格/ SIZE:	A1
---------------	--------	--------------	----

出图日期/DATE: 2021.06

图号/DRAWING NO. JS-42

版次 NO.	修改内容 DESCRIPTION	日期 DATE

条形码/BARCODE:

版权所有，不得复制、套用。
ALL RIGHTS RESERVED, DON'T COPIED, REPRODUCED.