


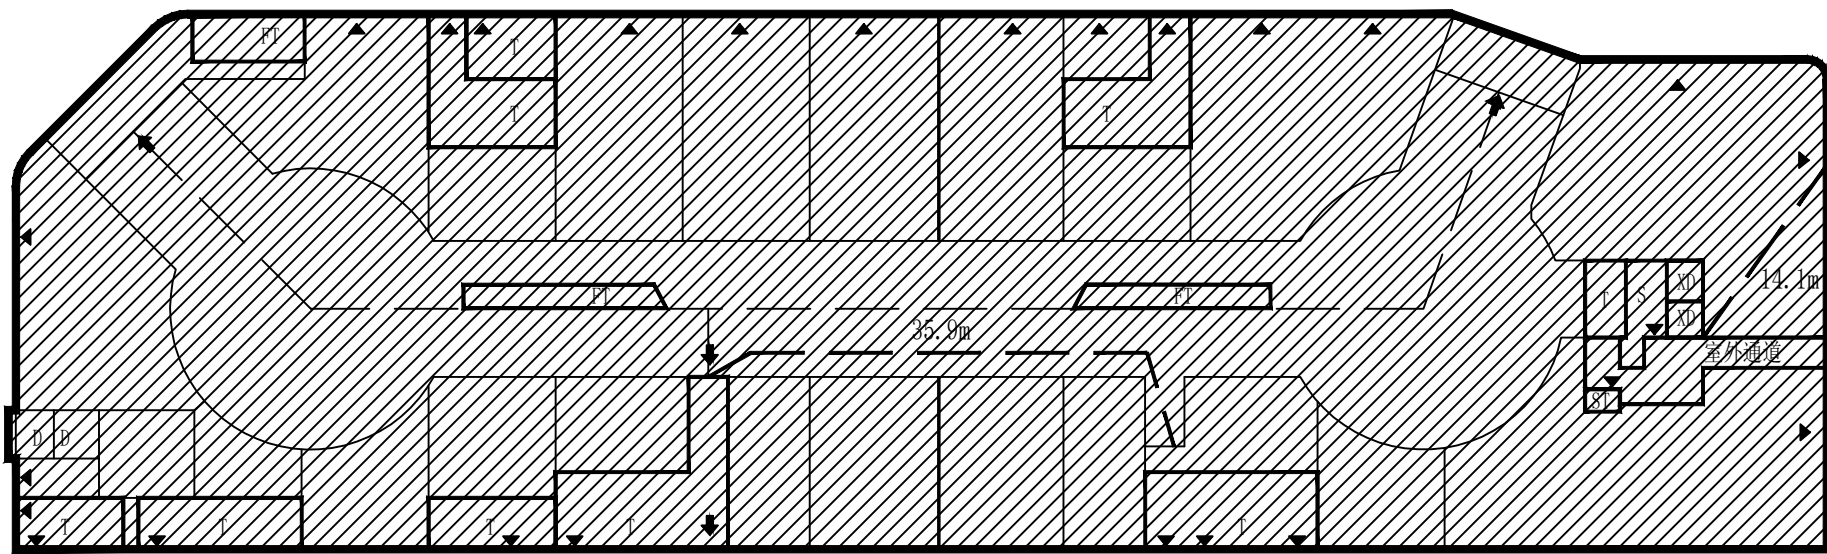

一层防火分区示意图 1:500


注：一层商场设置自动喷淋灭火系统
 本层为一个防火分区，防火分区面积为4129.28㎡，共有3个安全出口。
 房间内最远点至最近安全出口的距离为14.1m≤27.5m，最远疏散门至最近安全出口的距离为35.9m(≤37.5m)，满足规范要求。
 本层需要的疏散宽度为3692.11X0.43X1/100=15.87m(计算疏散宽度的面积是减掉一层所有楼梯间面积后的净面积)
 本层设计的疏散宽度为7.2X2+2.4=16.80m，满足规范要求。

一层平面图 1:150

本层建筑面积: 4129.28m²
总建筑面积: 22985.06m²
计容总建筑面积: 18157.36m²
不计容总建筑面积: 4827.70m²

图例

 灰砂加气混凝土砌块 (商铺隔墙)
 消火栓

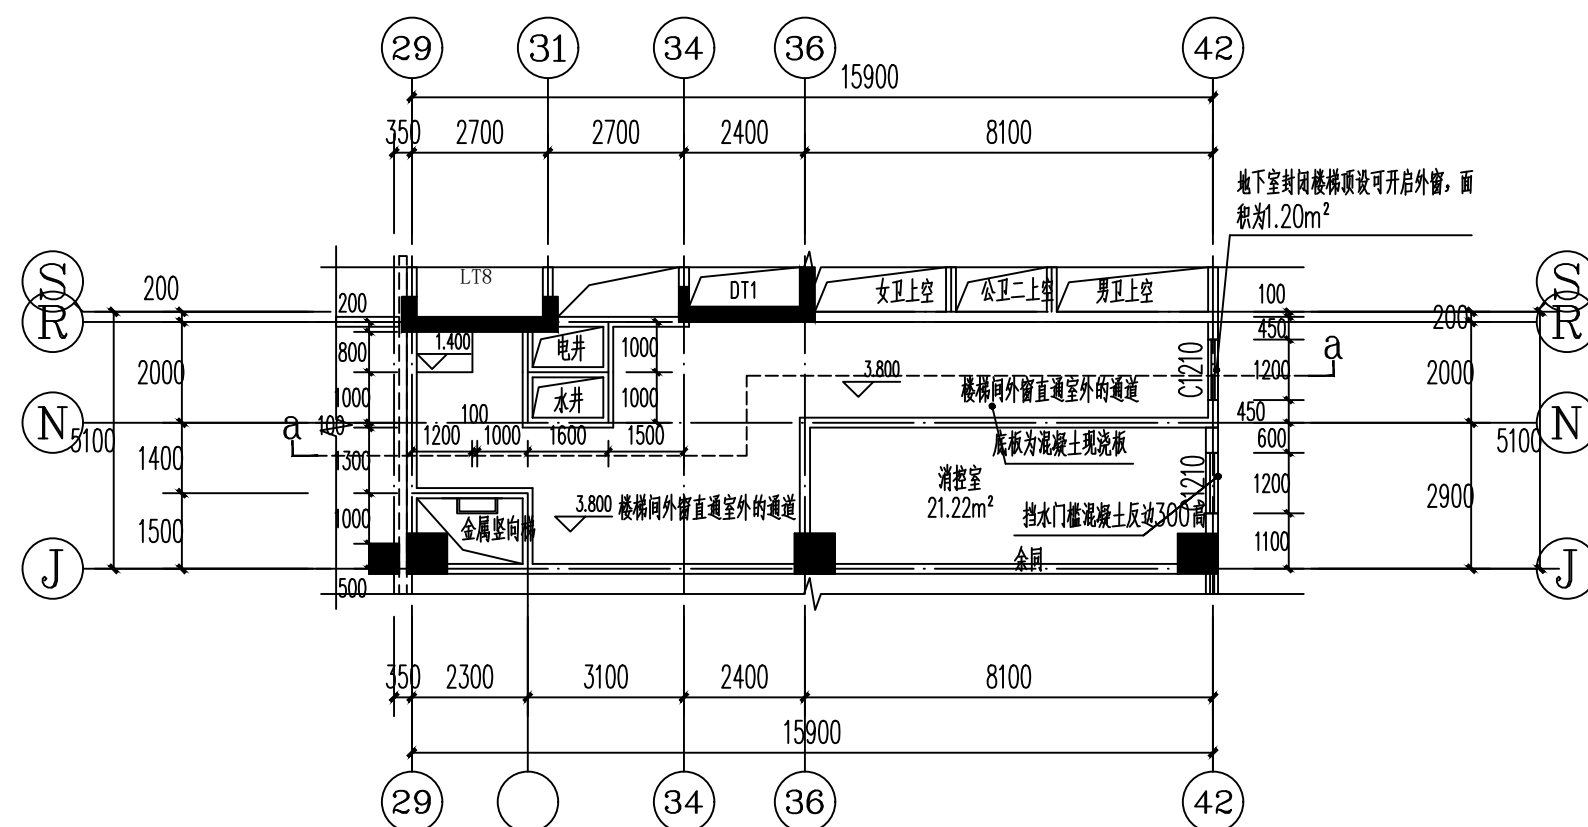

室外通道夹层平面图 1:150 注: a-a剖面图详IS-25

注明：

- 柱、柱位置尺寸详见详图。
- 除图中注明者外，门窗窗洞口的墙垛均为100mm或平柱、墙垛、墙中安装。
- 本工程所有外墙厚度均为240厚钢筋混凝土压加气混凝土砌块，墙垛墙体外侧均为100厚，内侧均为140厚。
商榷墙垛墙体外侧注明均为100厚灰砂加气混凝土砌块，其余墙垛均为200厚烧结实心页岩砖。
- 门窗台高小于900mm时，作防护栏杆具体做法详见11ZJ3401《建筑工程施工工艺安全操作规程》，防止人员坠落。
- 各种设备布置、管径、管进及埋设等具体做法应同时参照及配合专业图纸，以免遗漏。
- 本楼设自动喷淋灭火系统，消防栓位置见详图。
- 管道井及设备用房除防水进水的房间，下方应设300高C20混凝土盖板，厚度同楼板。
- 除室外外，卫生间明楼地面均标高+1.05；卫生间室间隔断墙顶部均为+1.03，以-1.12坡向地漏，（H为楼面标高），详见卫生间大详图。
- 所有外墙洞口、更衣室窗玻璃为钢化玻璃。
- 外墙窗洞口标高应比相应楼面完成面低26mm，并应有横坡过水，具体详见11ZJ-A-49。
- 外墙窗洞口标高11ZJ111-(A-26)，内窗洞口标高11ZJ111-(A-7)-4，地面标高11ZJ111-(A-7)-2，楼面完成面11ZJ111-(A-8)-1。
- 人行出入口及疏散门净高不小于2.1m的构造柱或墙体，其他地方设置不小于2m高的玻璃隔断，0.76mm厚双钢化玻璃夹层玻璃。
- 3-13疏散楼梯间门净宽不小于0.9mX1.0m，下楼梯室的地面不标+1.2m，同层标高+2.0m，未标明踏步，但位置可在室外寻识的楼梯图标，详见平面、立面图。
- 电梯轿厢净宽：轿厢1000X2200，轿厢宽1700X2200均同大样图不应小于1.0m，轿梯、扶梯梯宽+1.700，D3观光电梯轿厢内设防护栏杆。
- 玻璃幕墙自挑檐、悬空层的设置可参照《高规》总则第6.2.2条，开闭窗扇不大于3.2m。
- 玻璃幕墙玻璃与墙梁以及楼板的嵌固均采用弹性材料密封。
- 楼层门-玻璃窗在窗洞口内侧距洞口0.50m，内开或侧开，在玻璃窗下部做固定，固定高度为800mm或更高。
- 公共楼梯、电梯梯净宽为1.2m时，必须采取防止少年儿童攀登的措施，住宅建筑、电梯净宽为1.1m时，必须采取防止儿童攀登的措施。
- 图中各设备管洞尺寸及设备与设备专业图纸冲突时以设备专业图纸为准。

建设单位/CLIENT:

麻阳苗族自治县远桥房地产开发有限公司

项目名称/PROJECT:

远程国际

子项目名称/SUB-PROJECT:

远程国际

区位图/REGIONAL LOCATION MAP :



图纸名称/TITLE:

一层平面图

项目名称/PROJECT:

远程国际

设计 DESIGNED	古新辉	
校对 CHECKED	吴新红	
专业负责人 CHIEF	吴志刚	
项目负责人 PROJECT CHIEF	吴志刚	
审核 IDENTIFIED	黄履优	
审定 APPROVED	李 坚	

业务号/JOB NO.

设计阶段/STATUS: 施工图

专业/DISCIPLINE: 建施

比例/ SCALE:	1: 100
---------------	--------

出图日期/DATE: 2021.06

图号/DRAWING NO. JS-14

版次 NO.	修改内容 DESCRIPTION	日期 DATE

条形码/BARCODE:

版权所有，不得复制、套用。
ALL RIGHTS RESERVED, DON'T COPIED, REPRODUCED.