


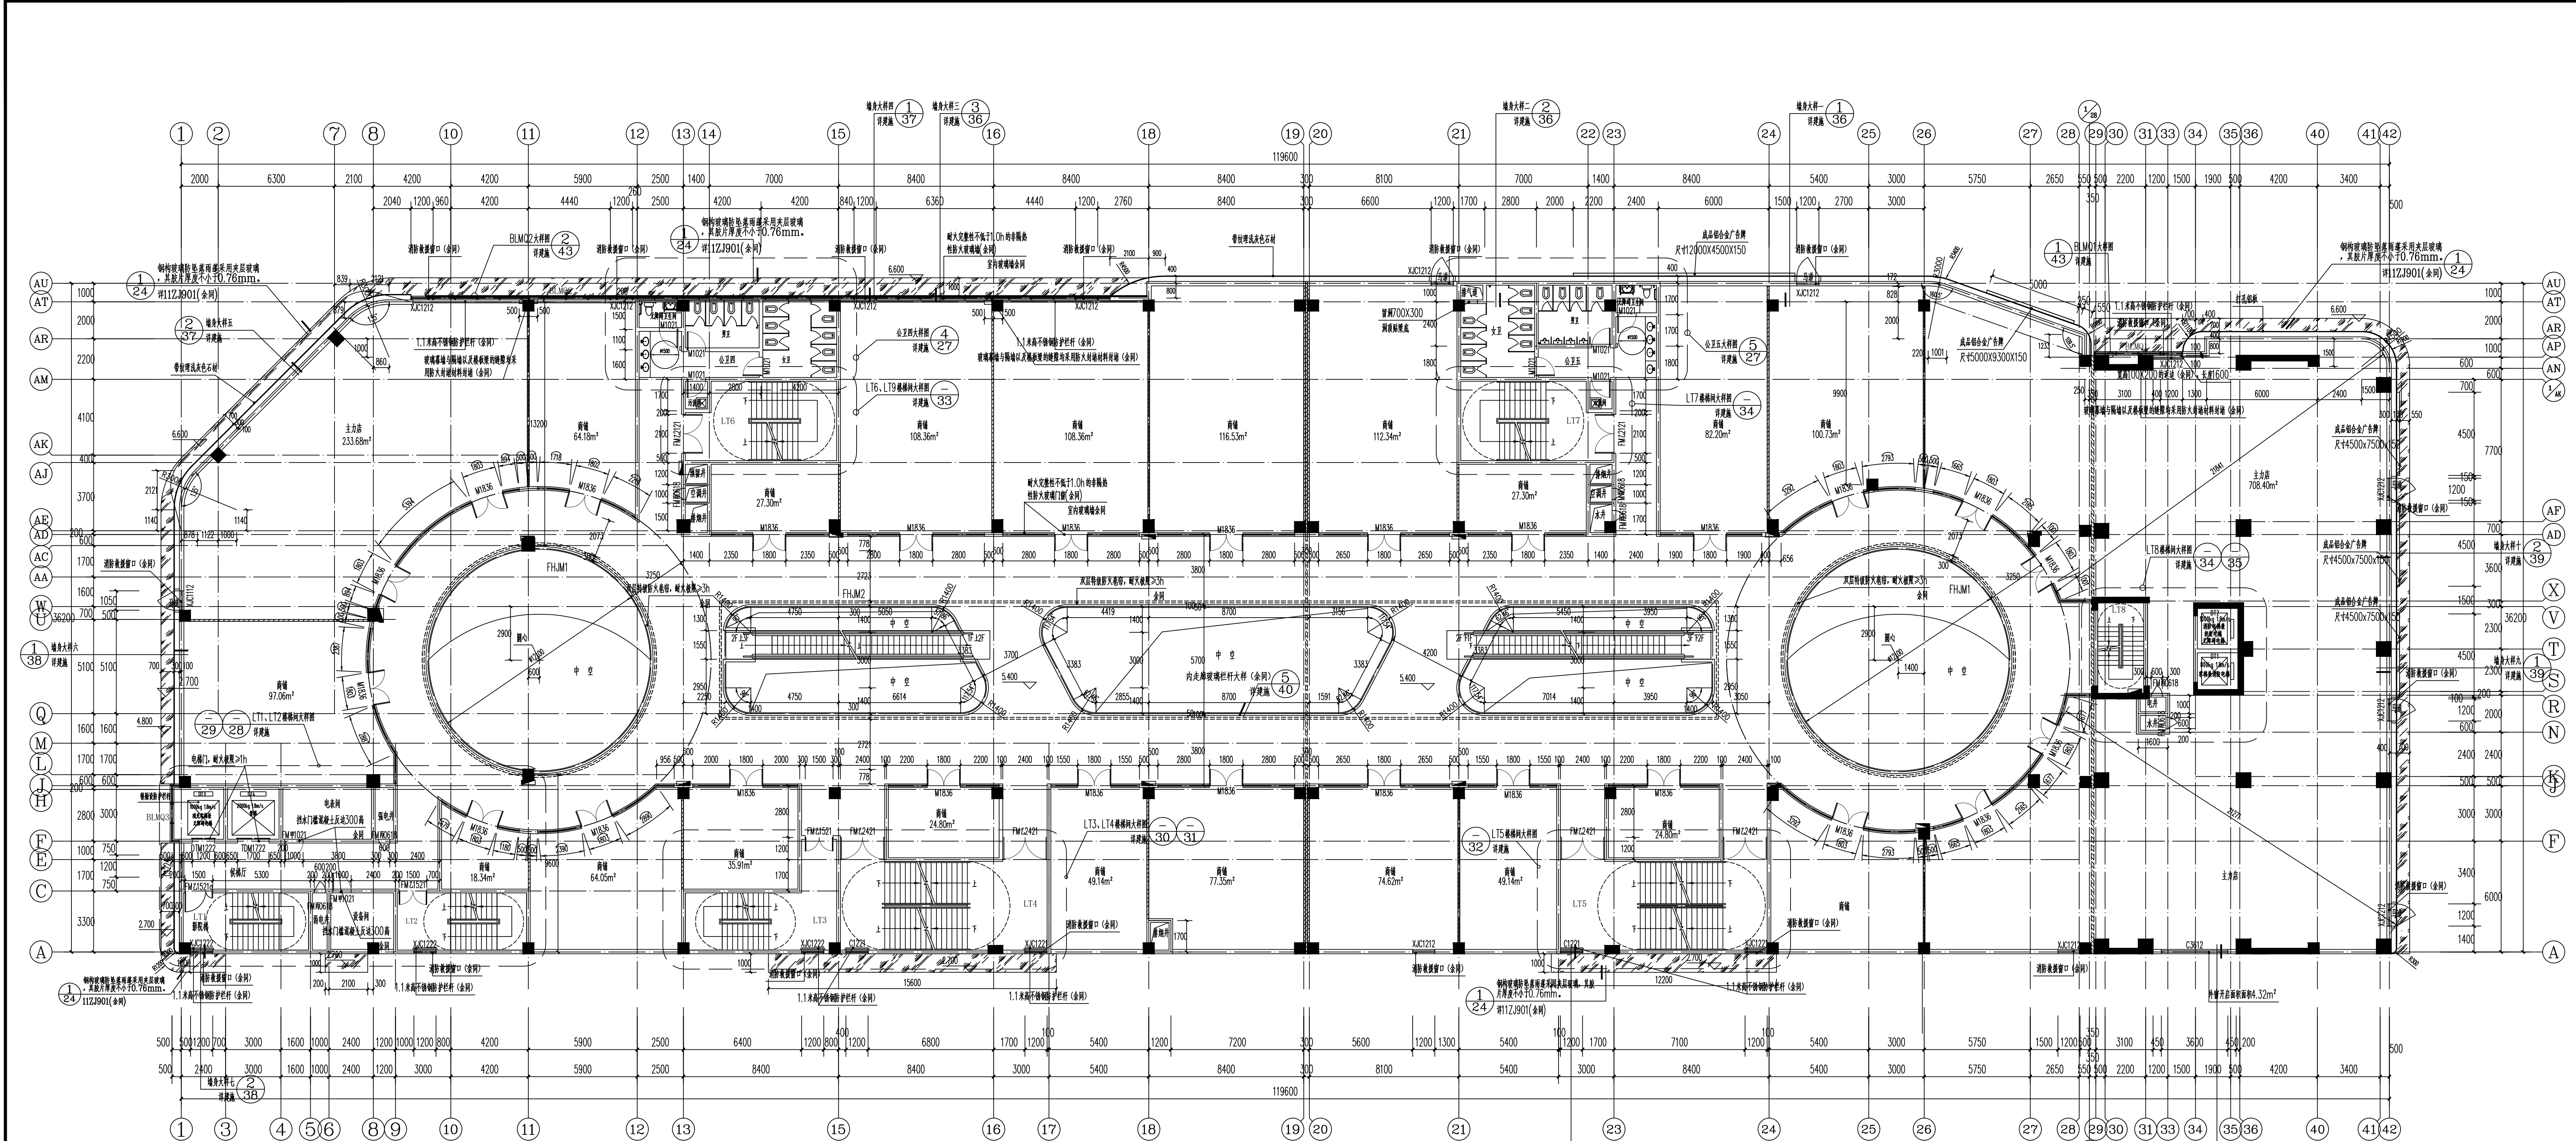


二层平面图 1:150

本层建筑面积：3767.79m²

图例

灰砂加气混凝土砌块（商隔隔墙）

消火栓

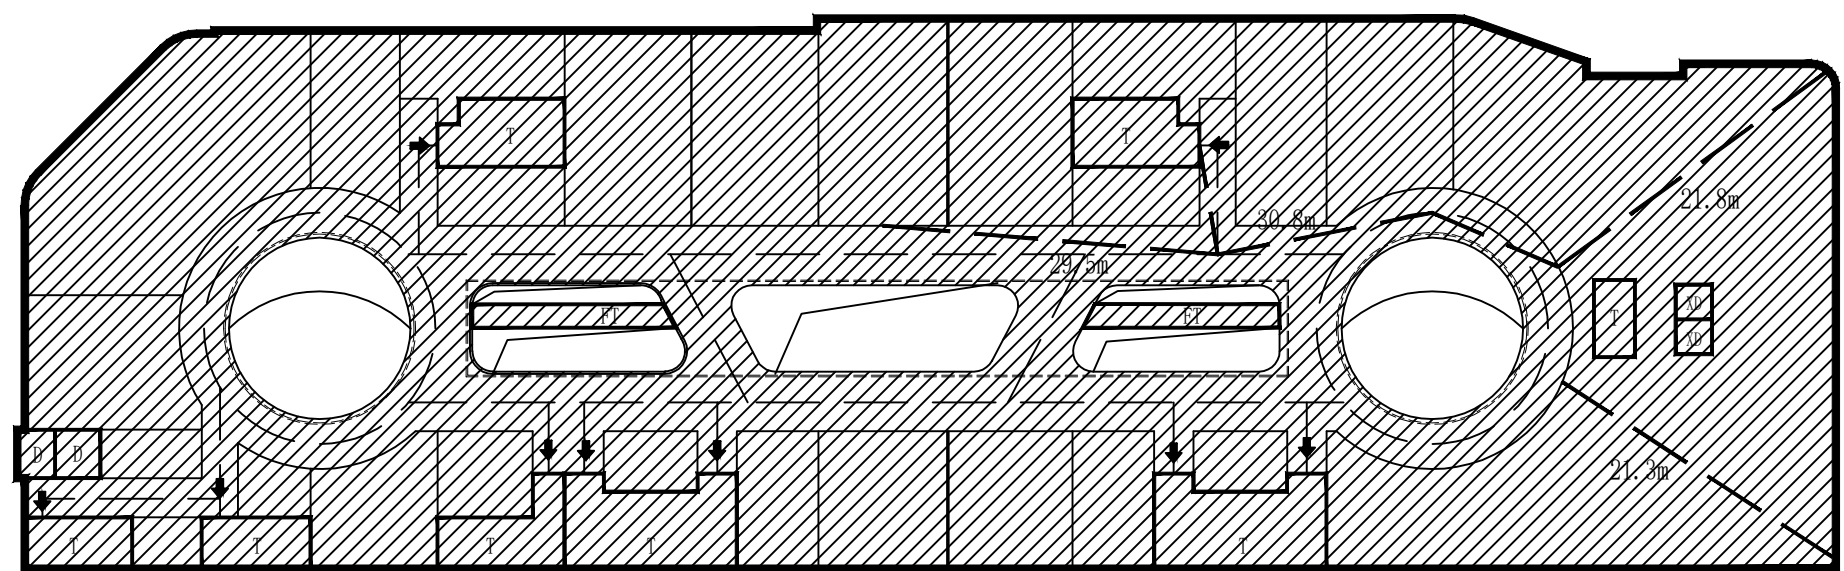

二层防火分区示意图 1:500

消防示意图例

S	合用前室及前室
T	疏散楼梯
ST	金属楼梯
D	客梯、货梯
FT	自动扶梯
XD	消防电梯
➡	安全出口

注：二层商场设置自动喷淋灭火系统

本层为一个防火分区，防火分区面积为3767.79m²，共有9个疏散楼梯，9个安全出口，其中LT11楼梯间为影院独有楼梯间。
房间内最远点至最近安全出口的距离为21.8m(≤27.5m)，最近疏散门至最近安全出口的距离为30.8m(≤37.5m)，满足规范要求。
本层需要的疏散宽度为3739.78X0.43X1/100=16.08m(计算疏散宽度的面积是减掉本层住宅楼梯间、消防电梯间面积的净面积)
本层设计的疏散宽度为2X1.475+2.325X2+2.34X2+2X2.075=16.43m，满足规范要求。

注明：

- 柱布置尺寸详结构图。
- 除图中除注明者外，门窗留洞处的墙垛均100mm或平柱、墙垛、墙中安装。
- 本工程所有外墙厚度均按240厚粉煤灰蒸压加气混凝土砌块，墙垛墙体外侧均100厚，内侧均40厚。
商隔隔墙除特殊注明外均100厚灰砂加气混凝土砌块，其余墙垛均200厚粉煤灰蒸压加气混凝土砌块。
- 凡窗台高小于900mm时，作防护栏杆具体做法详12J1401《栏杆制作要符合安全防护要求，以防上人攀爬。
- 各设备布置、管径、管架及附件等具体做法详12J1401《栏杆制作要符合安全防护要求，以防上人攀爬。
- 本建筑设自动喷淋灭火系统，消火栓位置见水施。
- 管道及设备同层敷设时，下方均设300mmC20混凝土门框，宽度同墙厚。
- 除注明外，卫生间楼地面标高均+0.05；卫生间前室楼面标高均+0.03。同=1%坡向地漏，（H为楼面标高），详见卫生间大样图。
- 所有室外卫生间、更衣室管道均为磨砂玻璃。
- 无障碍卫生间完成面与相应楼面完成面高差5mm，并应有坡度设置，具体详见卫生间详图。
- 外墙变形缝12J111-(A)-2-26，内墙及顶棚变形缝12J111-(A)-4-9，地面变形缝12J111-(A)-7-2，楼面变形缝12J111-(A)-8-1。
- 人行安全出入口除2个主出入口的钢梯结构外，其他地方设置外挑1.2m钢梯或外挑0.76mm厚双层钢化夹胶玻璃。
- 消防疏散出口的净宽均不小于1.0mX1.0m，下净距室内地面不大于1.2m，间距不大于2.0m，采用断桥玻璃，并应设置可在室外易于识别的明显标志，详见平面、立面图。
- 电梯层门客梯：洞口100X2200，货梯：洞口700X2200的耐火极限不应低于1.00h，客梯、货梯均按1.700m³D3观光电梯梯内应设防护栏。
- 楼梯间自然通风，每五层内设置可开启外窗面积不小于2m²，开闭间隔不大于三层。
- 各层楼梯间墙与隔墙以及楼梯间的墙体均采用防火材料封堵。
- 楼梯之间相邻的门洞口间距为800mm，间距不够的，在梯间外墙做设，设设高度为800mm高玻璃。
- 公共楼梯、客梯井净宽大于0.2m时，必须采取防止少年儿童坠落的措施；住宅楼梯、客梯井净宽大于0.11m时，必须采取防止儿童攀援的措施。
- 图注各设备尺寸均与相关设备厂家提供的尺寸为准。

建设单位/CLIENT:
麻阳苗族自治县远桥房地产开发有限公司

项目名称/PROJECT:
远程国际

子项目名称/SUB-PROJECT:
远程国际

区位图/REGIONAL LOCATION MAP:

广东建筑艺术设计院有限公司
GUANGDONG ARCHITECTURAL ARTISTIC DESIGN INSTITUTE CO.,LTD
■ 建筑方案设计：甲级 ■ 风景园林设计：乙级
■ 施工图设计：乙级 ■ 市政设计：乙级

图纸名称/TITLE:
二层平面图

项目名称/PROJECT:
远程国际

设计 DESIGNED	古新辉	
校对 CHECKED	吴新红	
专业负责人 CHIEF	吴志刚	
项目负责人 PROJECT CHIEF	吴志刚	
审核 IDENTIFIED	黄履优	
审定 APPROVED	李 坚	

业务号/JOB NO.
设计阶段/STATUS: 施工图

专业/DISCIPLINE: 建筑

比例/
SCALE: 1: 100 规格/
SIZE: A1

出图日期/DATE: 2021.06

图号/DRAWING NO. JS-15

版次 NO.	修改内容 DESCRIPTION	日期 DATE

条形码/BARCODE:

版权所有，不得复制或、套用。
ALL RIGHTS RESERVED, DON'T COPIED, REPRODUCED.