


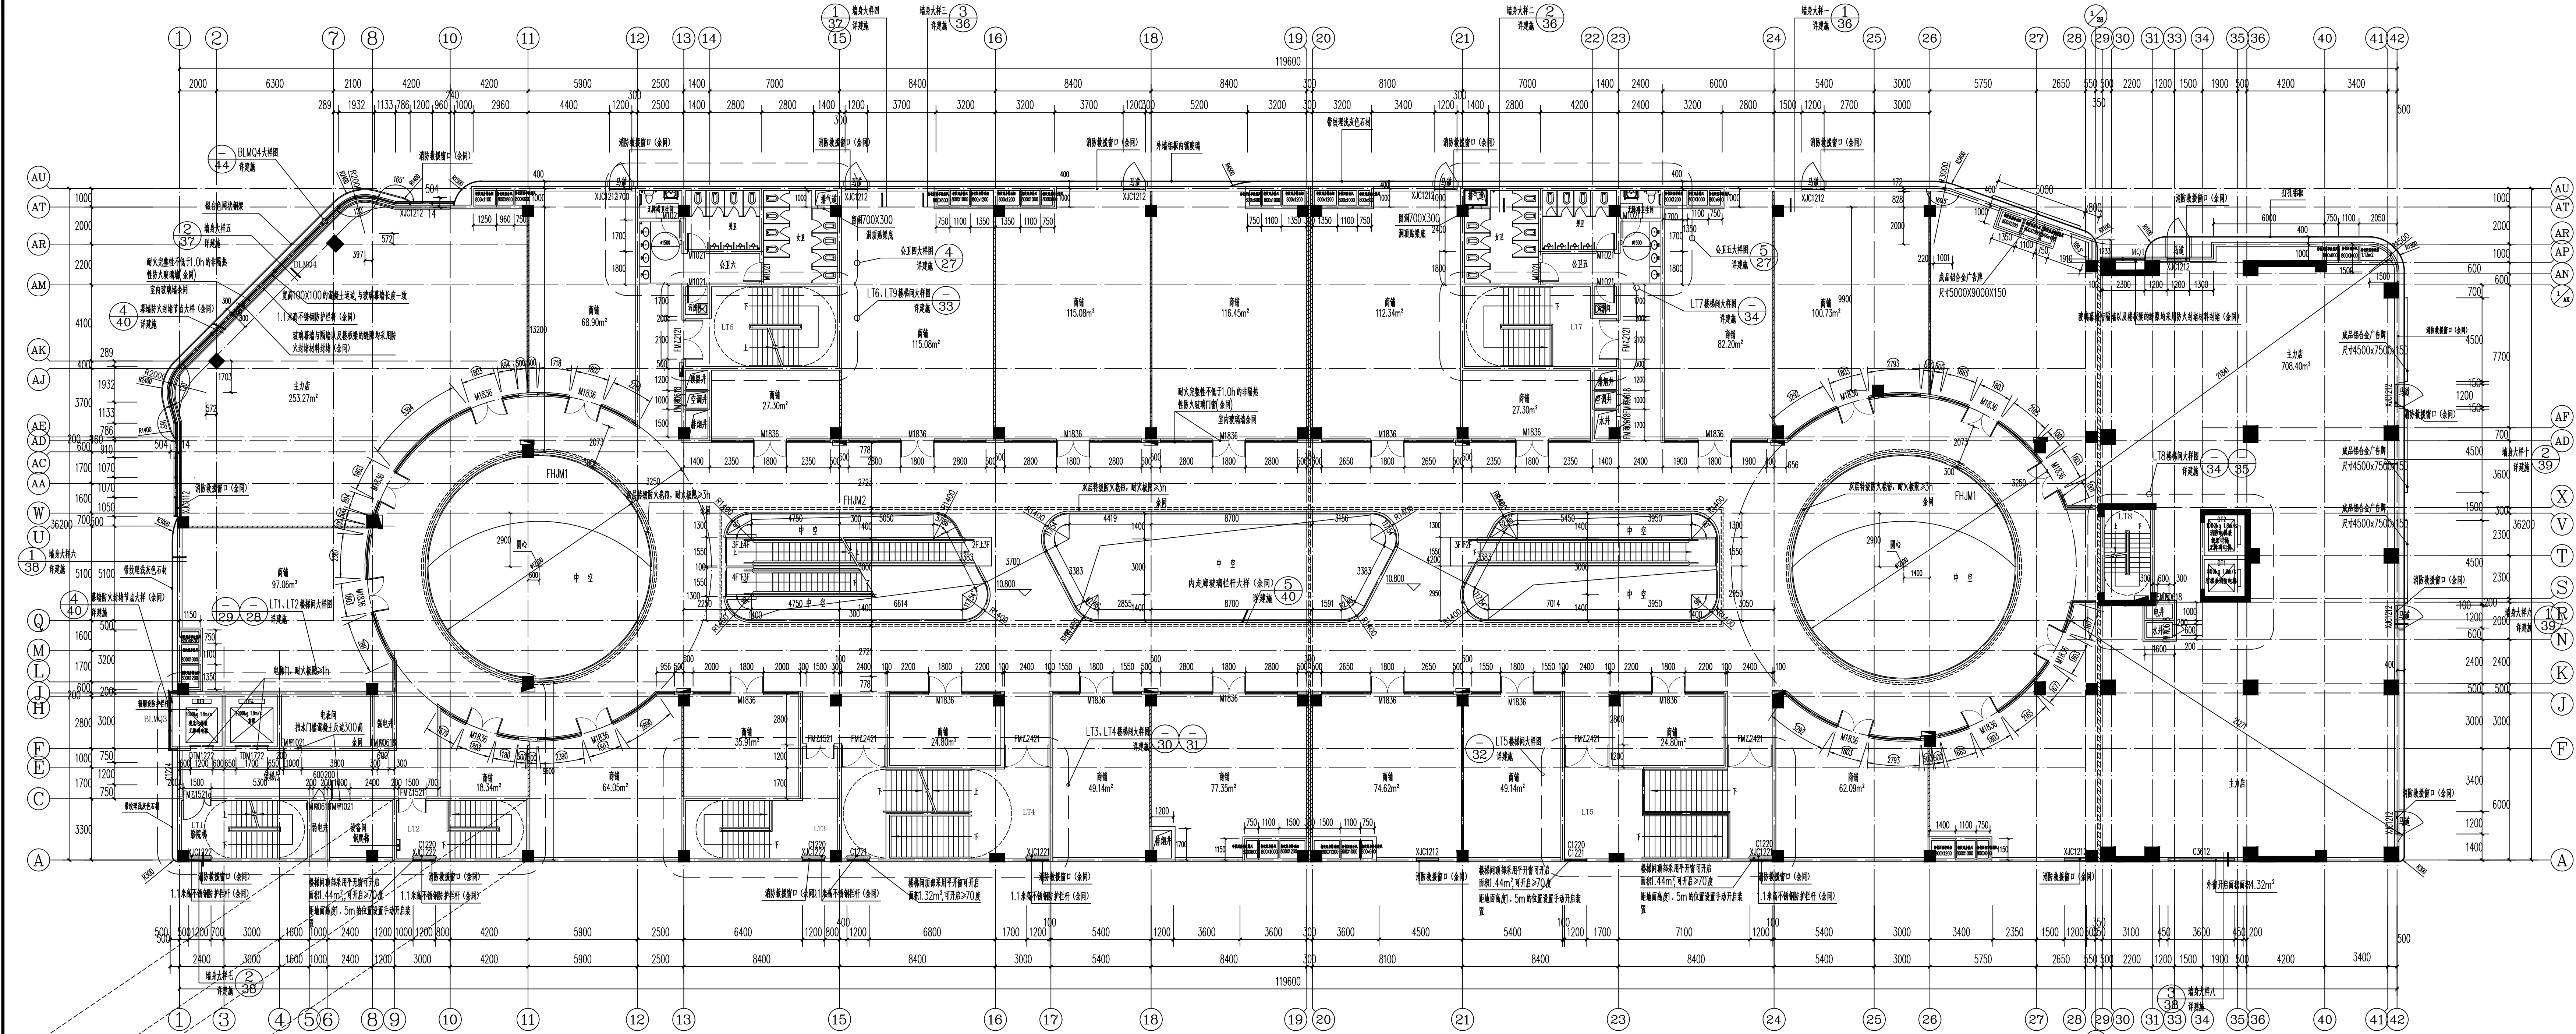

三层平面图 1:150

本层建筑面积: 3837.23m²

图例

灰砂加气混凝土砌块 (商铺隔墙)

消火栓

三层防火分区示意图 1:500

消防示意图例

|    |         |
|----|---------|
| S  | 合用前室及前室 |
| T  | 疏散楼梯    |
| ST | 金属楼梯    |
| D  | 客梯、货梯   |
| FT | 自动扶梯    |
| XD | 消防电梯    |
| ➡  | 安全出口    |

注: 三层商场设置自动喷淋灭火系统

本层为一个防火分区, 防火分区面积为3837.23m², 共有9个疏散楼梯, 9个安全出口, 其中LT11楼梯间为影院独有楼梯间。  
房间内最远点至最近安全出口的距离为21.8m(≤27.5m), 最近疏散门至最近安全出口的距离为30.8m(≤37.5m), 满足规范要求。  
本层需要的疏散宽度为3809.22X0.39X1/100+14.86m(计算疏散宽度的面积是减掉本层住宅楼梯间、消防电梯间面积的净面积)  
本层设计的疏散宽度为2X1.475+2.325X2+2.34X2+2X2.075=16.43m, 满足规范要求。

注明:

- 柱布置尺寸详结构图。
- 除图中除注明者外, 门窗洞口的墙体均为100mm厚平柱, 墙中安装。
- 本工程所有外墙厚度均为240mm厚粉煤灰蒸压加气混凝土砌块, 墙体厚度外侧100mm, 内侧为40mm。  
商铺隔墙除特殊注明外均为100mm厚灰砂加气混凝土砌块, 其余墙体均为200mm厚烧结页岩多孔砖。
- 凡窗台高小于900mm时, 作防护栏杆具体做法详见1Z J401。玻璃幕墙作符合安全防护要求, 以防止人攀爬。
- 各种设备管道、穿墙孔、管井及附件等具体做法详同时对照各专业图纸, 以免遗漏。
- 本建筑设自动喷淋灭火系统, 消防栓位置见水池。
- 管进井及设备间防水溢进房间, 门下方设300mm宽C20混凝土门槛, 宽度同墙厚。
- 除注明外, 卫生间楼面标高均为+0.05; 卫生间楼面标高均为+0.03, 以=1%坡度向地漏, (H为楼面标高), 详见卫生间大样图。
- 所有意外卫生间、更衣室玻璃均为磨砂玻璃。
- 无隔墙卫生间完成面比相应楼面完成面低5mm, 并应有坡度坡, 具体详见卫生间详图。
- 外墙变形缝缝1Z J111-(A-2)-26, 内墙及顶棚变形缝缝1Z J111-(A-4)-9, 地面变形缝缝1Z J111-(A-7)-2, 楼面变形缝缝1Z J111-(A-8)-1。
- 人行安全出入口除T2个出入口的钢化玻璃外, 其他地方设置外挑2m钢化玻璃雨篷, 0.76mm厚双层钢化夹层玻璃。
- 消防疏散出口的净宽均不小于1.0mX1.0m, 下脚距距地面不大于1.2m, 间距不大于2m, 采用钢化玻璃, 并应设置在室外易于识别的明显标志, 详见平面、立面图。
- 电梯层门客梯(洞口100X2200), 货梯(洞口700X2200)的耐火极限不应低于1.0h, 客梯、货梯基台+1.700。D3观光电梯轿厢内应设防护栏。
- 楼梯间自然通风, 每五层内设置可开启外窗总面积≥2m², 开窗间隔不大于三层。
- 各层玻璃幕墙与隔墙以及楼板的墙体均采用防火封堵材料封堵。
- 楼层之间竖向的门窗洞口间距≥800mm, 间距不够的, 在楼层外墙做进深, 进深高度为800mm高。
- 公共建筑, 当楼梯净宽大于0.2m时, 必须采取防止少年儿童攀爬的措施; 住宅建筑, 楼梯净宽大于0.11m时, 必须采取防止儿童攀爬的措施。
- 图中设备预留尺寸及位置与设备专业图纸冲突时及时通知设计院。

建设单位/CLIENT:

麻阳苗族自治县远桥房地产开发有限公司


项目名称/PROJECT:

远程国际

子项目名称/SUB-PROJECT:

远程国际

区位图/REGIONAL LOCATION MAP:

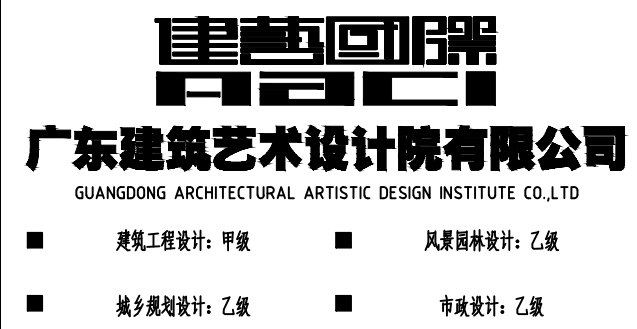

图纸名称/TITLE:

三层平面图

项目名称/PROJECT:

远程国际

设计

古新辉

校对

吴新红

专业负责人

吴志刚

项目负责人

吴志刚

审核

黄履优

审定

李 坚

业务号/JOB NO.

设计阶段/STATUS: 施工图

专业/DISCIPLINE: 建筑

比例/SCALE: 1: 100

规格/SIZE: A1

出图日期/DATE: 2021. 06

图号/DRAWING NO. JS-16

版次

修改内容

DESCRIPTION

日期

DATE

条形码/BARCODE:

版权所有, 不得复制或套用。  
ALL RIGHTS RESERVED, DON'T COPIED, REPRODUCED.