

建设单位/CLIENT:

麻阳苗族自治县远桥房地产开发有限公司


项目名称/PROJECT:

远程国际

子项目名称/SUB-PROJECT:

远程国际

区位图/REGIONAL LOCATION MAP :

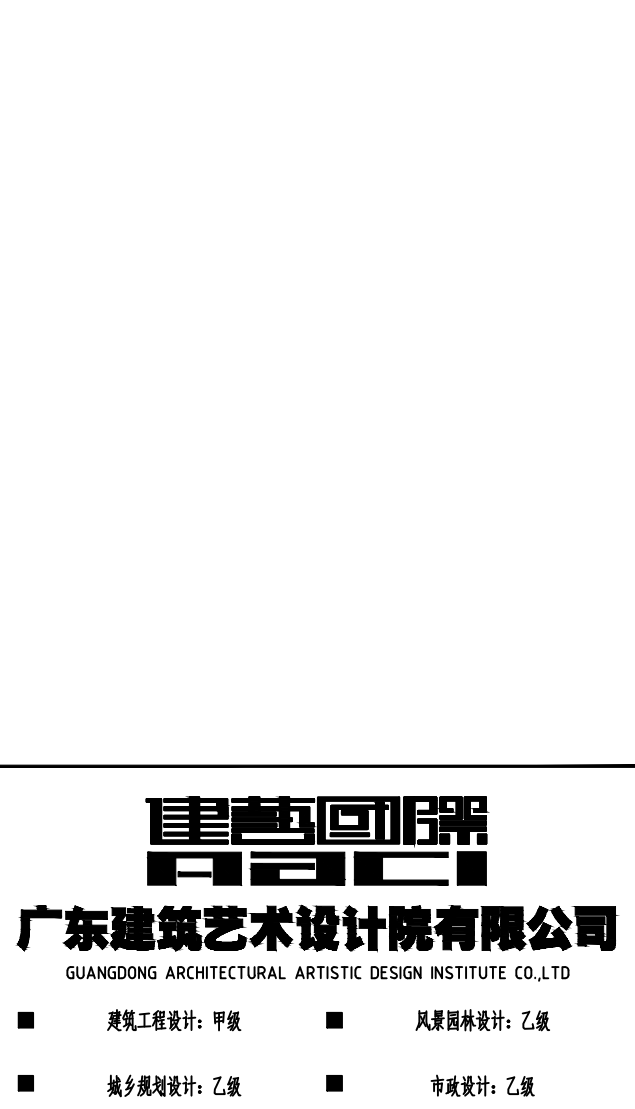

图纸名称/TITLE:

商业屋顶平面图
商业屋顶构件平面图

项目名称/PROJECT:

远程国际

NAME		NO.
------	--	-----

DESIGNED		
----------	--	---

CHECKED	大新江	美打江
---------	-----	-----

专业负责人 CHIEF	吴志刚	吴志刚
----------------	-----	-----

项目负责人
PROJECT CHIEF

吴志刚

吴志刚

审核 IDENTIFIED	黄履优	
------------------	-----	---

审定 APPROVED	李 坚	
----------------	-----	---

业务号/JOB NO.

设计阶段/STATUS: 施工图

专业 / DISCIPLINE: 建筑

比例/		规格/	
-----	--	-----	--

SCALE.		SIZE.	
--------	--	-------	--

FIG. 97 DRAWING NO. 35 10


版次 NO.	修改内容 DESCRIPTION	日期 DATE
-----------	---------------------	------------

[illegible][illegible]

条形码/BARCODE:

版权所有 不得复制 李田

ALL RIGHTS RESERVED, DON'T COPY, REPRODUCED.

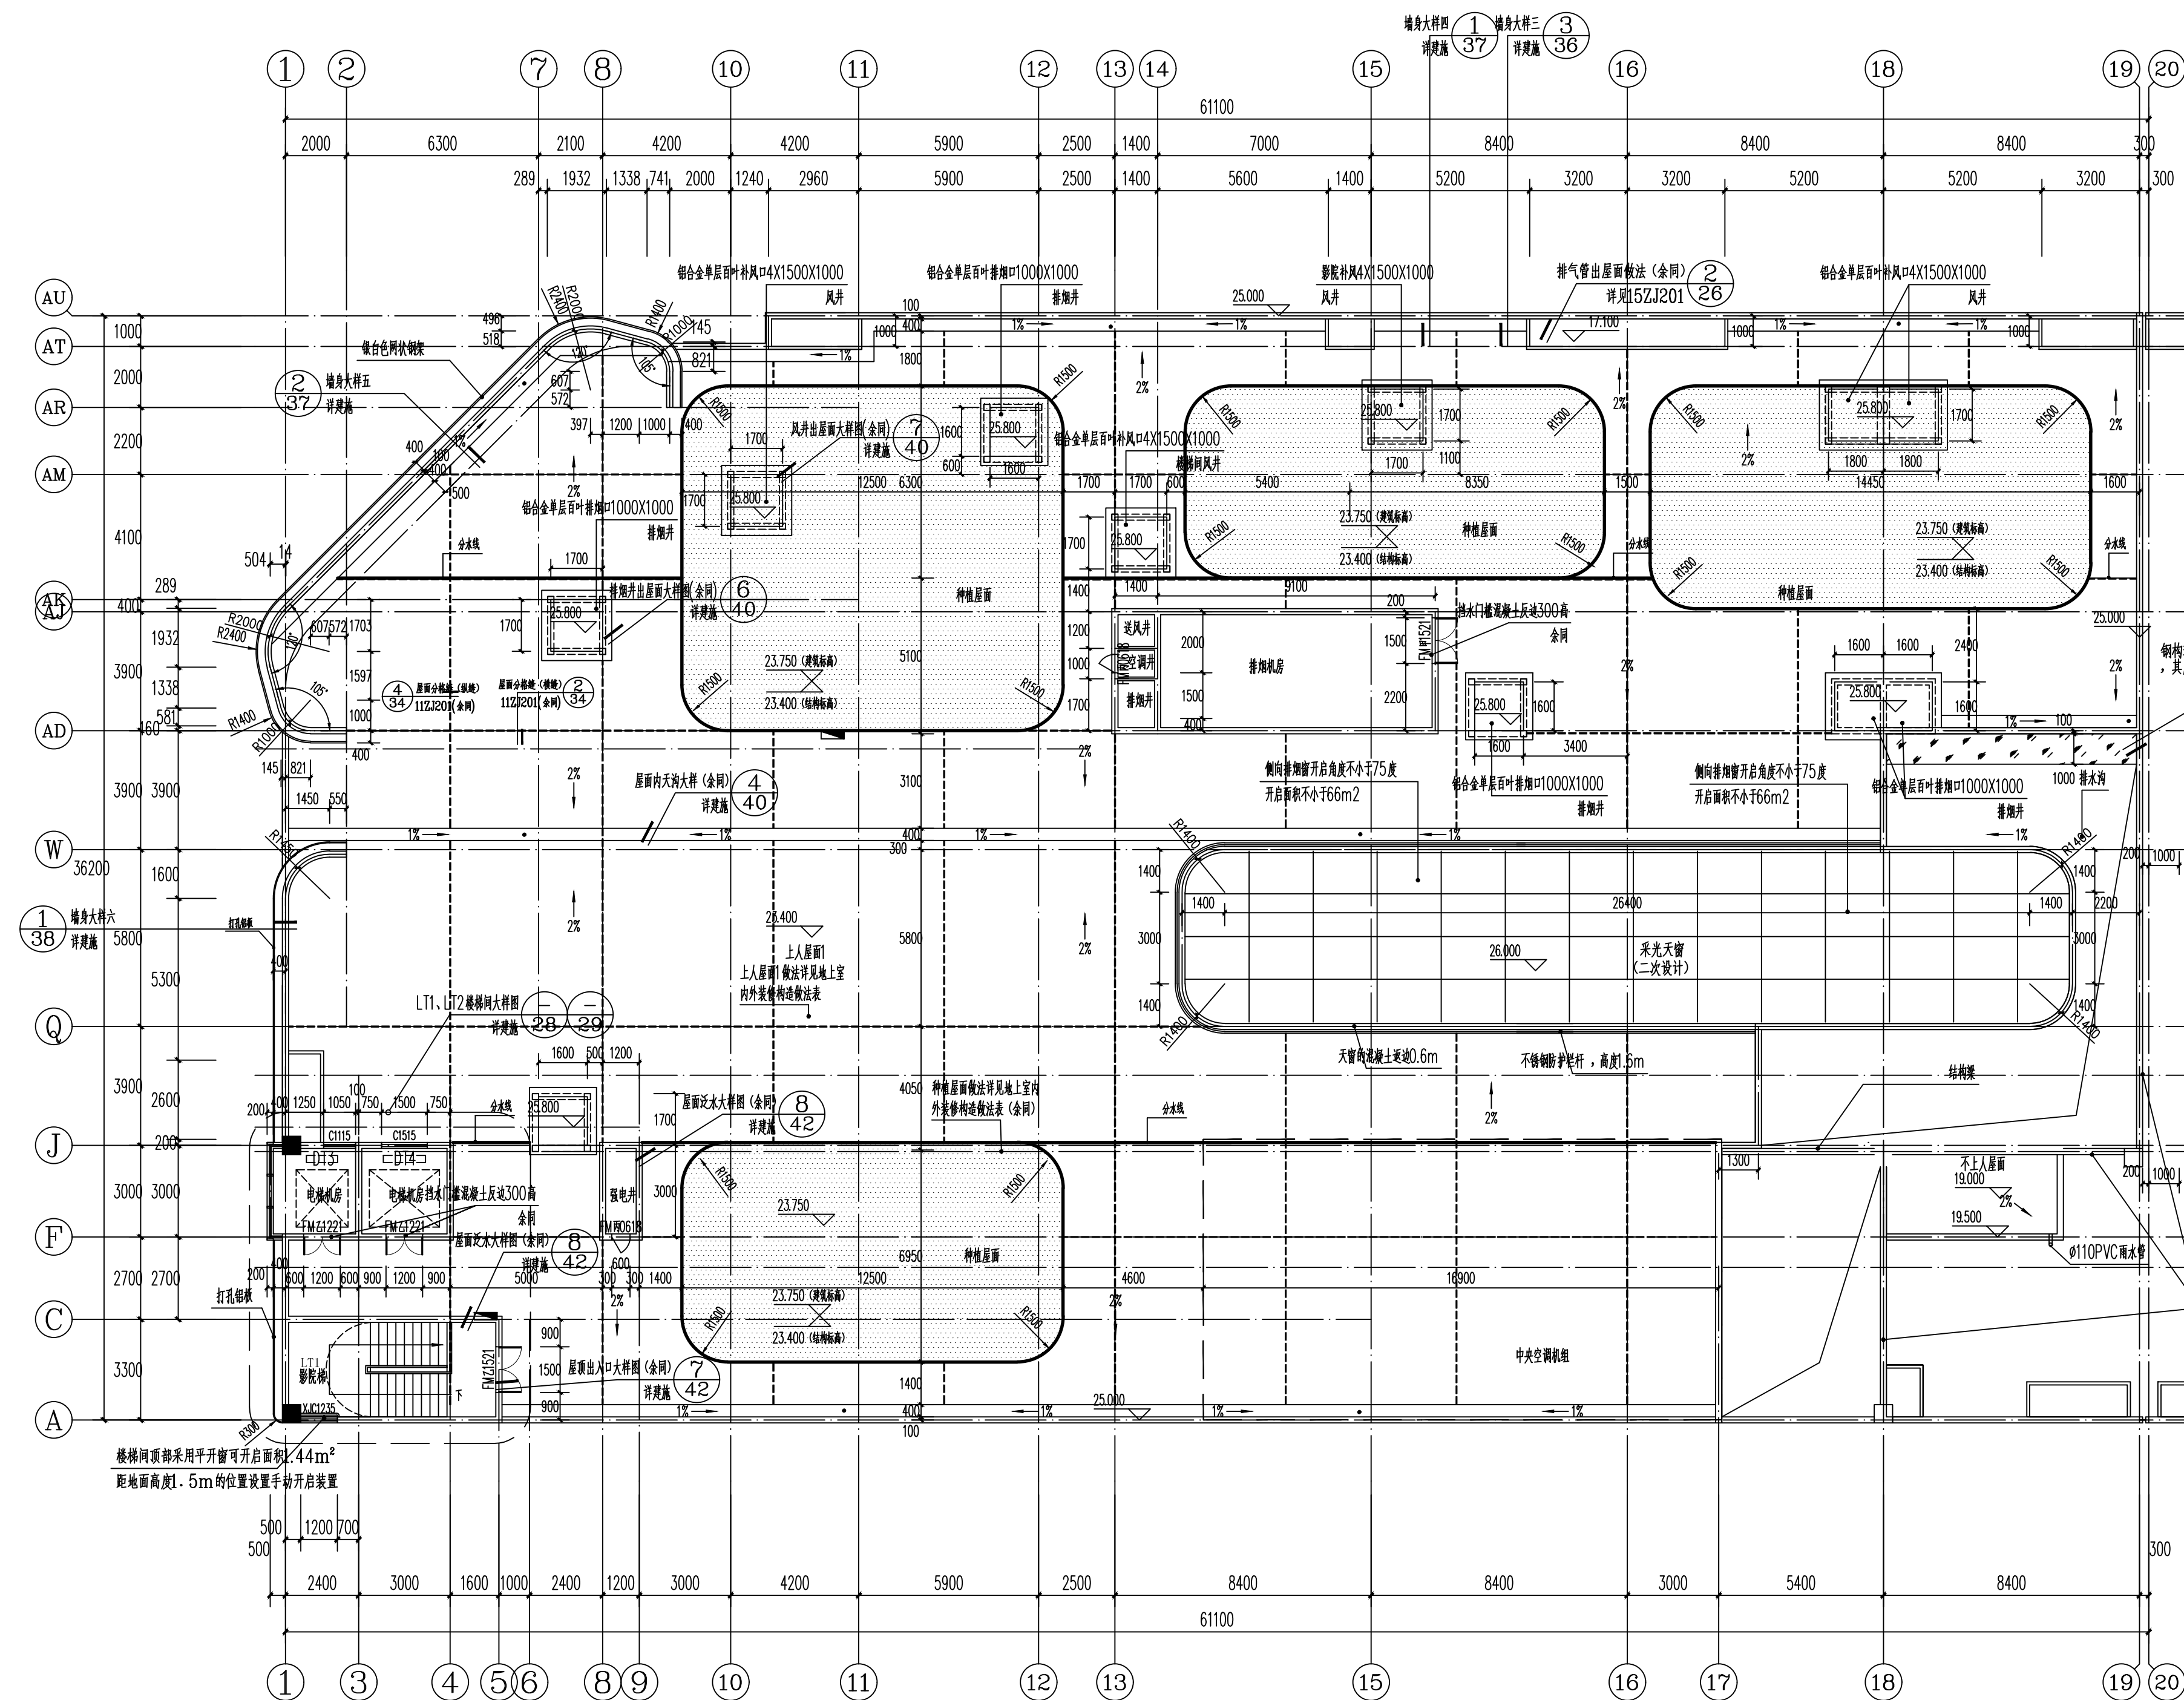

商业屋顶平面图 1:150


本层建筑面积: 82.85m²

图例

 消火栓

注明:

- 1、保温材料：难燃型挤塑聚苯板
防水材料为：4.0厚单组分聚氨酯防水涂料+3厚自粘聚合物改性沥青防水卷材
种植层①做法详见室上室内防水修缮和构造详图
种植层②做法详见室上室内防水修缮和构造详图
非上人屋面做法详见5ZJ201-122~126图
屋面防水做法详见5ZJ201-126图④⑤⑥ 分缝处6mx6m
屋面坡度详12ZJ111-4(1)-11/7、12ZJ111-4(1)-9、12ZJ111-4(1)-9、
- 2、屋面排水至屋面雨水排水下水管处设置集水坑，做法详见5ZJ201-126图④⑤
- 3、屋面排水110UPVC雨水管，做法详见115ZJ201-126图④⑤
- 4、檐口、雨水管处做泛水详5ZJ201-126图④⑤
- 5、檐口处屋面保护层详5ZJ201-126图④⑤ 排气穿出屋面做法详见5ZJ201-126图④⑤

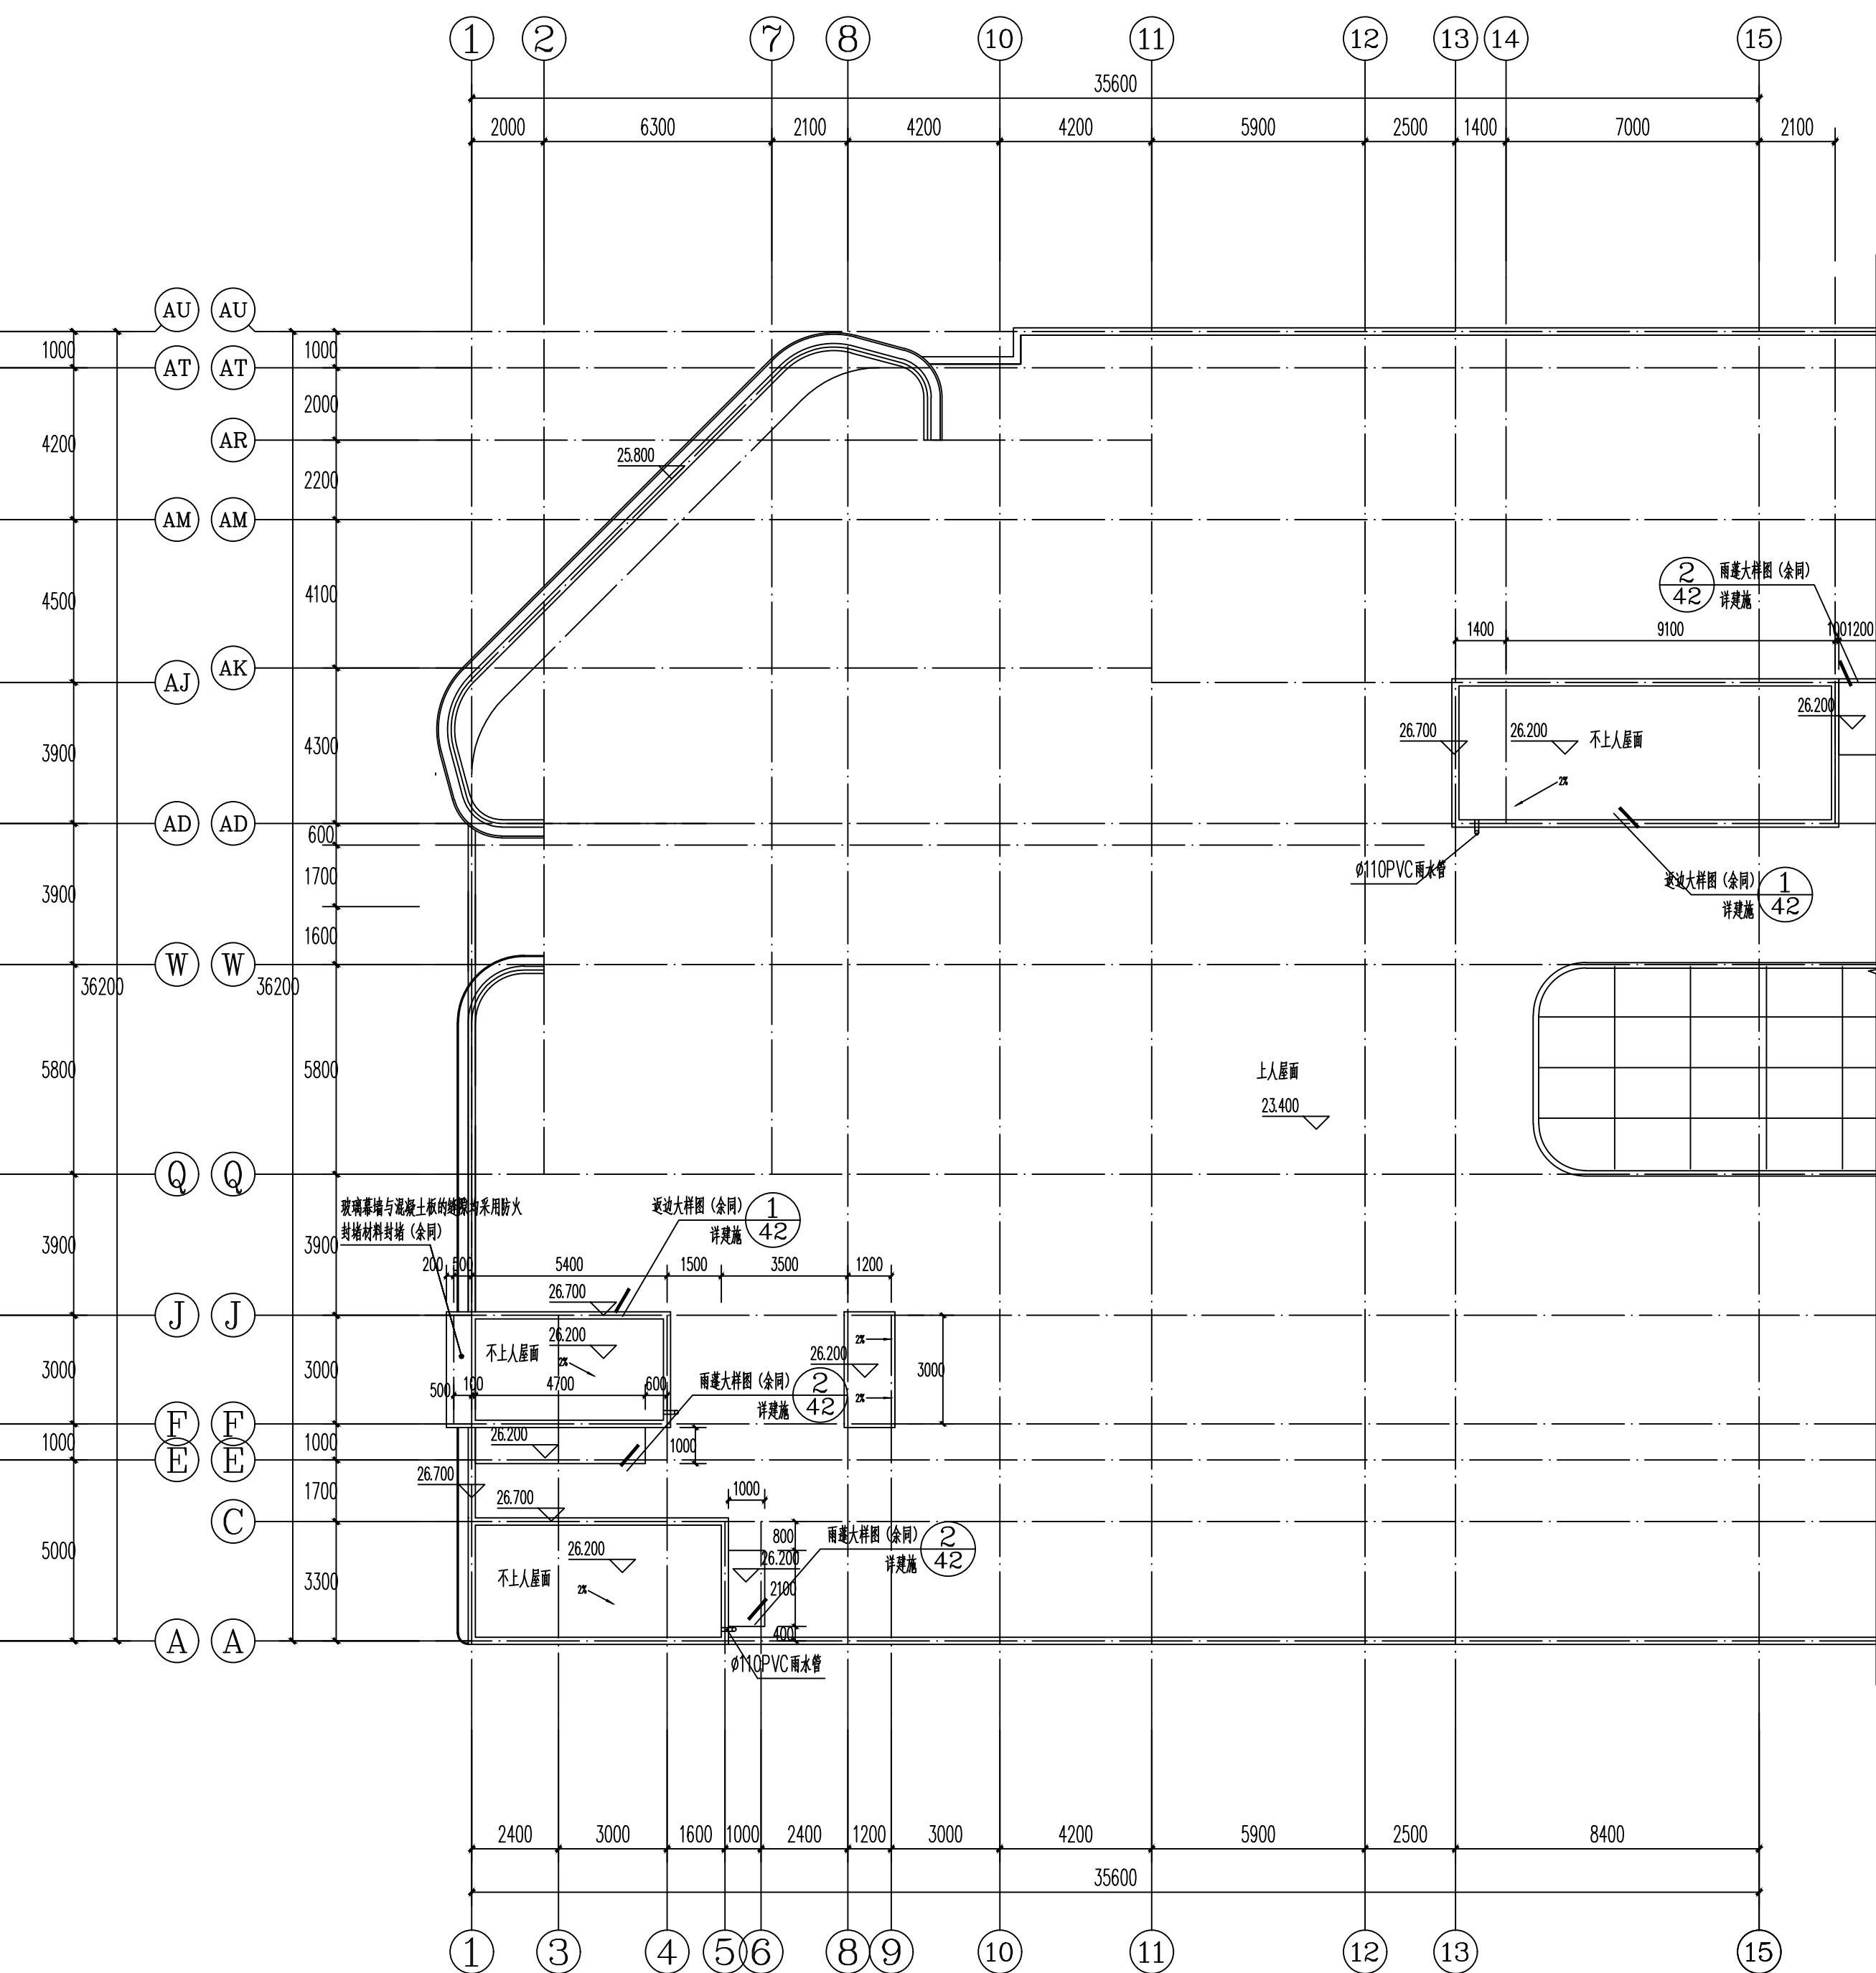

商业屋顶构件平面图 1:100