
 
 
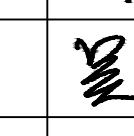
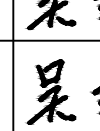
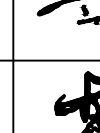
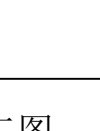
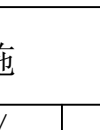


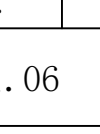

建设单位/CLIENT:			
麻阳苗族自治县远桥房地产开发有限公司			
项目名称/PROJECT: 远程国际			
子项目名称/SUB-PROJECT: 远程国际			
区位图/REGIONAL LOCATION MAP :			
 广东建筑艺术设计院有限公司 GUANGDONG ARCHITECTURAL ARTIST DESIGN INSTITUTE CO.,LTD ■ 建筑总体规划: 李坚 ■ 方案总体设计: 乙晨 ■ 建筑总体规划: 乙晨 ■ 方案总体设计: 乙晨			
图纸名称/TITLE: LT1、LT2楼梯间大样图一			
项目名称/PROJECT: 远程国际			
设计 DESIGNED	古新辉		
校对 CHECKED	吴新红		
专业负责人 CHIEF	吴志刚		
项目负责人 PROJECT CHIEF	吴志刚		
审核 IDENTIFIED	黄履优		
审定 APPROVED	李 坚		
业务号/JOB NO.			
设计阶段/STATUS: 施工图			
专业/DISCIPLINE: 建筑			
比例/ SCALE:	1: 100	规格/ SIZE:	A1
出图日期/DATE: 2021.06			
图号/DRAWING NO. JS- 28			
版次 NO.	修改内容 DESCRIPTION	日期 DATE	
条形码/BARCODE:			
版权所有，不得复制、套用。 ALL RIGHTS RESERVED, DON'T COPIED, REPRODUCED.			