

建设单位/CLIENT:

麻阳苗族自治县远桥房地产开发有限公司

项目名称/PROJECT:

远程国际

子项目名称/SUB-PROJECT:

远程国际

区位图/REGIONAL LOCATION MAP :



图纸名称/TITLE:

①~④②轴立面图

项目名称/PROJECT:

远程国际

设计

DESIGNED

校对
CHECKED

专业负责人

CHIEF

项目负责人
PROJECT CHIEF

PROJECT DATE

审核

IDENTIFIED

审定

业务号/JOB NO.

设计阶段/STATUS: 施工图

专业/DISCIPLINE: 建施

比例/	1	100
-----	---	-----

SCALE:	1: 100	SIZE:
--------	--------	-------

出图日期/DATE: 2021.0

© 2006 The Authors

图号/DRAWING NO. JS-22

版次	修改内容
----	------

NO.	DESCRIPTION
-----	-------------


[illegible]

--	--

--	--

条形码/BARCODE:

ALL RIGHTS RESERVED, DON'T COPIE

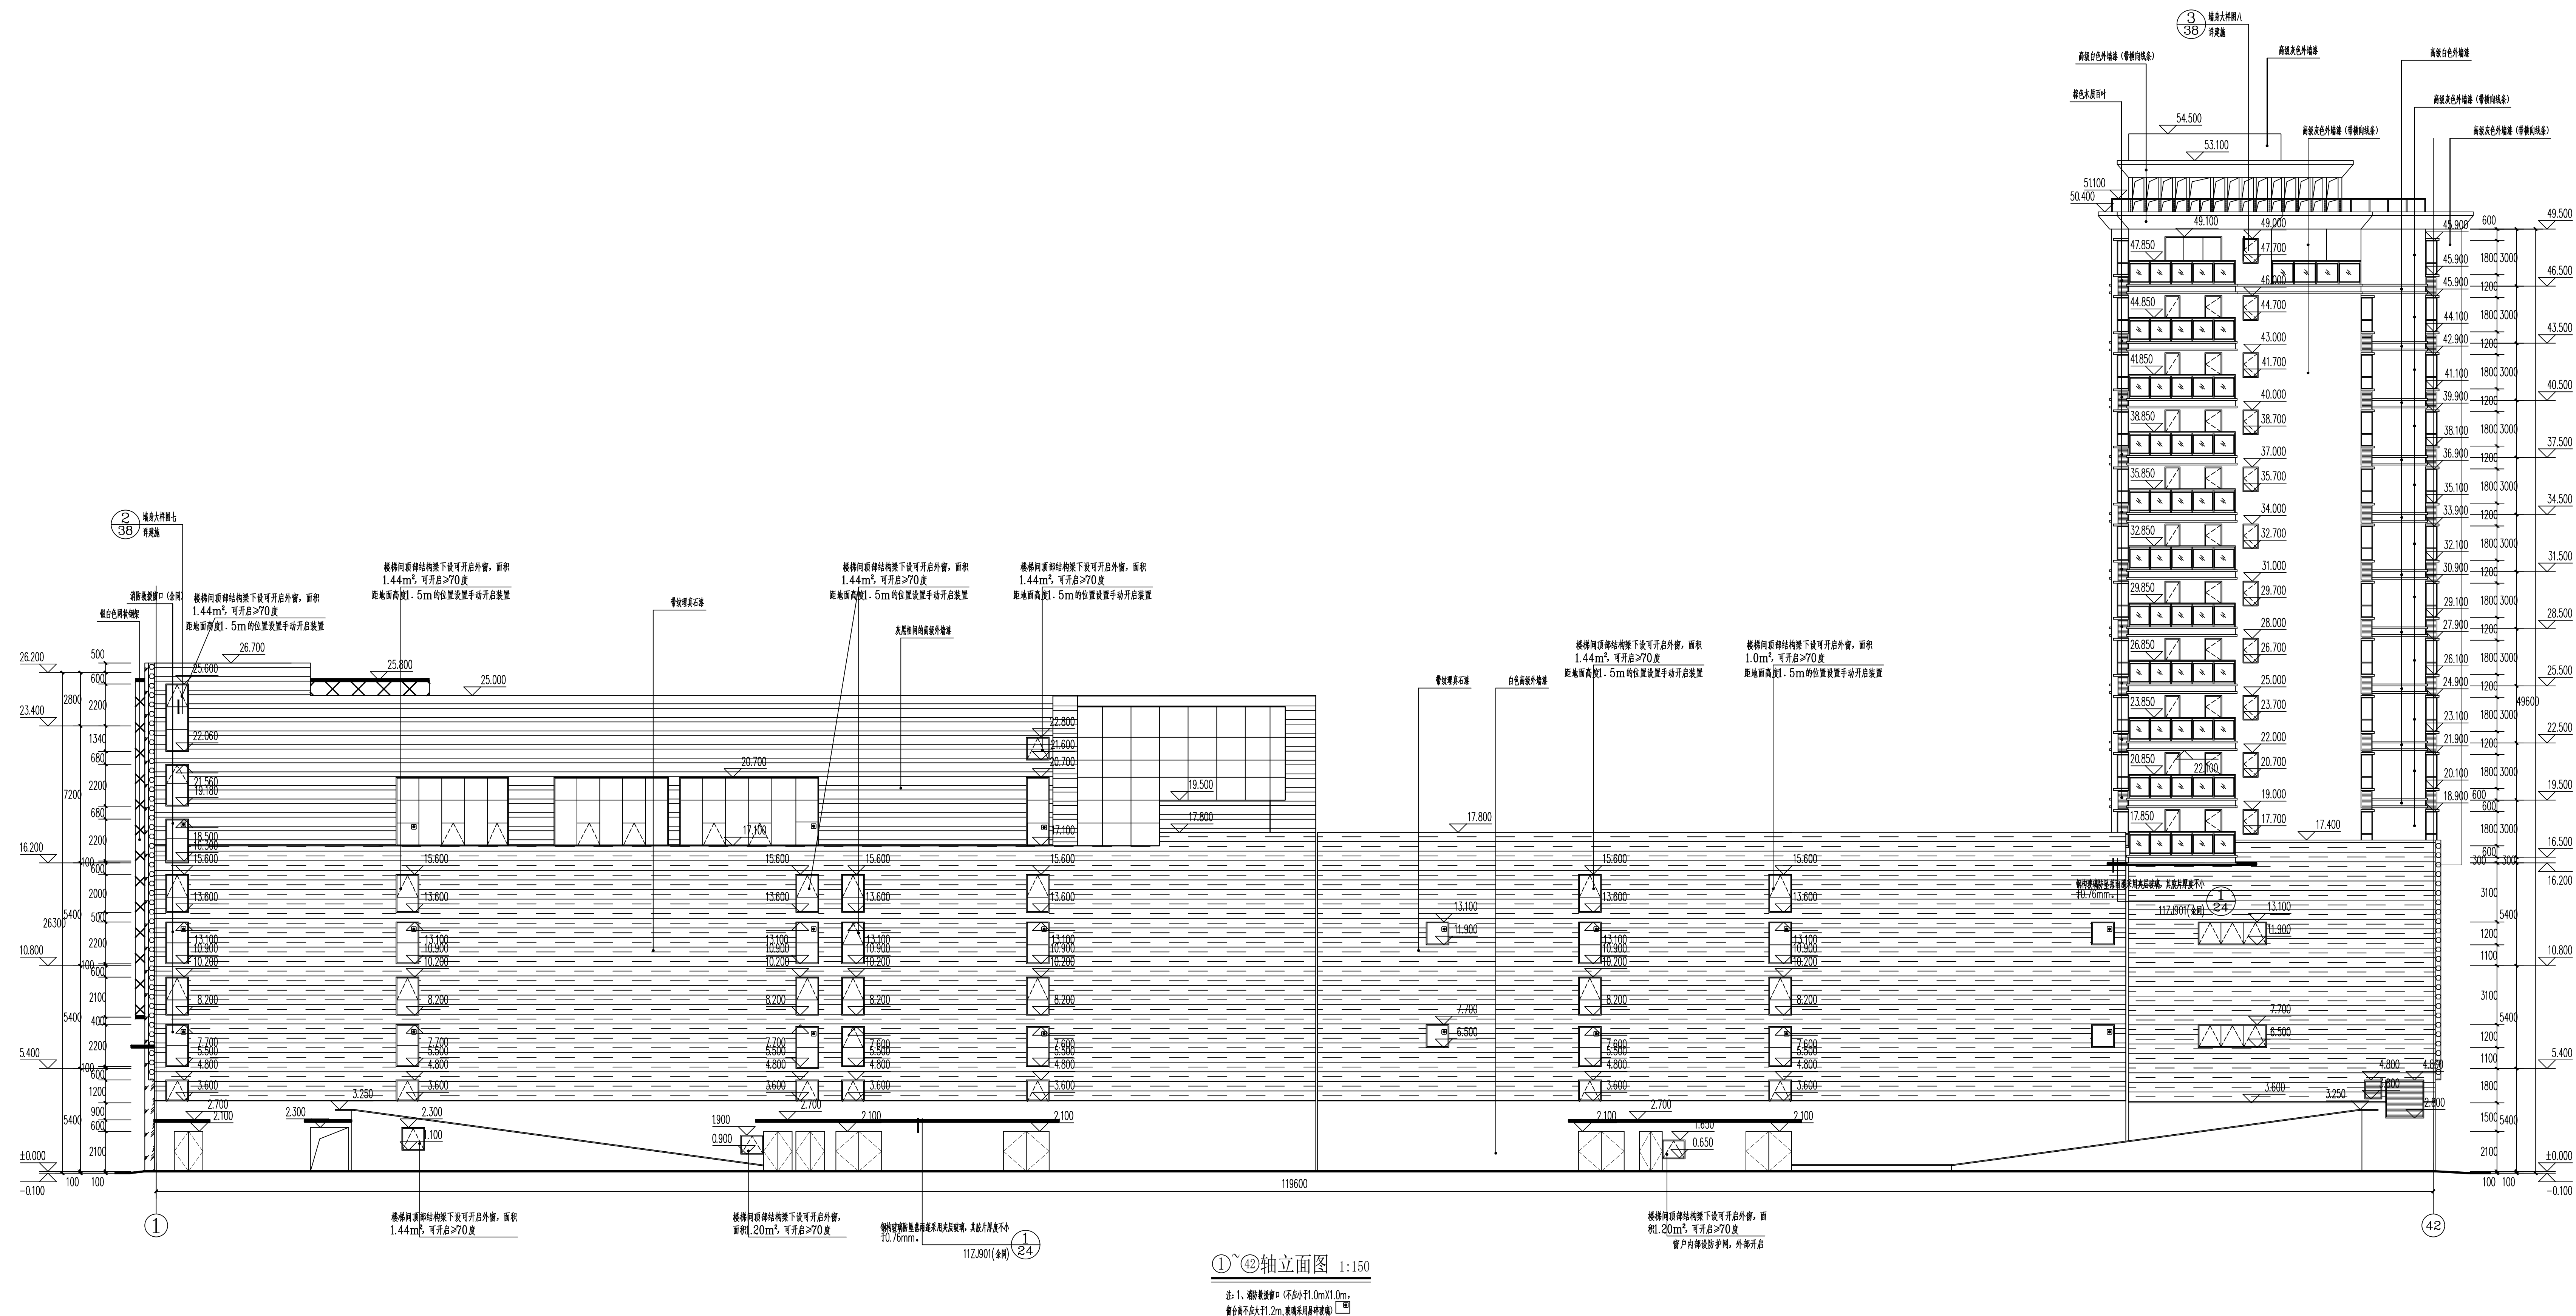

①~④②轴立面图 1:150

注: 1、消防救援窗口(不应小于1.0mX1.0m, 窗台高不应大于1.2m, 玻璃采用易碎玻璃)

版权所有，不得复制、套用。
ALL RIGHTS RESERVED, DON'T COPIED, REPRODUCED.