

麻阳苗族自治县远桥房地产开发有限公司

子项目名称/SUB-PROJECT:	远程国际
--------------------	------

1-1剖面图

项目名称/PROJECT:	远程国际
---------------	------

设计 DESIGNED	古新辉	
校对 CHECKED	吴新红	
专业负责人 CHIEF	吴志刚	
项目负责人 PROJECT CHIEF	吴志刚	
审核 IDENTIFIED	黄履优	
审定 APPROVED	李 坚	

业务号/JOB NO.

设计阶段/STATUS: 施工图

专业/DISCIPLINE: 建施

比例/ SCALE:	1: 100	规格/ SIZE:	A1
---------------	--------	--------------	----


出图日期/DATE: 2021.06

图号/DRAWING NO. JS-24

版次 NO.	修改内容 DESCRIPTION	日期 DATE

条形码/BARCODE:

版权所有，不得复制、套用。
ALL RIGHTS RESERVED, DON'T COPIED, REPRODUCED.

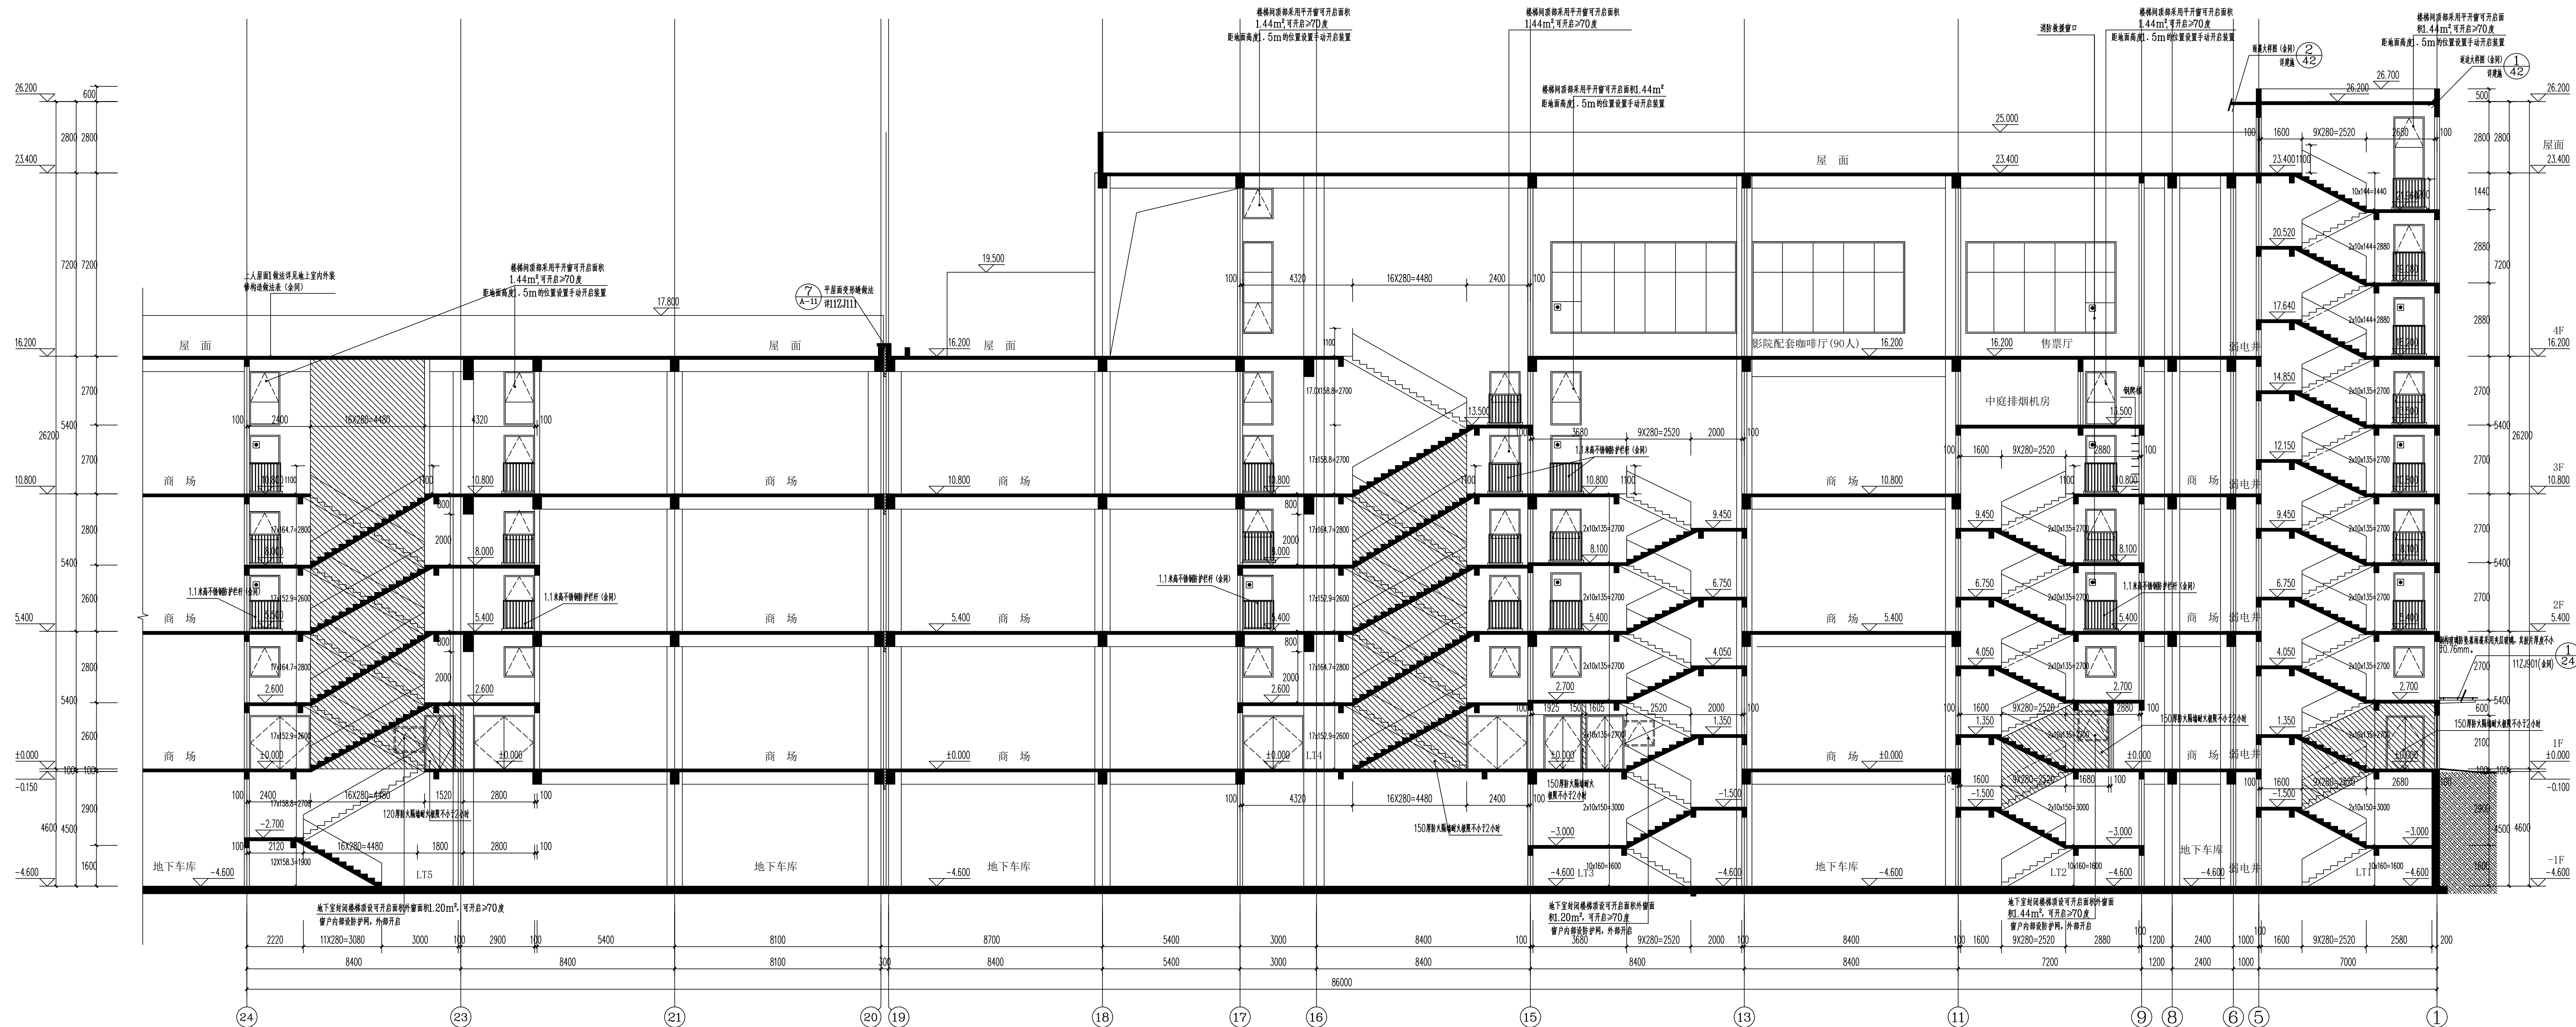

1-1剖面图 1:100

注: LT1~LT5剖面图
消防玻璃窗(不应小于1.0m×1.0m,
窗台高不应大于1.2m,玻璃采用夹层玻璃)

- 1.本工程梯档踏步高、宽、步数及平台宽度等详见梯档大样图。梯档栏杆采用不锈钢栏杆900高，详11ZJ401-13工程梯档大样11ZJ401-3~16；当扶手水平长度4.0~5.0m时，栏杆净高不低于1100。
- 2.起步详11ZJ40138-6；扶手与填充端连接详11ZJ401-42~5，防滑详05ZJ401-39~6
- 3.梯档大样1110，以防坠落网处。
- 4.凡梯高小于900mm时，作防护栏杆具体做法详见11ZJ401-46（~~栏杆~~制作要符合安全防护要求，如防止人员攀爬。