





建设单位/CLIENT:		
麻阳苗族自治县远桥房地产开发有限公司		
项目名称/PROJECT:		
远程国际		
子项目名称/SUB-PROJECT:		
远程国际		
区位图/REGIONAL LOCATION MAP :		
远桥国际 广东远桥艺术设计院有限公司 SHANGHAI ARCHITECTURAL ARTISTIC DESIGN INSTITUTE CO.,LTD ■ 建筑方案设计: 甲级 ■ 风景园林设计: 乙级 ■ 城乡规划编制: 乙级 ■ 市政设计: 乙级		
图纸名称/TITLE:		
车道1-1剖面 自动扶梯剖面图、a-a剖面图 3-3剖面图、5-5剖面图		
项目名称/PROJECT:		
远程国际		
设计 DESIGNED	古新辉	
校对 CHECKED	吴新红	
专业负责人 CHIEF	吴志刚	
项目负责人 PROJECT CHIEF	吴志刚	
审核 IDENTIFIED	黄履优	
审定 APPROVED	李 坚	
业务号/JOB NO.		
设计阶段/STATUS: 施工图		
专业/DISCIPLINE: 建筑		
比例/ SCALE:	1: 100	规格/ SIZE: A1
出图日期/DATE: 2021.06		
图号/DRAWING NO. JS-25		
版次 NO.	修改内容 DESCRIPTION	日期 DATE
条形码/BARCODE:		
版权所有, 不得复制、套用。 ALL RIGHTS RESERVED, DON'T COPIED, REPRODUCED.		

1.本工程楼梯踏步高、宽、步数及平台宽度等详楼梯大样,楼梯栏杆采用不锈钢栏杆900高,详11ZJ401-13-W扶手详11ZJ401-37-16,(注:当扶手水平长度大于0.5m时,栏杆净高不低于1100)。
2.起步详11ZJ40138-6;扶手与填充墙连接详11ZJ401-42-5,防滑详05ZJ401-39-6
3.梯井大于110,均做防坠网处理。