

建设单位/CLIENT:

麻阳苗族自治县远桥房地产开发有限公司

项目名称/PROJECT:

远程国际

子项目名称/SUB-PROJECT:

远程国际

区位图/REGIONAL LOCATION MAP :





图纸名称/TITLE:

2-2剖面图、4-4剖面图
A-A断面图、B-B断面图

项目名称/PROJECT:

远程国际

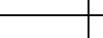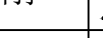设计 DESIGNED	古新辉	
校对 CHECKED	吴新红	
专业负责人 CHIEF	吴志刚	
项目负责人 PROJECT CHIEF	吴志刚	
审核 IDENTIFIED	黄履优	
审定 APPROVED	李 坚	

业务号/JOB NO.

设计阶段/STATUS: 施工图

专业/DISCIPLINE:

比例/ SCALE:	1: 100	规格/ SIZE:	A1
---------------	--------	--------------	----


出图日期/DATE: 2021.06

图号/DRAWING NO. JS-26

版次 NO.	修改内容 DESCRIPTION	日期 DATE


条形码/BARCODE:

版权所有，不得复制、套用。
ALL RIGHTS RESERVED, DON'T COPIED, REPRODUCED.

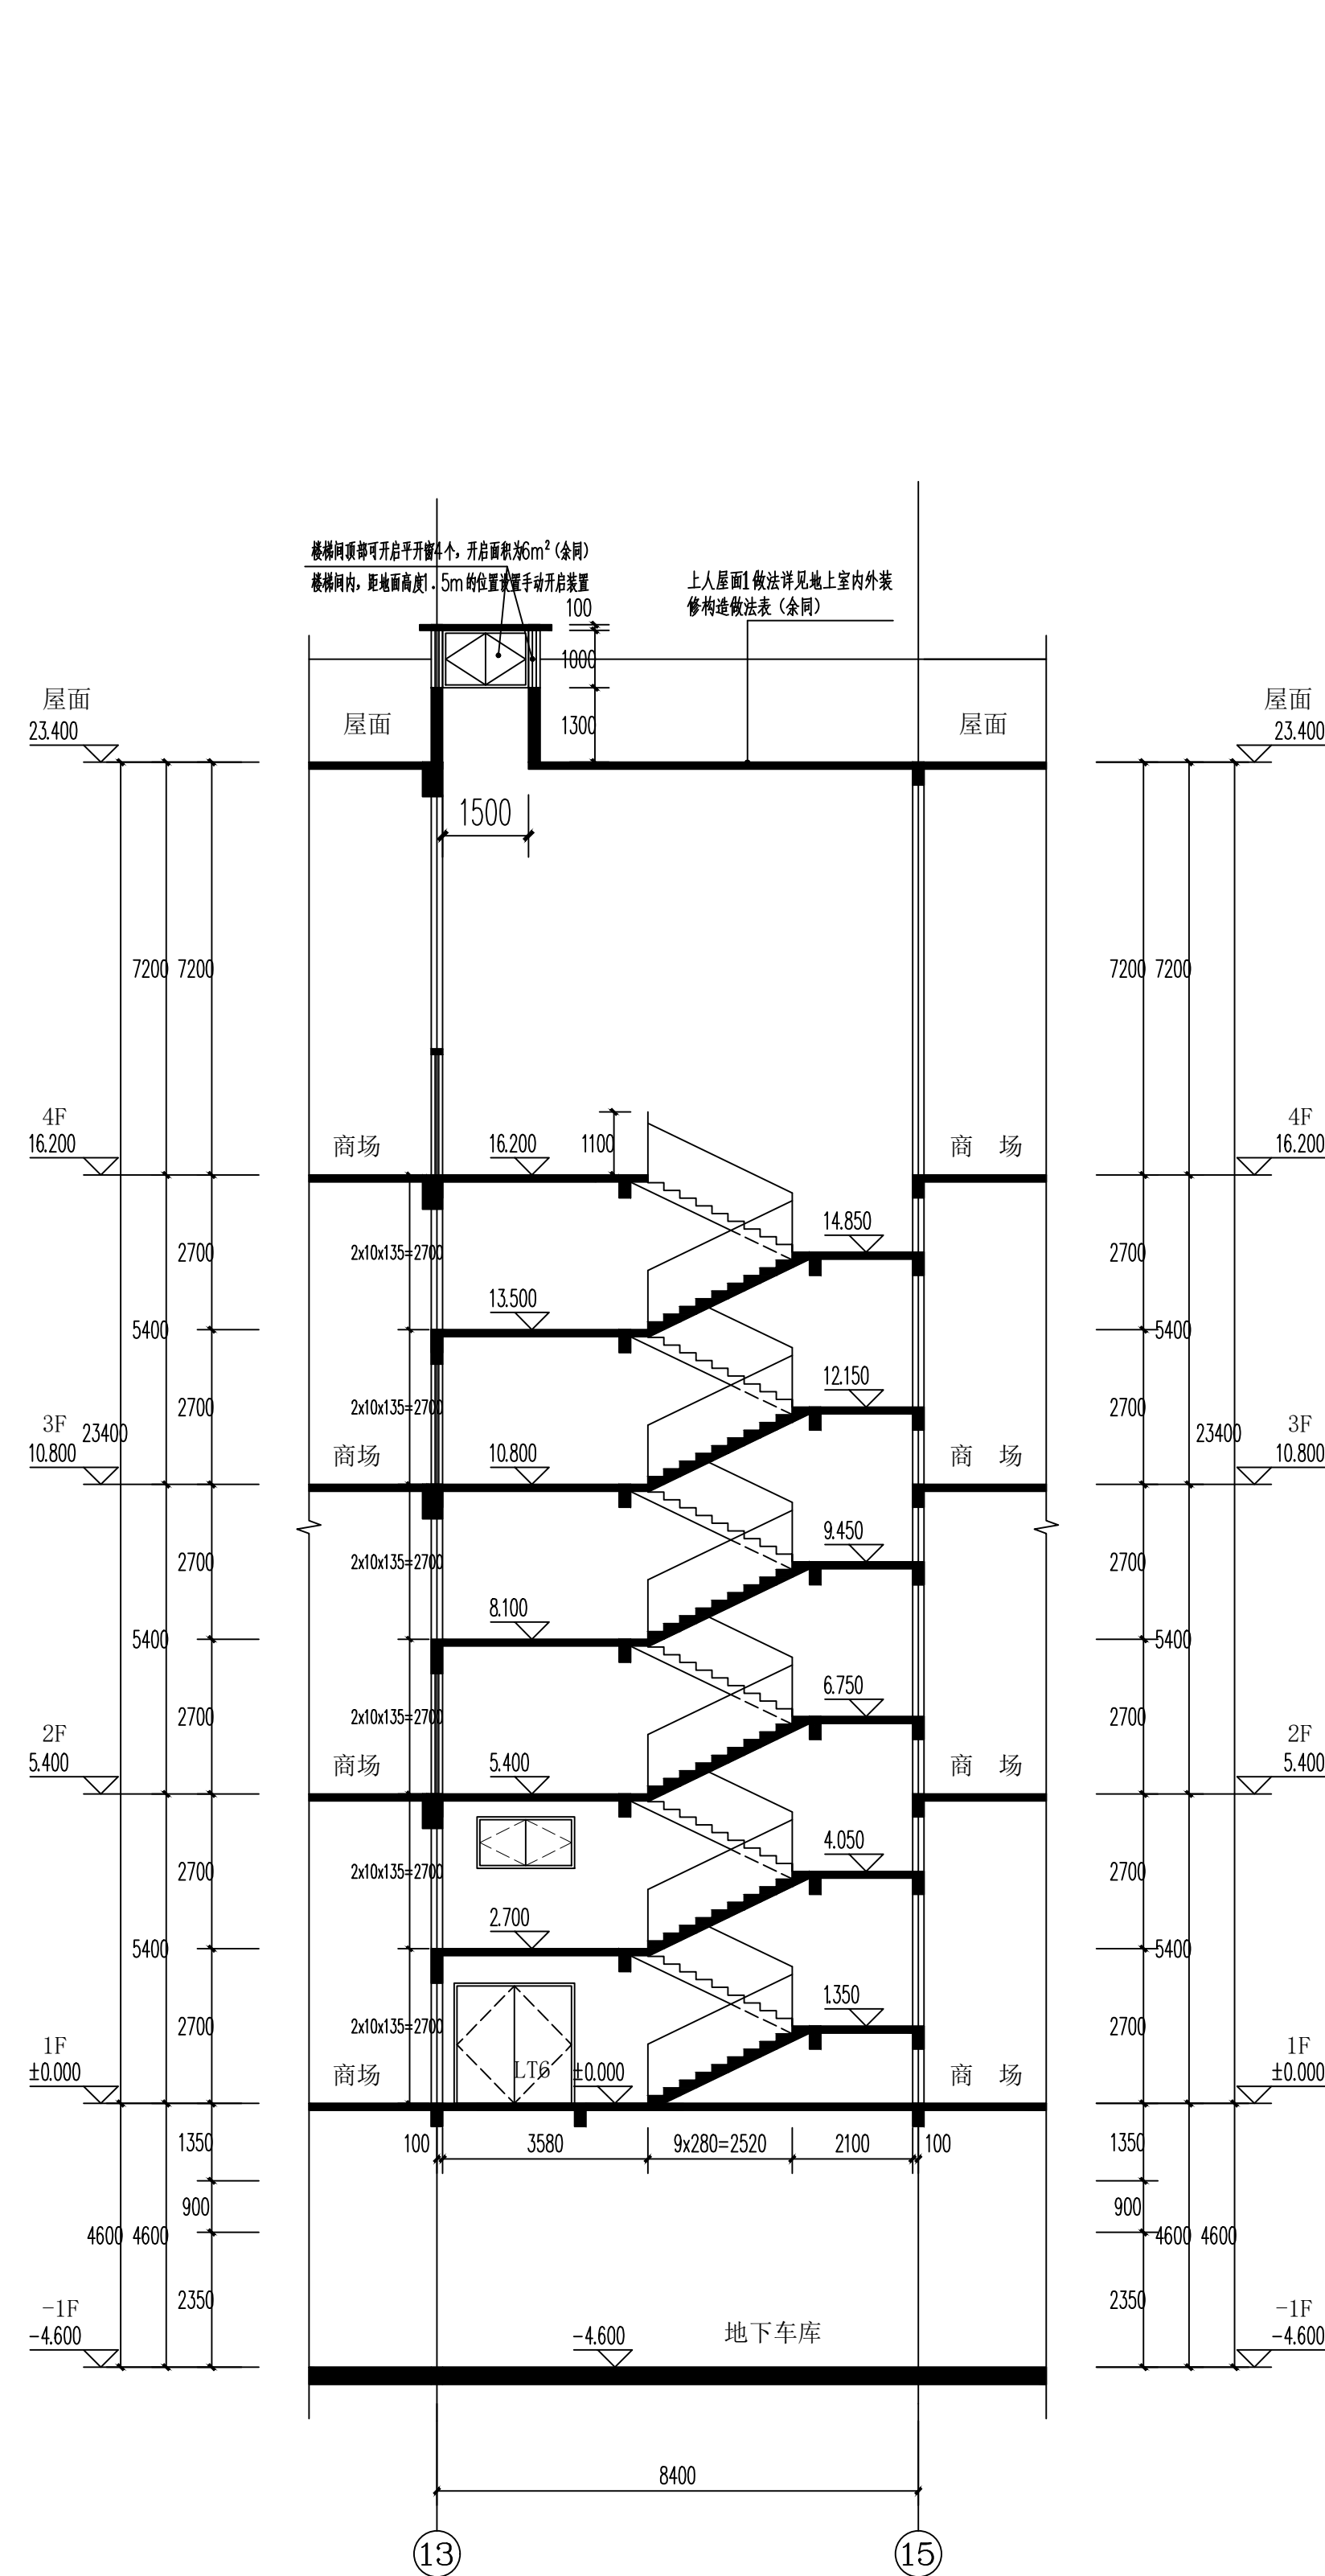


2-2剖面图 1:100

注：LT6剖面图

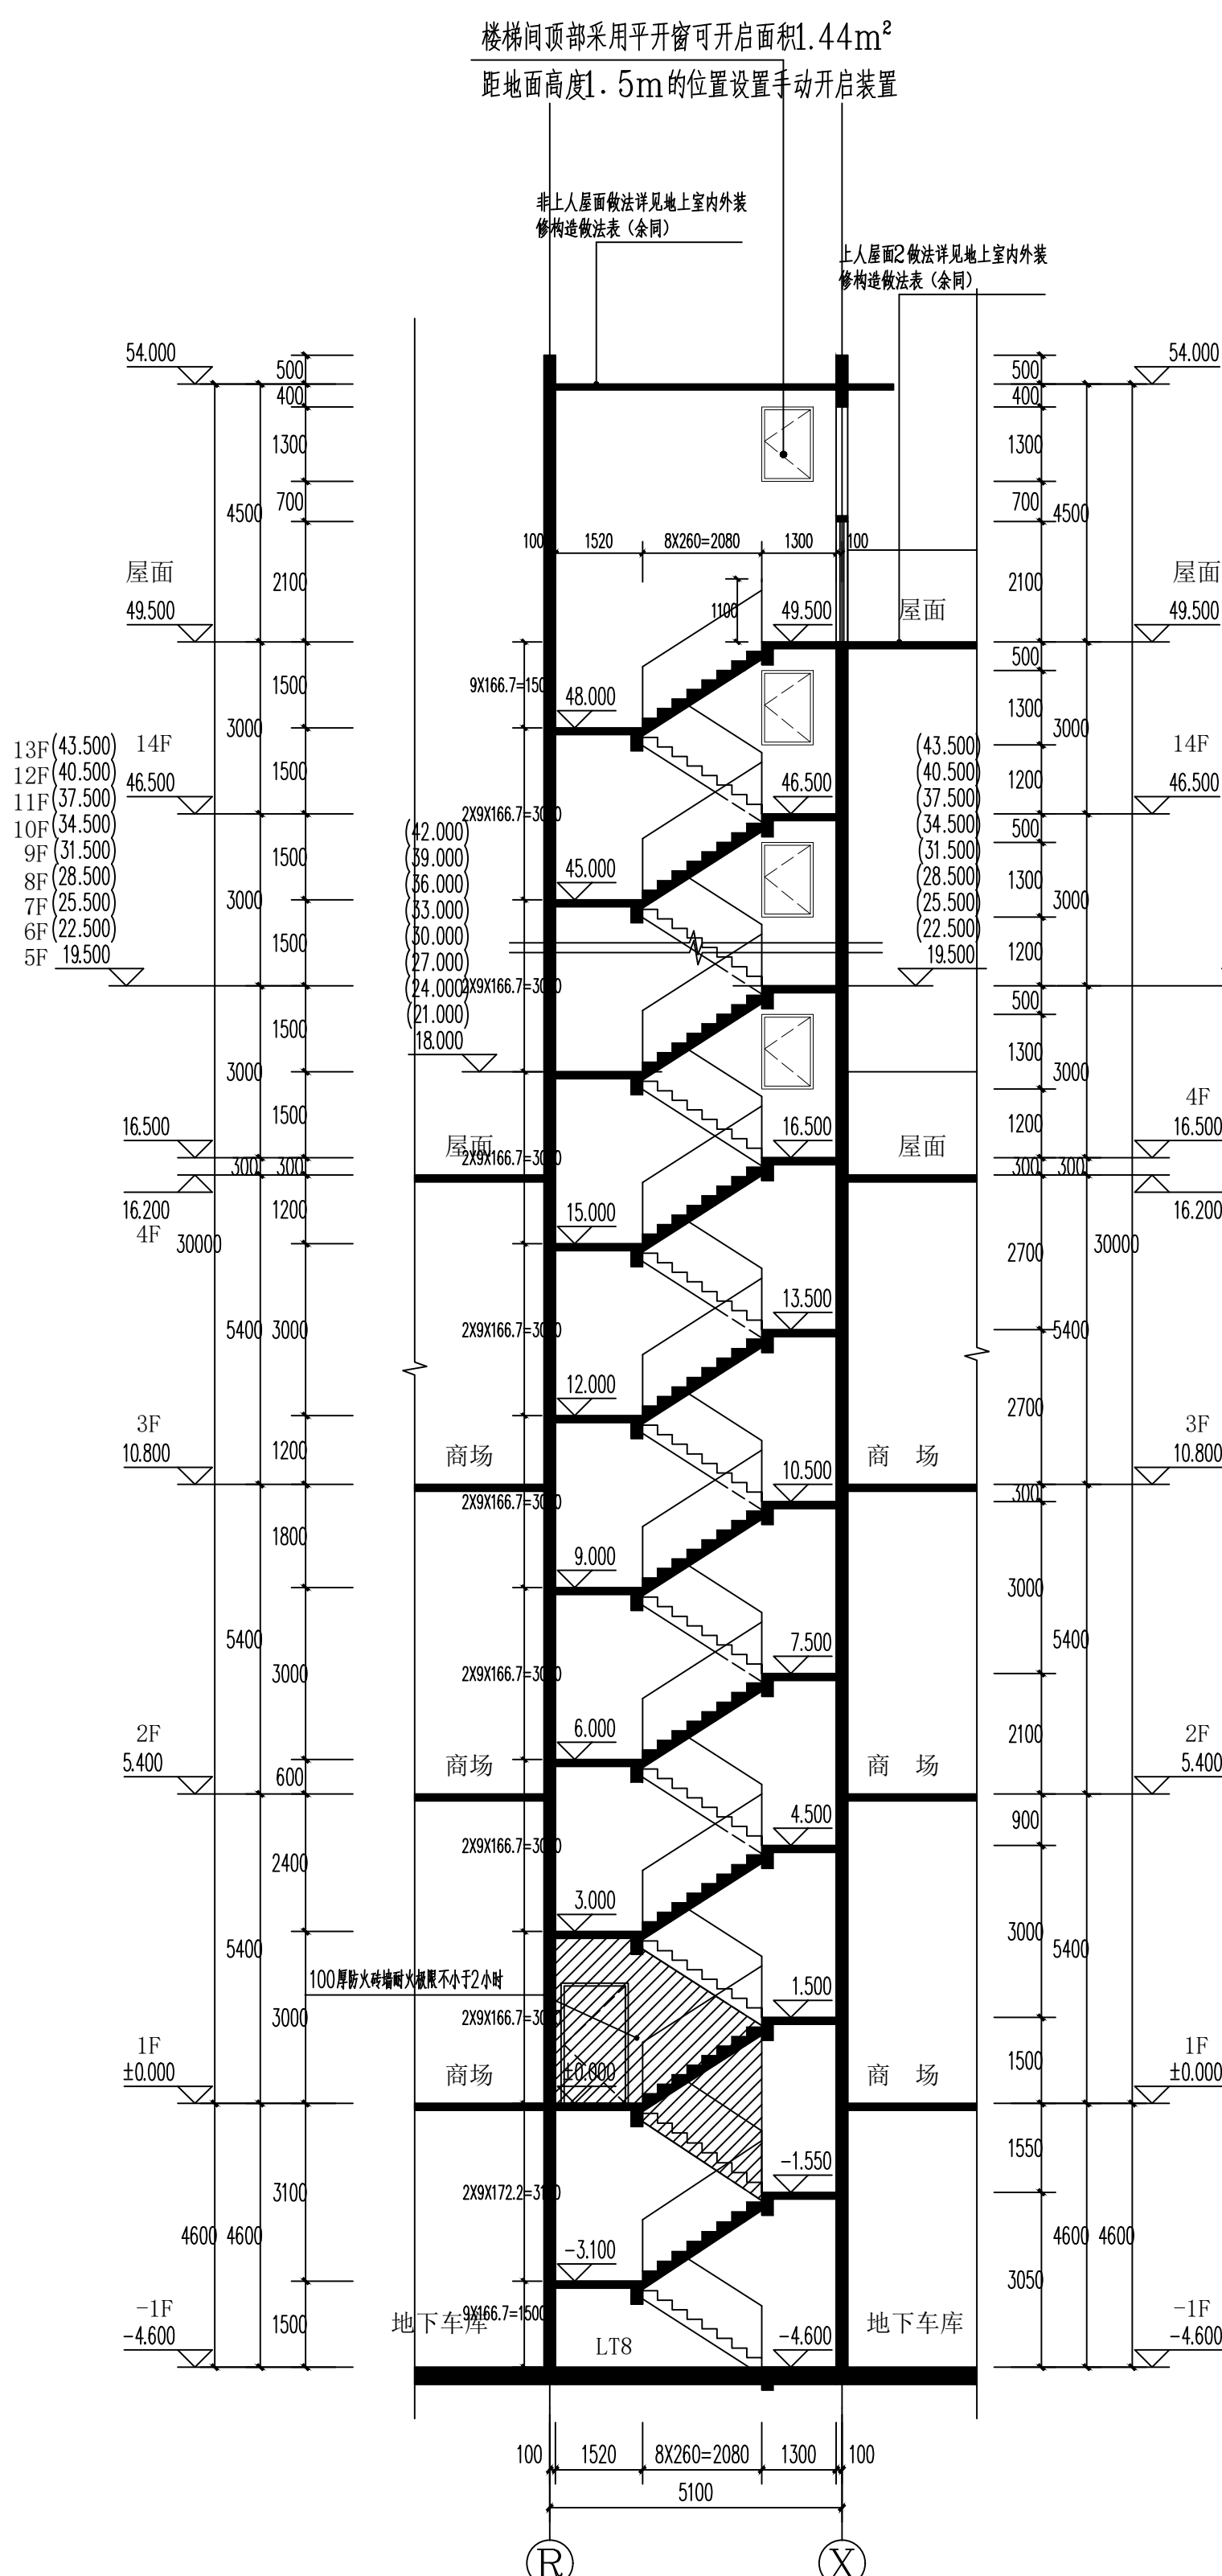

4-4剖面图 1:100

注: LT8剖面图

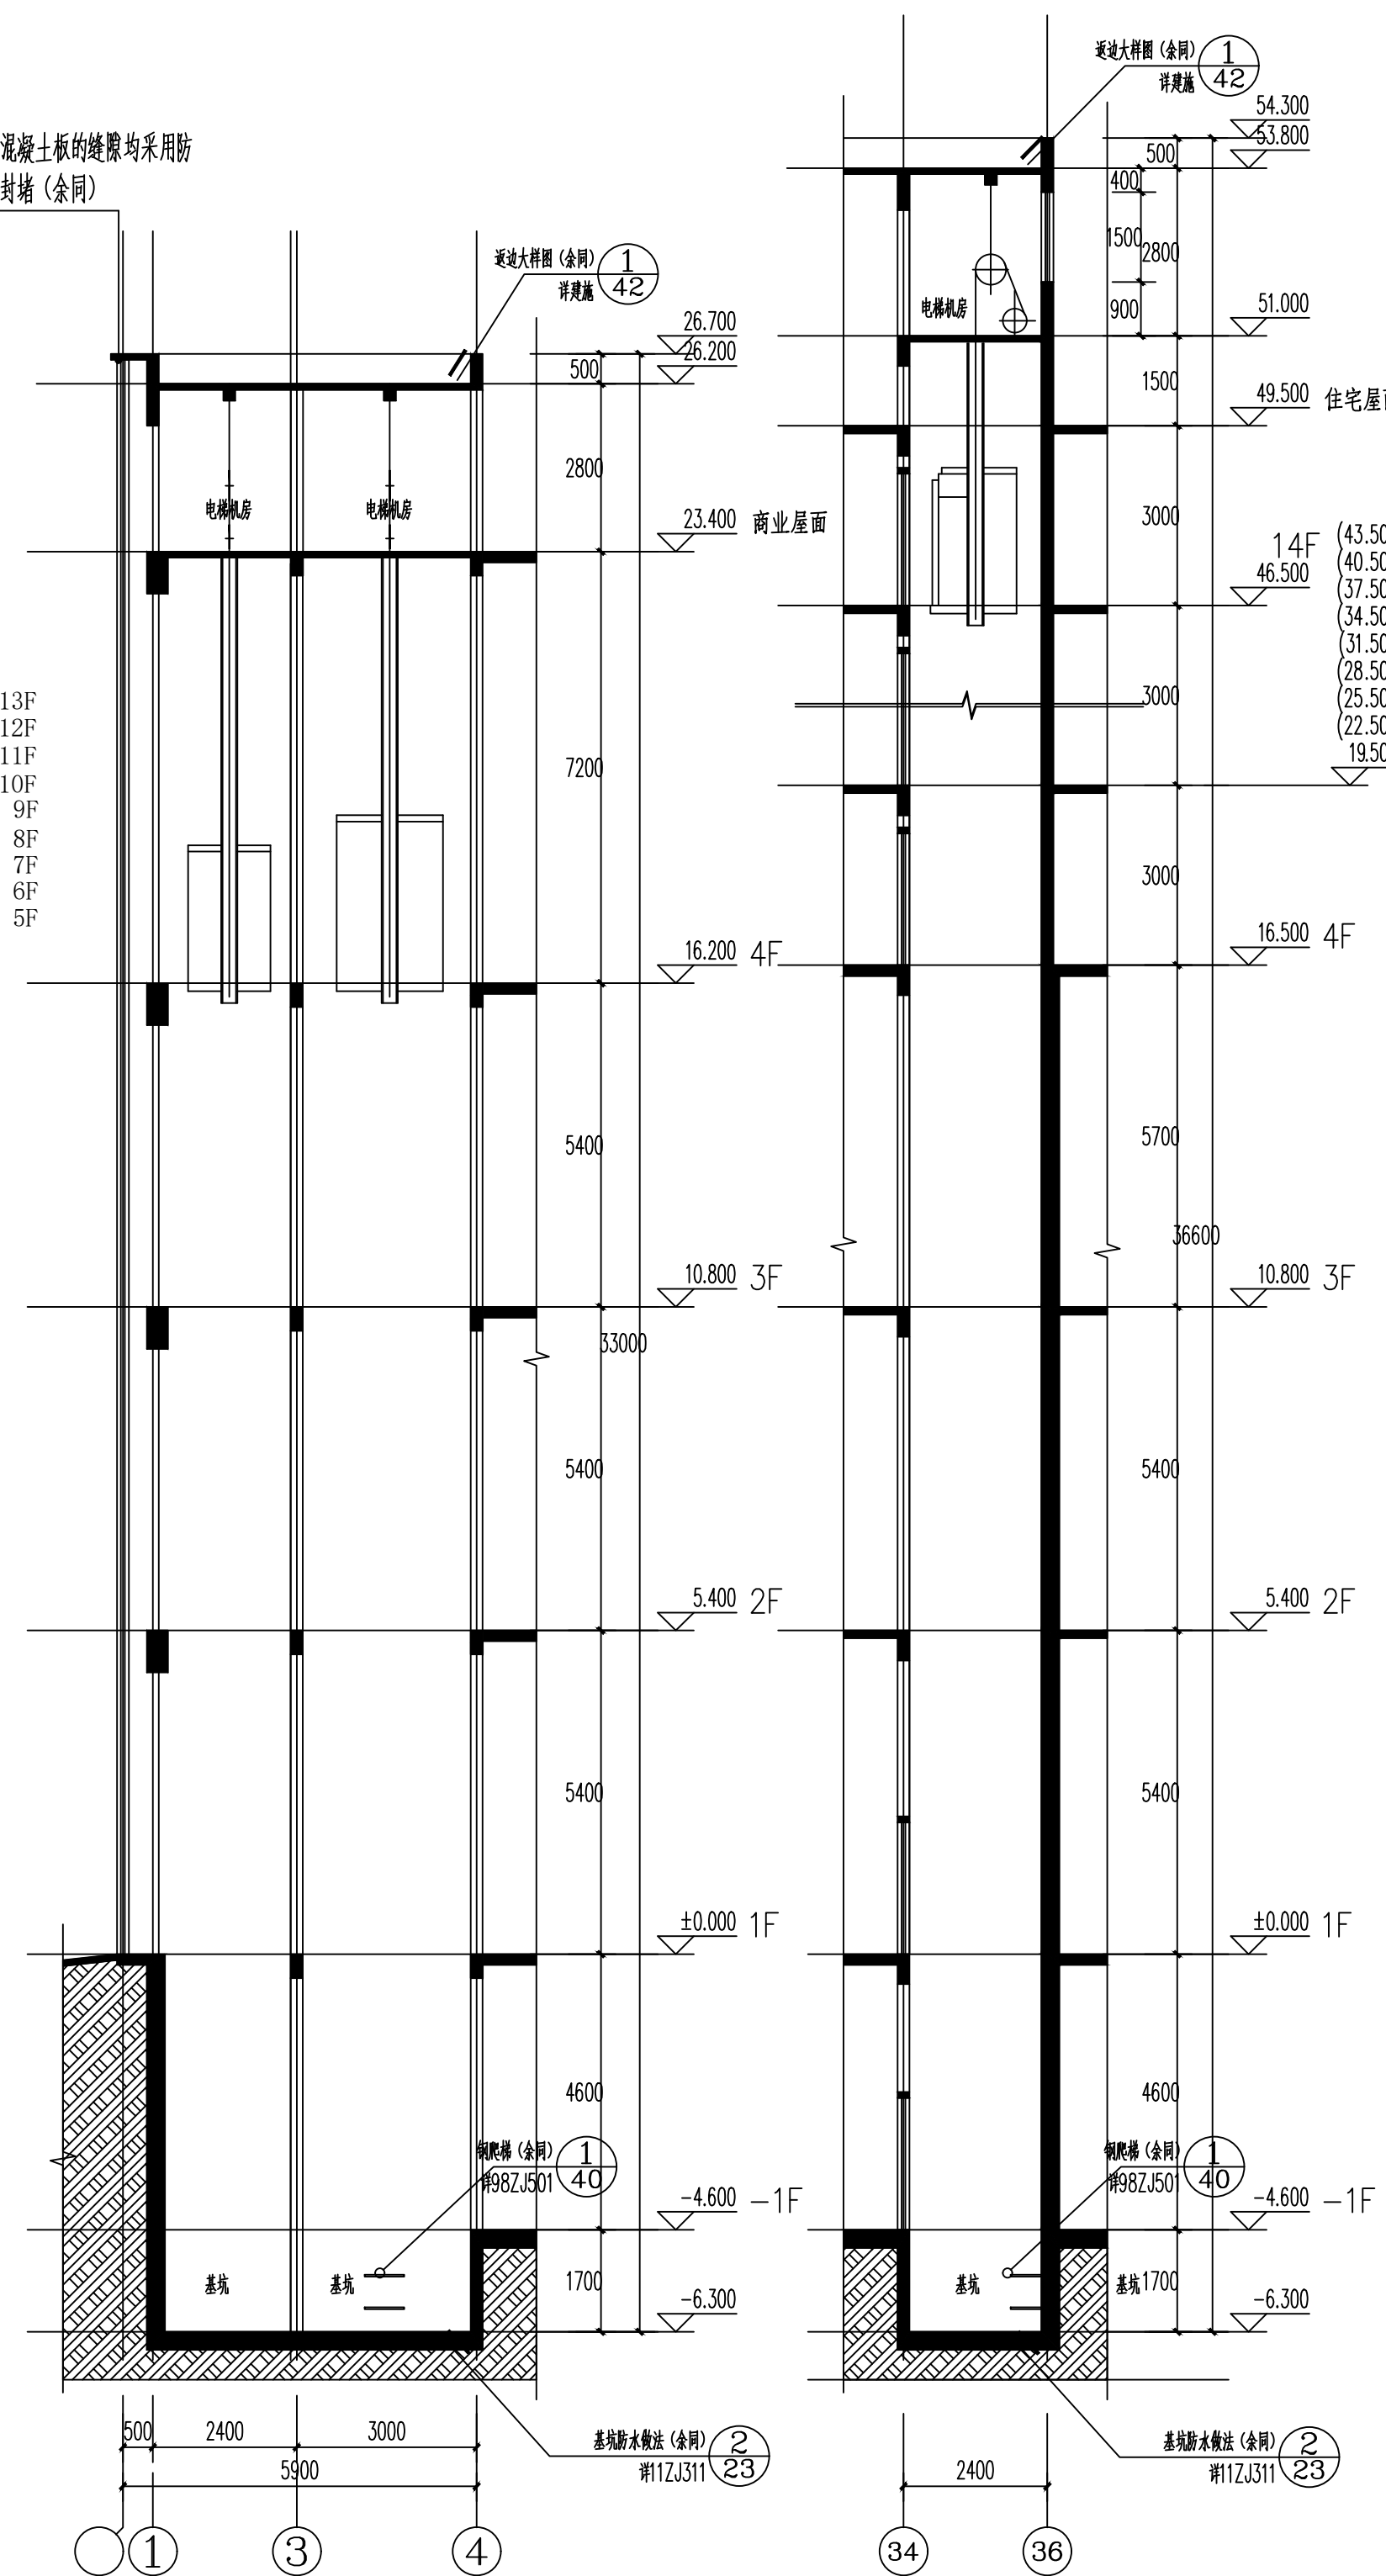

A-A断面图 1:100

B-B断面图 1:100

- 1.本工程楼梯踏步高、宽、步数及平台宽度等详楼梯大样。楼梯栏杆采用不锈钢栏杆900高,详11ZJ401-13-W扶手详11ZJ401-37-16,(注:当扶手水平长度大于0.5m时,栏杆净高不低于100)。
- 2.起步详11ZJ403-6;扶手与填充墙连接详11ZJ401-42-5,防滑详05ZJ401-39-6
- 3.梯井大于1100,均做防坠网处理。