
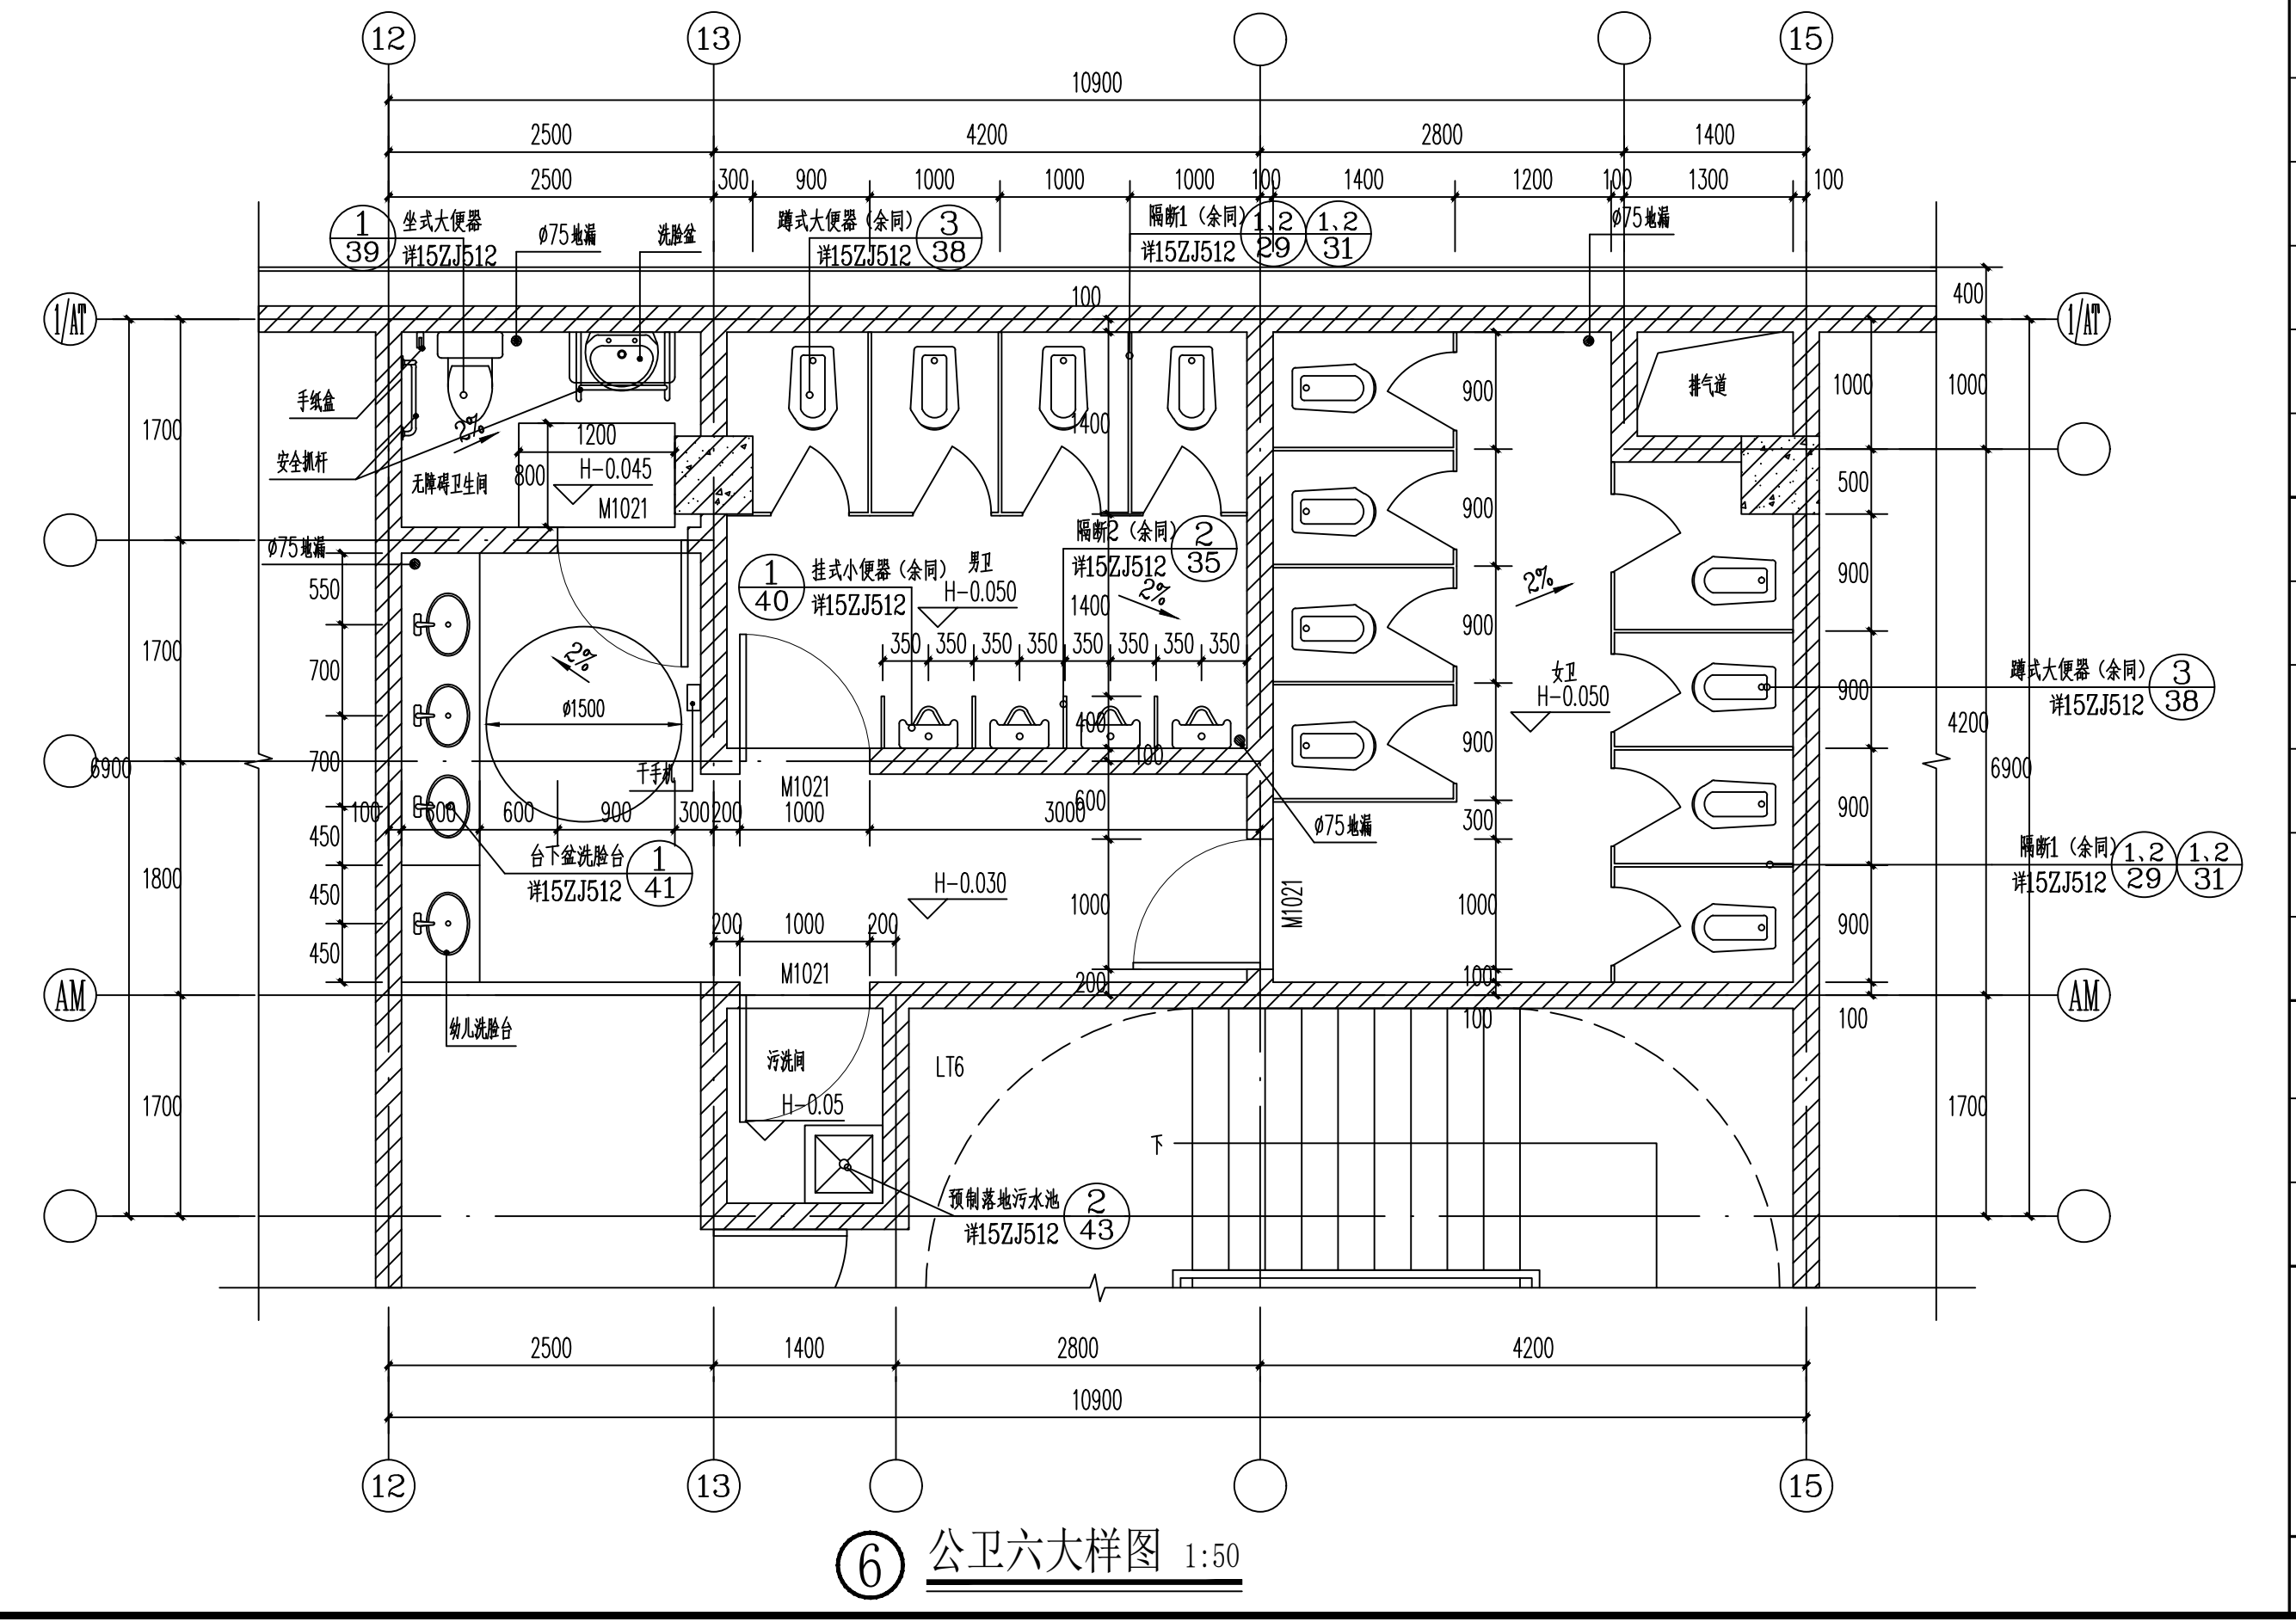
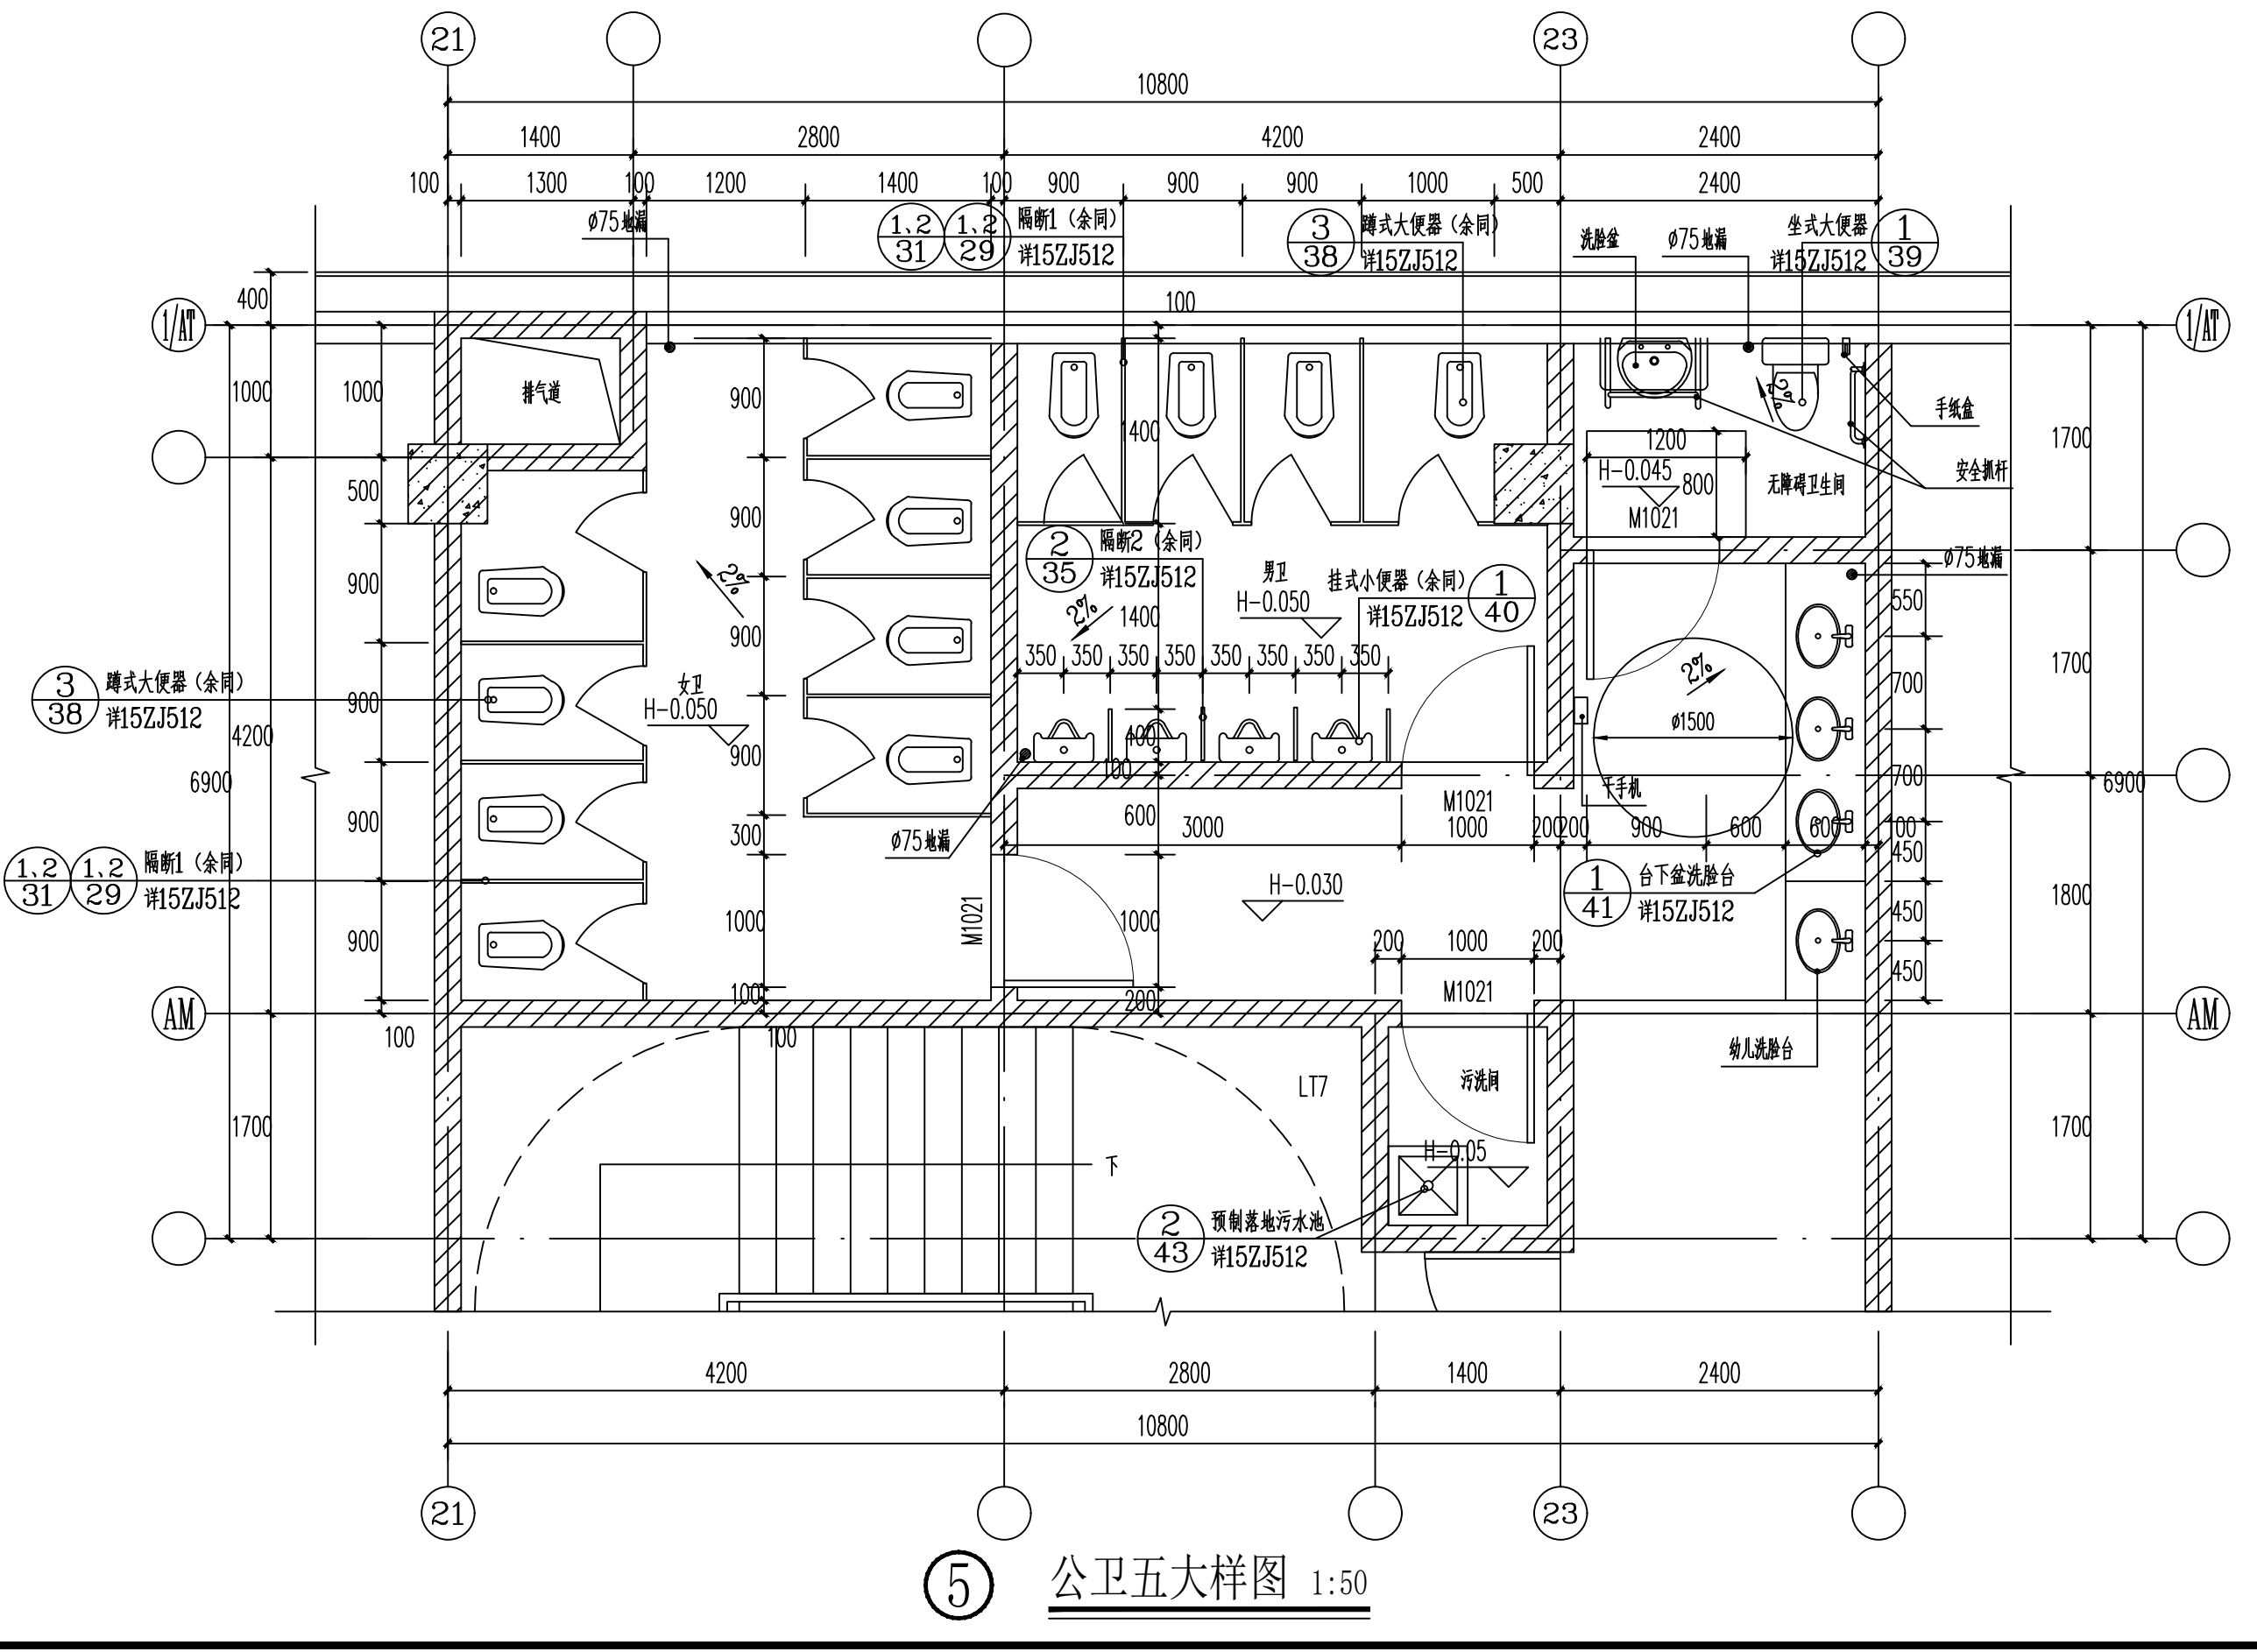
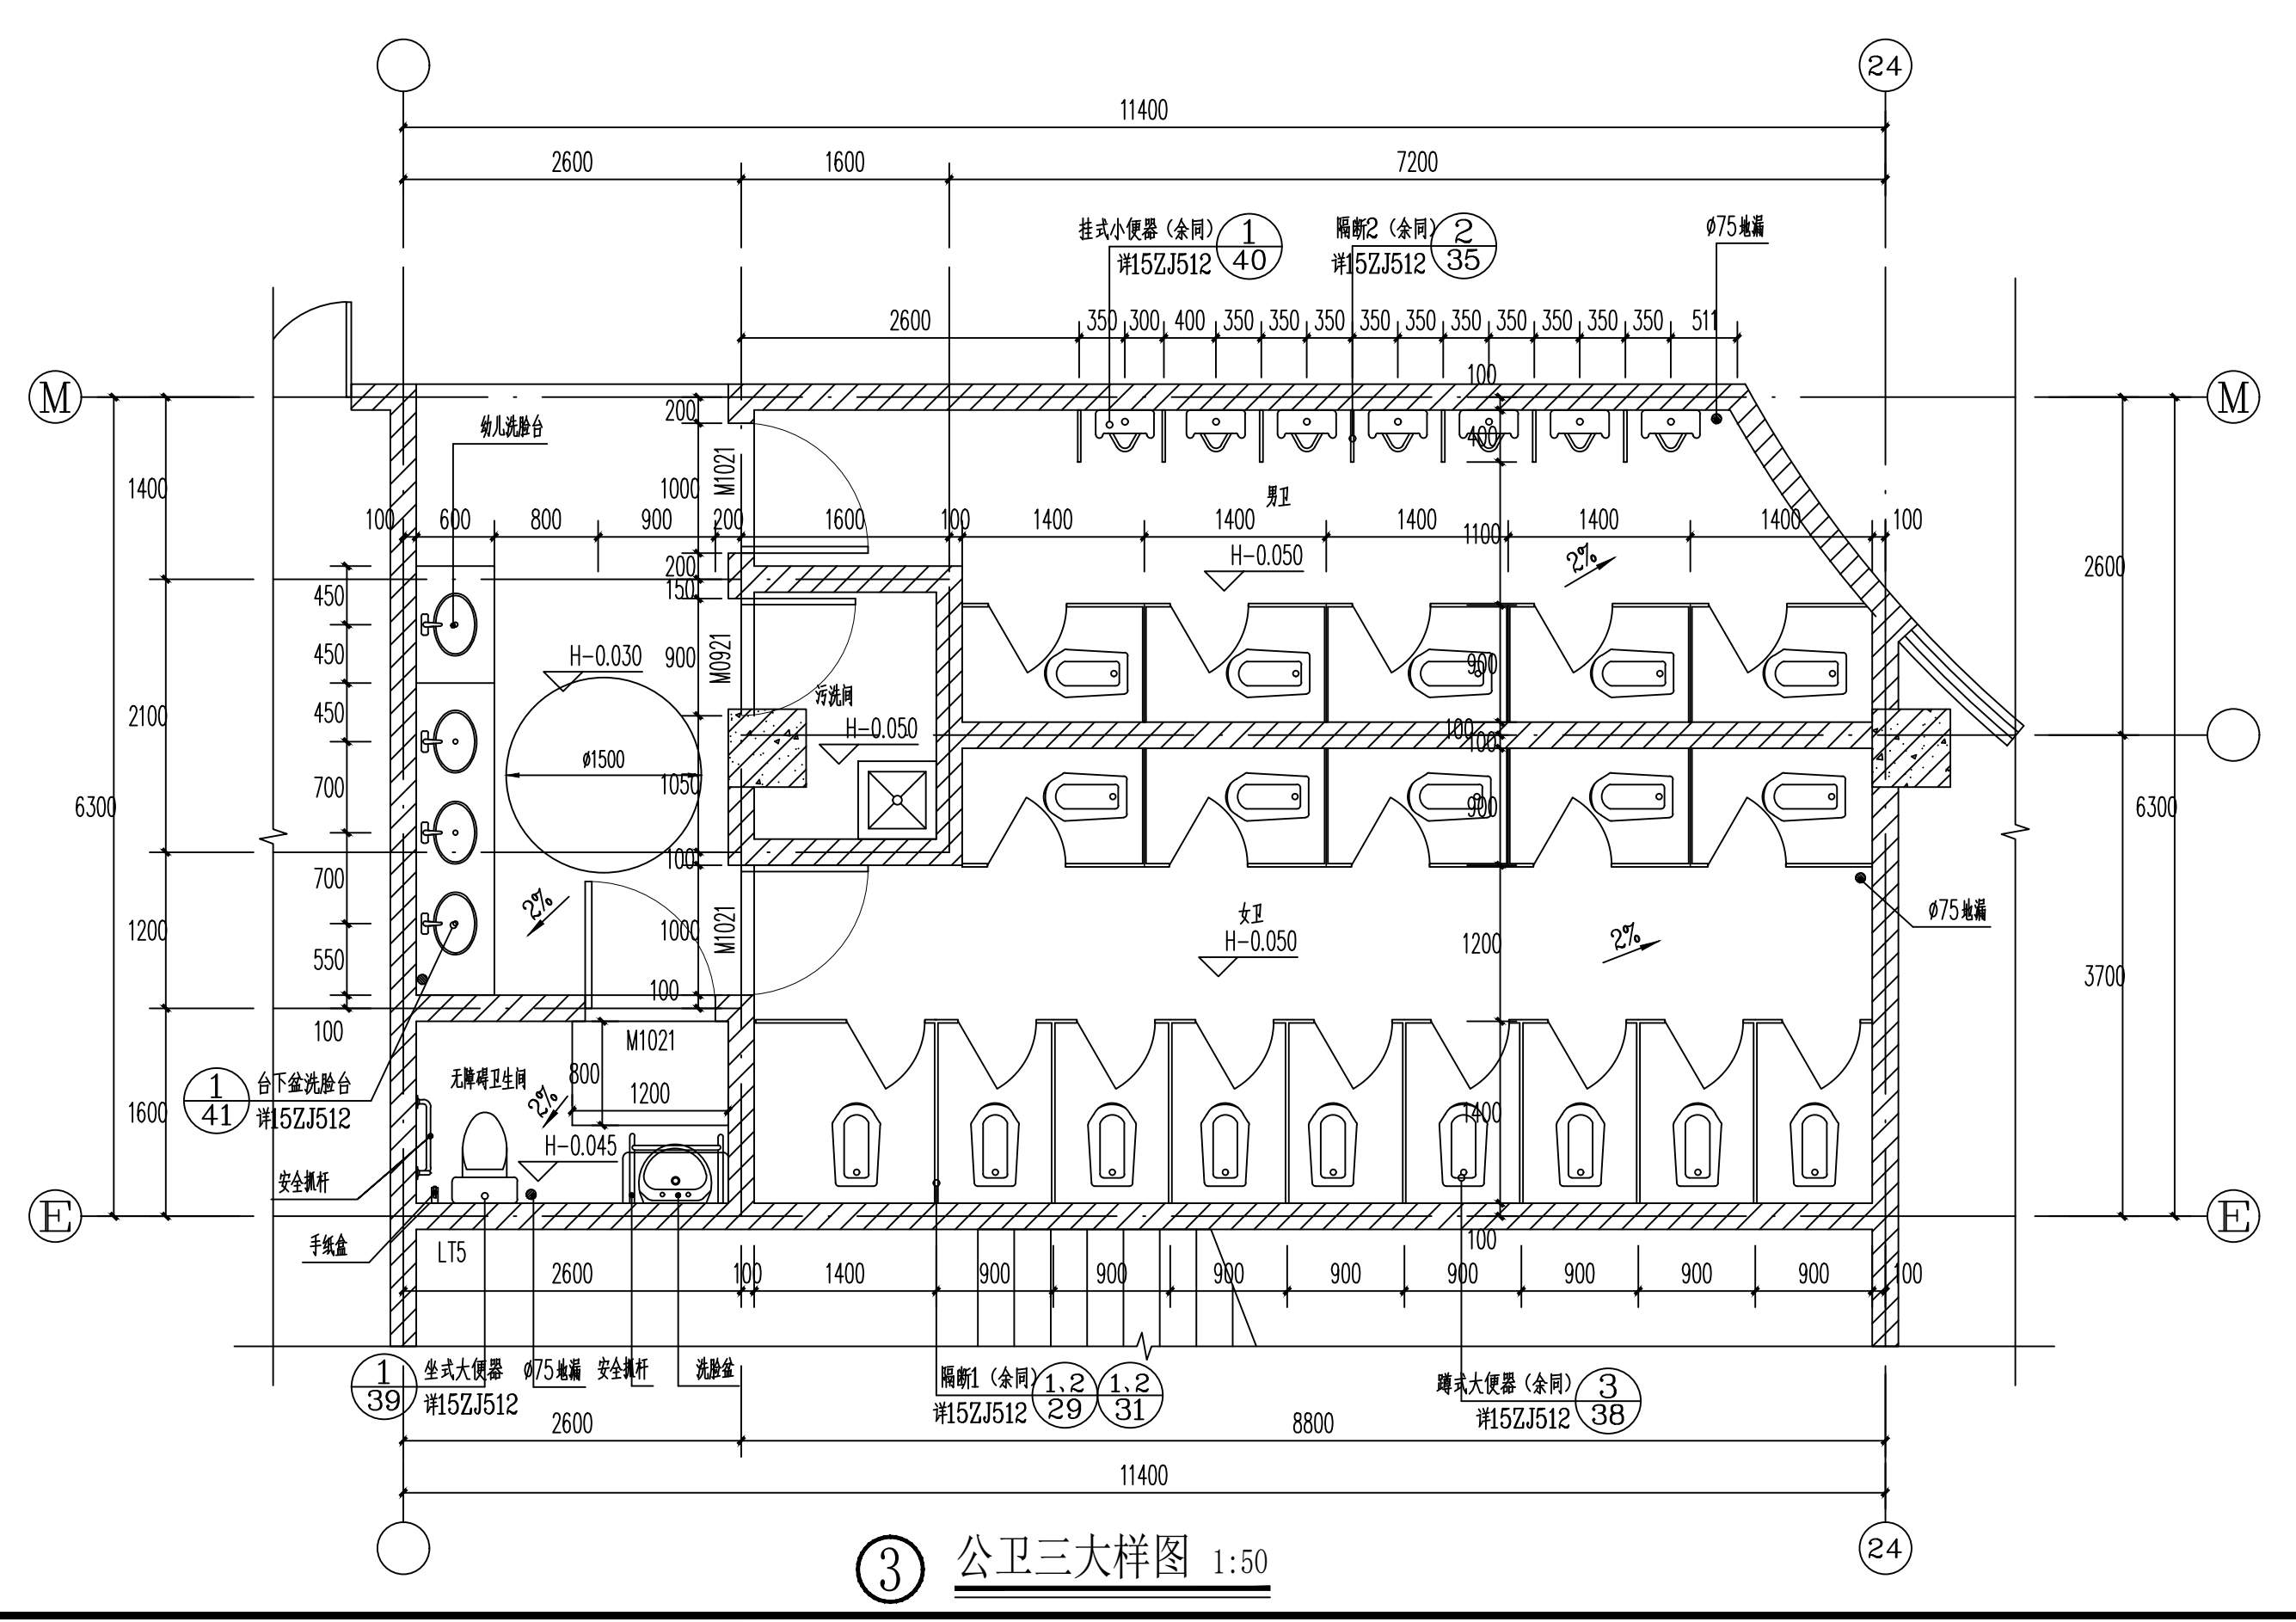
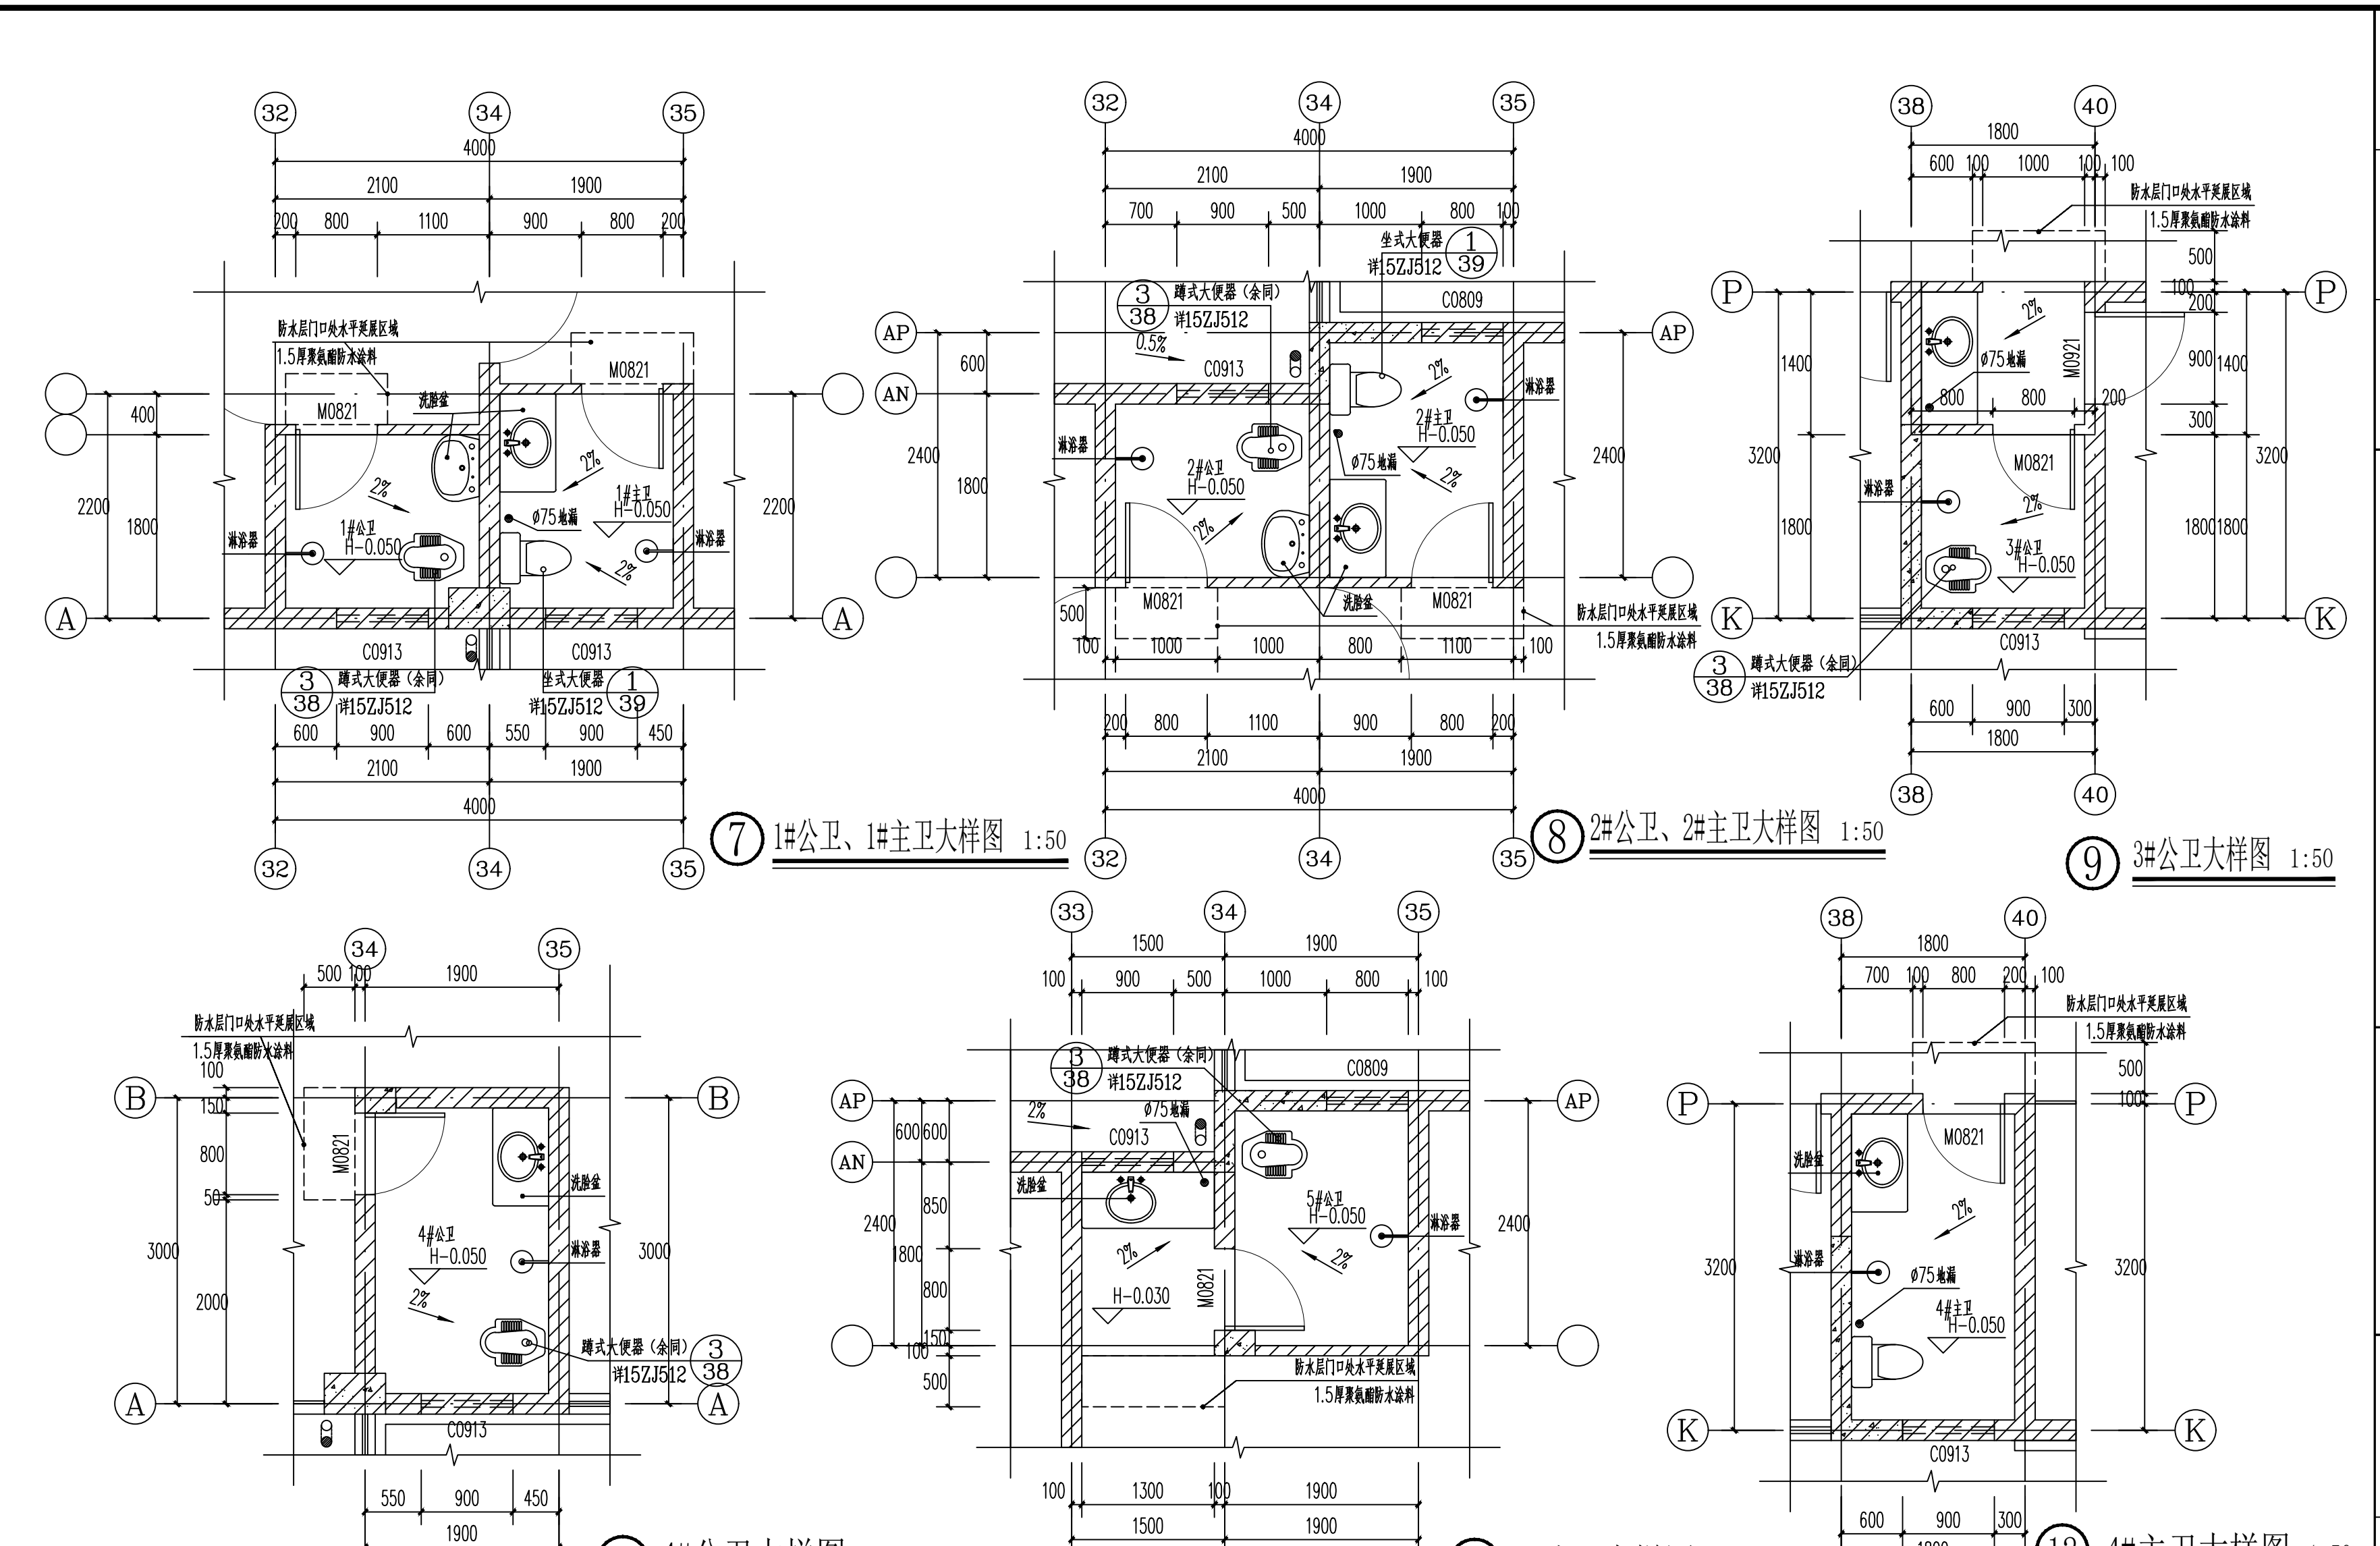
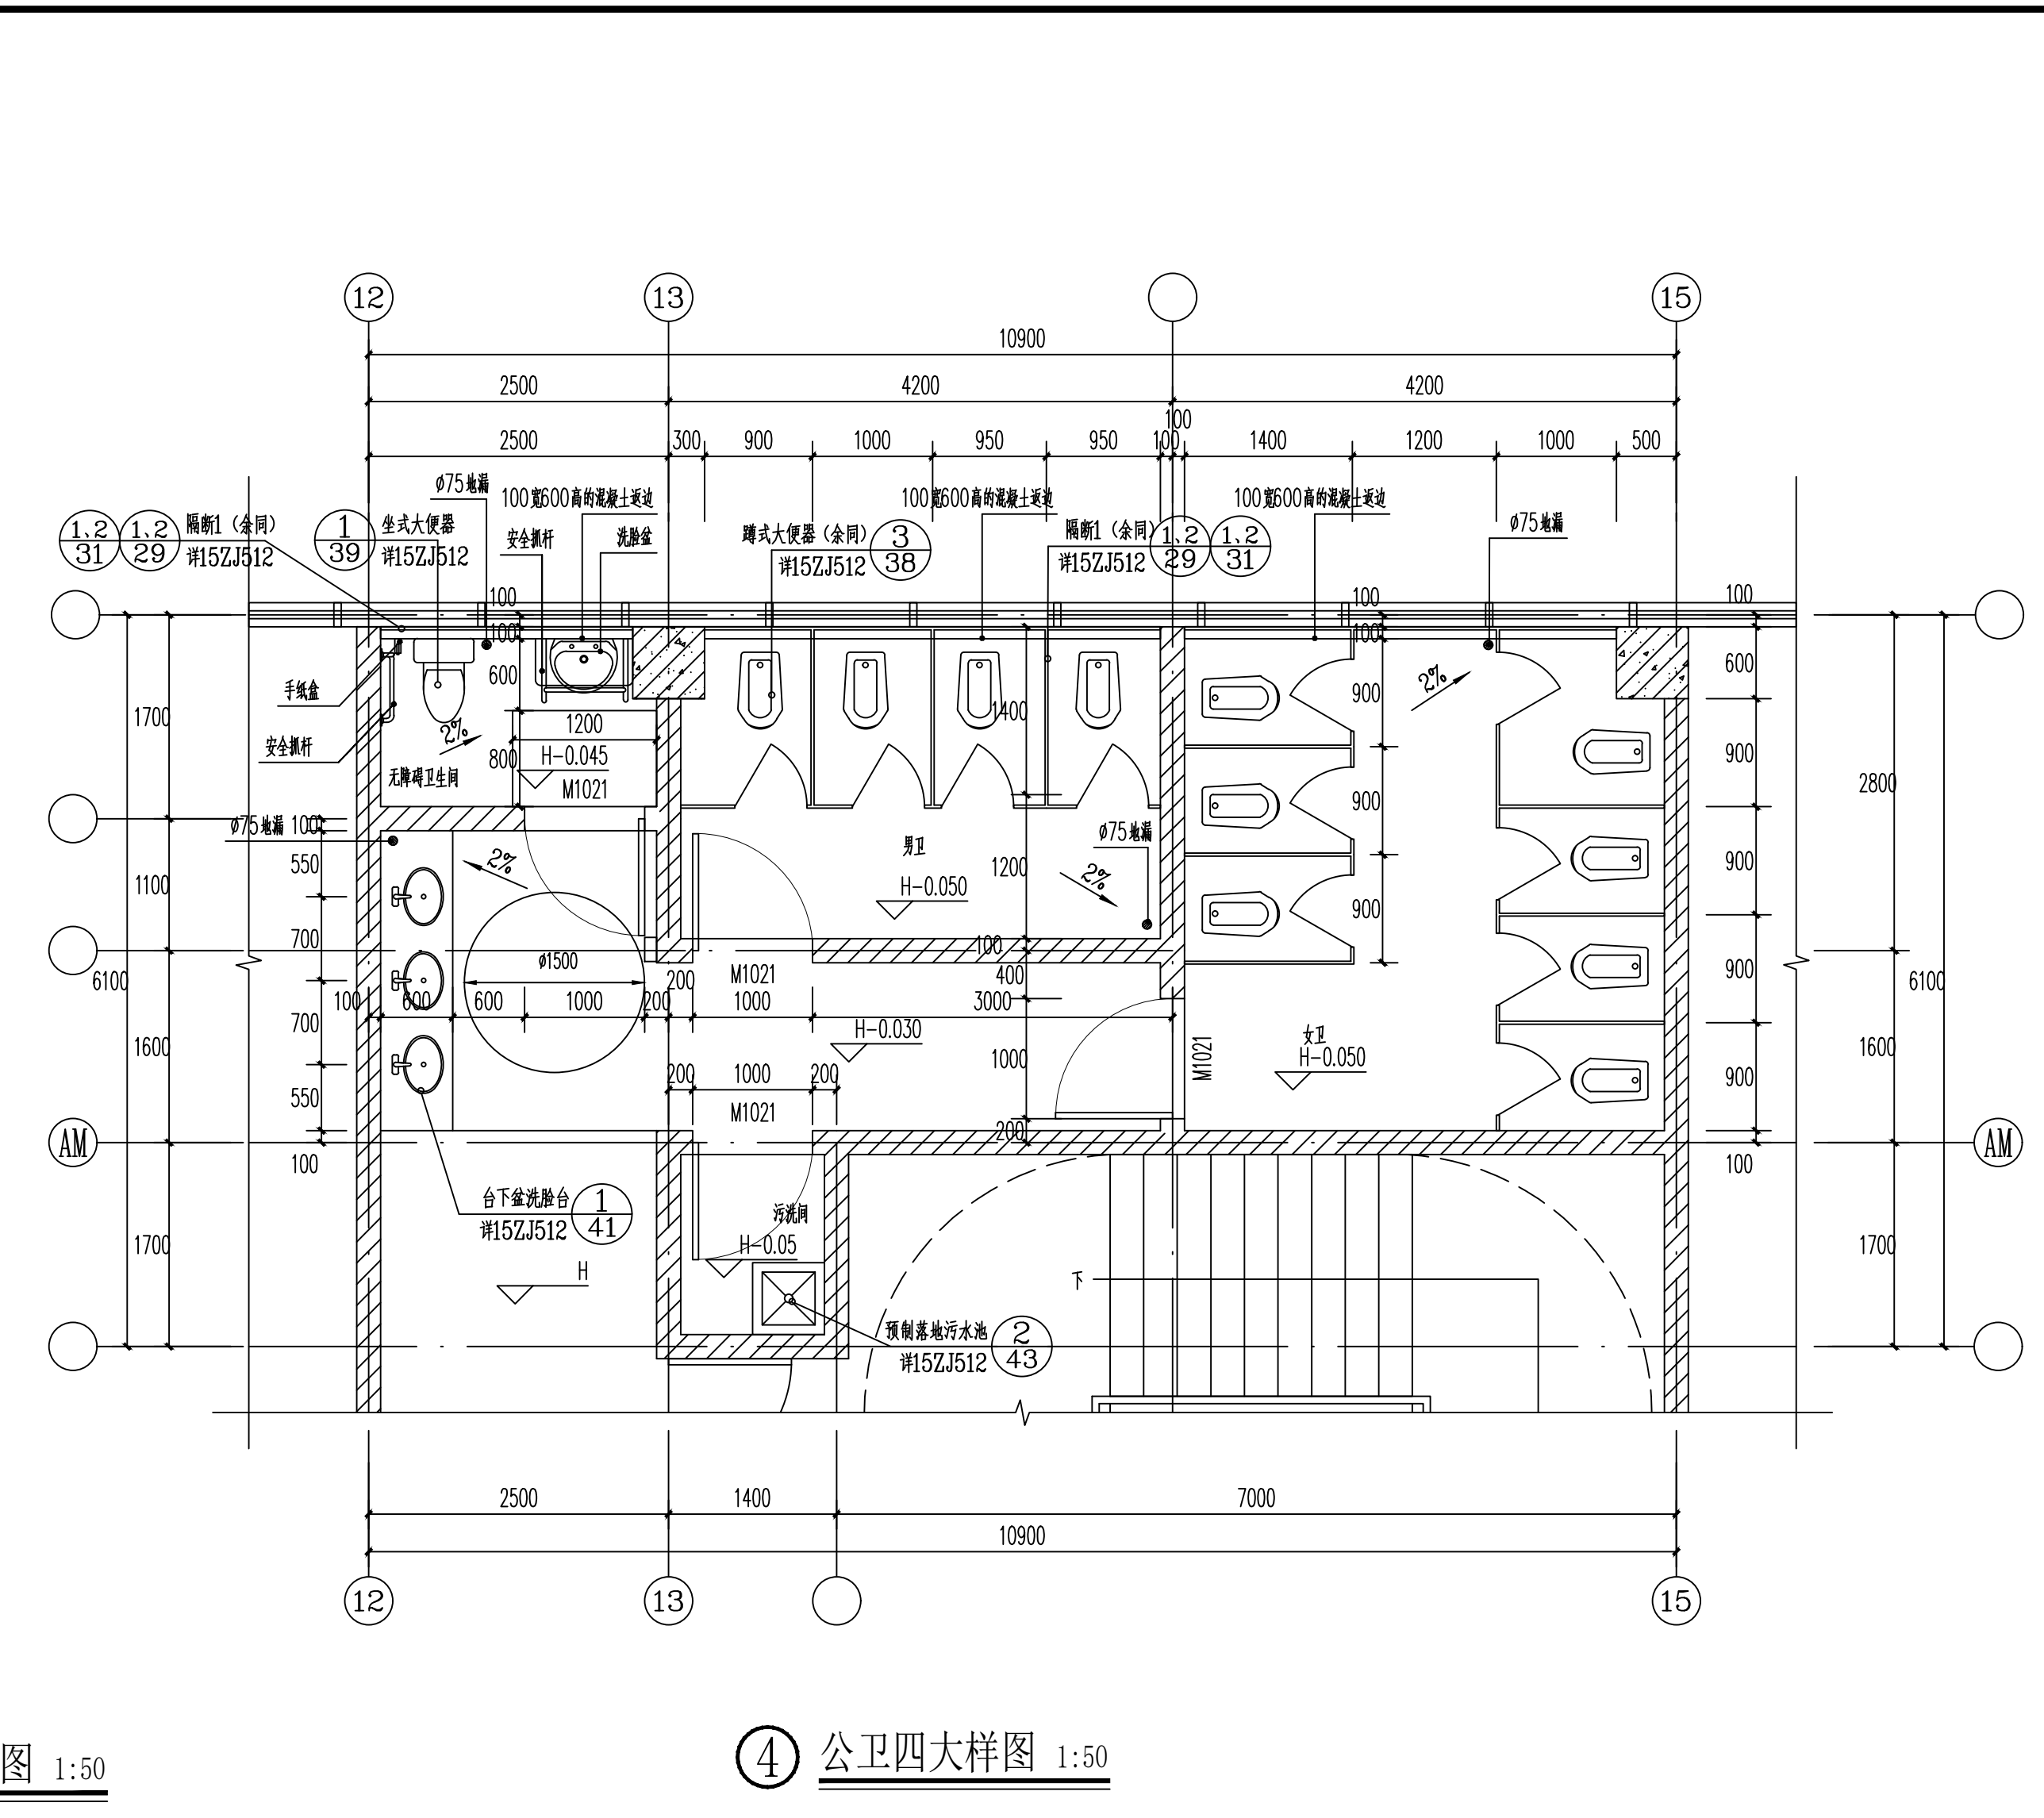


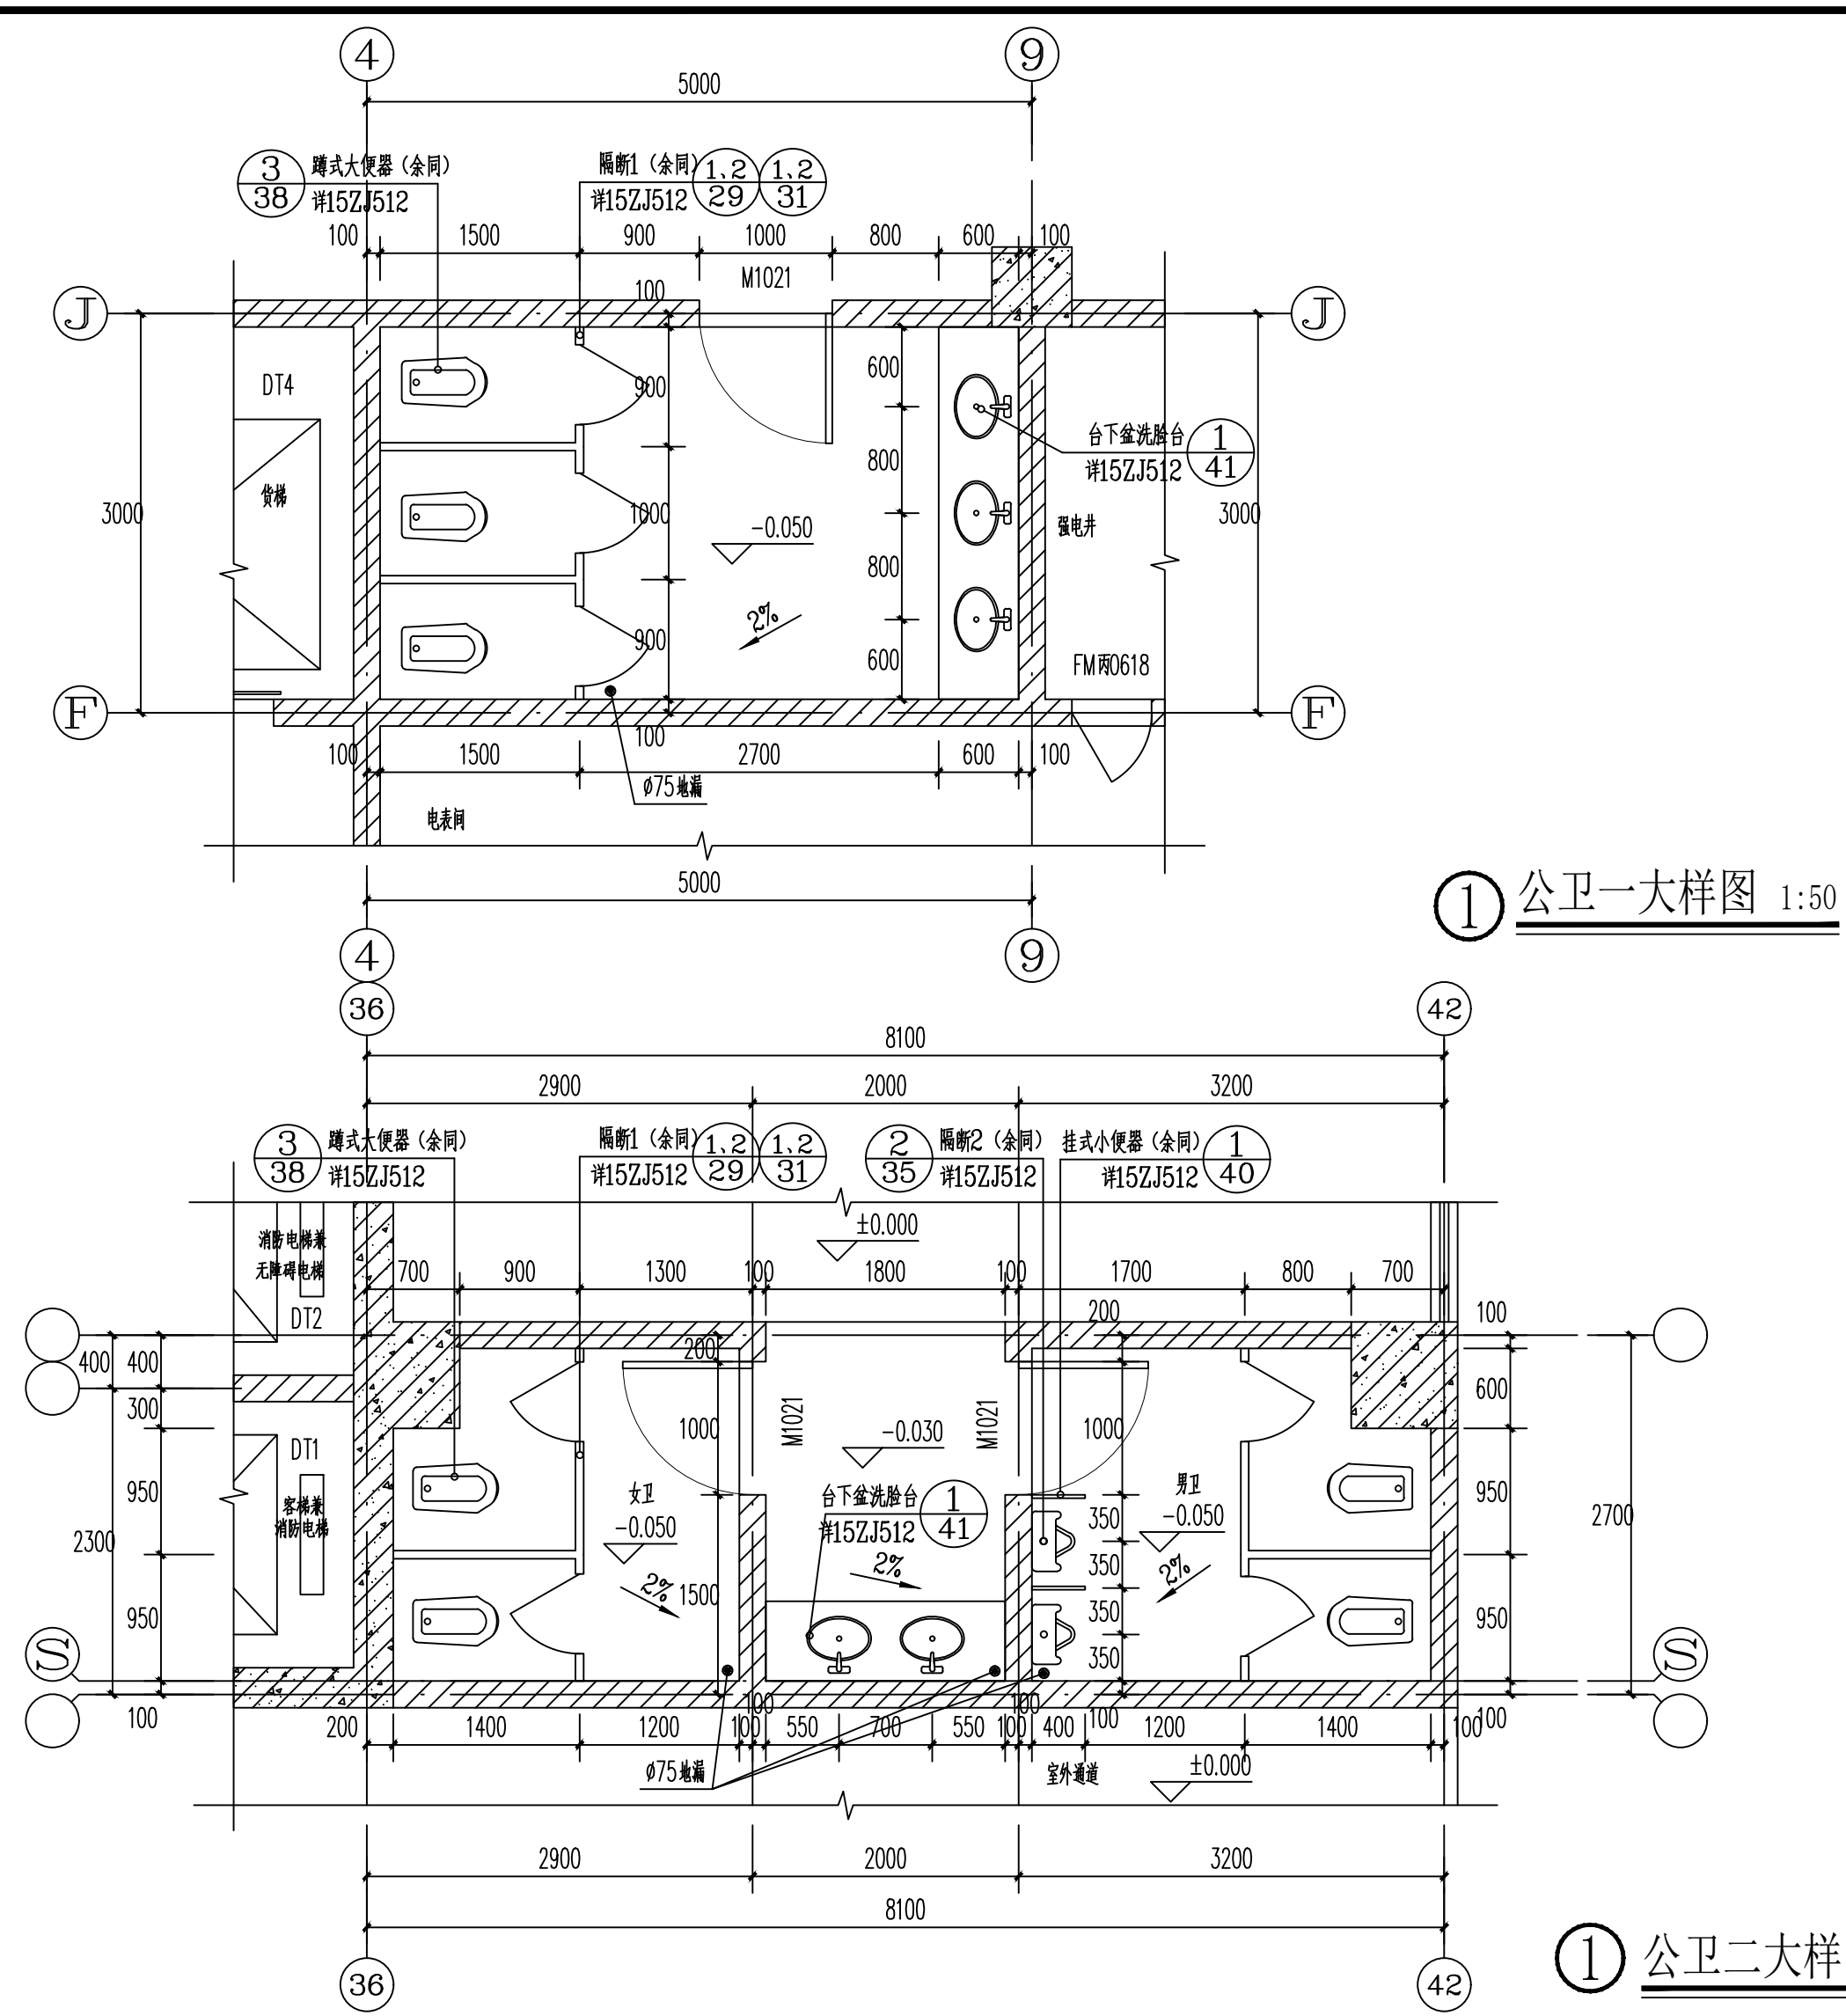

建设单位/CLIENT: 麻阳苗族自治县远桥房地产开发有限公司

项目名称/PROJECT: 远程国际

子项目名称/SUB-PROJECT: 远程国际

区位图/REGIONAL LOCATION MAP:

广东建筑艺术设计院有限公司
GUANGDONG ARCHITECTURAL ARTISTIC DESIGN INSTITUTE CO., LTD.
■ 建筑方案设计: 甲级 ■ 风景园林设计: 乙级
■ 城乡规划设计: 乙级 ■ 市政工程设计: 乙级

图纸名称/TITLE: 卫生间大样图

项目名称/PROJECT: 远程国际

设计 DESIGNED	古新辉	古新辉
校对 CHECKED	吴新红	吴新红
专业负责人 CHIEF	吴志刚	吴志刚
项目负责人 PROJECT CHIEF	吴志刚	吴志刚
审核 IDENTIFIED	黄展优	黄展优
审定 APPROVED	李 坚	李 坚

业务号/JOB NO.

设计阶段/STATUS: 施工图

专业/DISCIPLINE: 建施

比例/
SCALE: 1: 100 规格/
SIZE: A1

出图日期/DATE: 2021. 06

图号/DRAWING NO. JS-27

版次 NO.	修改内容 DESCRIPTION	日期 DATE

条形码/BARCODE:

版权所有, 不得复制、套用。
ALL RIGHTS RESERVED, DON'T COPIED, REPRODUCED.