




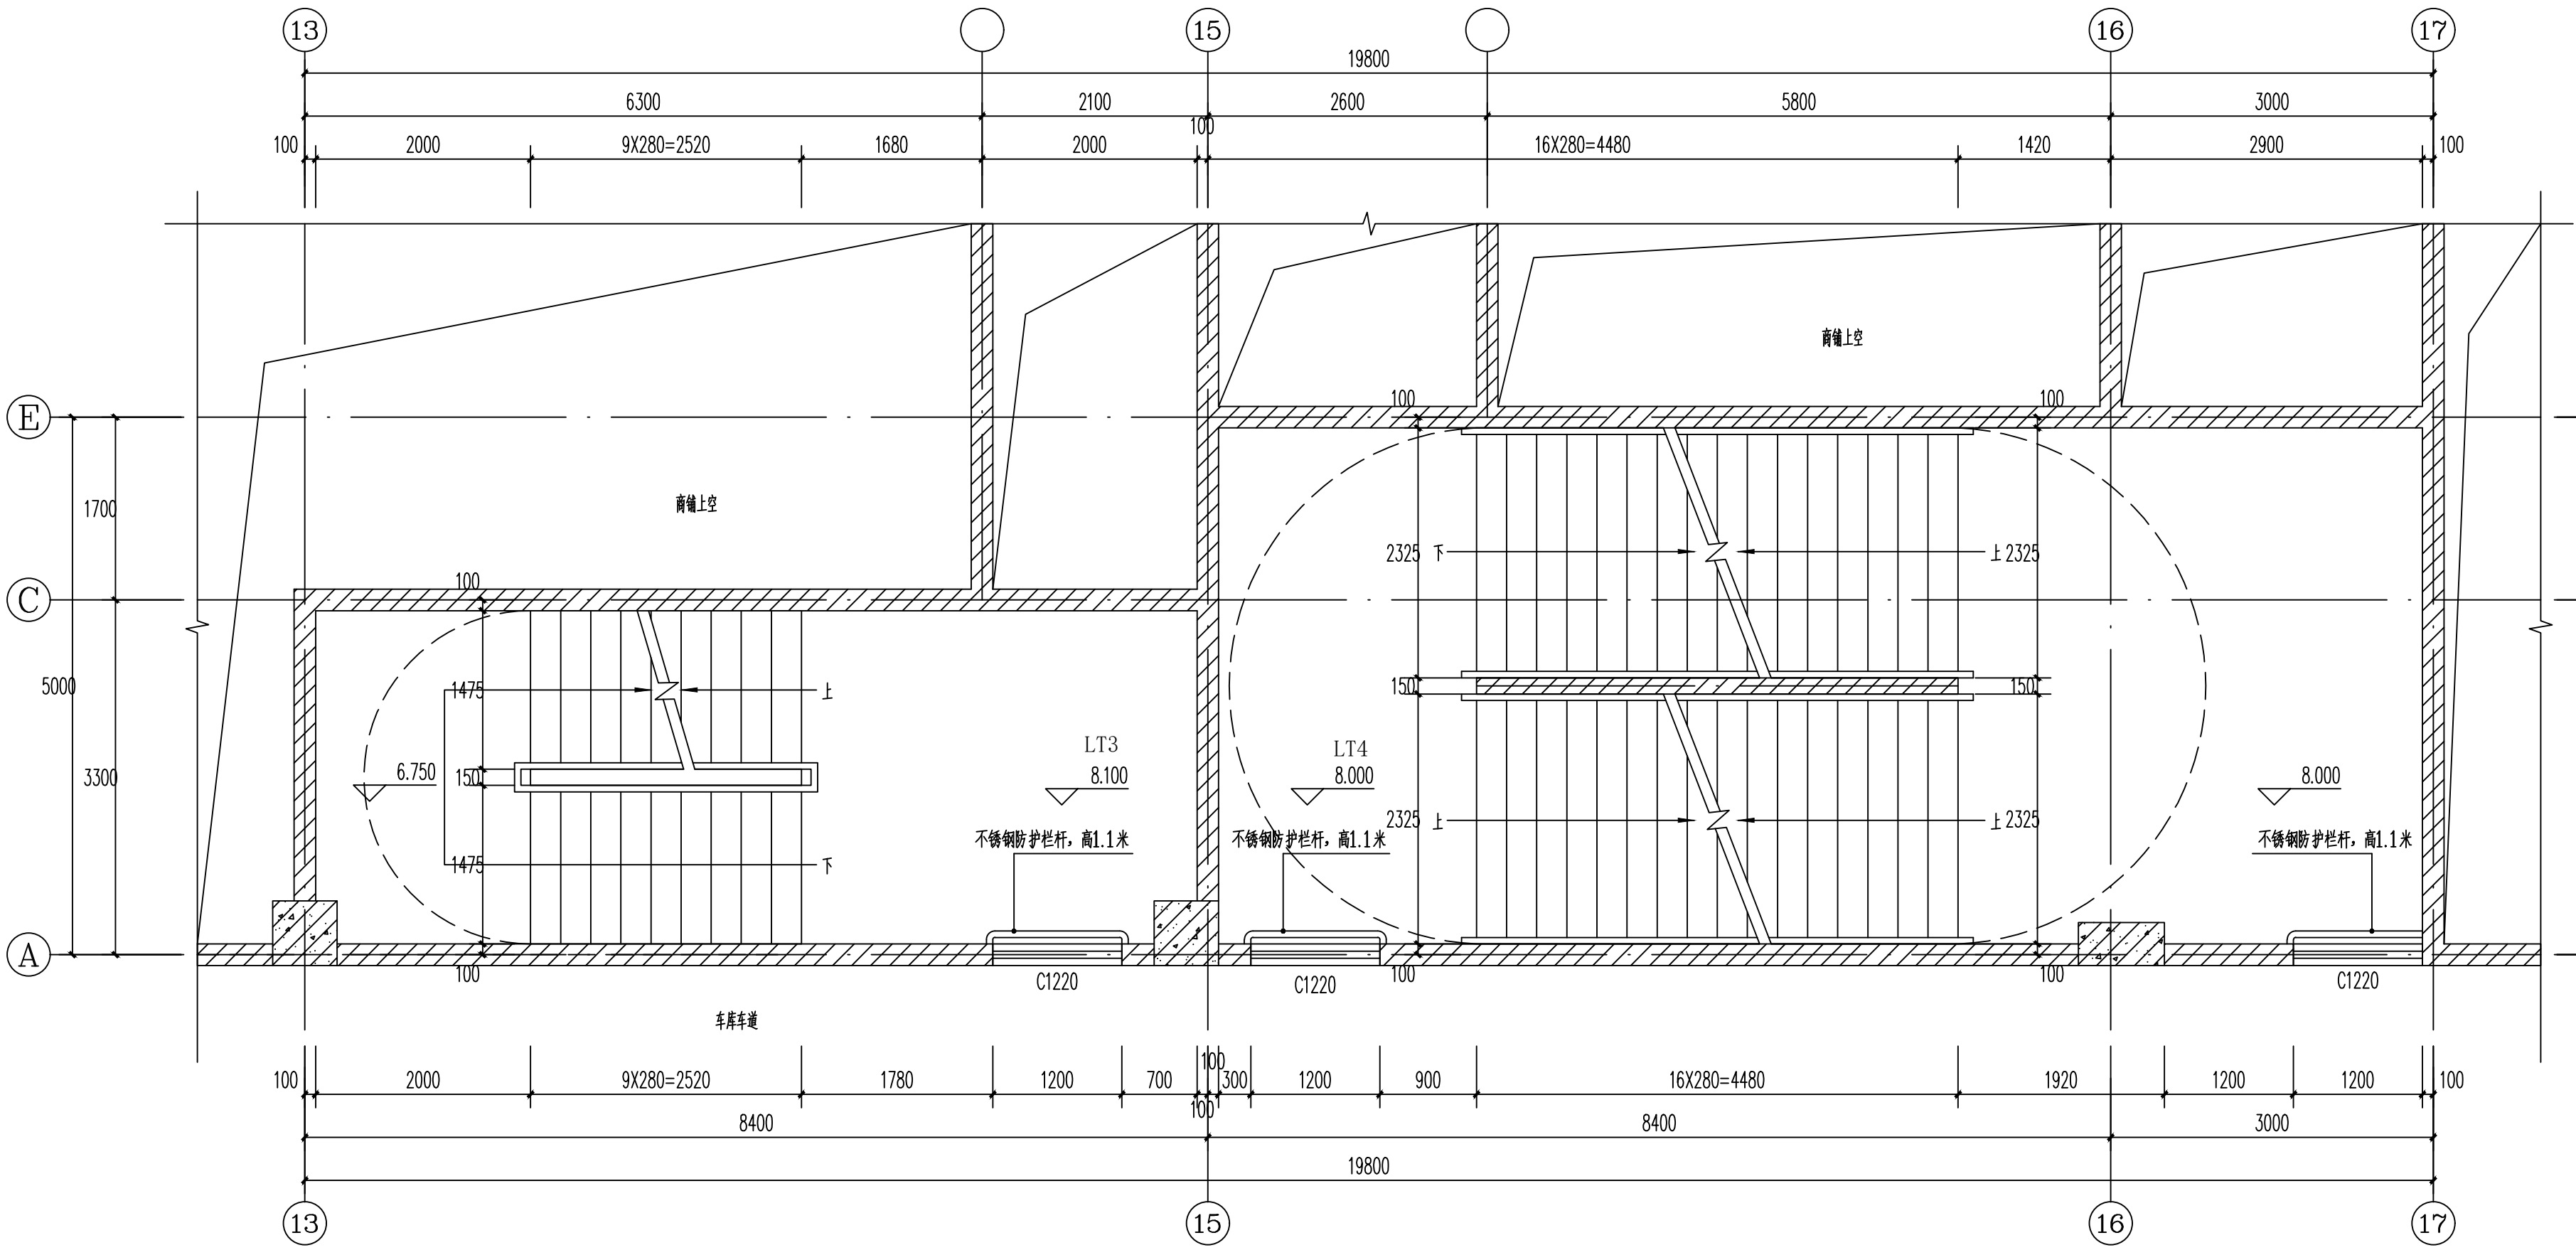


LT3、LT4楼梯间H=8.100处平面图 1:50

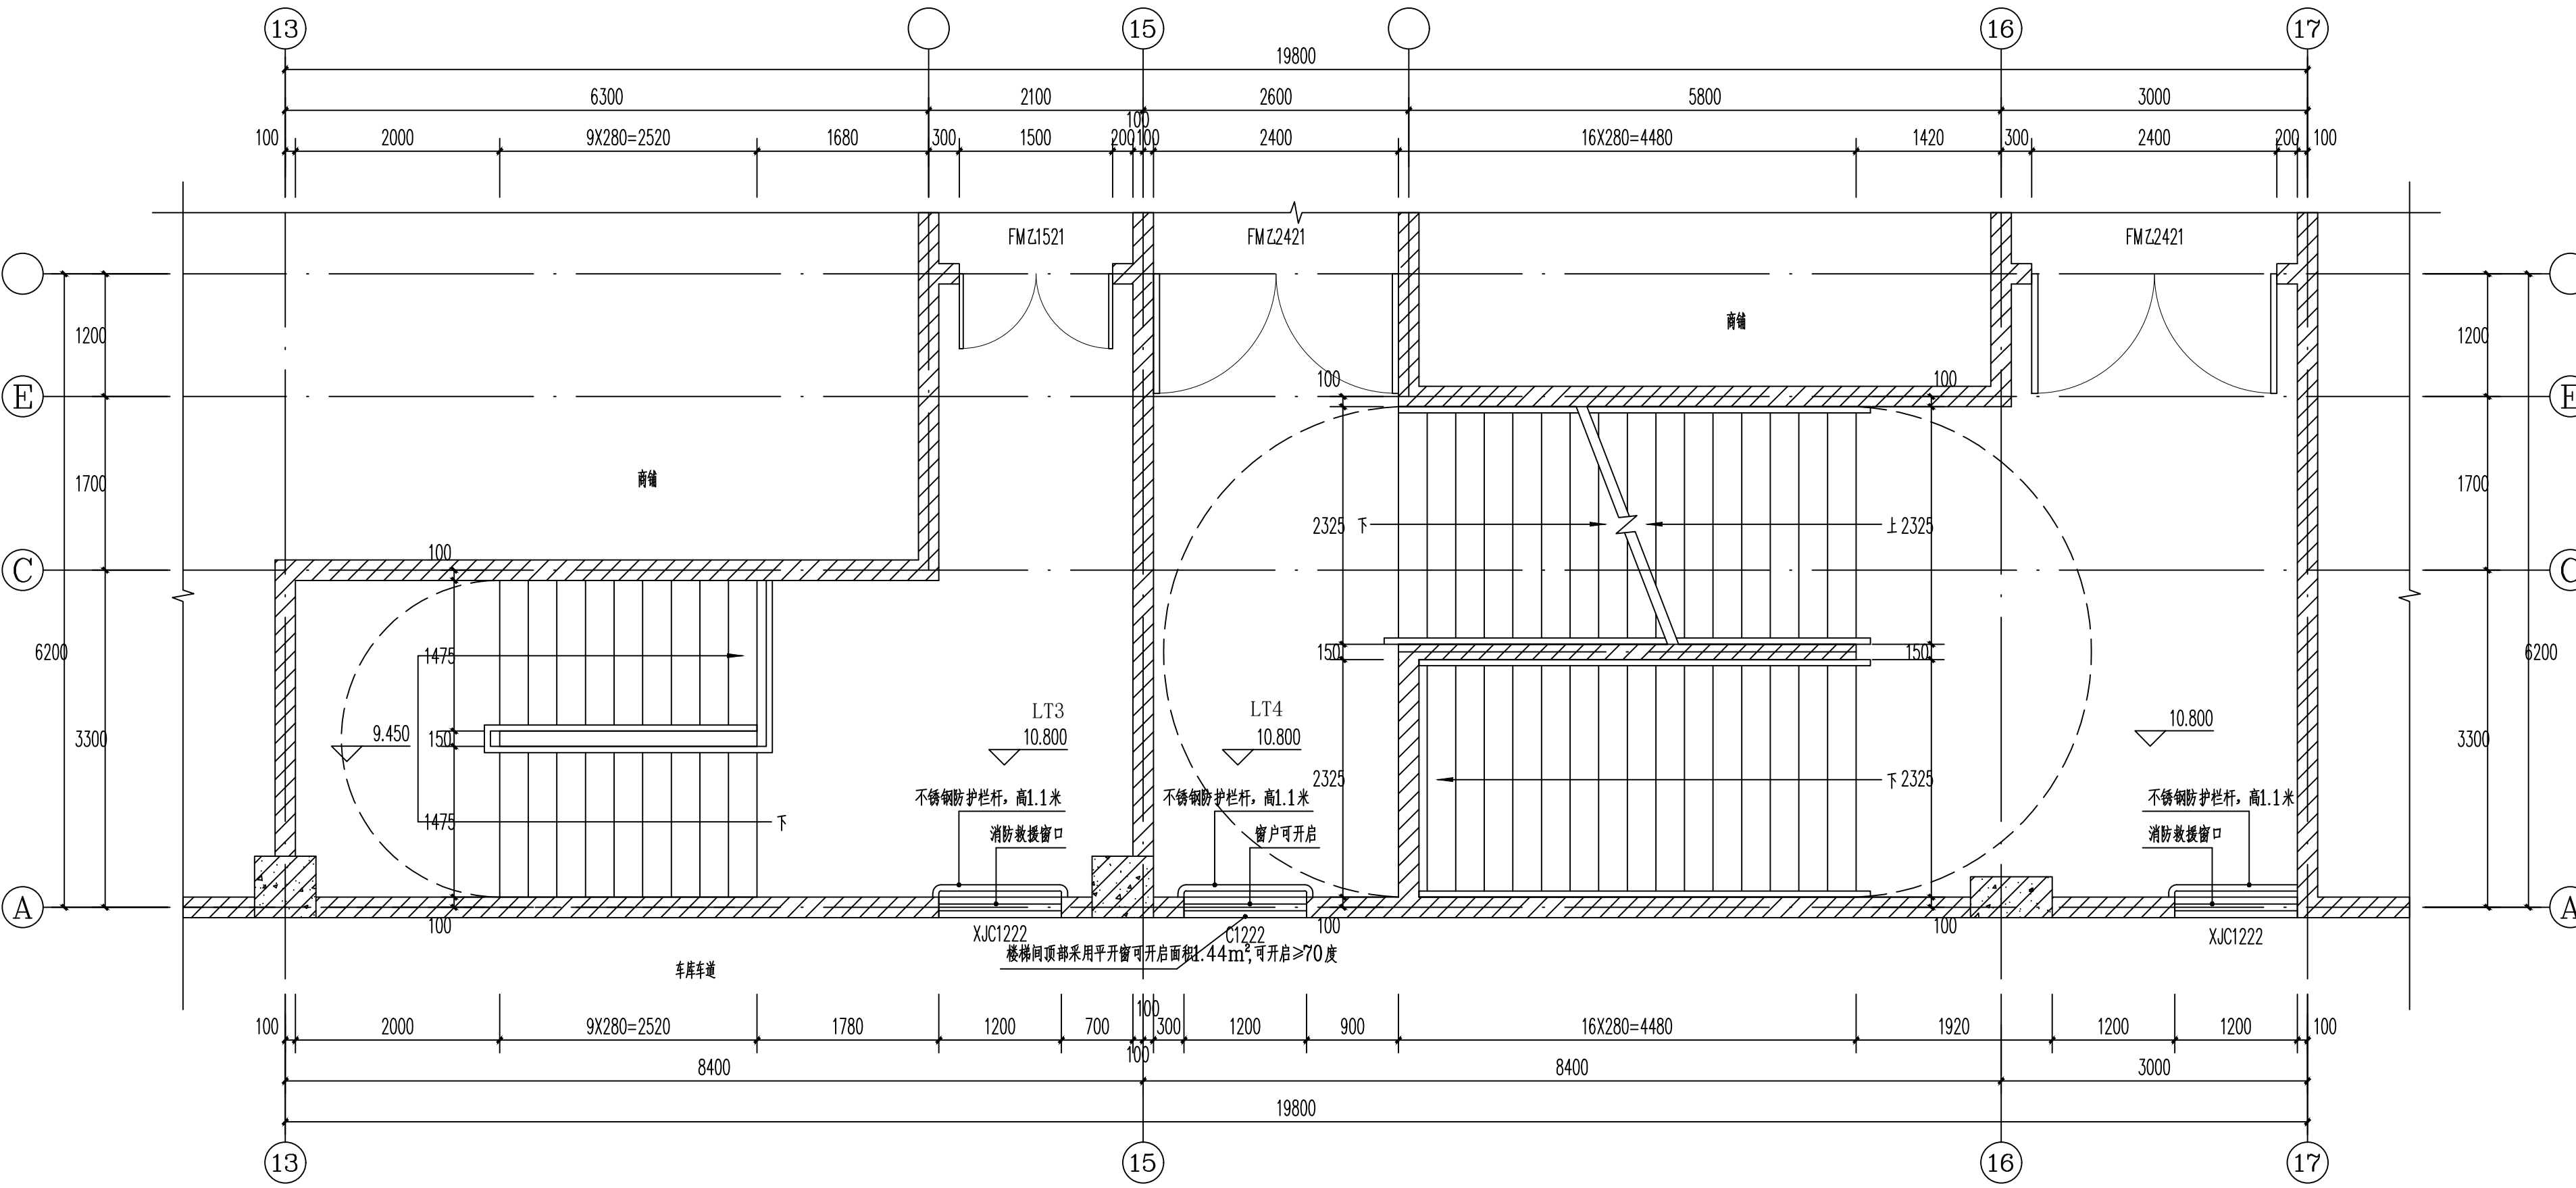


LT3、LT4楼梯间三层平面图 1:50

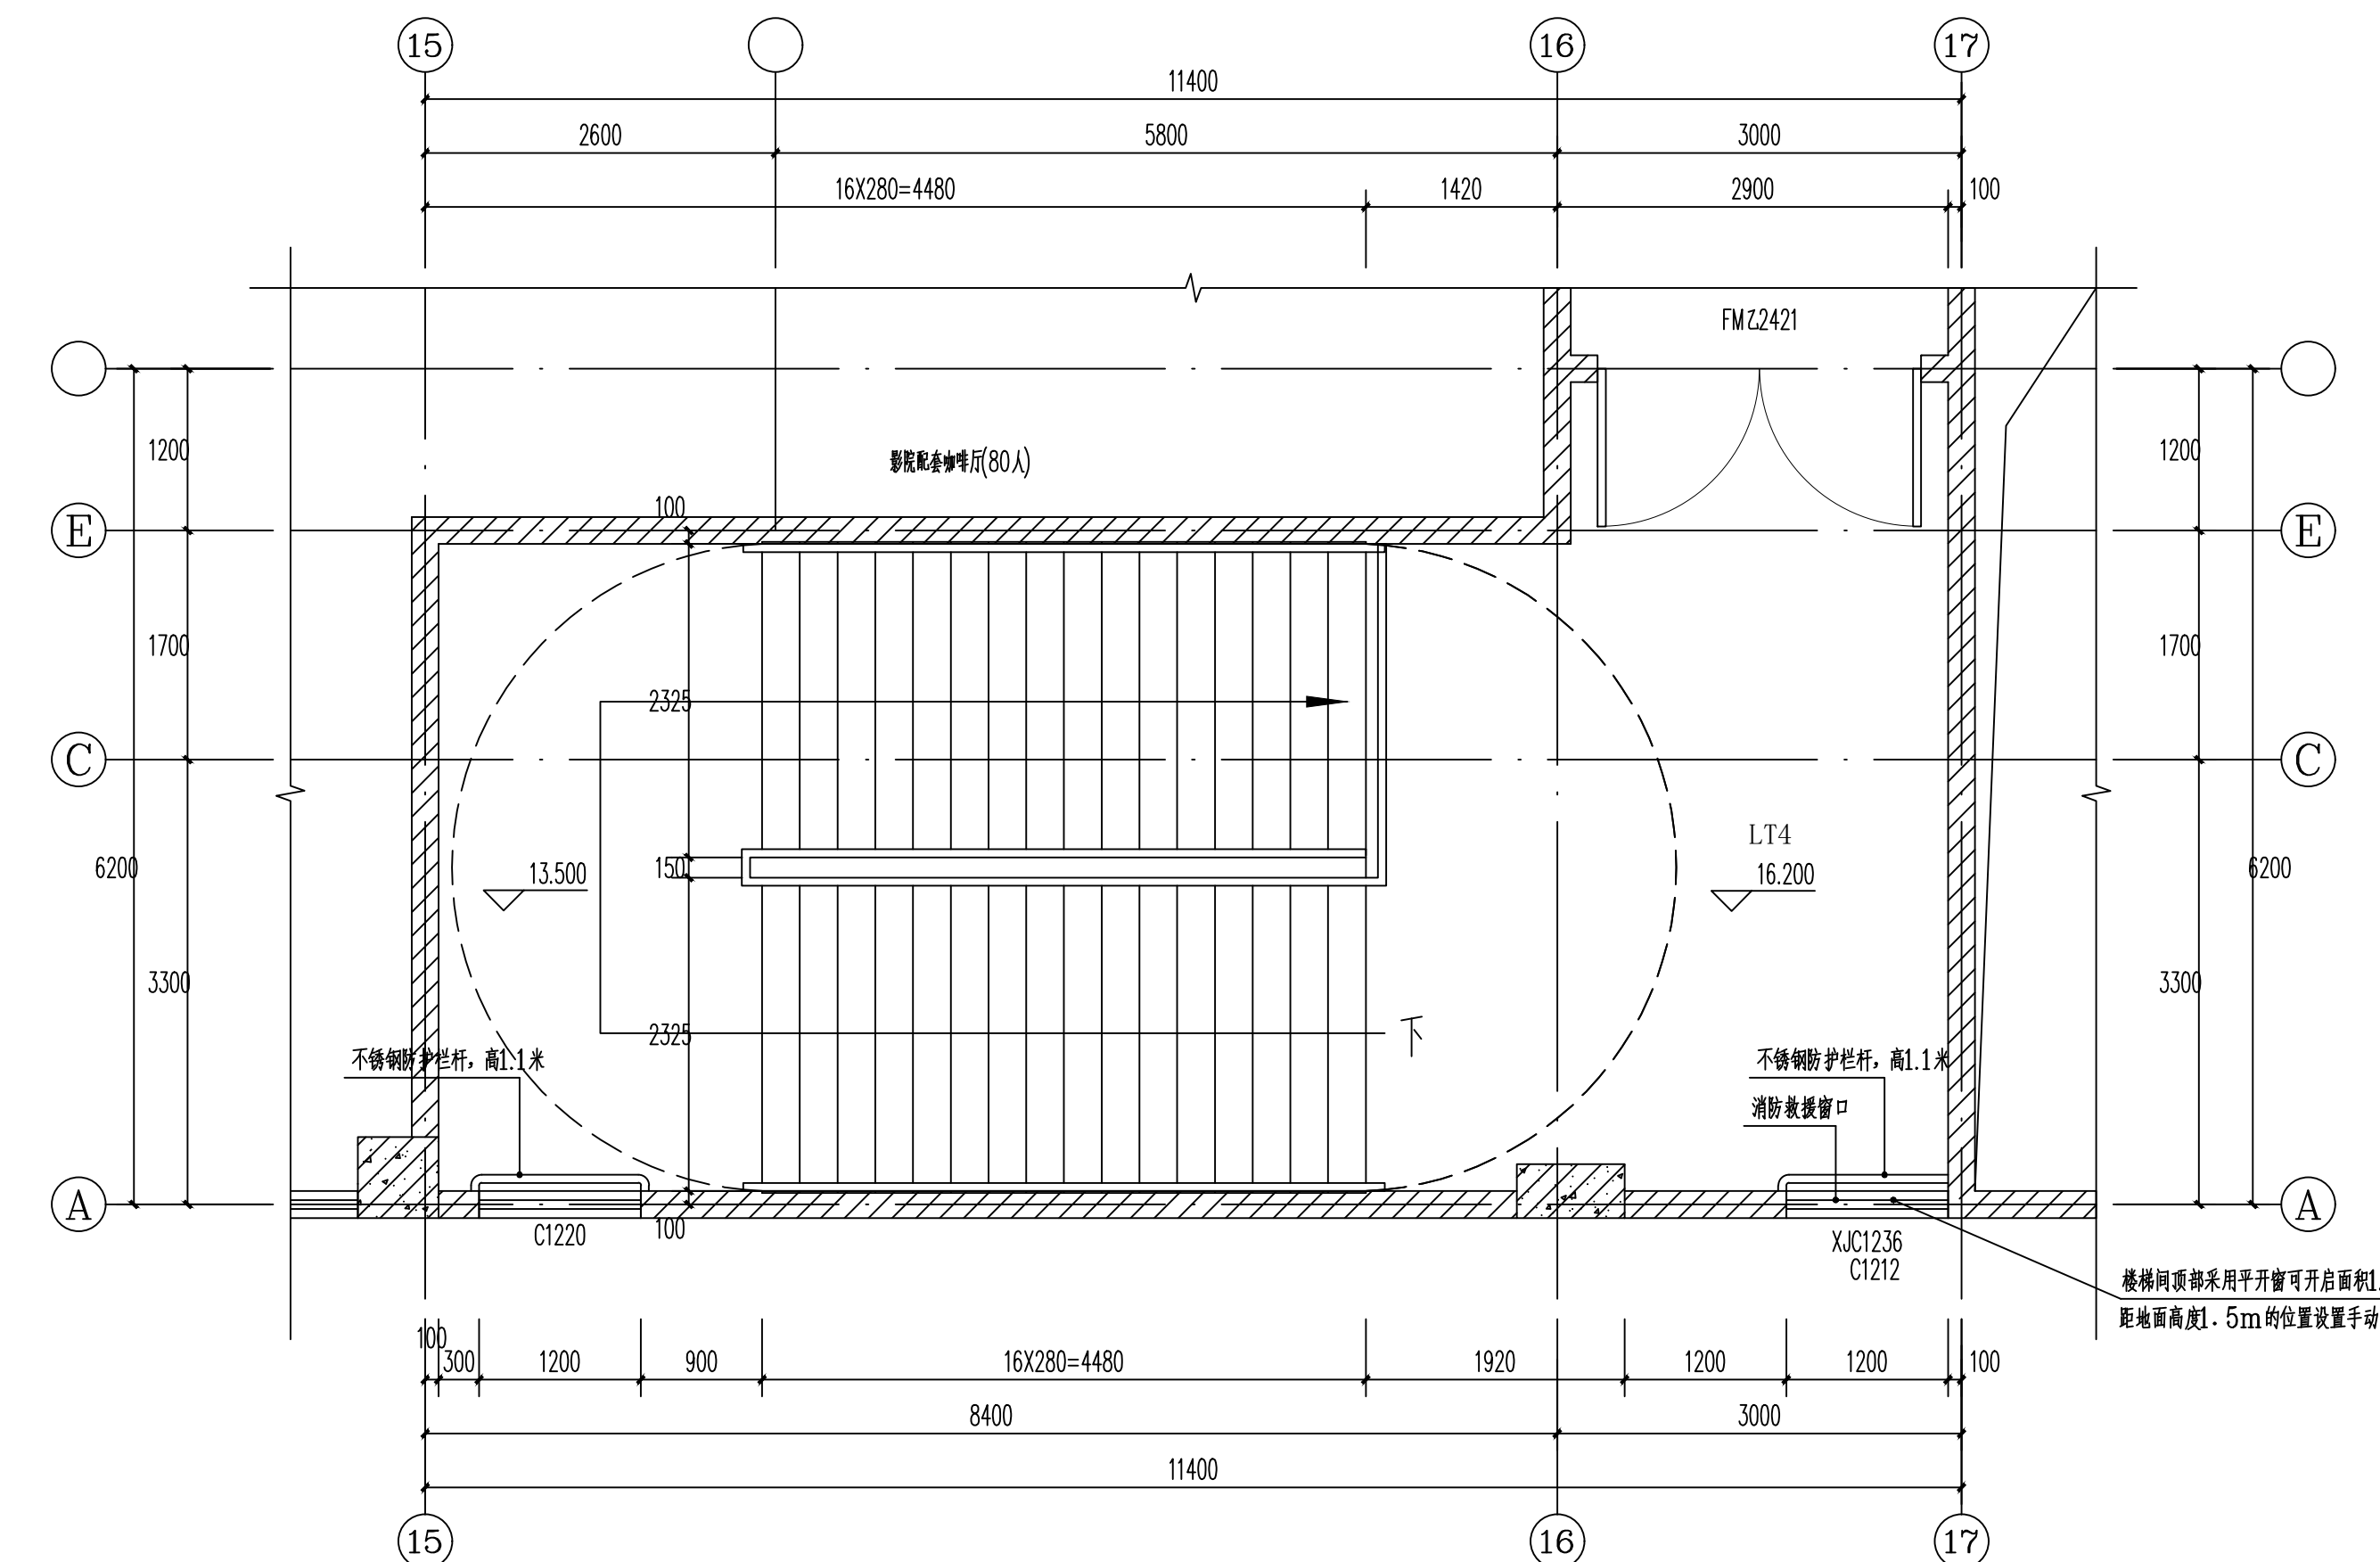


LT4楼梯间四层平面图 1:50

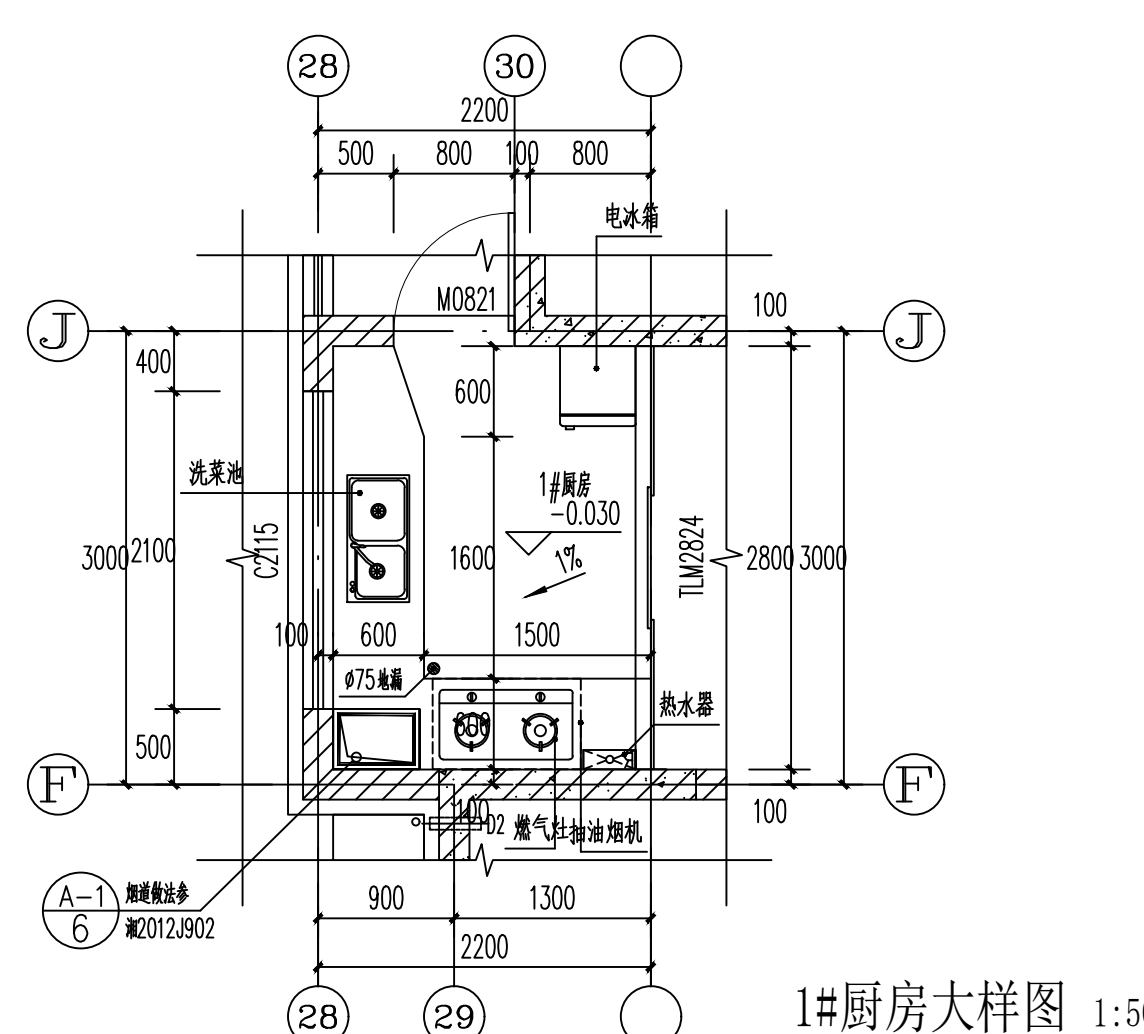


1#厨房大样图 1:50

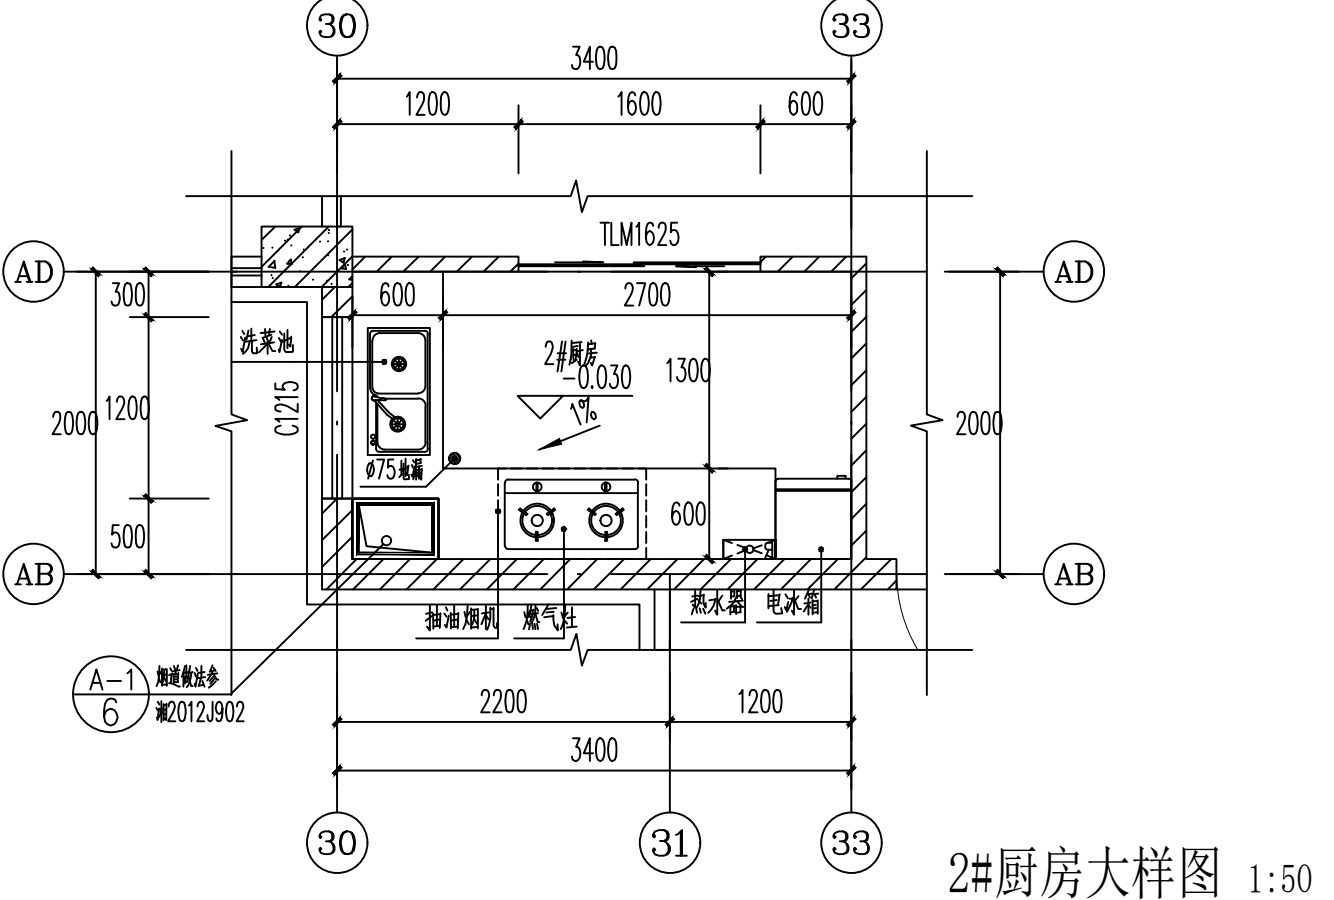


2#厨房大样图 1:50

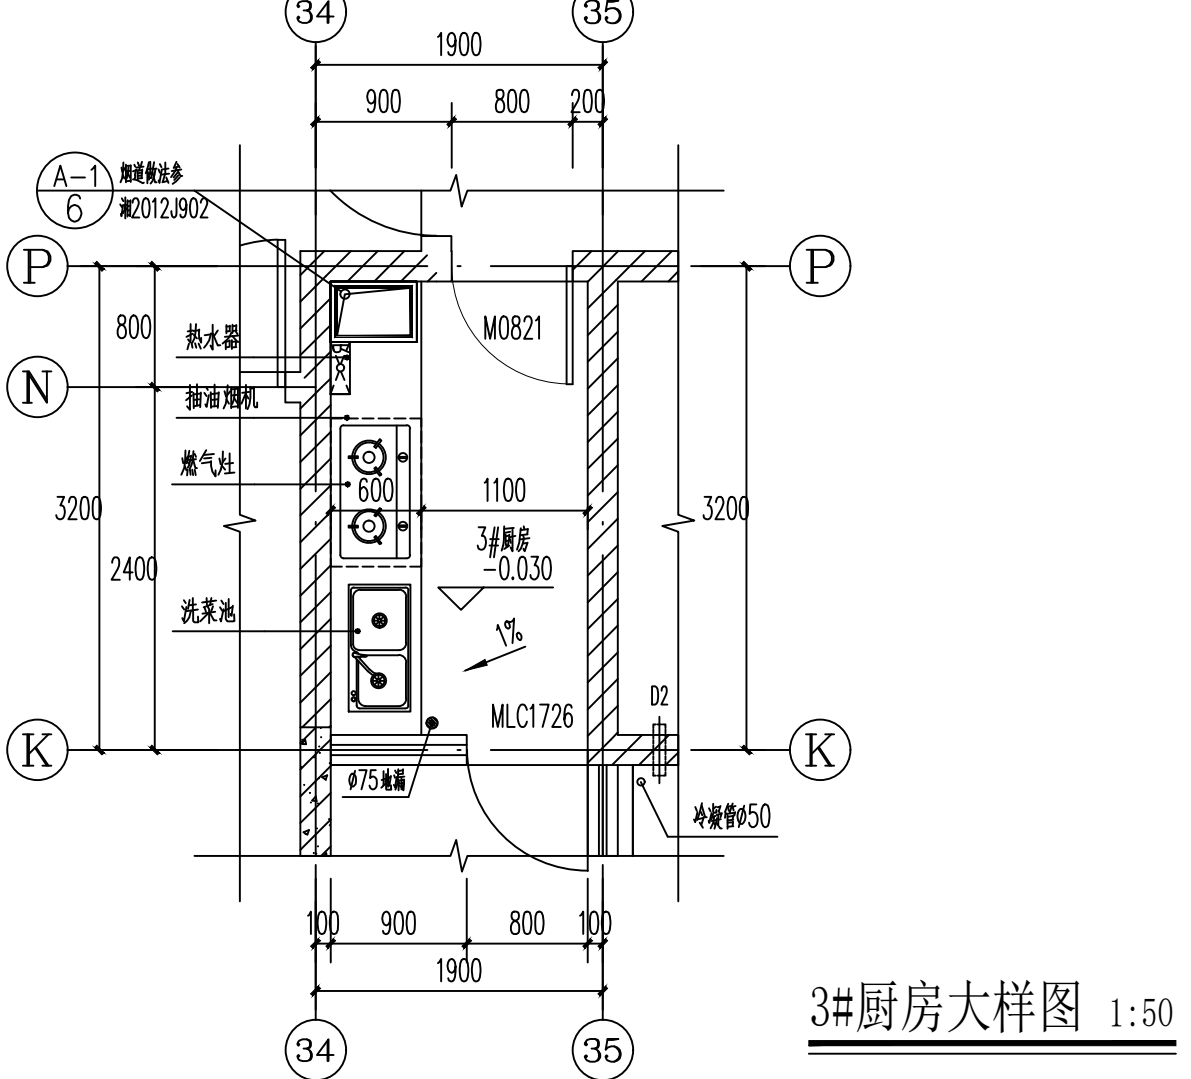

3#厨房大样图 1:50

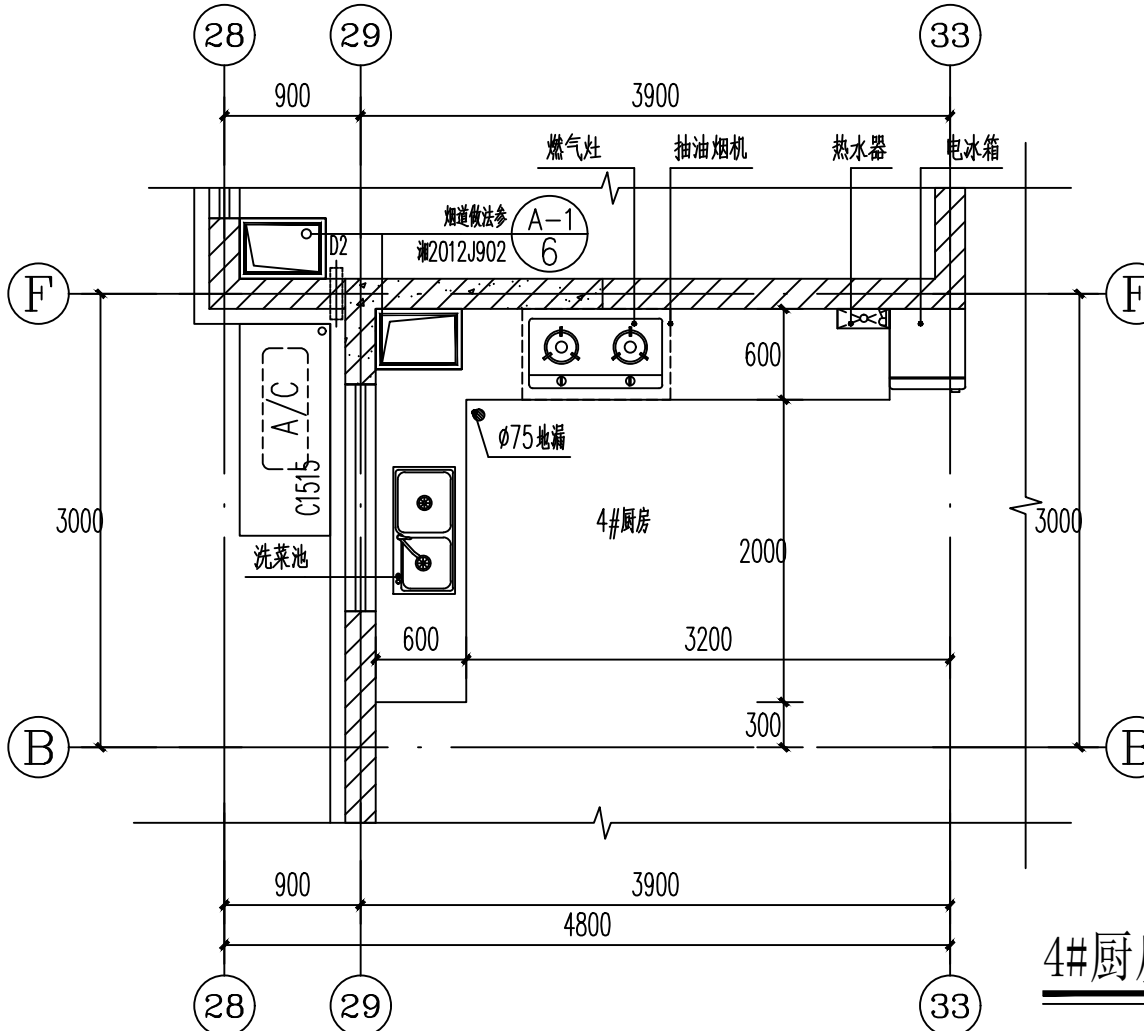

4#厨房大样图 1:50

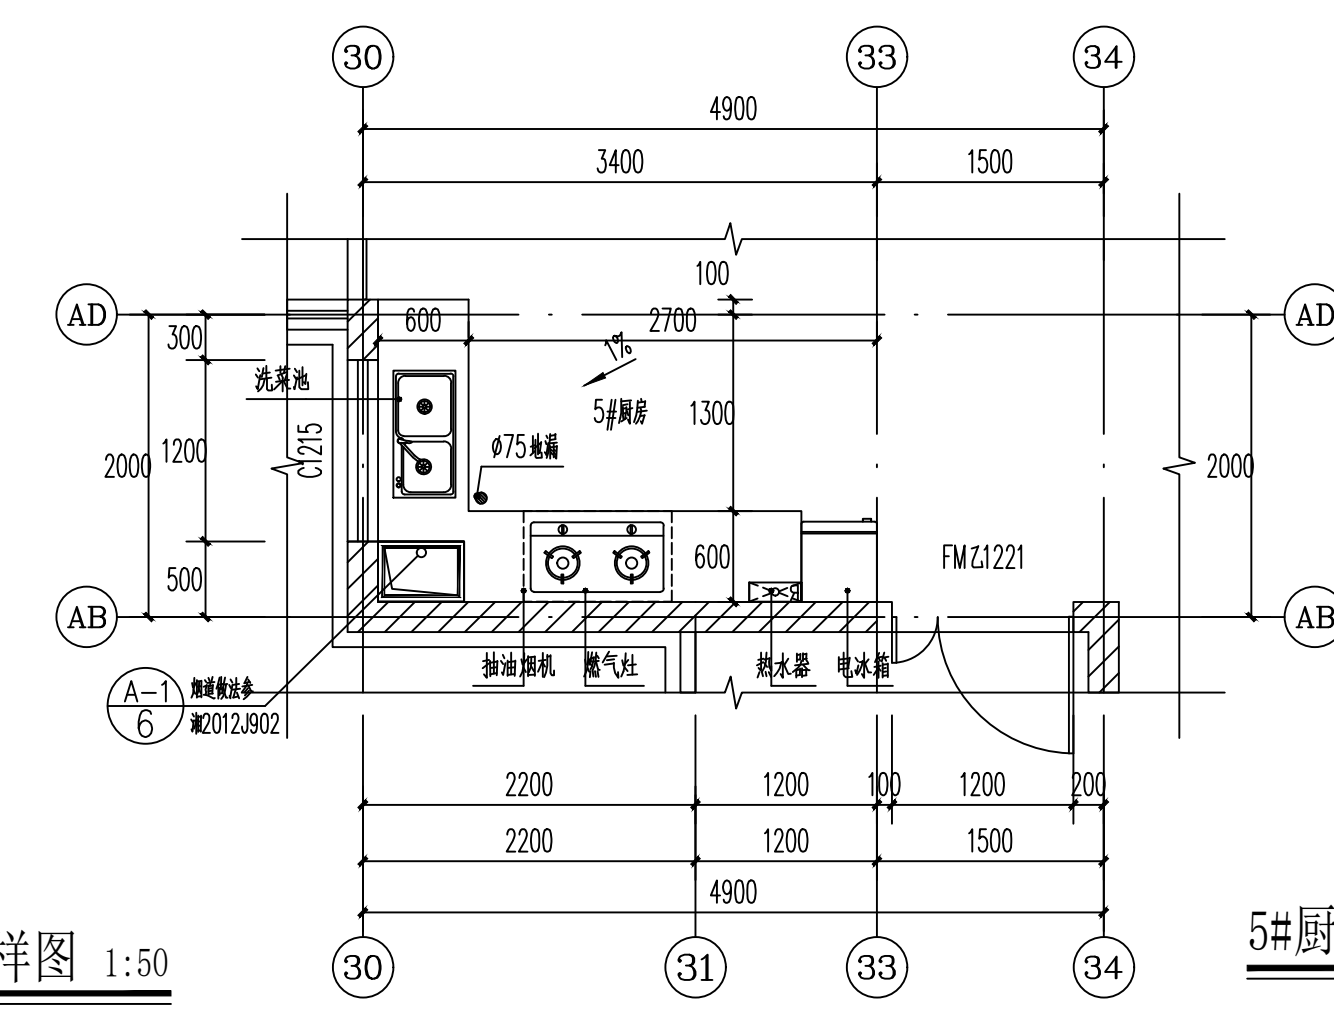

5#厨房大样图 1:50

建设单位/CLIENT:

麻阳苗族自治县远桥房地产开发有限公司

项目名称/PROJECT:

远程国际

子项目名称/SUB-PROJECT:

远程国际

区位图/REGIONAL LOCATION MAP :



图纸名称/TITLE:

LT3、LT4楼梯间大样图二  
厨房大样图

项目名称/PROJECT:

远程国际

|                        |     |  |
|------------------------|-----|--|
| 设计<br>DESIGNED         | 古新辉 |  |
| 校对<br>CHECKED          | 吴新红 |  |
| 专业负责人<br>CHIEF         | 吴志刚 |  |
| 项目负责人<br>PROJECT CHIEF | 吴志刚 |  |
| 审核<br>IDENTIFIED       | 黄展优 |  |
| 审定<br>APPROVED         | 李 坚 |  |

业务号/JOB NO.

设计阶段/STATUS: 施工图

专业/DISCIPLINE: 建筑

比例/  
SCALE: 1: 100

规格/  
SIZE: A1

出图日期/DATE: 2021.06

图号/DRAWING NO. JS-31

| 版次<br>NO. | 修改内容<br>DESCRIPTION | 日期<br>DATE |
|-----------|---------------------|------------|
|           |                     |            |
|           |                     |            |
|           |                     |            |

条形码/BARCODE:

版权所有，不得复制、套用。  
ALL RIGHTS RESERVED, DON'T COPIED, REPRODUCED.