


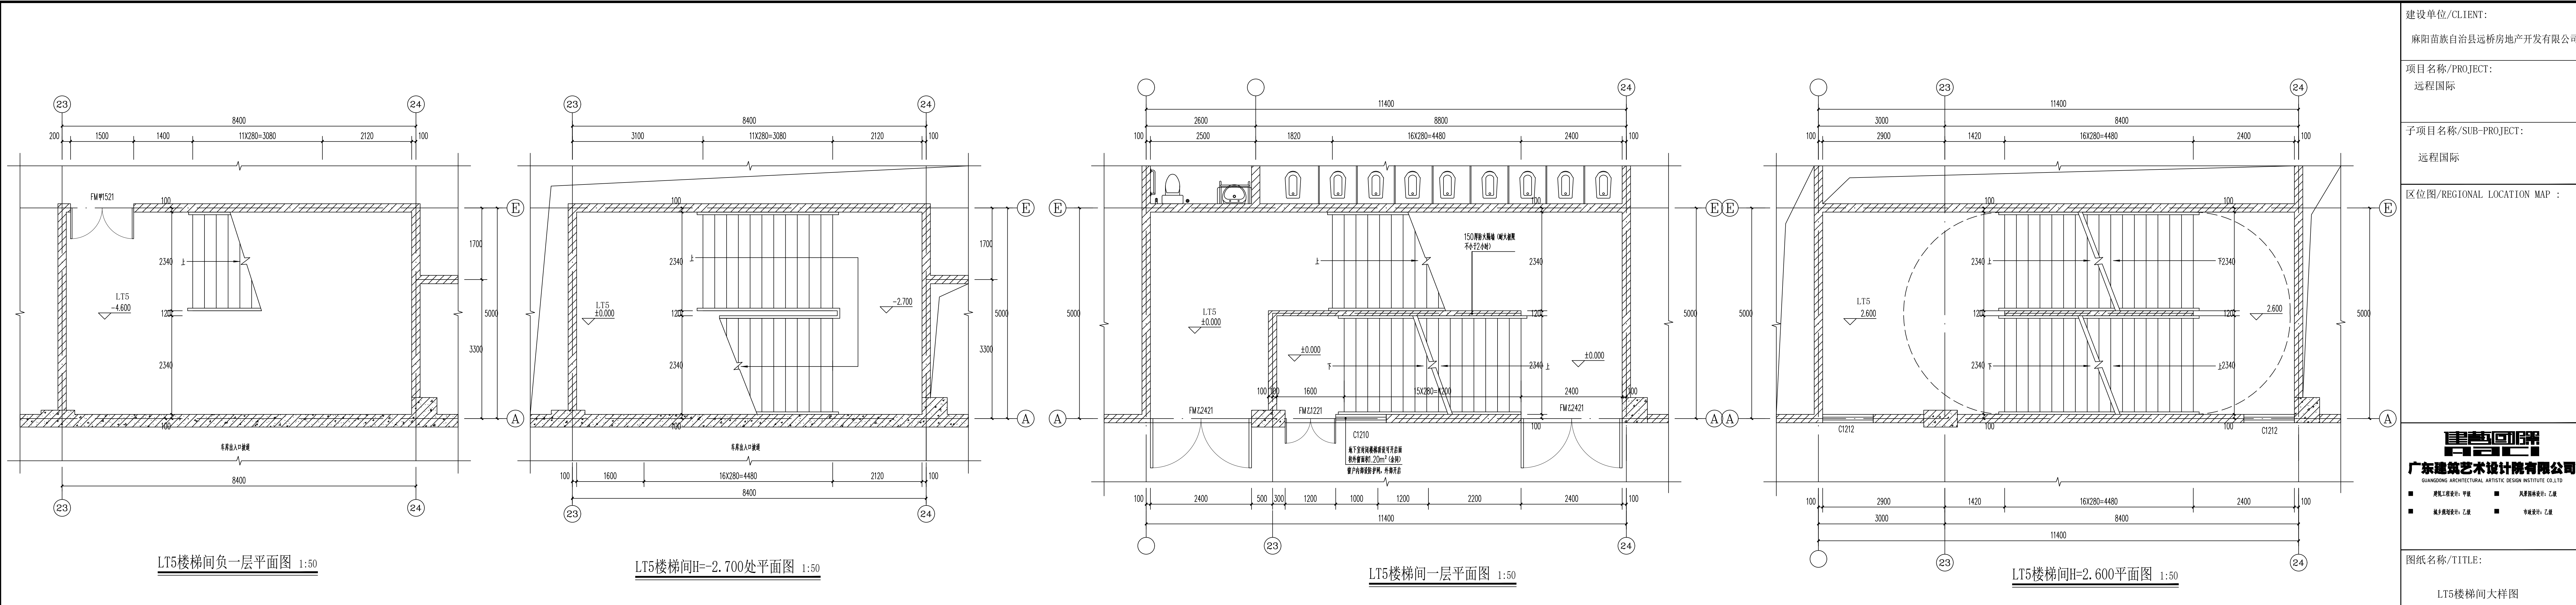

建设单位/CLIENT: 麻阳苗族自治县远桥房地产开发有限公司		
项目名称/PROJECT: 远程国际		
子项目名称/SUB-PROJECT: 远程国际		
区位图/REGIONAL LOCATION MAP :		
售楼部 广东建筑艺术设计院有限公司 GUANGDONG ARCHITECTURAL ARTISTIC DESIGN INSTITUTE CO.,LTD ■ 建筑方案设计: 甲级 ■ 风景园林设计: 乙级 ■ 城乡规划设计: 乙级 ■ 市政工程设计: 乙级		
图纸名称/TITLE: LT5楼梯间大样图		
项目名称/PROJECT: 远程国际		
设计 DESIGNED	古新辉	
校对 CHECKED	吴新红	
专业负责人 CHIEF	吴志刚	
项目负责人 PROJECT CHIEF	吴志刚	
审核 IDENTIFIED	黄展优	
审定 APPROVED	李 坚	
业务号/JOB NO.		
设计阶段/STATUS: 施工图		
专业/DISCIPLINE: 建施		
比例/ SCALE:	1: 100	规格/ SIZE: A1
出图日期/DATE: 2021. 06		
图号/DRAWING NO. JS-32		
版次 NO.	修改内容 DESCRIPTION	日期 DATE
条形码/BARCODE:		
版权所有，不得复制、套用。 ALL RIGHTS RESERVED, DON'T COPIED, REPRODUCED.		

