




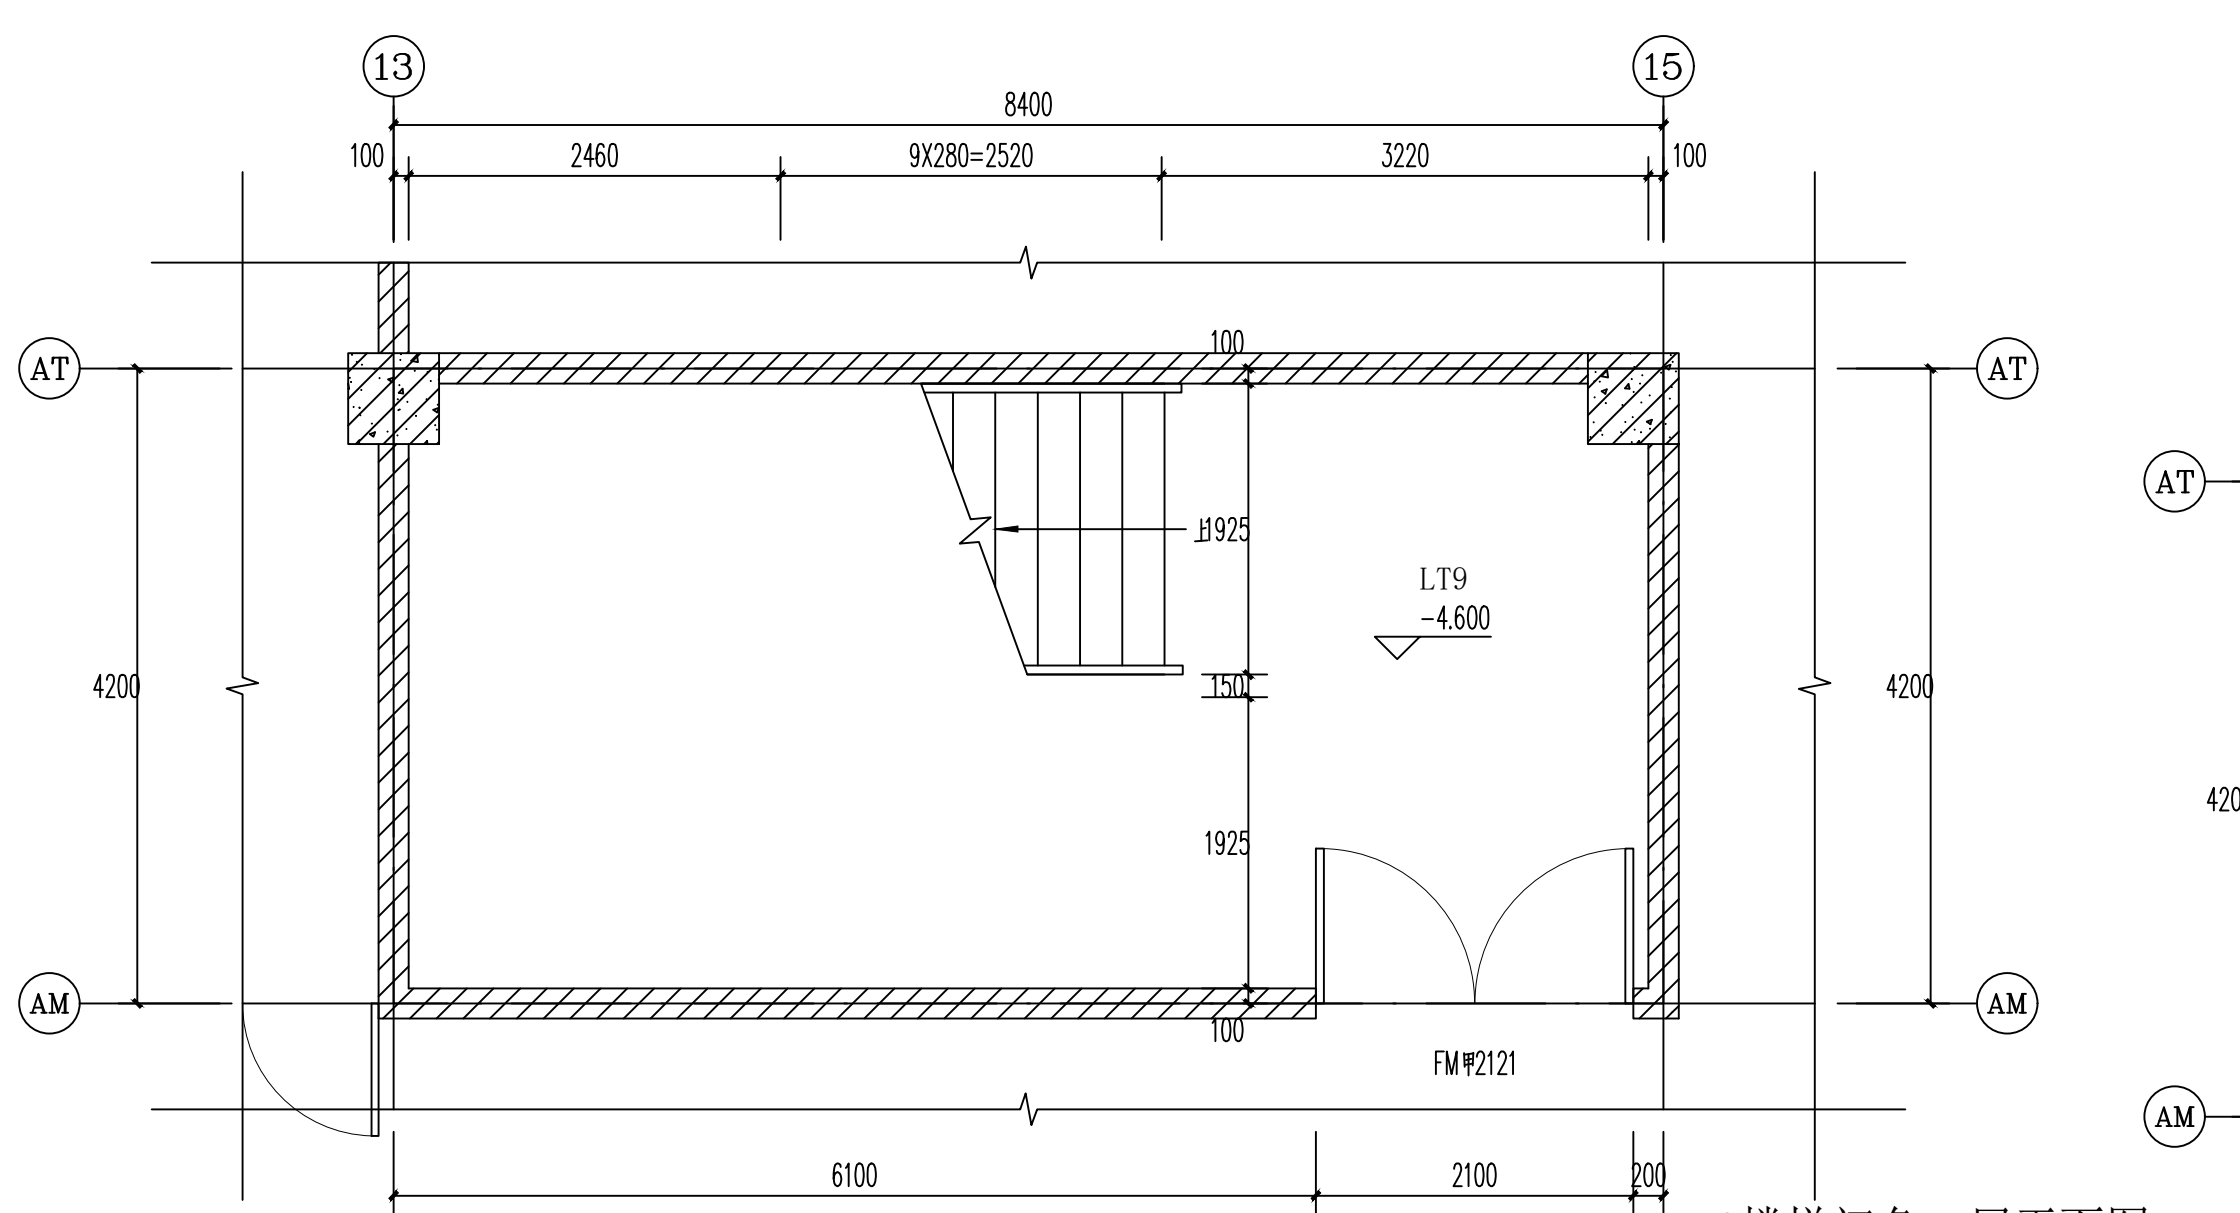


LT9楼梯间负一层平面图 1:50

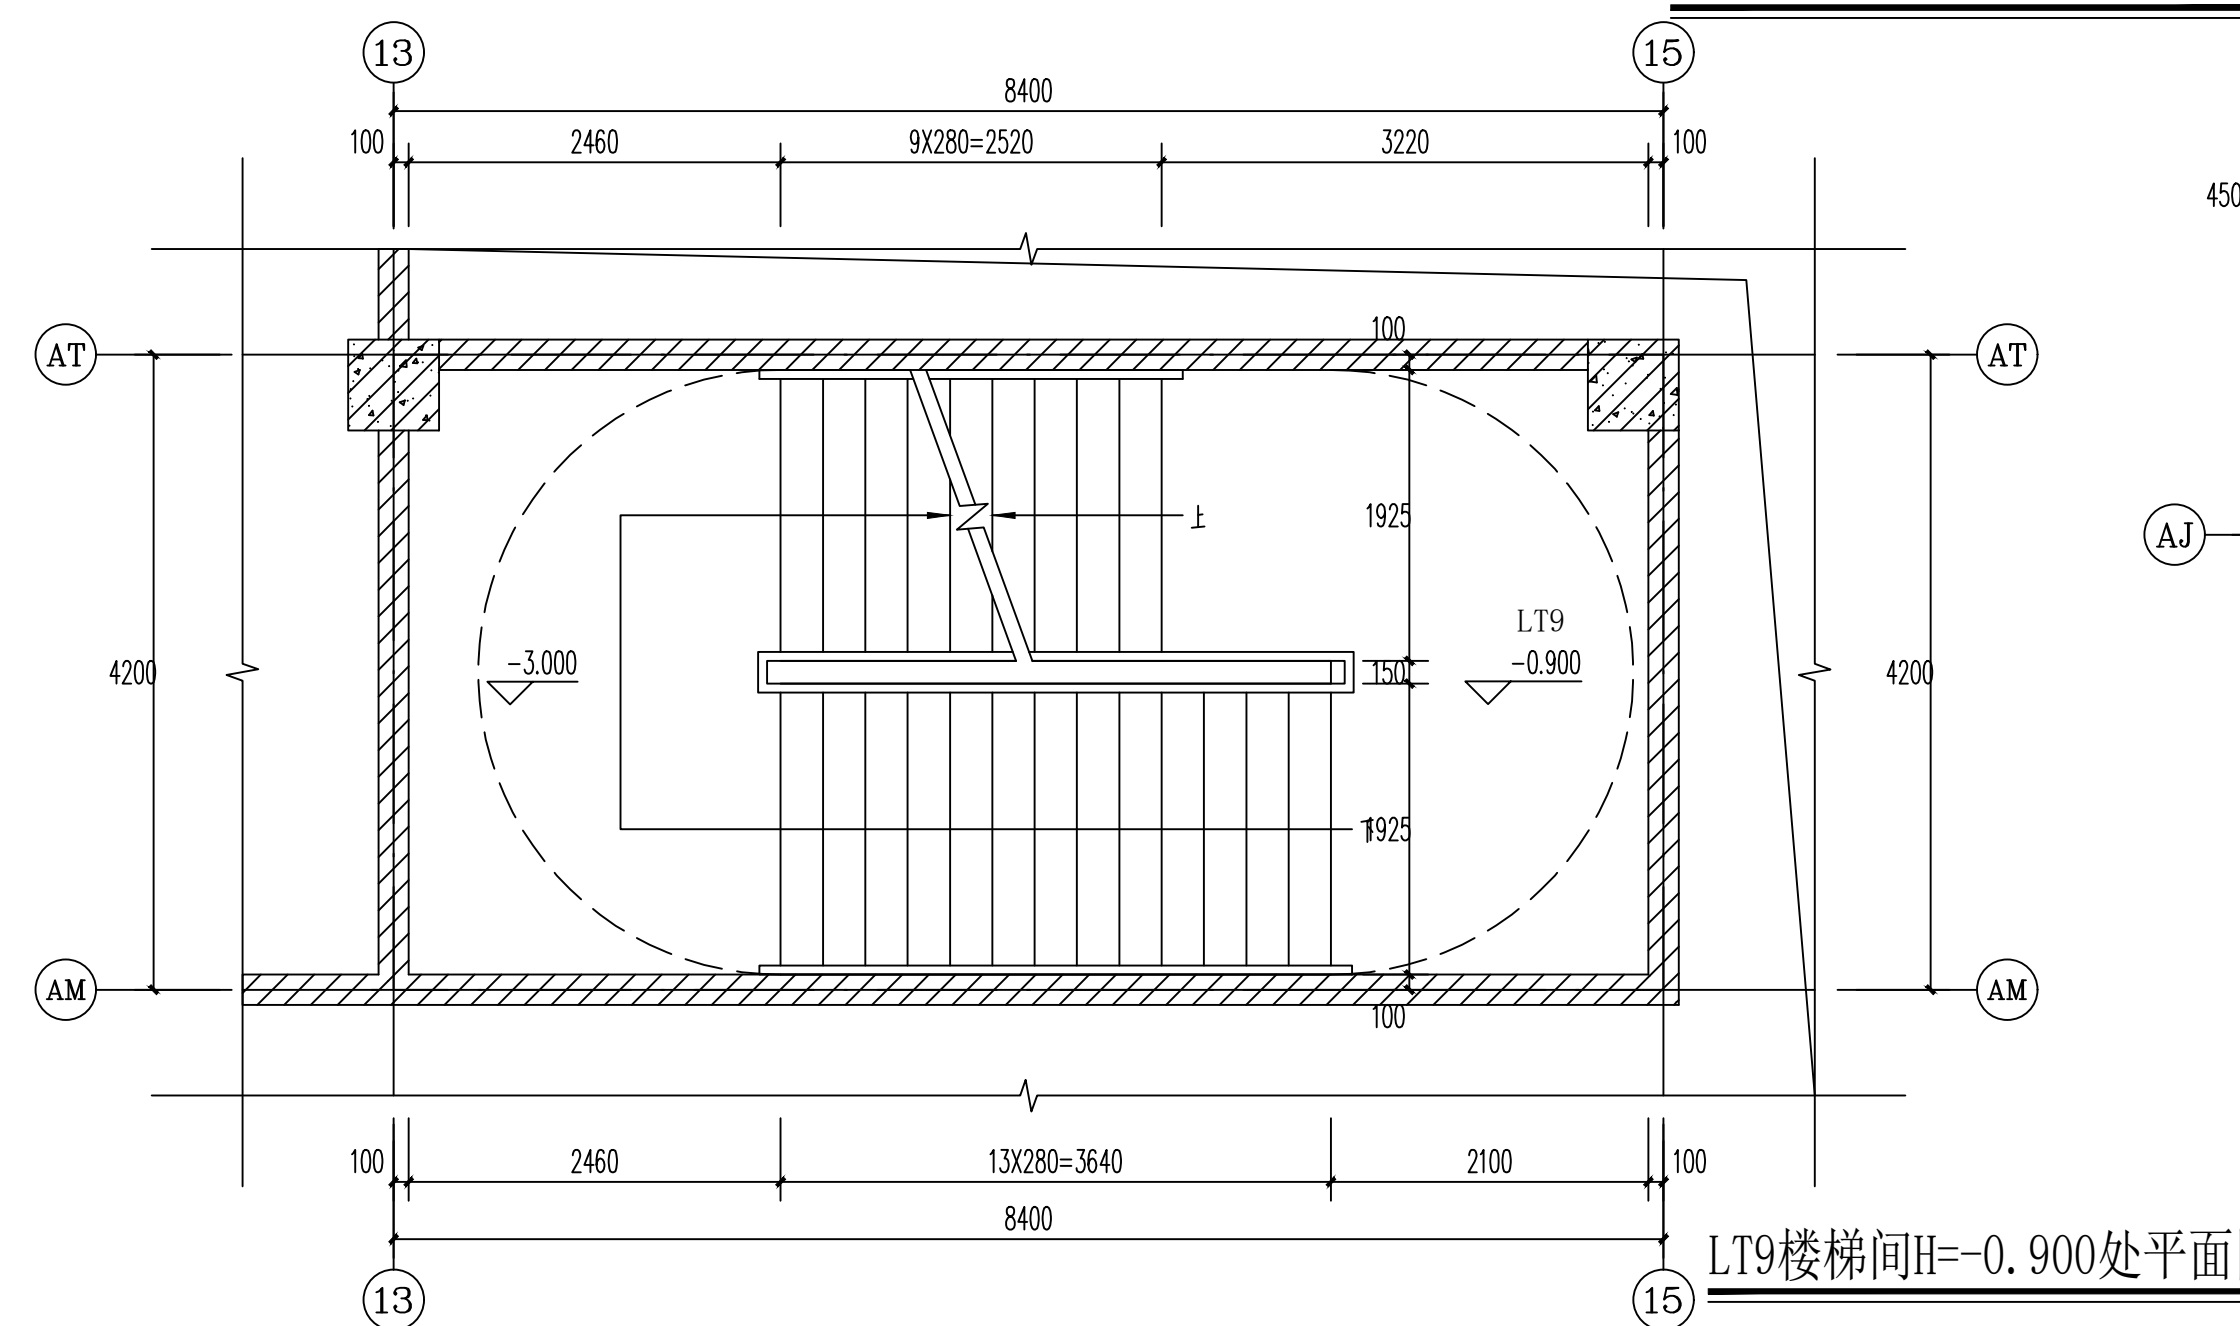


LT9楼梯间H=-0.900处平面图 1:50

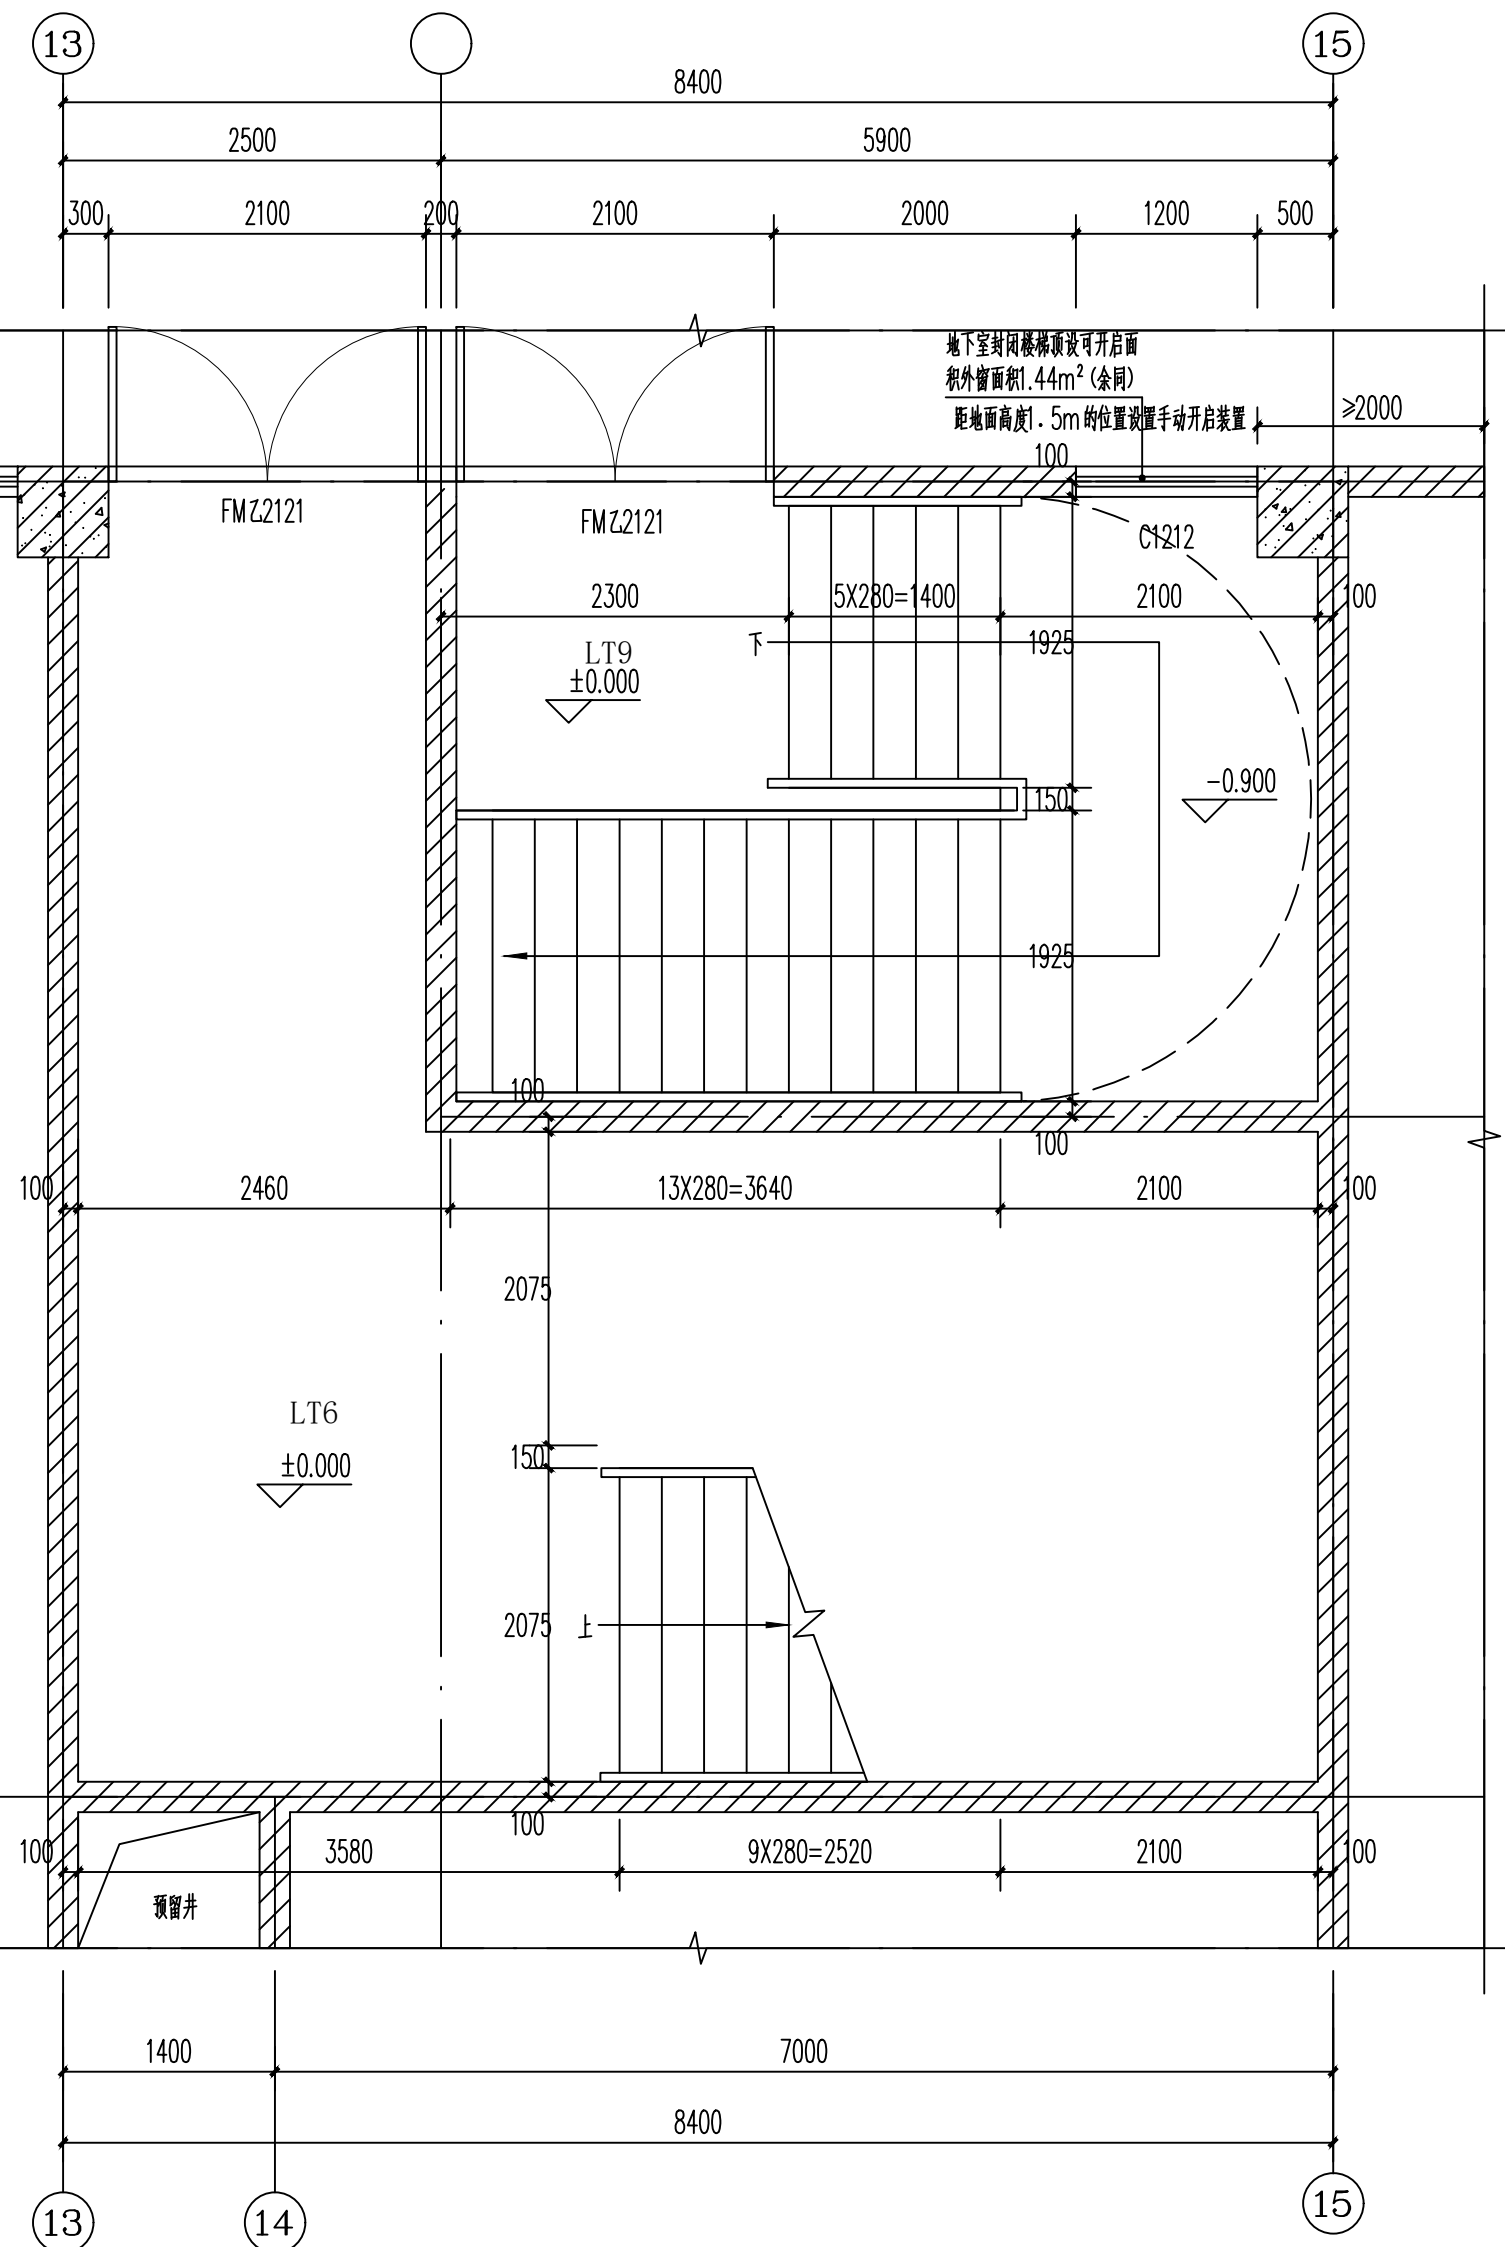


LT6、LT9楼梯间一层平面图 1:50

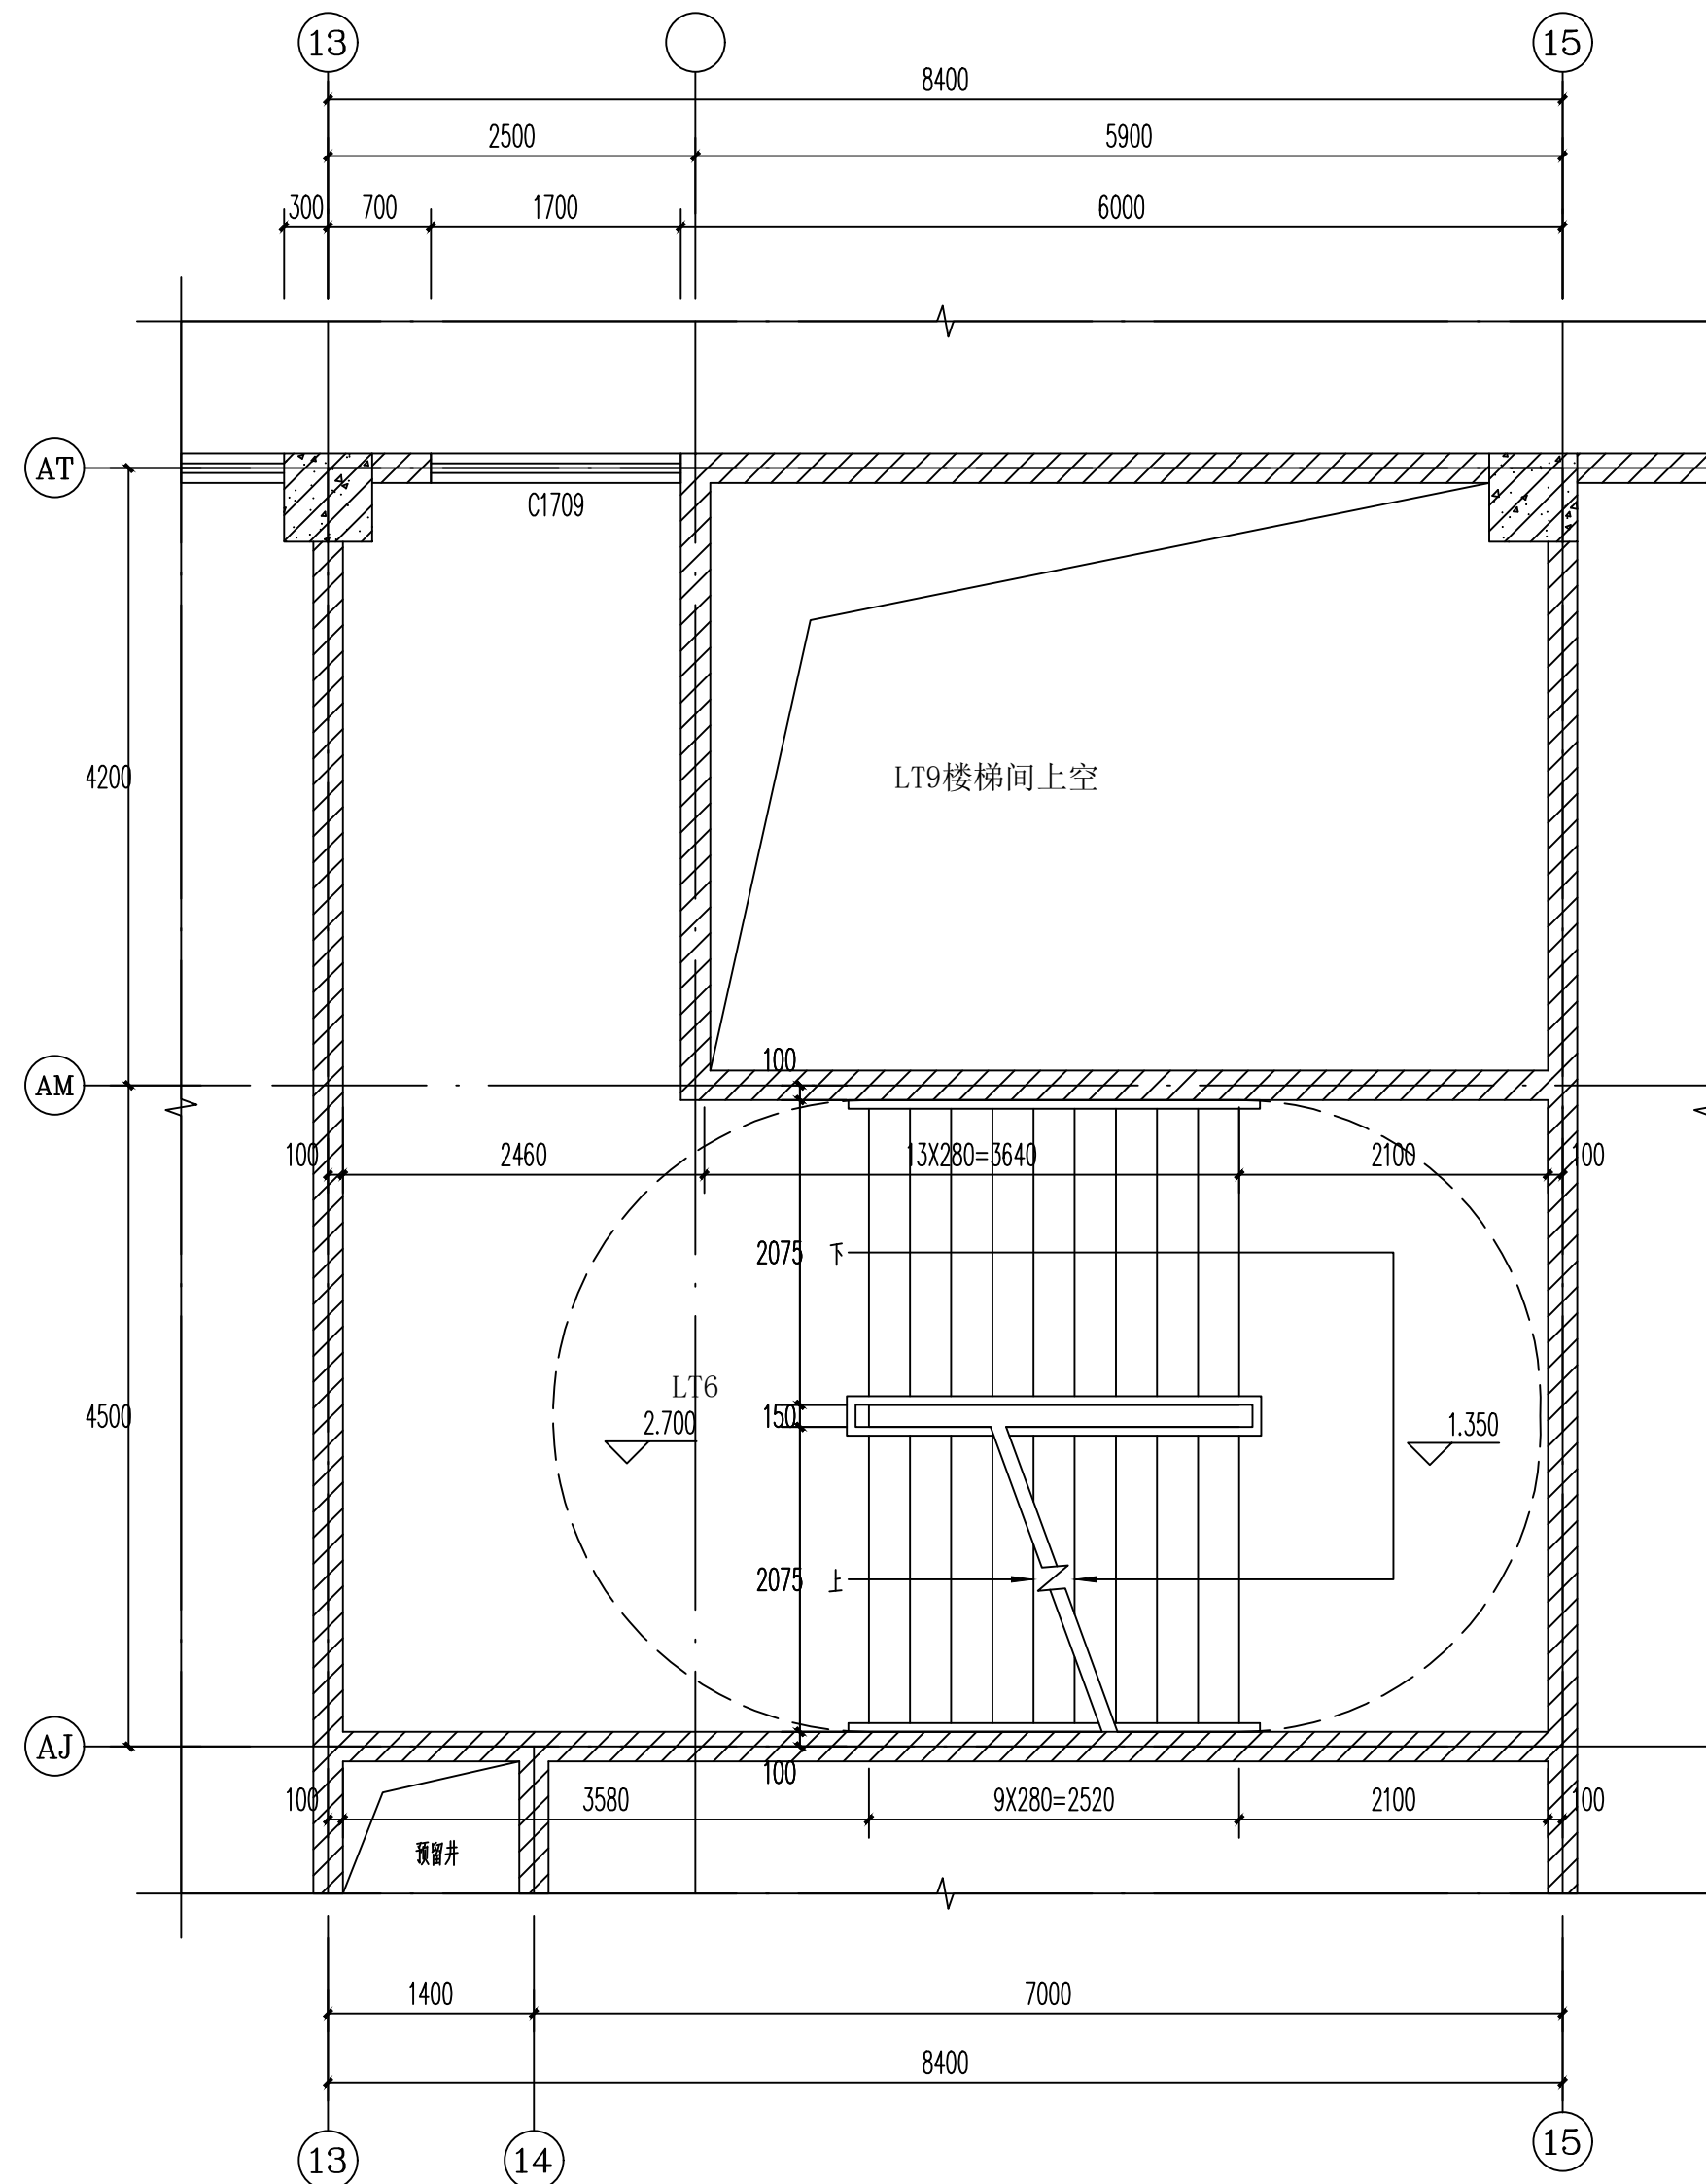


LT6楼梯间H=2.700处平面图 1:50

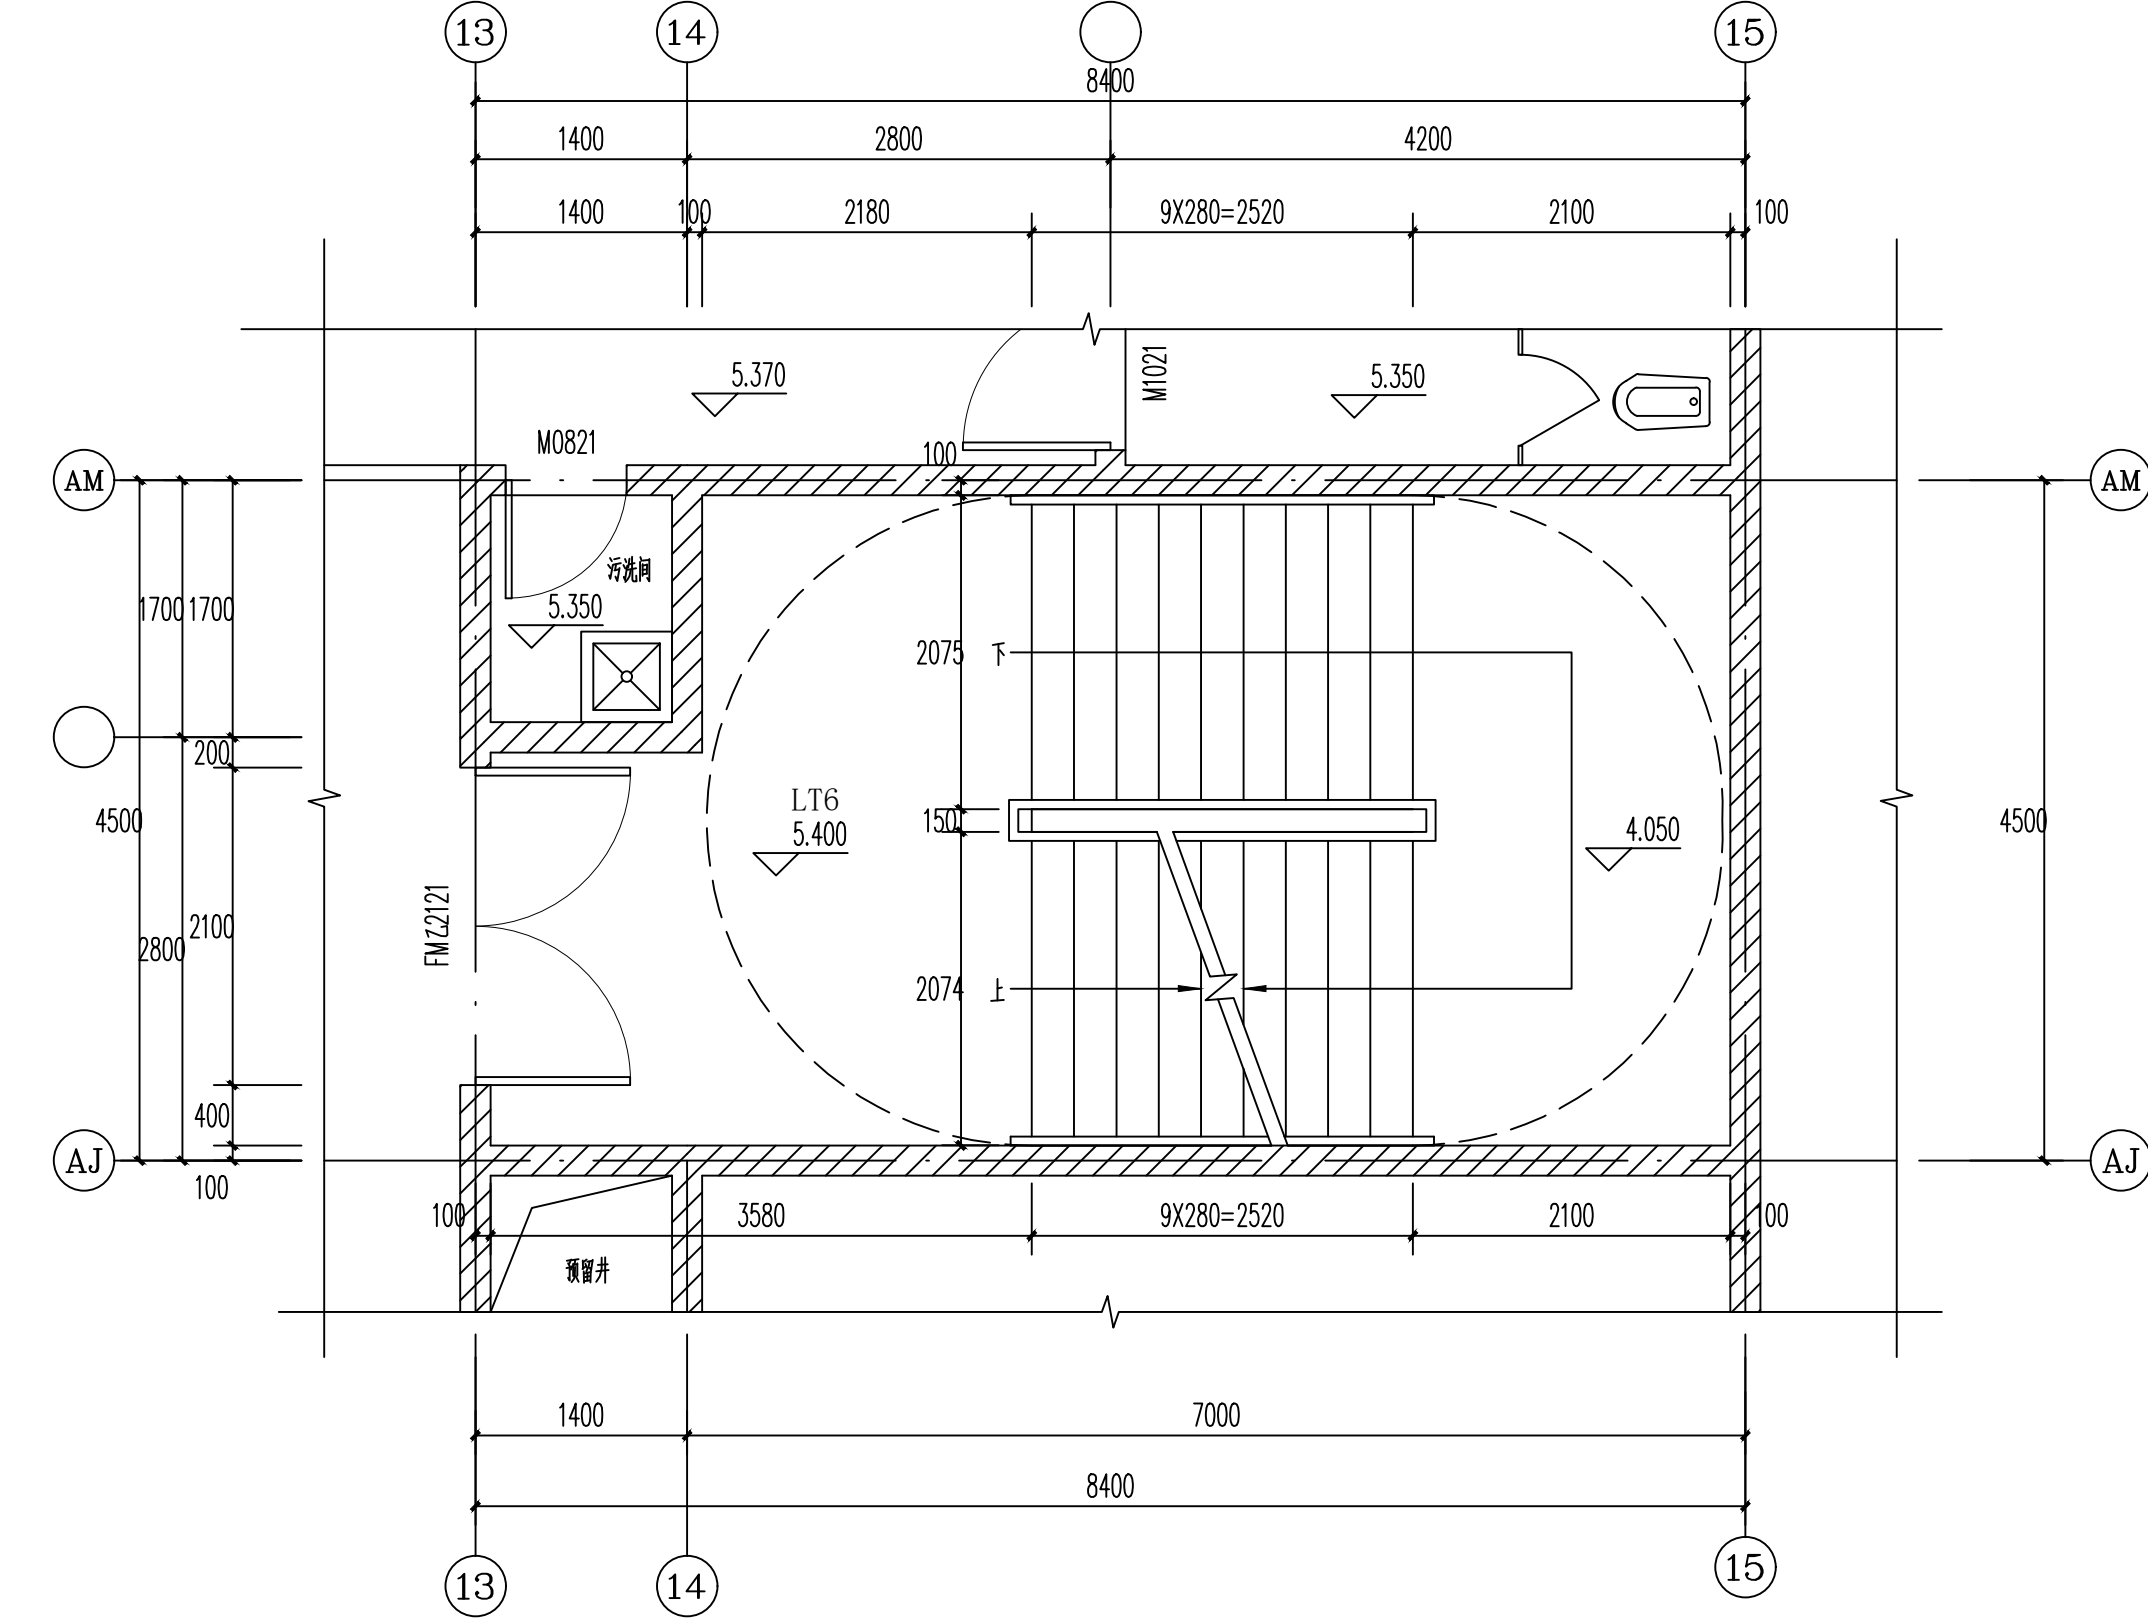


LT6楼梯间二层平面图 1:50

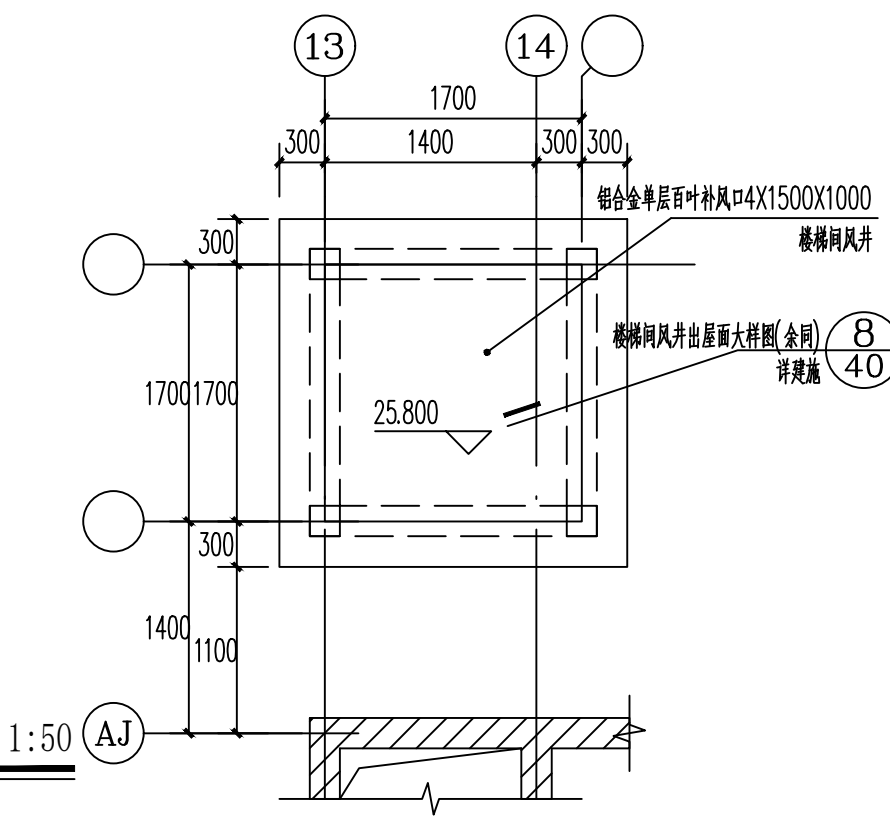


LT6楼梯间屋顶风井平面图 1:50

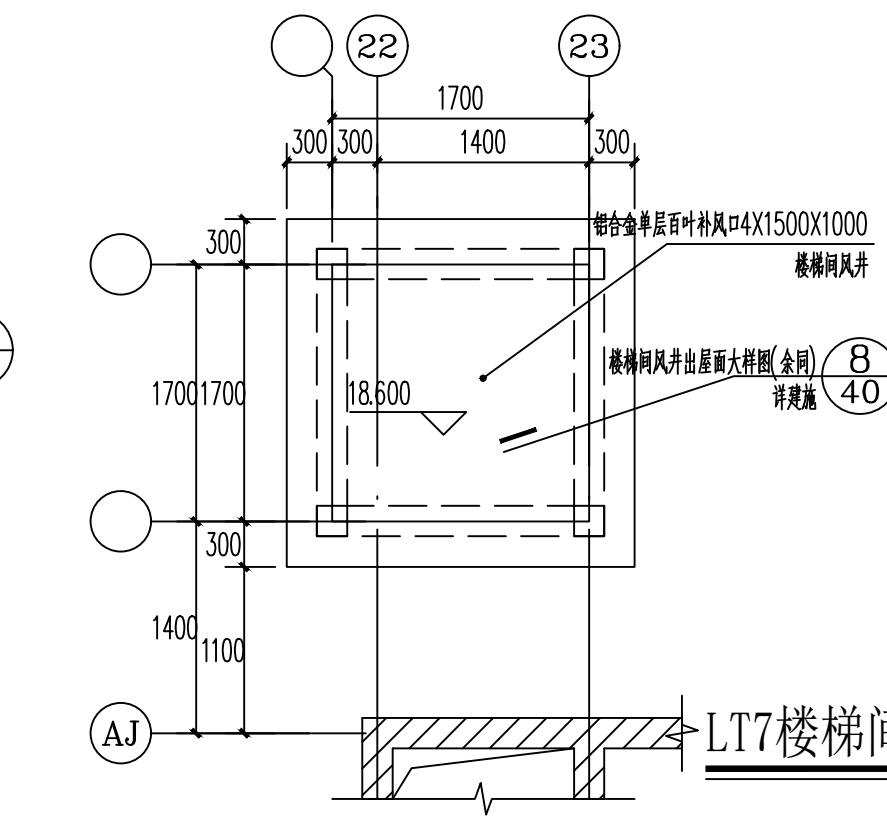


LT7楼梯间屋顶风井平面图 1:50

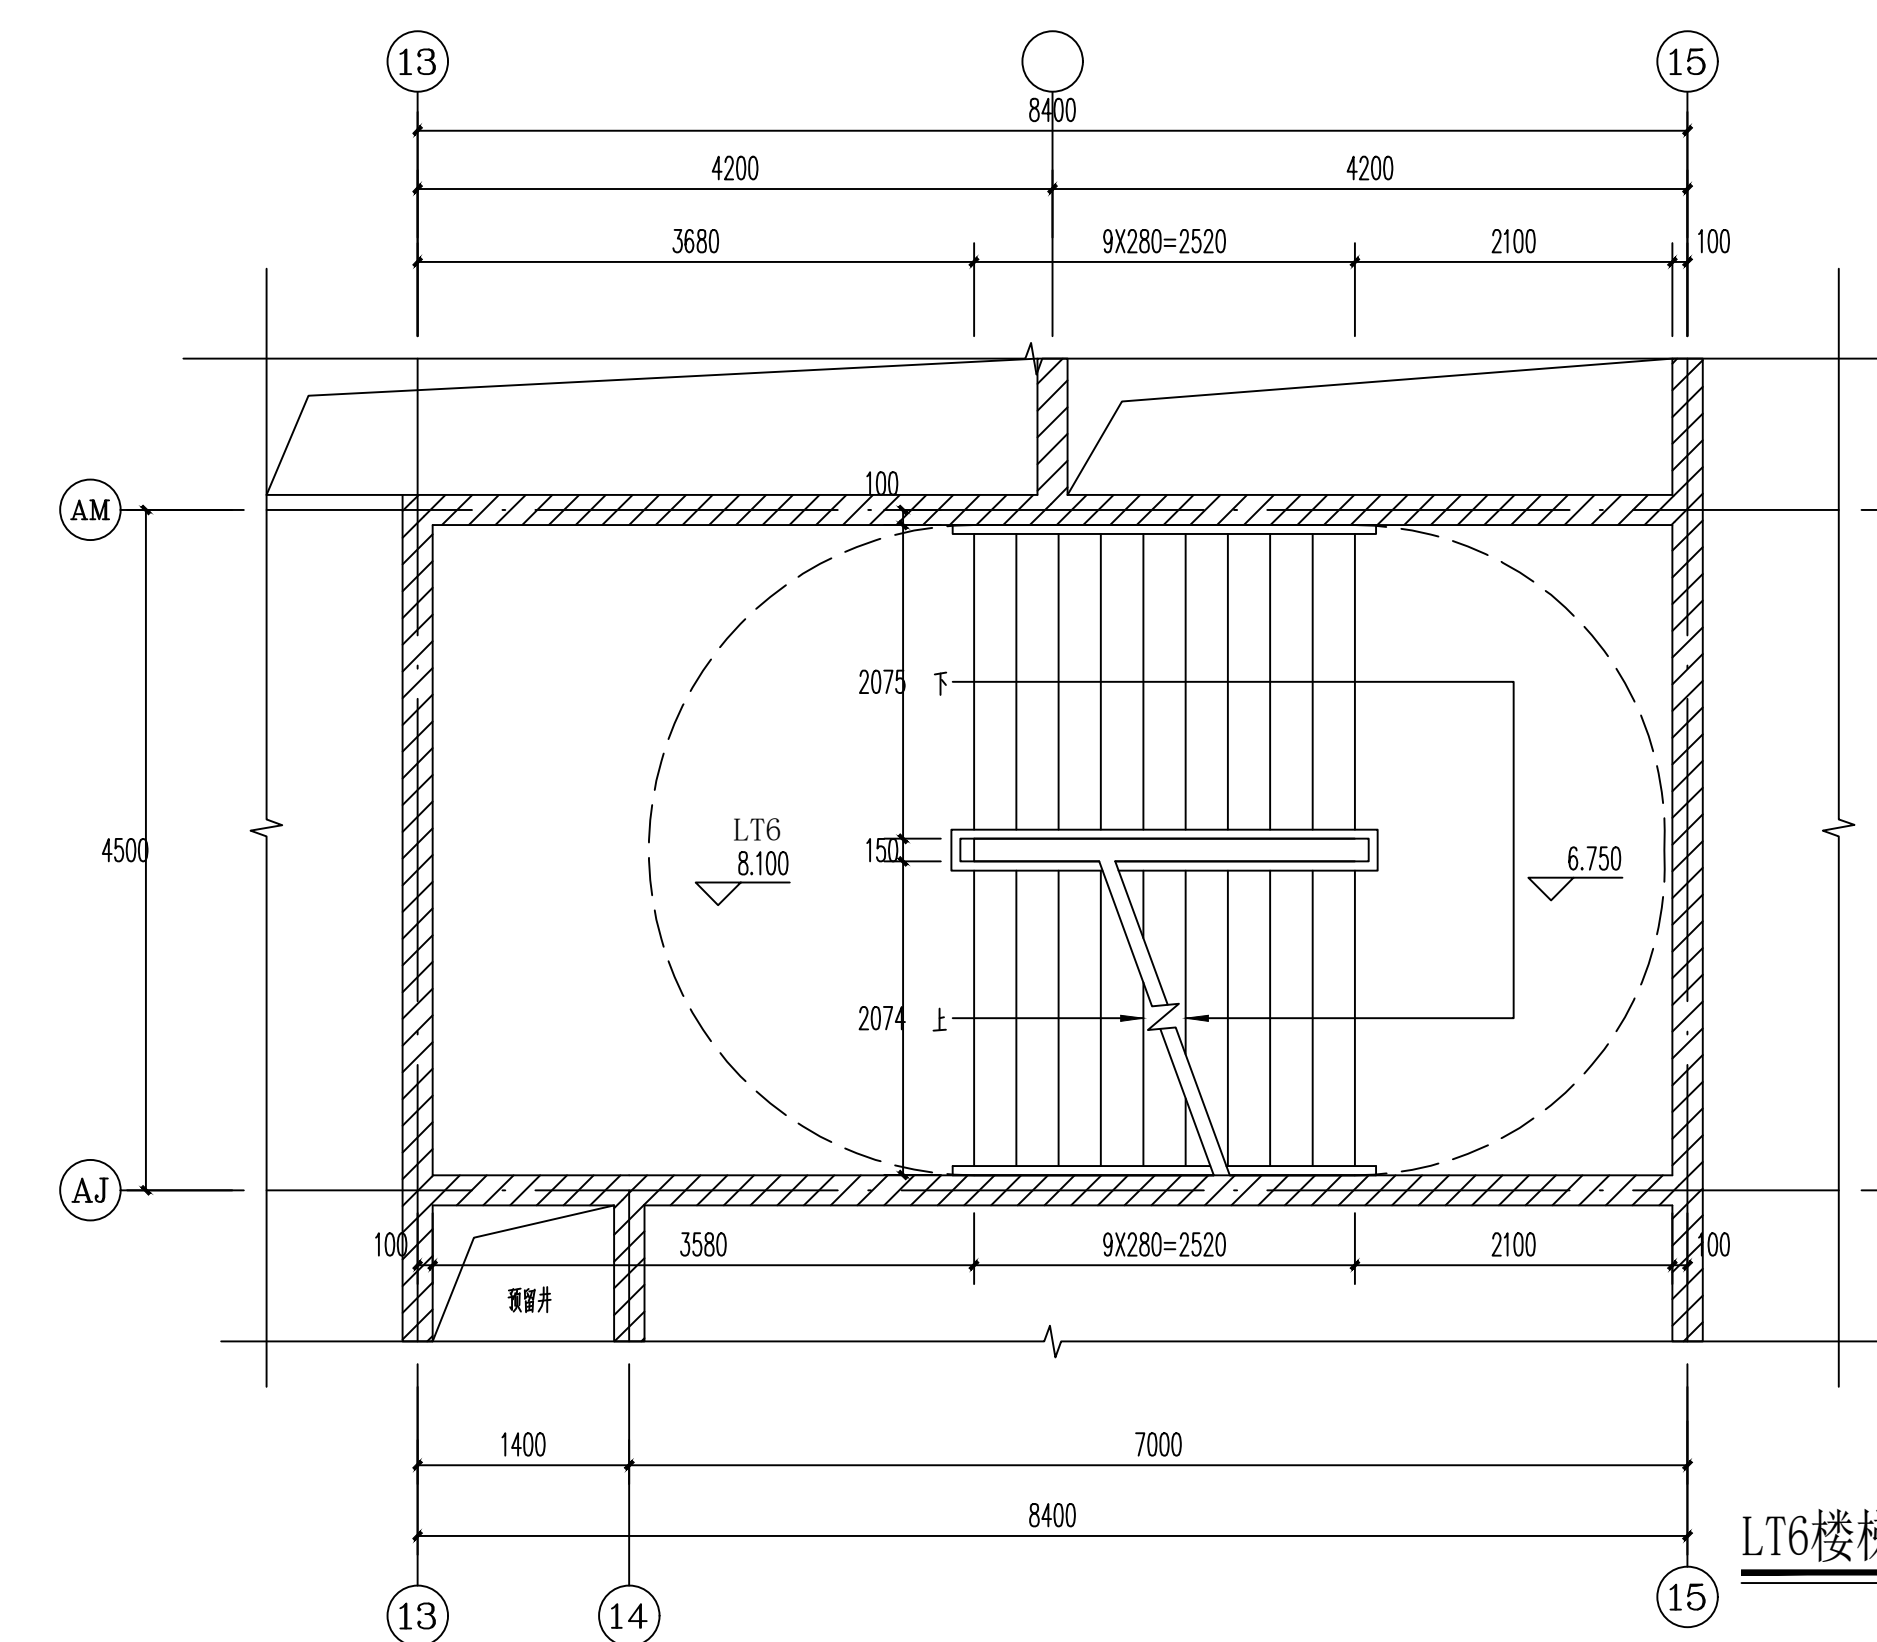


LT6楼梯间H=8.100处平面图 1:50

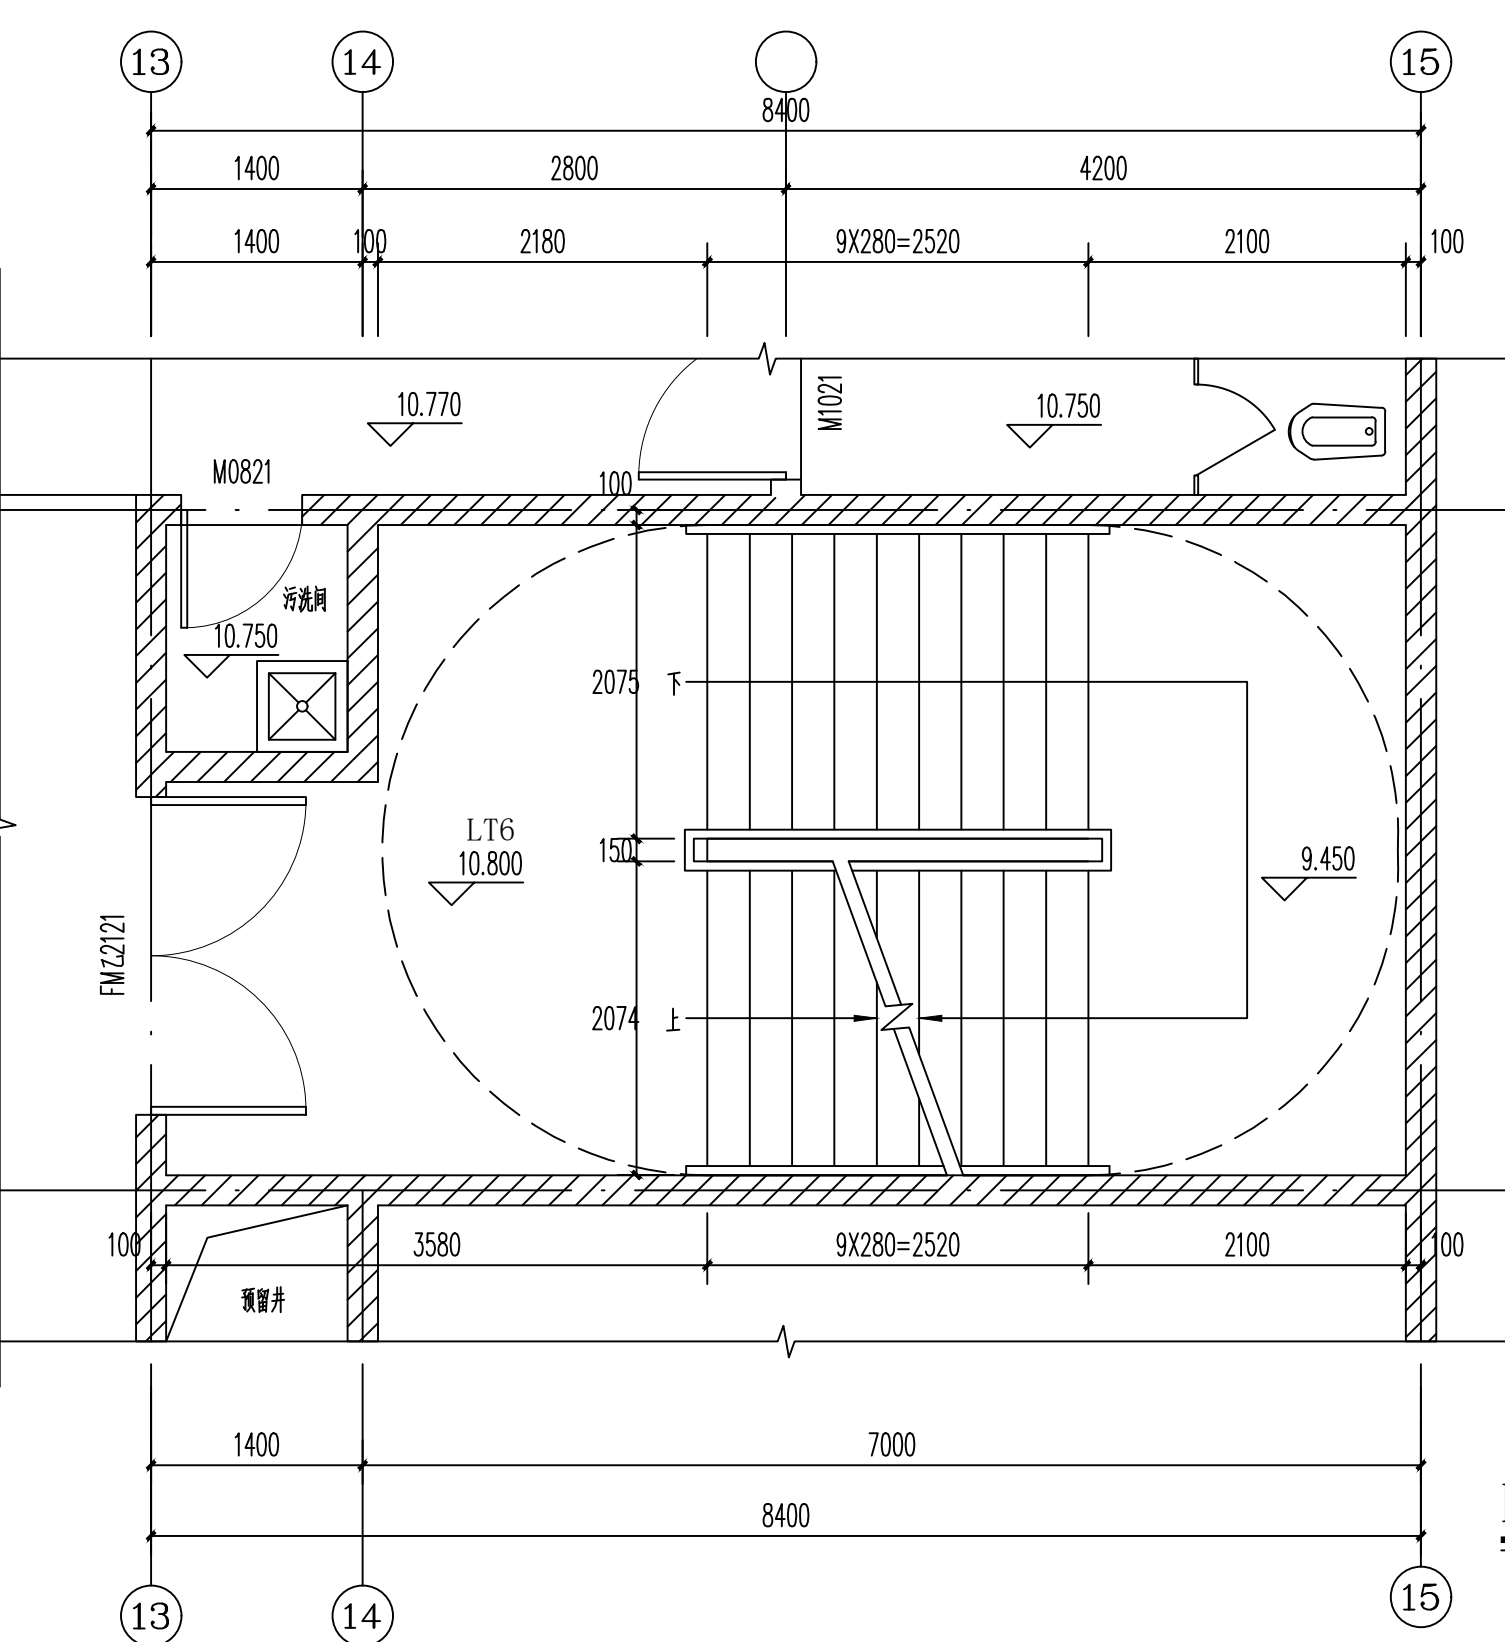

LT6楼梯间三层平面图 1:50

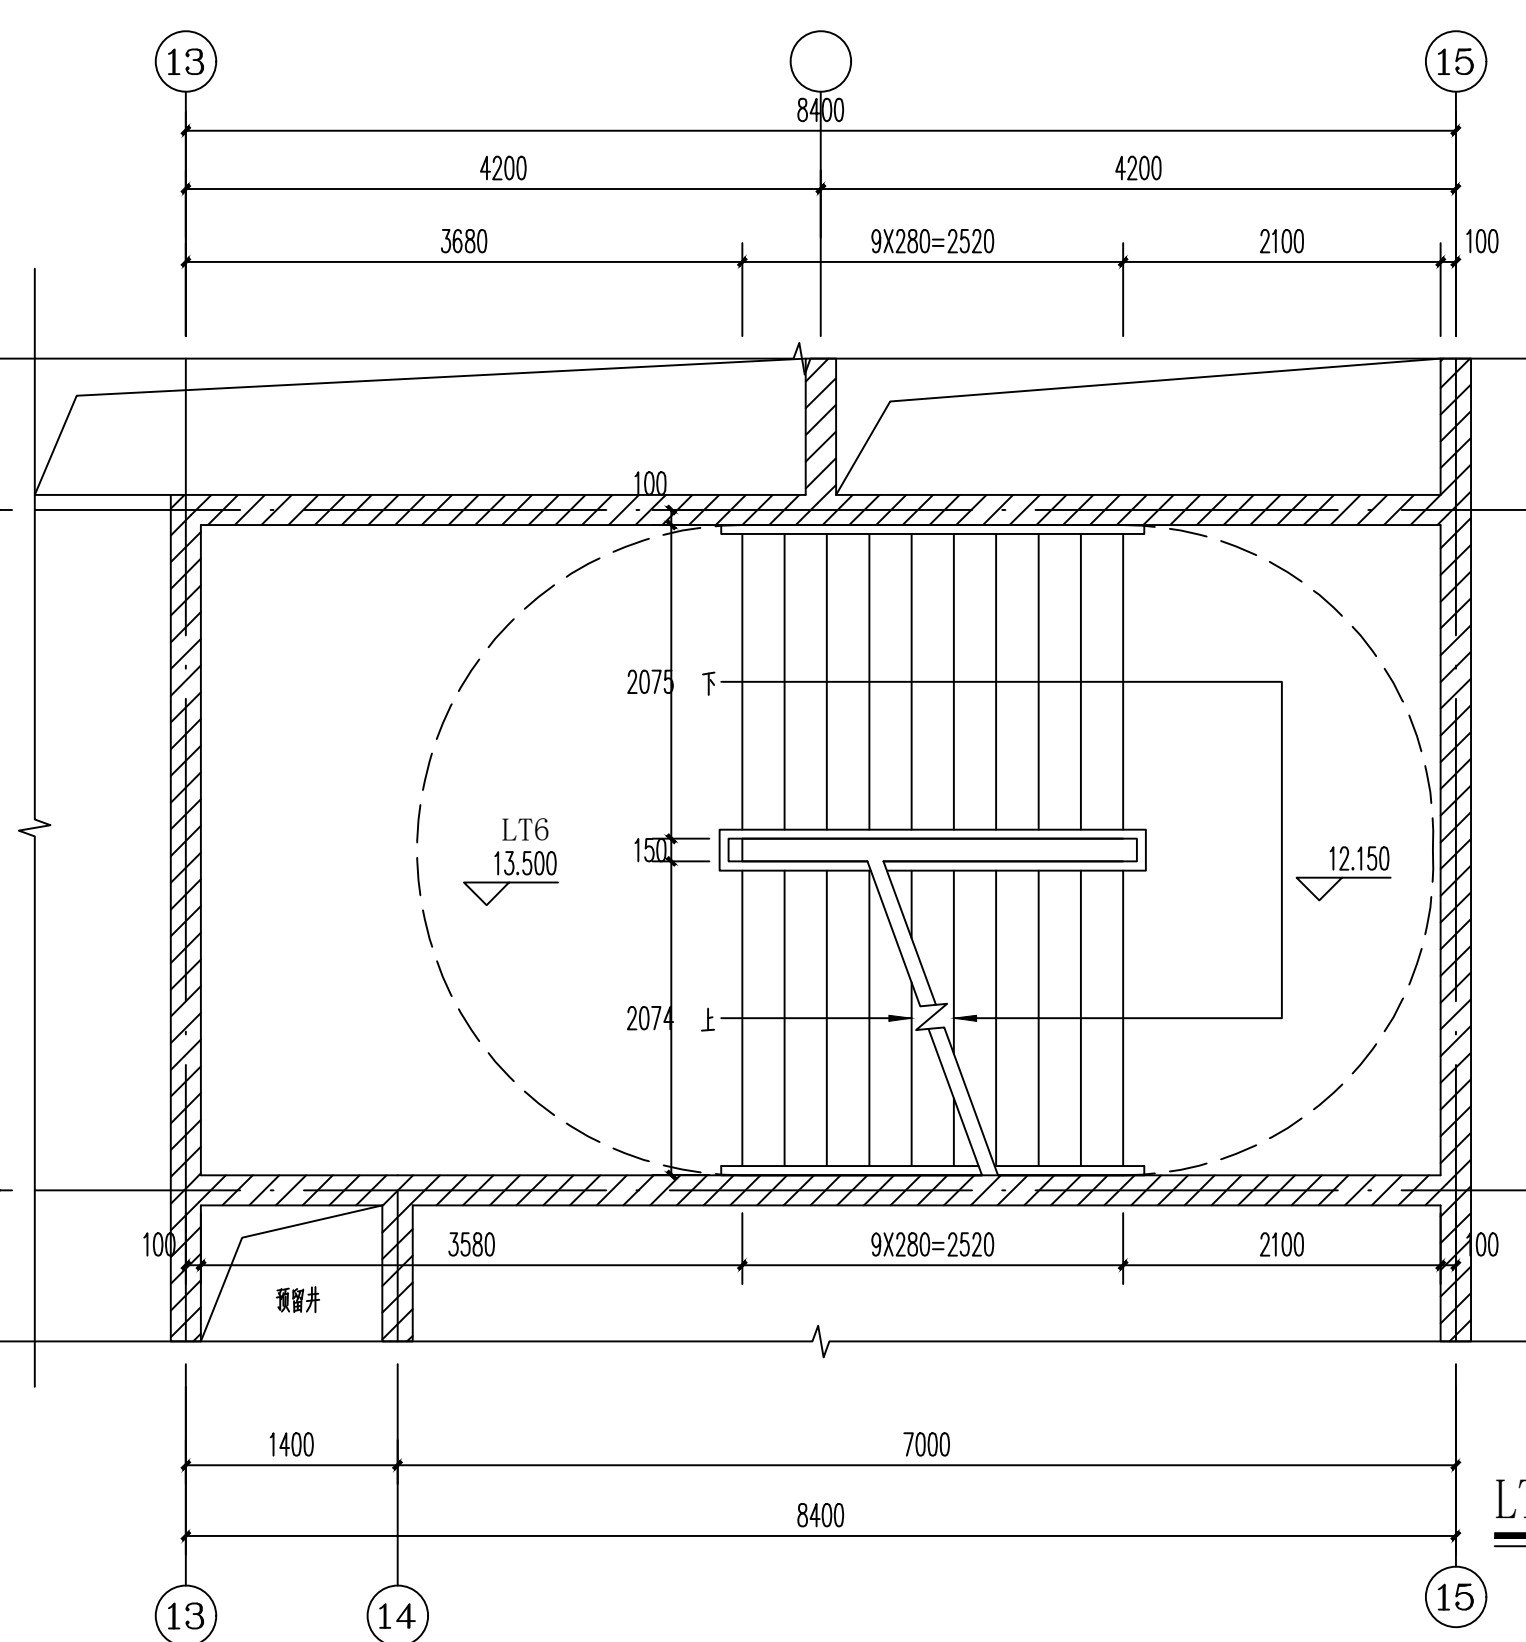

LT6楼梯间H=13.500处平面图 1:50

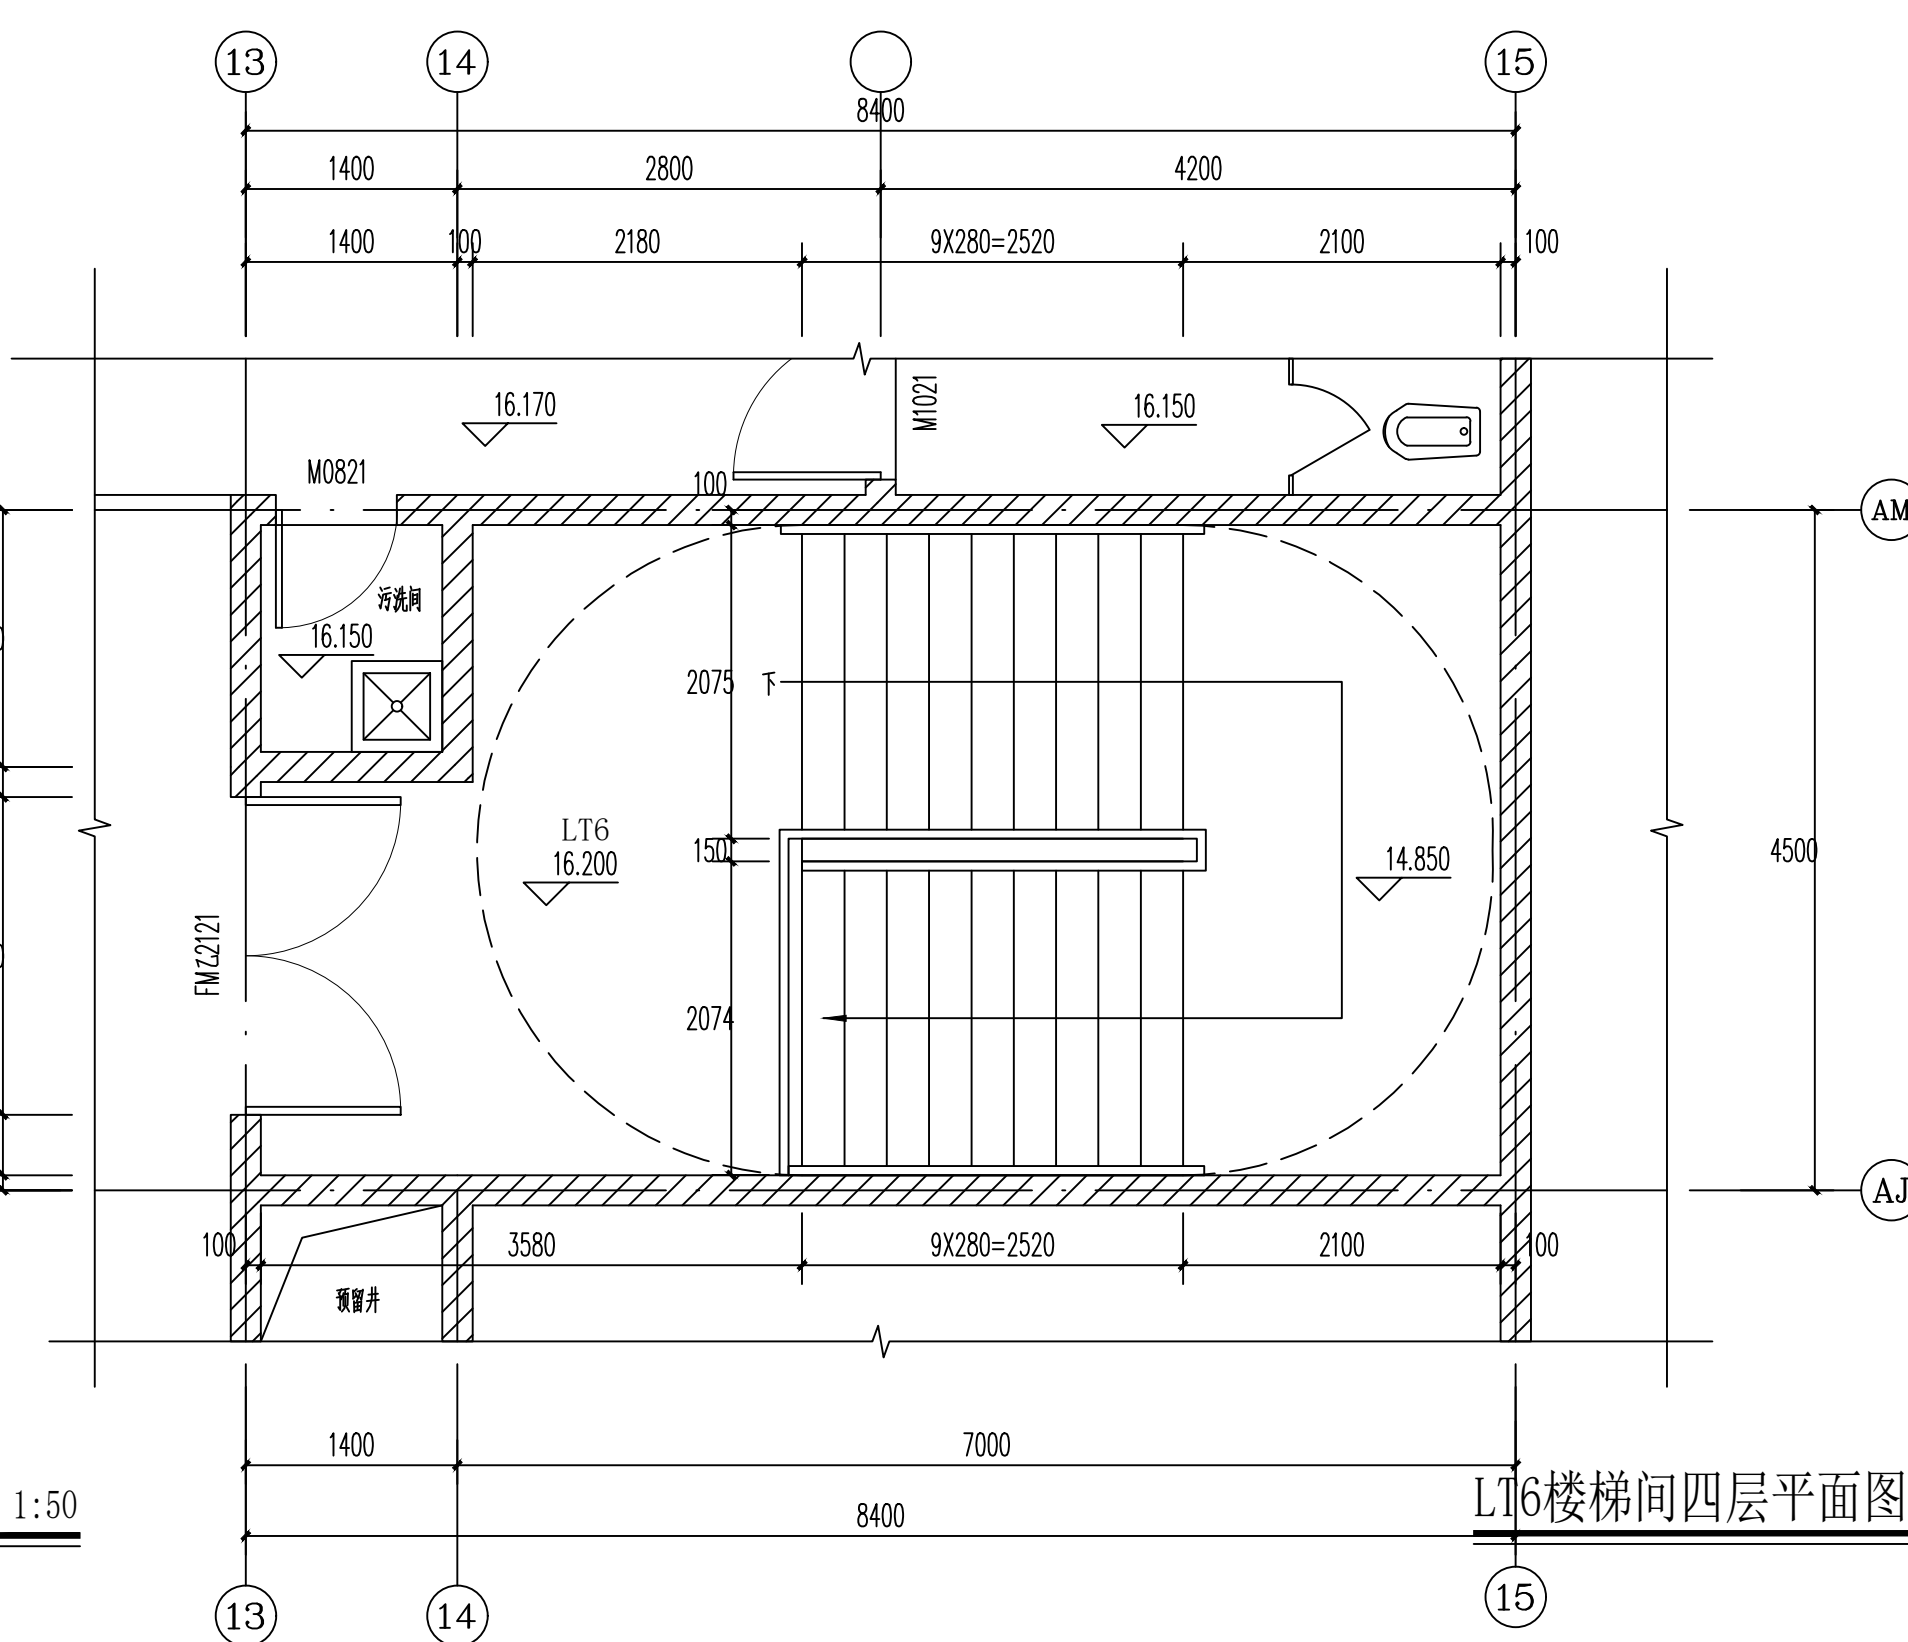

LT6楼梯间四层平面图 1:50

建设单位/CLIENT:

麻阳苗族自治县远桥房地产开发有限公司

项目名称/PROJECT:

远程国际

子项目名称/SUB-PROJECT:

远程国际

区位图/REGIONAL LOCATION MAP :

<