

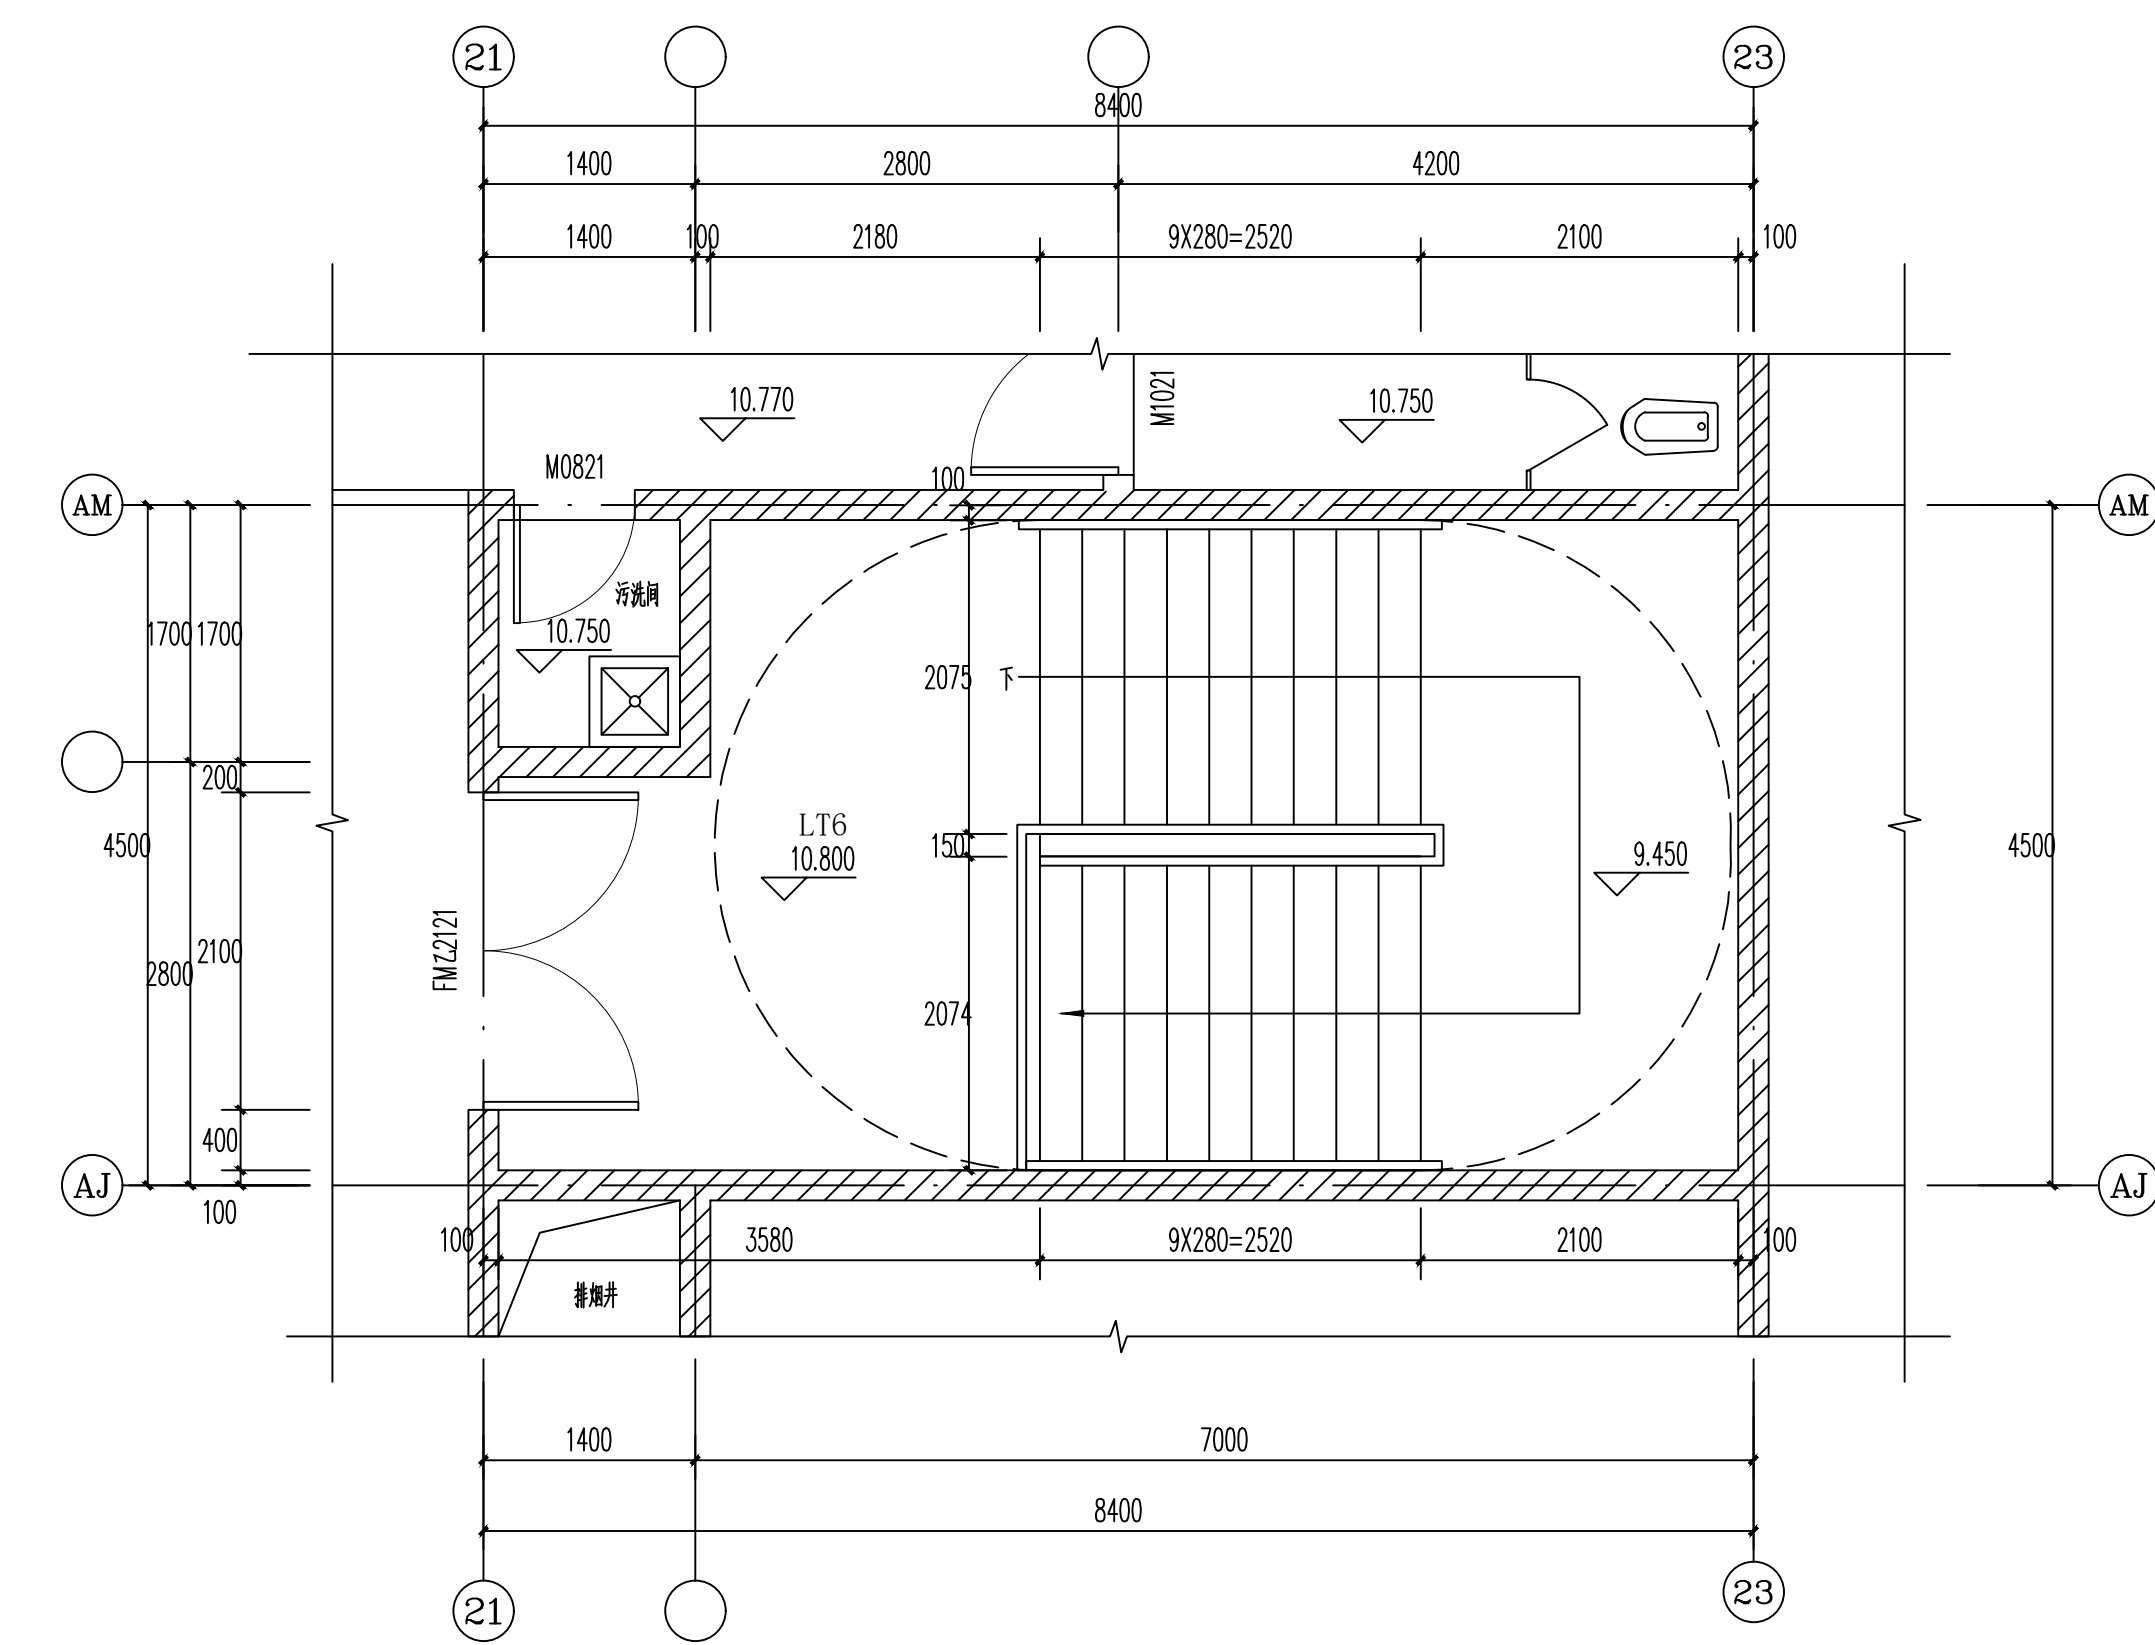
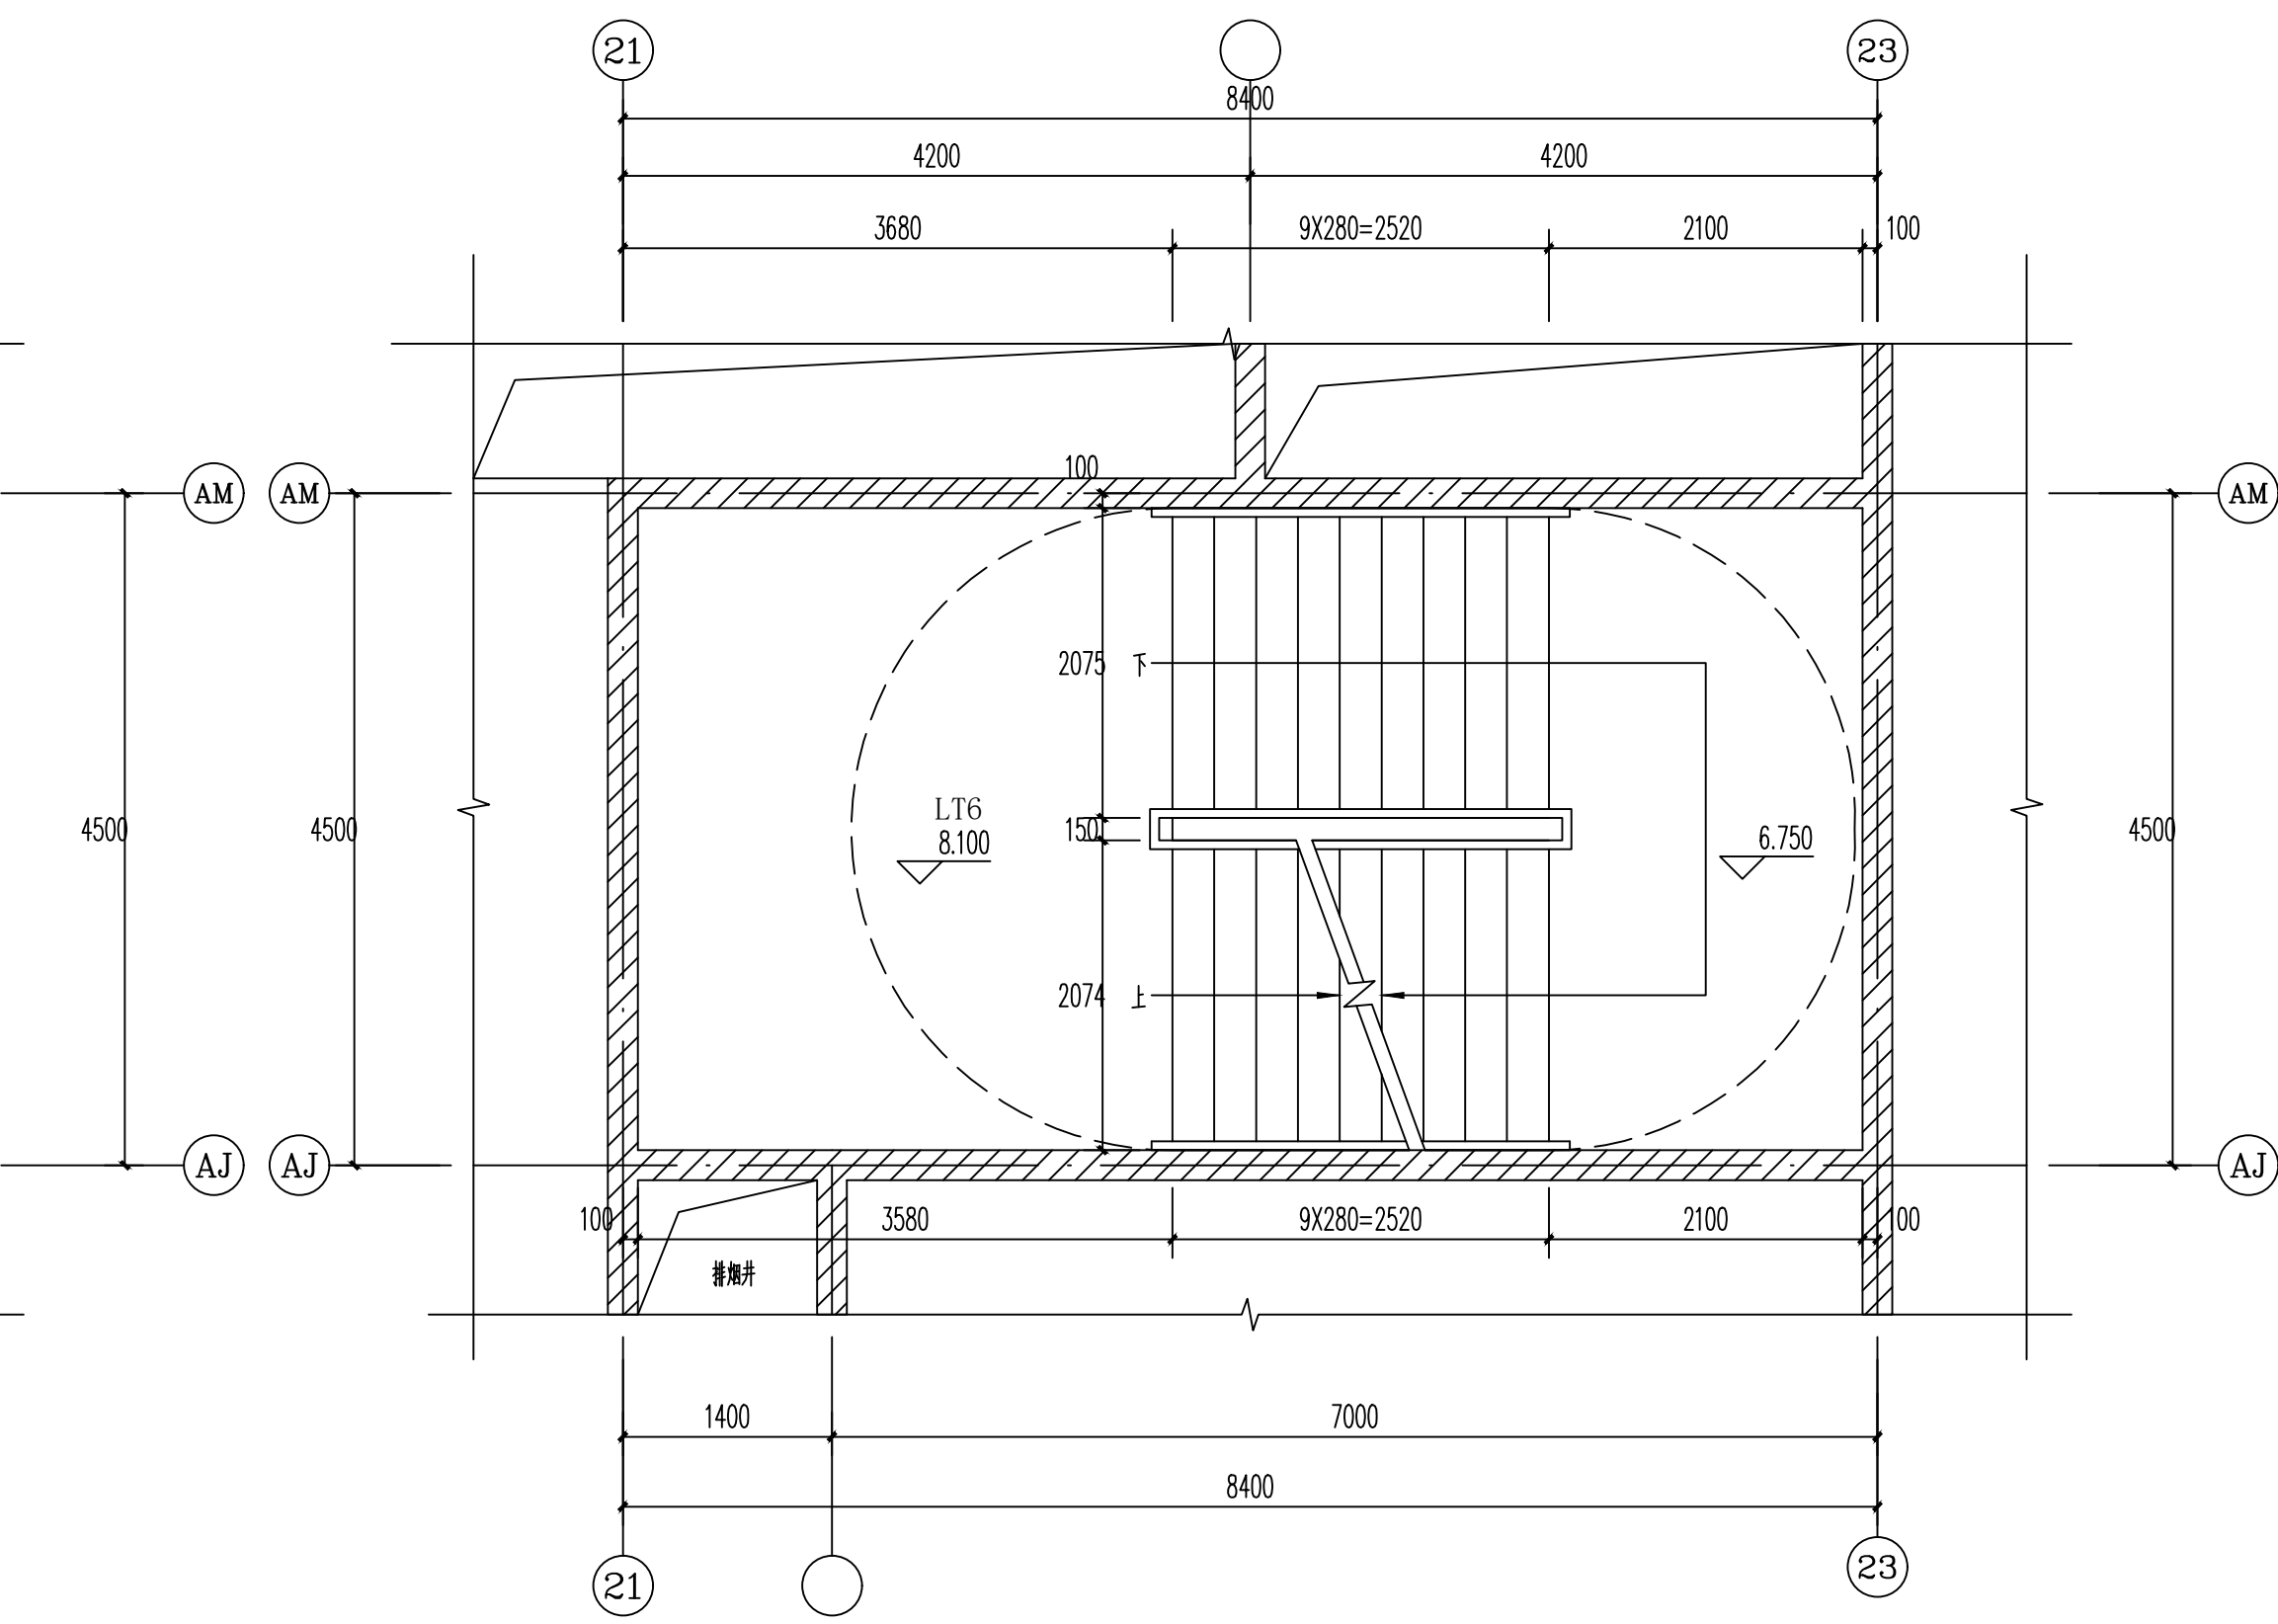
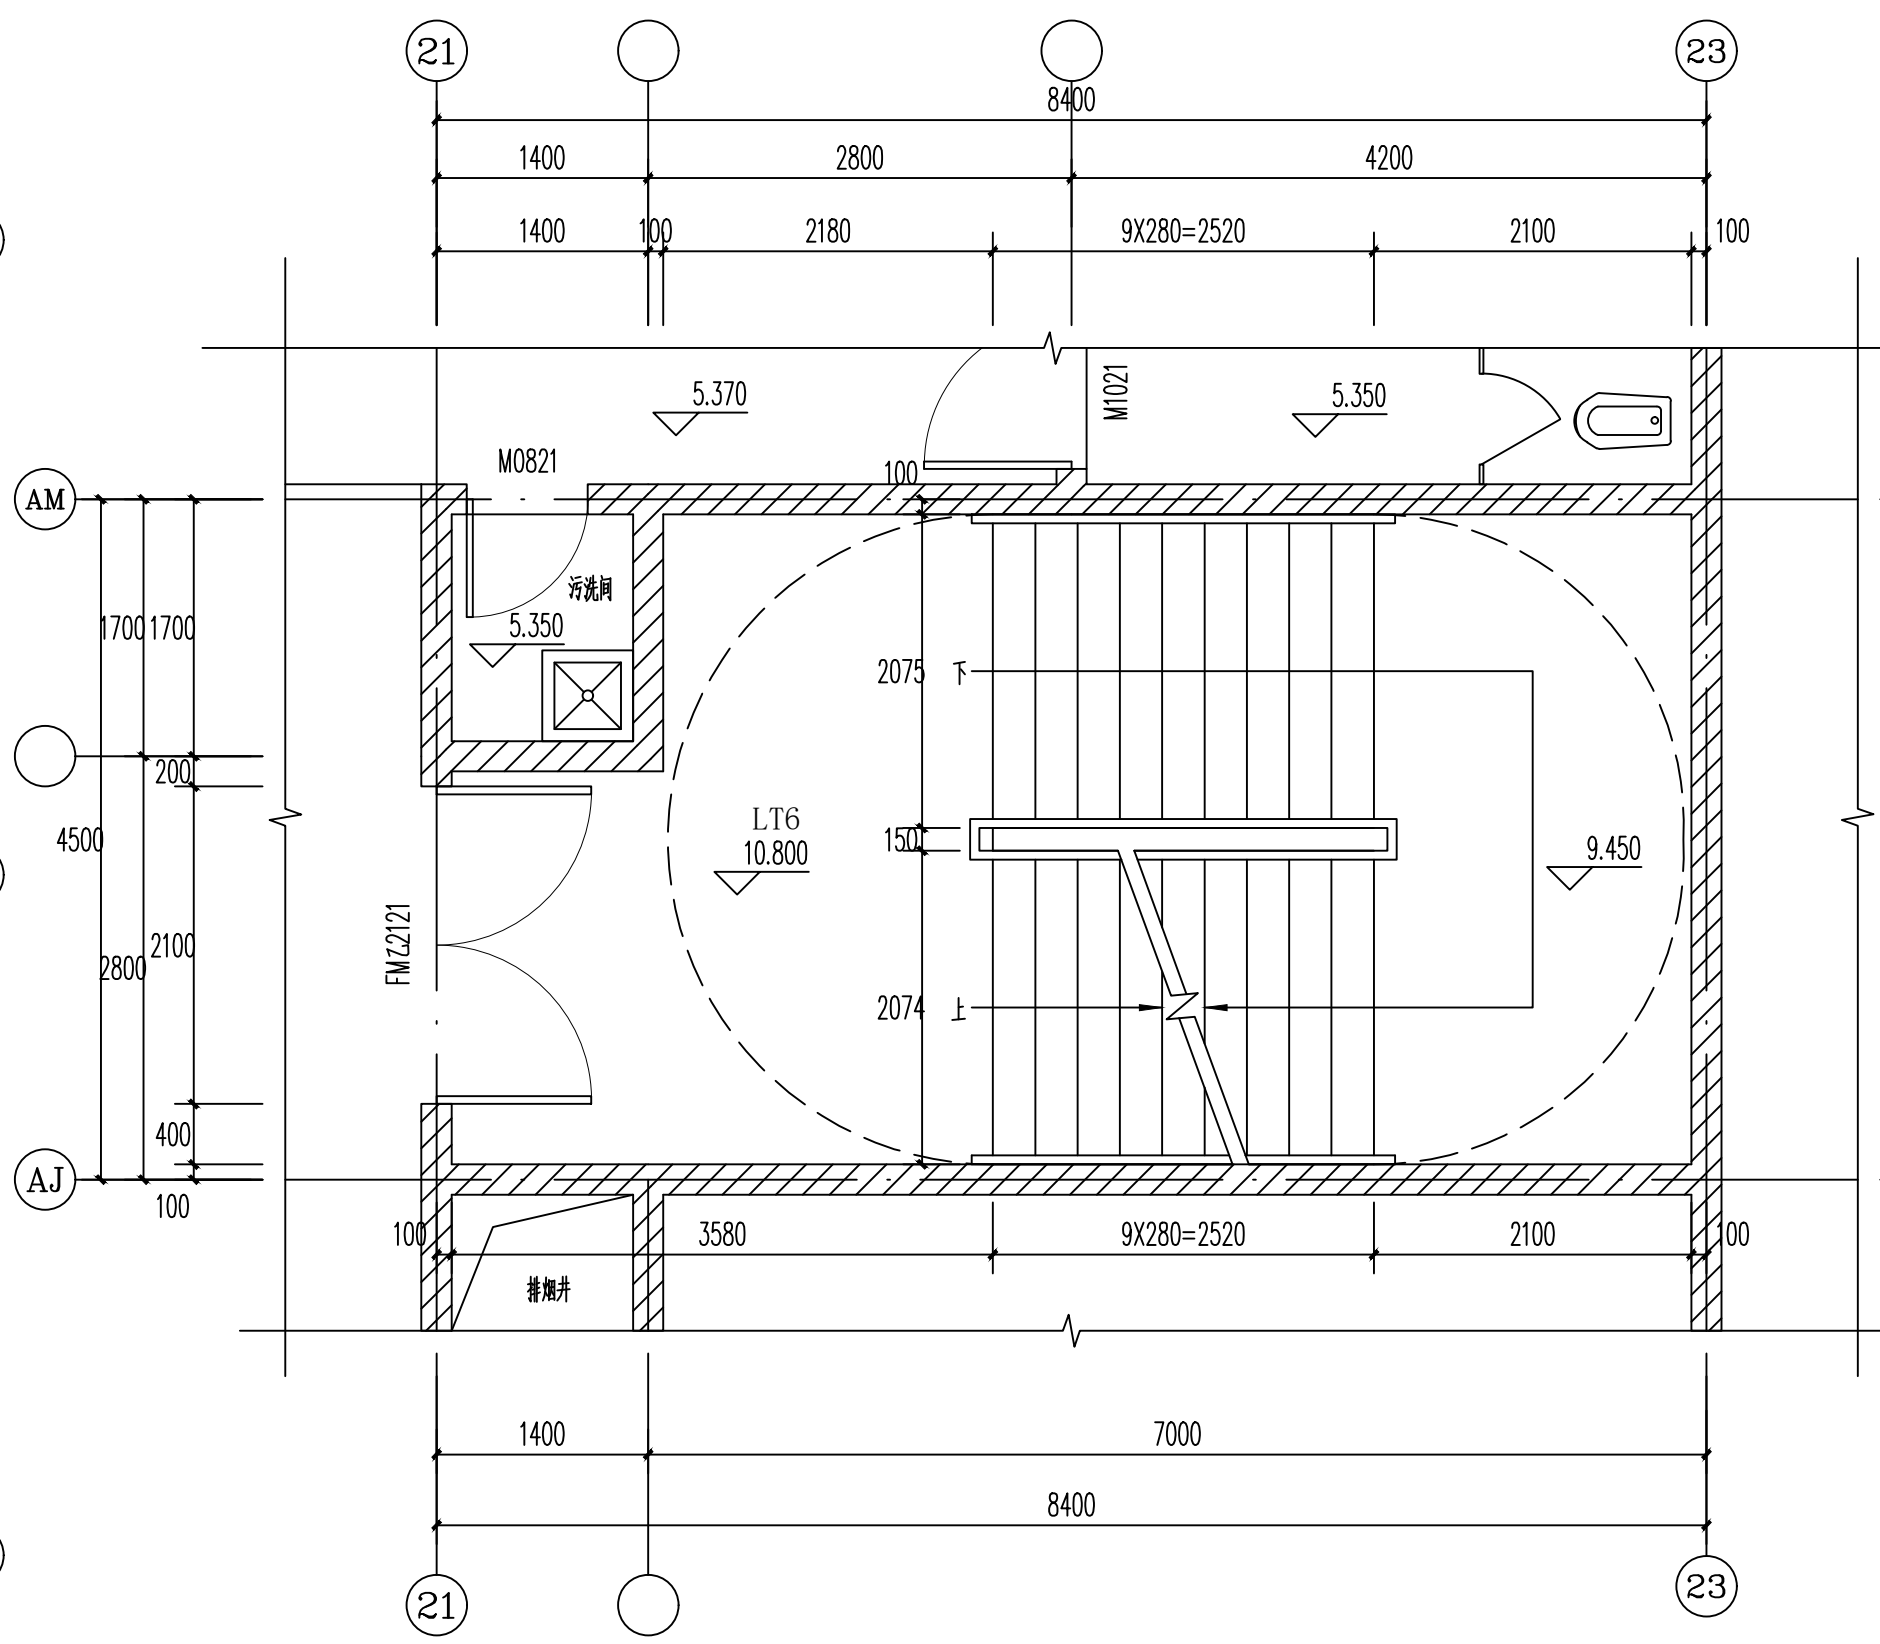
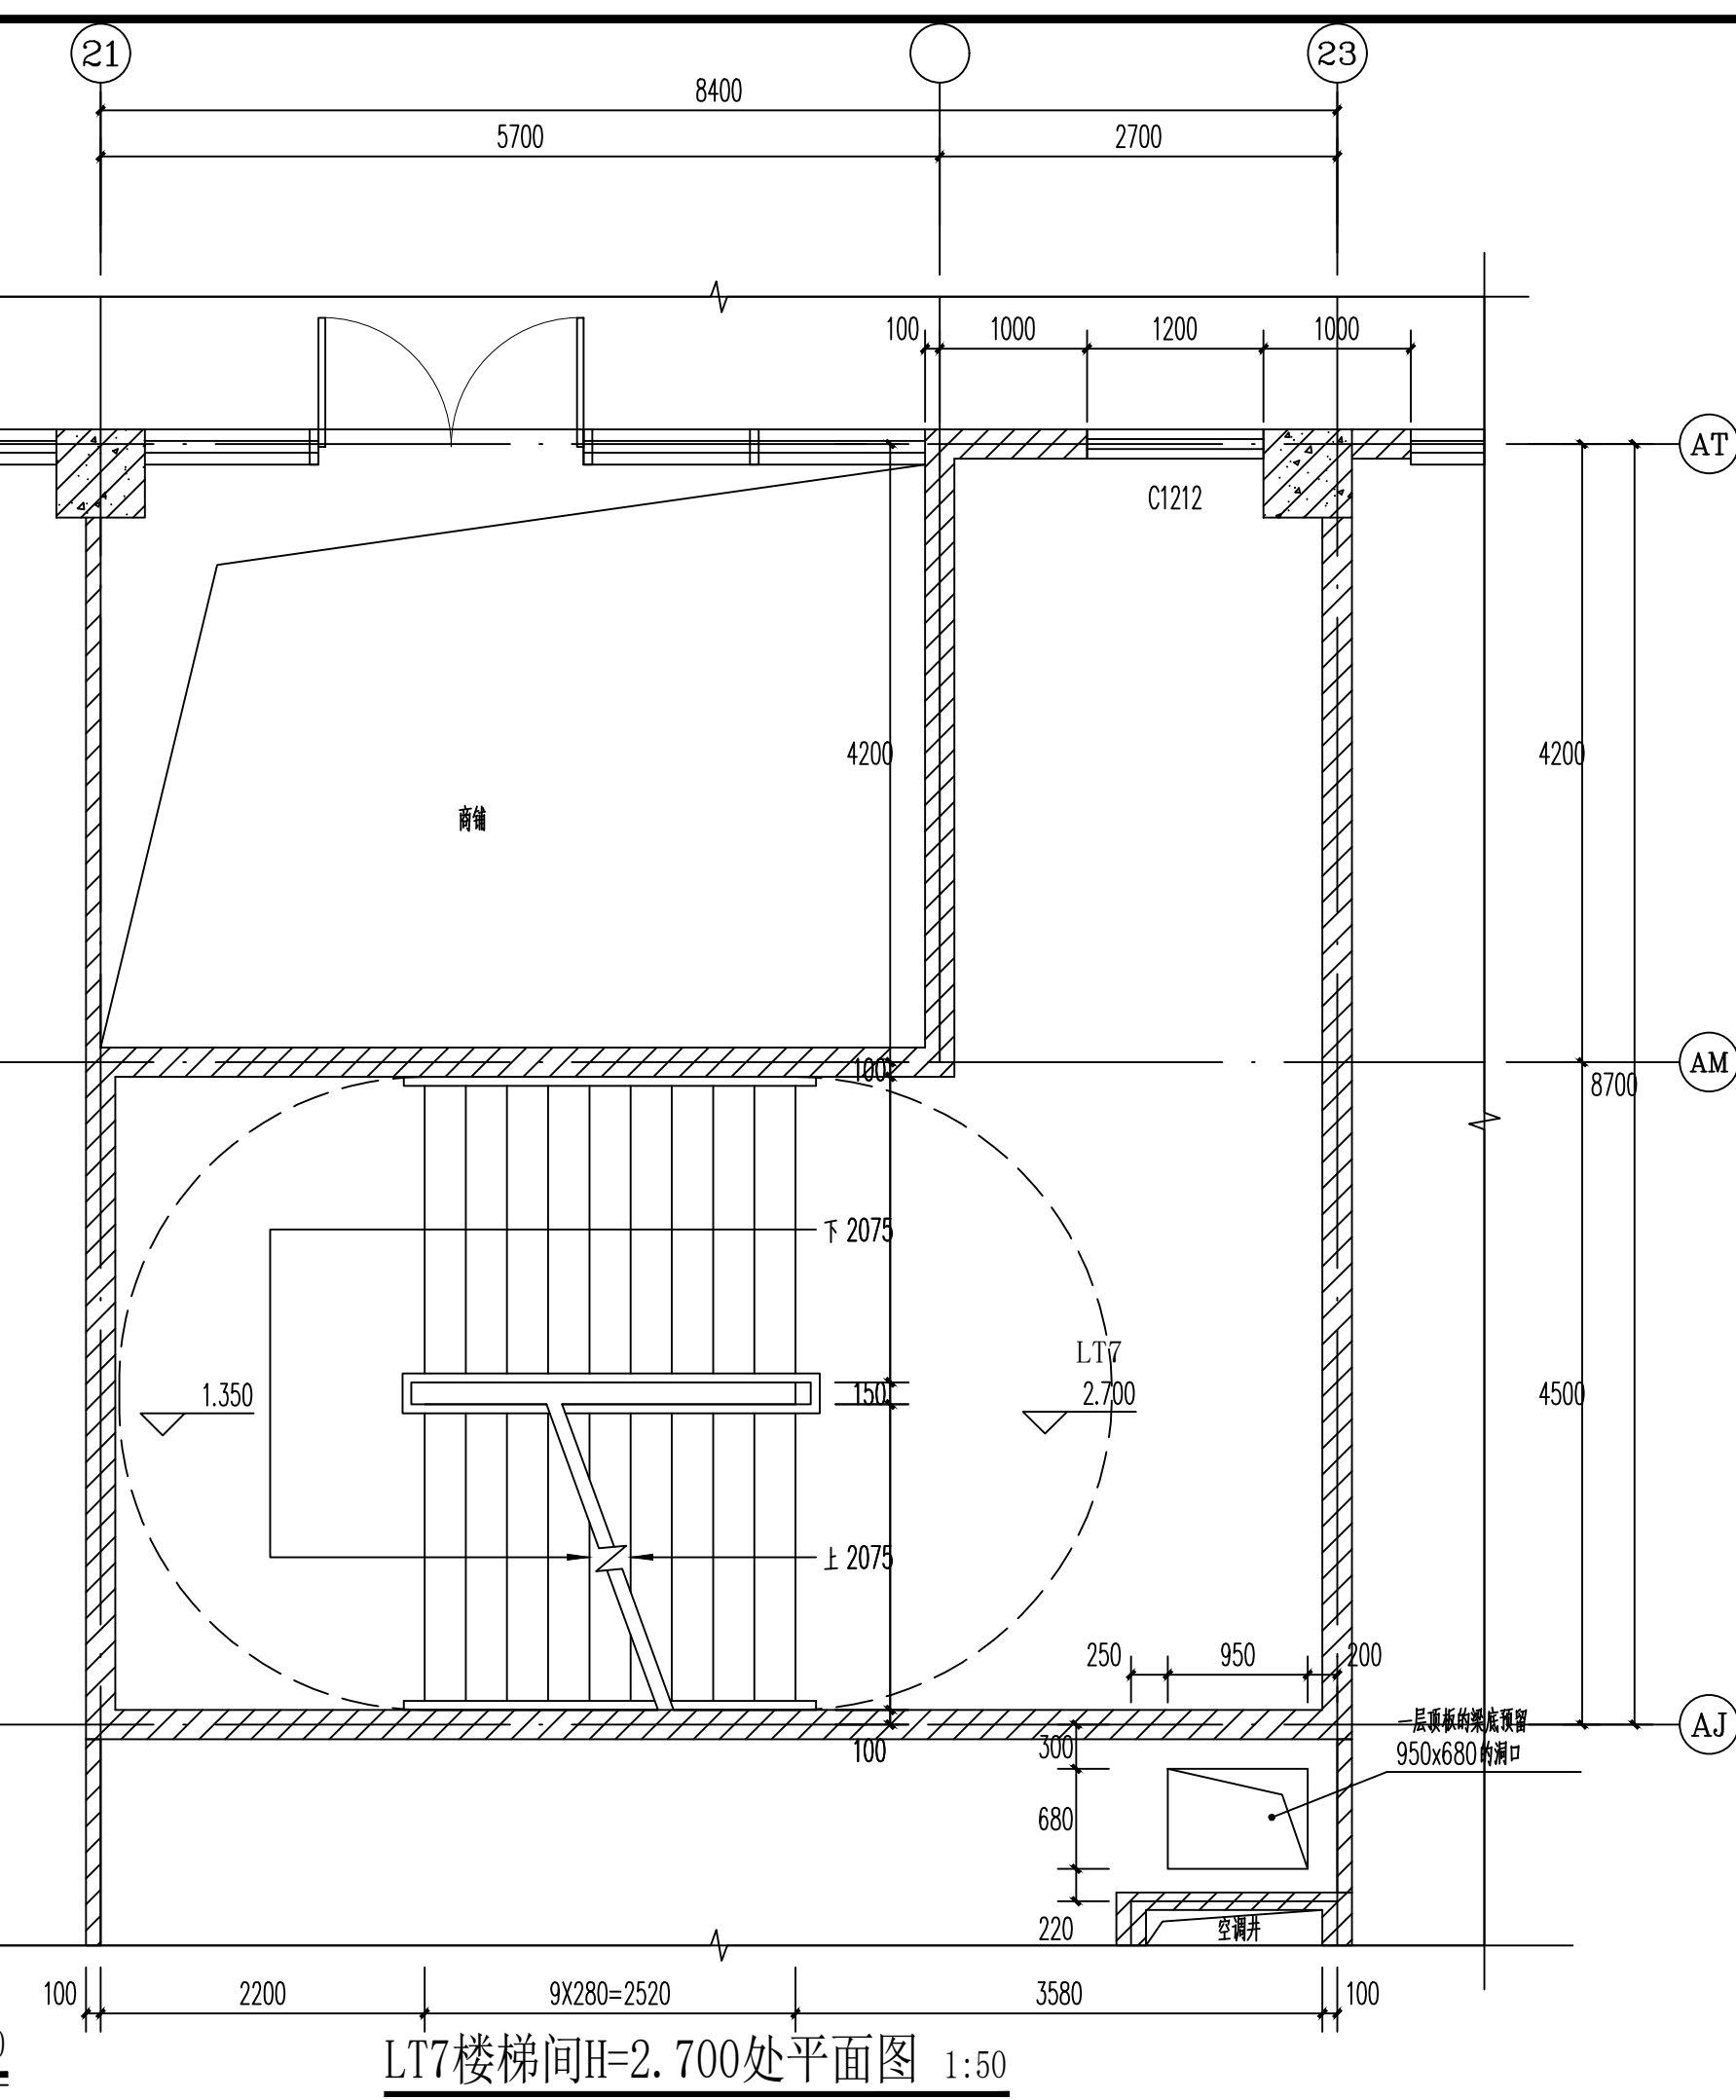
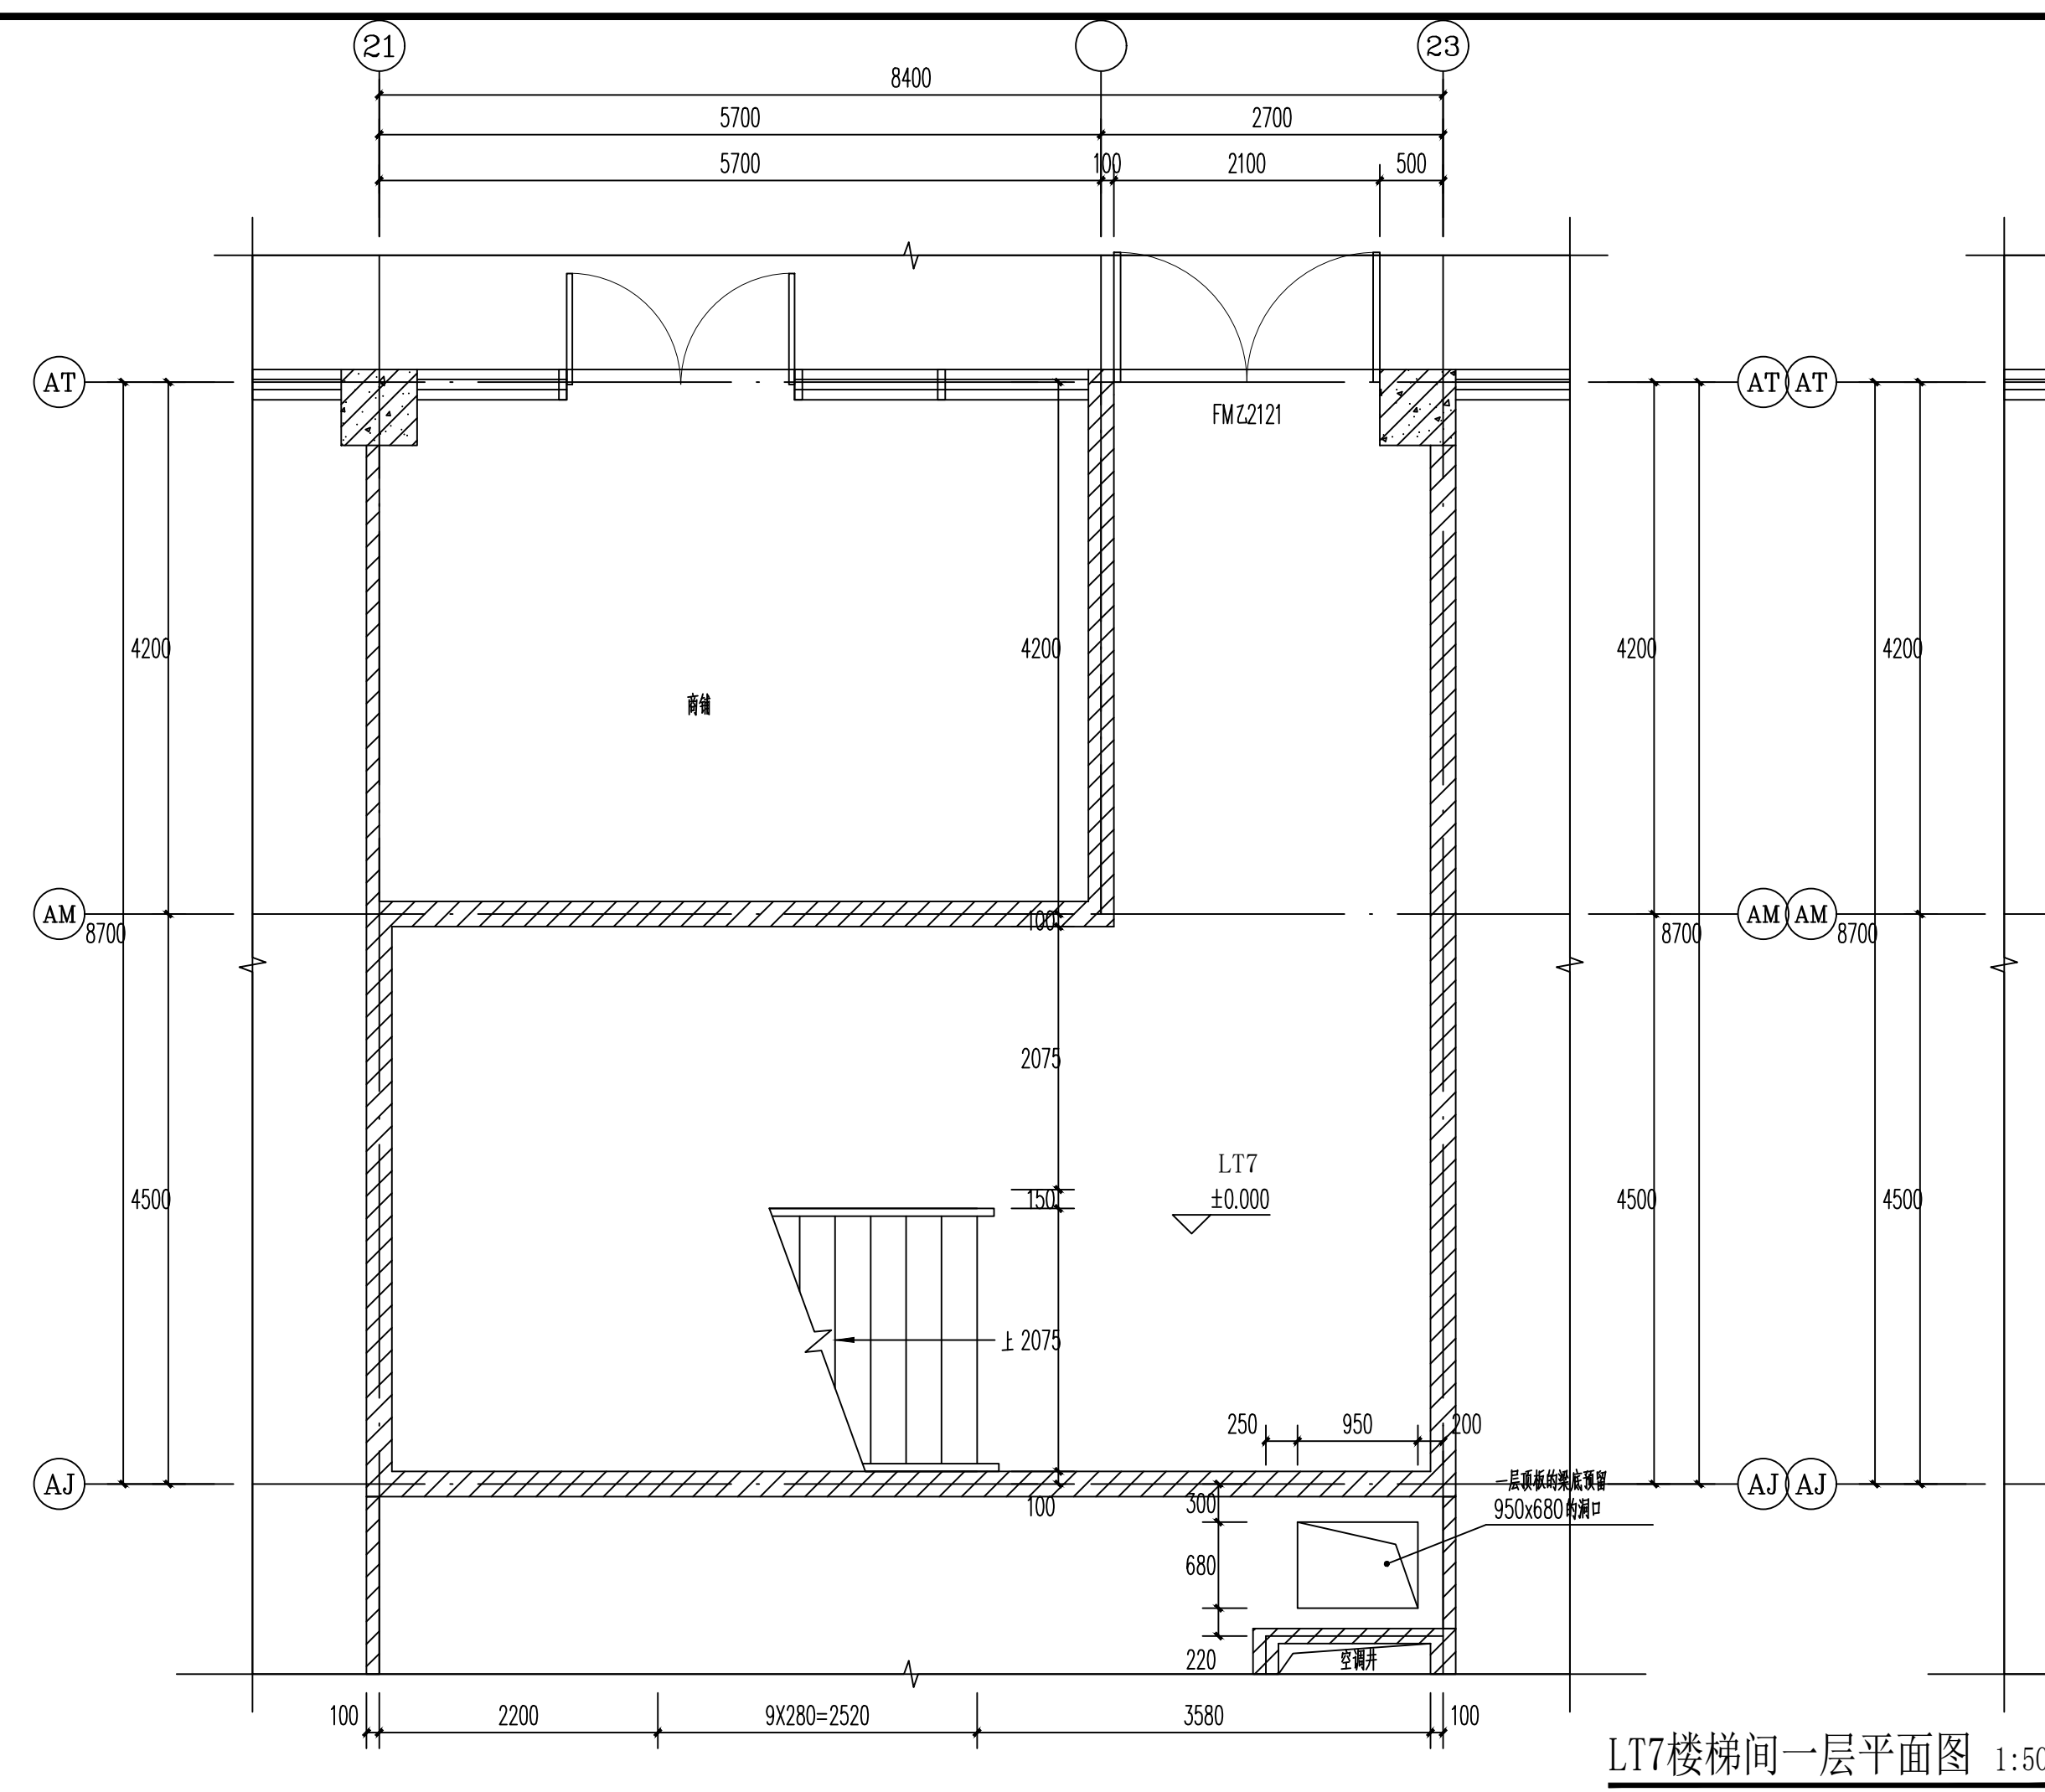


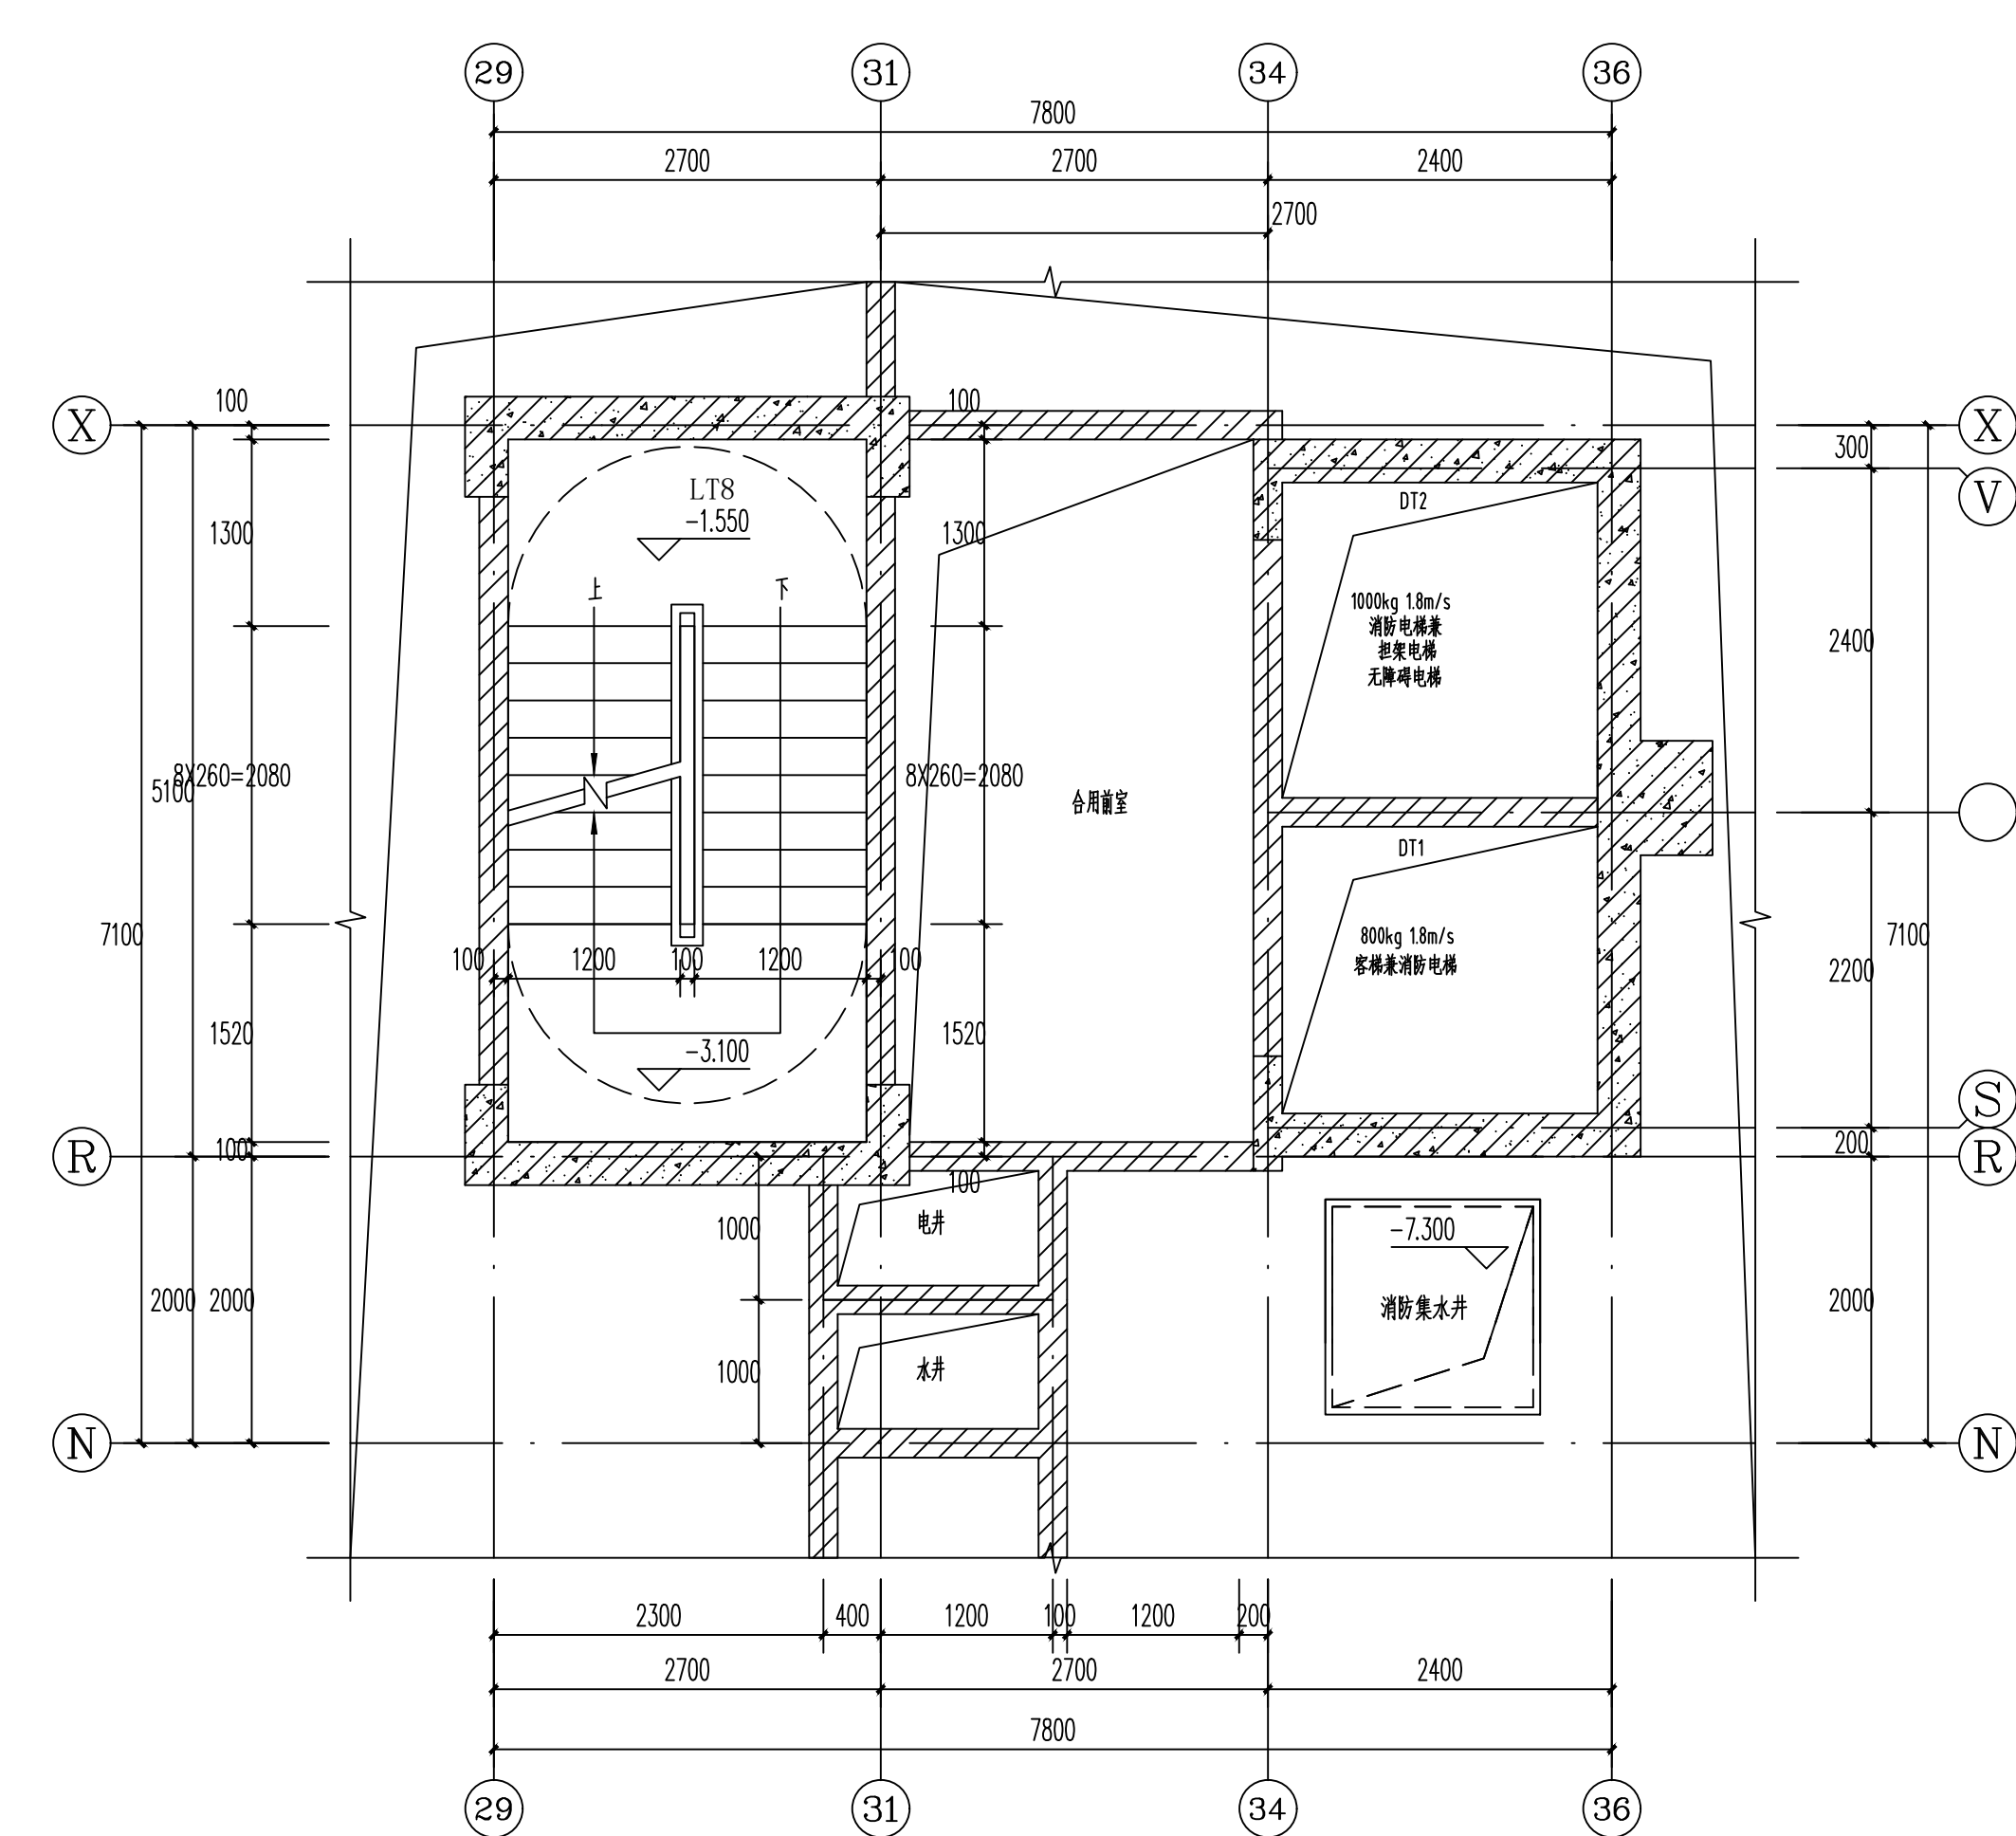

LT7楼梯间三层平面图 1:50

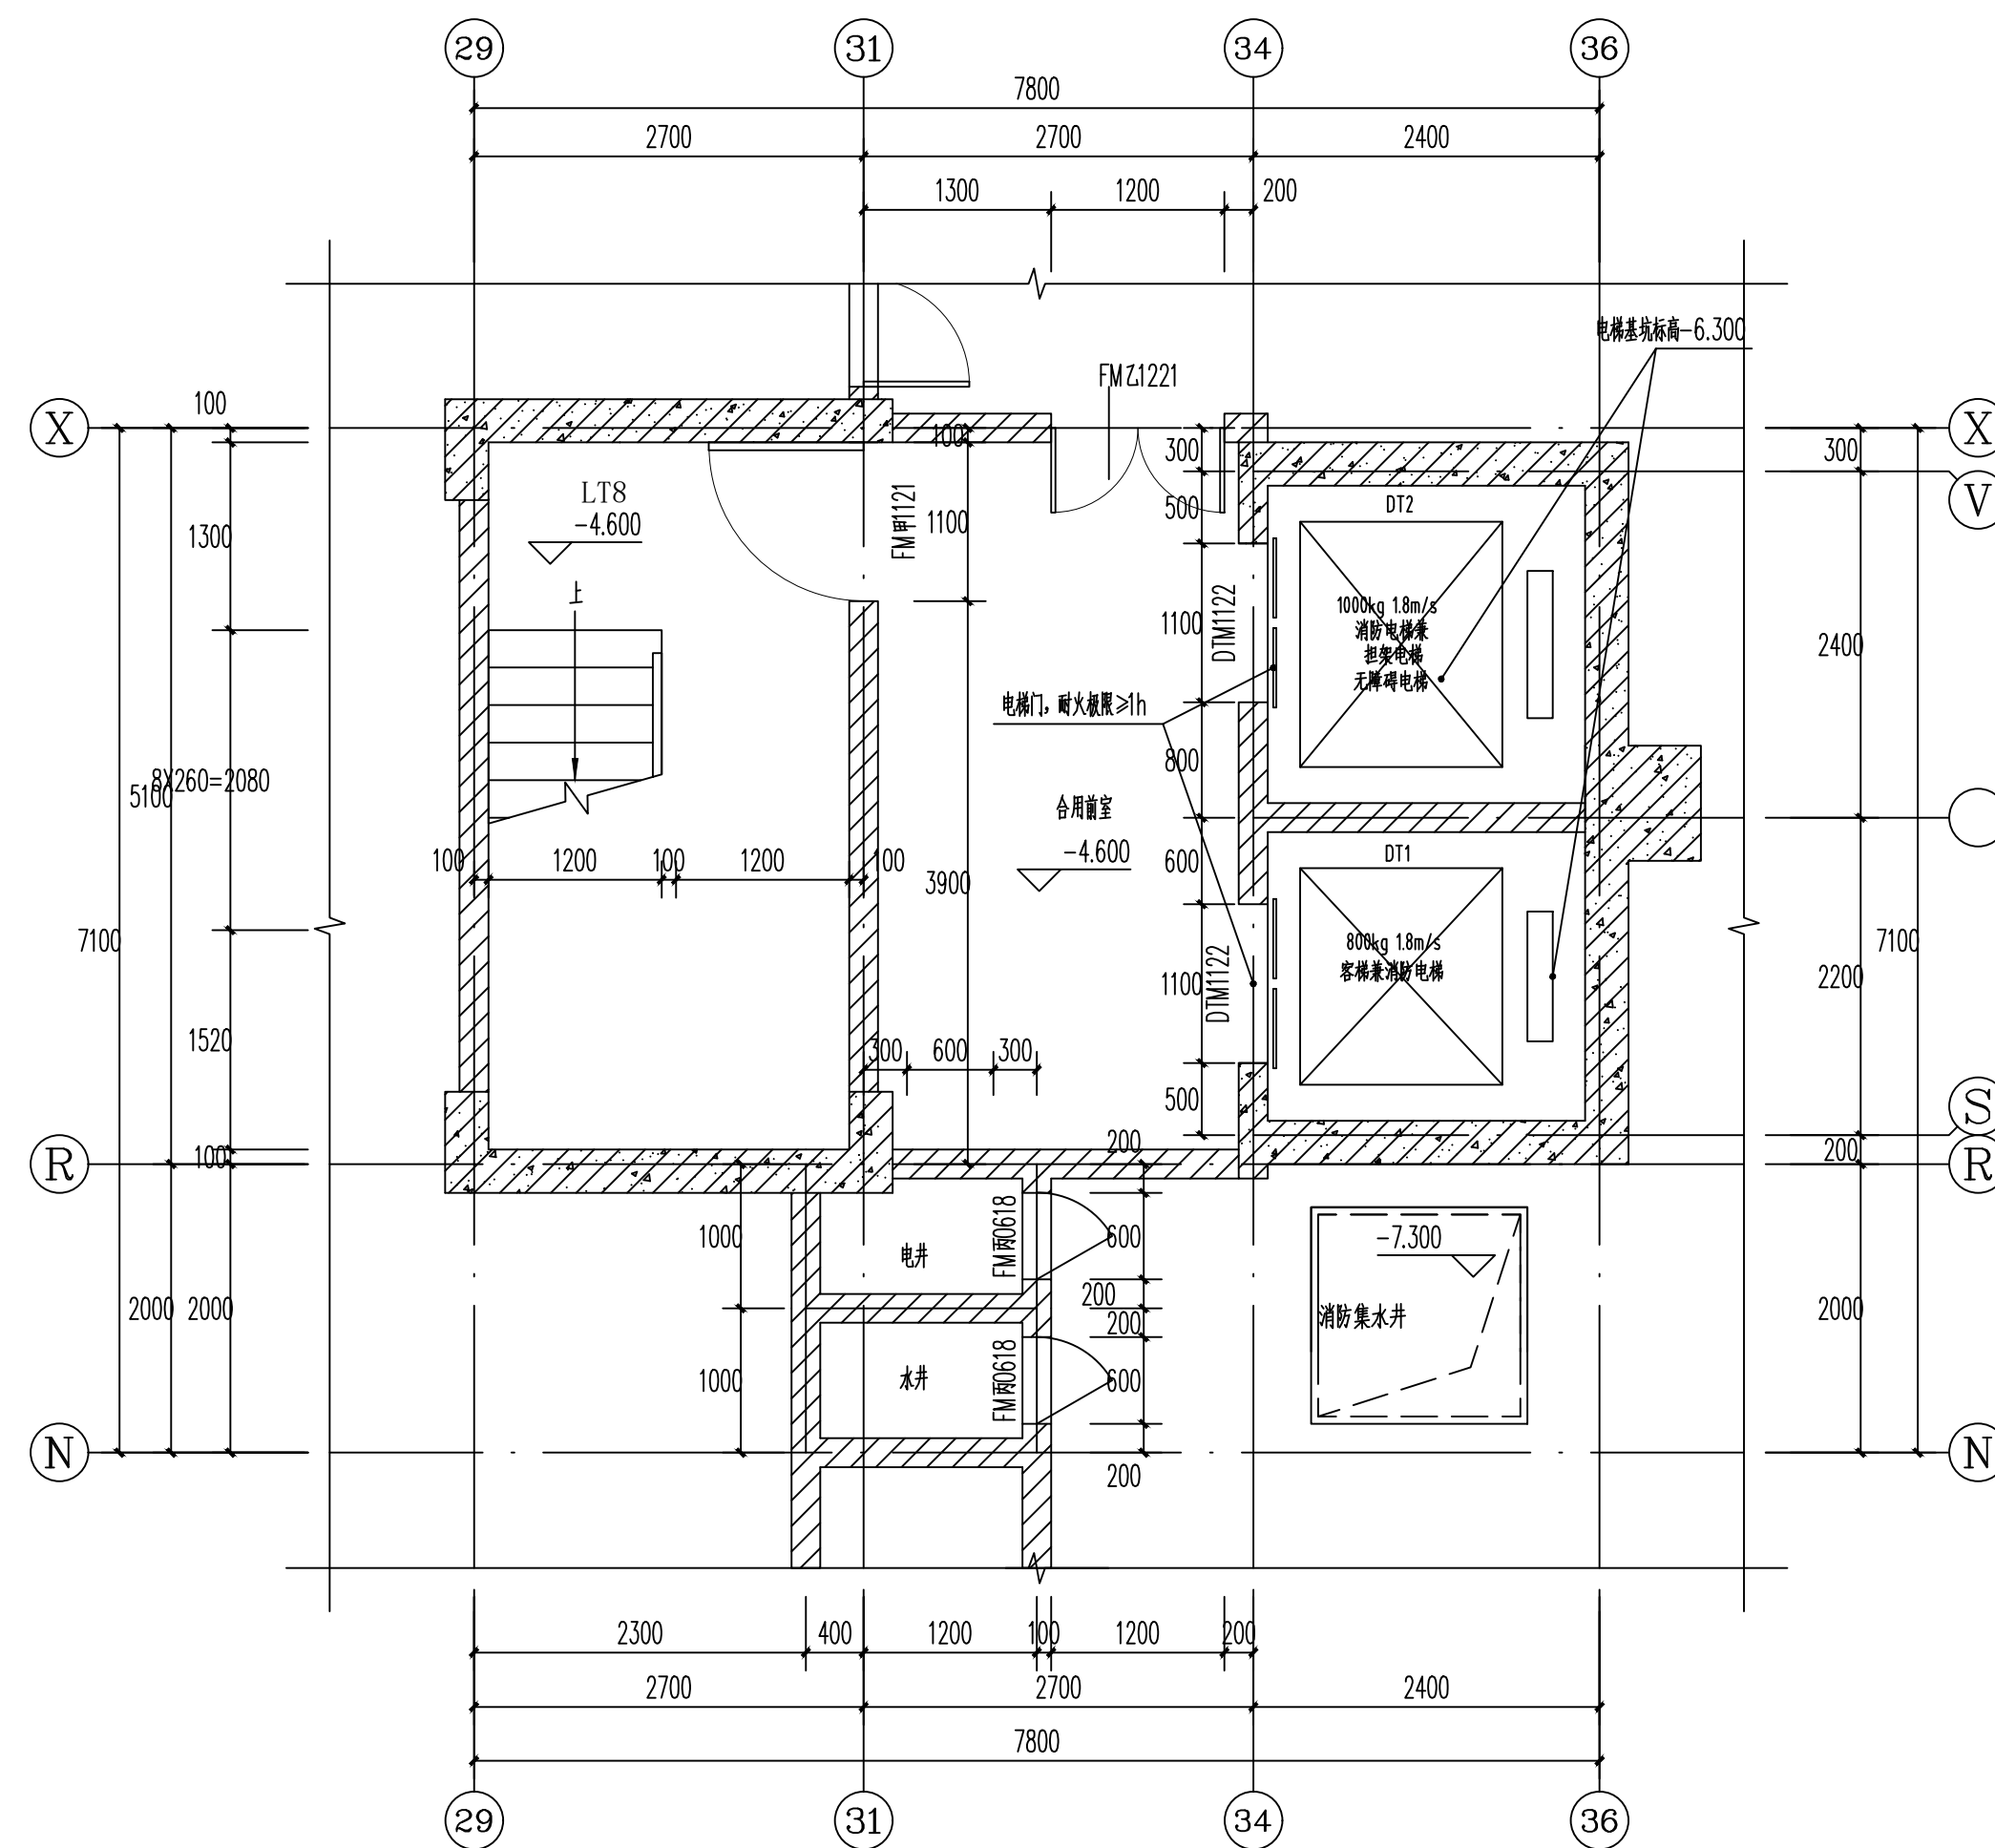

建设单位/CLIENT:

麻阳苗族自治县远桥房地产开发有限公司

项目名称/PROJECT:

远程国际

子项目名称/SUB-PROJECT:

远程国际

区位图/REGIONAL LOCATION MAP :



图纸名称/TITLE:

LT7楼梯间大样图

LT8楼梯间大样图一

项目名称/PROJECT:

远程国际

设计	古新辉	陈永红
----	-----	-----

DESIGNED		
DATE		

校对 CHECKED	吴新红	吴新红
---------------	-----	-----

专业负责人	吕士刚	吕士刚
-------	-----	-----

CHIEF	关志刚	关志刚

项目负责人 PROJECT CHIEF	吴志刚	吴志刚
------------------------	-----	-----

业务号/JOB NO.

设计阶段/STATUS: 施工图

专业/DISCIPLINE: 建施

比例/		规格/	
-----	--	-----	--

出图日期/DATE: 2021.06

图号/DRAWING NO. JS-34

版次	修改内容	日期
----	------	----

条形码/BARCODE:

版权所有，不得复制、套用。
ALL RIGHTS RESERVED, DON'T COPIED, REPRODUCED.