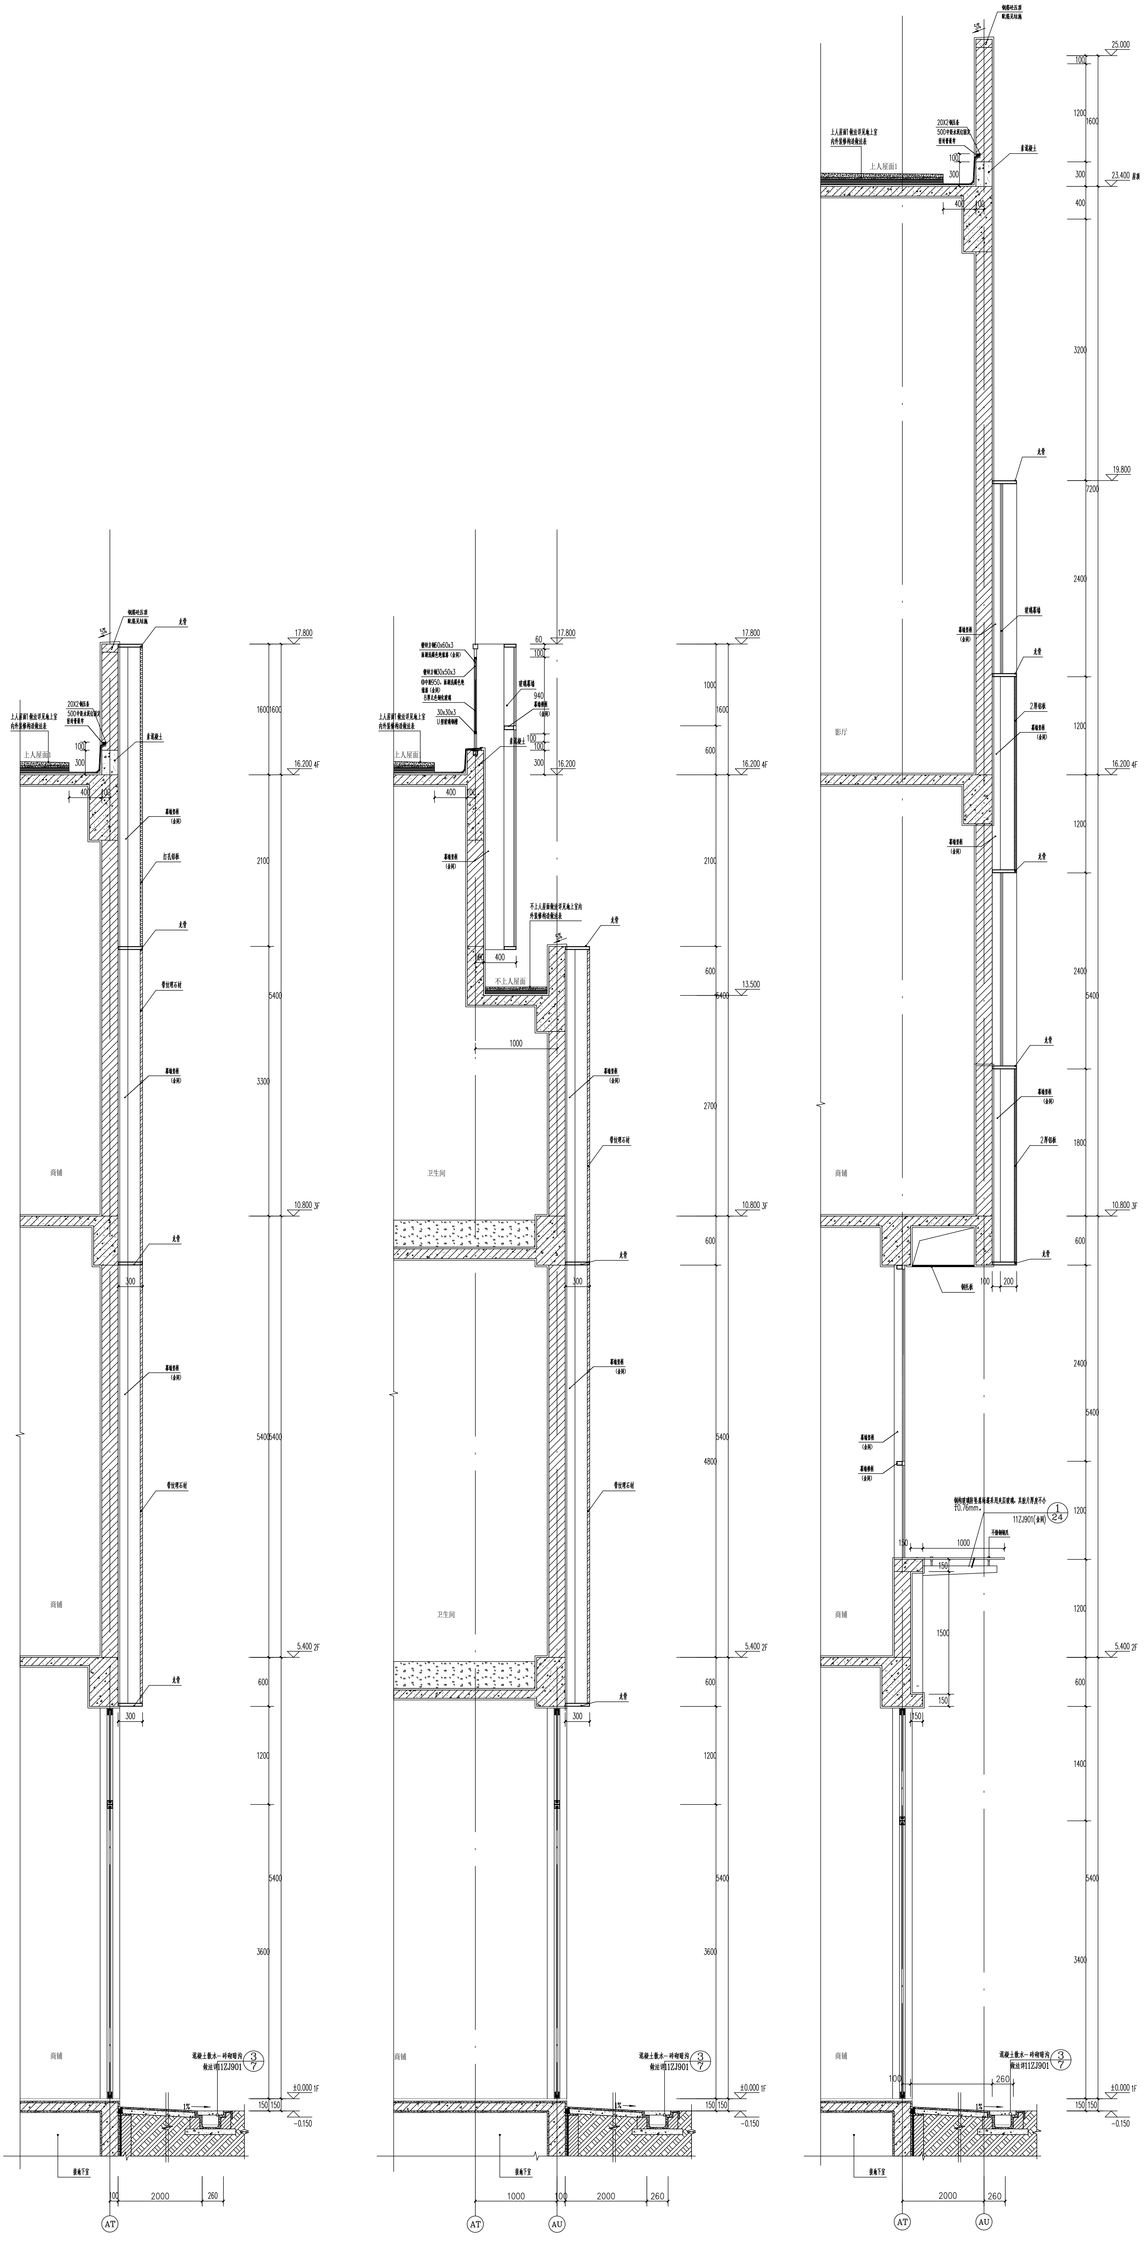

①墙身大样一 1:25

②墙身大样二 1:25

③墙身大样三 1:25

建设单位/CLIENT：
麻阳苗族自治县远怀房地产开发有限公司

项目名称/PROJECT：
远怀国际

子项目名称/SUB-PROJECT：
远程国际

区位图/REGIONAL LOCATION MAP：

广东建筑艺术设计院有限公司
GUANGDONG ARCHITECTURAL ART DESIGN INSTITUTE CO.,LTD.

图纸名称/TITLE：
墙身大样图一
墙身大样图二
墙身大样图三

项目名称/PROJECT：
远程国际

设计/DESIGNED	古振辉	
校对/CHECKED	吴新红	
专业负责人/CHIEF	吴志刚	
项目负责人/PROJECT CHIEF	吴志刚	
审核/INSPECTED	黄佩伦	
审定/APPROVED	李 军	

业务号/JOB NO.

设计阶段/STATUS：施工图

专业/DISCIPLINE：建施

比例/SCALE：1：100　图纸/SIZE：A1

出图日期/DATE：2021.06

图号/DRAWING NO.：JS-36

条形码/BARCODE：

NO.	DESCRIPTION	DATE
版次	修改内容	日期

ALL RIGHTS RESERVED. COPYRIGHT © 版权所有 侵权必究