
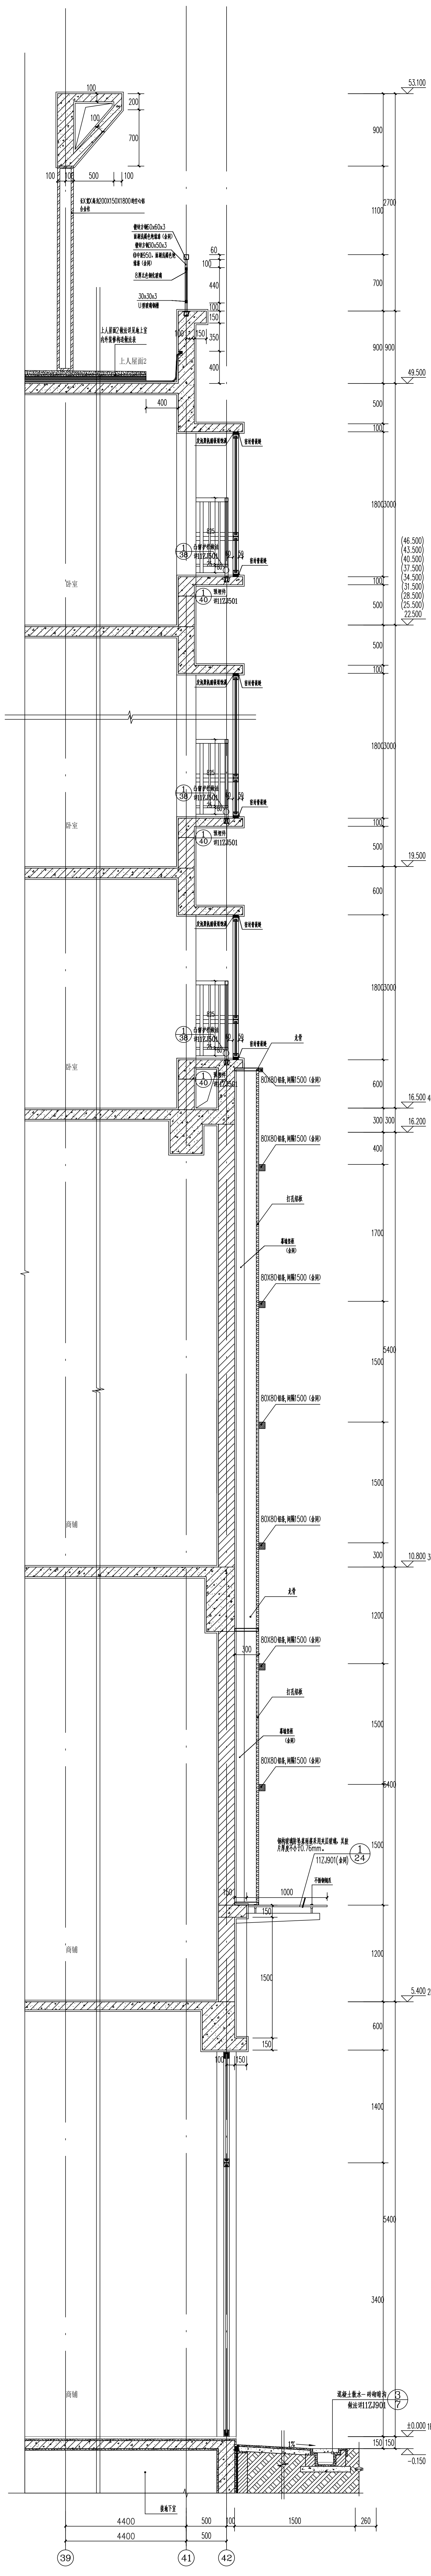


① 墙身大样九 1:25

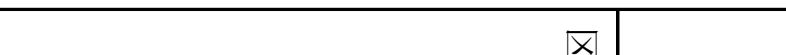

② 墙身大样十 1:25

建设单位/CUSTOMER:																					
肇庆市端州南滨房地产开发有限公司																					
项目名称/PROJECT:																					
远程国际																					
子项目名称/SUB-PROJECT:																					
远程国际																					
区位图/REGIONAL LOCATION MAP :																					
																					
图纸名称/TITLE:																					
端身大样图九 墙身大样图十																					
项目名称/PROJECT:																					
远程国际																					
<table><tr><th>设计/DRAWN</th><td>古耀辉</td></tr><tr><th>CHECKED</th><td>吴新红</td></tr><tr><th>专业负责人</th><td>吴志刚</td></tr><tr><th>项目负责人</th><td>吴志刚</td></tr><tr><th>PROJECT CLIENT</th><td>黄耀虎</td></tr><tr><th>审核</th><td>李坚</td></tr><tr><th>DENY/FIELD</th><td></td></tr><tr><th>审定</th><td></td></tr><tr><th>APPROVED</th><td></td></tr></table>				设计/DRAWN	古耀辉	CHECKED	吴新红	专业负责人	吴志刚	项目负责人	吴志刚	PROJECT CLIENT	黄耀虎	审核	李坚	DENY/FIELD		审定		APPROVED	
设计/DRAWN	古耀辉																				
CHECKED	吴新红																				
专业负责人	吴志刚																				
项目负责人	吴志刚																				
PROJECT CLIENT	黄耀虎																				
审核	李坚																				
DENY/FIELD																					
审定																					
APPROVED																					
业务号/JOB NO.																					
设计阶段/STATUS: 施工图																					
专业/DISCIPLINE: 建筑																					
比例/SCALE:	1:100	规格/SIZE:	A1																		
出图日期/DATE: 2021.06																					
图号/DWGING NO.: JS-39																					
版次/NO.	修改内容/DESCRIPTION	日期/DATE																			
备注/REMARKS:																					
版权所有，不得复制或，意月																					
ALL RIGHTS RESERVED. ANY COPIES ARE PROHIBITED.																					