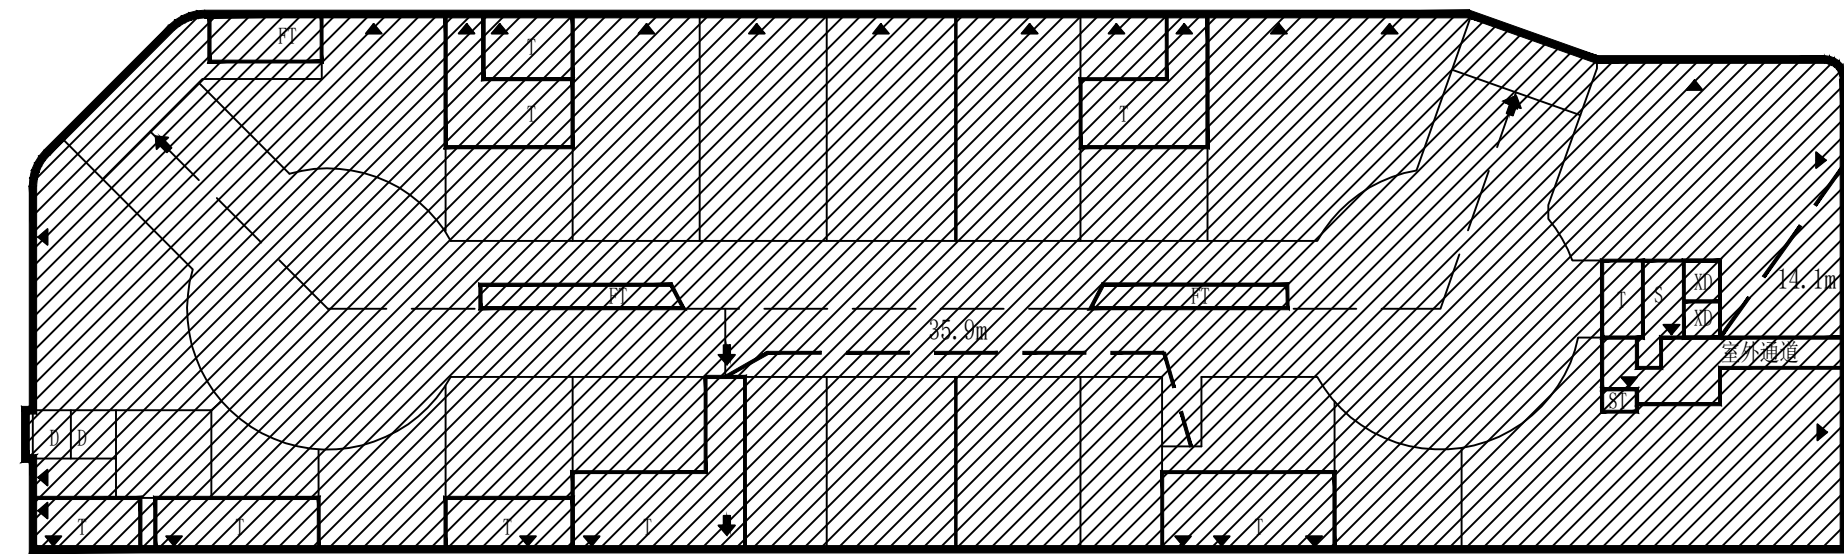




一层防火分区示意图 1:500

注：一层商场设置自动喷淋灭火系统

本层为一个防火分区，防火分区分区面积为4129.28㎡，共有3个安全出口。

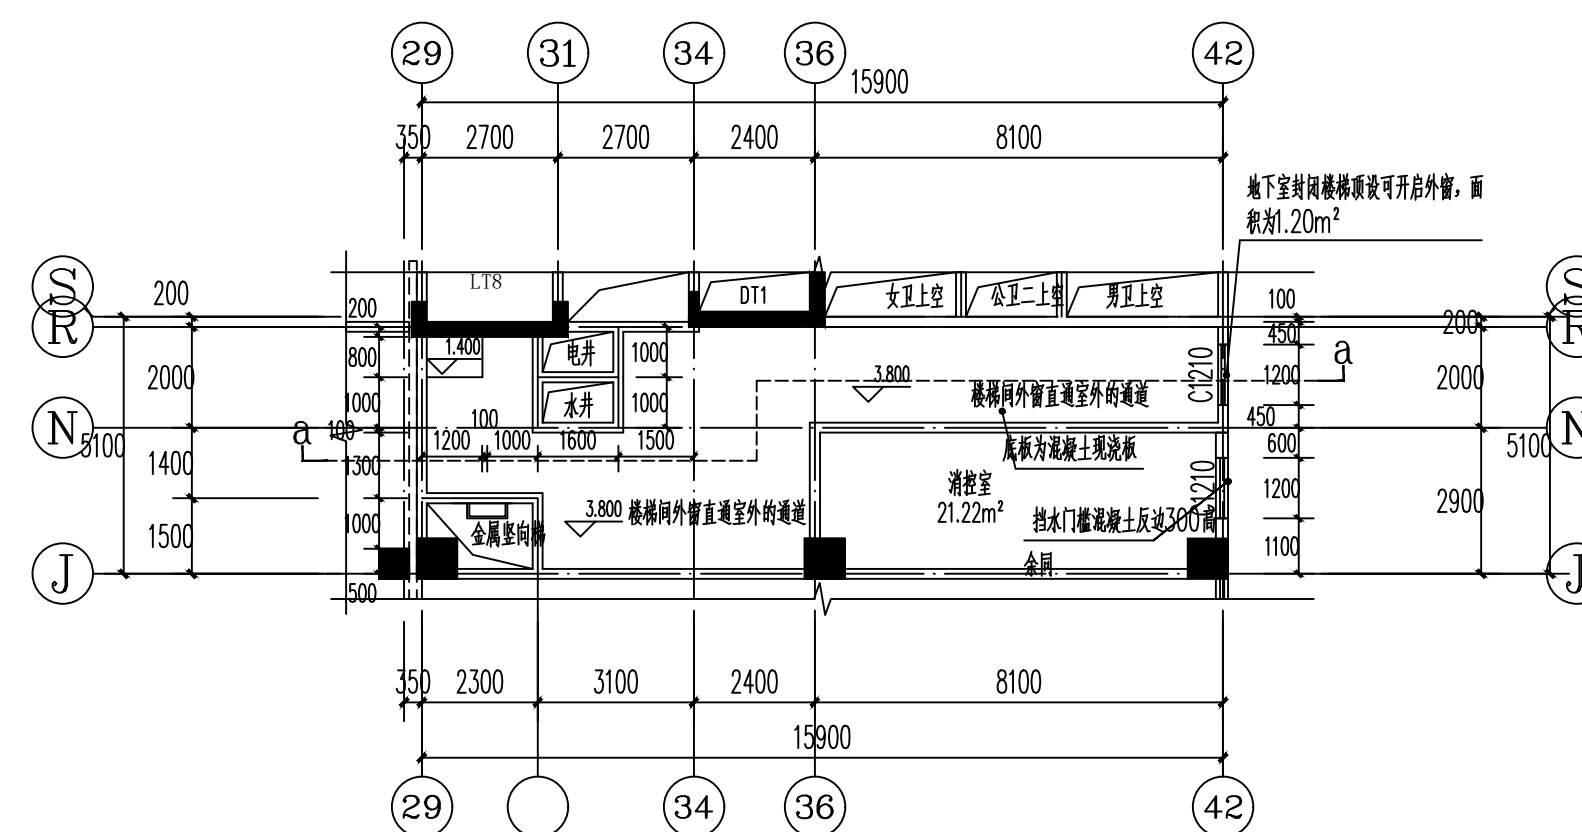
房间内最远点至最近安全出口的距离为14.1m（≤27.5m），最近疏散门至最近安全出口的距离为35.9m（≤37.5m），满足规范要求。

本层需要的疏散宽度为3692.11X0.43X1.100/15=87m（计算疏散宽度的面积是减掉一层所有楼梯间面积后的净面积）

本层设计的疏散宽度为7.2X2+2=16.80m，满足规范要求。

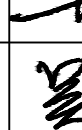
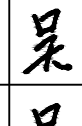
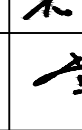
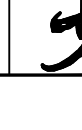
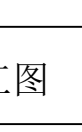
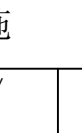
本层建筑面积: 4129.28m²
总建筑面积: 22985.06m²
计容总建筑面积: 18157.36m²
不计容总建筑面积: 4827.70m²

 灰砂加气混凝土砌块 (商铺隔墙)
 消火栓



室外通道夹层平面图 1:150 注: a-a剖面图详IS-25

1. 柱布置尺寸详附图。
2. 除图中除注明者外, 门窗洞口的墙垛均100mm或平柱、墙垛、墙中设置。
3. 本工程所有外墙厚度均按240厚砌体灰浆加气混凝土砌块, 墙垛墙柱外挑100mm, 内挑140mm。
4. 外墙除墙垛外挑外其余均100mm厚砂加气混凝土砌块, 其墙垛墙柱均200mm烧结实心页岩砖。
5. 凡窗台高小于900mm时, 窗台栏板栏板高度按图J1ZJ401《建筑详图制作安全安全防护要求》, 以防止人员攀爬。
6. 各种设备管、穿墙管、管道及附件等具体做法同时参照各专业施工图。
7. 本建筑屋面为平坡屋面, 檐口位置见屋面图。
8. 屋面采用挤塑泡沫保温隔热层, 门口下方设置300mm高200mm宽门门槛, 高度同屋面。
9. 除注明外, 卫生间地面标高均按+1.05; 卫生间厨房卫生间标高均为+0.03, 以±12楼为地面, (H为楼面标高), 详见卫生间大样图。
10. 所有室外卫生间、更衣室宜设玻璃门磨砂玻璃。
11. 外墙采用卫生间完成面与相应装饰完成面隔5mm, 并应有坡度过渡, 具体详见卫生间详图。
12. 大样详图按J1J11-1-(A)-26, 内檐顶面顶面详图按J1J11-1-(A)-4-9, 地面详图按J1J11-1-(A)-7-2, 楼面详图按J1J11-1-(A)-8-1。
13. 人行安全出入口除J1Z-2主出入口的墙垛外, 其他地方墙垛高度≥2m墙垛玻璃厚度, 0.76mm厚双层钢化夹层玻璃。
14. 玻璃除墙垛外的宽度不小于0.1m, 0.1m, 下部固定高度不小于1.2m, 门宽不小于2.0m, 采用玻璃门, 玻璃门设置可在室外易于识别的明显标志, 详见平面图、立面图。
15. 大样图按J1Z-2, 洞口100x2200, 窗洞1700x2200的窗洞高度不应小于1.00m, 窗洞、窗洞按1.700-1.700-D3透光不透明玻璃门玻璃门。
16. 玻璃门自然通风, 每层设置可开启窗扇面积≥2m², 开启面积不大于三层。
17. 各层楼梯间楼梯间、每层设置自然通风的楼梯间采用防火材料材料材料。
18. 楼梯间自然通风: 门窗洞口距踏步800mm, 间距不小于, 在楼梯间外墙面设置, 距离高度800mm减小量。
19. 公共楼梯, 当楼梯净宽为2.2m时, 必须采取至少两人同时疏散的措施; 住宅楼梯, 楼梯净宽为2.1m时, 必须采取至少两人同时疏散的措施。
20. 中庭设置排烟罩尺寸及位置与设备专业图纸冲突时以本专业为准。

建设单位/CLIENT:					
麻阳苗族自治县远桥房地产开发有限公司					
项目名称/PROJECT: 远程国际					
子项目名称/SUB-PROJECT: 远程国际					
区位图/REGIONAL LOCATION MAP :					
 广东建筑艺术设计研究院有限公司 GUANGDONG ARCHITECTURAL ARTISTIC DESIGN INSTITUTE CO.,LTD ■ 建筑方案设计：甲级 ■ 风景园林设计：乙级 ■ 城乡规划设计：乙级 ■ 市政设计：乙级					
图纸名称/TITLE: 一层平面图					
项目名称/PROJECT: 远程国际					
设计 DESIGNED		古新辉			
校对 CHECKED		吴新红			
专业负责人 CHIEF		吴志刚			
项目负责 A PROJECT CHIEF		吴志刚			
审核 IDENTIFIED		黄履优			
审定 APPROVED		李 坚			
业务号/JOB NO.					
设计阶段/STATUS: 施工图					
专业/DISCIPLINE: 建筑					
比例/ SCALE:		1: 100		规格/ SIZE:	A1
出图日期/DATE:				2021. 06	
图号/DRAWING NO. JS-14					
版次 NO.		修改内容 DESCRIPTION			日期 DATE
条形码/BARCODE:					
版权所有，不得复制、套用。 ALL RIGHTS RESERVED, DON'T COPY, REPRODUCE					