

麻阳苗族自治县远桥房地产开发有限公司

子项目名称/SUB-PROJECT:	远程国际
--------------------	------

广东建筑艺术设计院有限公司
 GUANGDONG ARCHITECTURAL ARTISTIC DESIGN INSTITUTE CO.,LTD

■ 建筑室内设计：甲级 ■ 风景园林设计：乙级

■ 城乡规划设计：乙级 ■ 市政设计：乙级

1-1剖面图

项目名称/PROJECT:	远程国际
---------------	------

设计 DESIGNED	古新辉	
校对 CHECKED	吴新红	
专业负责人 CHIEF	吴志刚	
项目负责人 PROJECT CHIEF	吴志刚	
审核 IDENTIFIED	黄履优	
审定 APPROVED	李 坚	

业务号/JOB NO.

设计阶段/STATUS: 施工图

专业/DISCIPLINE: 建施

比例/ SCALE:	1: 100	规格/ SIZE:	A1
---------------	--------	--------------	----


出图日期/DATE: 2021.06

图号/DRAWING NO. JS-24

版次 NO.	修改内容 DESCRIPTION	日期 DATE

条形码/BARCODE:

版权所有，不得复制、套用。
ALL RIGHTS RESERVED, DON'T COPIED, REPRODUCED.

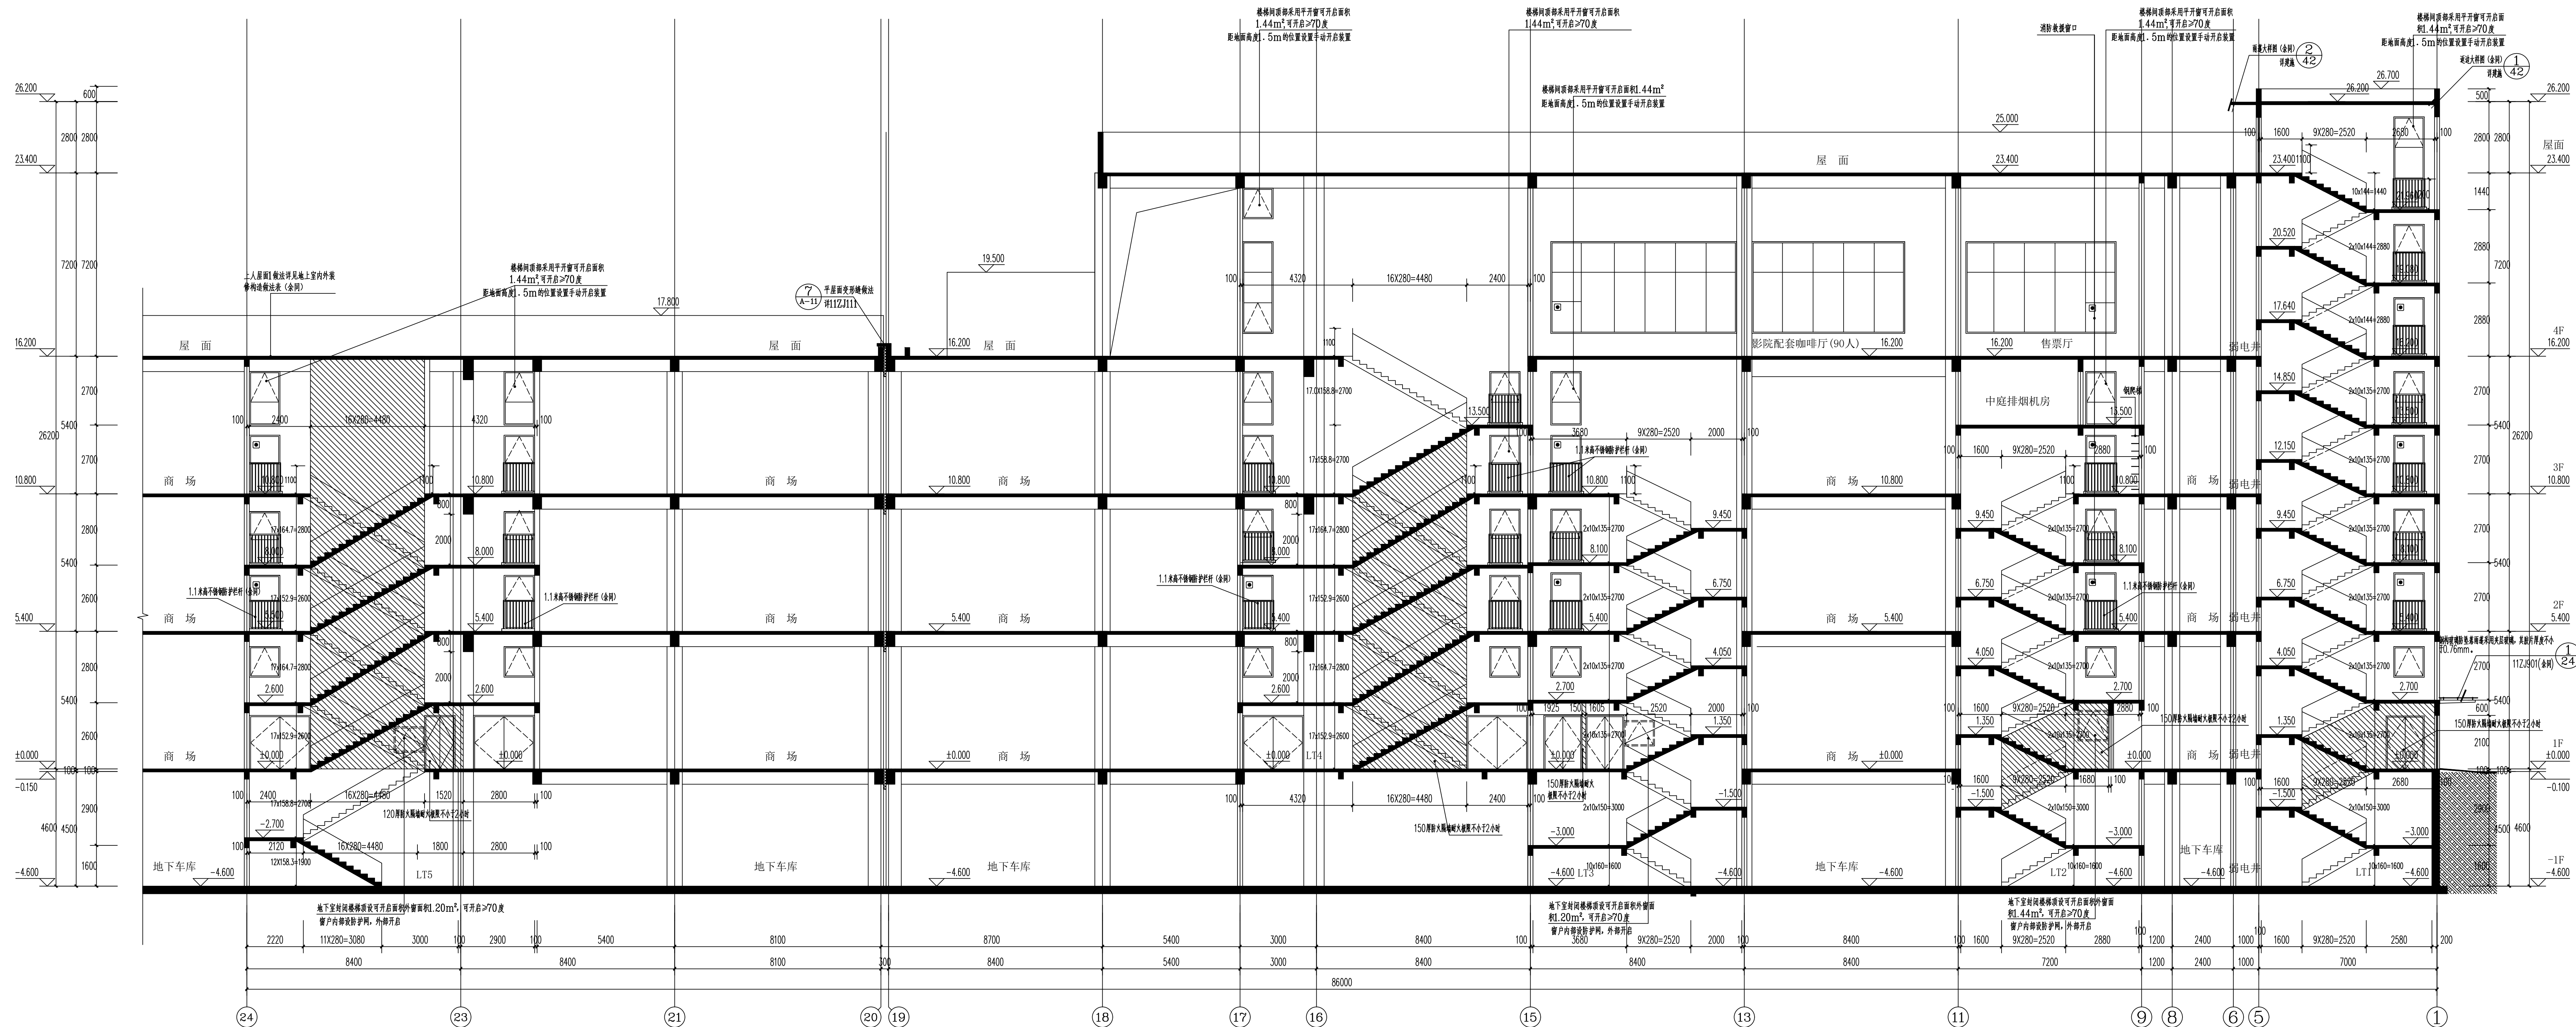

1-1剖面图 1:100

注: LT1~LT5剖面图
消防玻璃窗(不应小于1.0m×1.0m,
窗台高不应大于1.2m,玻璃采用夹层玻璃)

- 1.本工程梯梯除净宽、步数及平台宽度等按梯样大样，梯样栏杆采用不锈钢栏杆900高，详11ZJ401-13-7大样详11ZJ401-37-16；（注：当扶手水平高度+70.5m时，栏杆净高不低于1100。）
- 2.起步详11ZJ40138-6；扶手与填充墙连接详11ZJ401-42-5，防滑详11ZJ401-39-6
- 3.梯边大1110，加做防坠网处理。
- 4.凡栏杆高小于900mm时，作防护栏杆具体做法详见11ZJ401-40-16制作要符合安全防护要求，以阻止人攀爬。