




车道1-1剖面 1:100

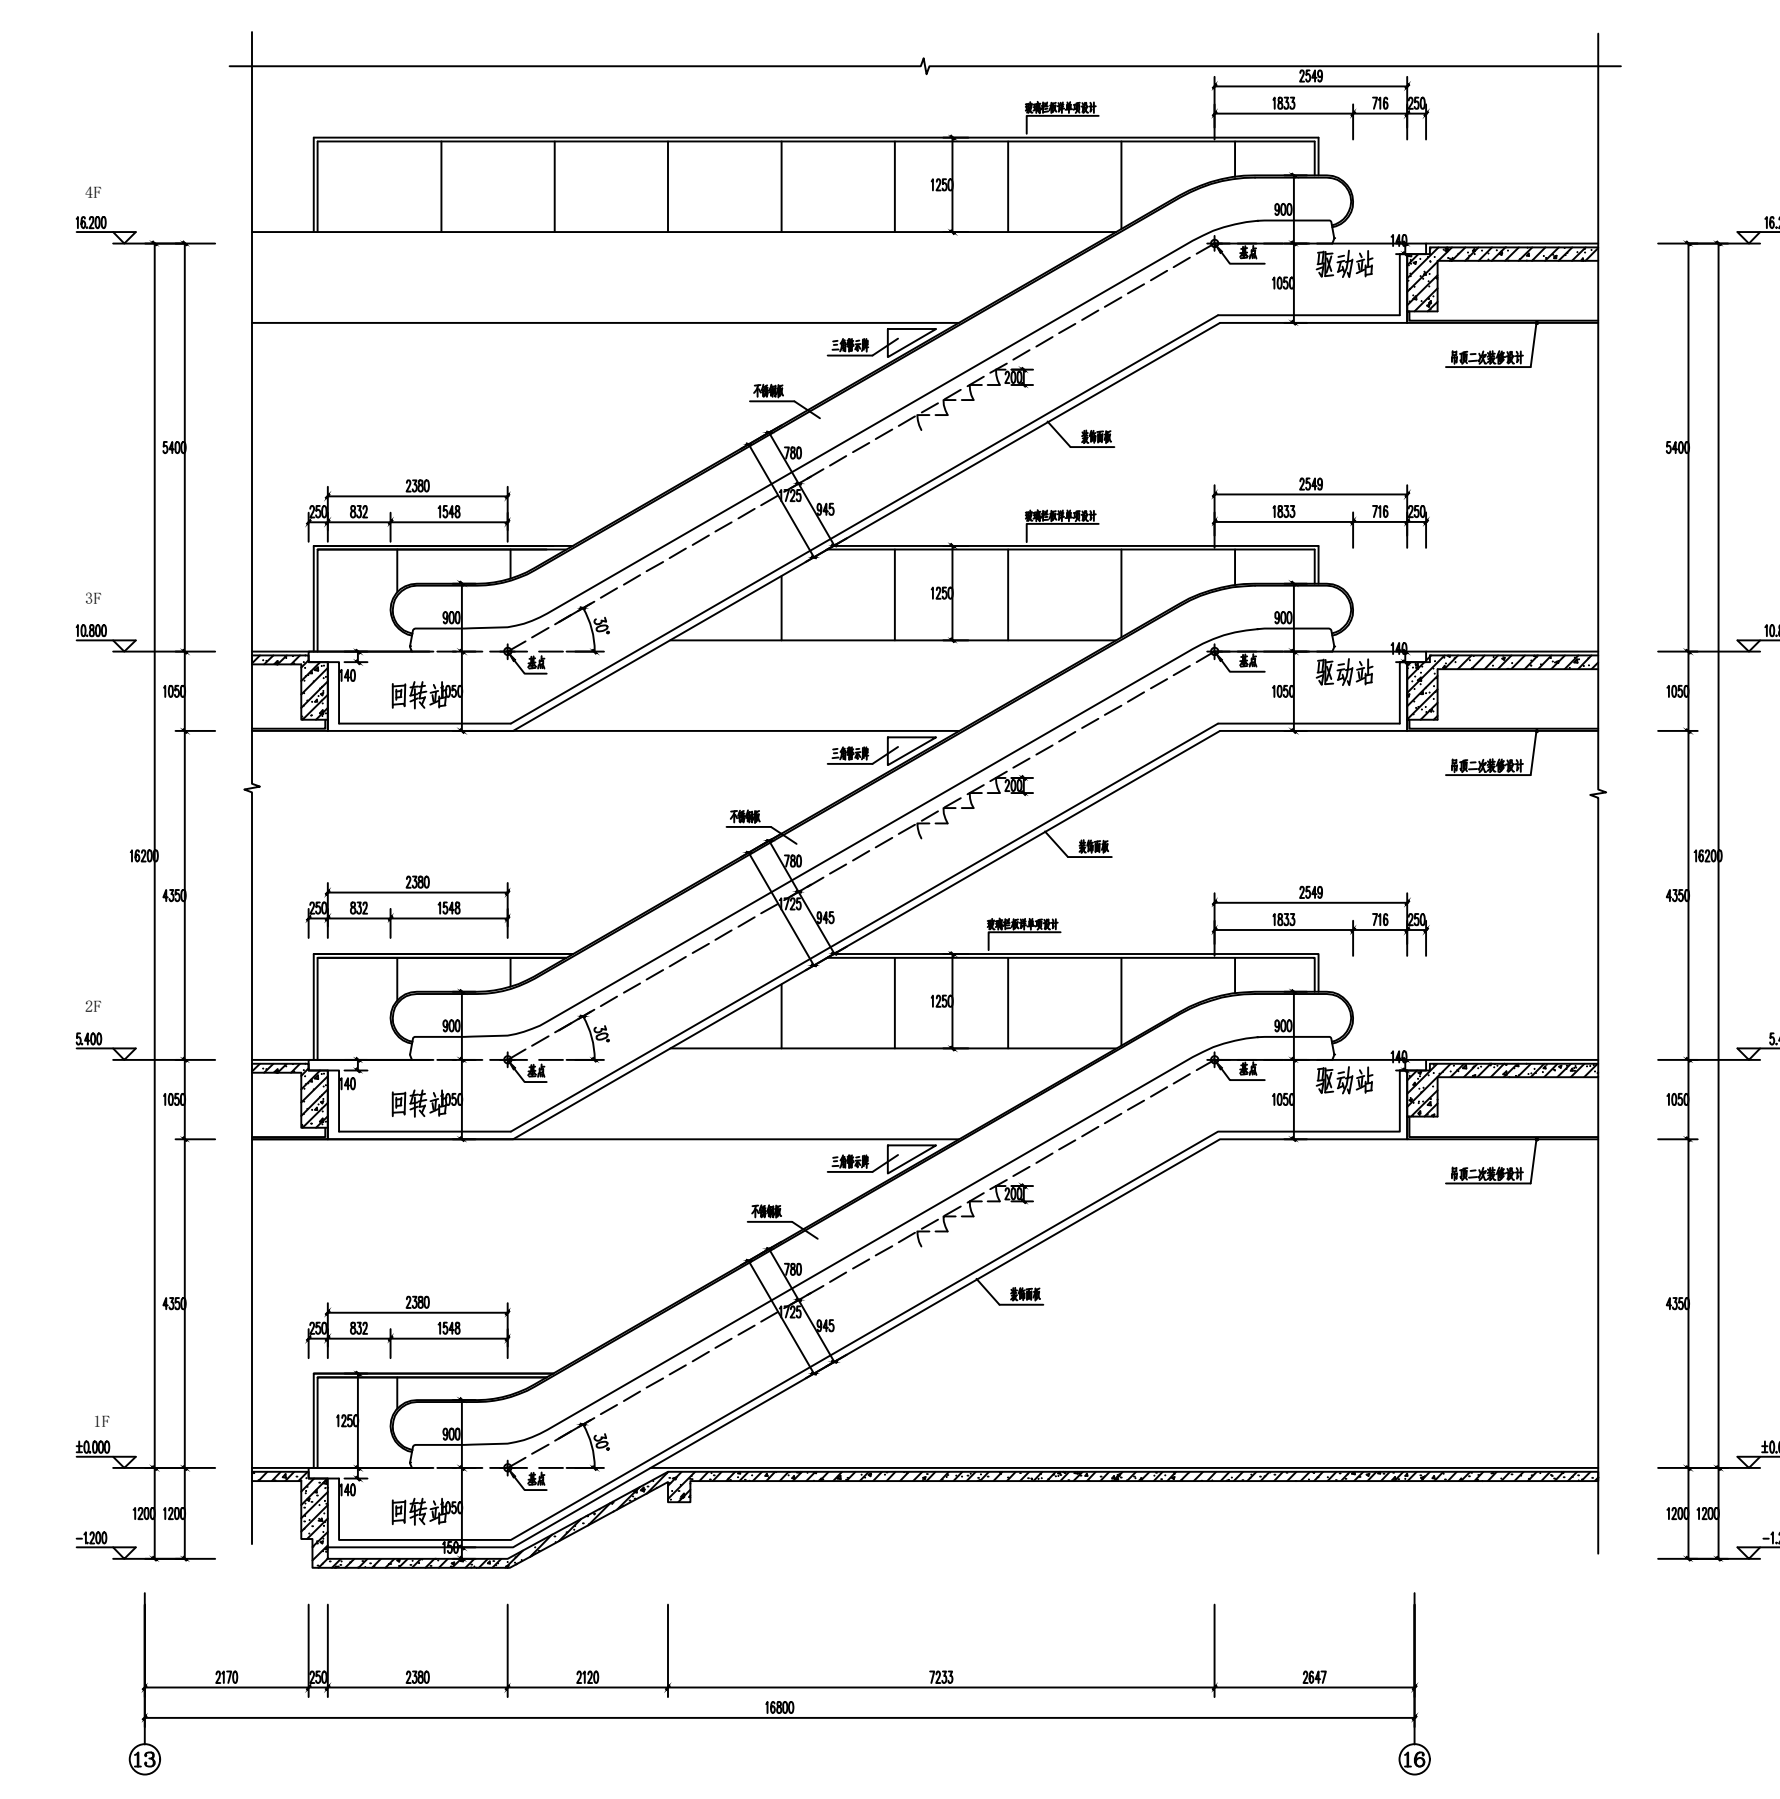


FT-01自动扶梯剖面图 1:50

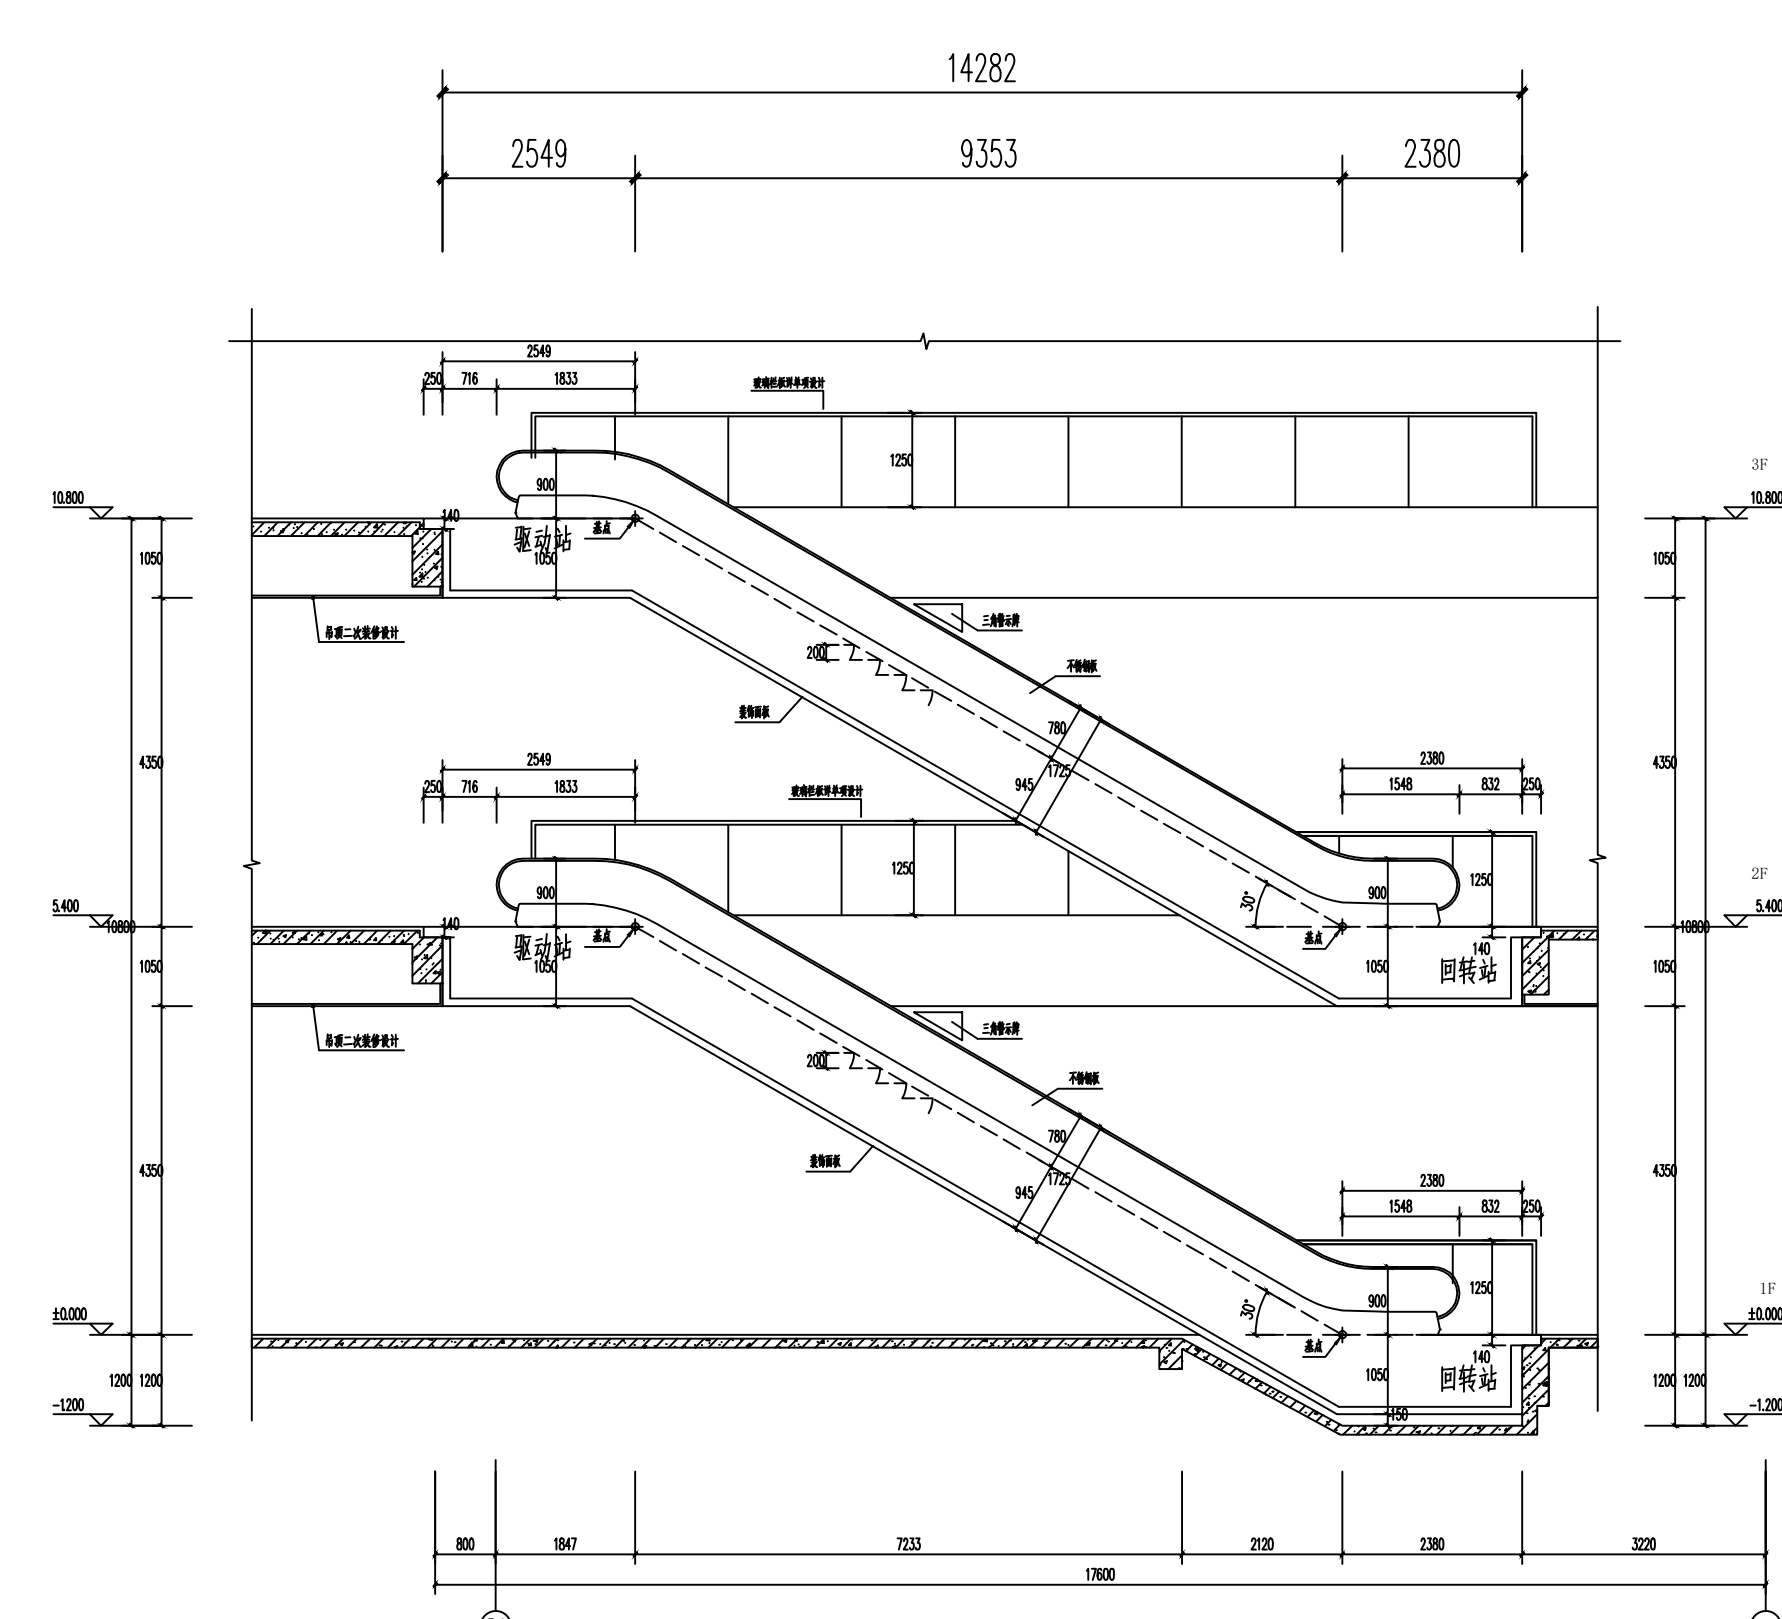


FT-02自动扶梯剖面图 1:5

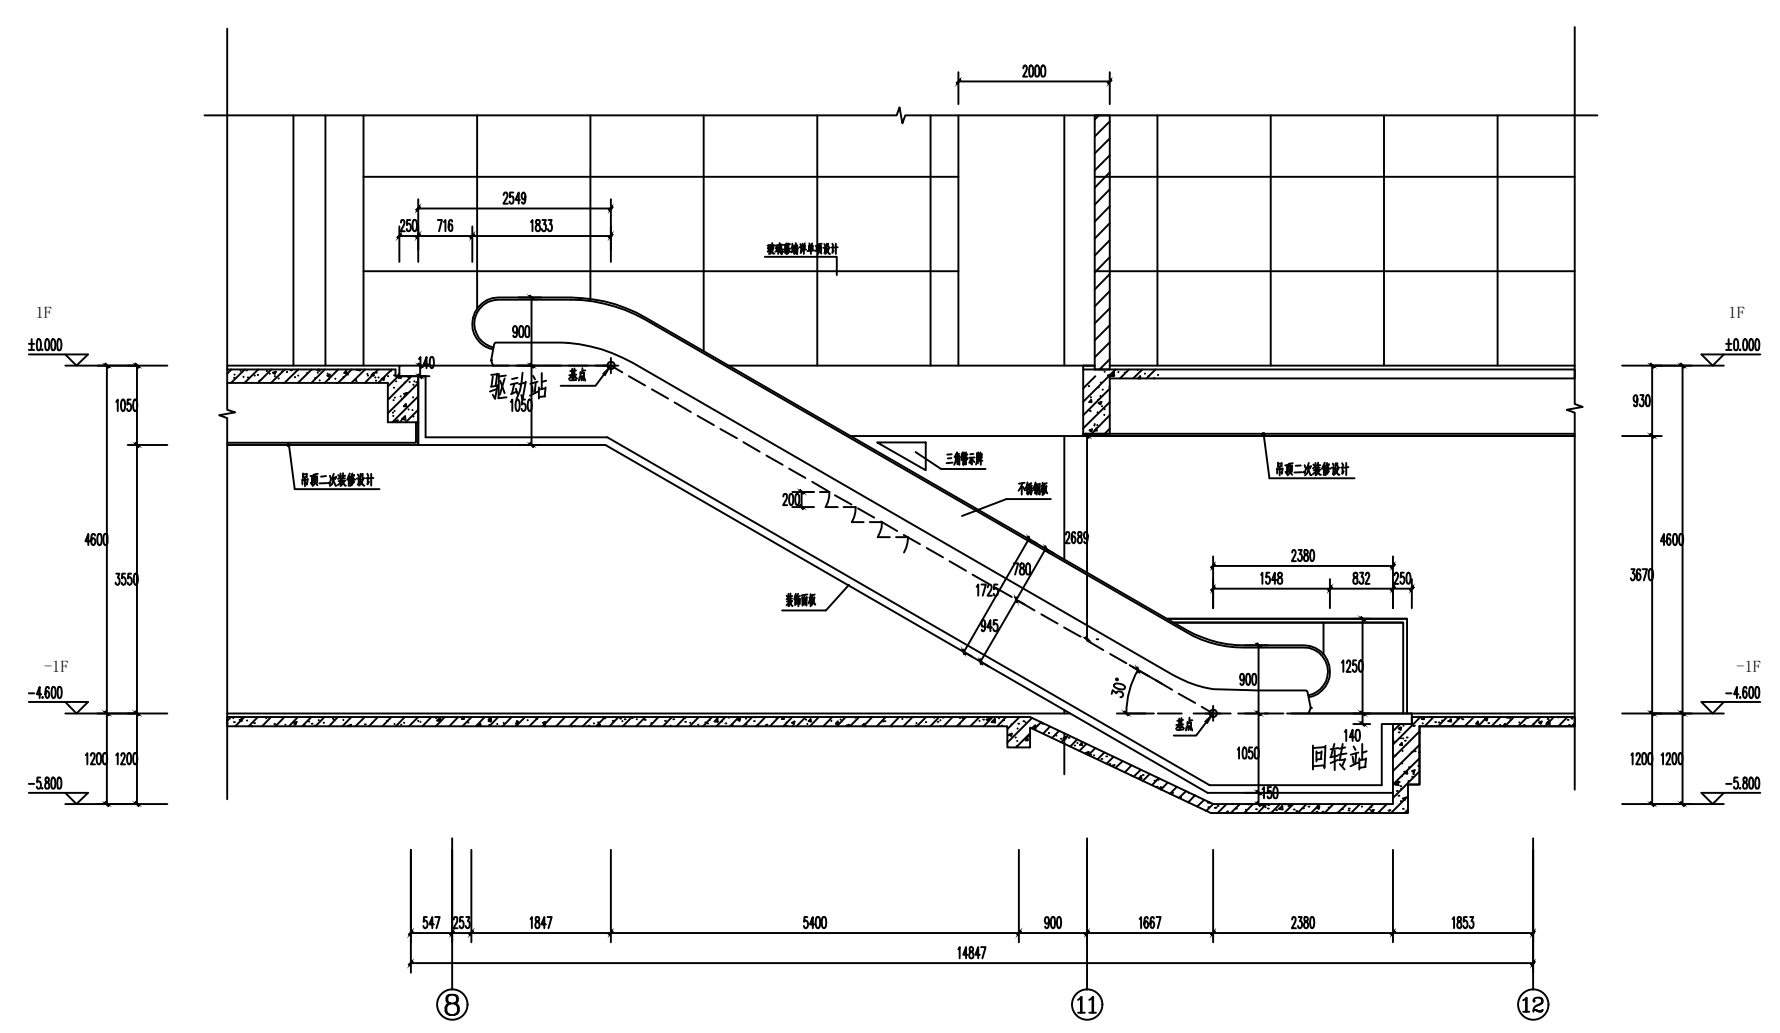


FT-03自动扶梯剖面图 1:5

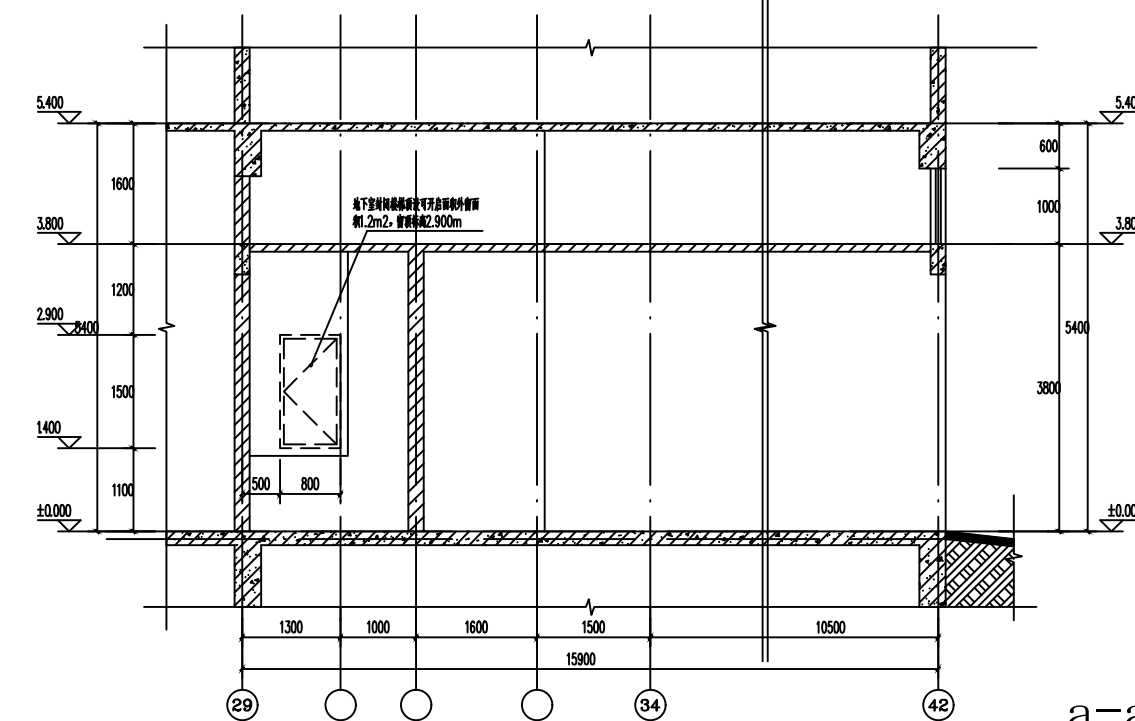

a-a剖面图 1:100

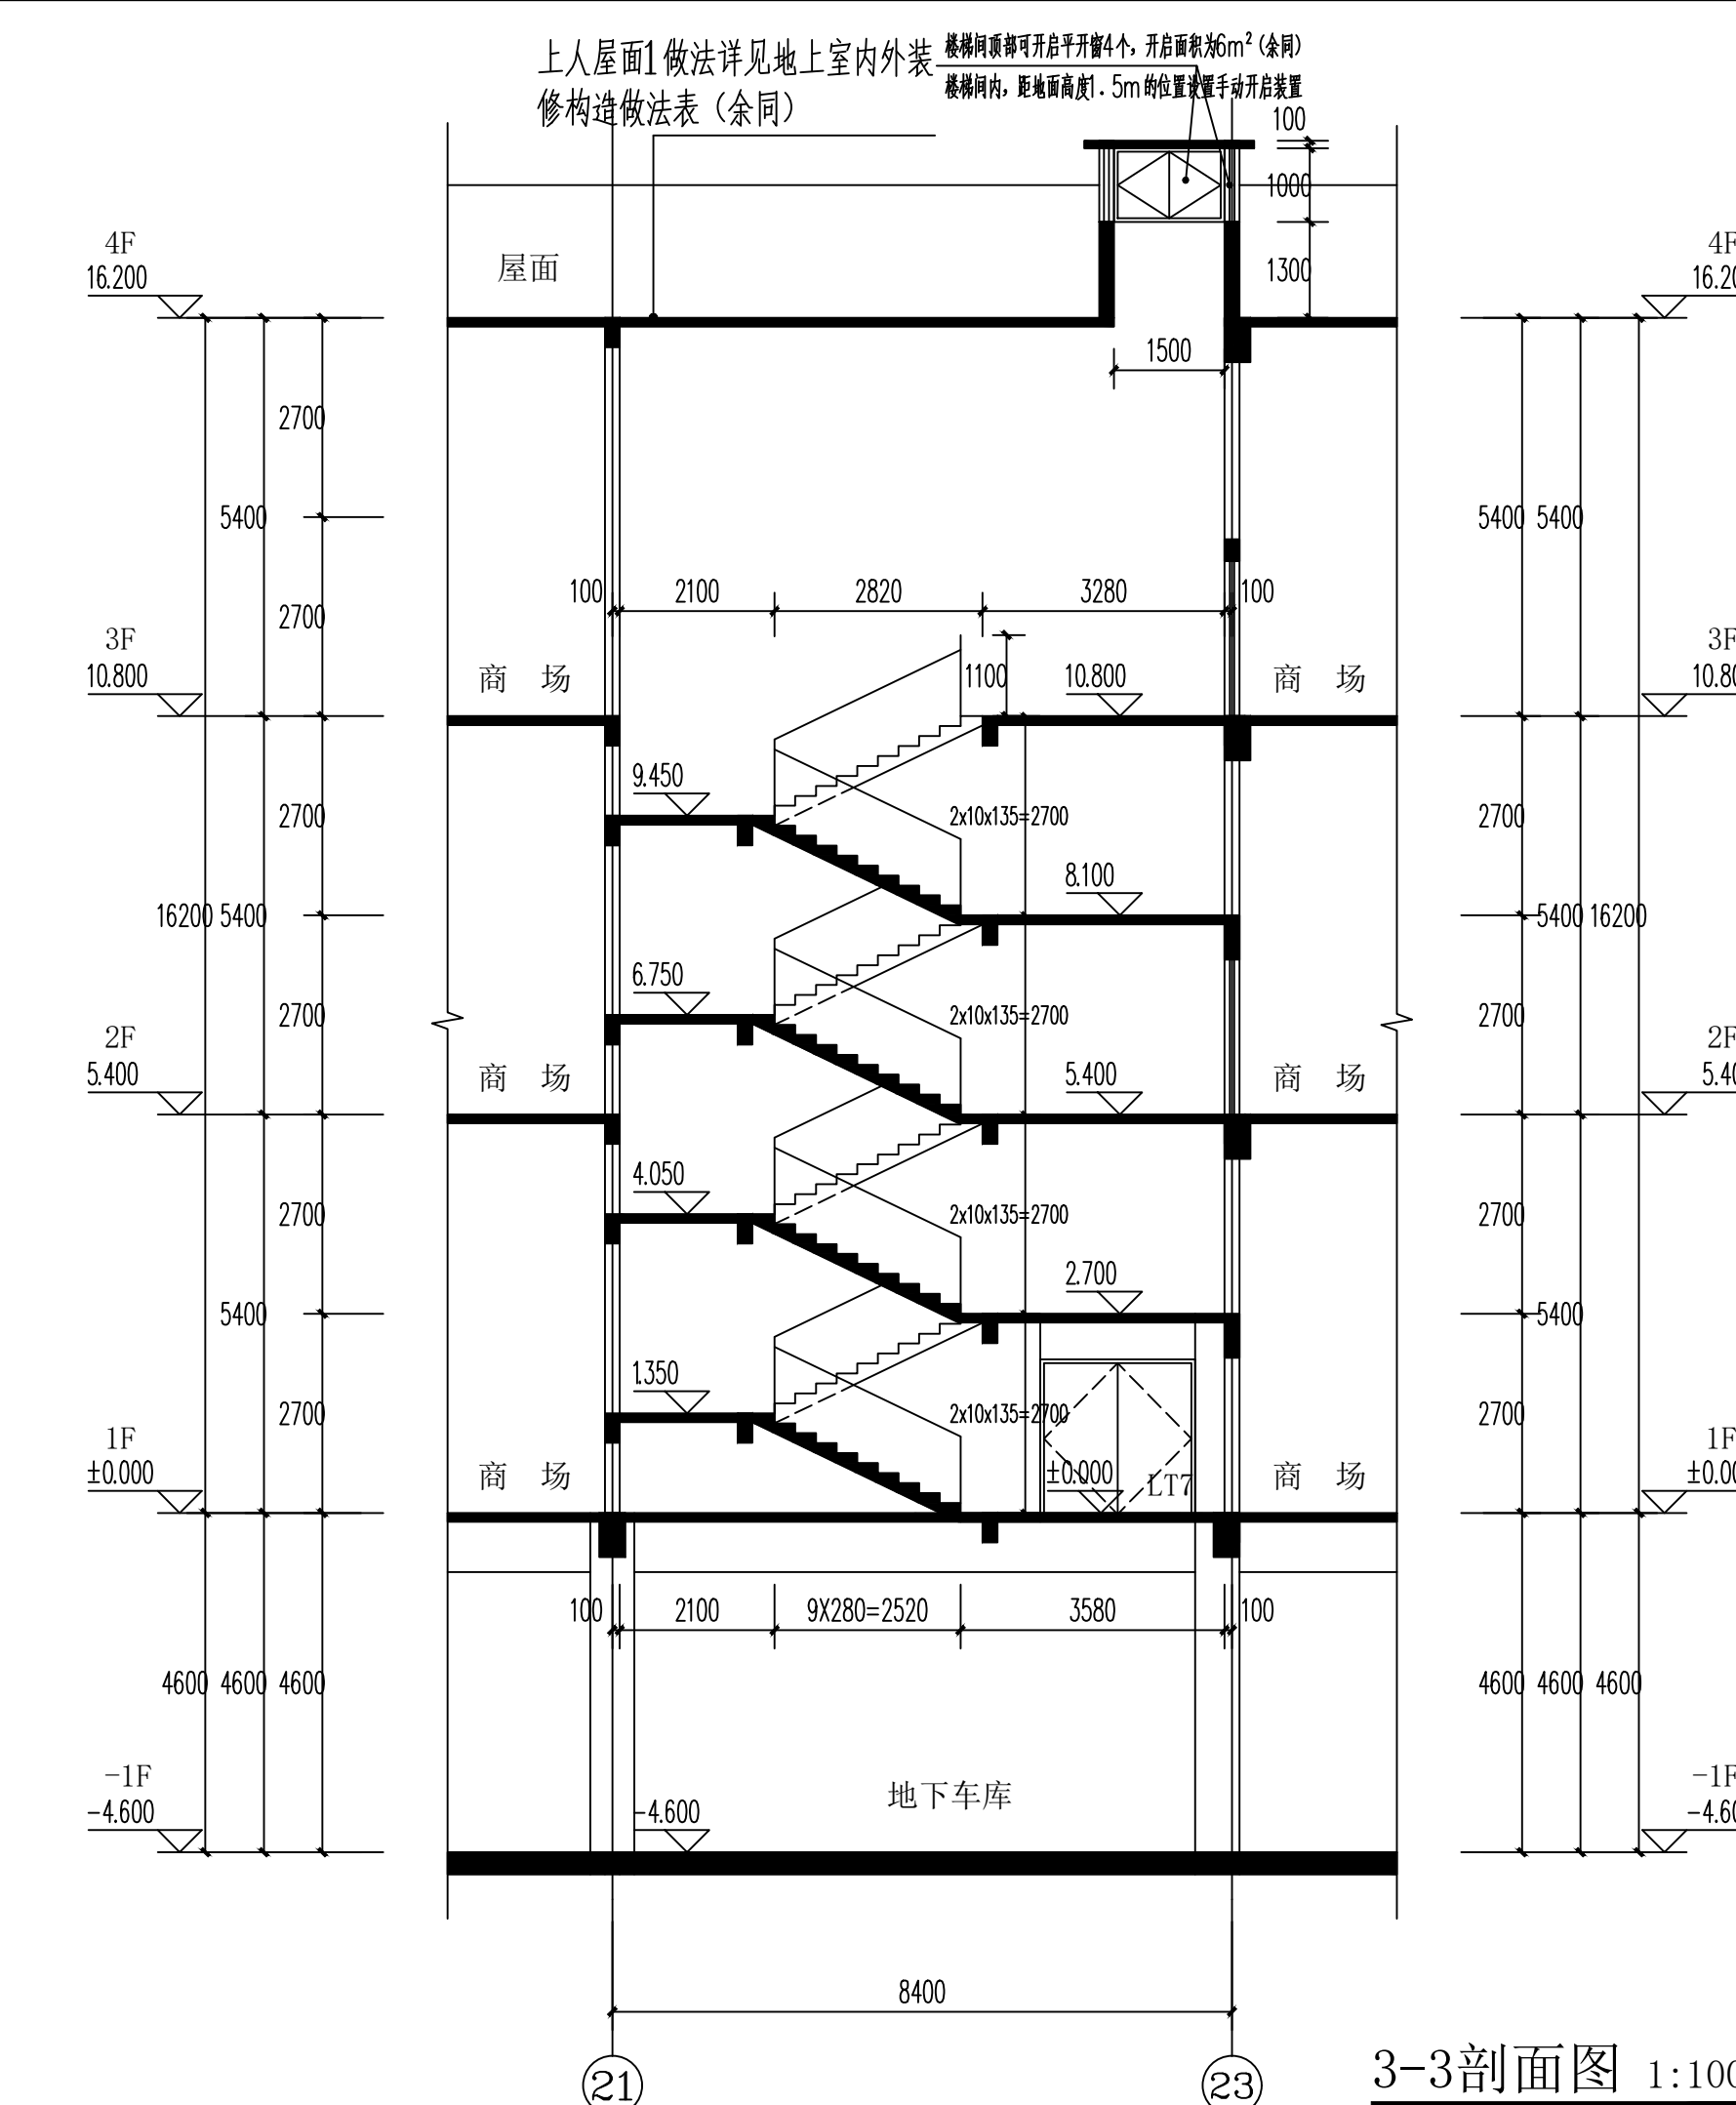

3-3剖面图 1:100

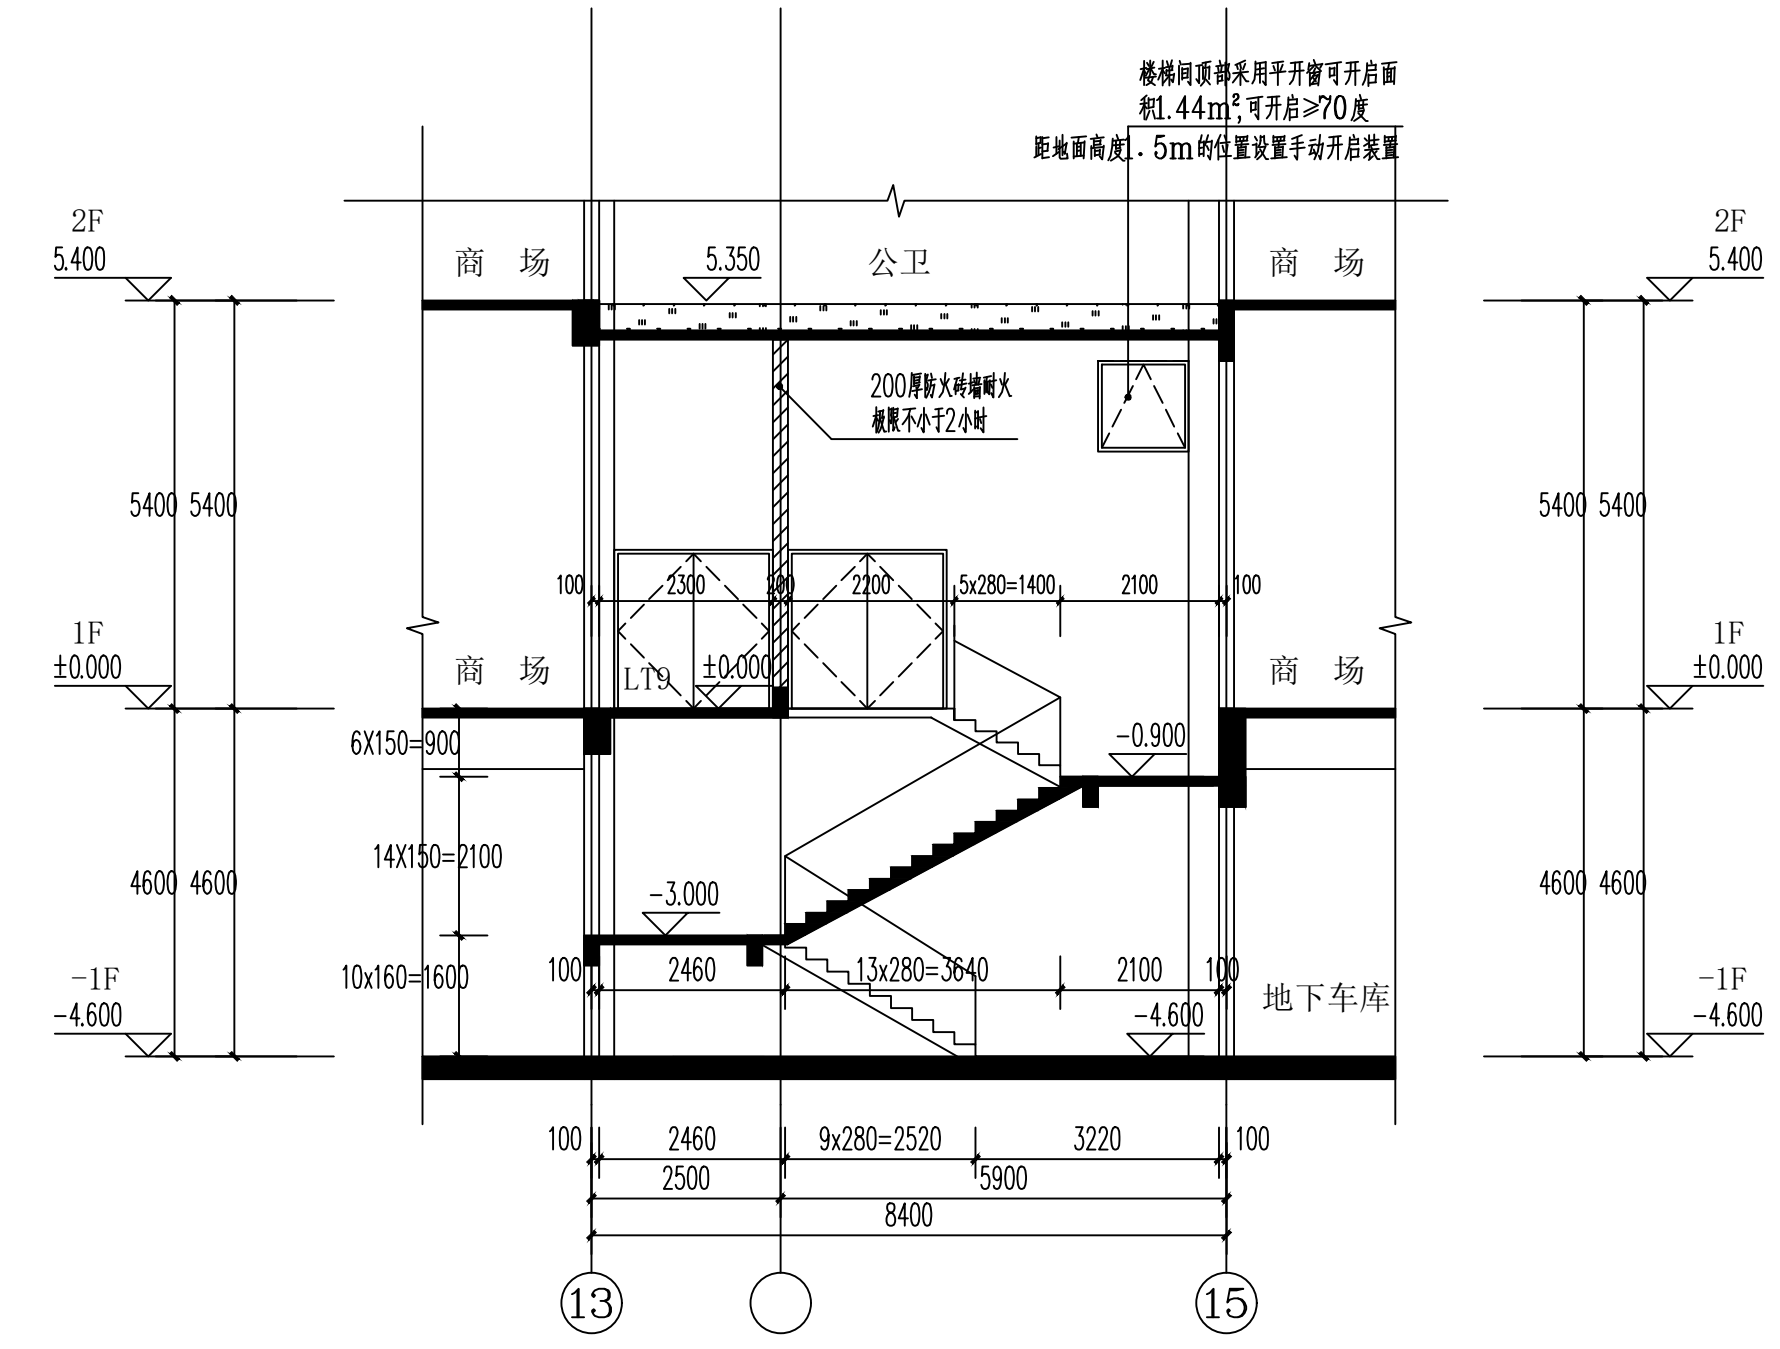

5-5剖面图 1:100

注：LT9剖面图

1.本工程楼梯踏步高、宽、步数及平台宽度等详楼梯大样。楼梯栏杆采用不锈钢栏杆900高,详11ZJ401-13-W扶手详11ZJ401-37-16。(注:当扶手水平长度大于0.5m时,栏杆高度不低于1100)。
2.起步详11ZJ40138-6;扶手与填充墙连接详11ZJ401-42-5,防滑详05ZJ401-39-6
3.梯井大于110,均做防坠网处理。

建设单位/CLIENT:

麻阳苗族自治县远桥房地产开发有限公司

项目名称/PROJECT:
远程国际

子项目名称/SUB-PROJECT:

远程国际

区位图/REGIONAL LOCATION MAP :



图纸名称/TITLE:

车道1-1剖面
自动扶梯剖面图、a-a剖面图
3-3剖面图、5-5剖面图

项目名称/PROJECT:

远程国际

设计 DESIGNED	古新辉	
校对 CHECKED	吴新红	
专业负责人 CHIEF	吴志刚	
项目负责人 PROJECT CHIEF	吴志刚	
审核 IDENTIFIED	黄履优	
审定 APPROVED	李 坚	

业务号/JOB NO.

设计阶段/STATUS: 施工图

专业/DISCIPLINE: 建施

比例/ SCALE:	1: 100	规格/ SIZE:	A1
---------------	--------	--------------	----

出图日期/DATE: 2021.06

图号/DRAWING NO. JS-25

版次 NO.	修改内容 DESCRIPTION	日期 DATE
-----------	---------------------	------------

条形码/BARCODE:

版权所有，不得复制、套用。
ALL RIGHTS RESERVED. DON'T COPIED, REPRODUCED.