




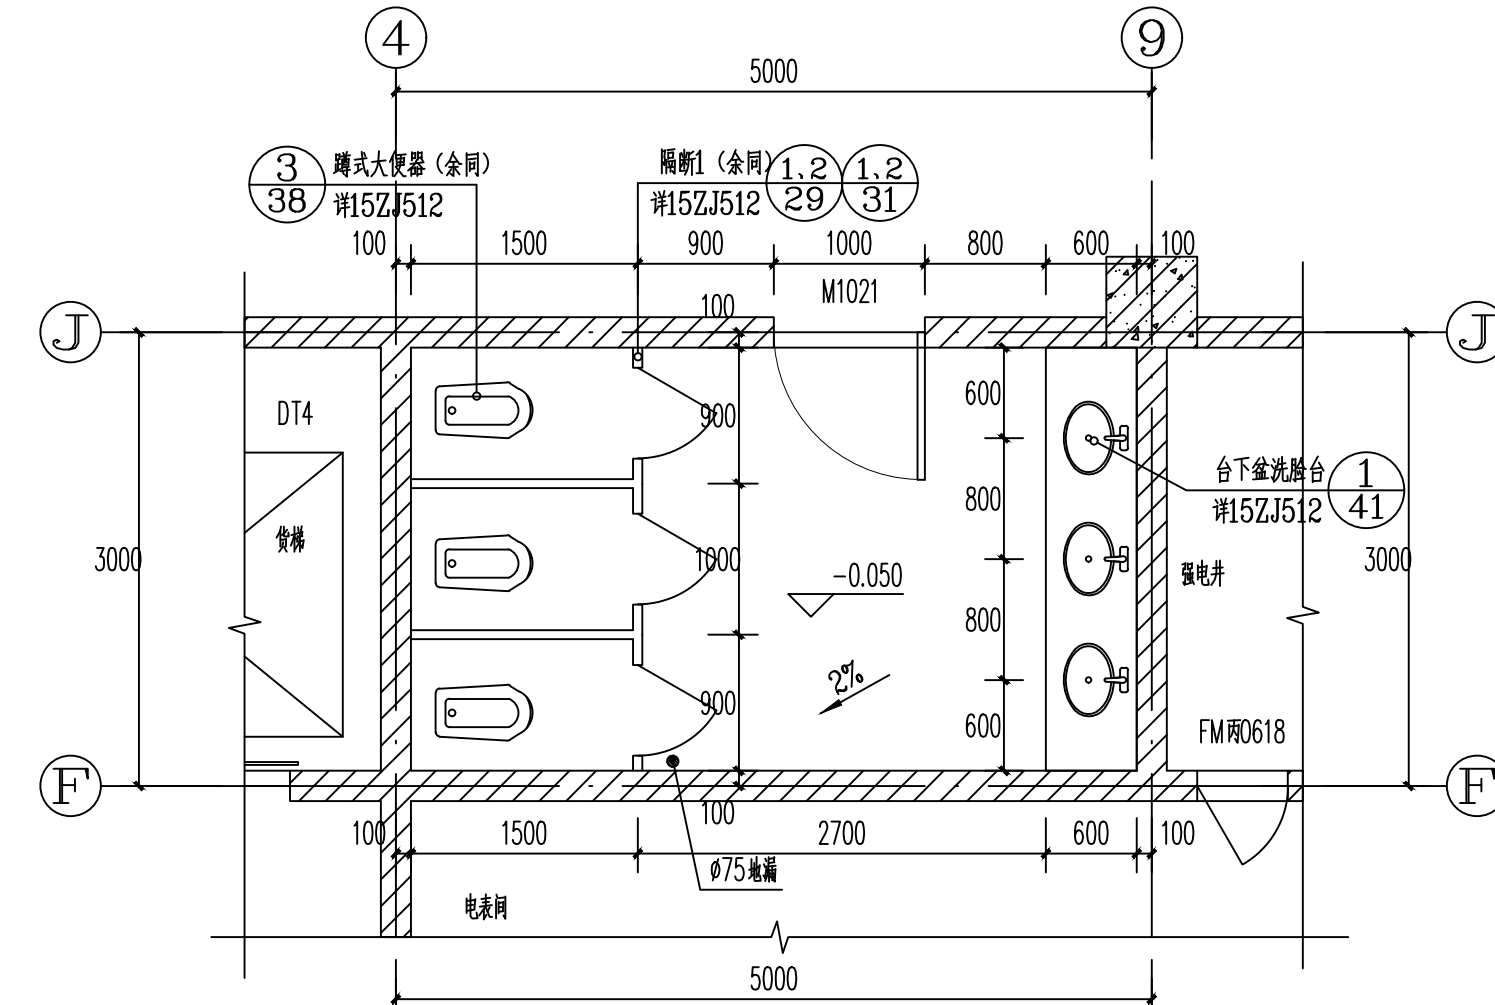


① 公卫一大样图 1:50

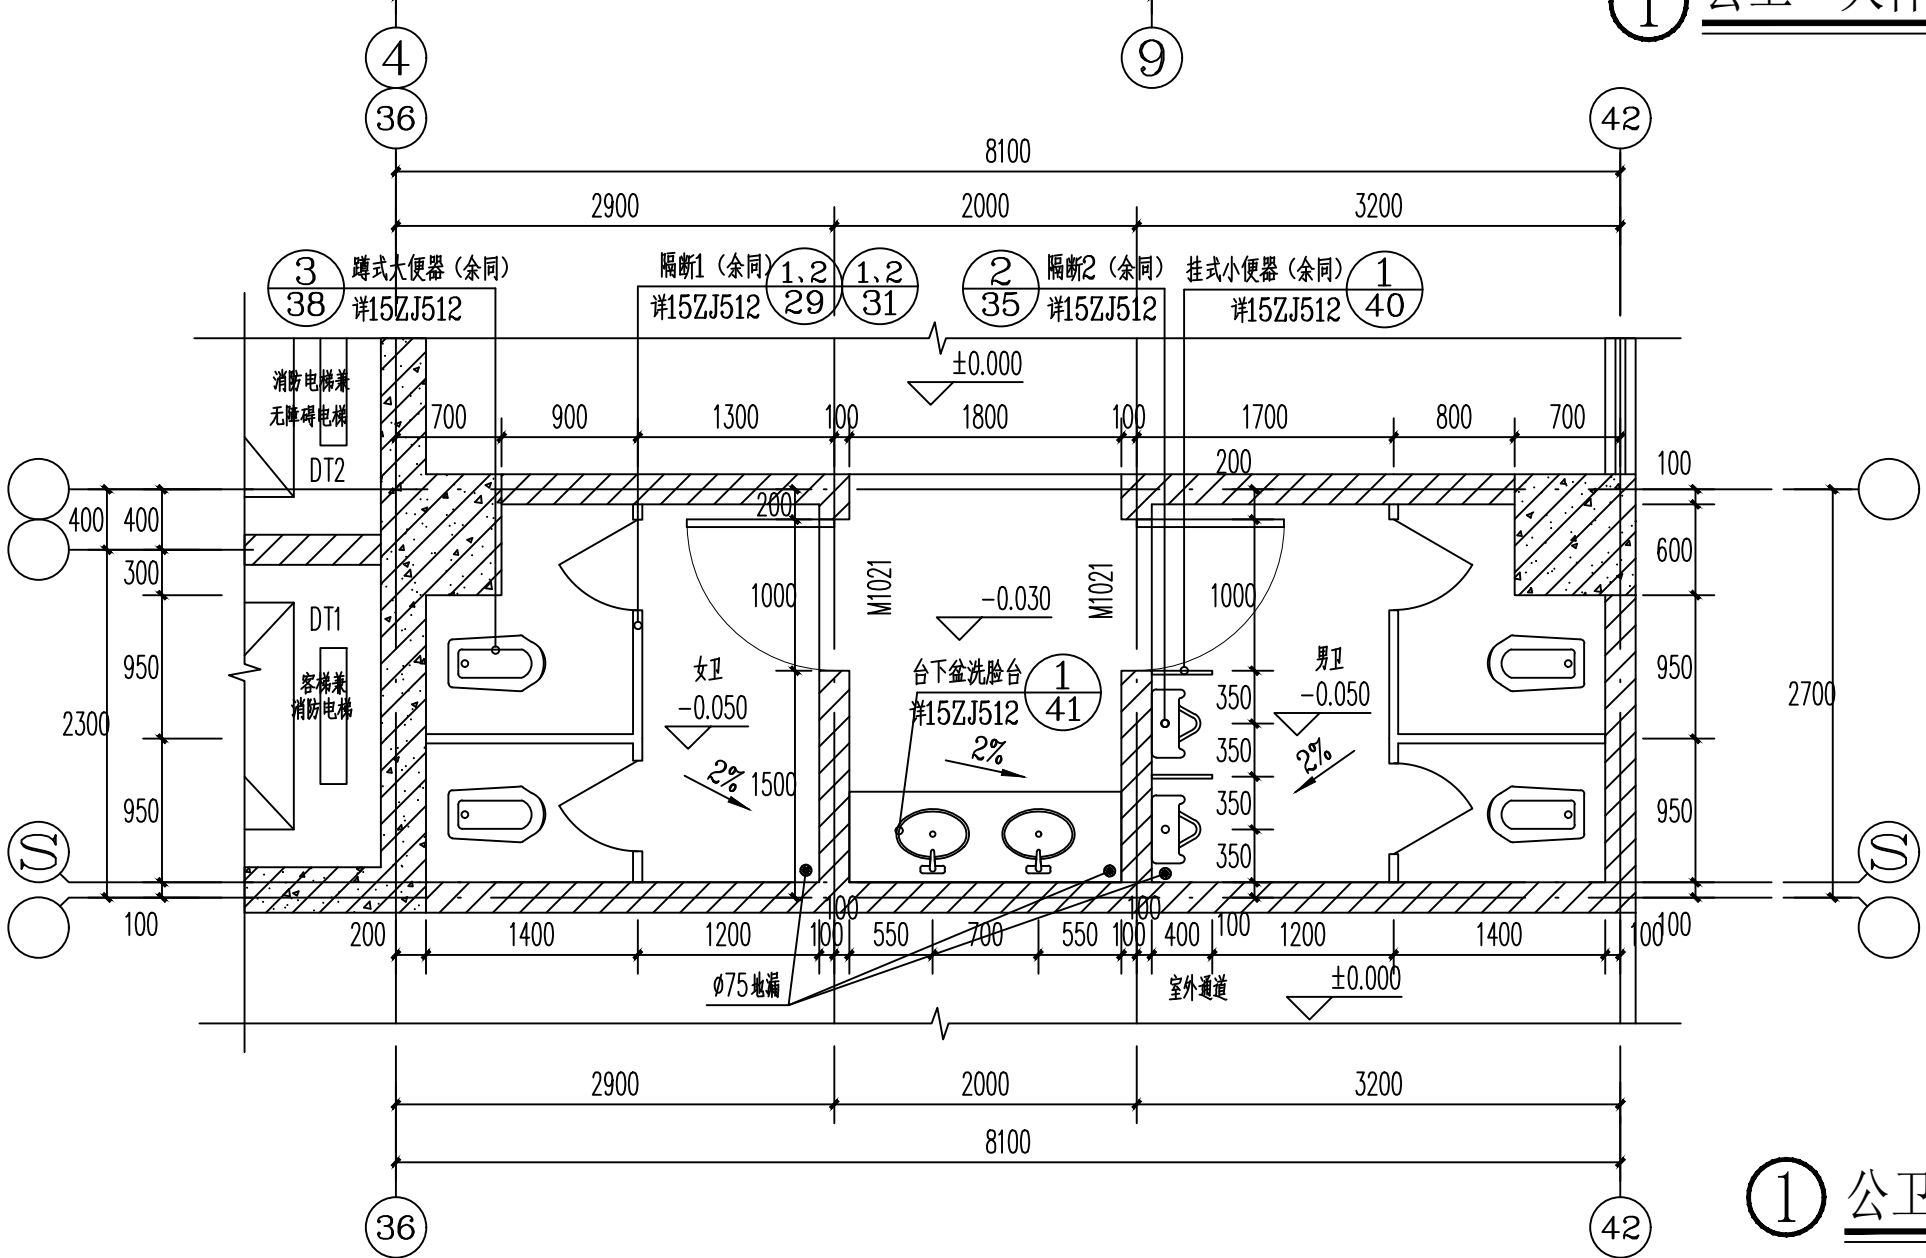


① 公卫二大样图 1:50

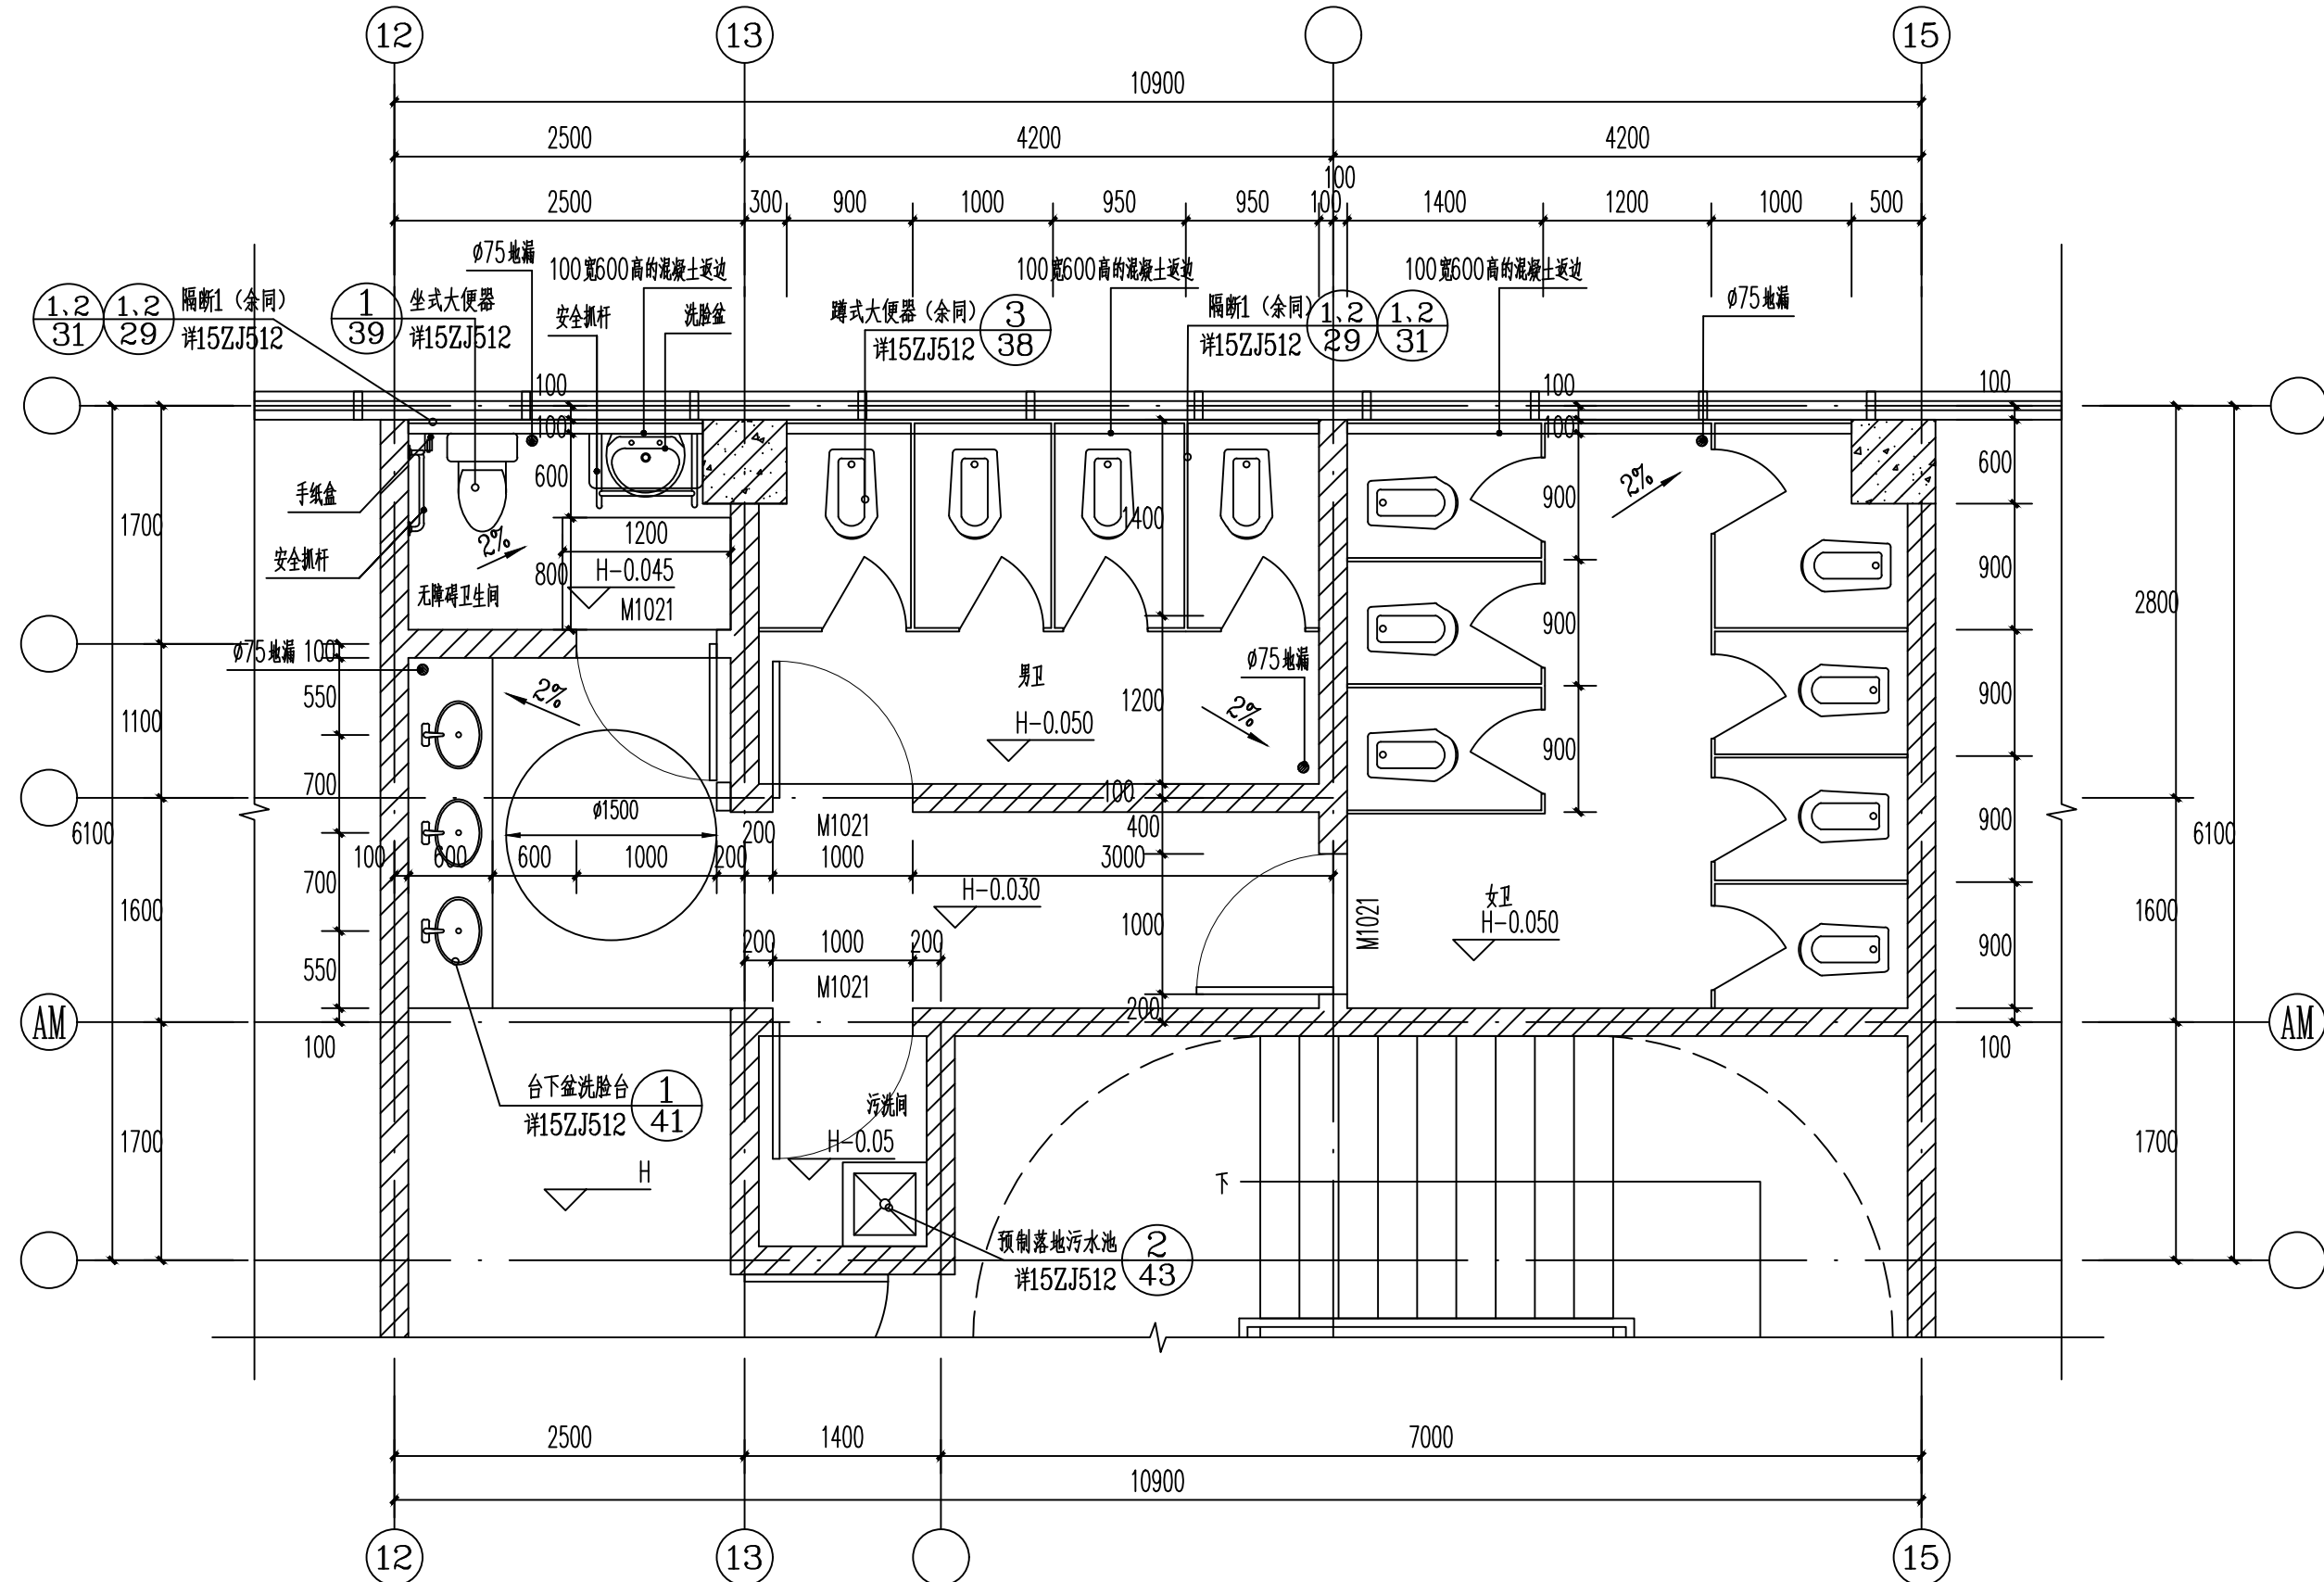


④ 公卫四大样图 1:50

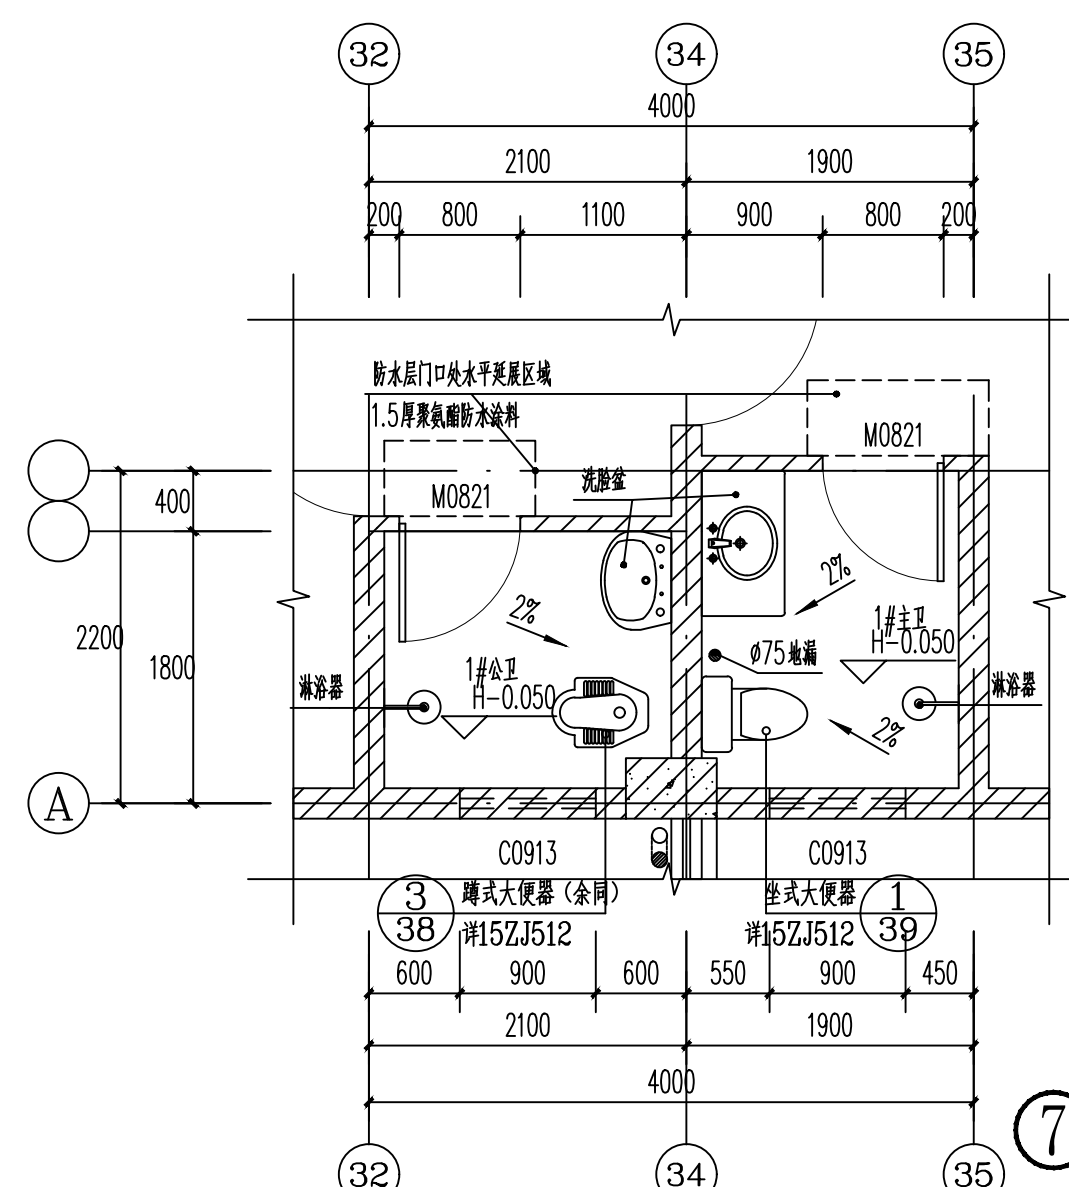


⑦ 1#公卫、1#主卫大样图 1:50

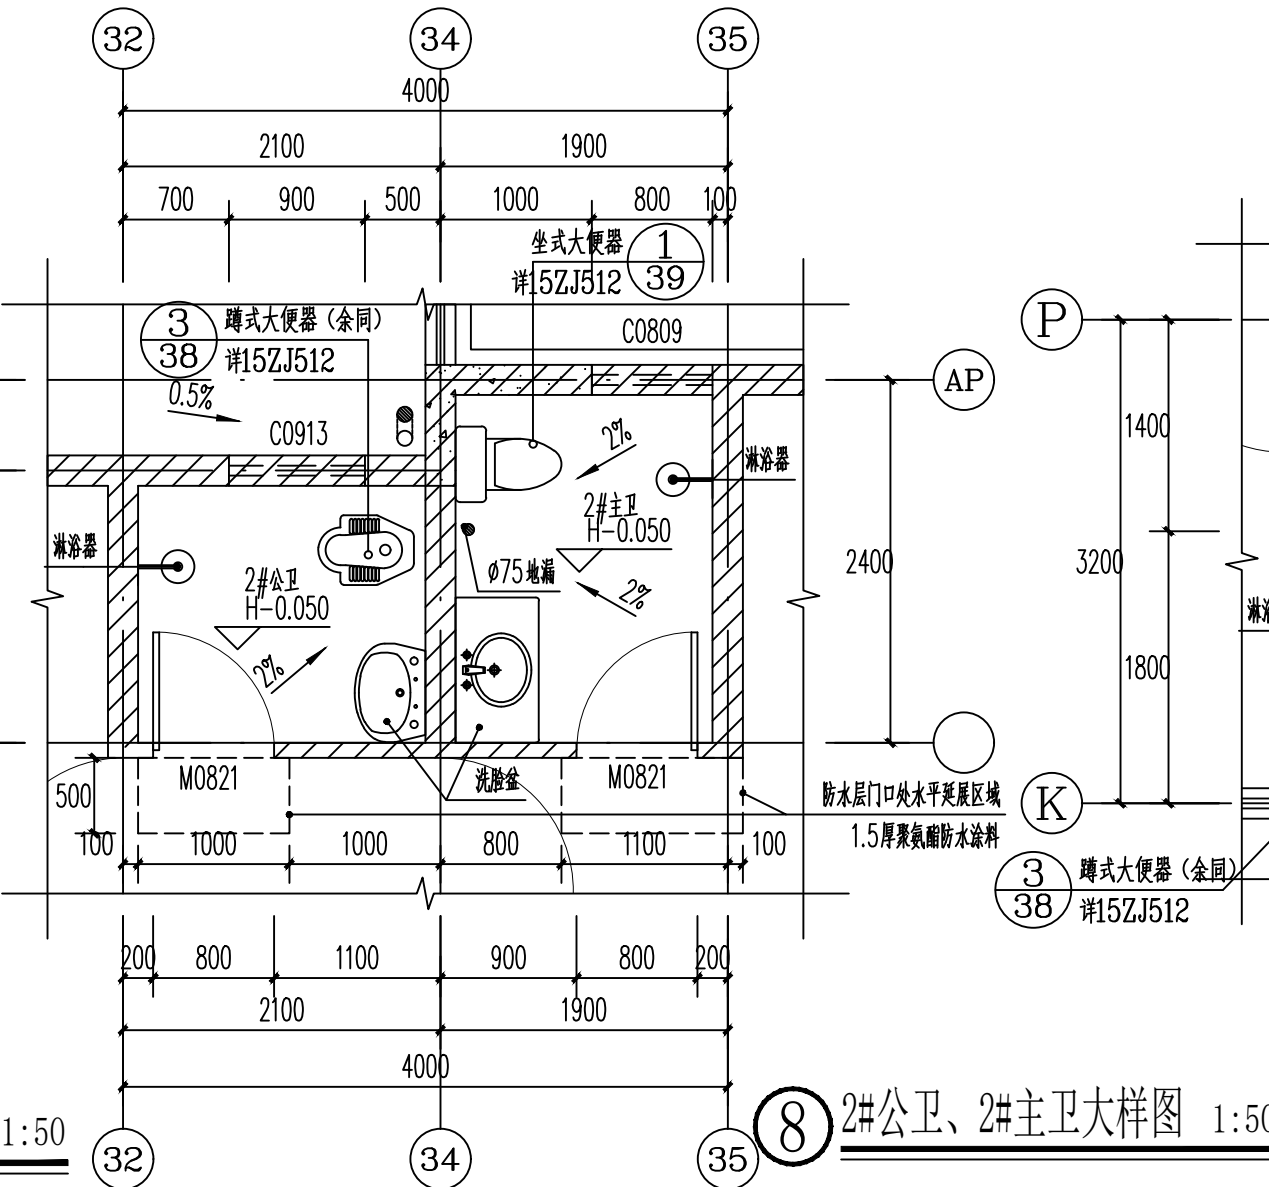


⑧ 2#公卫、2#主卫大样图 1:50

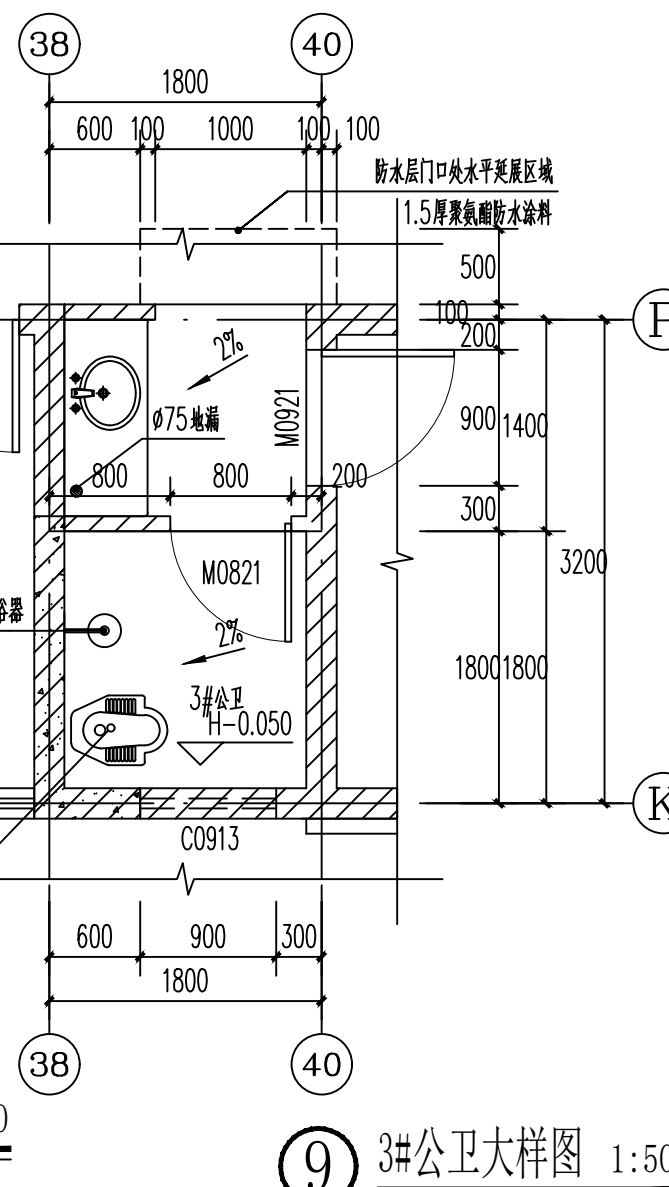


⑨ 3#公卫大样图 1:50

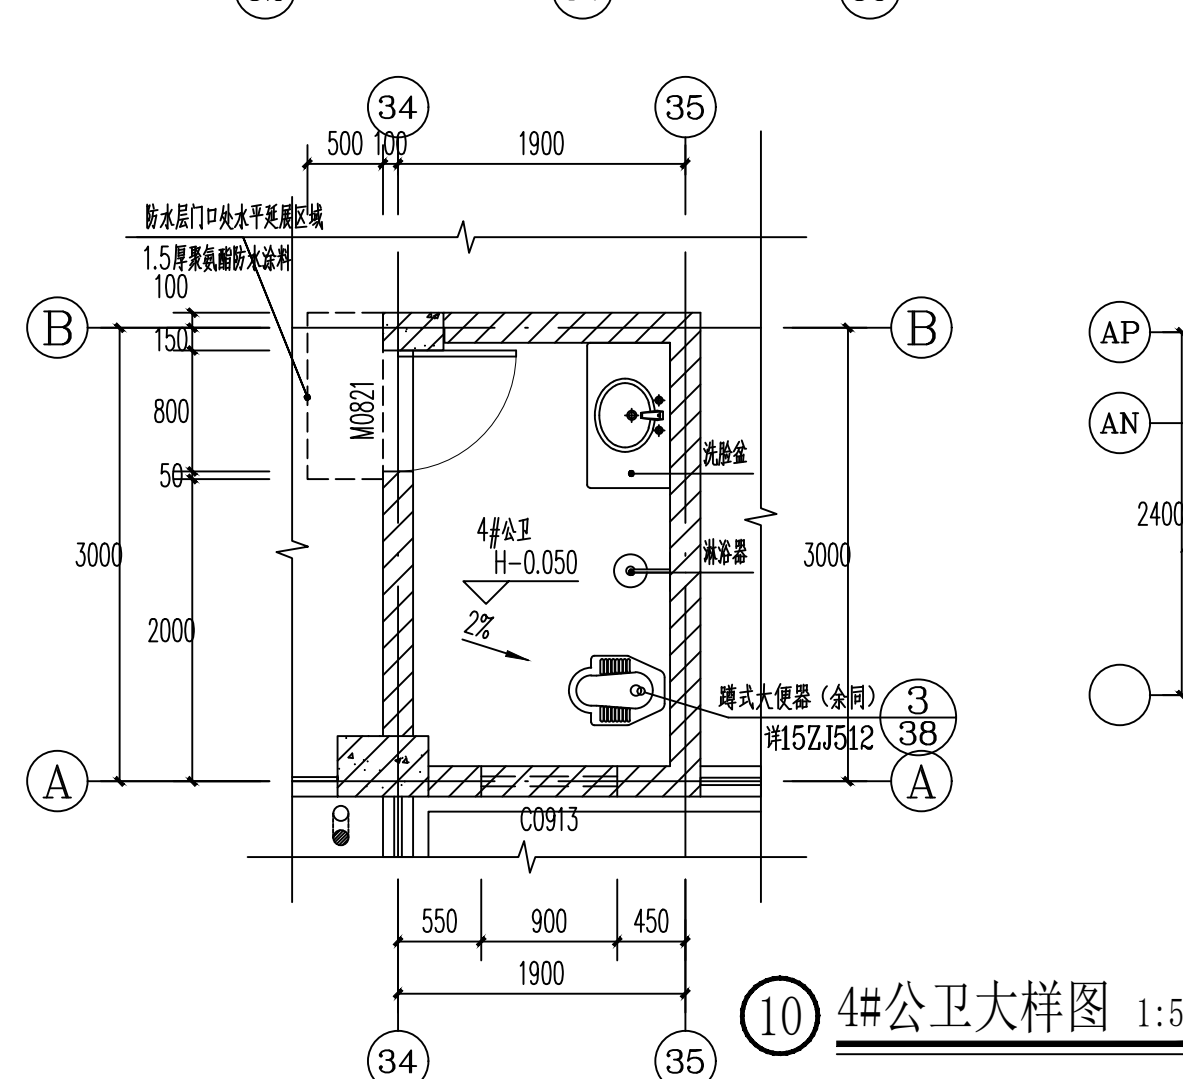


⑩ 4#公卫大样图 1:50

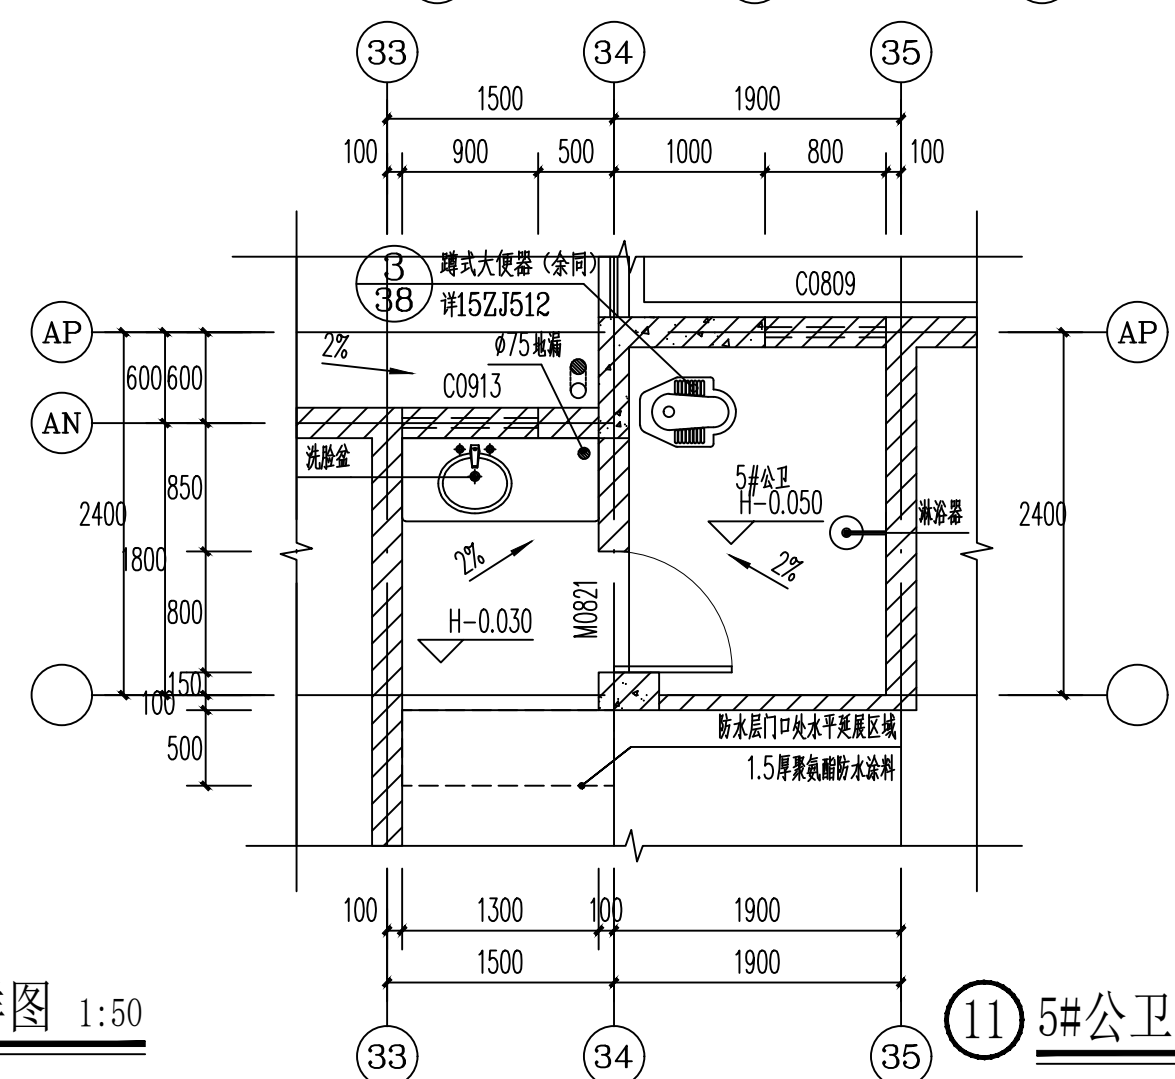


⑪ 5#公卫大样图 1:50

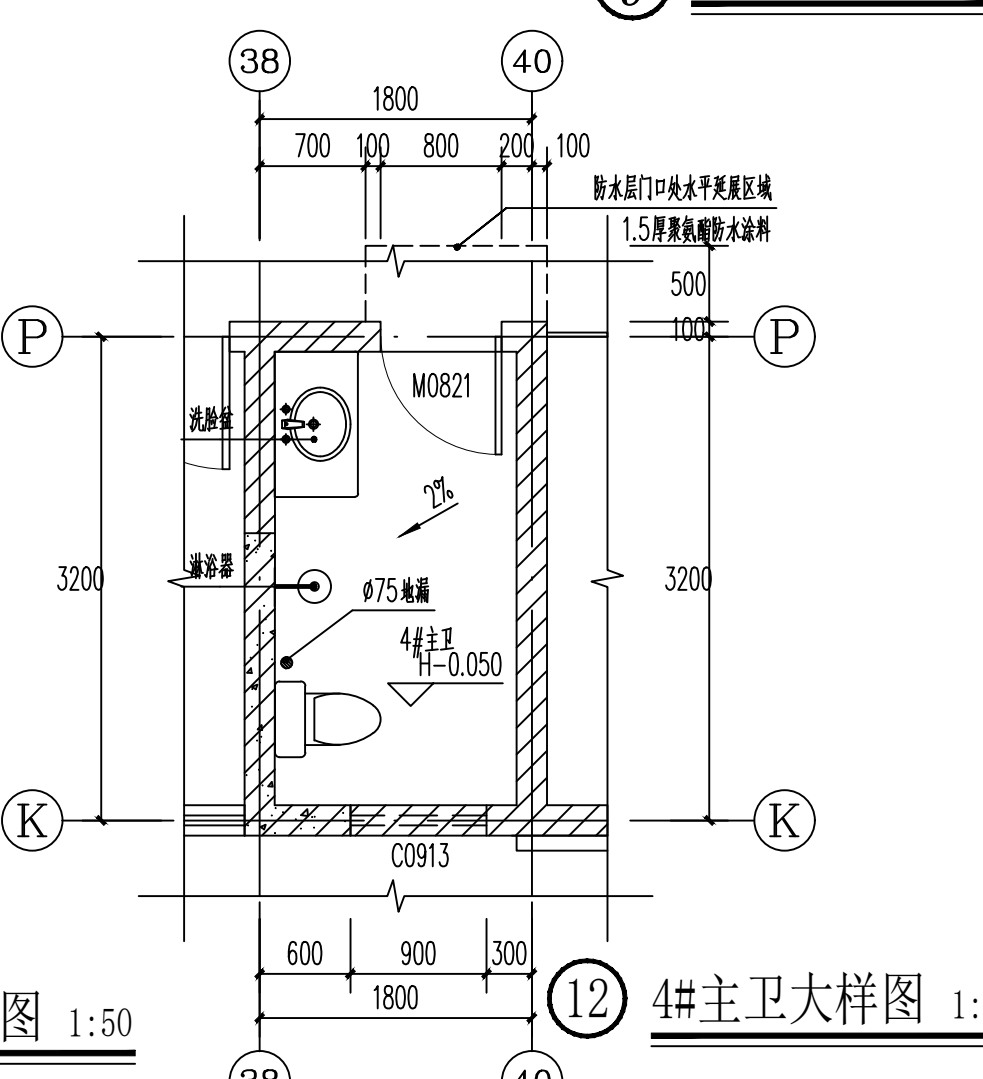


⑫ 4#主卫大样图 1:50

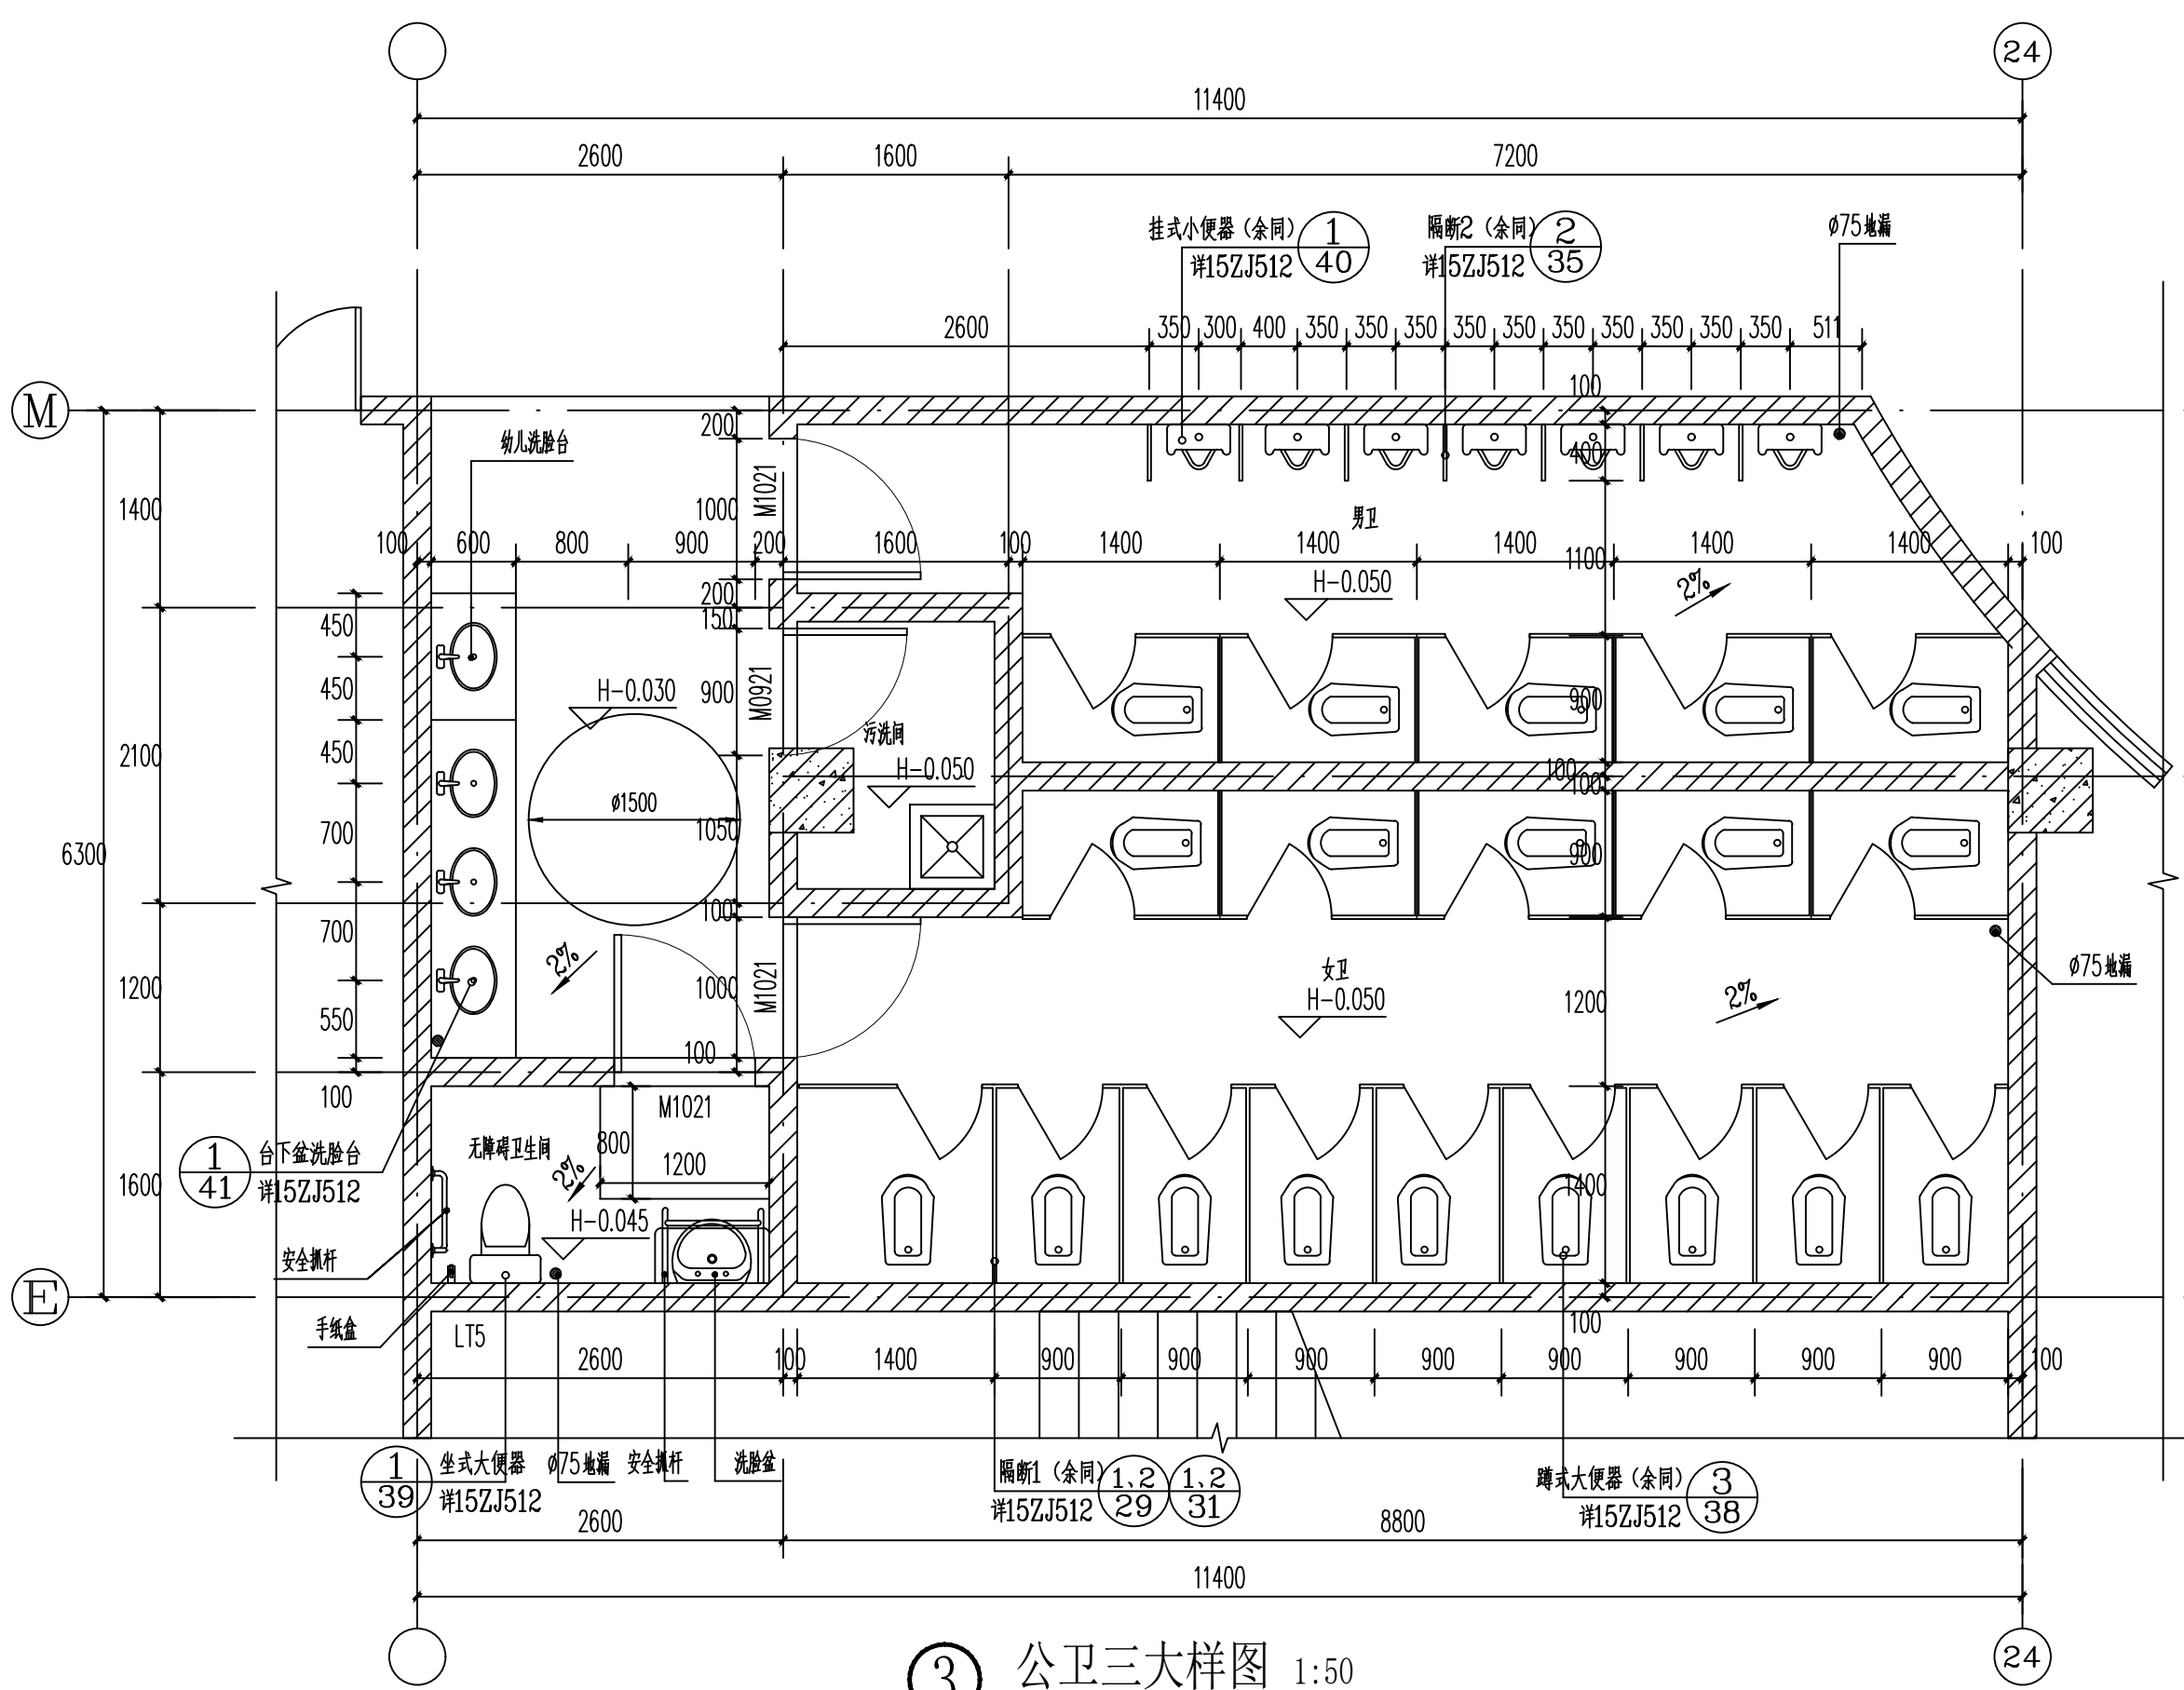

③ 公卫三大样图 1:50

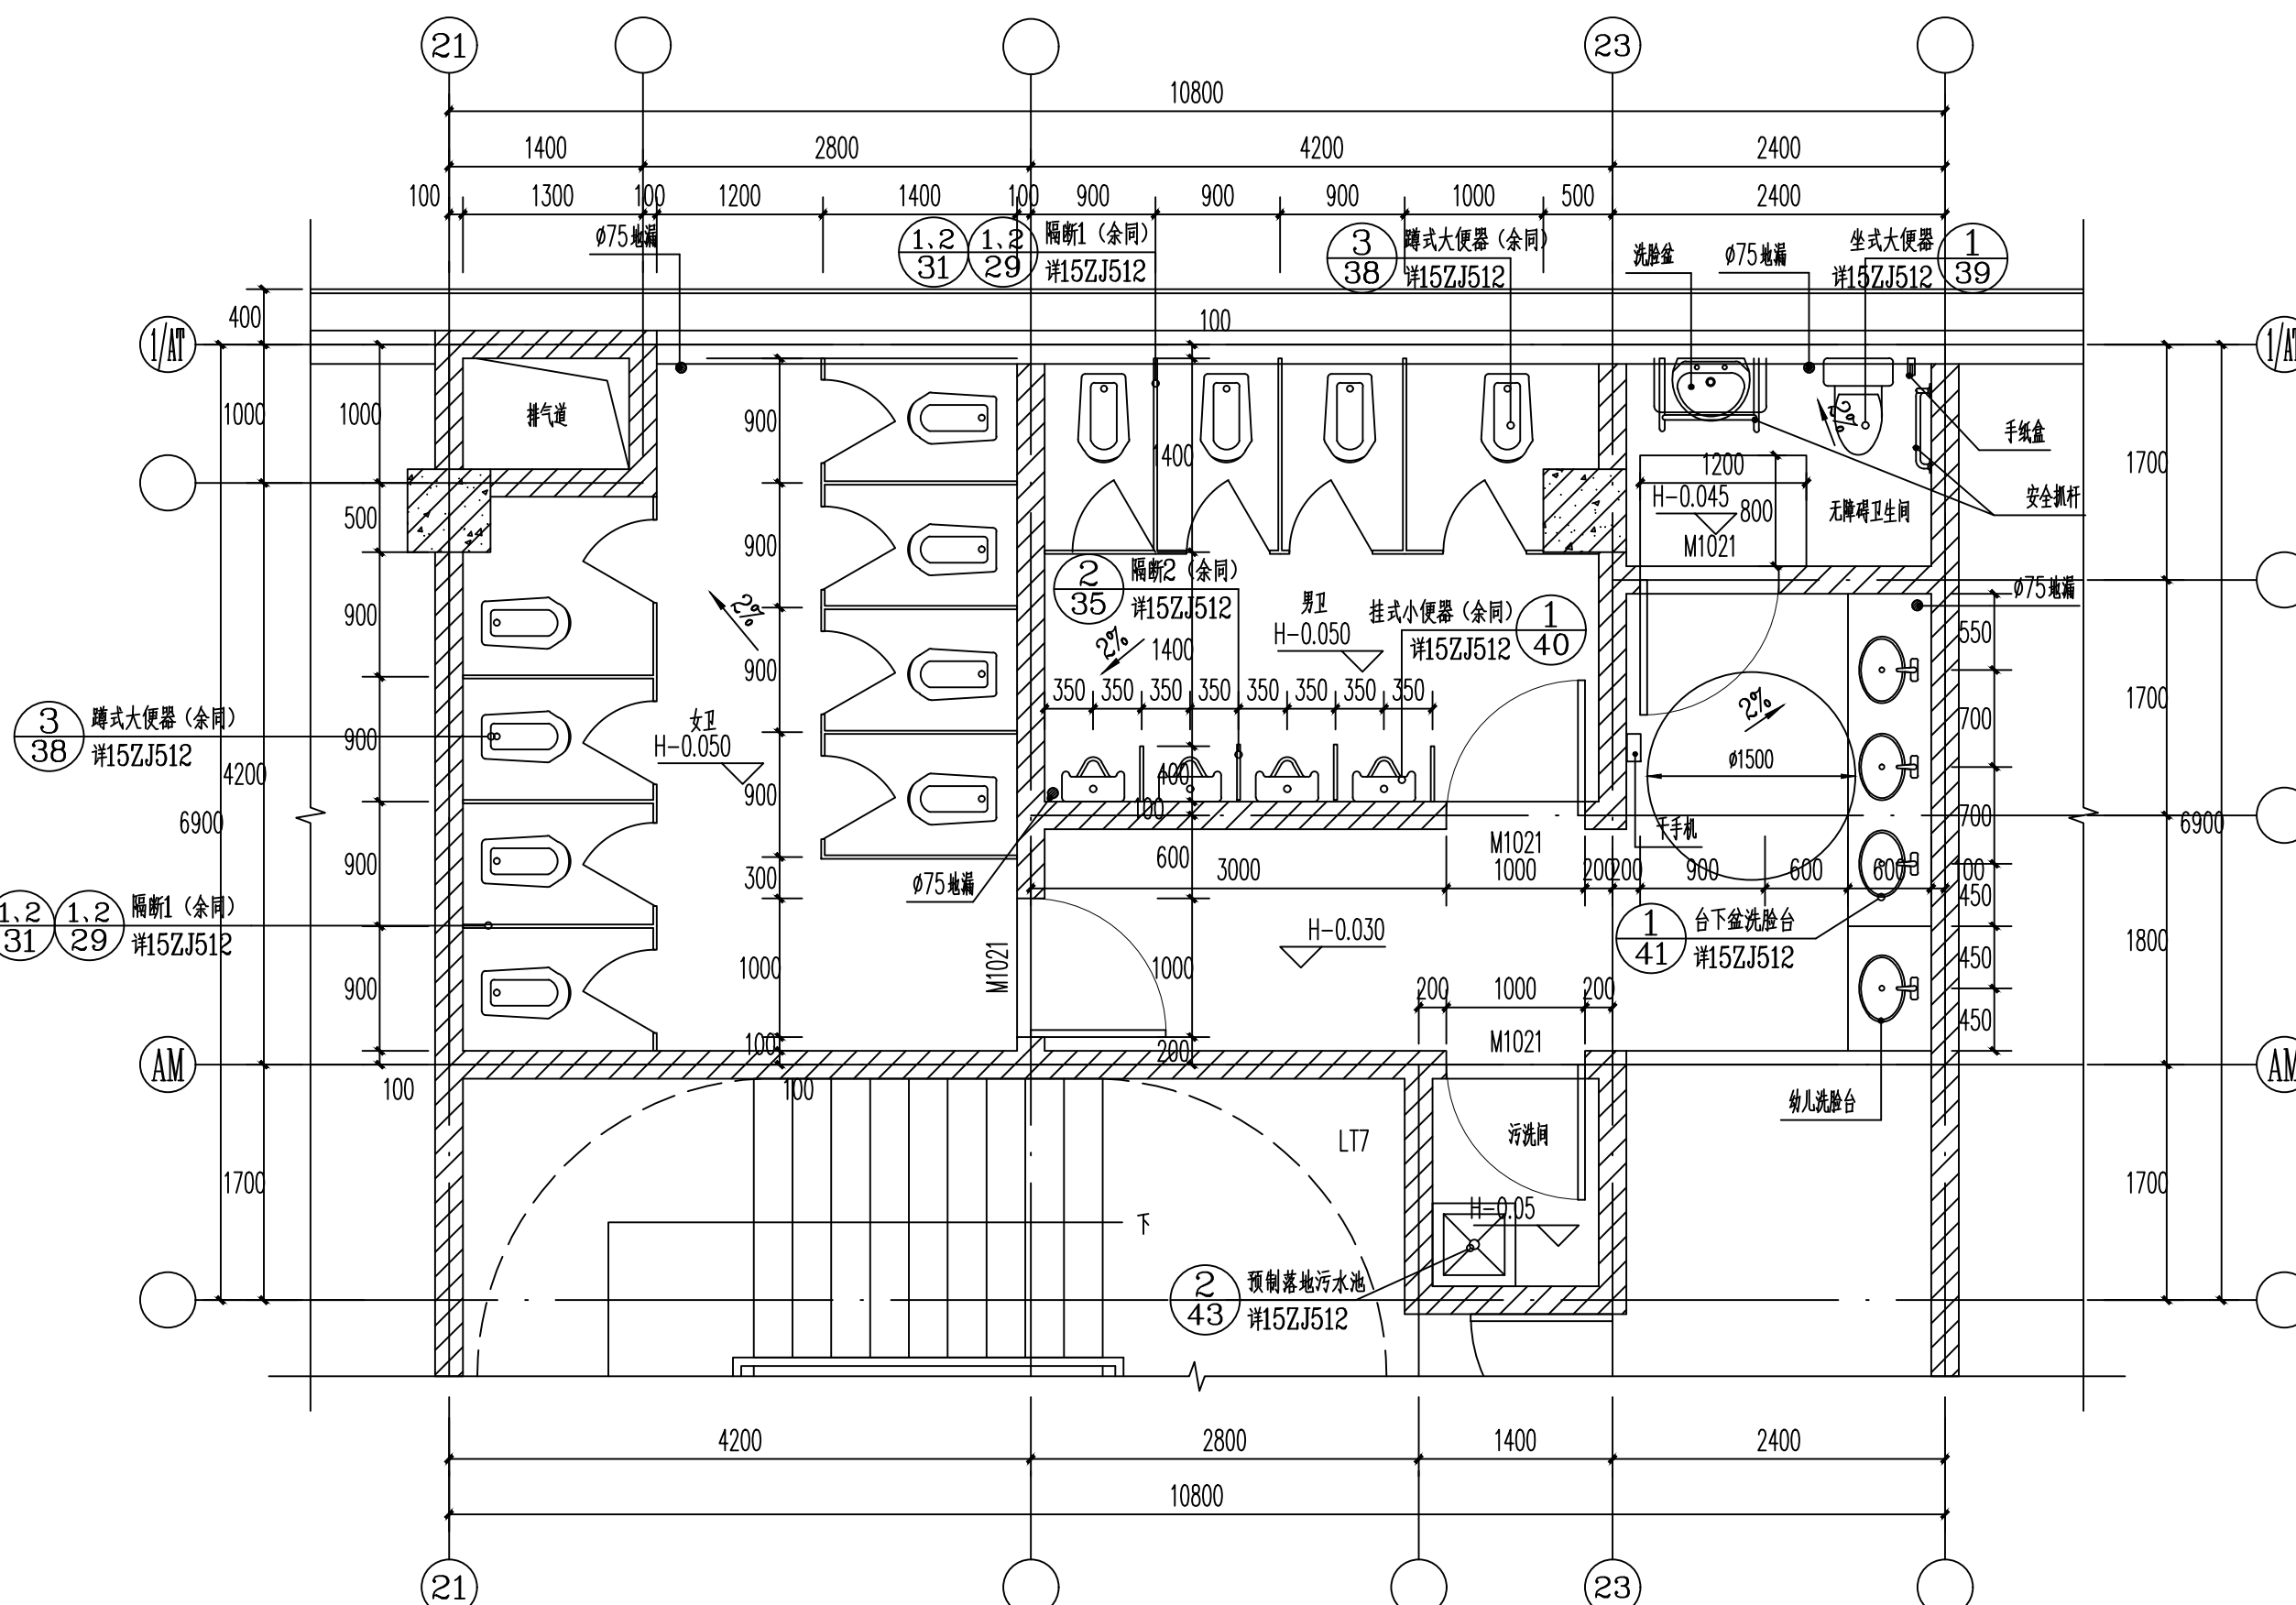

⑤ 公卫五大样图 1:50

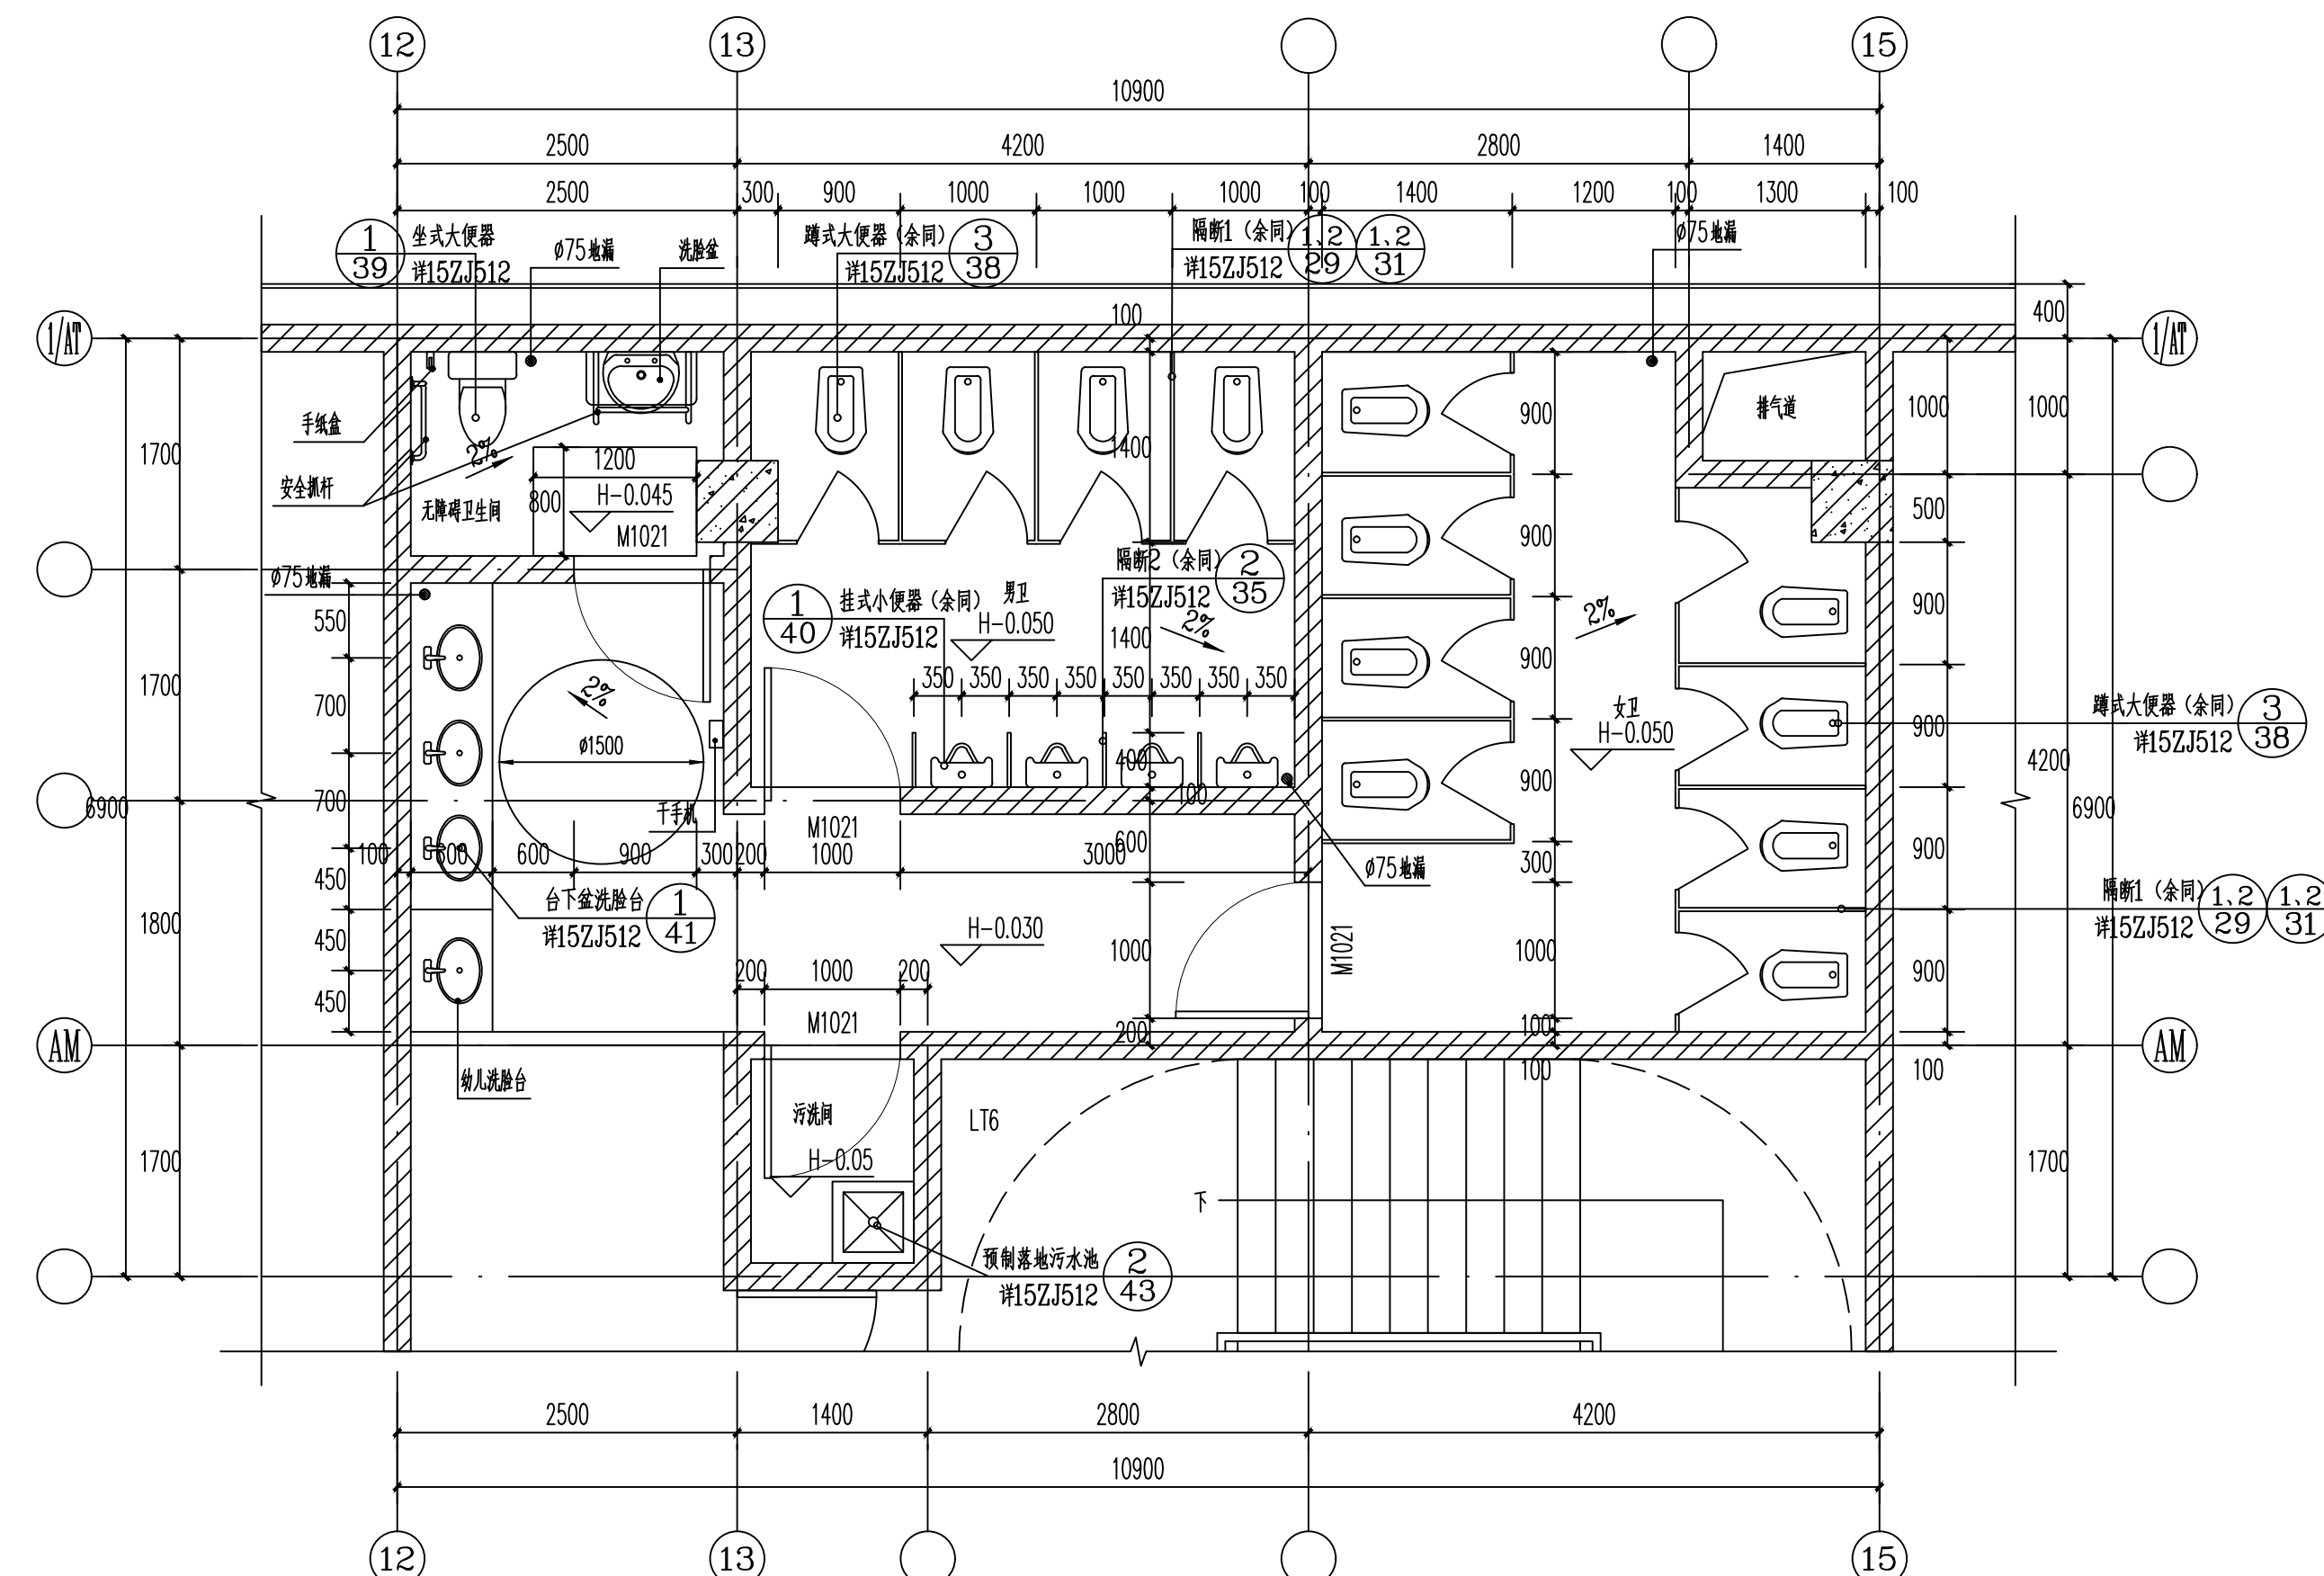

⑥ 公卫六大样图 1:50

建设单位/CLIENT:			麻阳苗族自治县远桥房地产开发有限公司		
项目名称/PROJECT:			远程国际		
子项目名称/SUB-PROJECT:			远程国际		
区位图/REGIONAL LOCATION MAP :			 广东建筑艺术设计院有限公司 GUANGDONG ARCHITECTURAL ARTISTIC DESIGN INSTITUTE CO.,LTD ■ 建筑方案设计: 甲级 ■ 风景园林设计: 乙级 ■ 城乡规划设计: 乙级 ■ 市政工程设计: 乙级		
图纸名称/TITLE:			卫生间大样图		
项目名称/PROJECT:			远程国际		
设计 DESIGNED	古新辉		校对 CHECKED	吴新红	
专业负责人 CHIEF	吴志刚		项目负责人 PROJECT CHIEF	吴志刚	
审核 IDENTIFIED	黄展优		审定 APPROVED	李 坚	
业务号/JOB NO.					
设计阶段/STATUS:			施工图		
专业/DISCIPLINE:			建筑		
比例/ SCALE:	1: 100	规格/ SIZE:	A1		
出图日期/DATE:			2021.06		
图号/DRAWING NO.			JS-27		
版次 NO.	修改内容 DESCRIPTION		日期 DATE		
条形码/BARCODE:					