
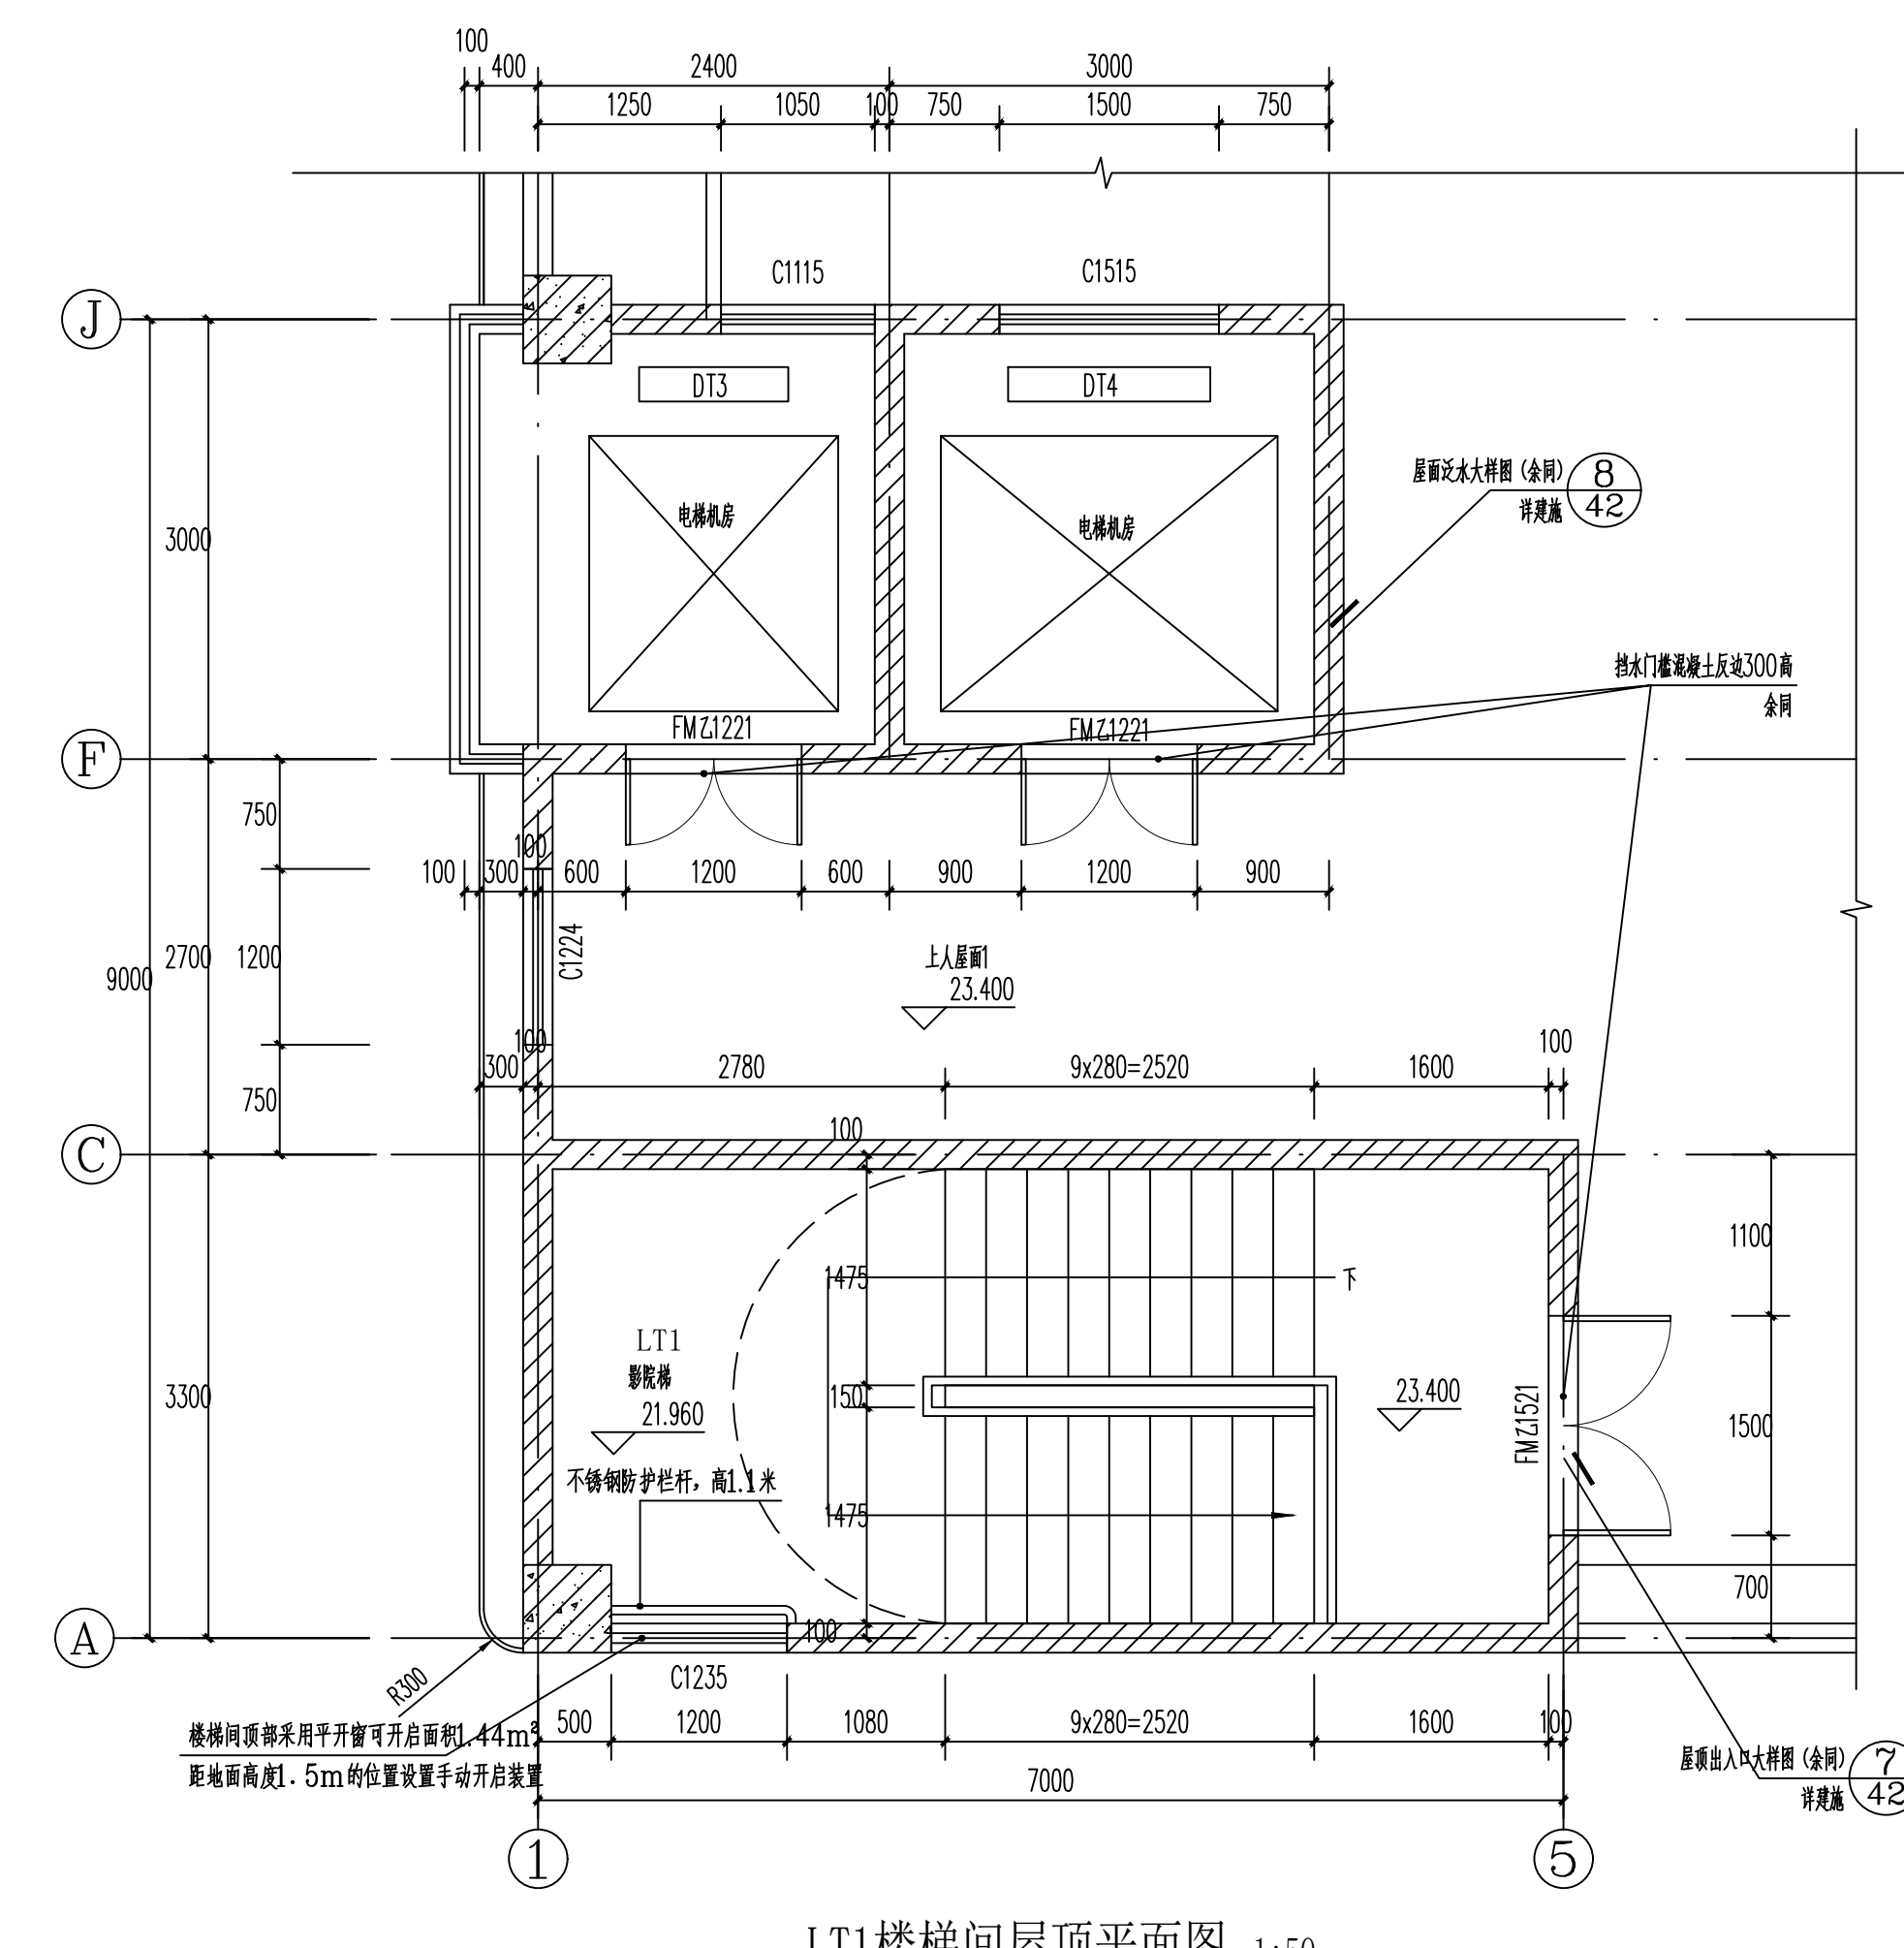
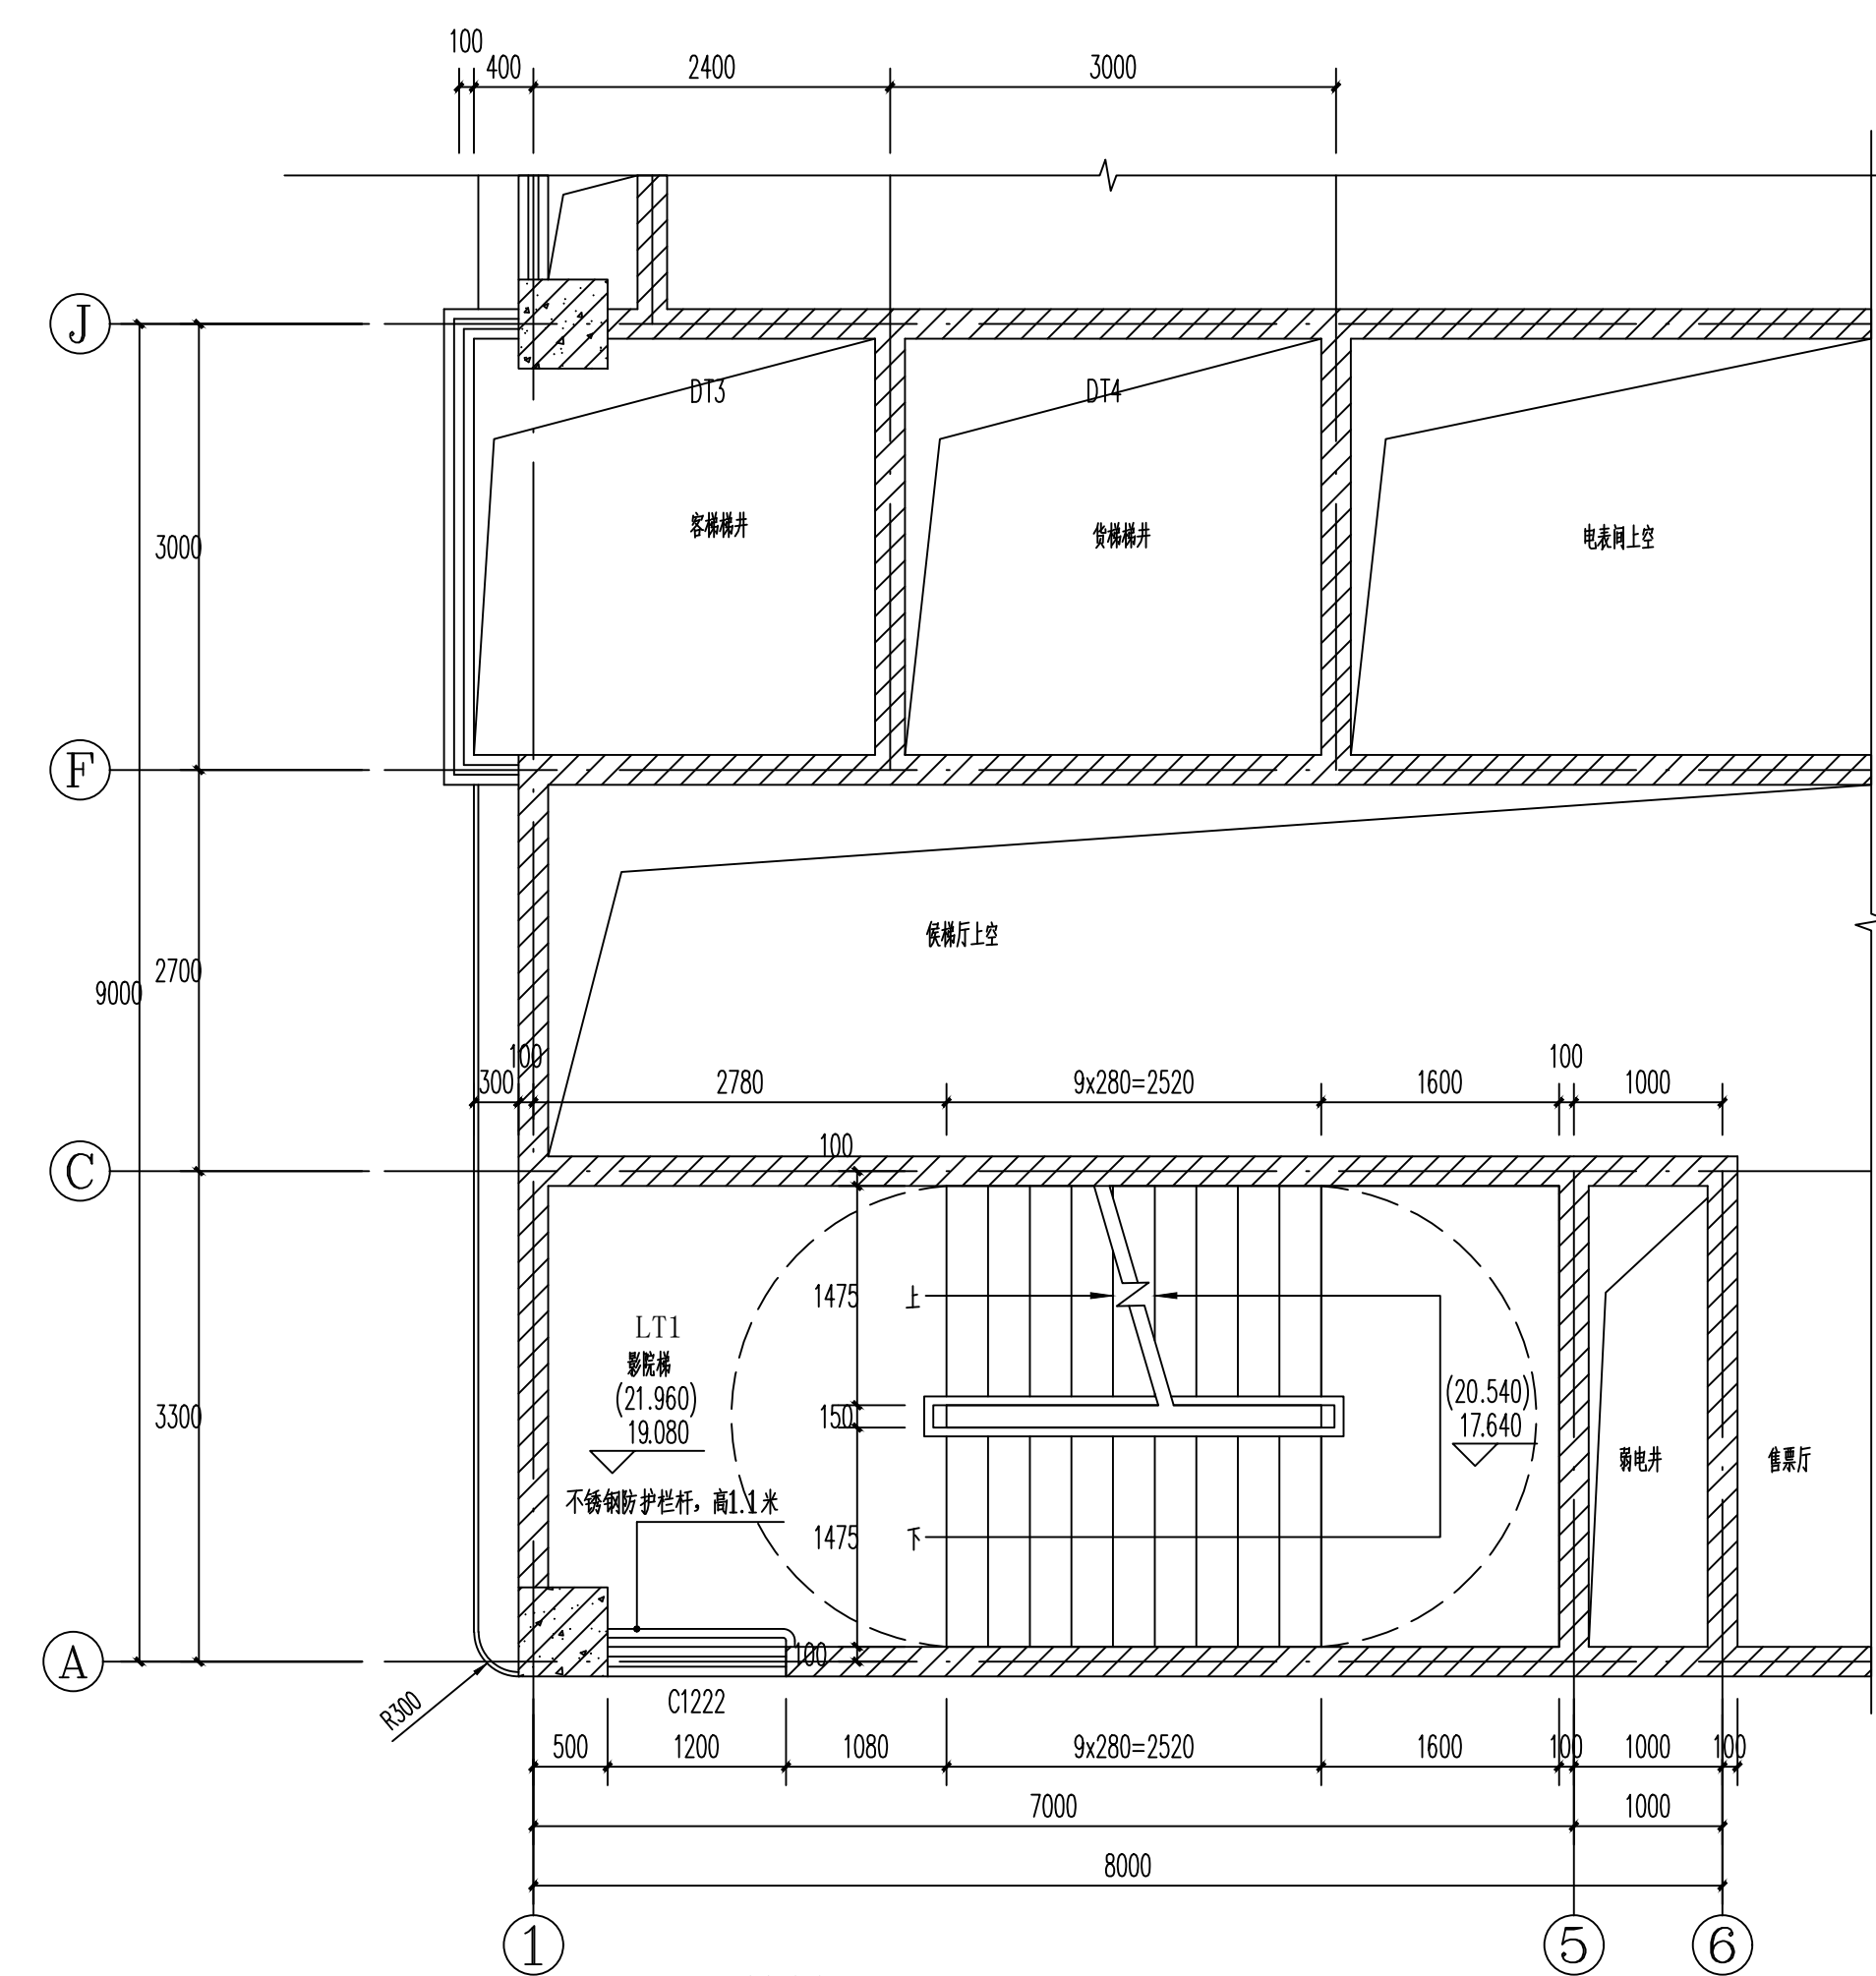
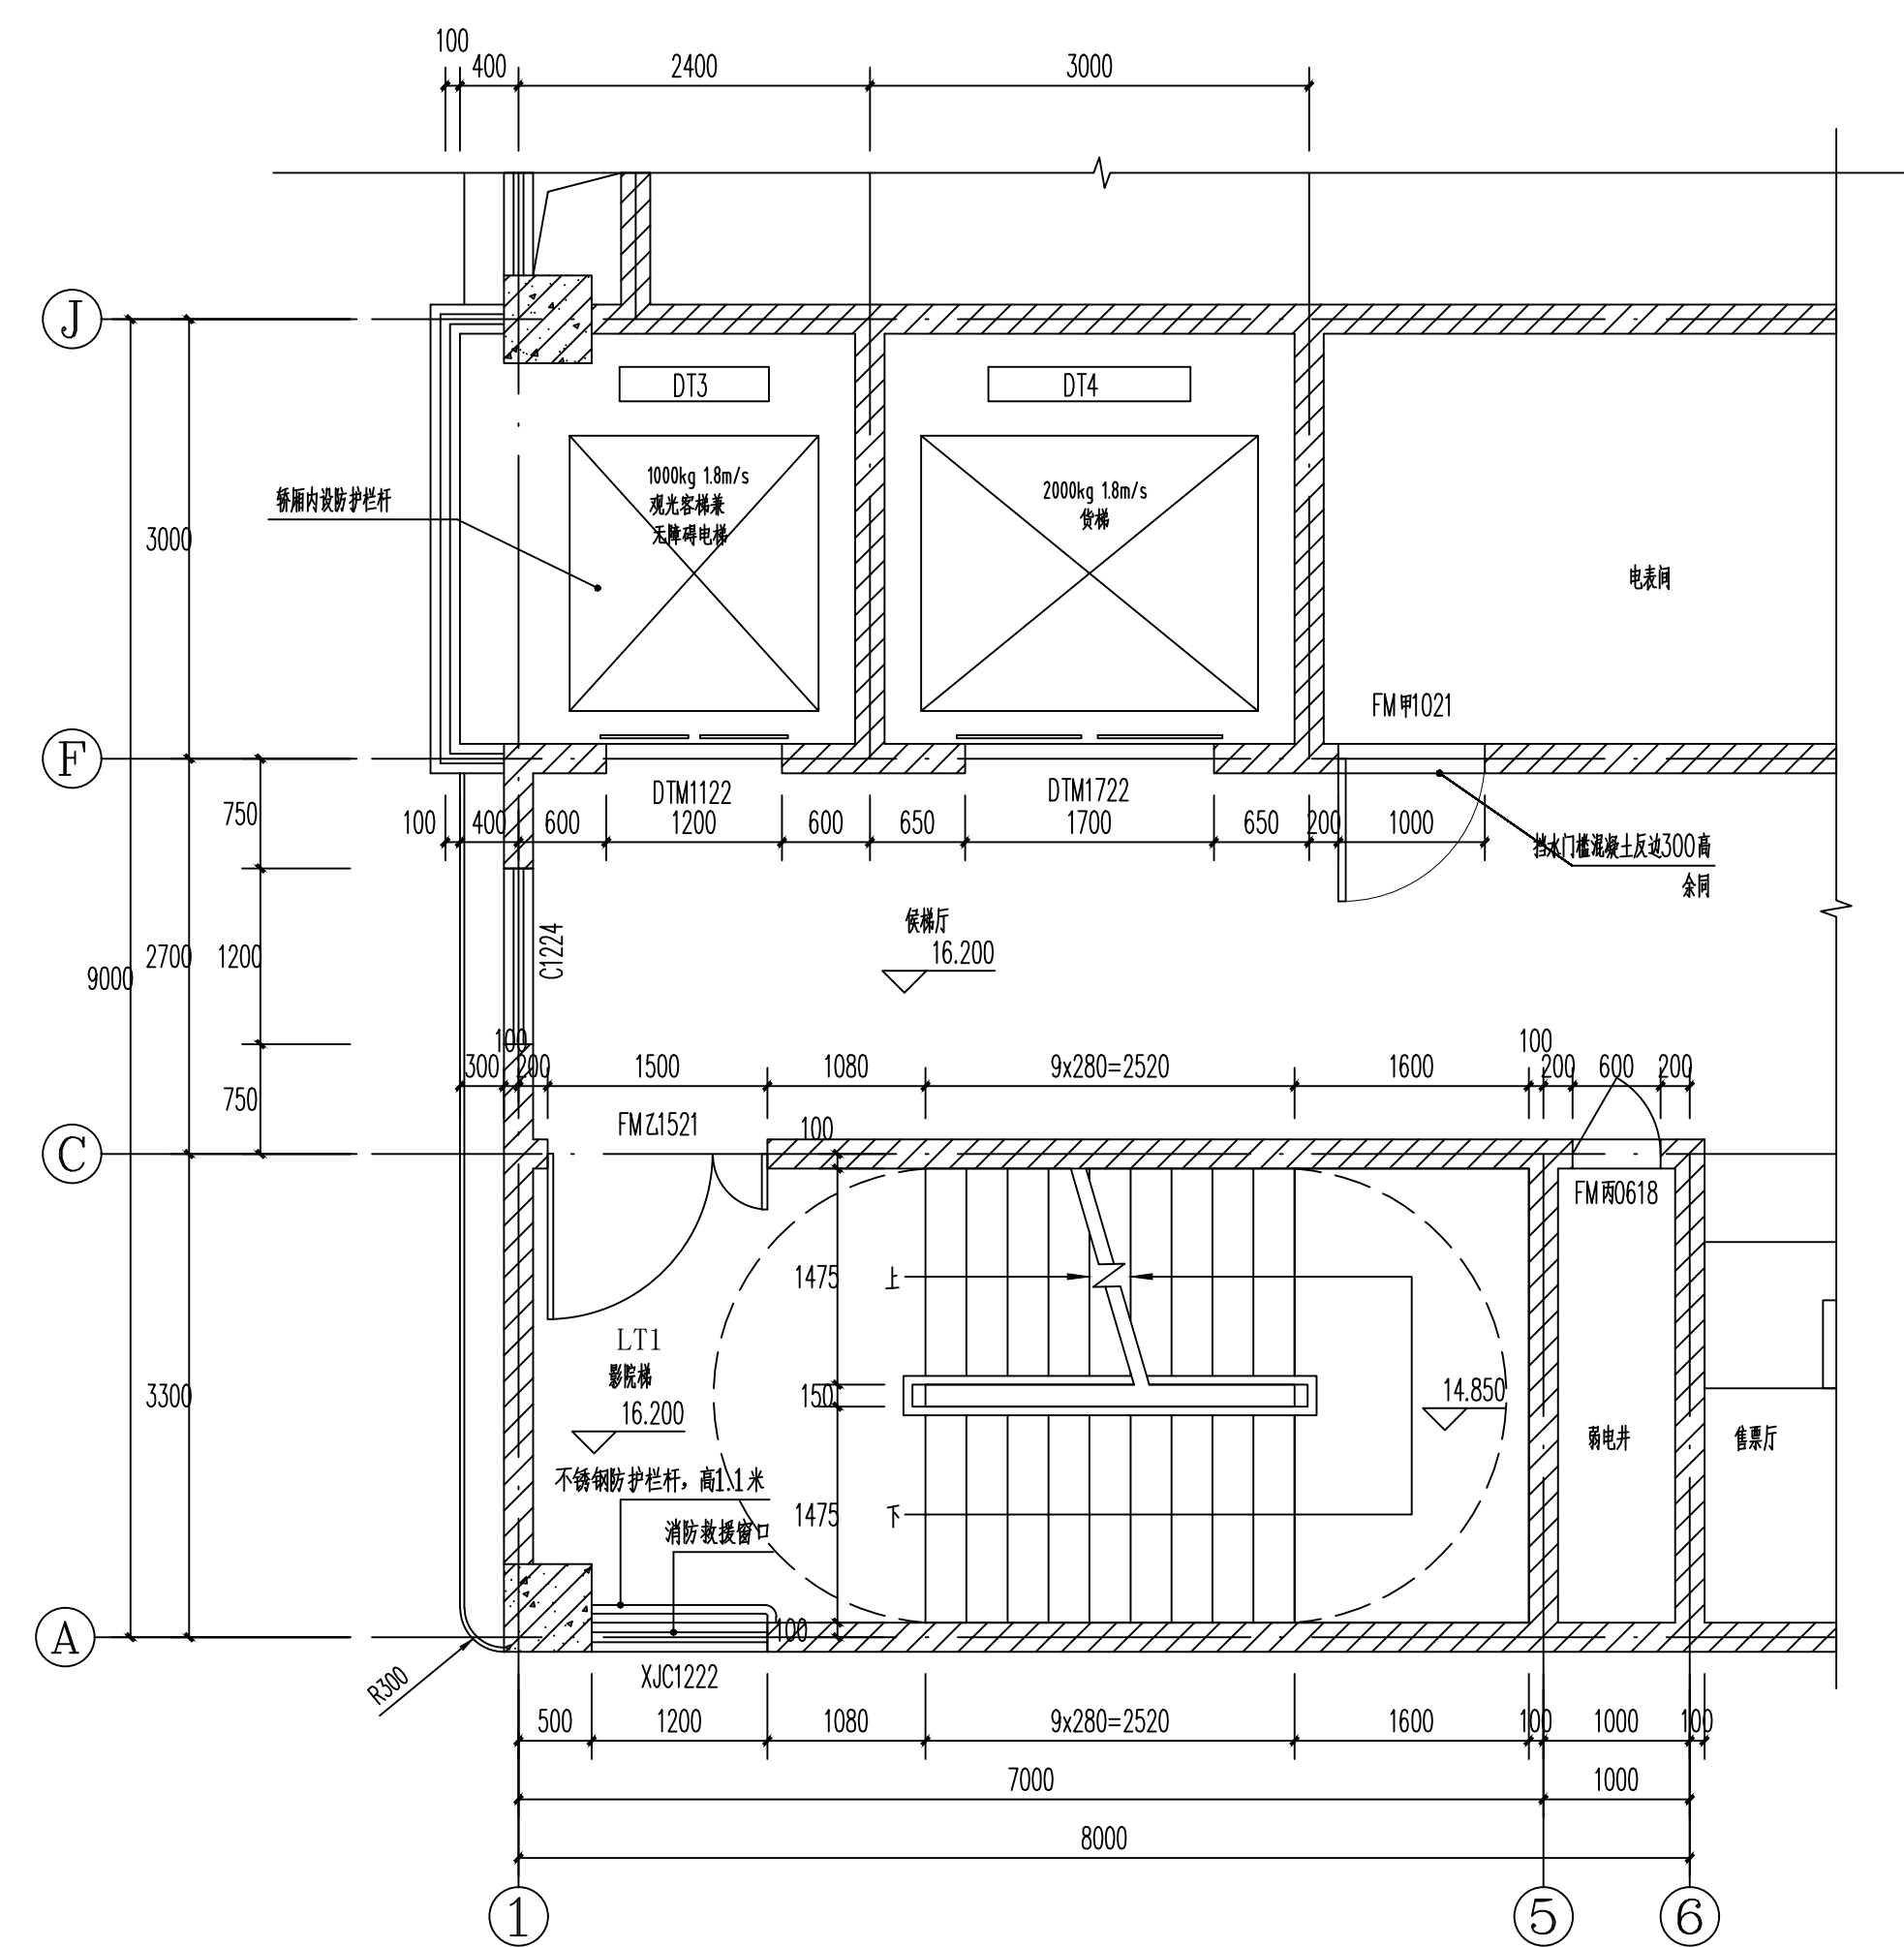
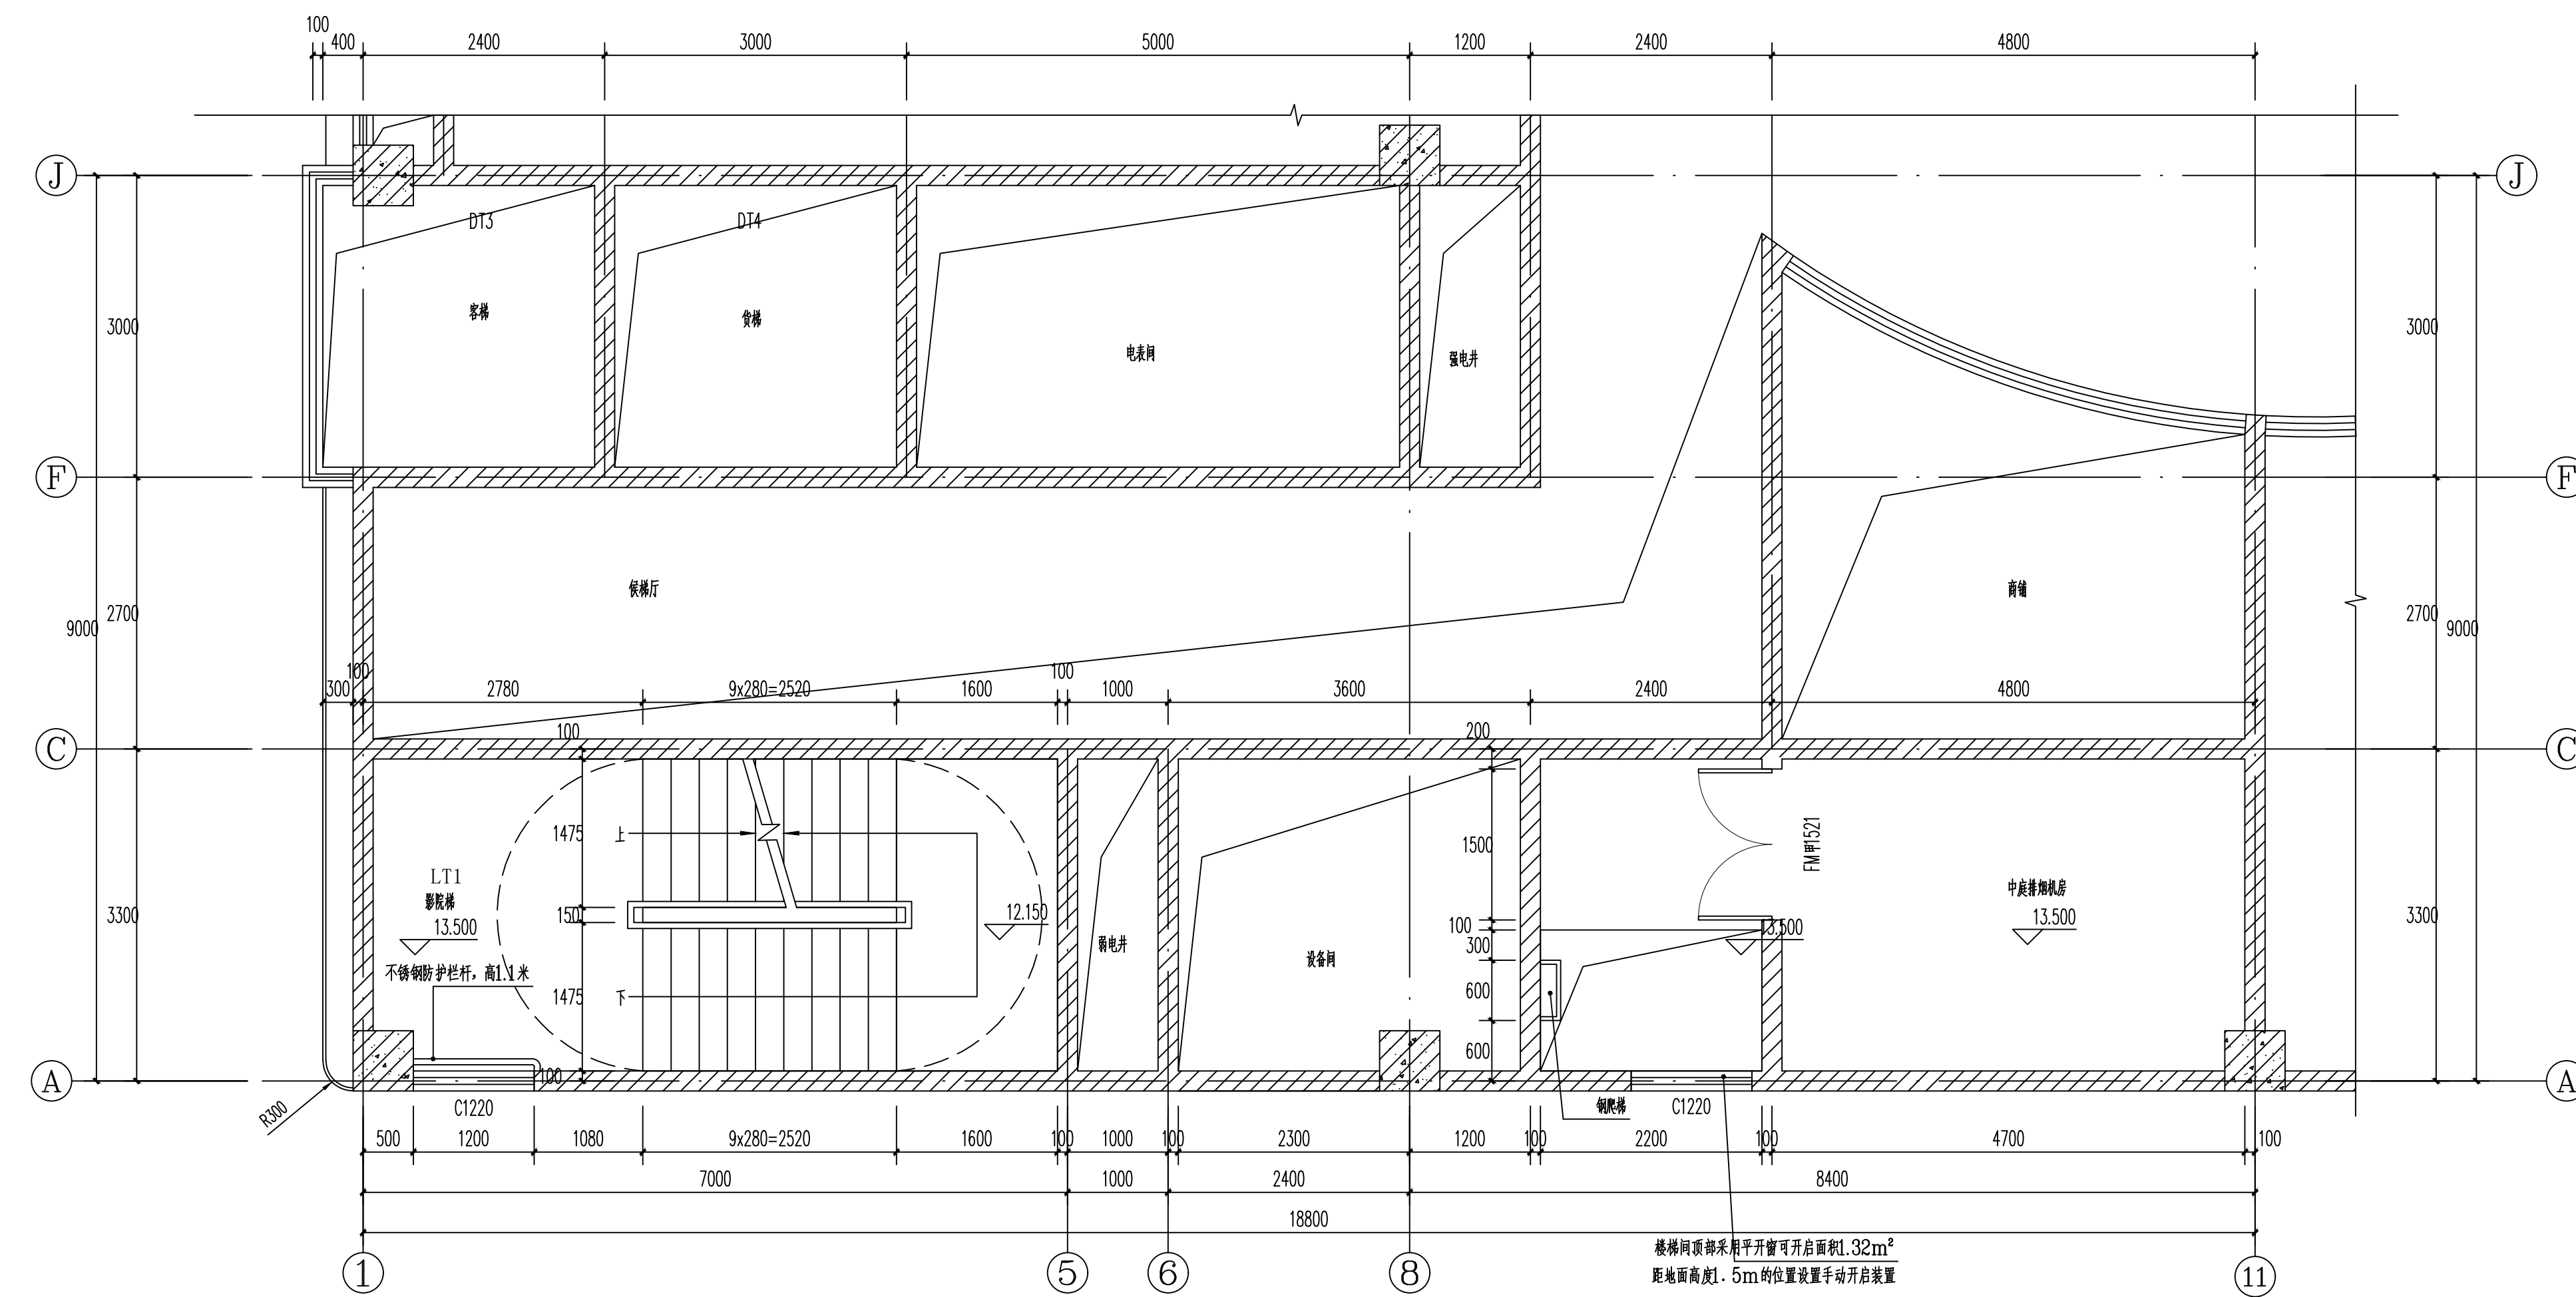


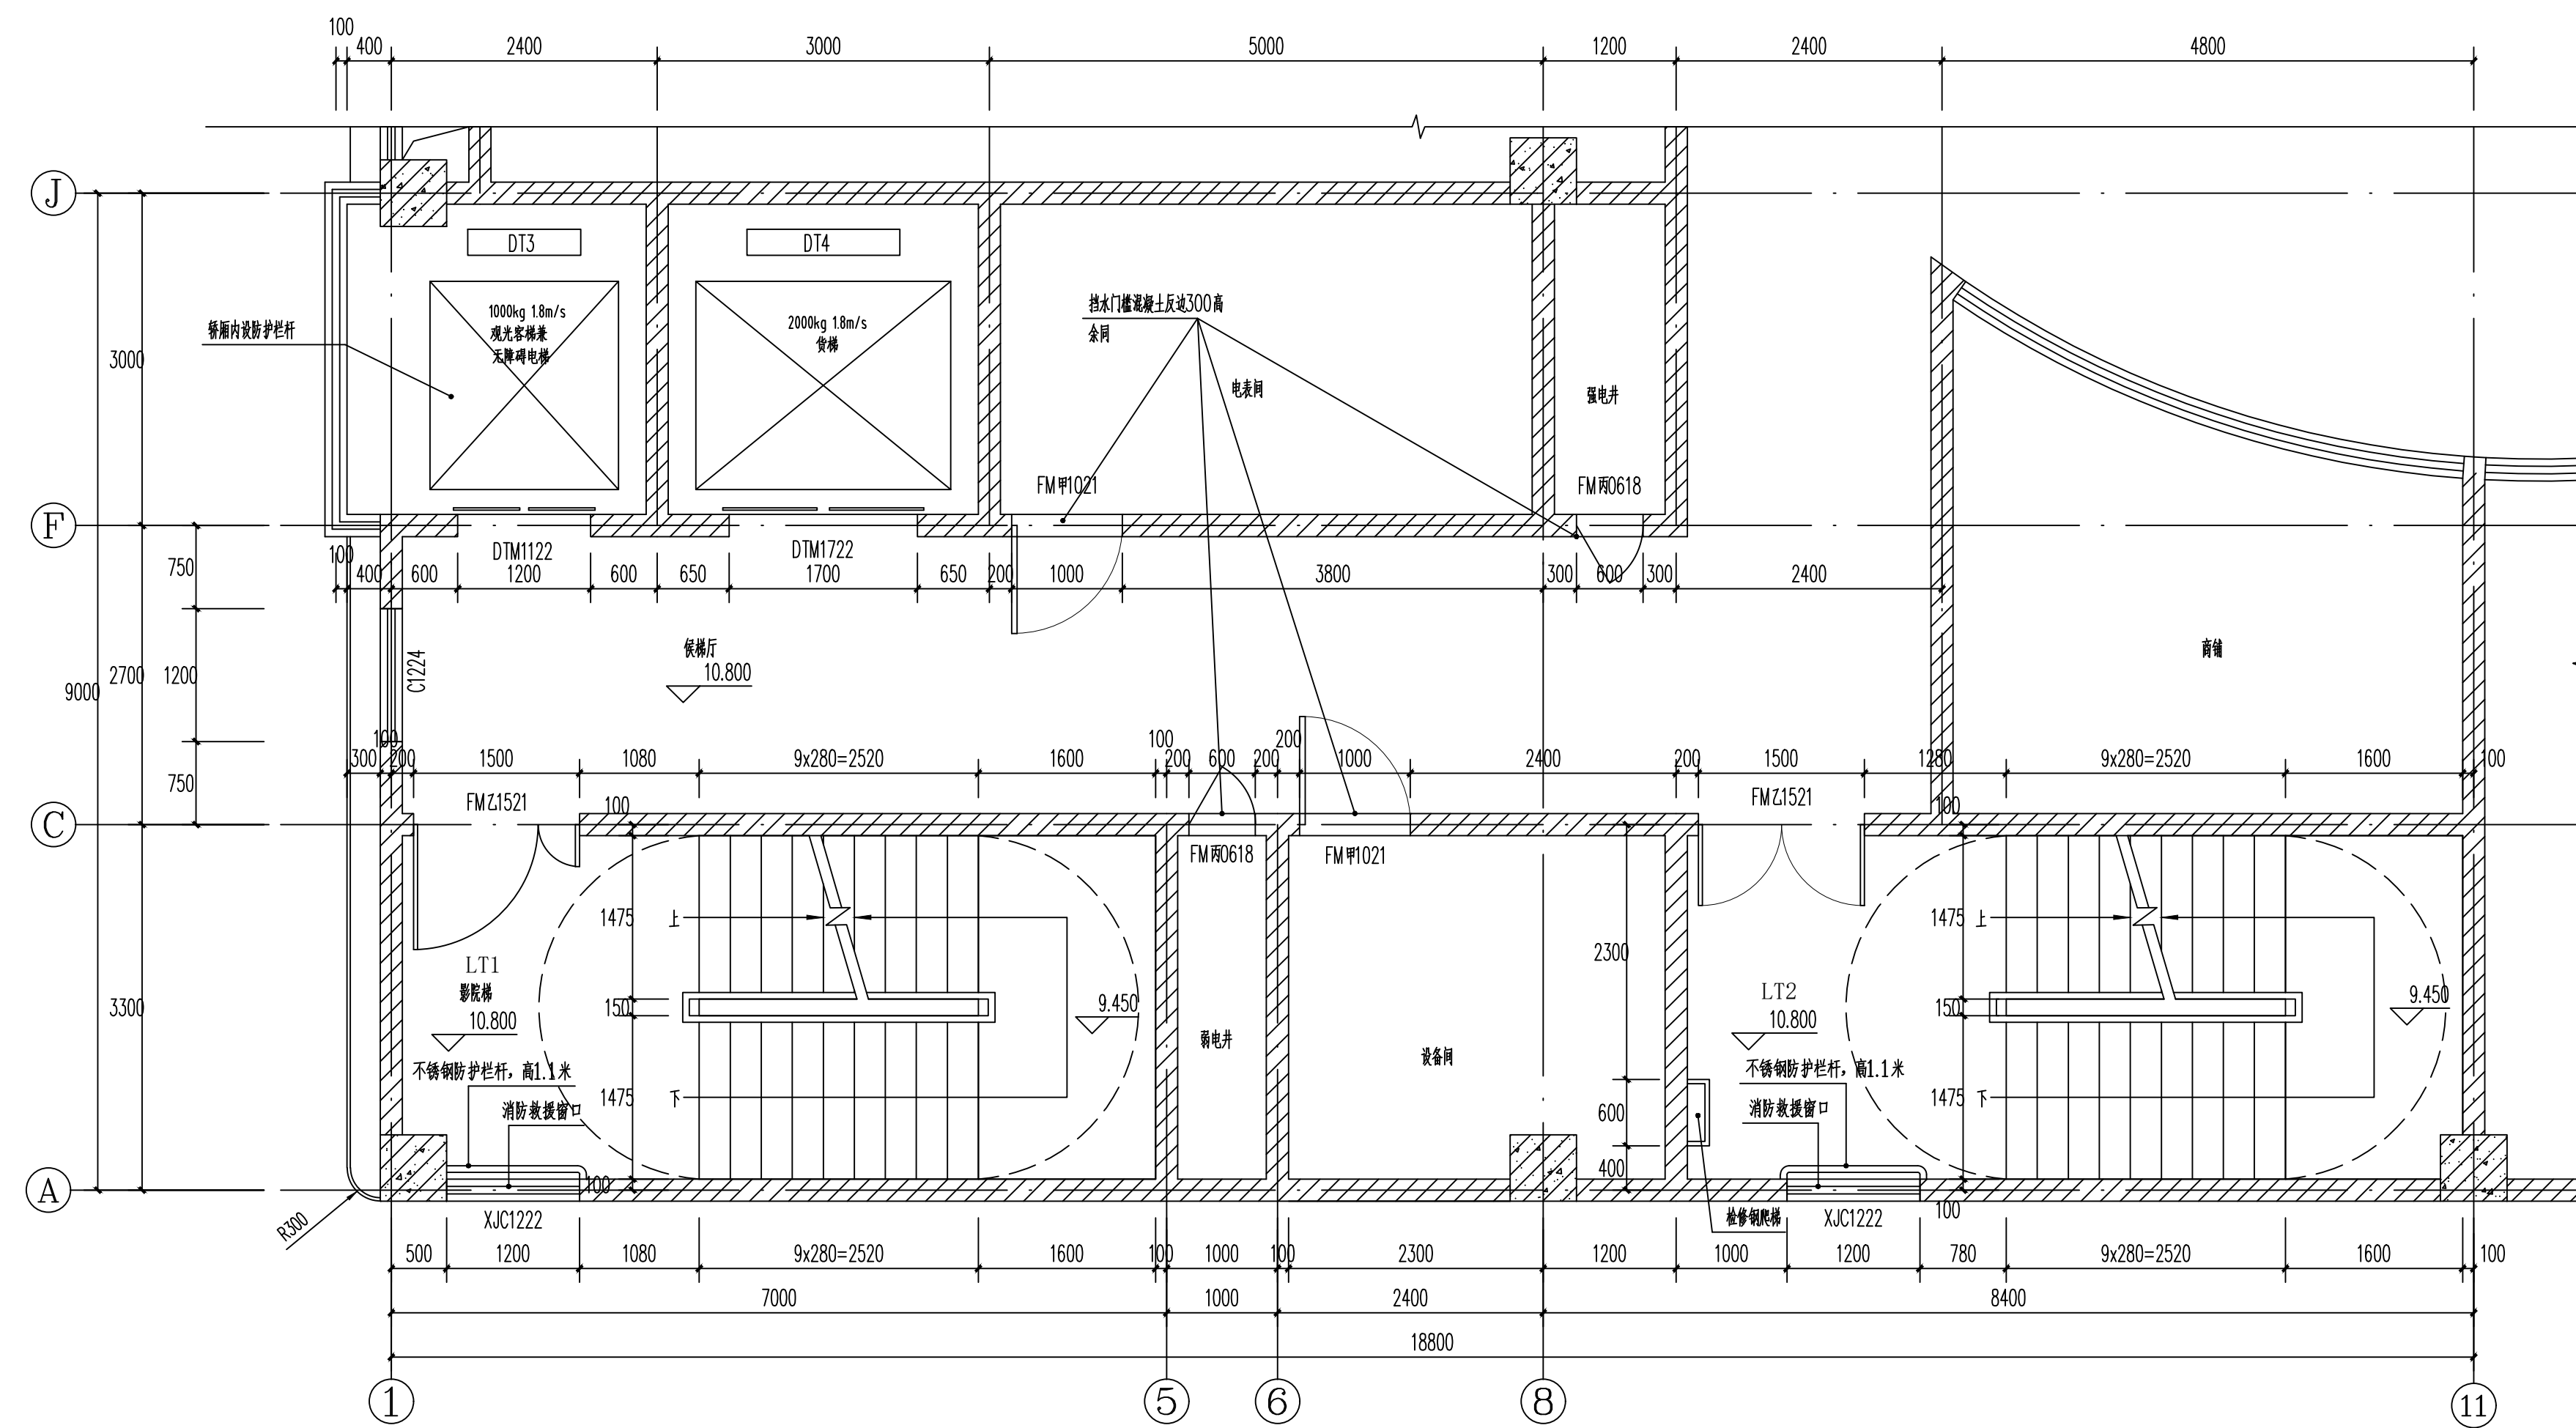

建设单位/CLIENT:

麻阳苗族自治县远桥房地产开发有限公司

项目名称/PROJECT:

远程国际

子项目名称/SUB-PROJECT:

远程国际

区位图/REGIONAL LOCATION MAP :



图纸名称/TITLE:

LTI、LT2楼梯间大样图二

项目名称/PROJECT:

远程国际

设计	古新辉	陈松
----	-----	----

DESIGNED		
DATE		12/1

校对 CHECKED	吴新红	吴新红
---------------	-----	-----

专业负责人	呈志刚	呈志刚
-------	-----	-----

CHIEF	吴志刚	吴志刚
项目负责人	吴志刚	吴志刚

项目负责人 PROJECT CHIEF	吴志刚	吴志刚
------------------------	-----	-----

业务号/JOB NO.

设计阶段/STATUS: 施工图

专业/DISCIPLINE: 建施

比例/	1 : 100	规格/	A1
-----	---------	-----	----

出图日期/DATE: 2021.06

图号/DRAWING NO. JS-29

版次	修改内容	日期
----	------	----

条形码/BARCODE:

版权所有，不得复制、套用。
ALL RIGHTS RESERVED, DON'T COPIED, REPRODUCED.