




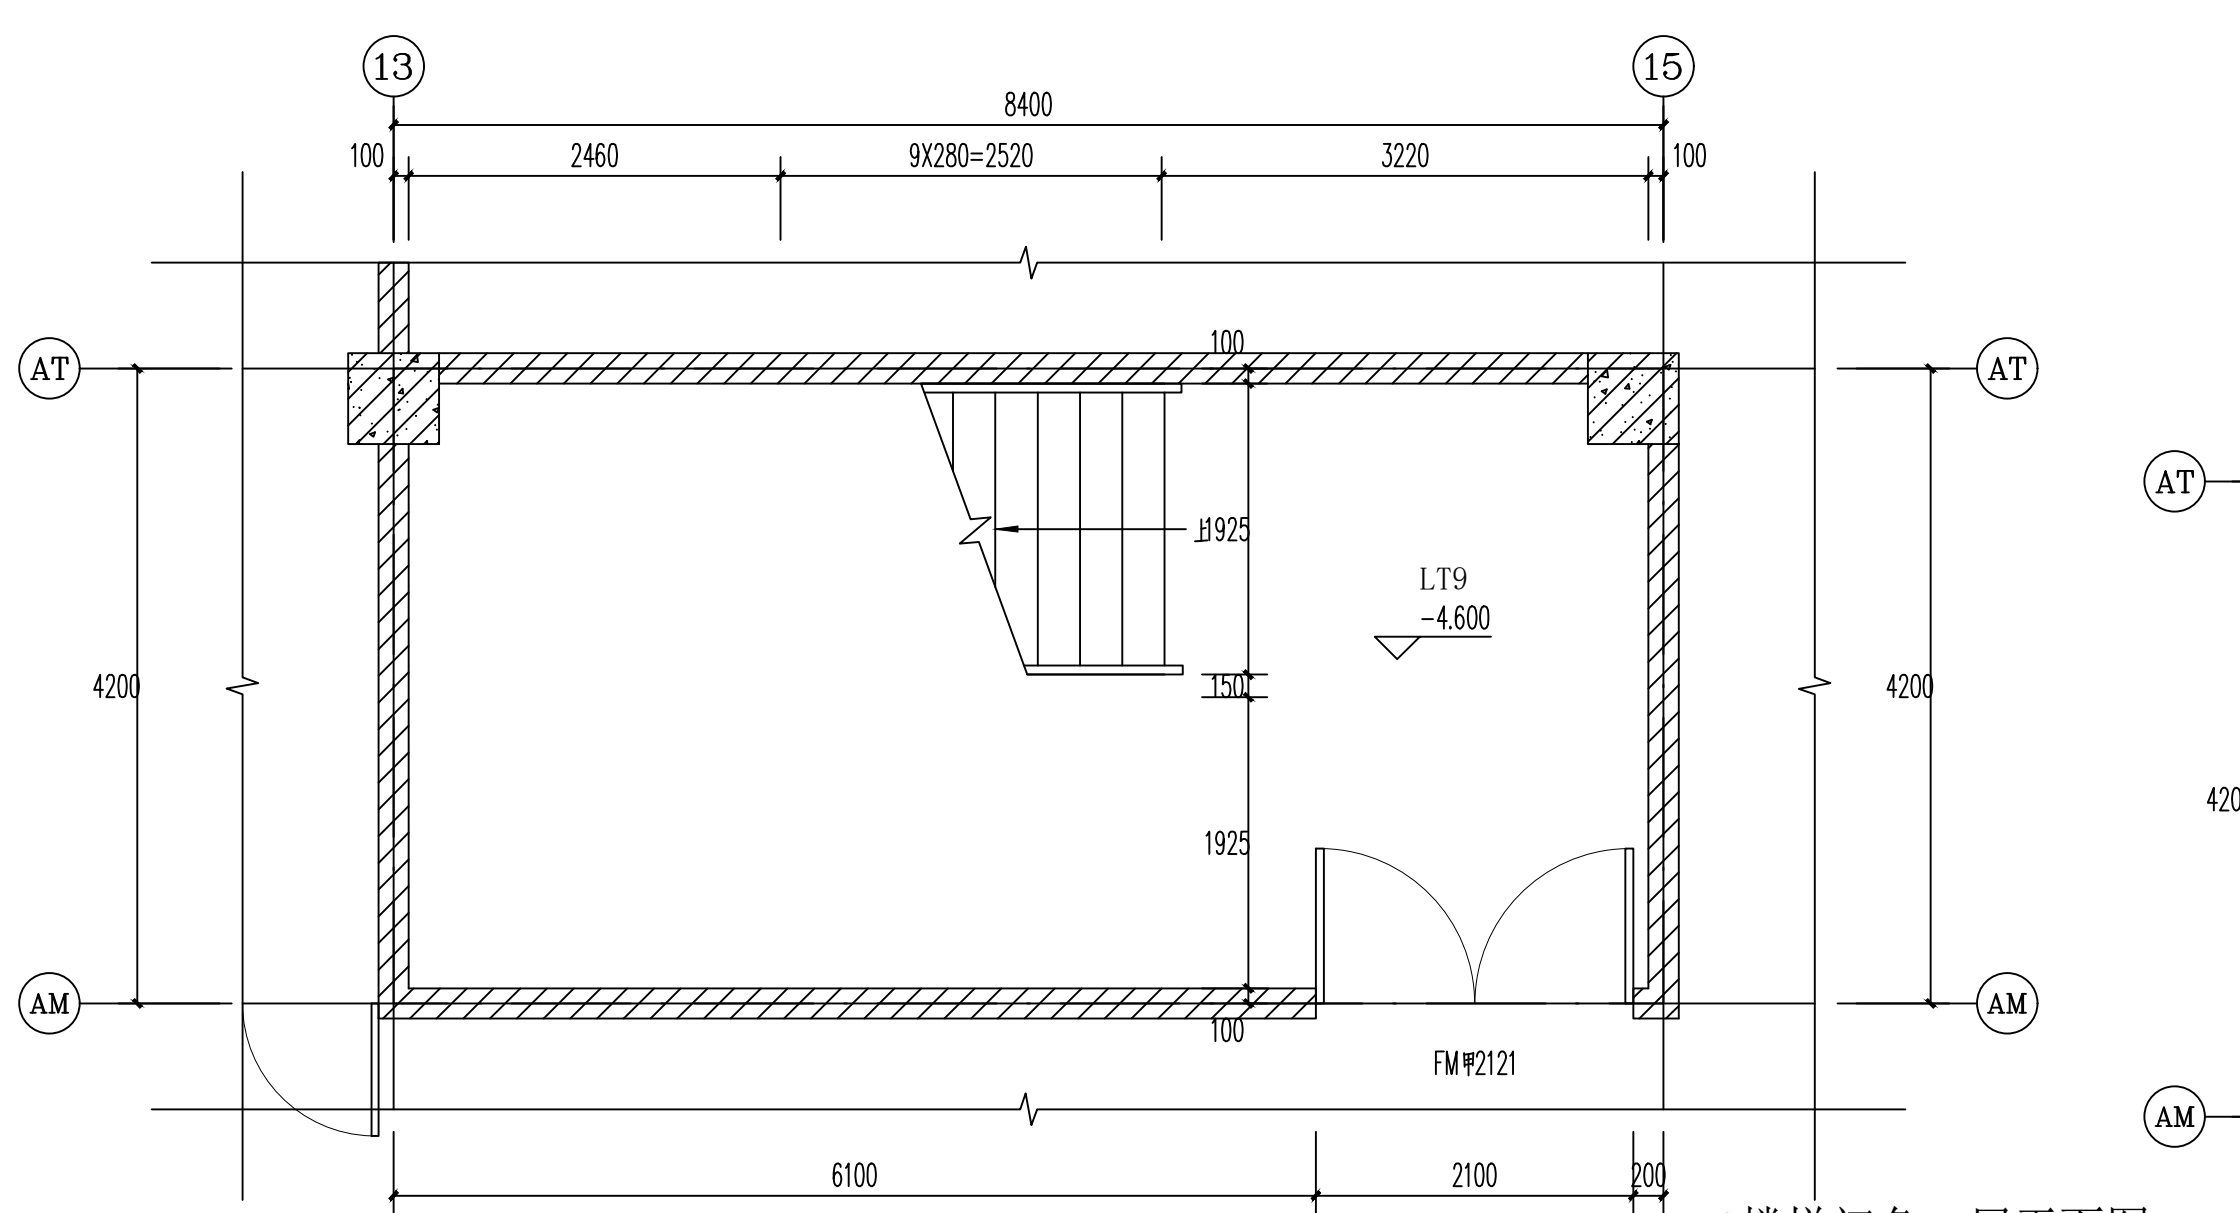


LT9楼梯间负一层平面图 1:50

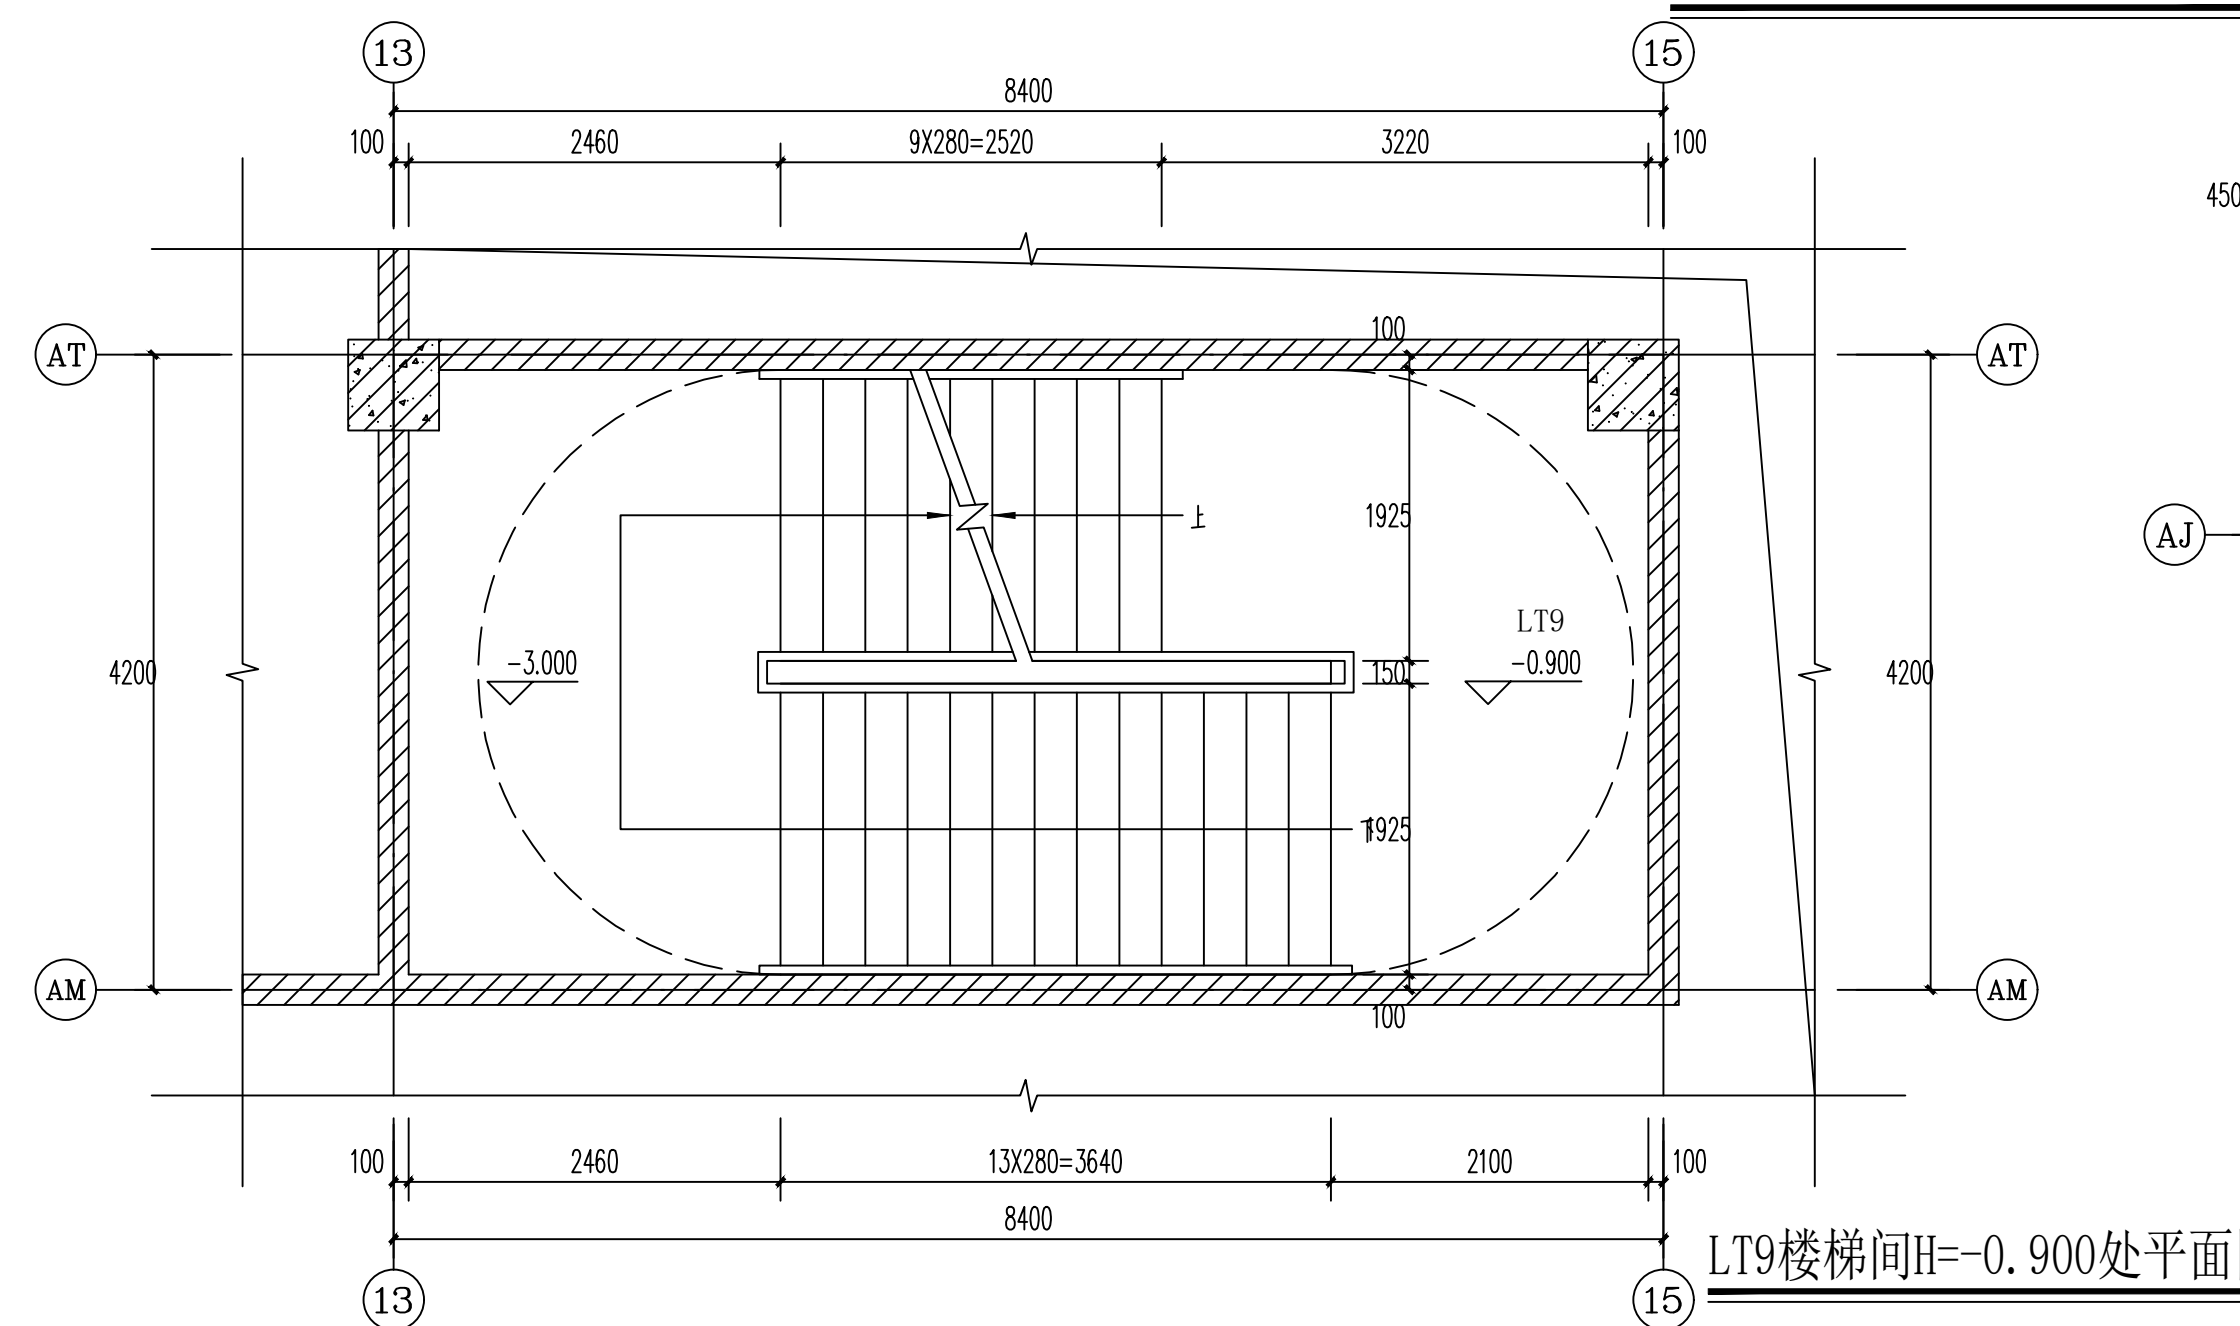


LT9楼梯间H=-0.900处平面图 1:50

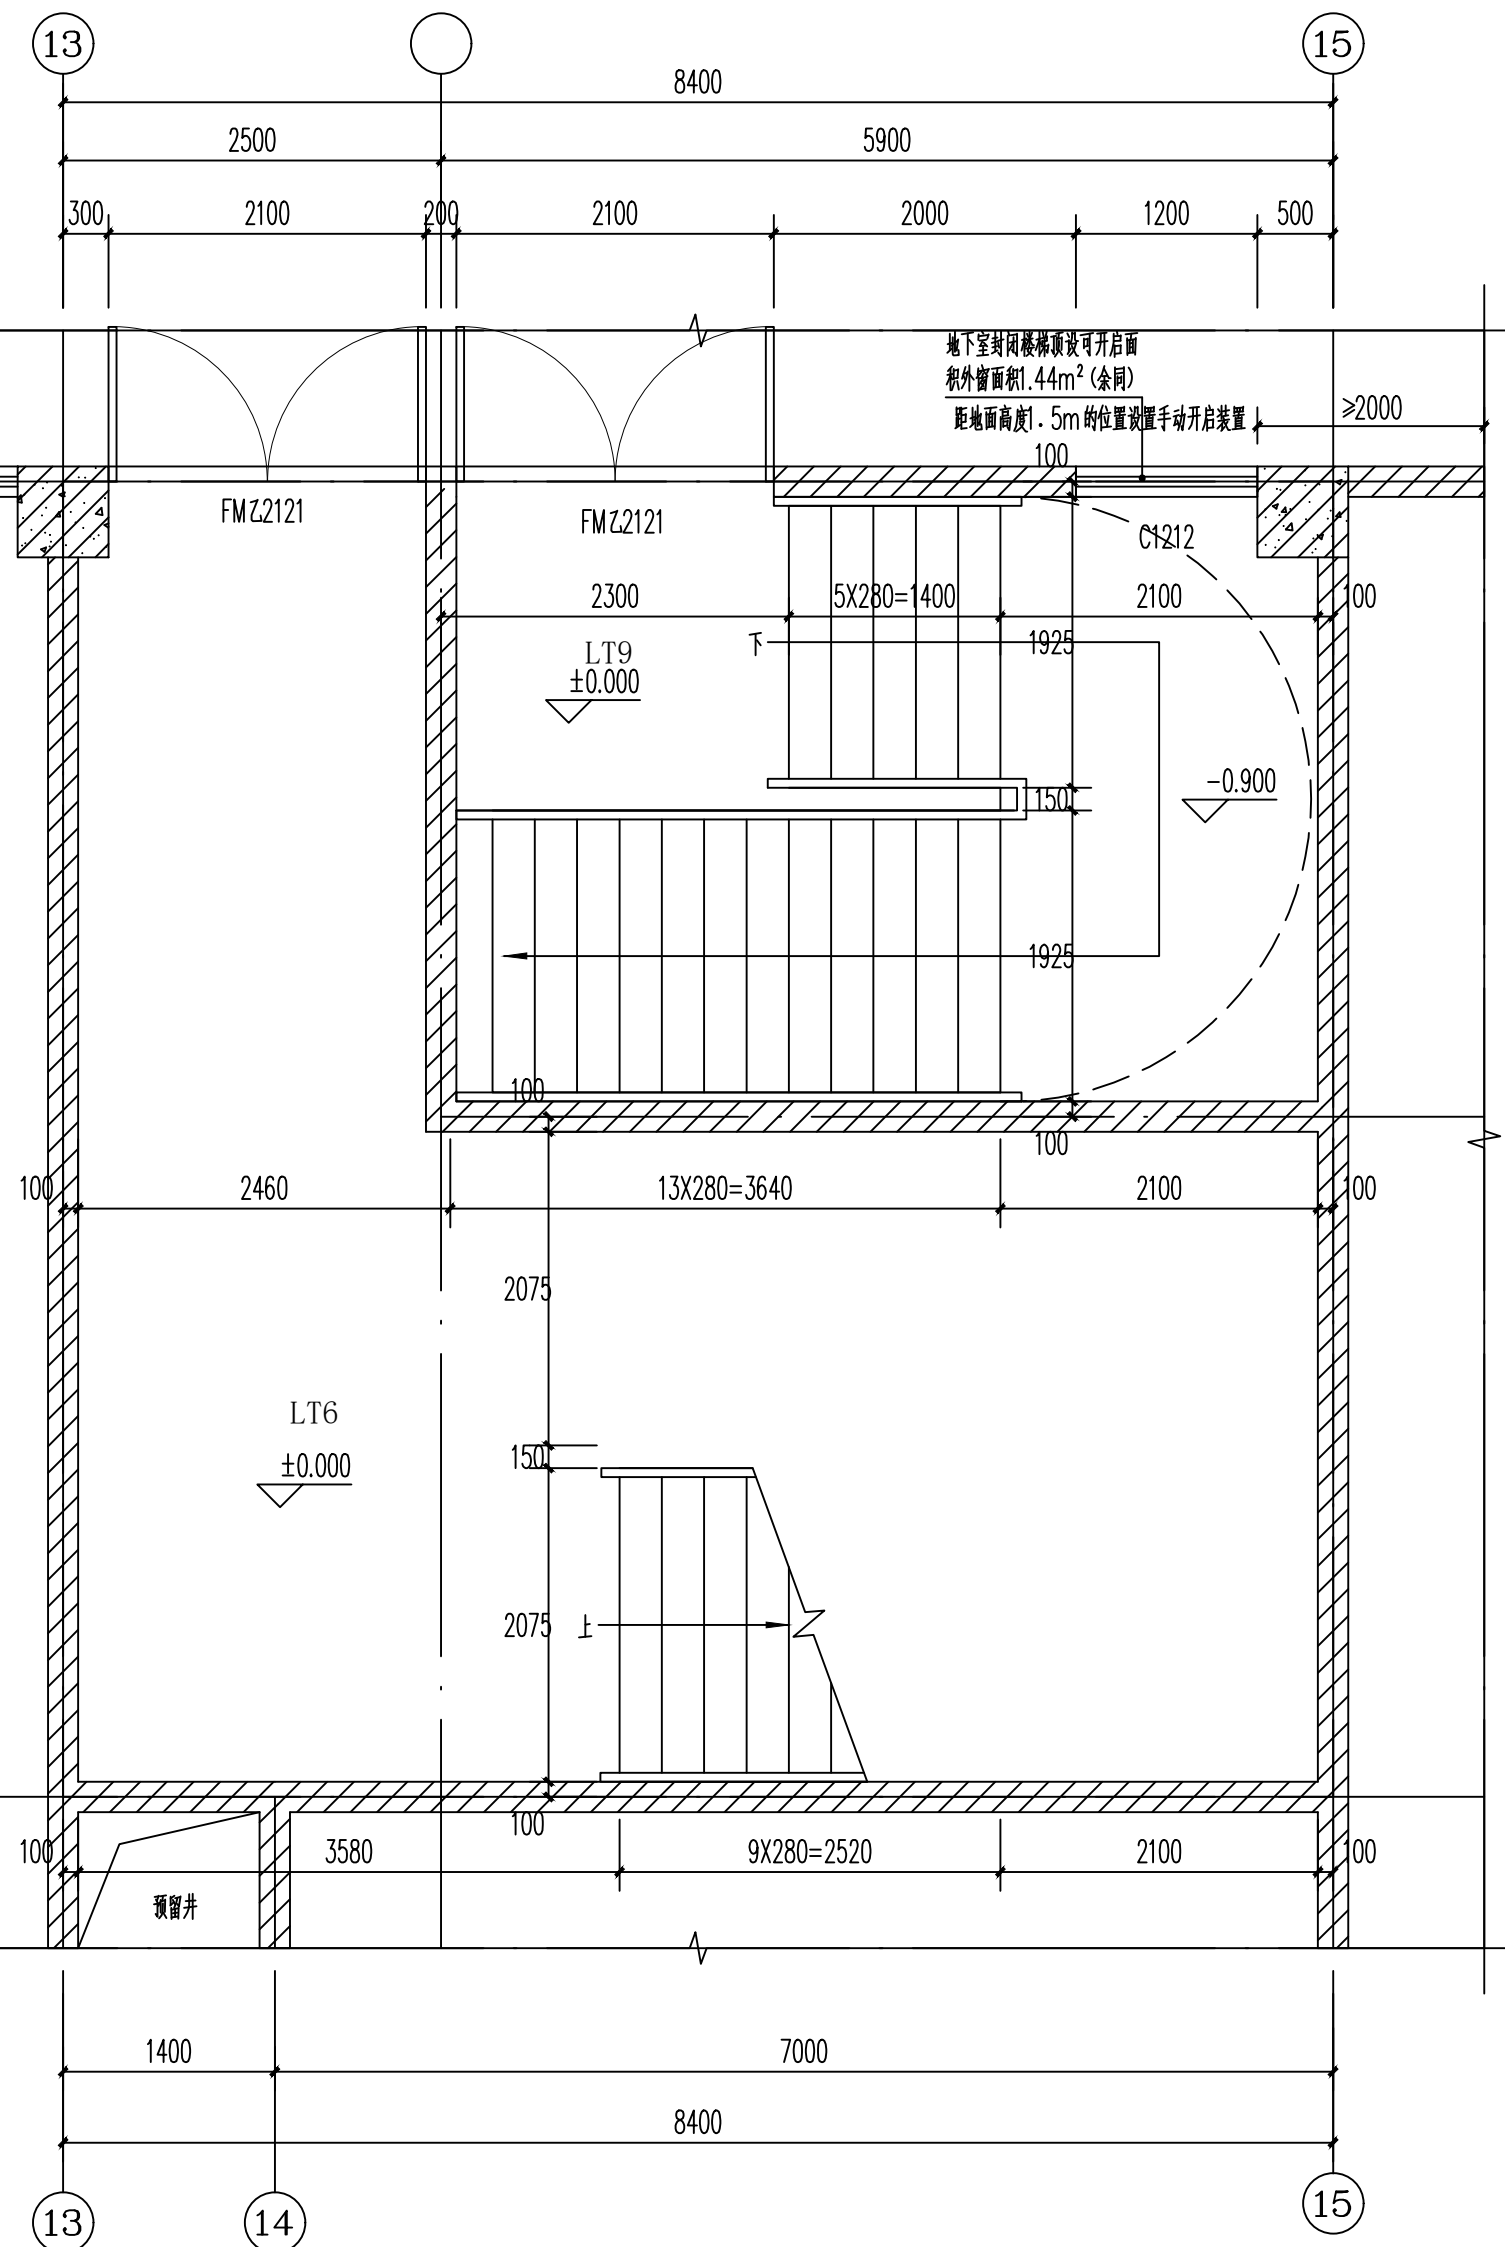


LT6、LT9楼梯间一层平面图 1:50

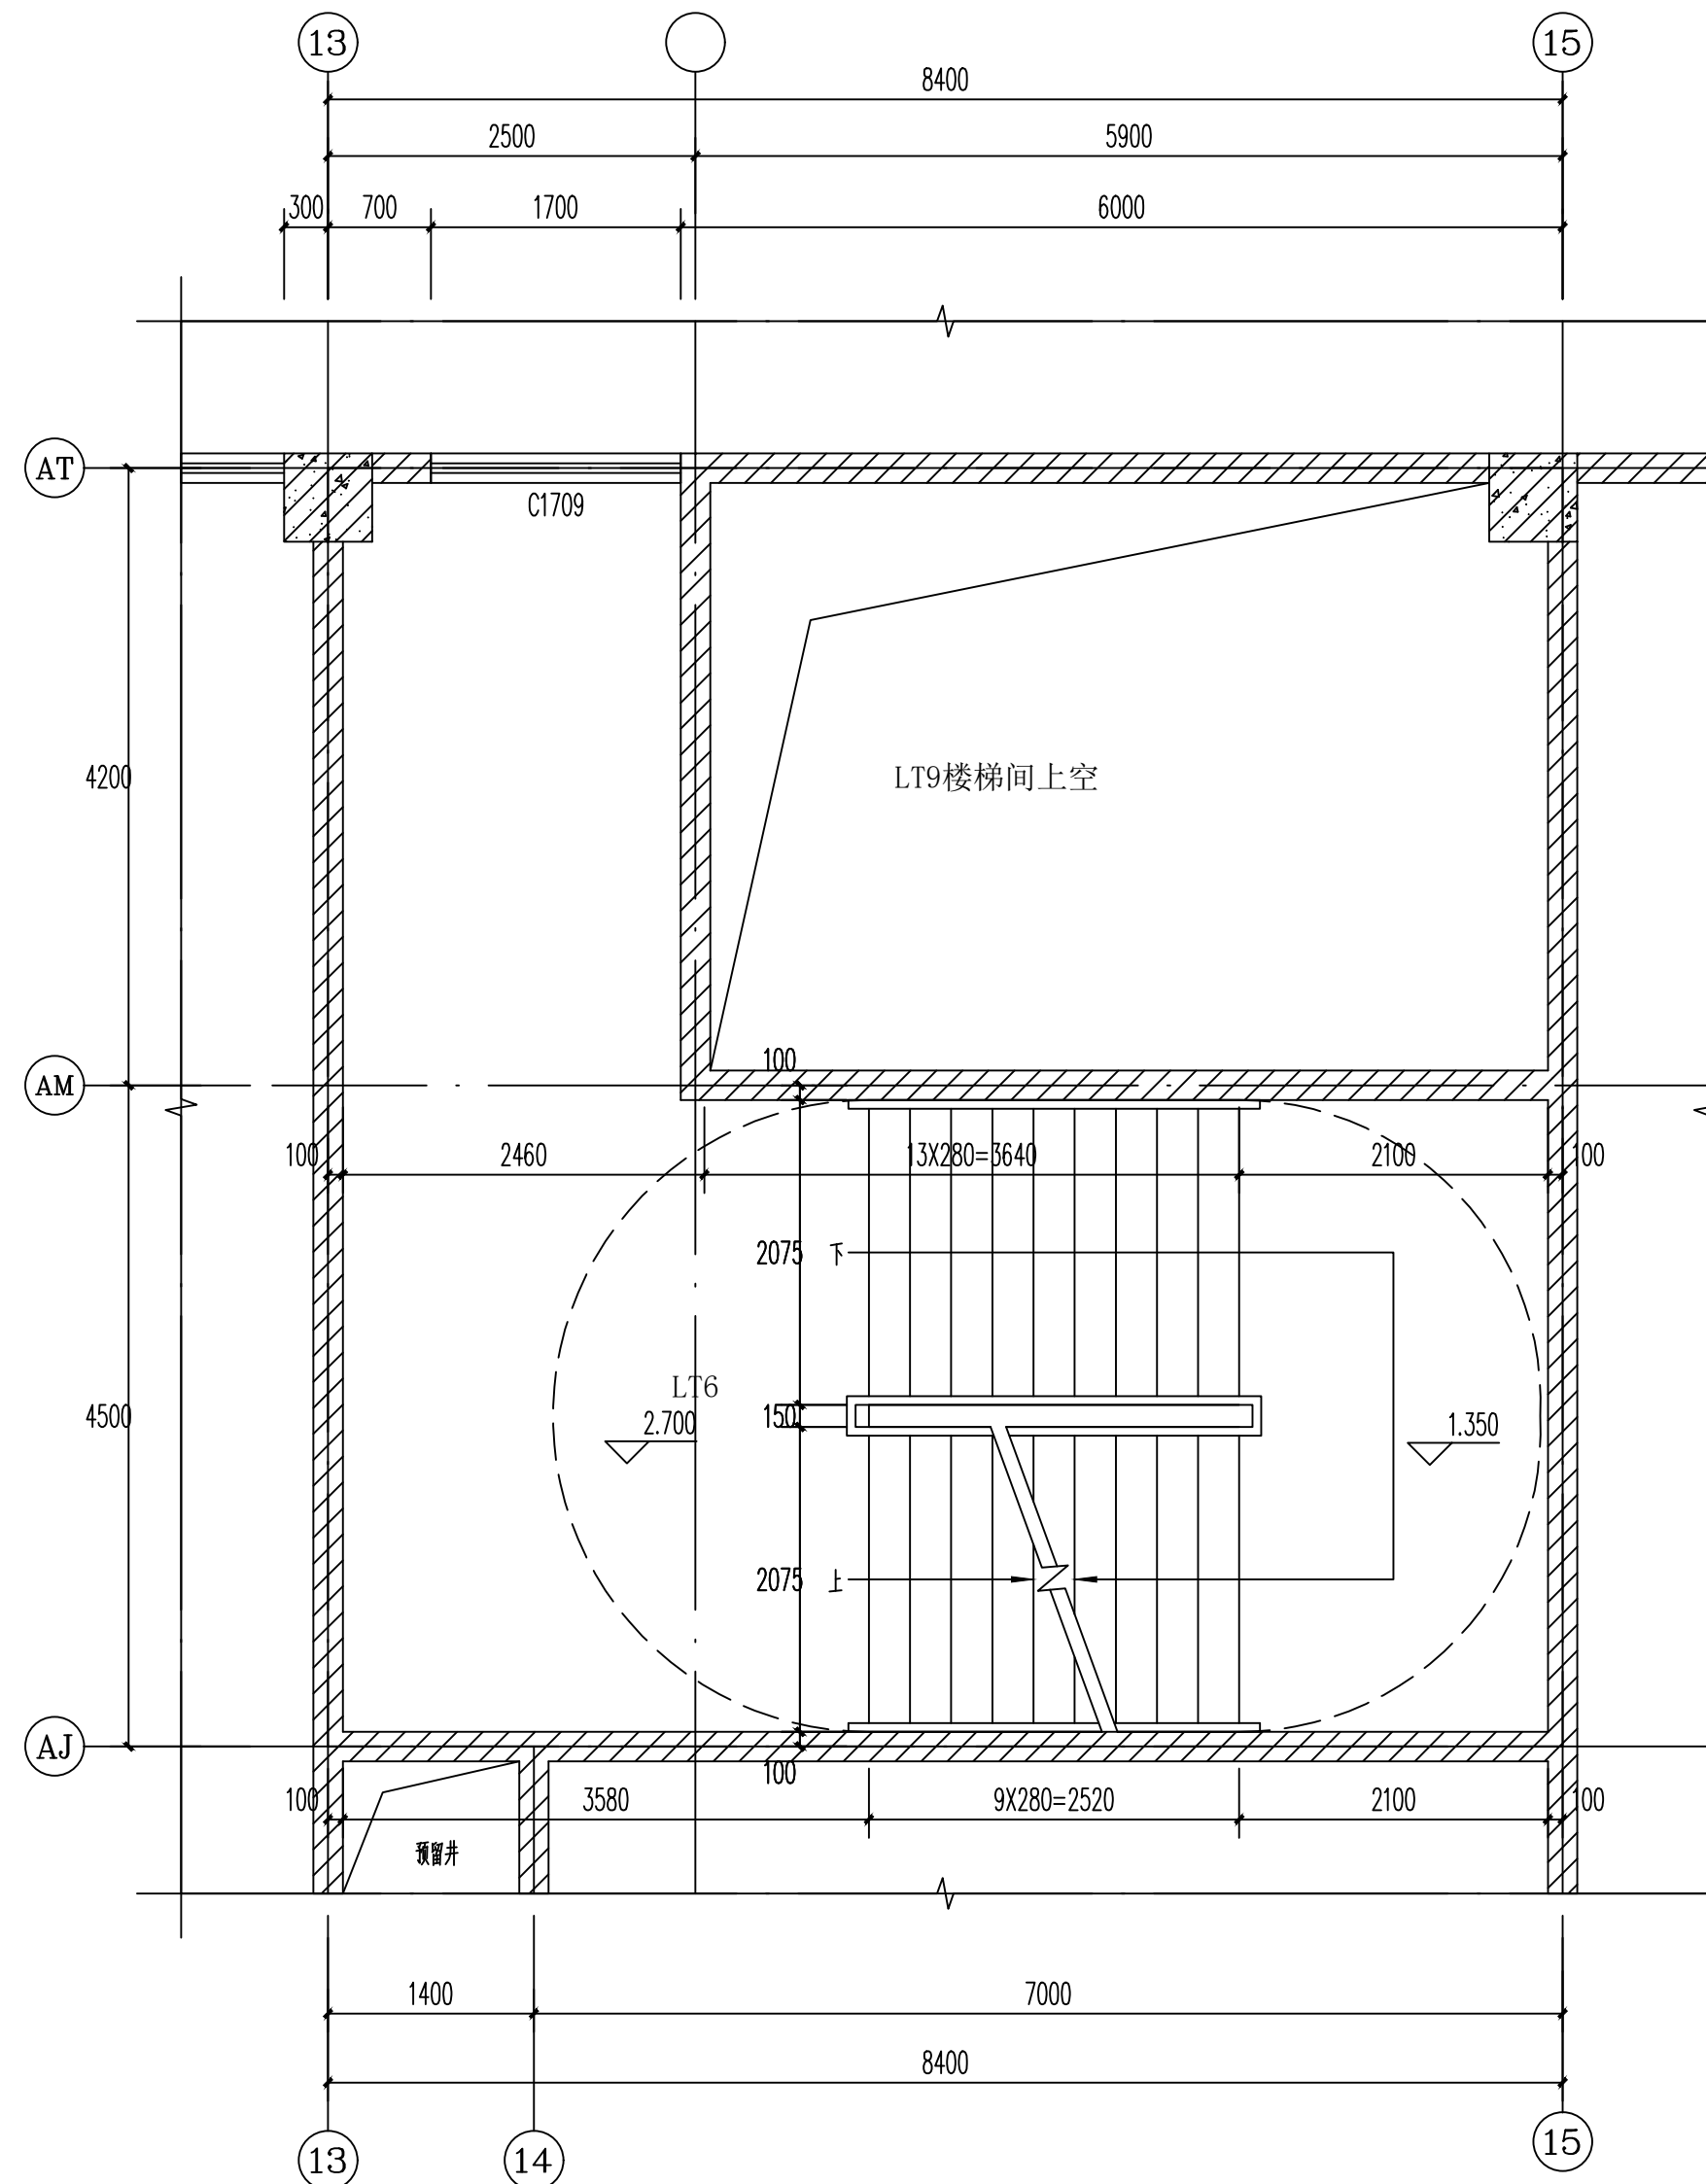


LT6楼梯间H=2.700处平面图 1:50

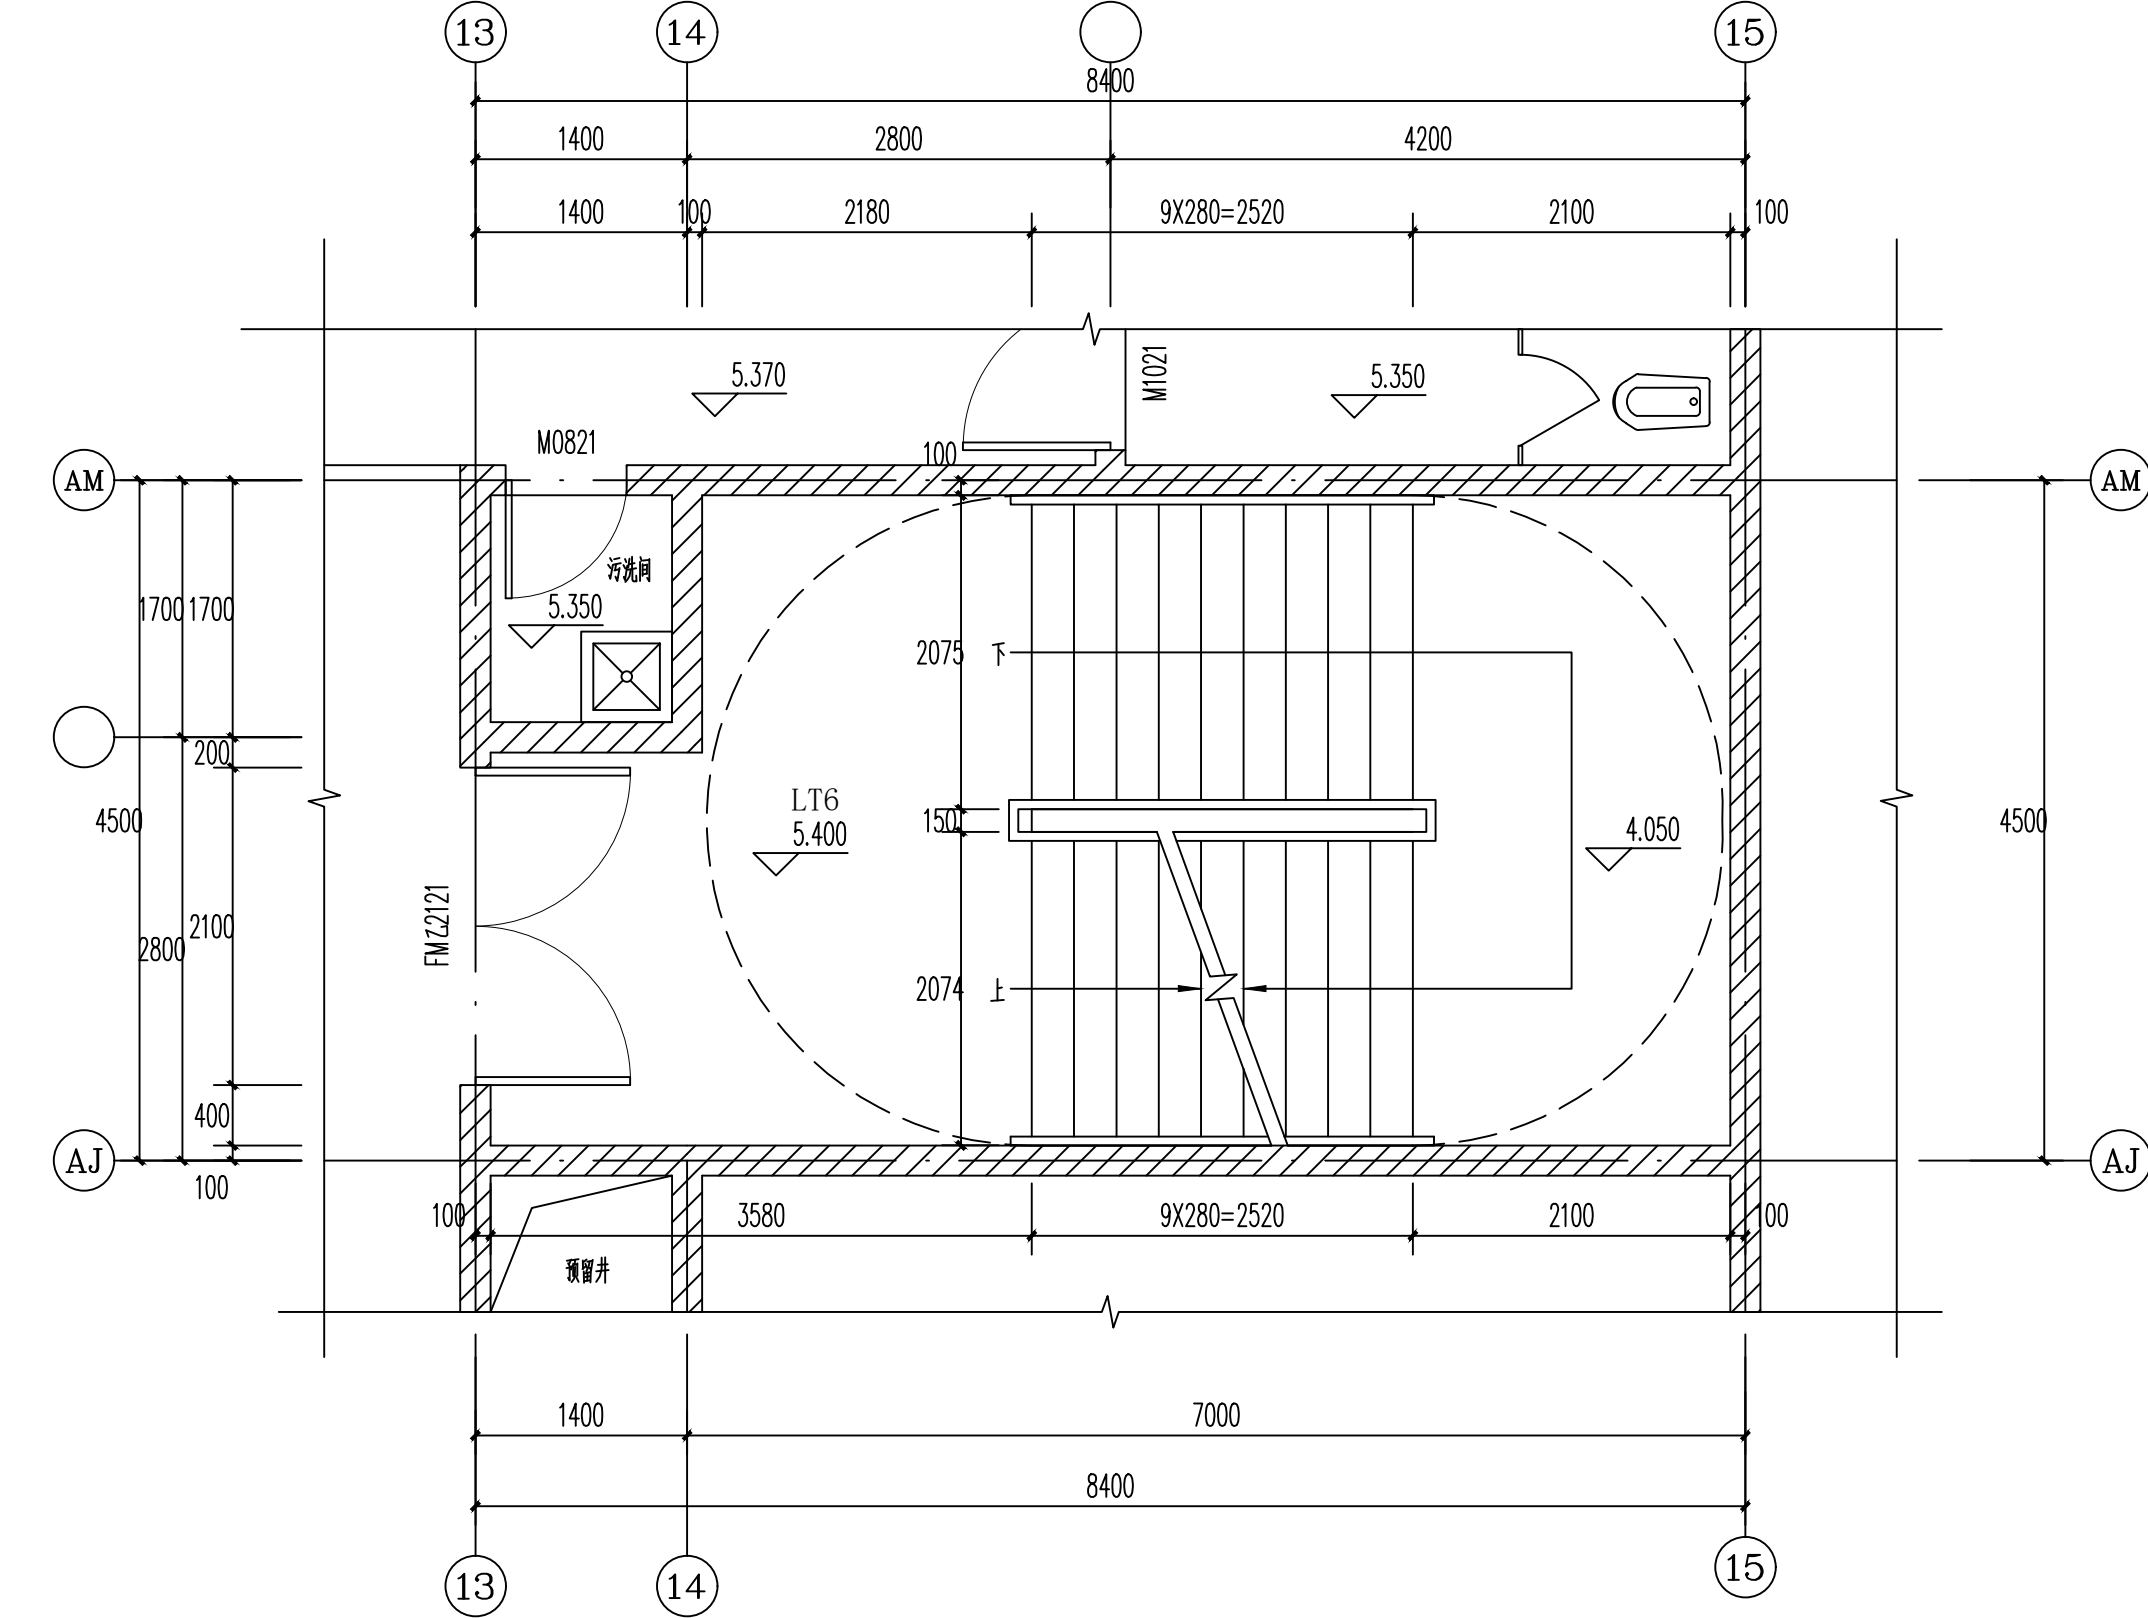


LT6楼梯间二层平面图 1:50

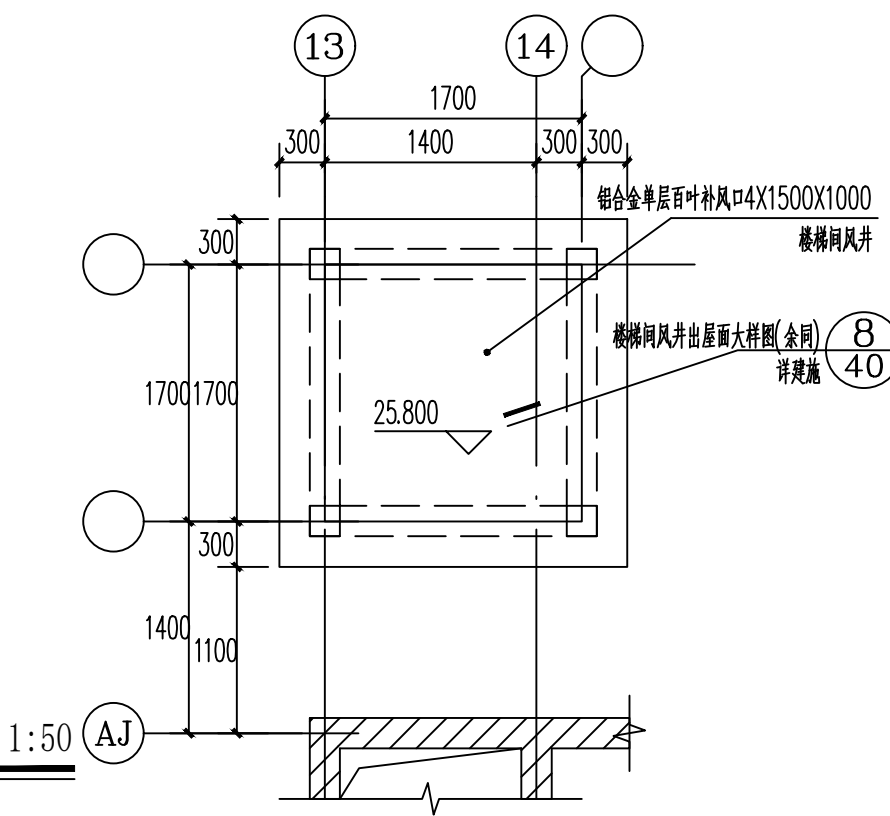


LT6楼梯间屋顶风井平面图 1:50

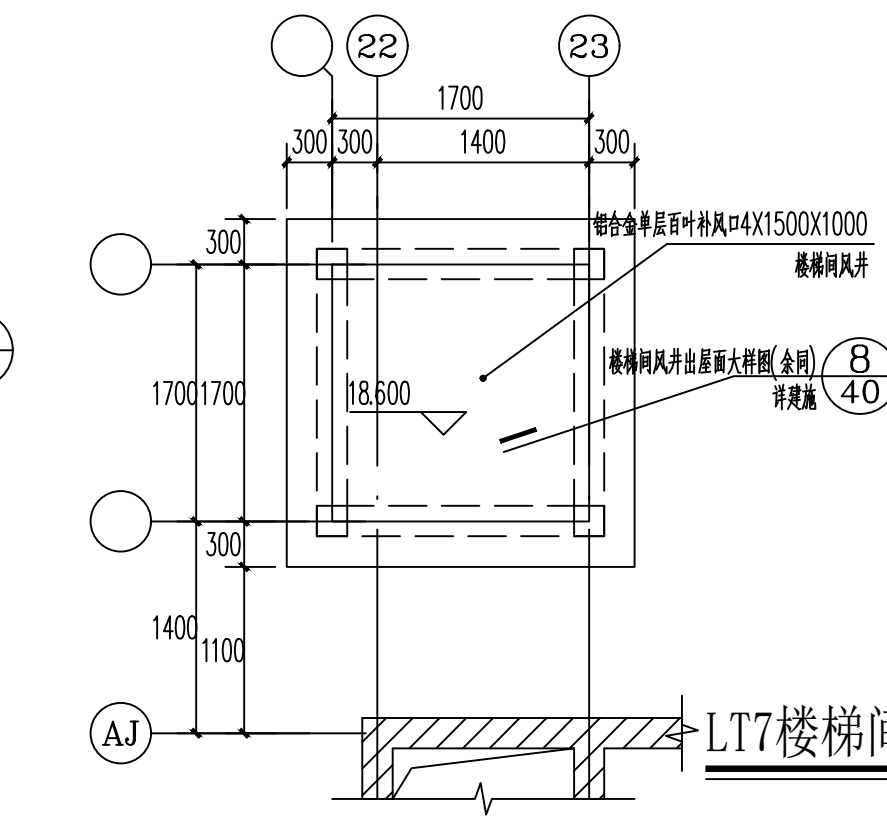


LT7楼梯间屋顶风井平面图 1:50

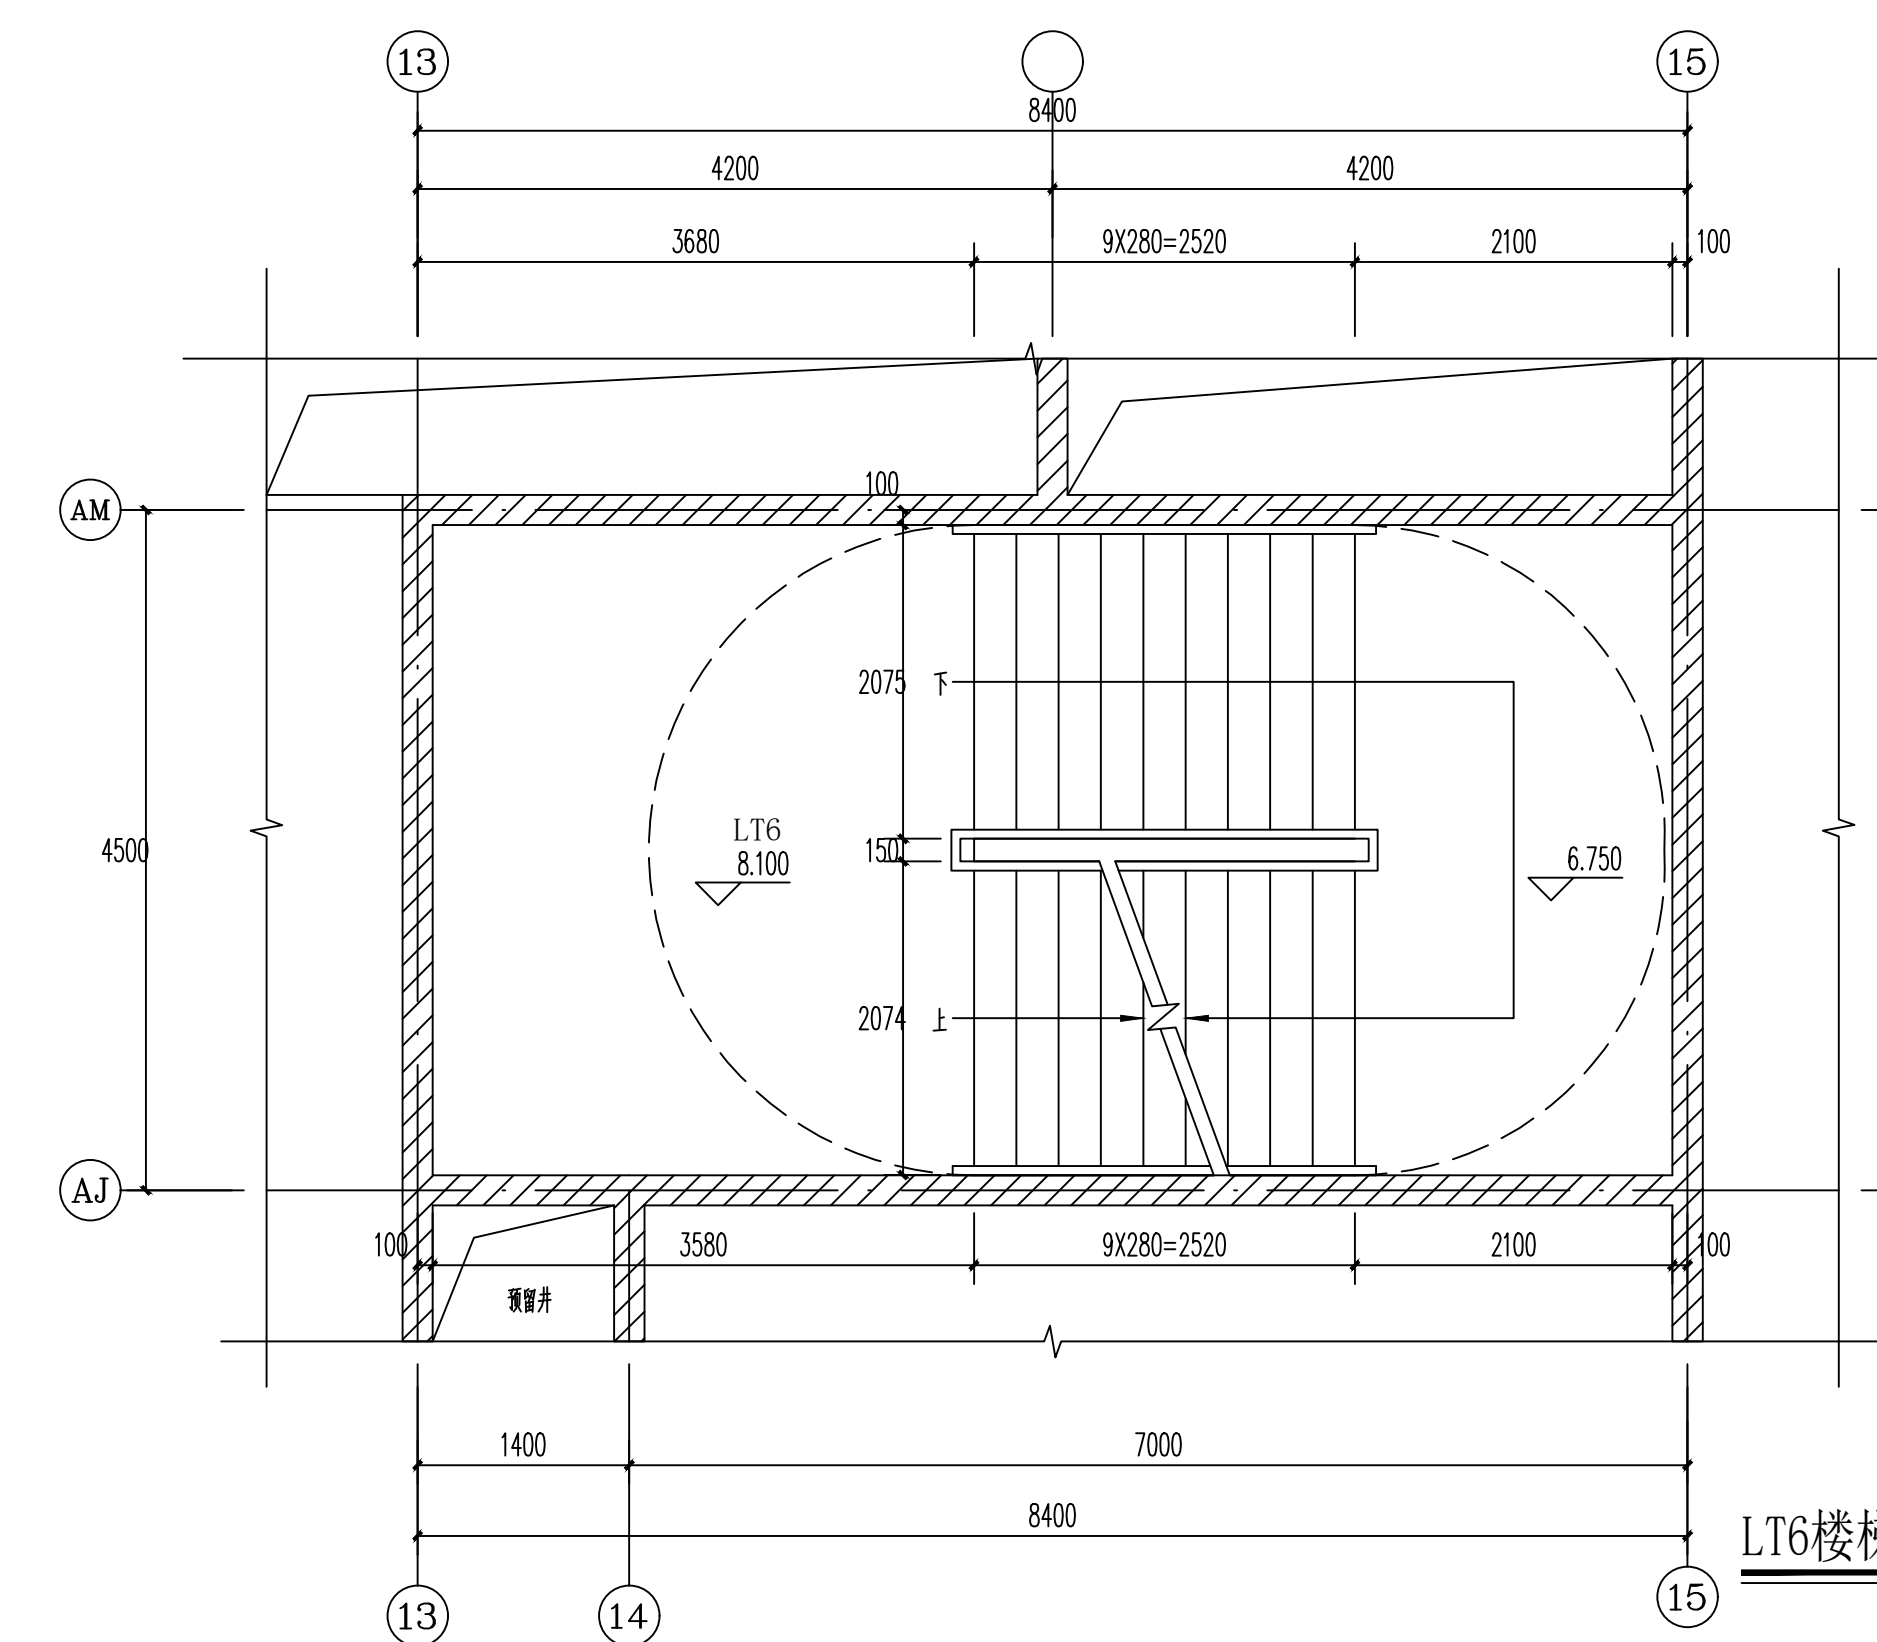


LT6楼梯间H=8.100处平面图 1:50

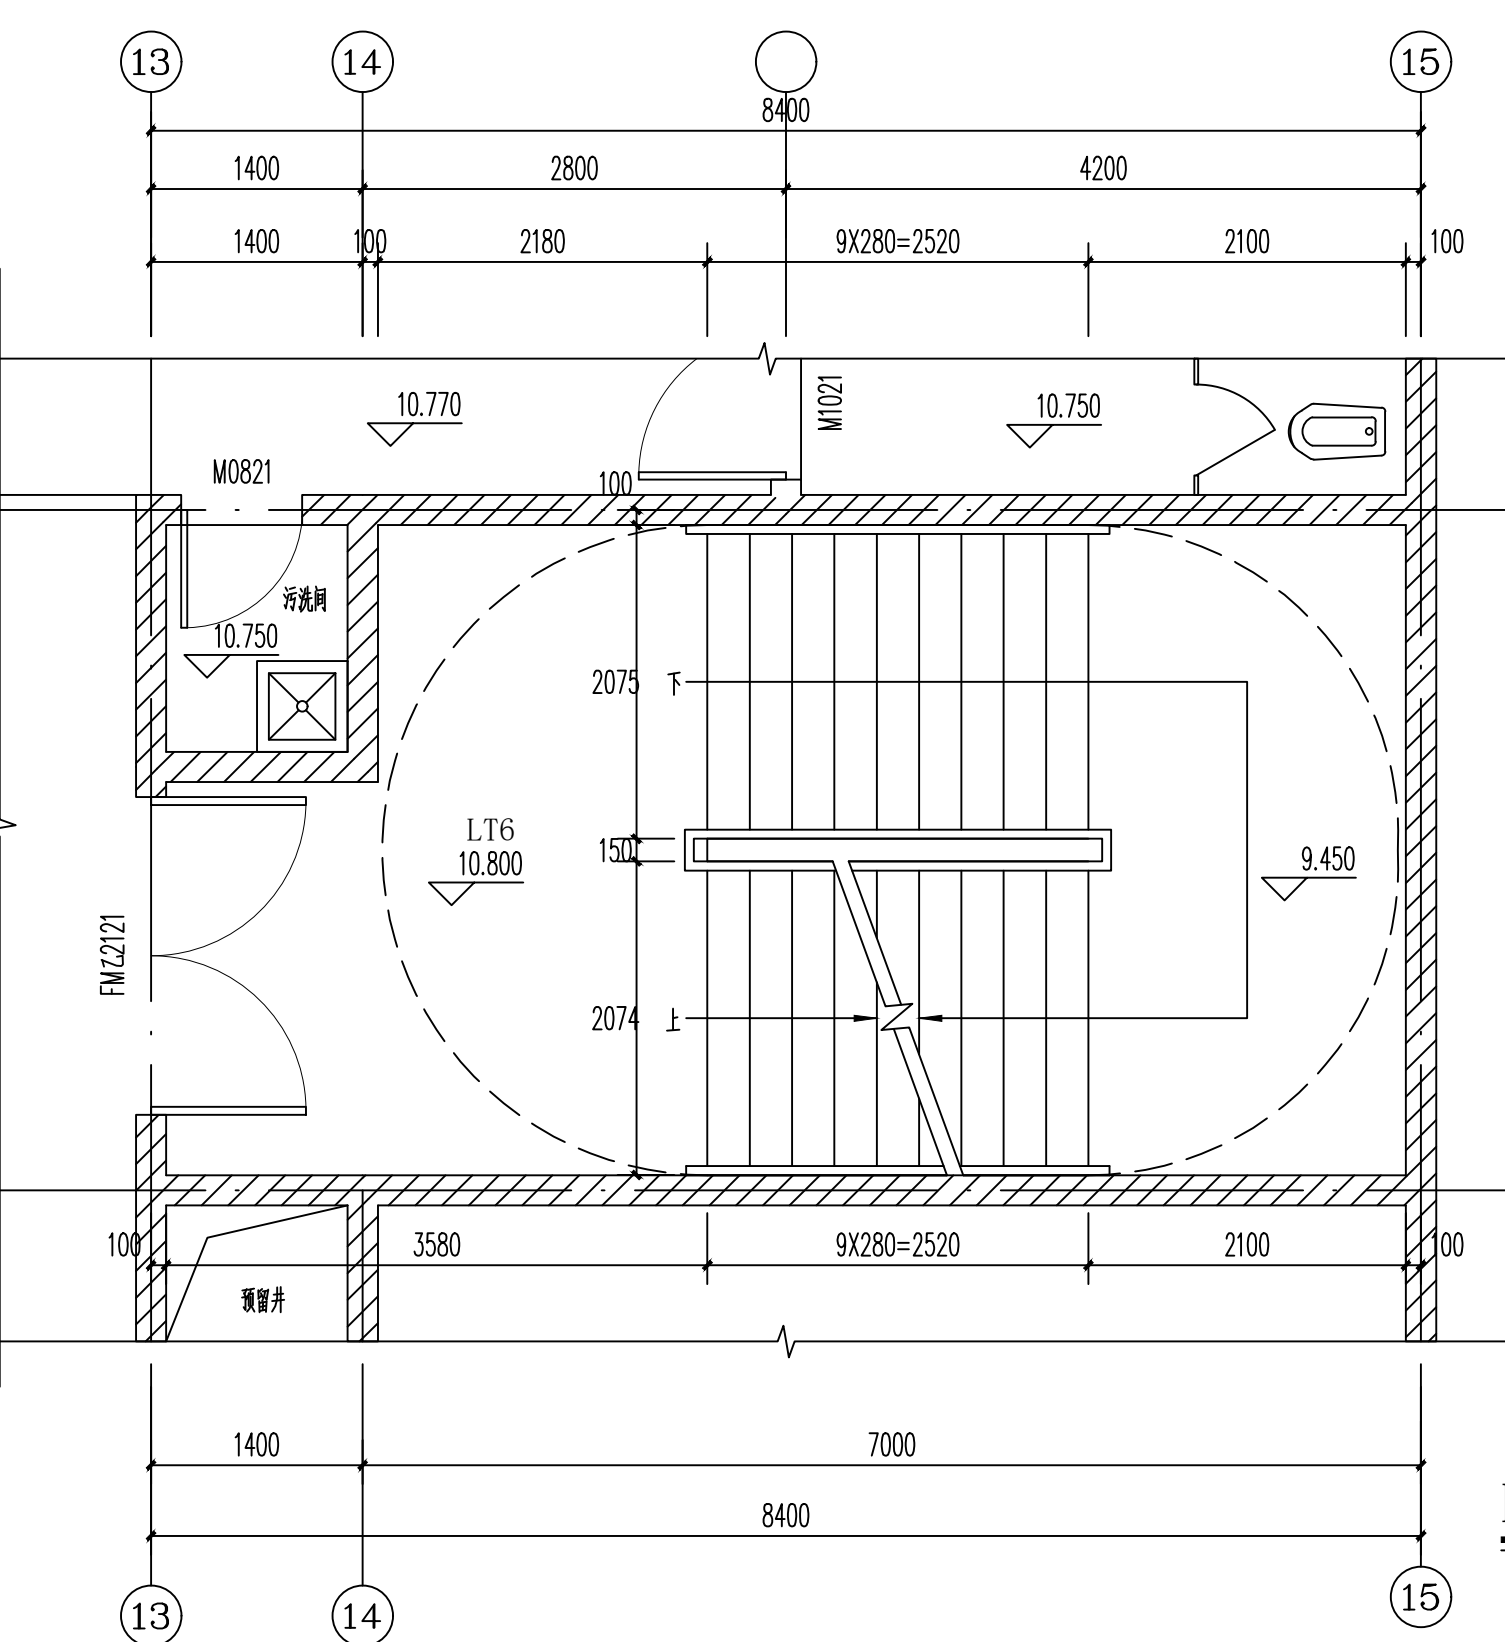

LT6楼梯间三层平面图 1:50

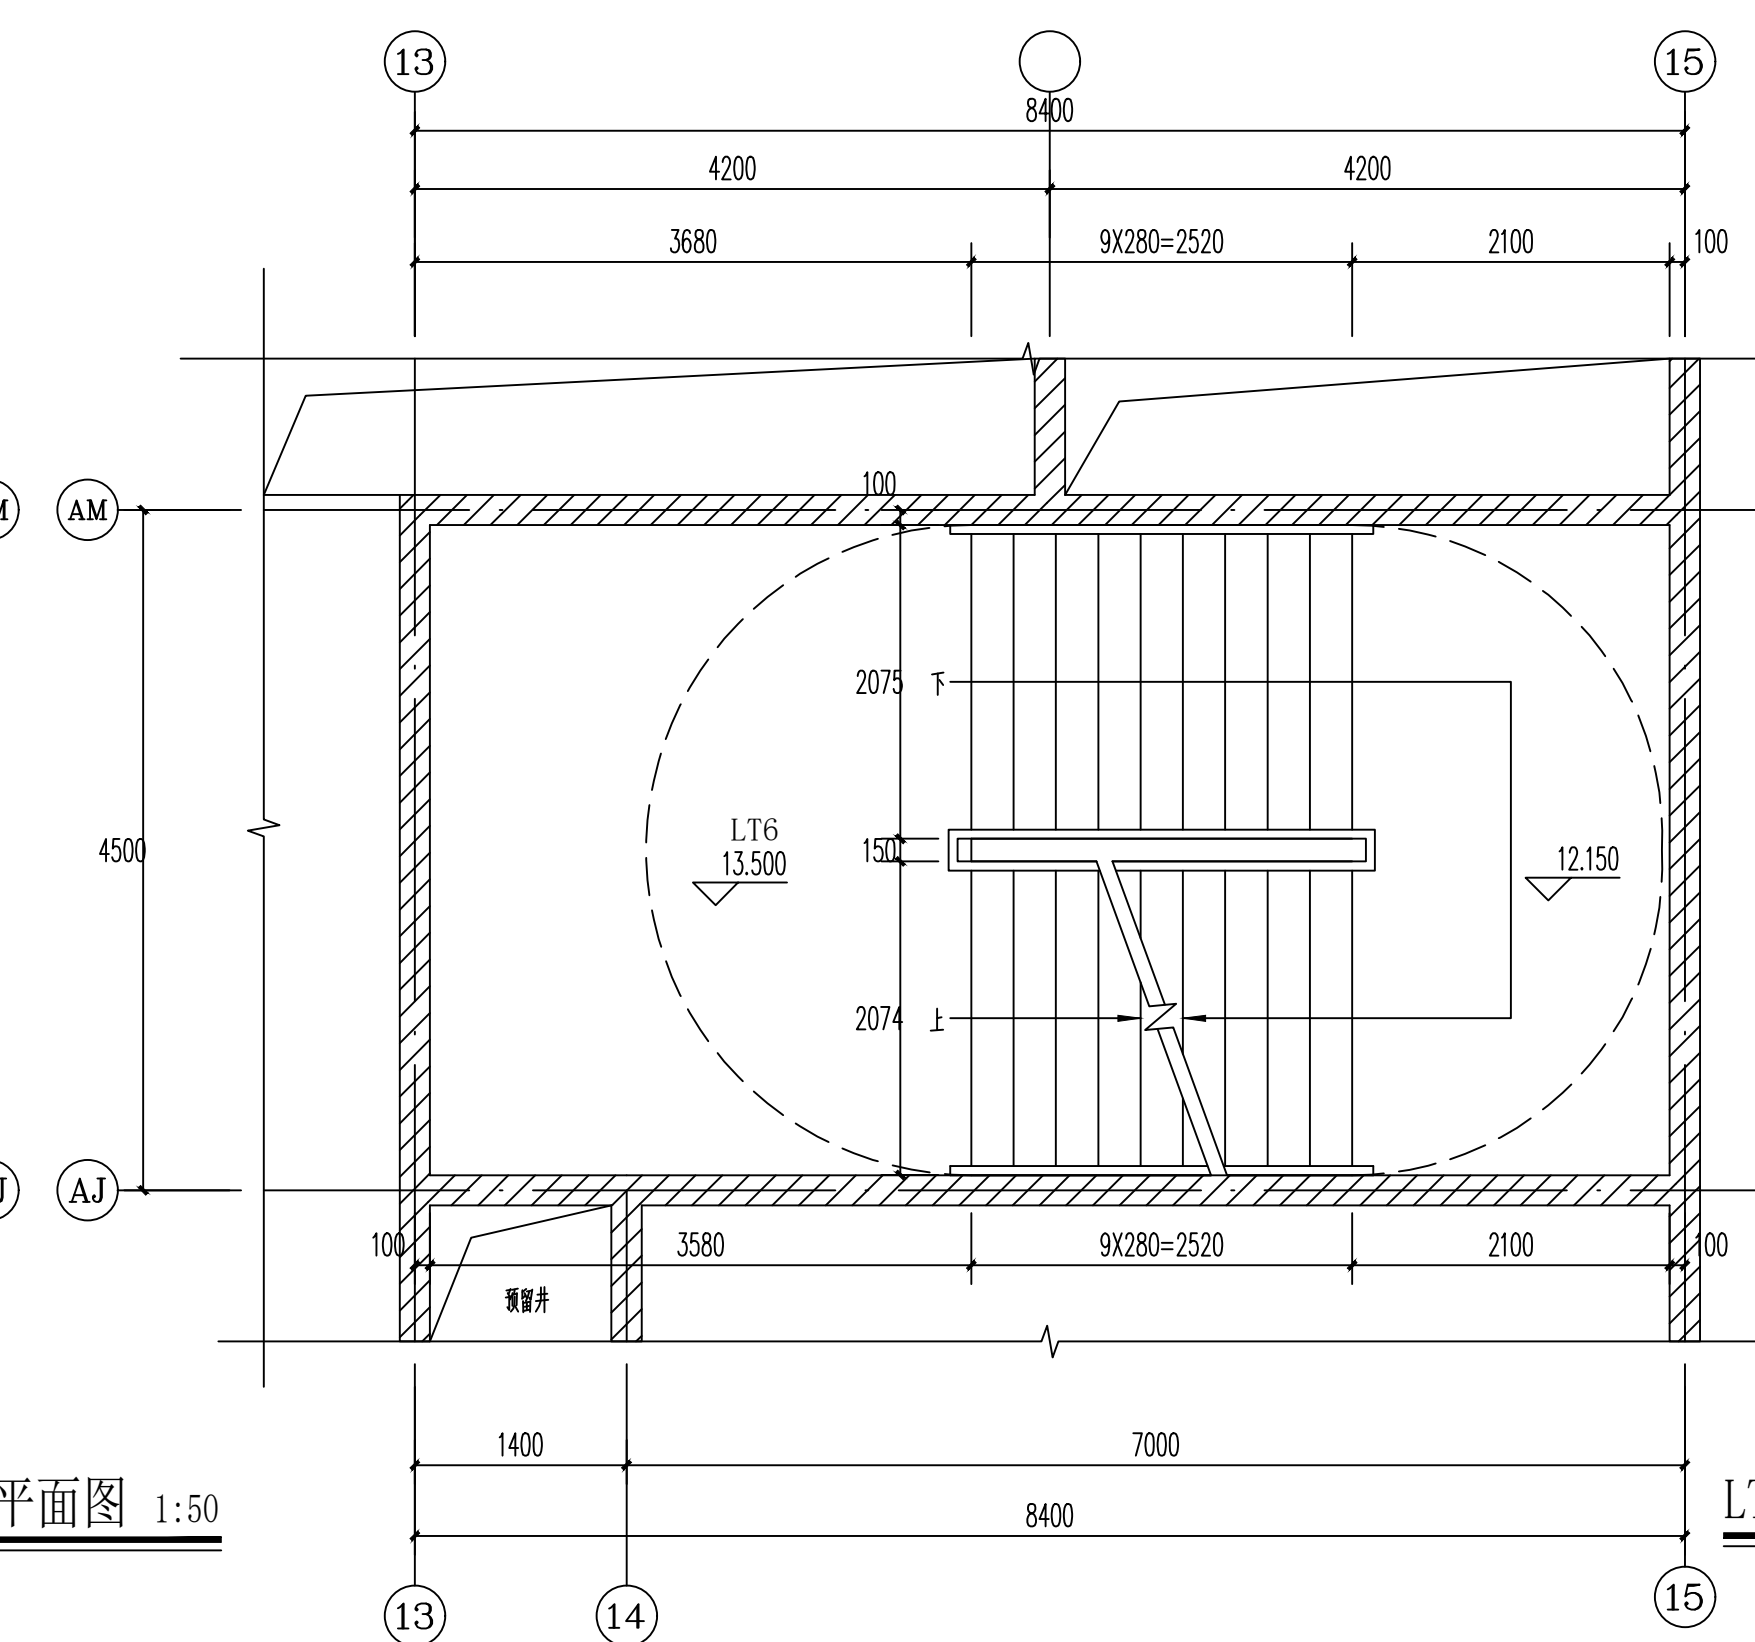

LT6楼梯间H=13.500处平面图 1:50

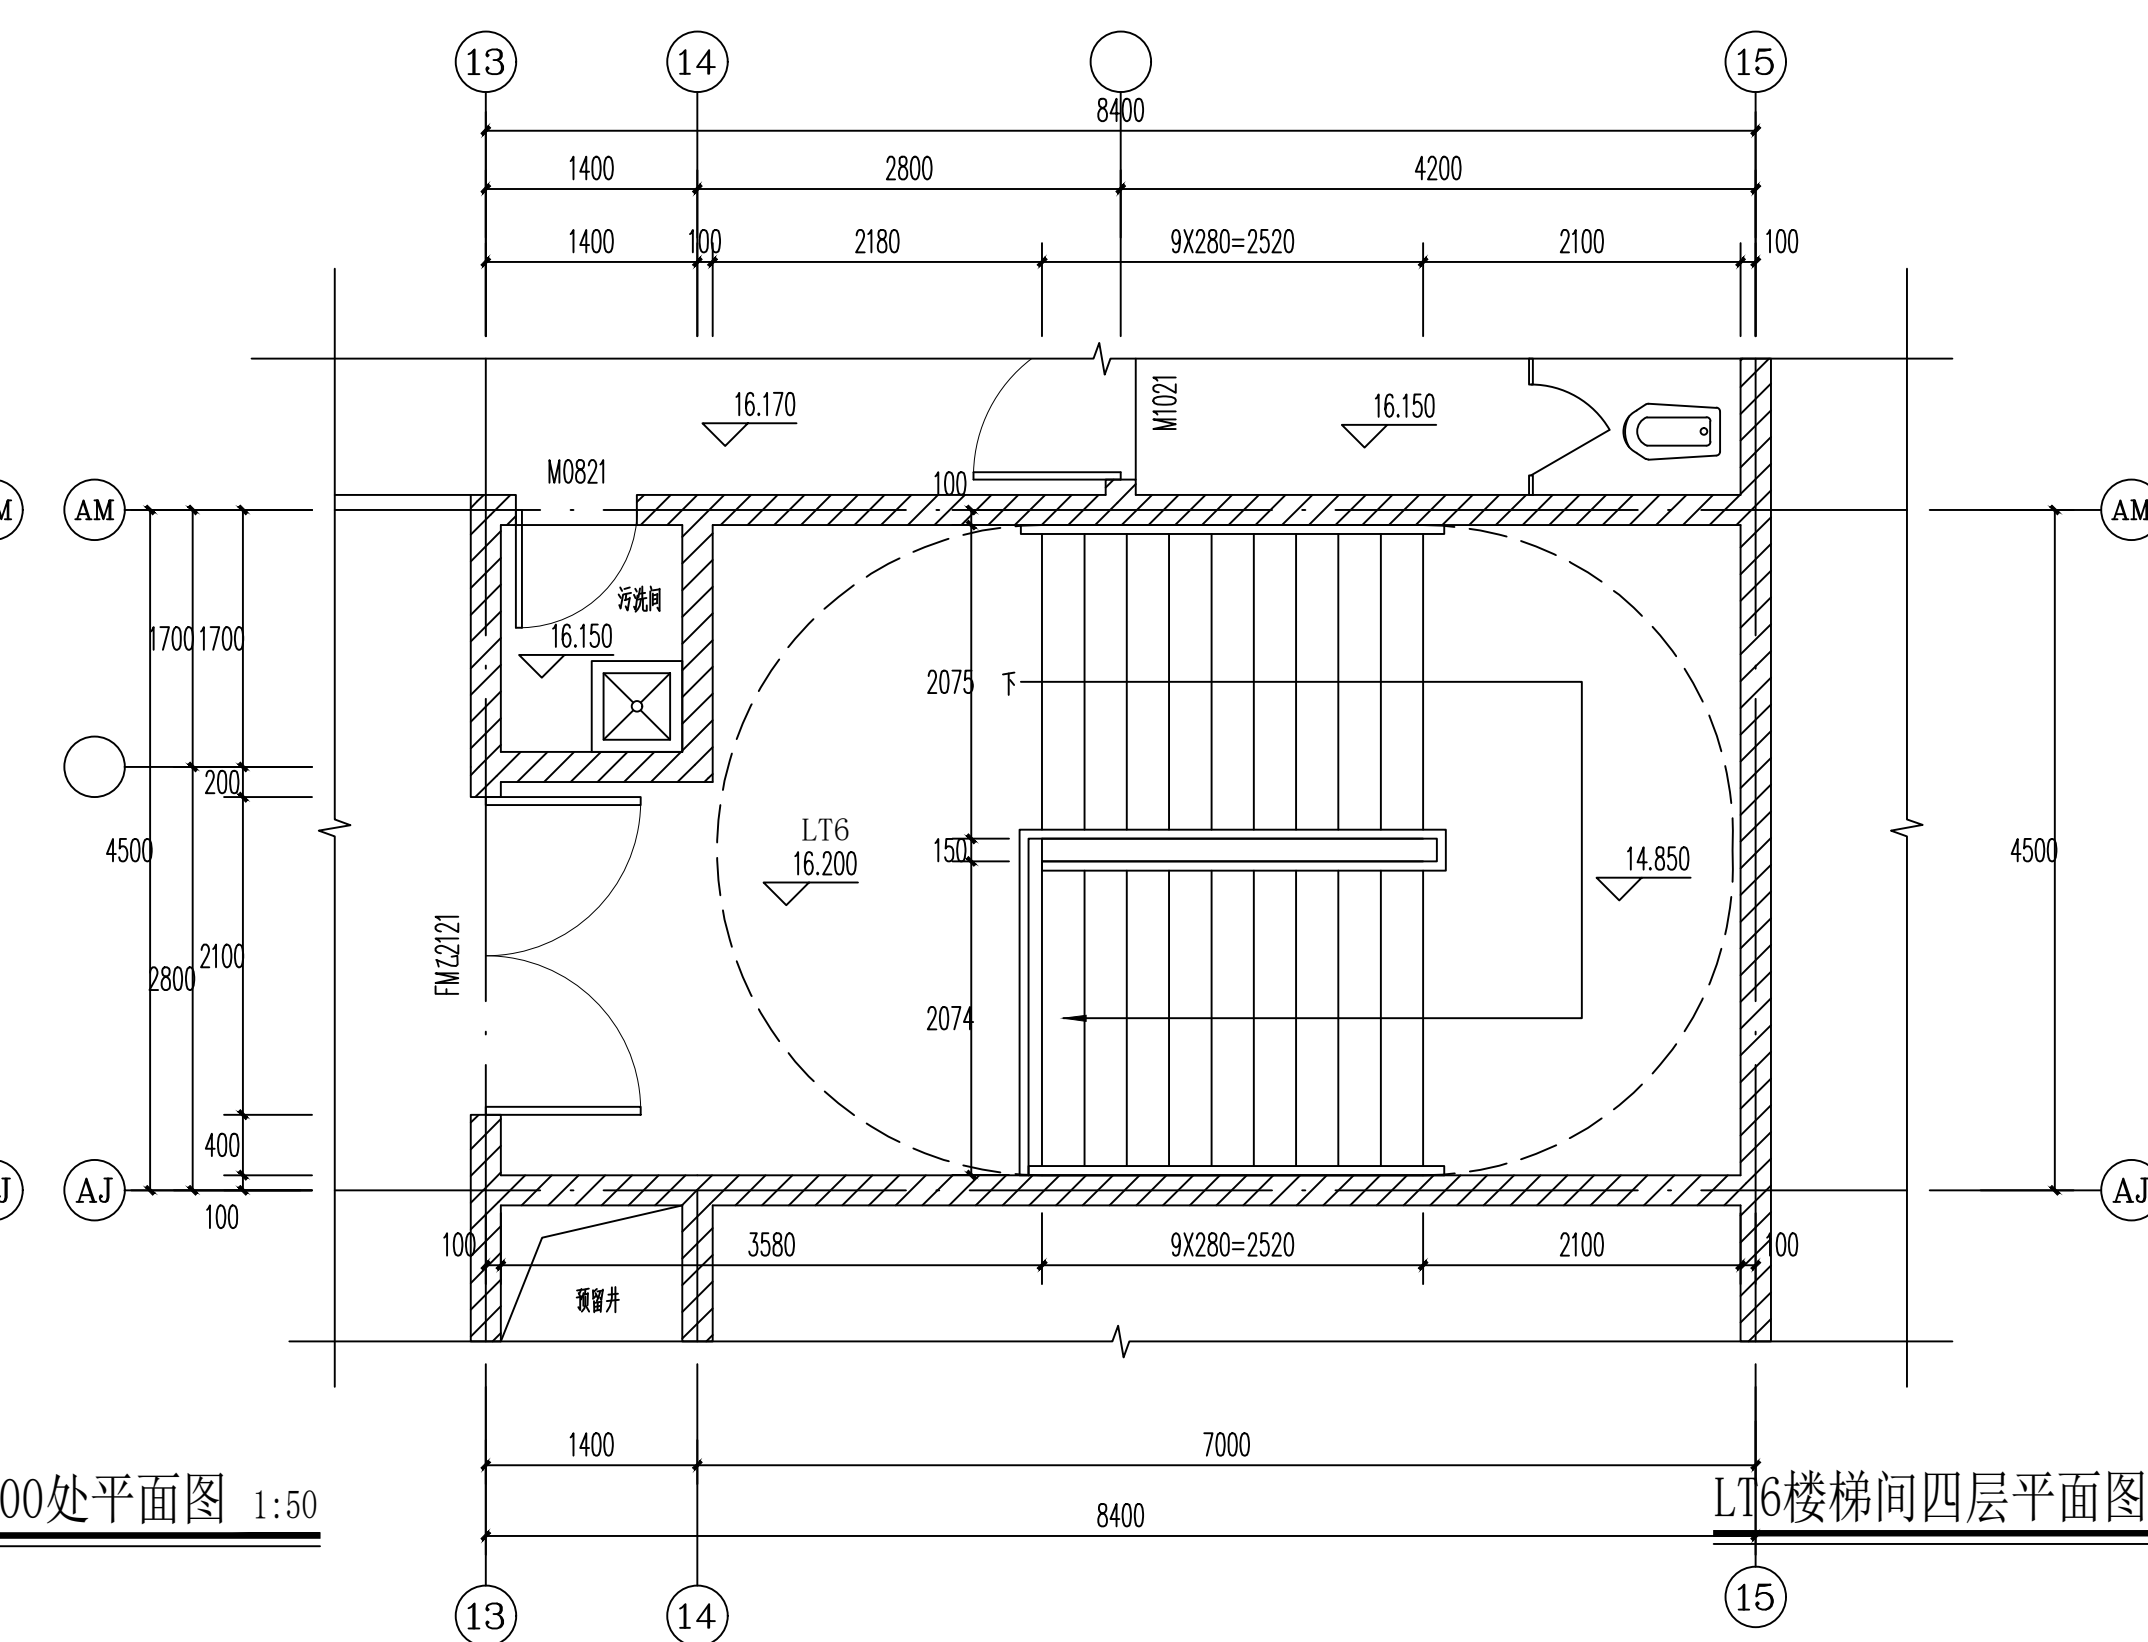

LT6楼梯间四层平面图 1:50

建设单位/CLIENT:
麻阳苗族自治县远桥房地产开发有限公司

项目名称/PROJECT:
远程国际

子项目名称/SUB-PROJECT:
远程国际

区位图/REGIONAL LOCATION MAP :

广东建筑艺术设计院有限公司
GUANGDONG ARCHITECTURAL ARTISTIC DESIGN INSTITUTE CO.,LTD
■ 建筑方案设计: 甲级 ■ 风景园林设计: 乙级
■ 城乡规划设计: 乙级 ■ 市政工程设计: 乙级

图纸名称/TITLE:
LT6、LT9楼梯间大样图

项目名称/PROJECT:
远程国际

设计 DESIGNED	古新辉	
校对 CHECKED	吴新红	
专业负责人 CHIEF	吴志刚	
项目负责人 PROJECT CHIEF	吴志刚	
审核 IDENTIFIED	黄展优	
审定 APPROVED	李 坚	

业务号/JOB NO.

设计阶段/STATUS: 施工图

专业/DISCIPLINE: 建筑

比例/SCALE: 1: 100 规格/SIZE: A1

出图日期/DATE: 2021. 06

图号/DRAWING NO. JS-33

版次 NO.	修改内容 DESCRIPTION	日期 DATE

条形码/BARCODE:

版权所有, 不得复制、套用。
ALL RIGHTS RESERVED, DON'T COPIED, REPRODUCED.