




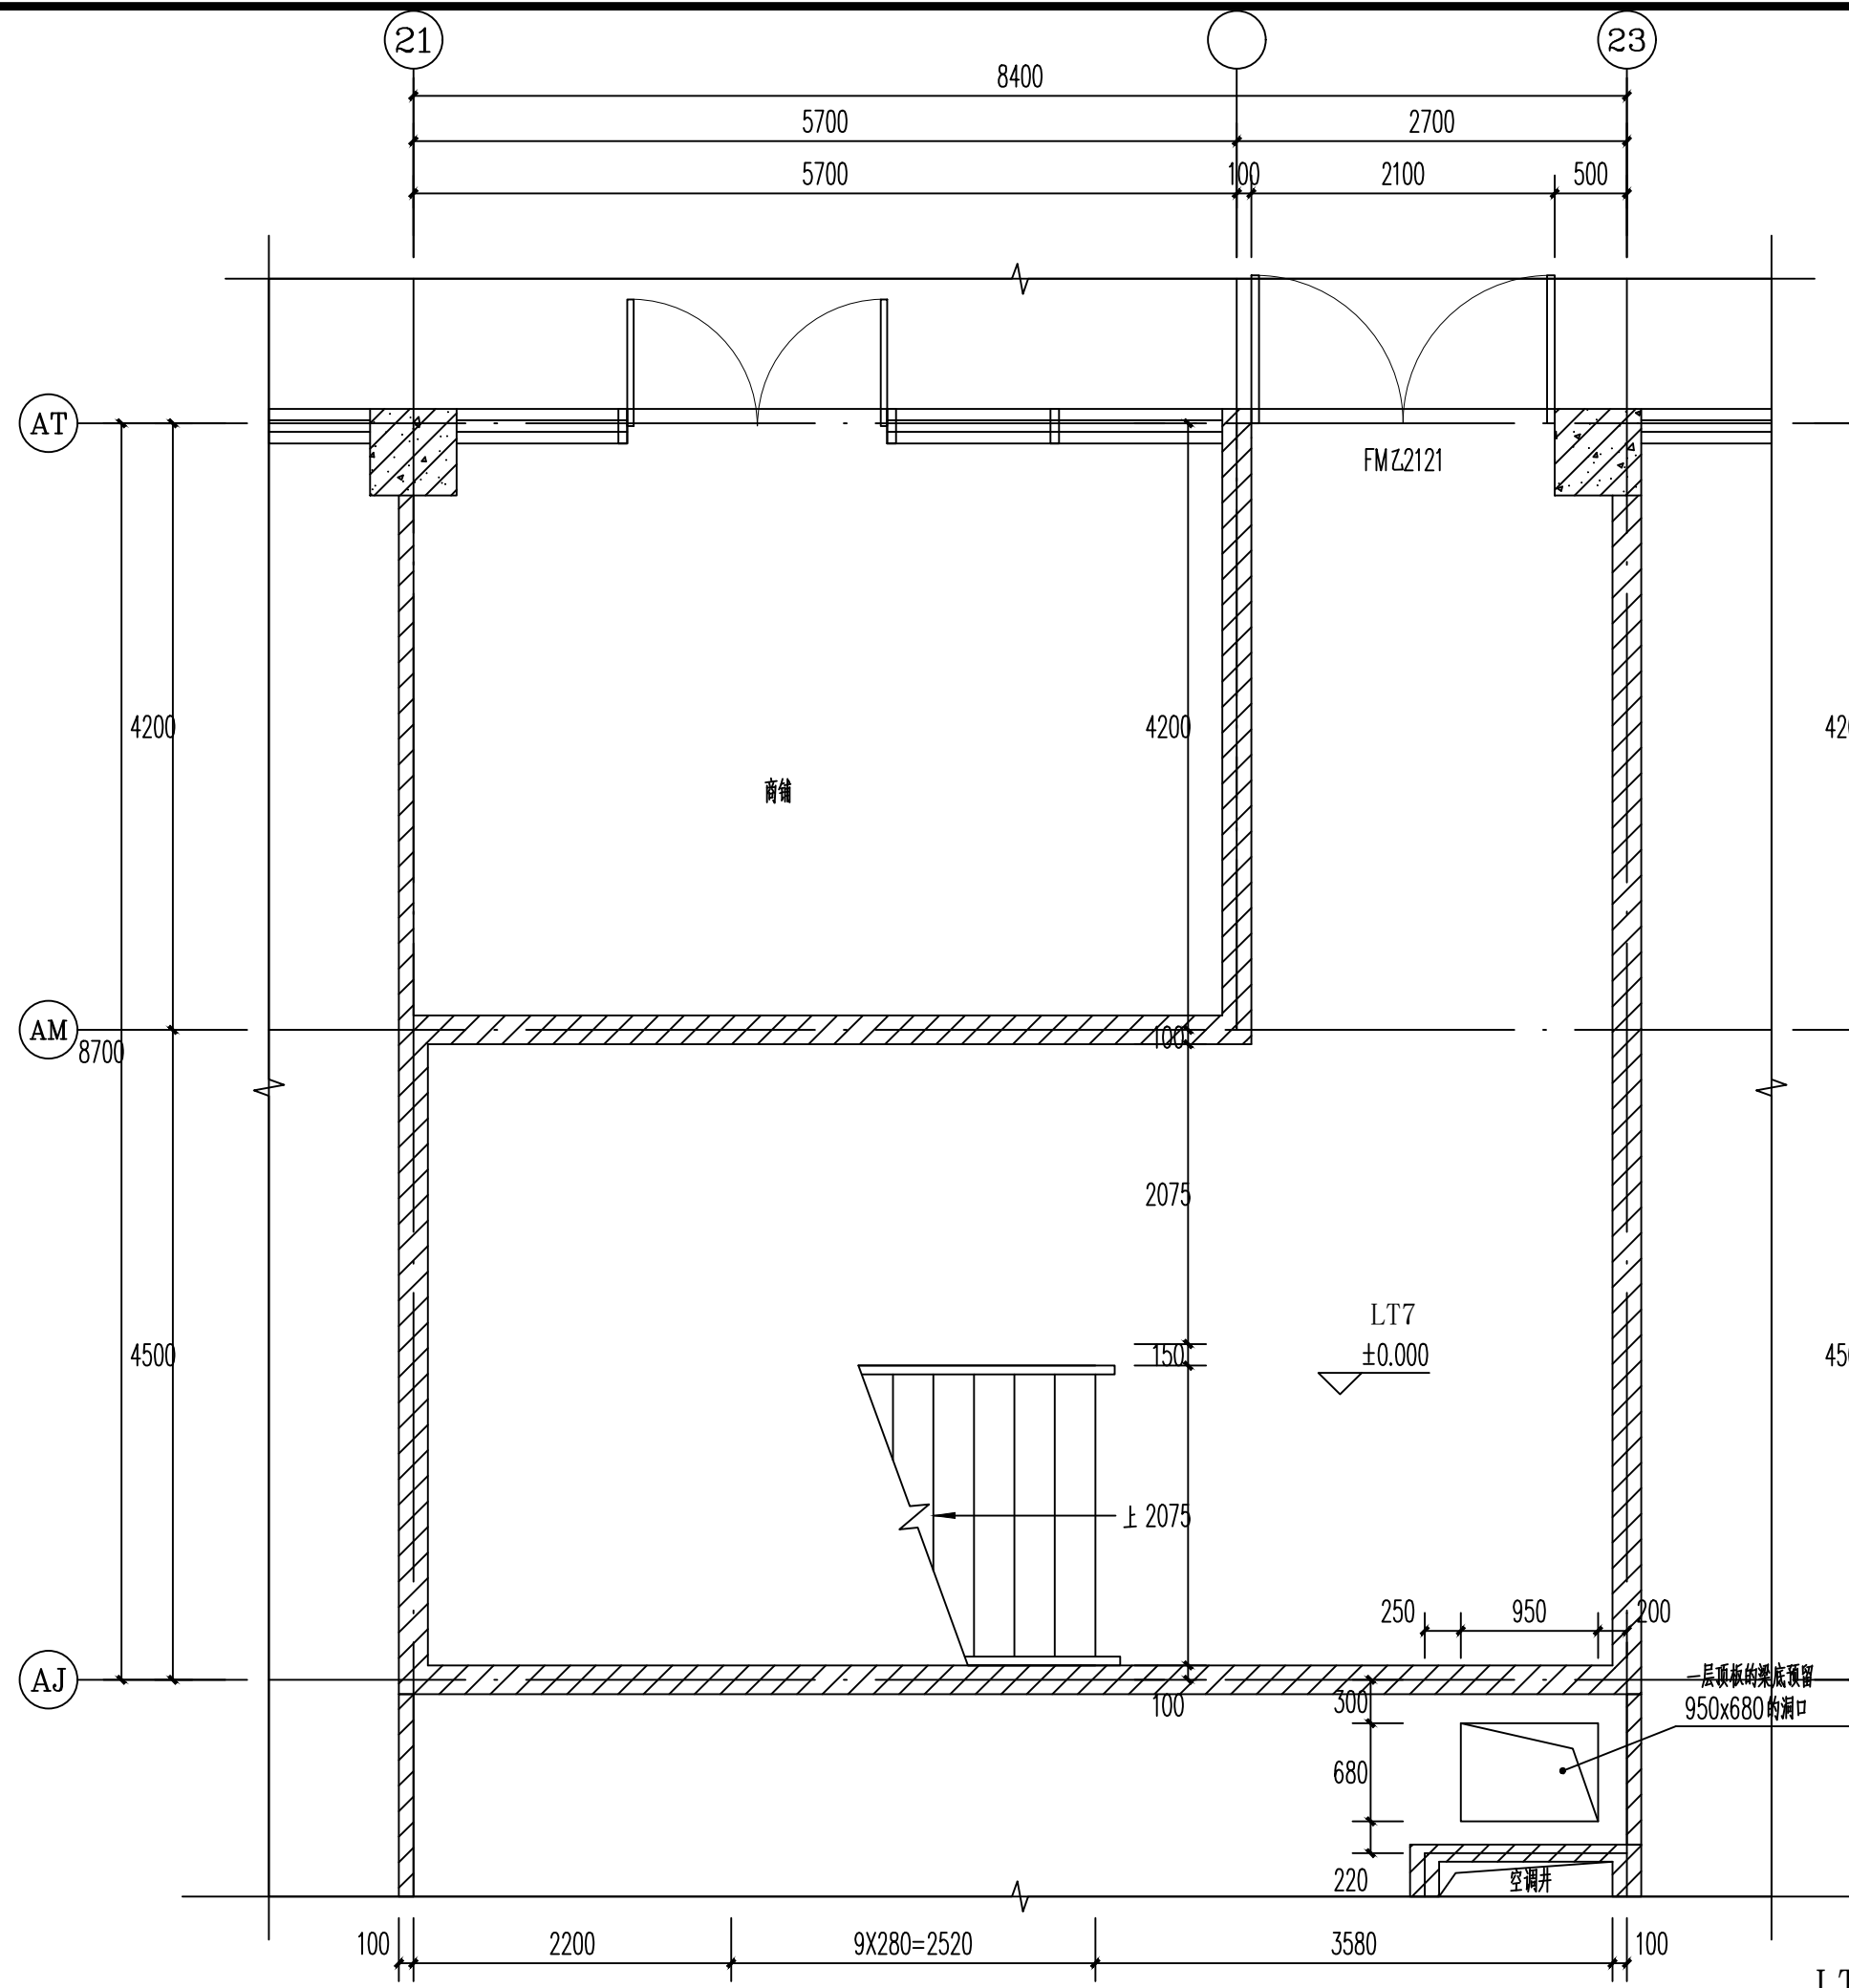


LT7楼梯间一层平面图 1:50

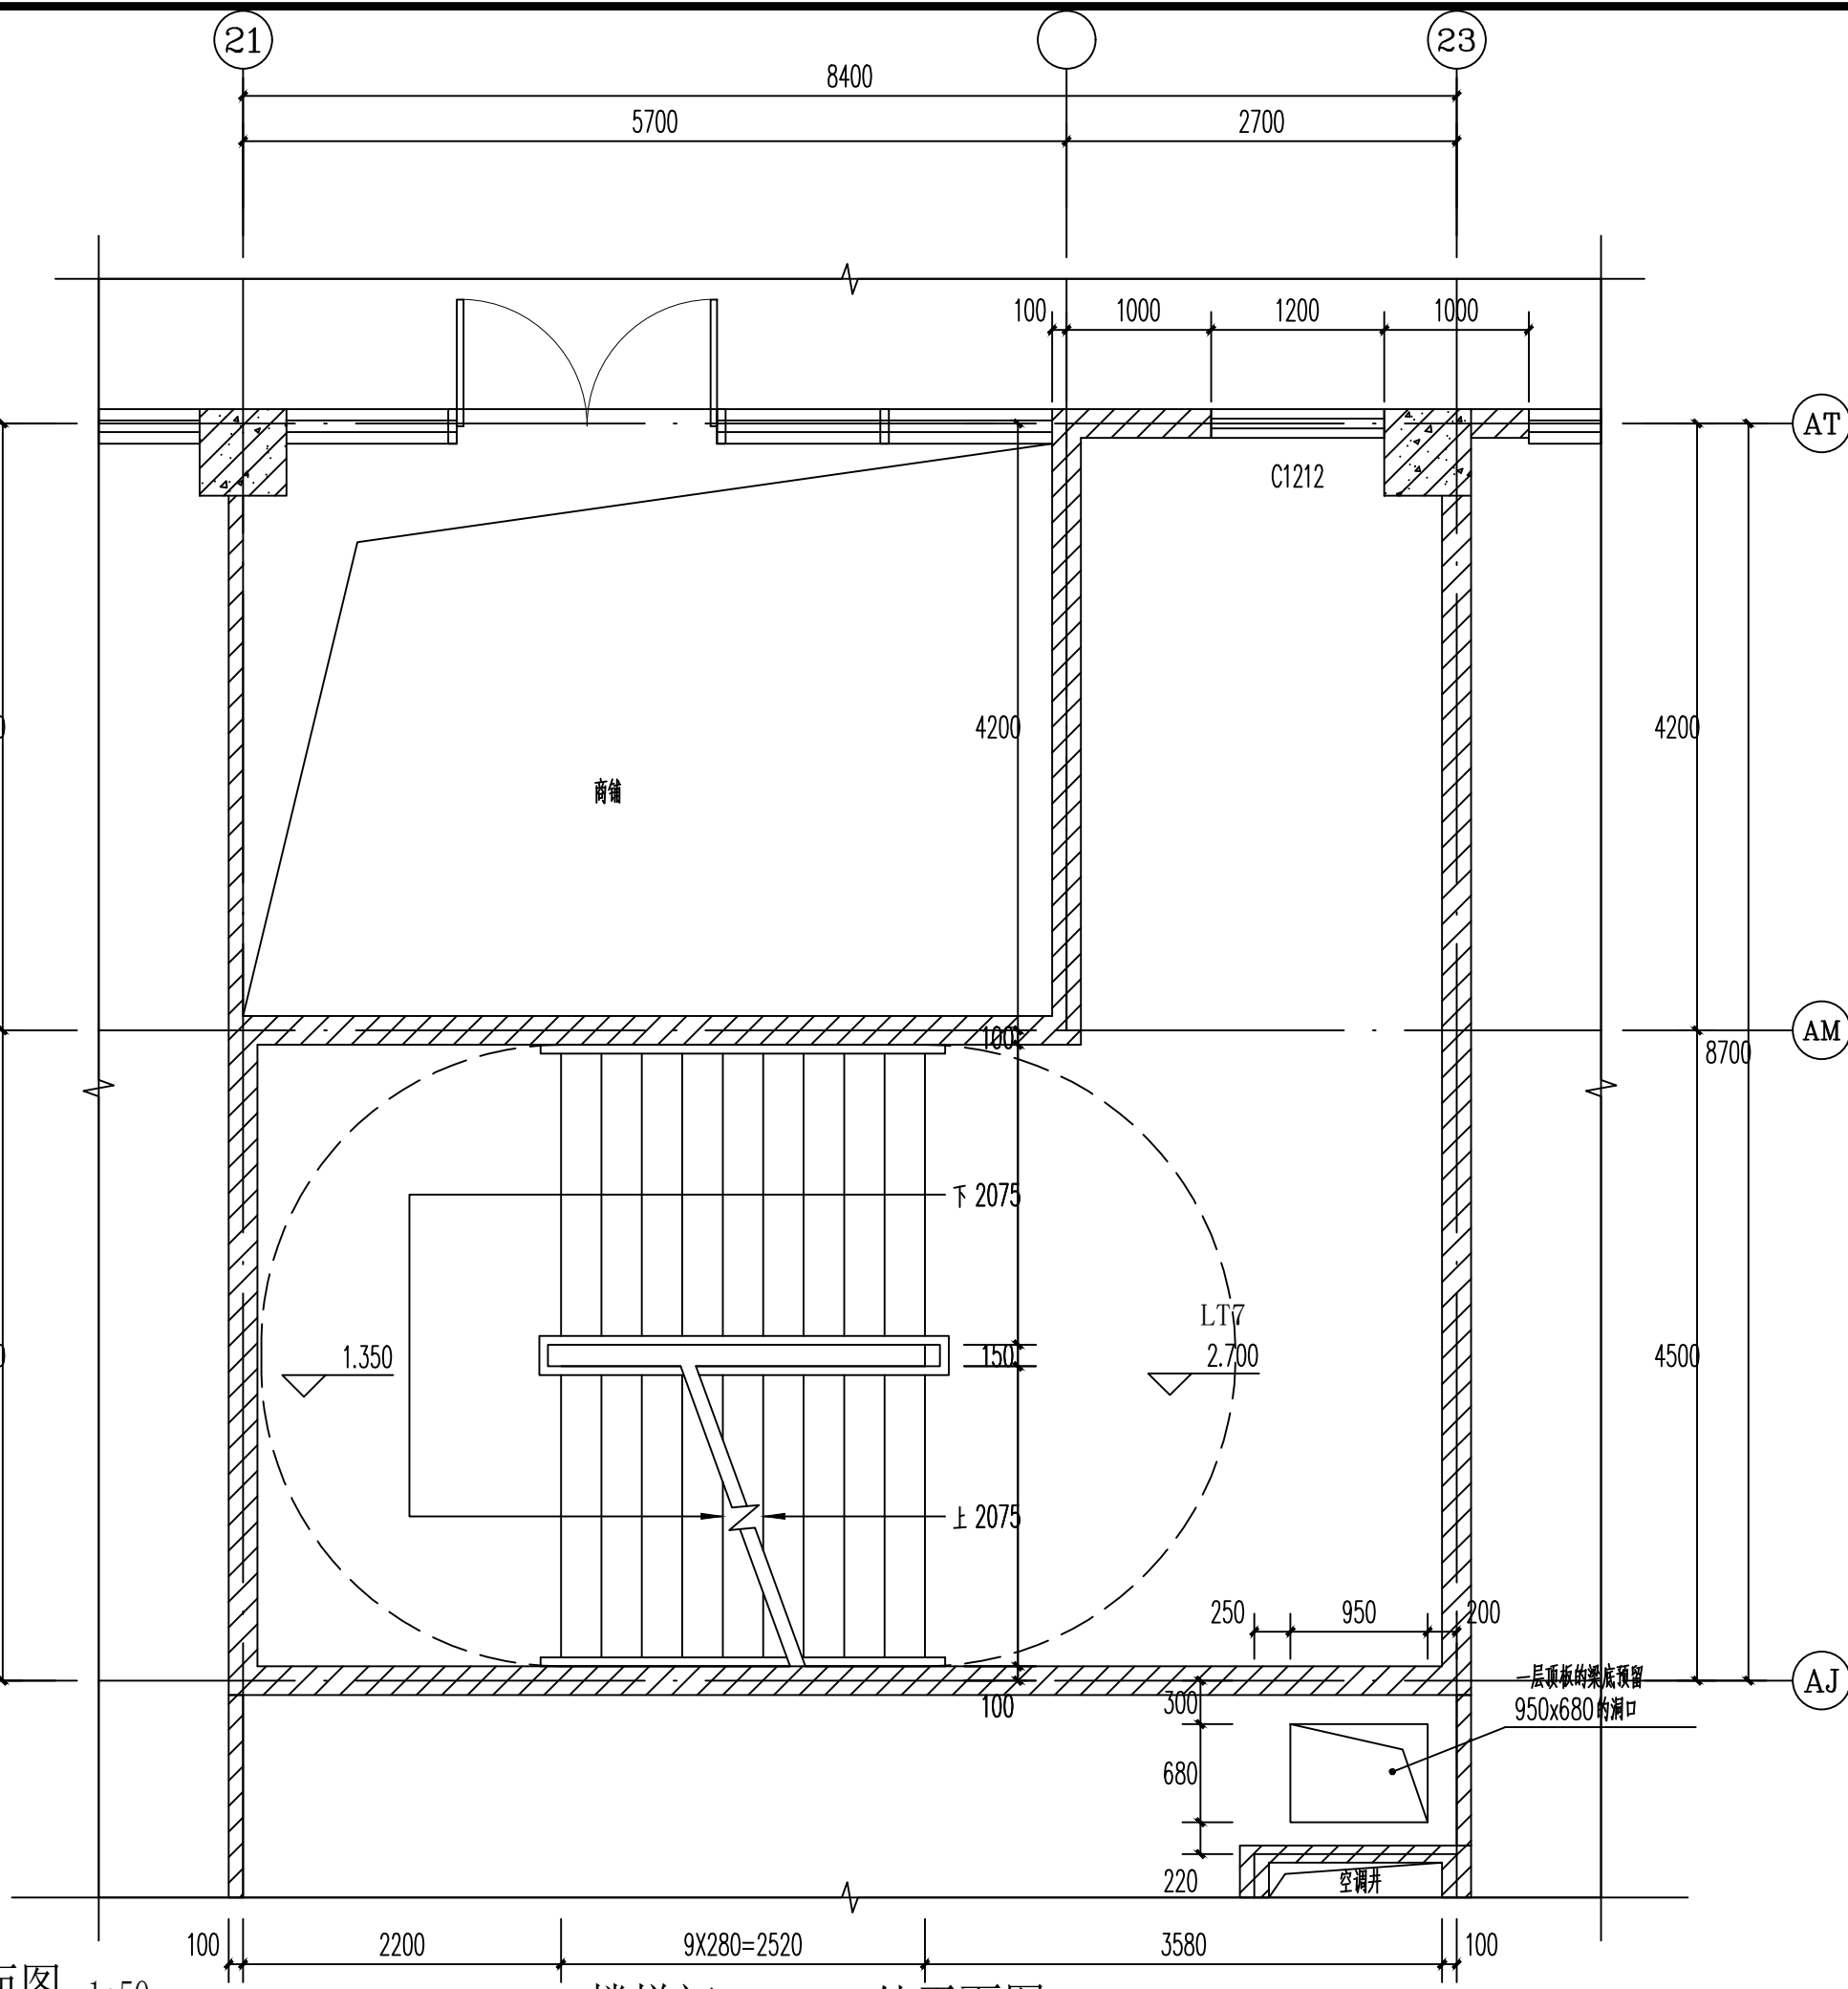


LT7楼梯间H=2.700处平面图 1:50

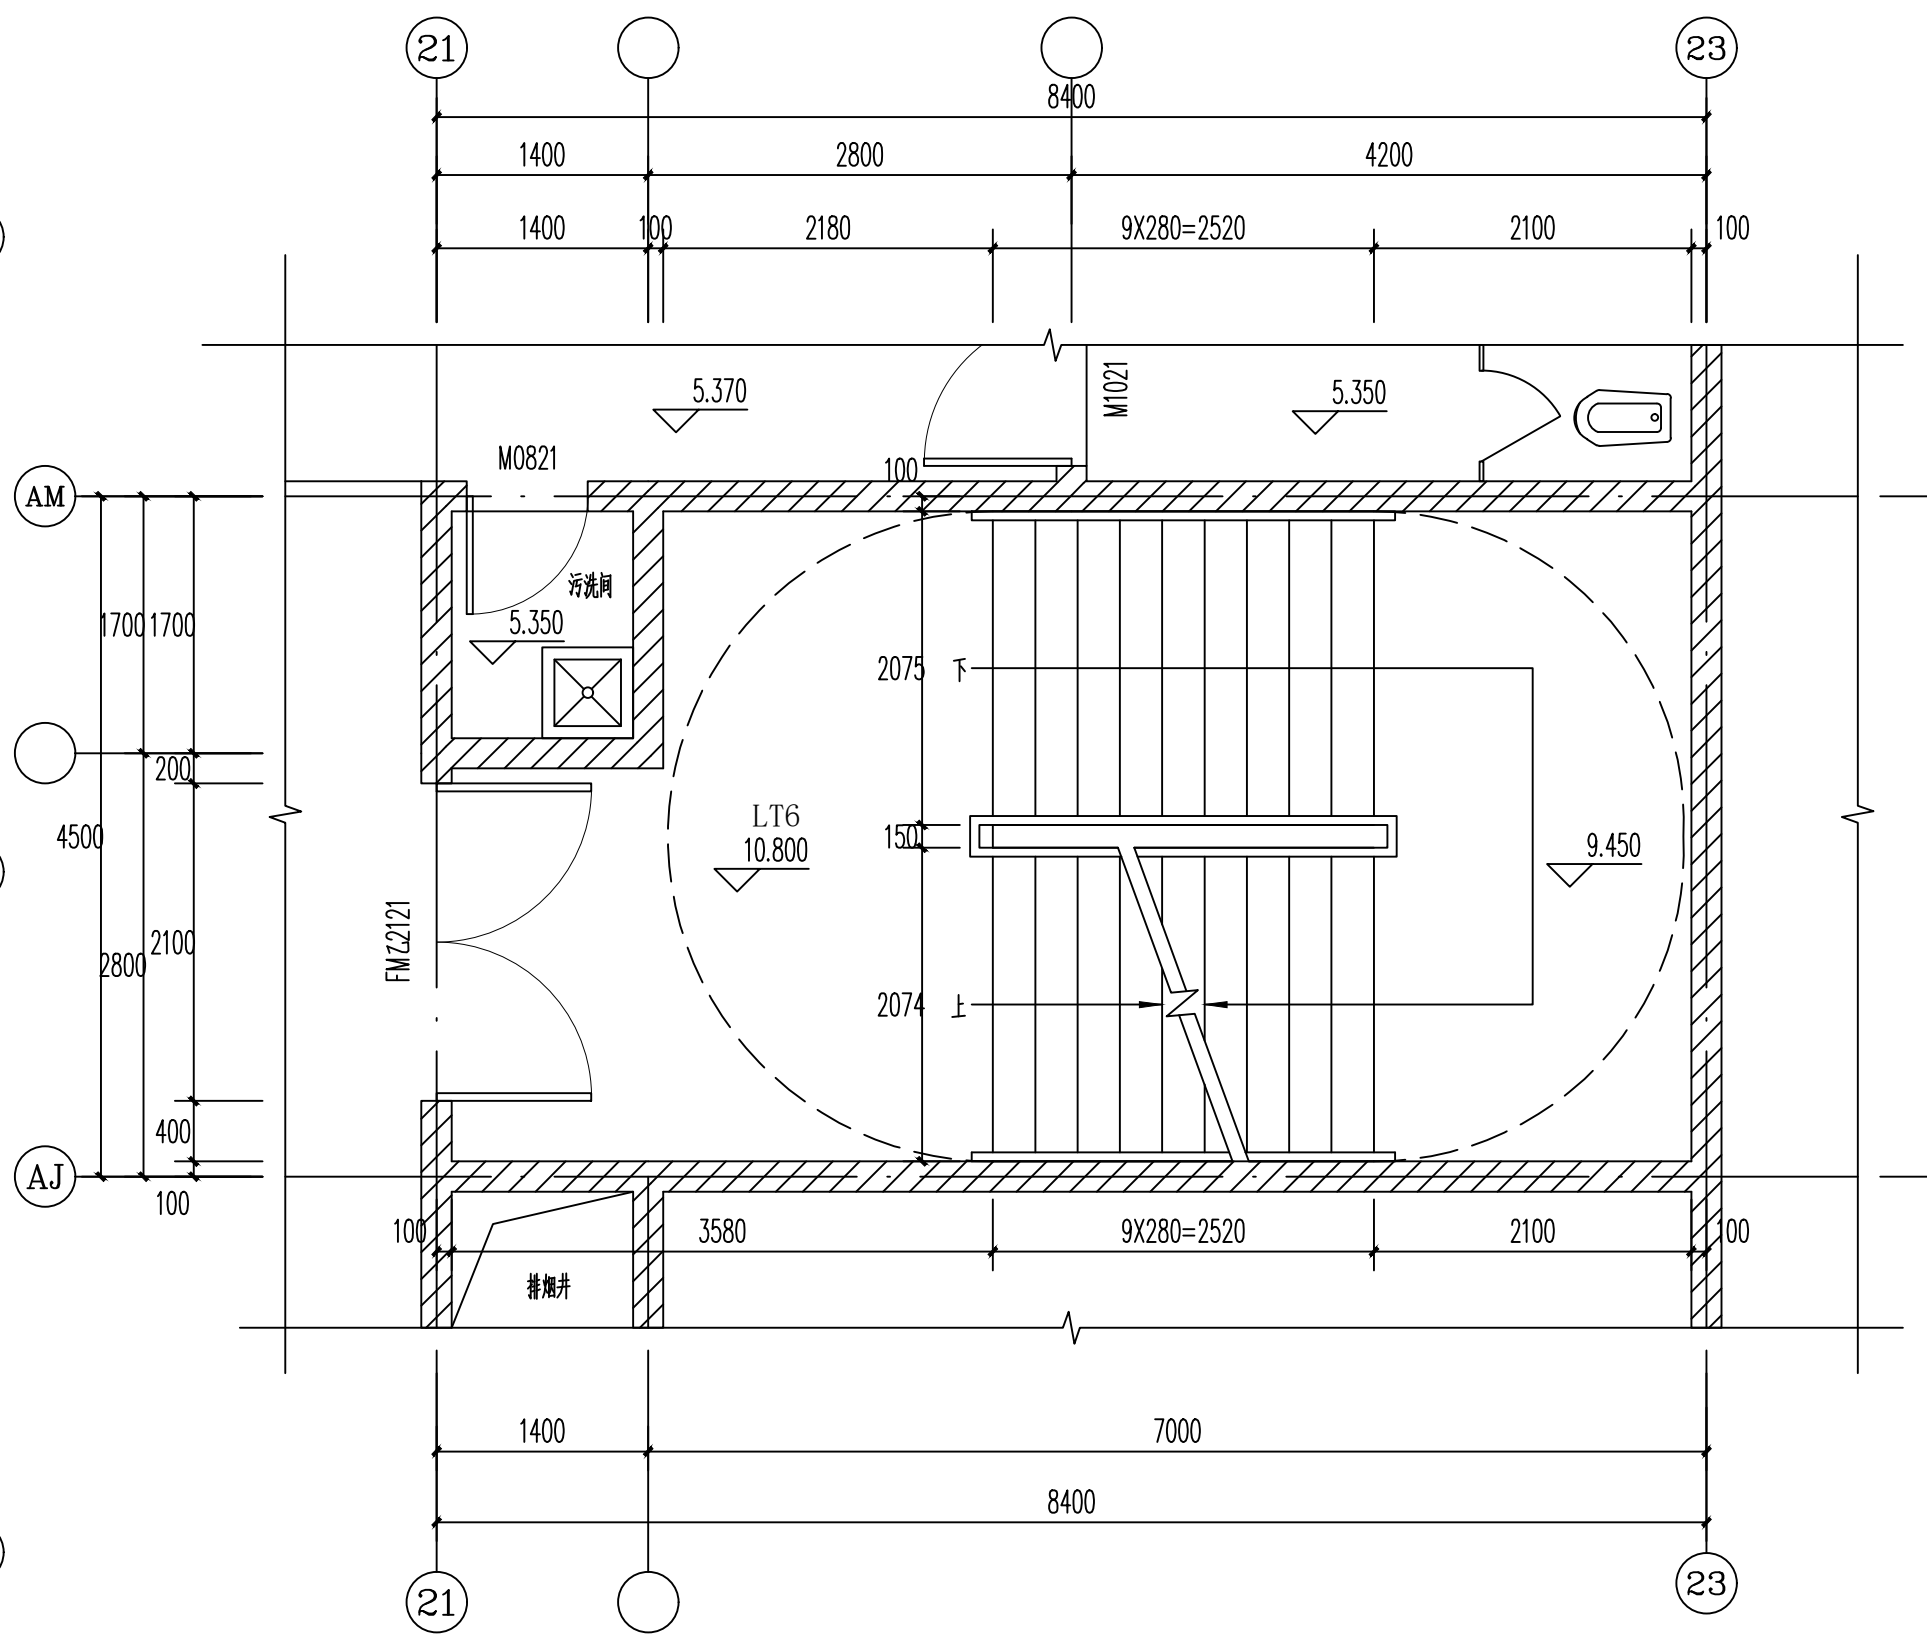

LT7楼梯间二层平面图 1:50

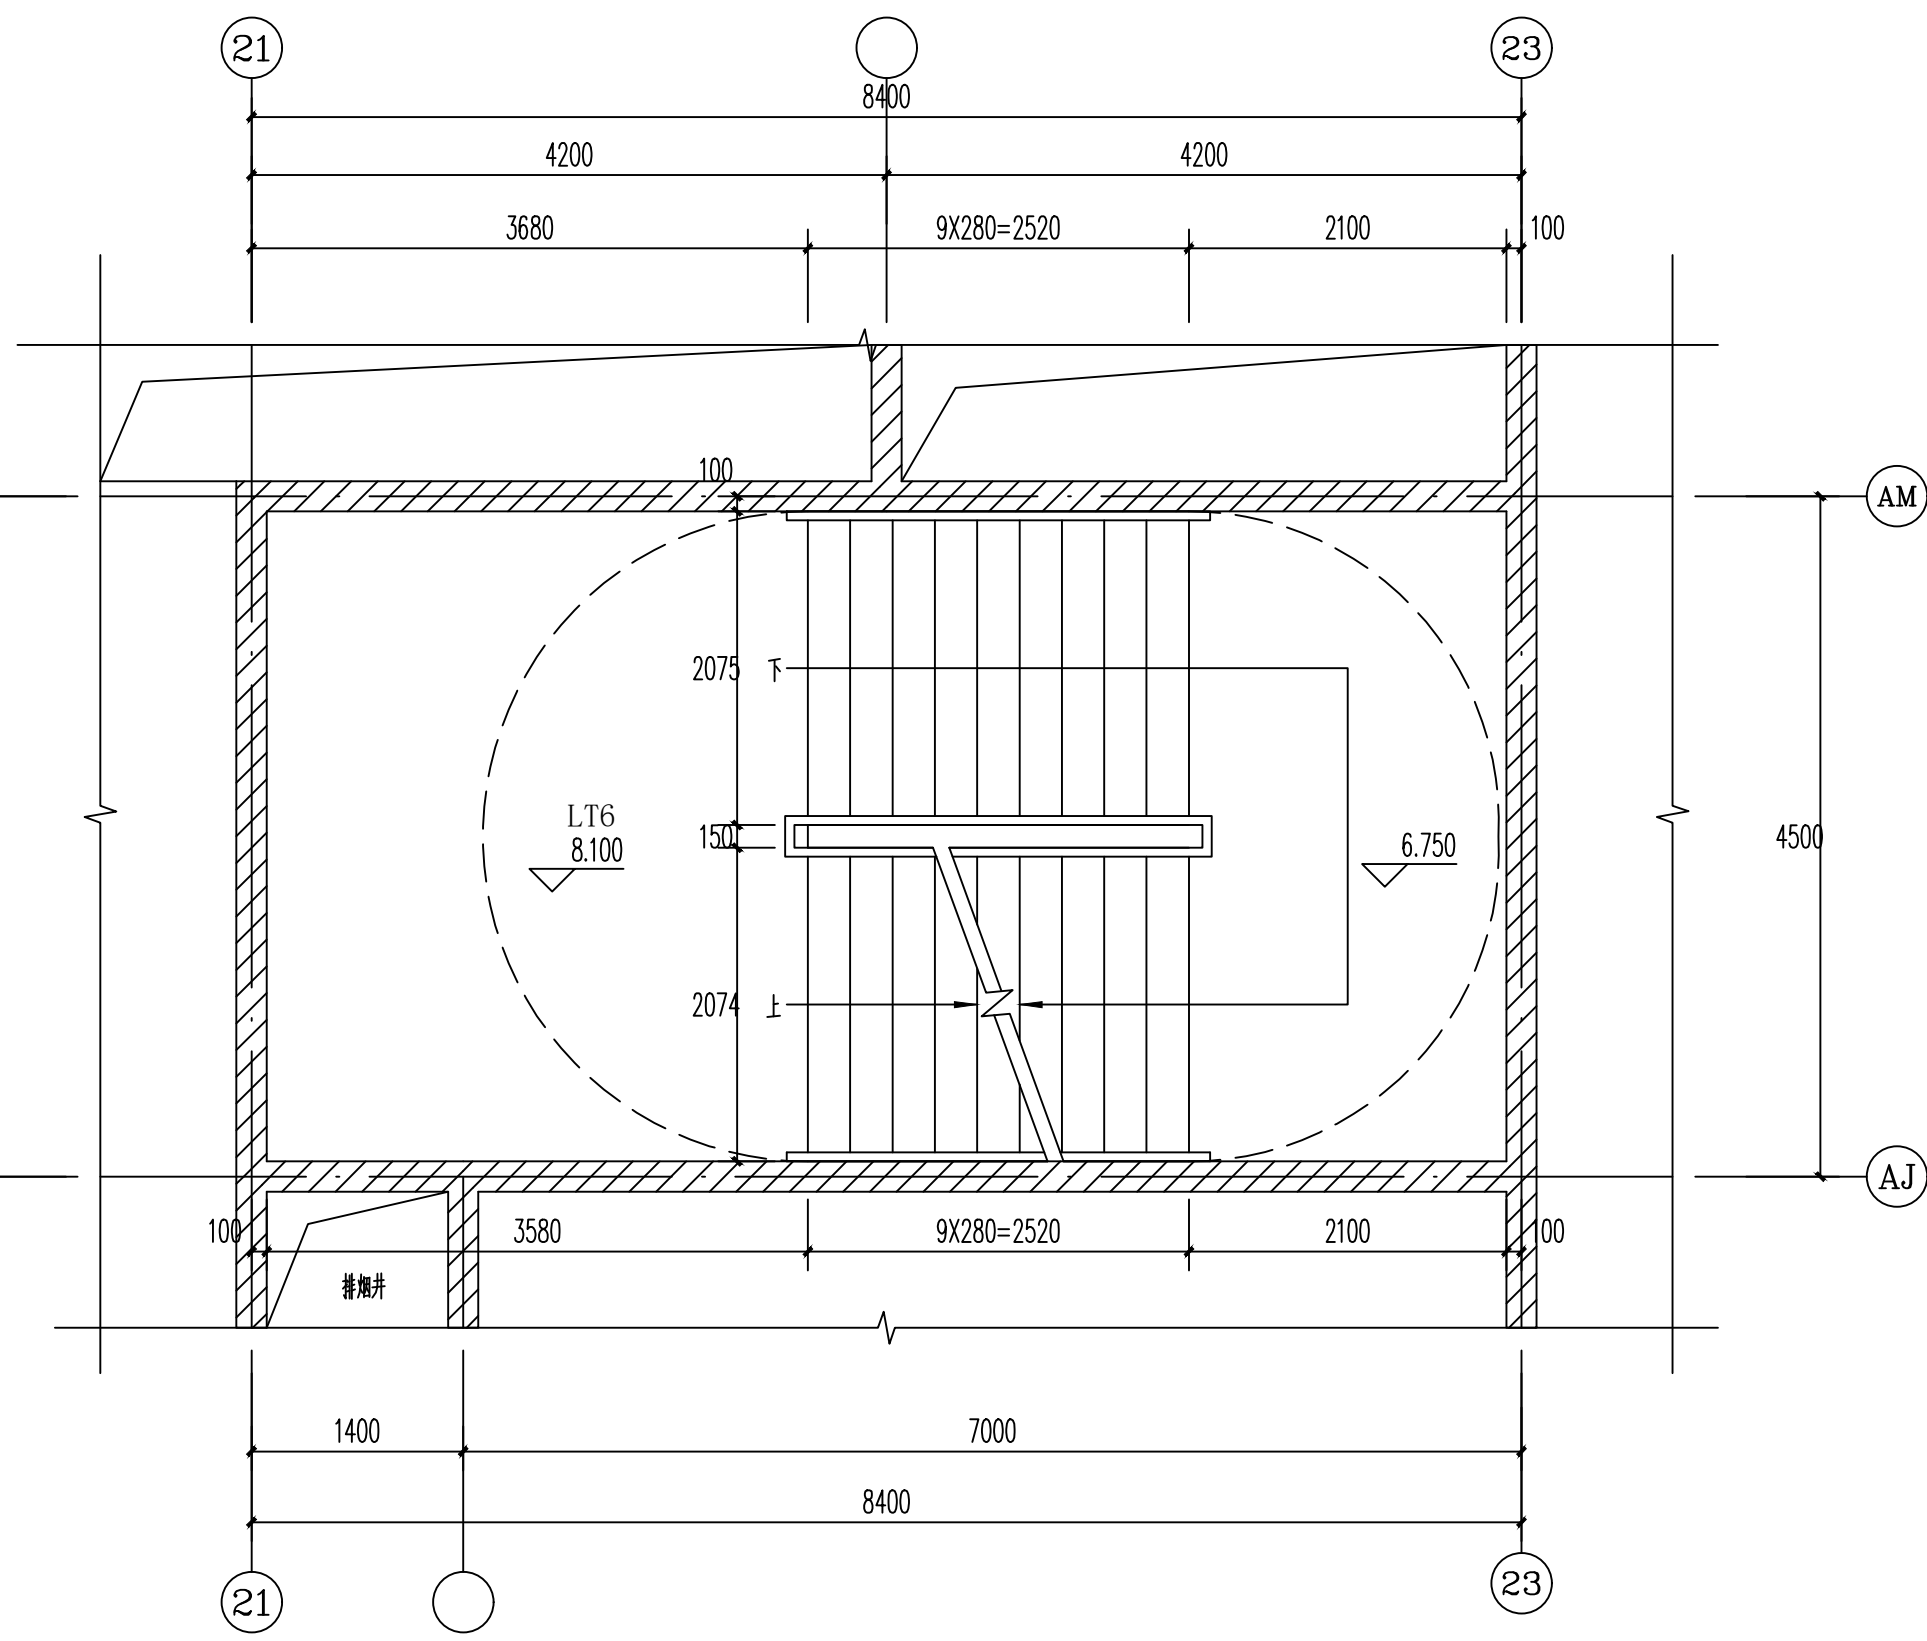


LT7楼梯间H=8.100处平面图 1:50

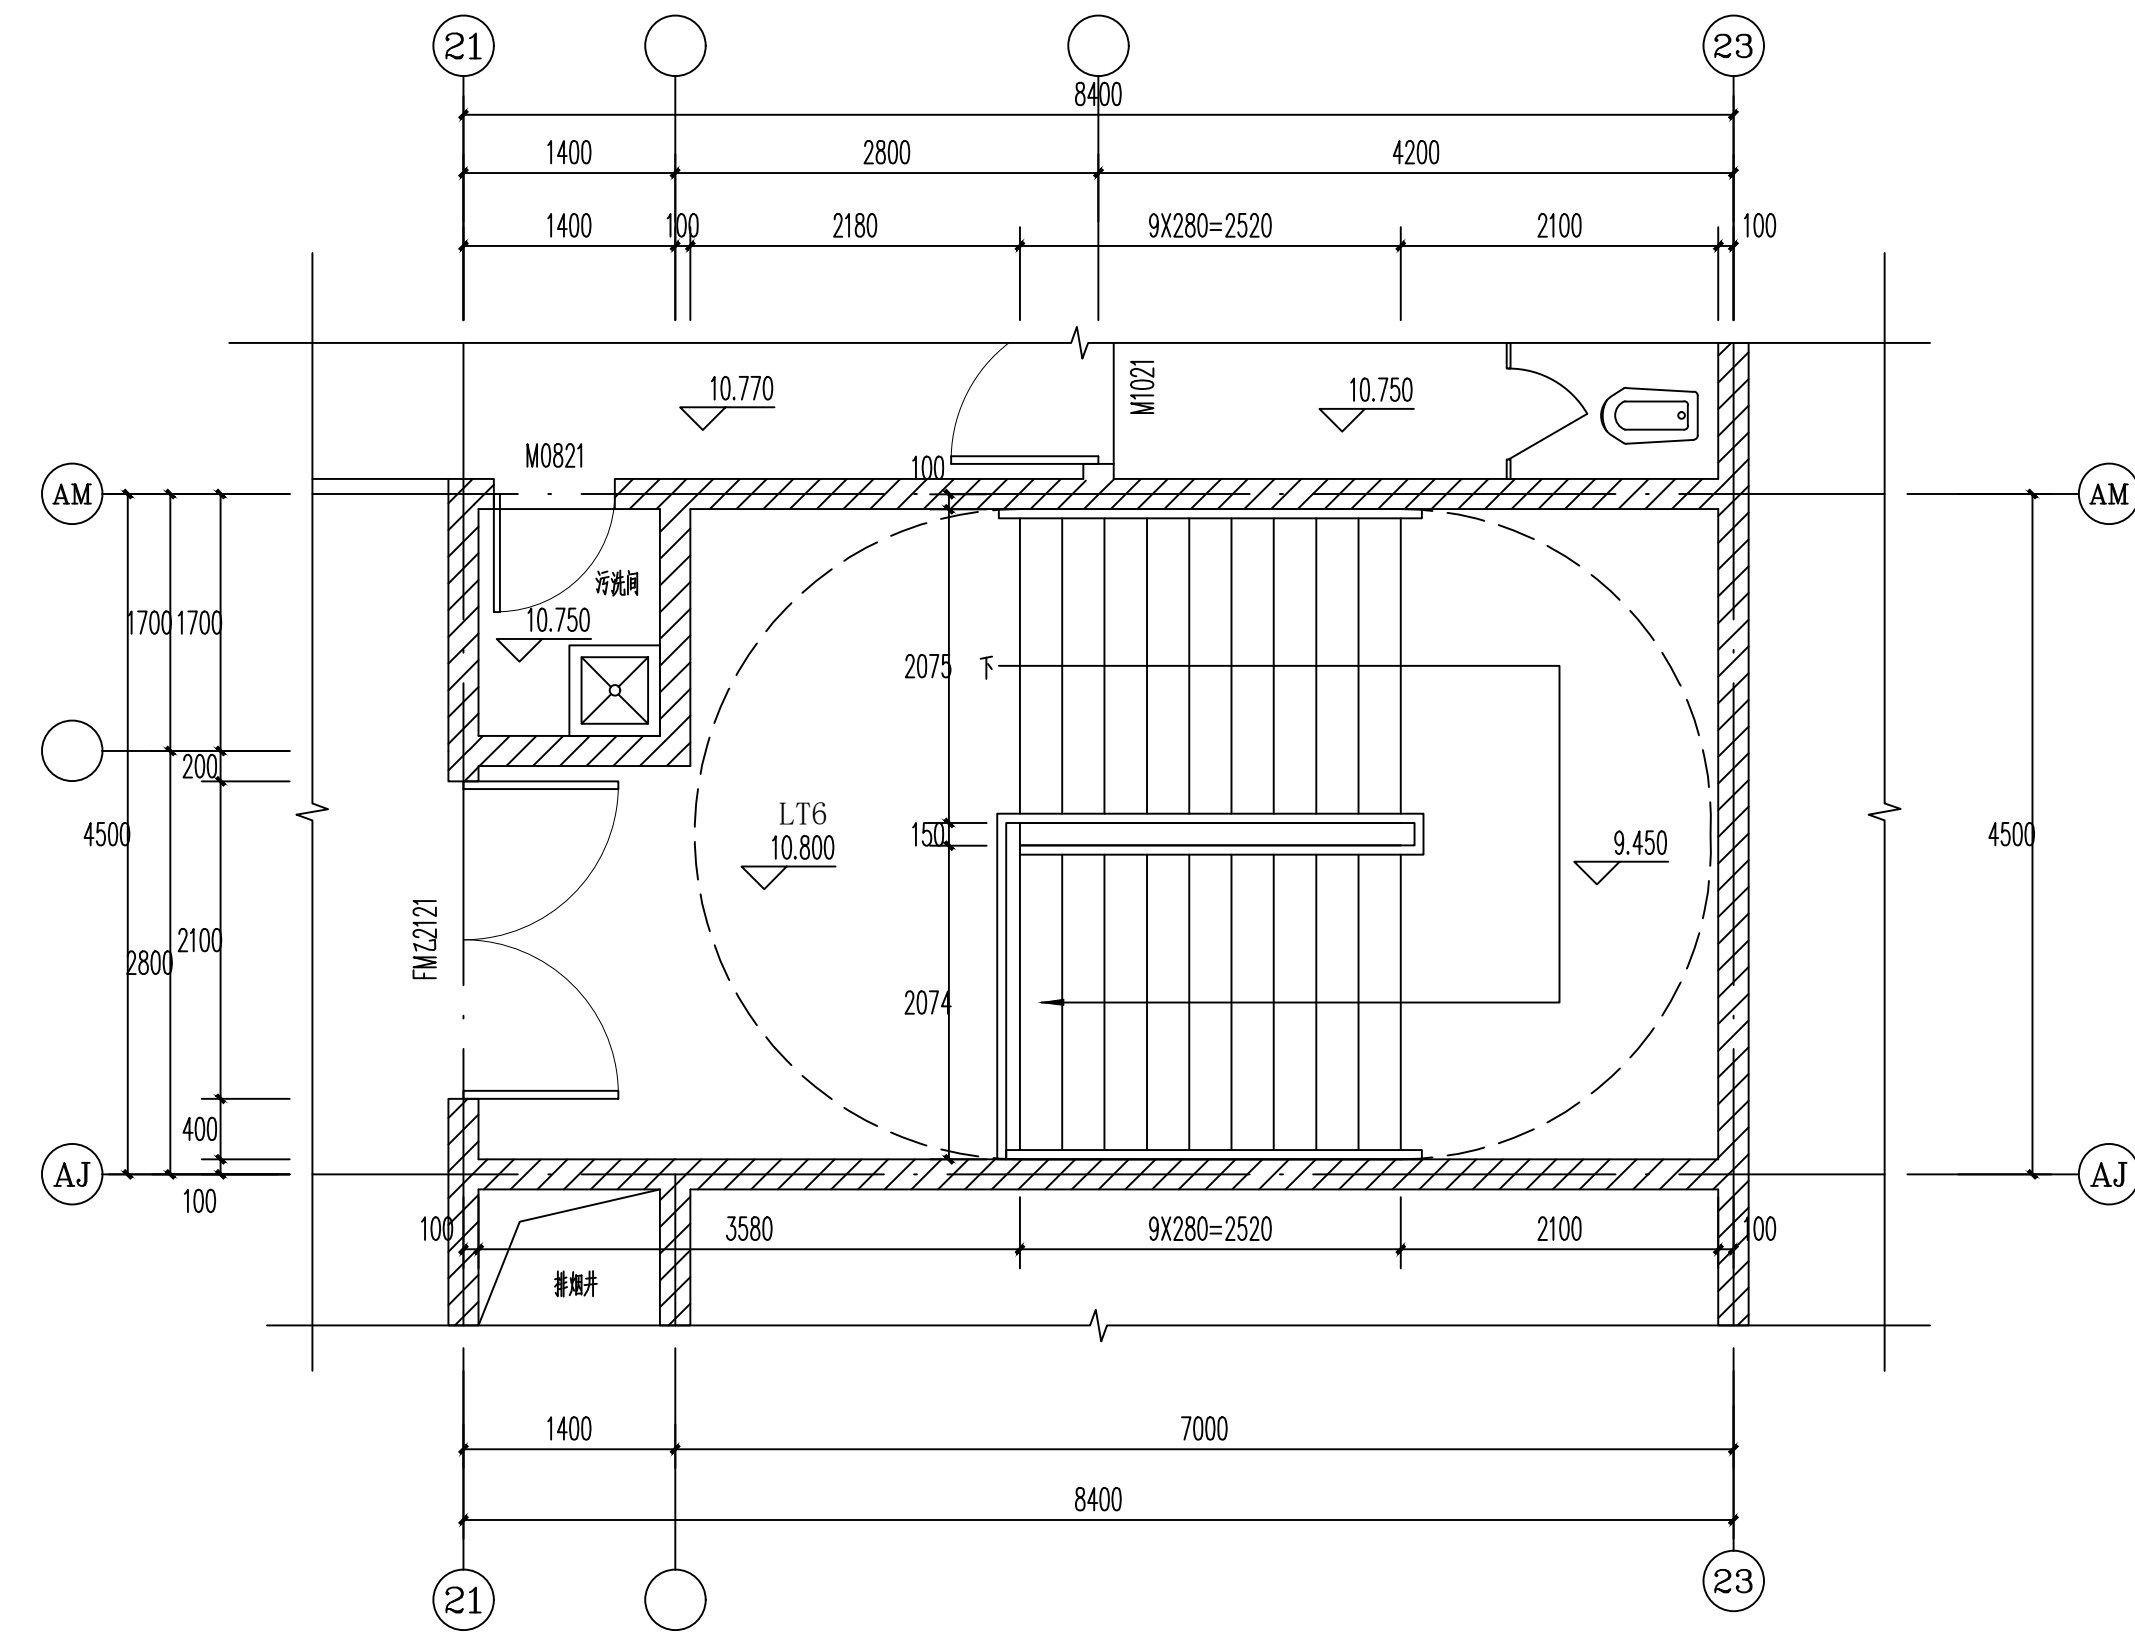


LT7楼梯间三层平面图 1:50

LT7楼梯间屋顶风井平面图详JS-28

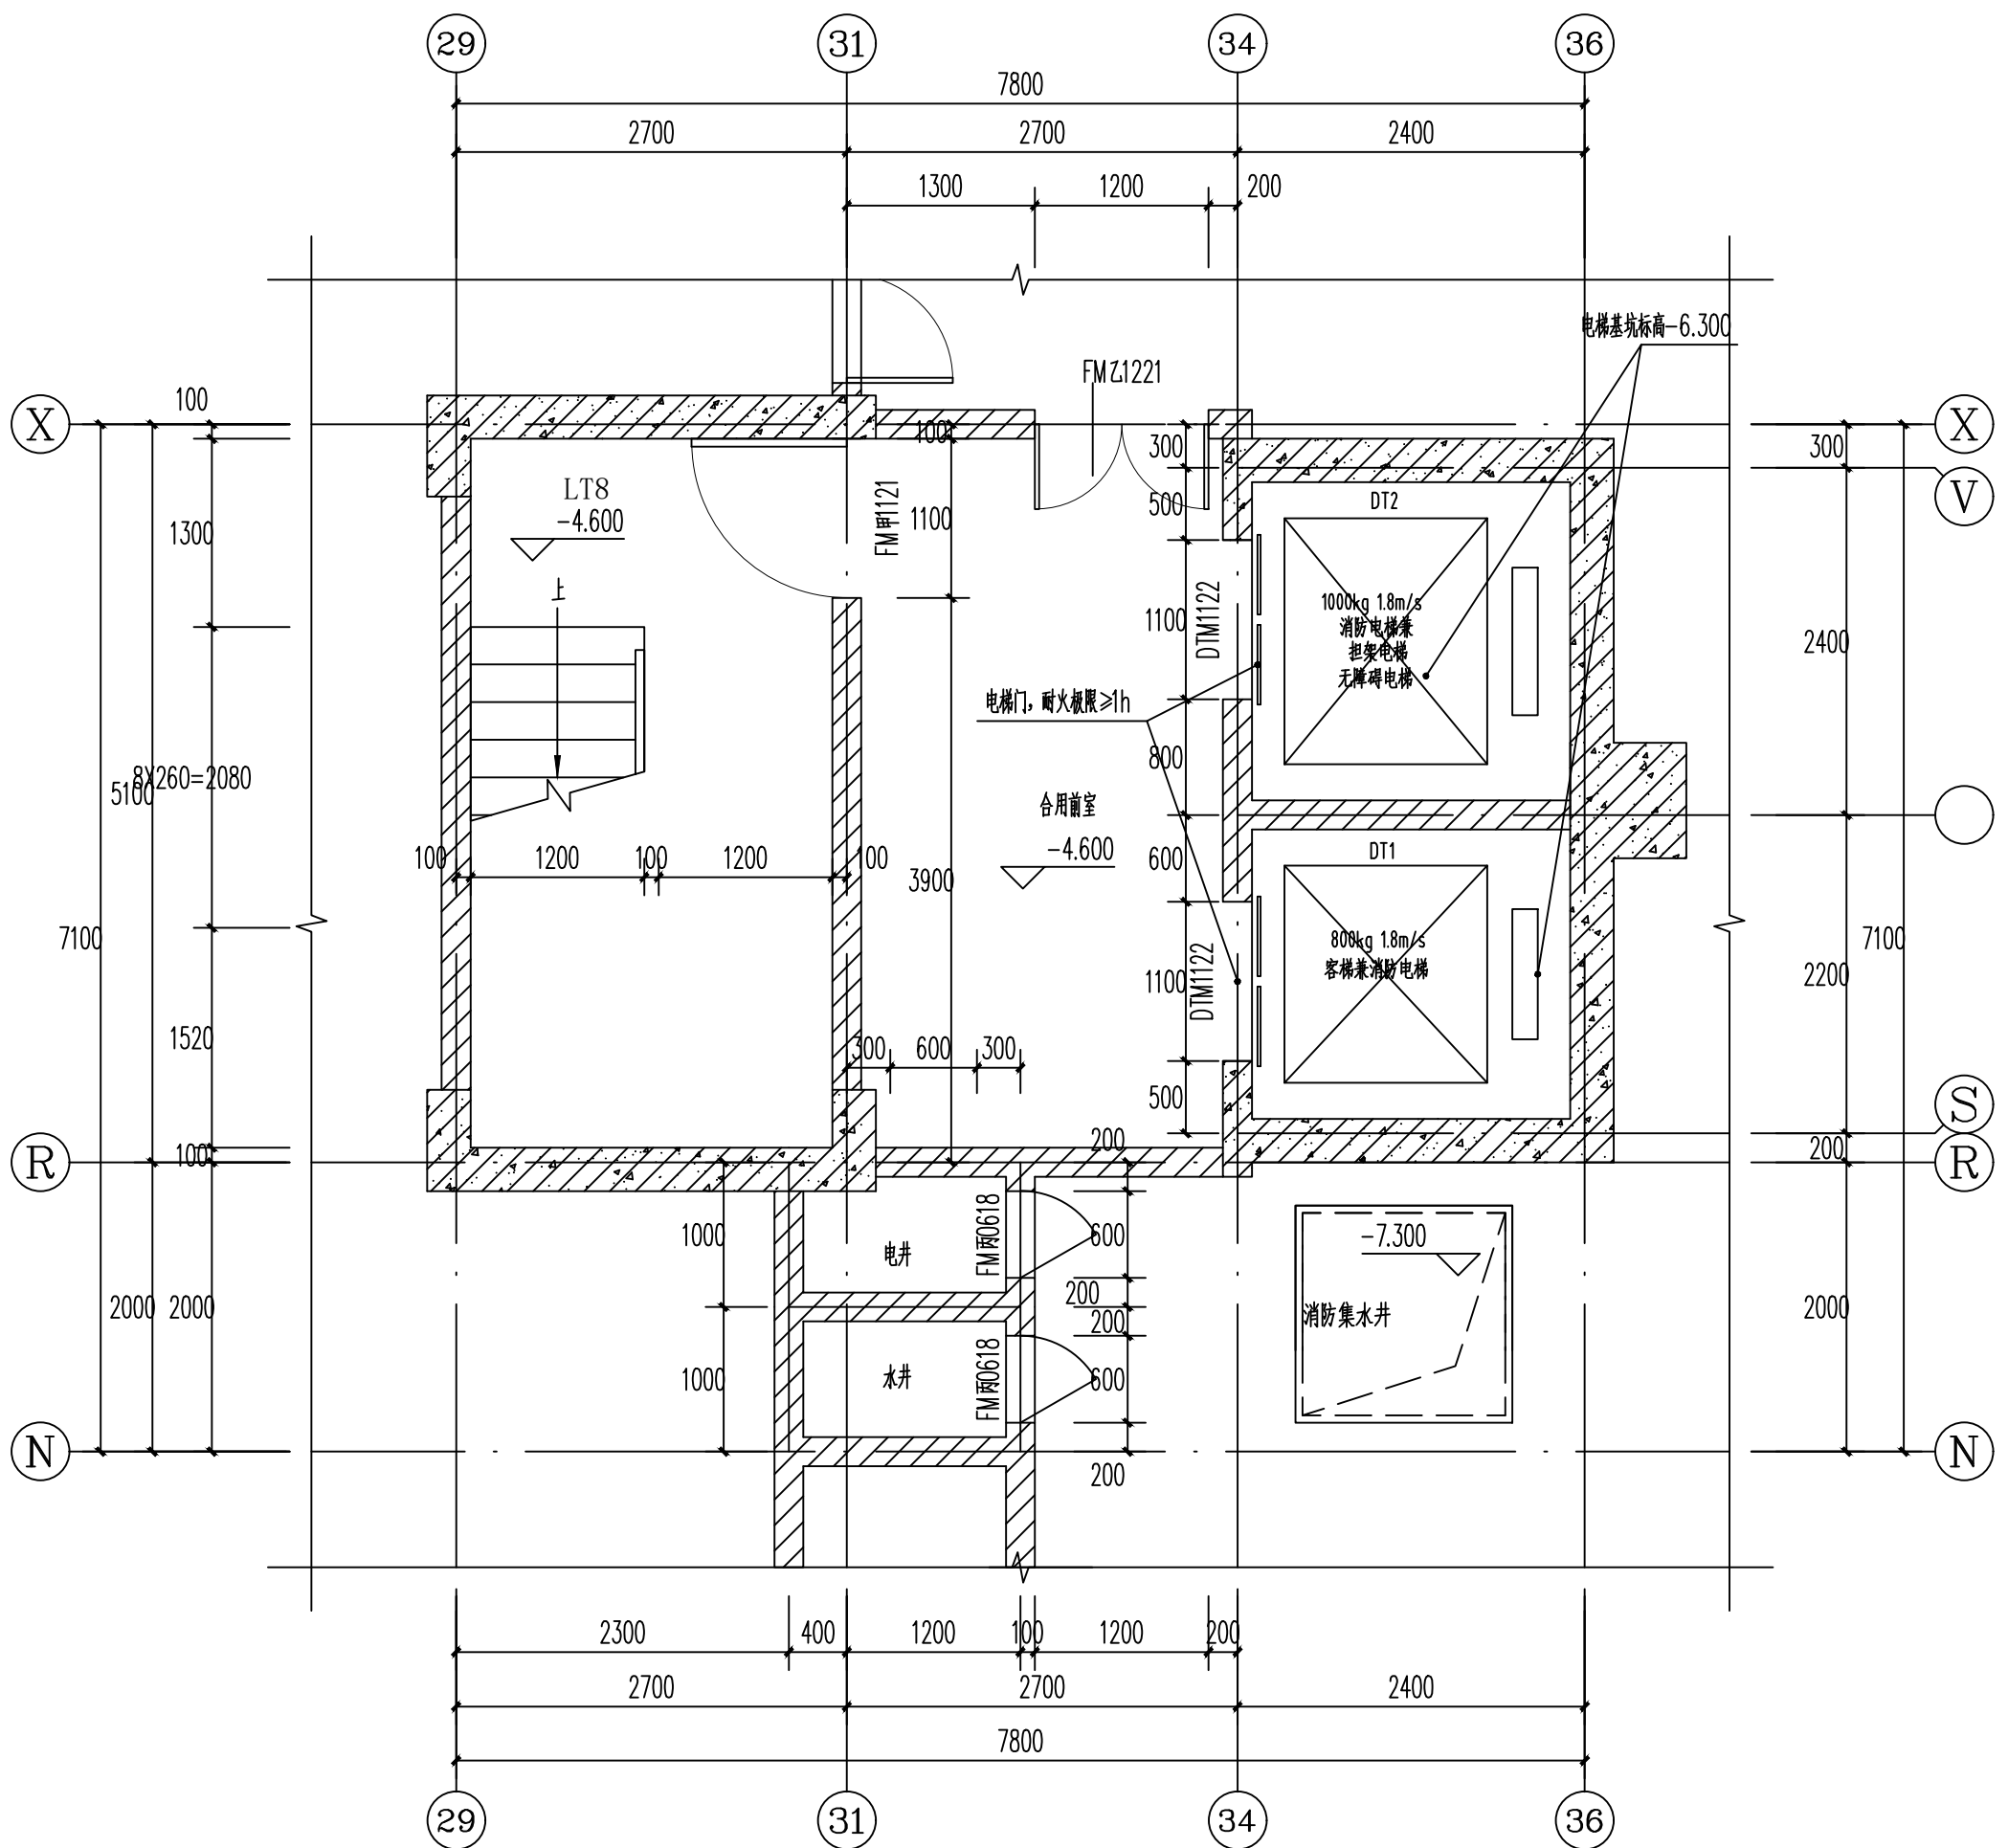

LT8楼梯间负一层平面图 1:50

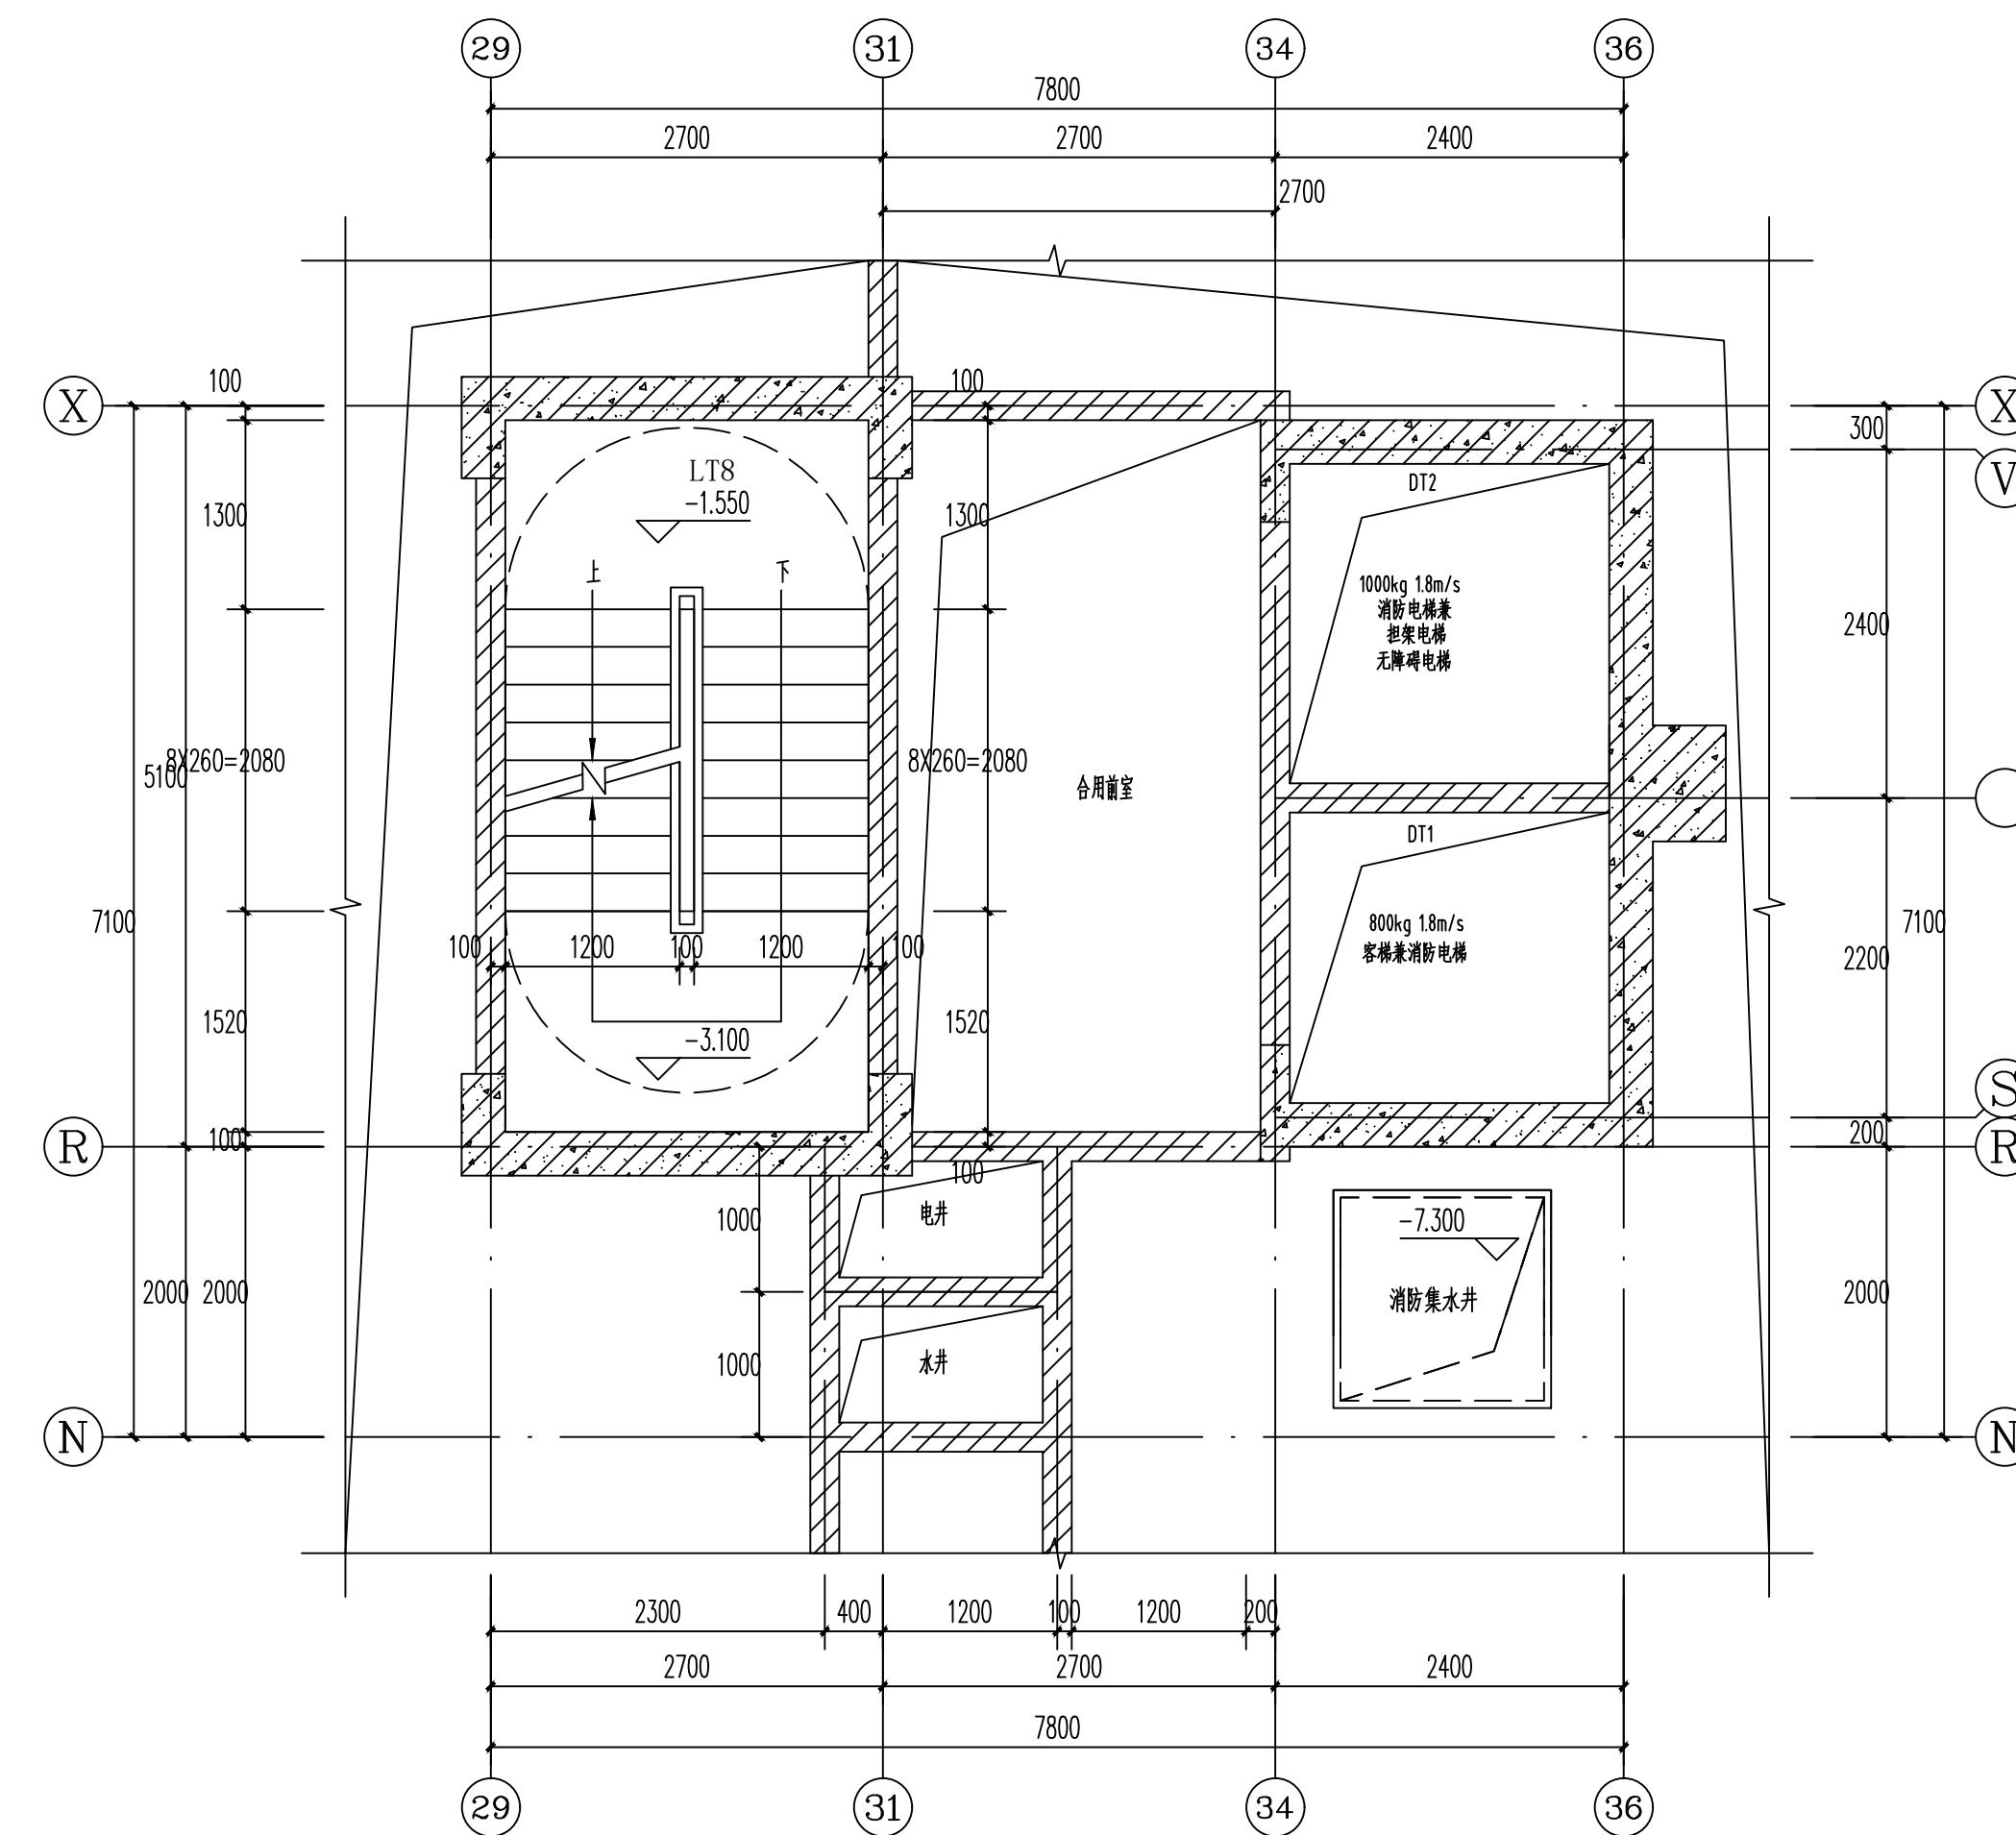

LT8楼梯间H=-1.550处平面图 1:50

建设单位/CLIENT:
麻阳苗族自治县远桥房地产开发有限公司
项目名称/PROJECT:
远程国际
子项目名称/SUB-PROJECT:
远程国际
区位图/REGIONAL LOCATION MAP :

图纸名称/TITLE:
LT7楼梯间大样图
LT8楼梯间大样图一

项目名称/PROJECT:
远程国际
设计 DESIGNED
校对 CHECKED
专业负责人 CHIEF
项目负责人 PROJECT CHIEF
审核 IDENTIFIED
审定 APPROVED
业务号/JOB NO.
设计阶段/STATUS: 施工图
专业/DISCIPLINE: 建筑
比例/ SCALE: 1: 100
规格/ SIZE: A1
出图日期/DATE: 2021.06
图号/DRAWING NO. JS-34
版次 NO.
修改内容 DESCRIPTION
日期 DATE
条形码/BARCODE:
版权所有，不得复制、套用。 ALL RIGHTS RESERVED, DON'T COPIED, REPRODUCED.