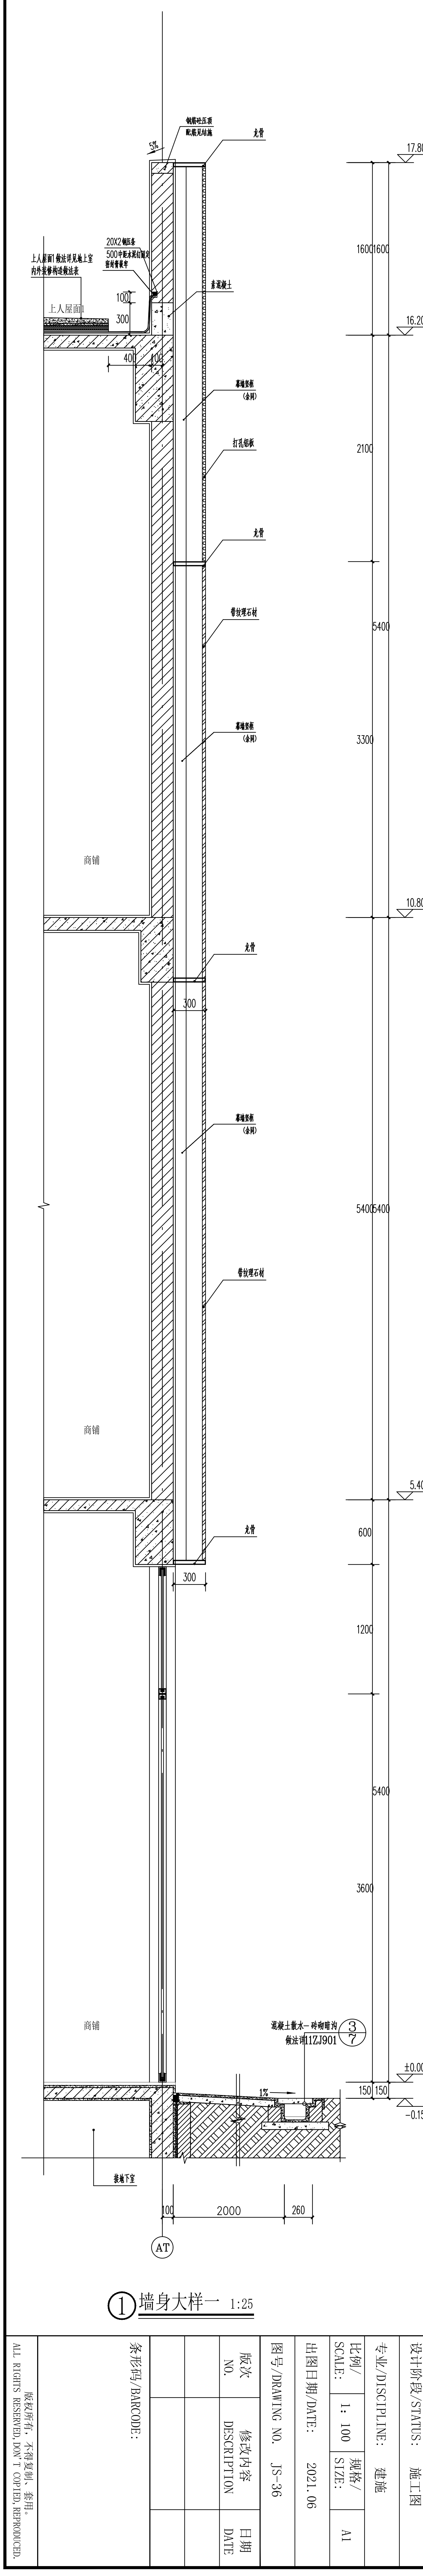

①墙身大样一 1:25

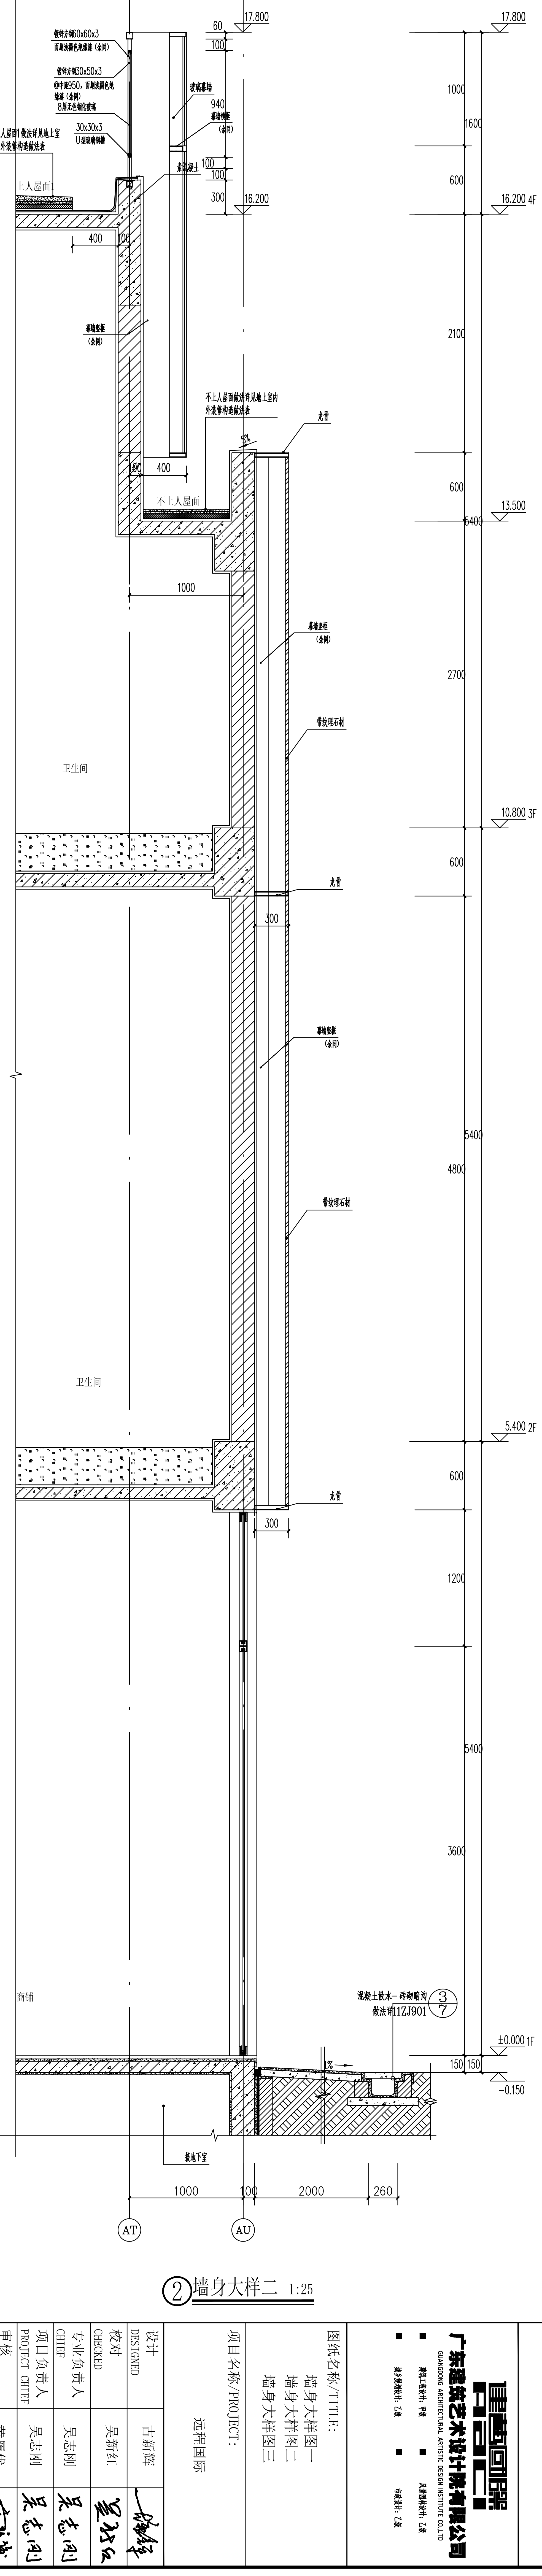

②墙身大样二 1:25

③墙身大样三 1:25

建设单位/CLIENT:
麻阳苗族自治县远桥房地产开发有限公司

项目名称/PROJECT:
远程国际

子项目名称/SUB-PROJECT:
远程国际

区位图/REGIONAL LOCATION MAP:

广东建筑艺术设计院有限公司
GUANGDONG ARCHITECTURAL ARTISTIC DESIGN INSTITUTE CO.,LTD
■ 建筑工程设计：甲级　■ 风景园林设计：乙级
■ 城乡规划设计：乙级　■ 市政设计：乙级

图纸名称/TITLE:
墙身大样图一
墙身大样图二
墙身大样图三

项目名称/PROJECT:
远程国际

设计 DESIGNED	古新辉	
校对 CHECKED	吴新红	
专业负责人 CHIEF	吴志刚	吴志刚
项目负责人 PROJECT CHIEF	吴志刚	吴志刚
审核 IDENTIFIED	黄履优	
审定 APPROVED	李坚	

业务号/JOB NO.

设计阶段/STATUS: 施工图

专业/DISCIPLINE: 建施

比例/SCALE: 1:100　规格/SIZE: A1

出图日期/DATE: 2021.06

图号/DRAWING NO. JS-36

版次 NO.	修改内容 DESCRIPTION	日期 DATE

条形码/BARCODE:

版权所有，不得复制、套用。
ALL RIGHTS RESERVED,DON'T COPIED,REPRODUCED.