


① 墙身大样九 1:25

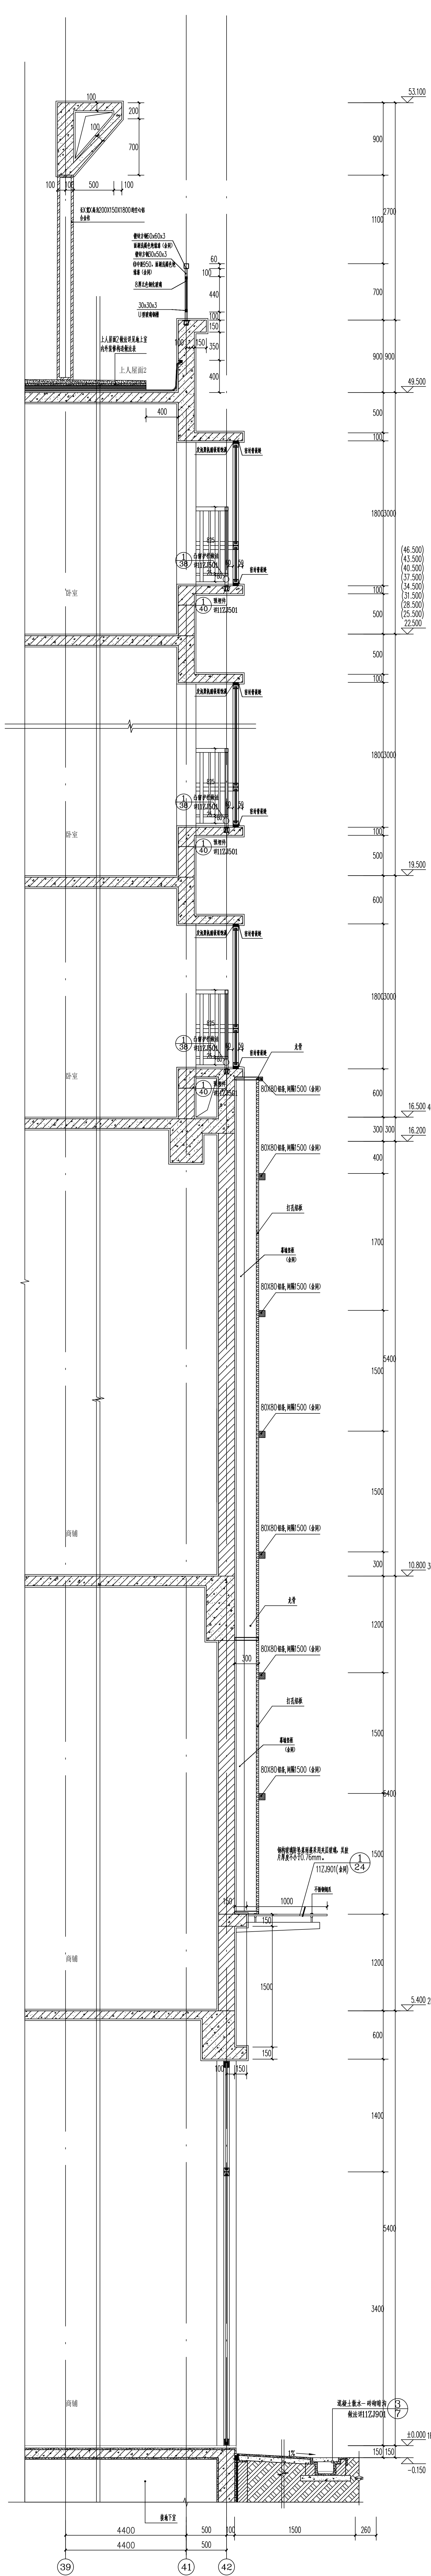

② 墙身大样十 1:25

建设单位/CUSTOMER:					
肇庆市住房和城乡建设局					
项目名称/PROJECT:					
远翔国际					
子项目名称/SUB-PROJECT:					
远翔国际					
区位图/REGIONAL LOCATION MAP:					
					
图纸名称/TITLE:					
塔身大样图九 塔身大样图十					
项目名称/PROJECT:					
远翔国际					
设计 DISCIPLINE: 校对 CHECKED: 审核 REVIEWED: 项目负人 PROJECT CHIEF: 审批 APPROVED:					
业务号 JOB NO.					
设计阶段 STATUS: 施工图					
专业/DISCIPLINE: 建筑					
比例/SCALE: 1:100 规格/SIZE: A1					
出图日期 DATE: 2021.06					
图号/DWG NO.: JS-39					
版次 NO. 修改内容 DESCRIPTION 日期 DATE					
备注/REMARKS:					
说明: 本图仅供参考, 不作为施工依据。					
文件路径: E:\Projects\远翔国际\施工图\塔身大样图九.dwg					