

建设单位/CLIENT:
麻阳苗族自治县远桥房地产开发有限公司

项目名称/PROJECT:
远程国际

子项目名称/SUB-PROJECT:
远程国际

区位图/REGIONAL LOCATION MAP :

广东建筑艺术设计院有限公司
GUANGDONG ARCHITECTURAL ARTISTIC DESIGN INSTITUTE CO.,LTD

■ 建筑方案设计: 甲级 ■ 风景园林设计: 乙级
■ 城乡规划设计: 乙级 ■ 市政设计: 乙级

图纸名称/TITLE:
消防水池A-A剖面图
地下室防水做法大样图一、二
节点大样图一

项目名称/PROJECT:
远程国际

设计 DESIGNED	古新辉	
校对 CHECKED	吴新红	
专业负责人 CHIEF	吴志刚	
项目负责人 PROJECT CHIEF	吴志刚	
审核 IDENTIFIED	黄履优	
审定 APPROVED	李 坚	

业务号/JOB NO.

设计阶段/STATUS: 施工图

专业/DISCIPLINE: 建筑

比例/
SCALE: 1: 100 规格/
SIZE: A1






出图日期/DATE: 2021. 06

图号/DRAWING NO. JS-40

版次 NO.	修改内容 DESCRIPTION	日期 DATE


条形码/BARCODE:

版权所有, 不得复制、套用。
ALL RIGHTS RESERVED, DON'T COPIED, REPRODUCED.

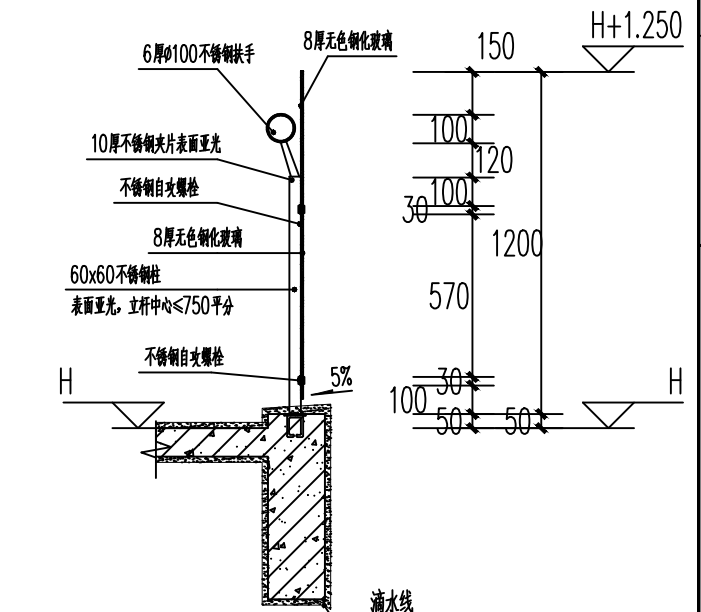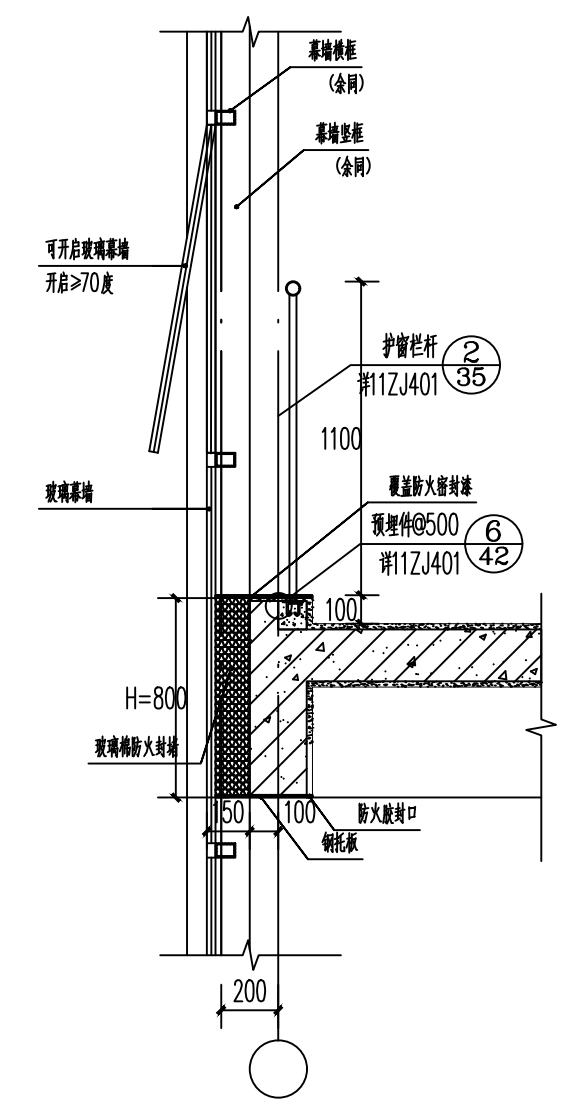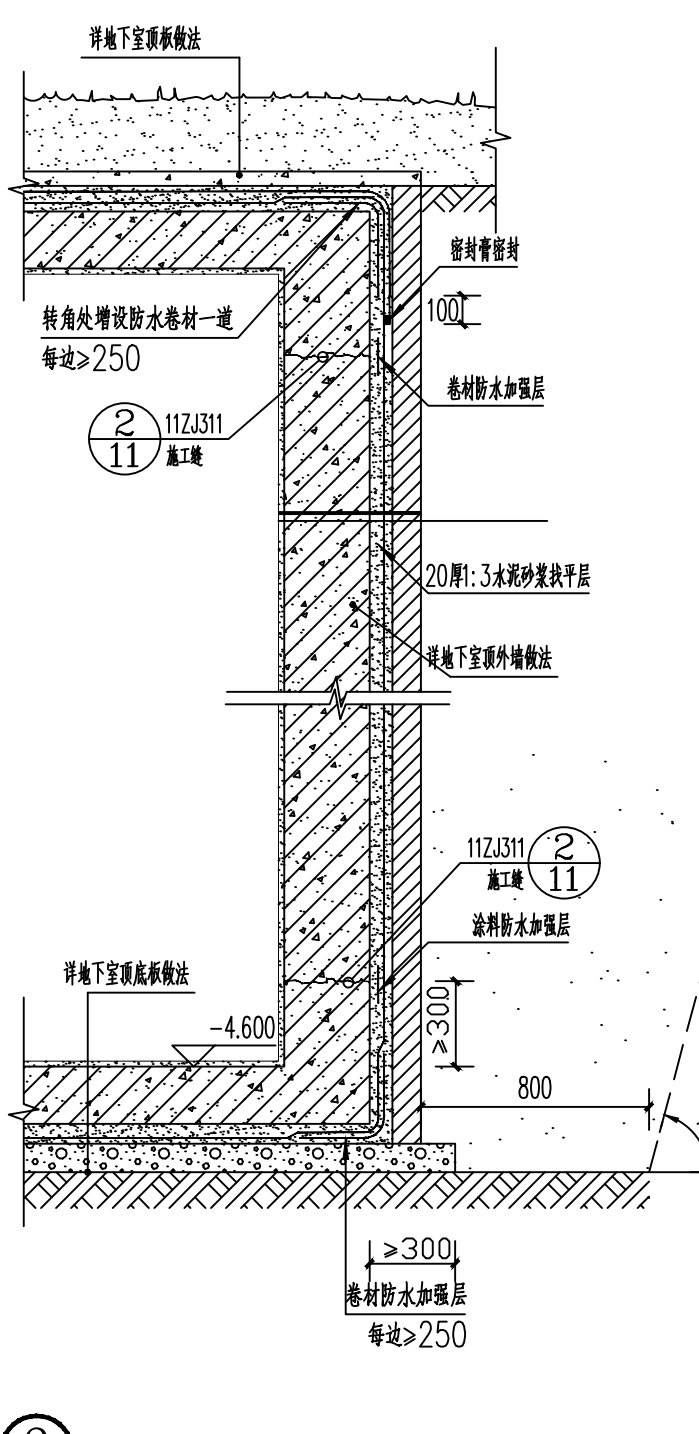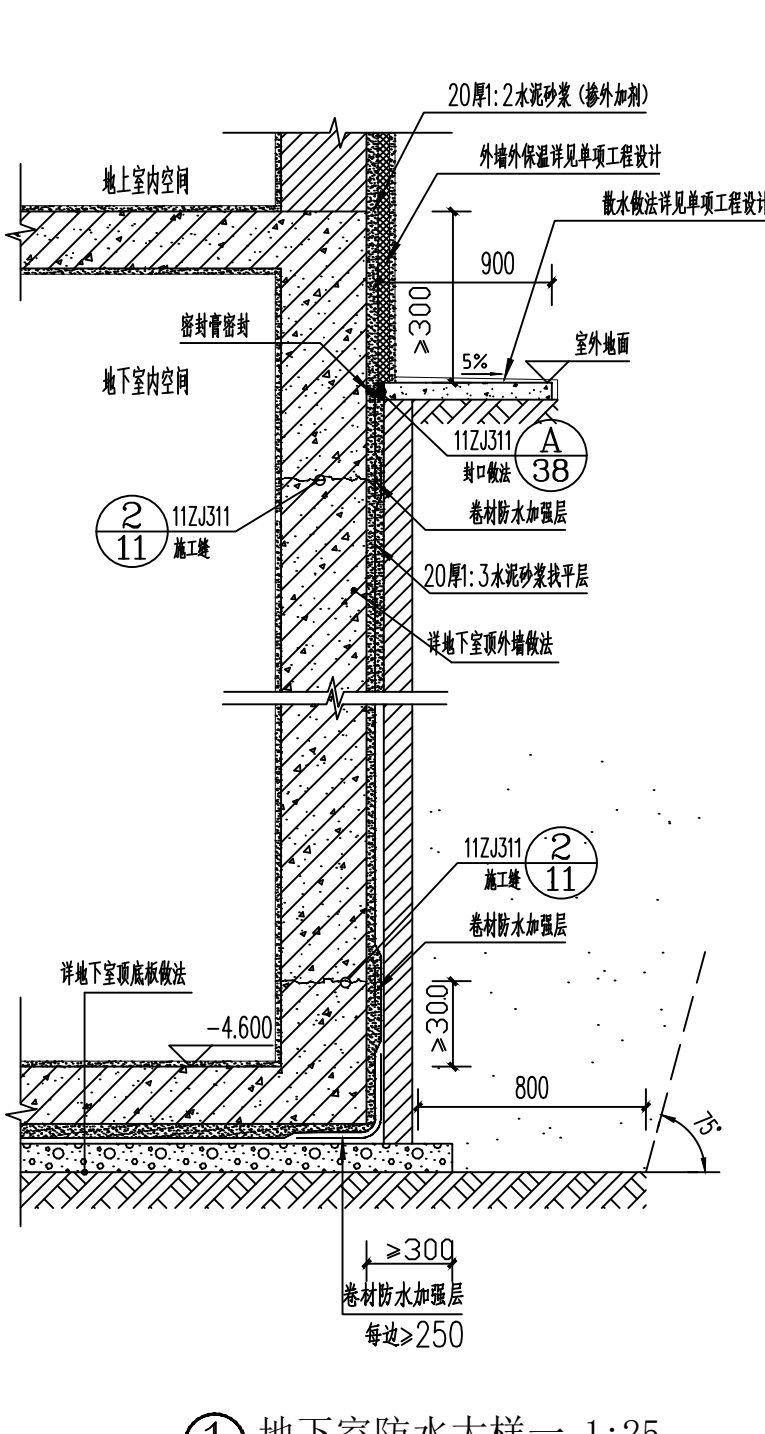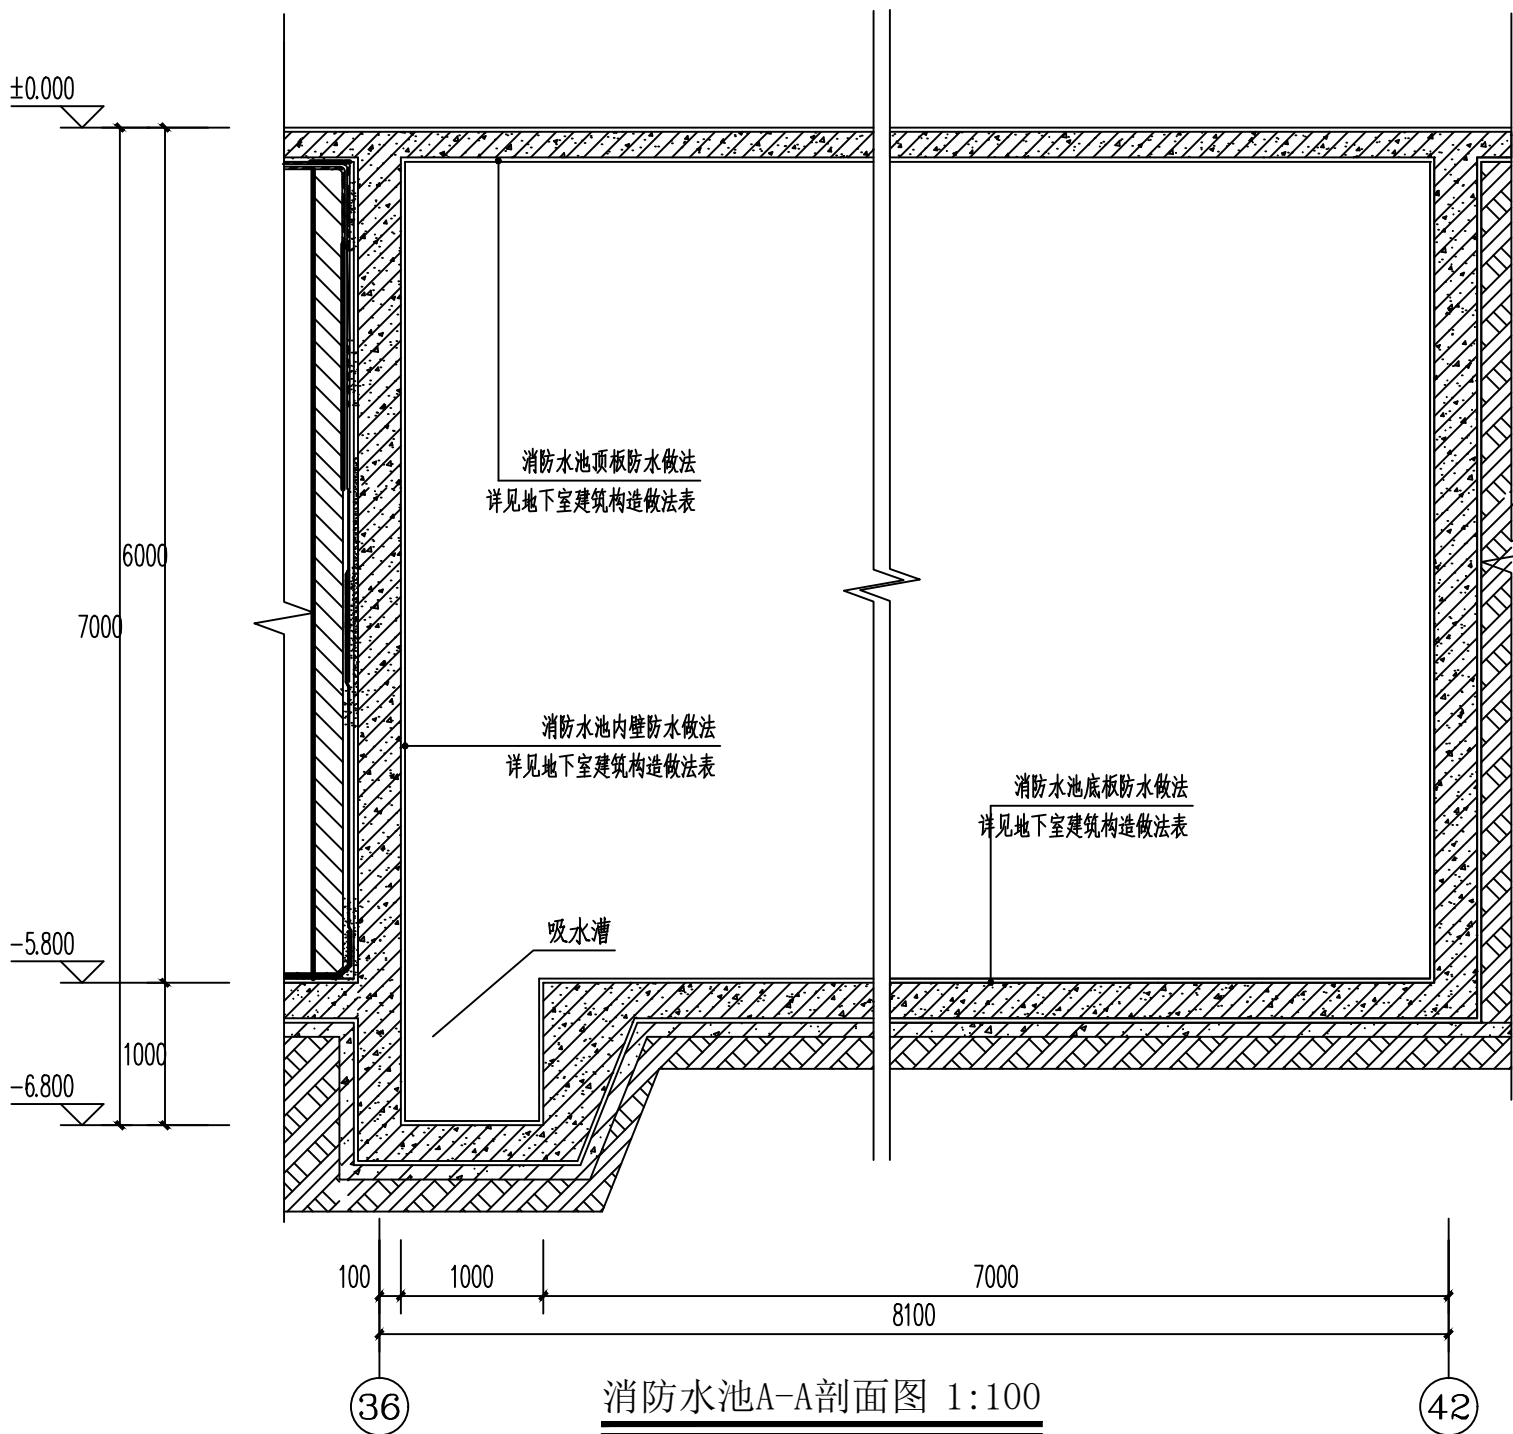


③ 幕墙防火封堵节点大样 1:50


⑤ 内走廊玻璃栏杆大样 1:50

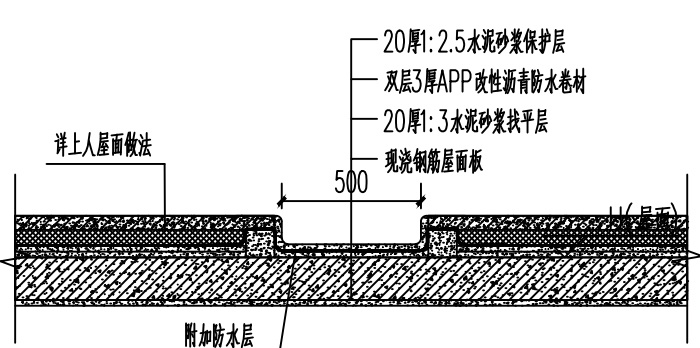


④ 屋面内天沟大样 1:50

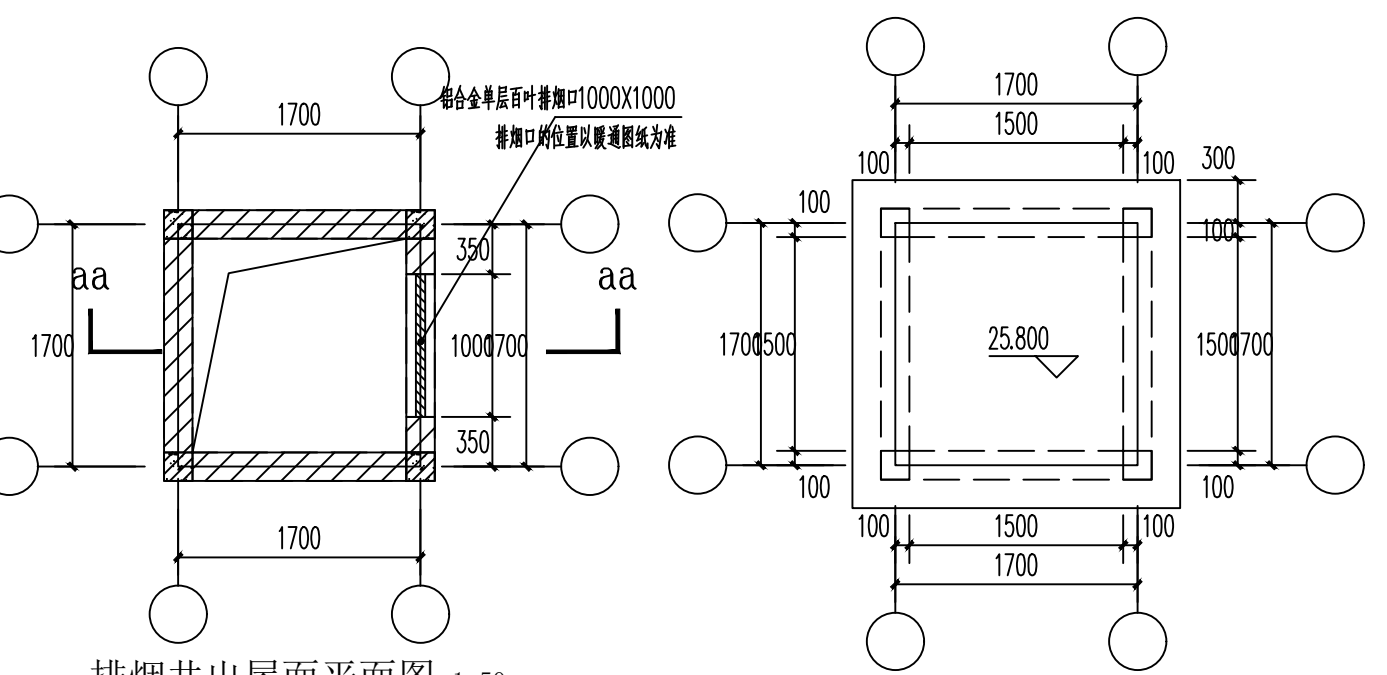


⑥ 排烟井出屋面部大样图 1:50

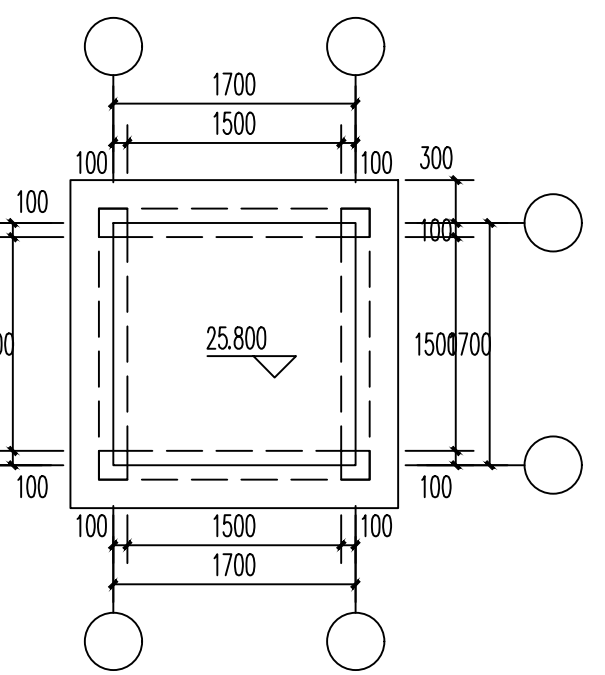


排烟井出屋面部大样图 1:50

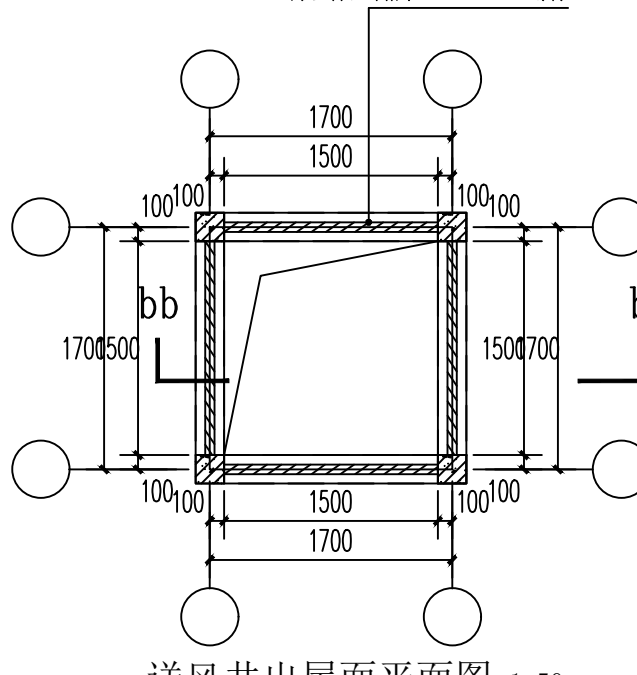


⑦ 送风井出屋面部大样图 1:50

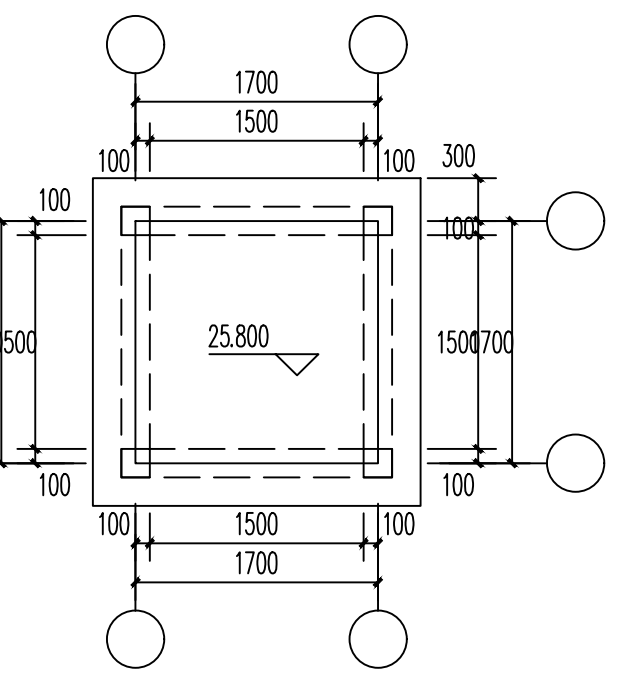


送风井出屋面部大样图 1:100

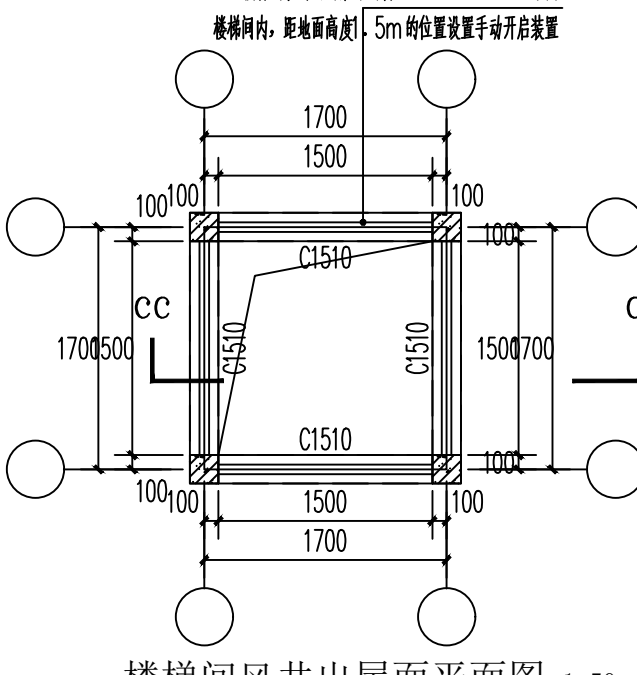

⑧ 楼梯间风井出屋面部大样图 1:50

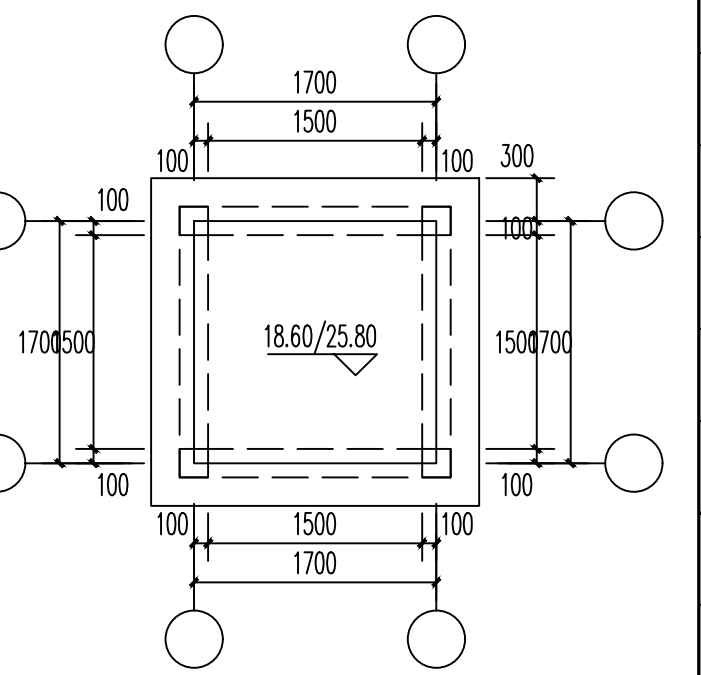


楼梯间风井出屋面部大样图 1:50

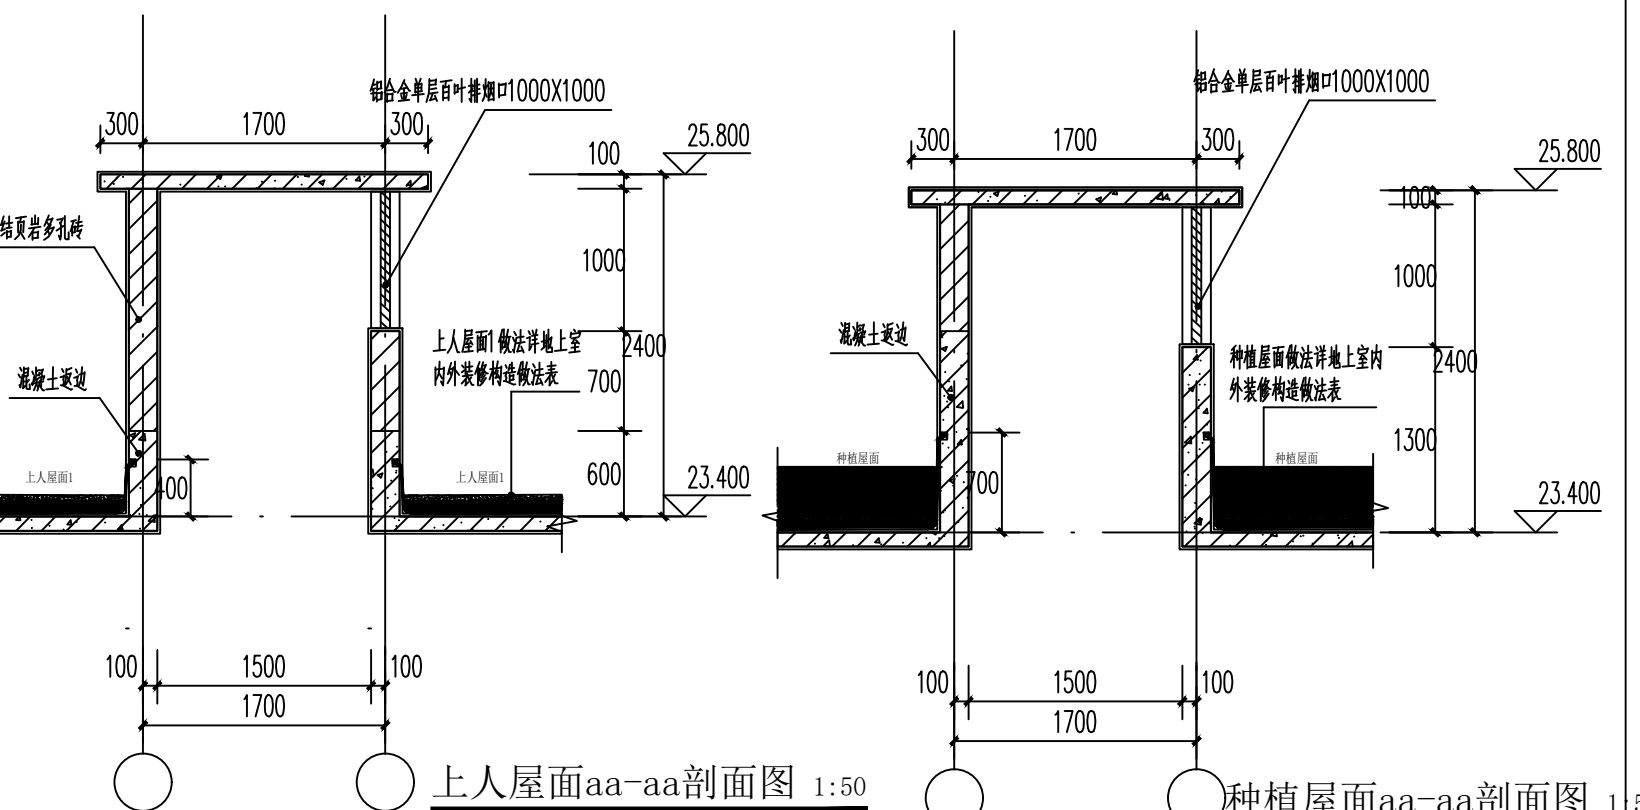


上人屋面aa-aa剖面图 1:50


种植屋面aa-aa剖面图 1:50

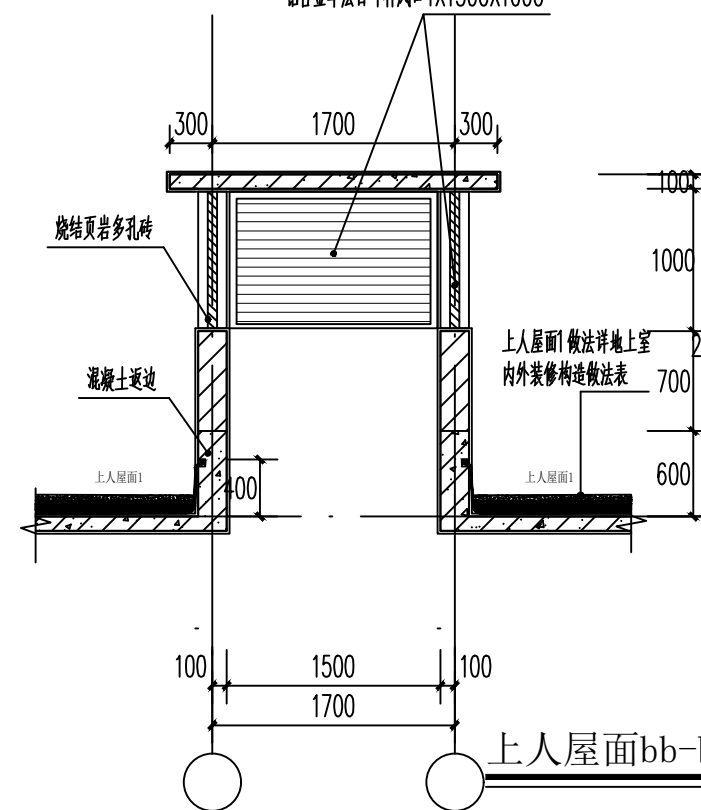

上人屋面bb-bb剖面图 1:50

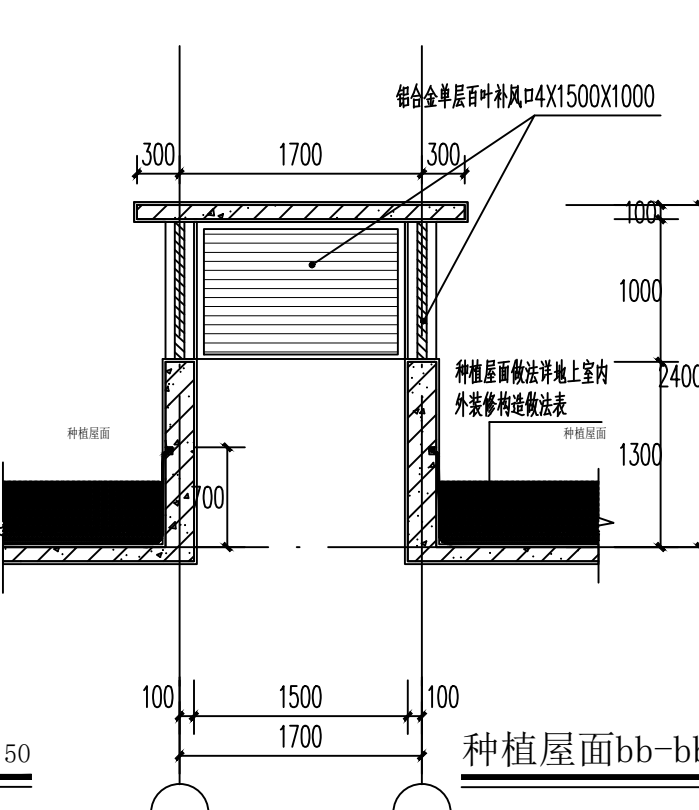

种植屋面bb-bb剖面图 1:50

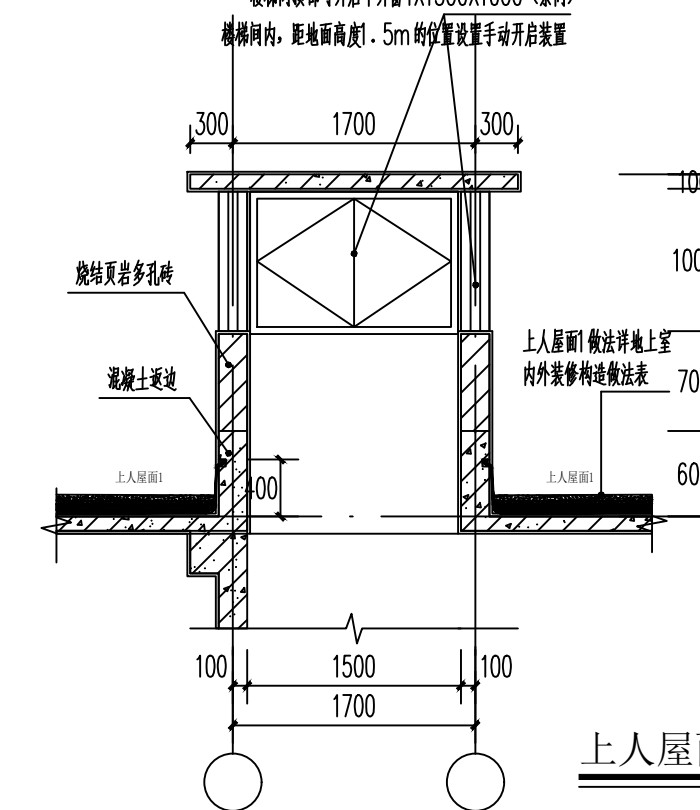

上人屋面cc-cc剖面图 1:50