

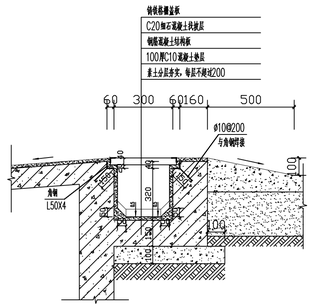



① 车道室外地面截水沟大样 1:25

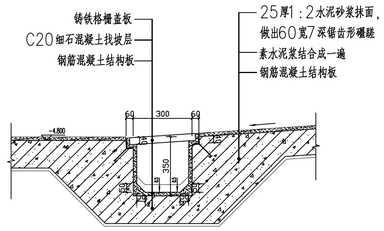


② 车道室内地面截水沟大样 1:25

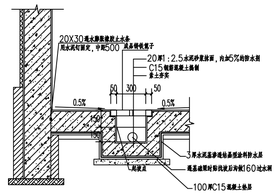


③ 300宽排水沟大样 1:25

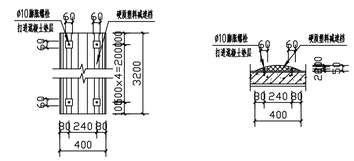


④ 塑料减速档 1:25

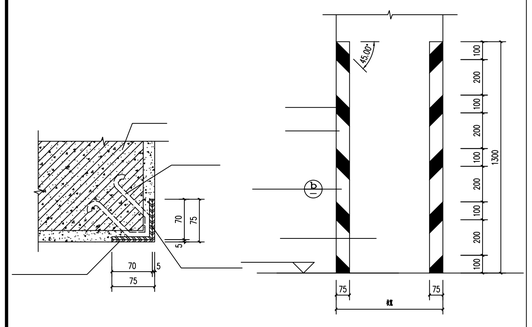


⑤ 车库墙柱防撞保护节点 1:5

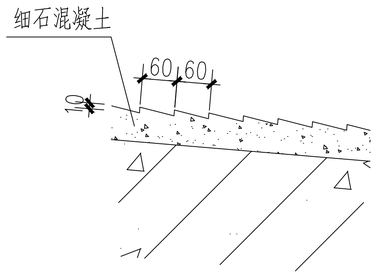


⑥ 车道防滑礓磋详图 1:5

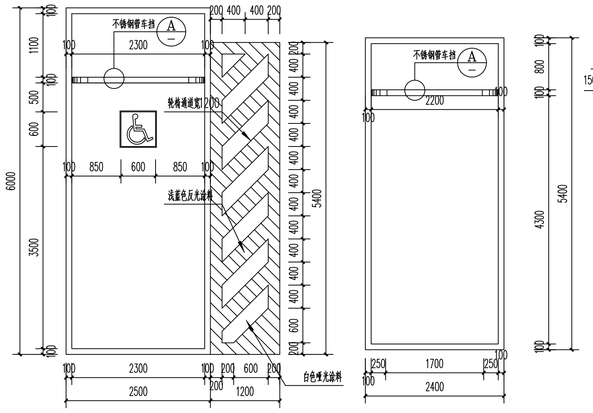


⑦ 无障碍停车位 1:50

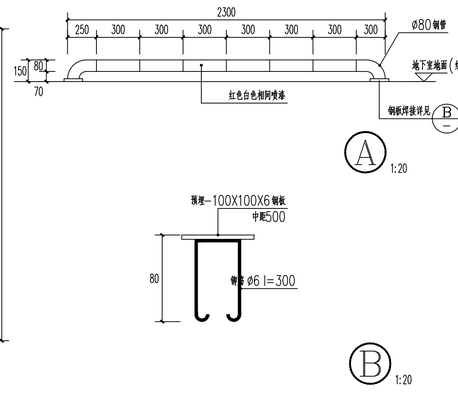


⑧ 普通停车位 1:50

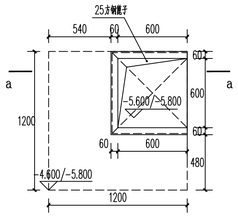


集水井平面图 1:25

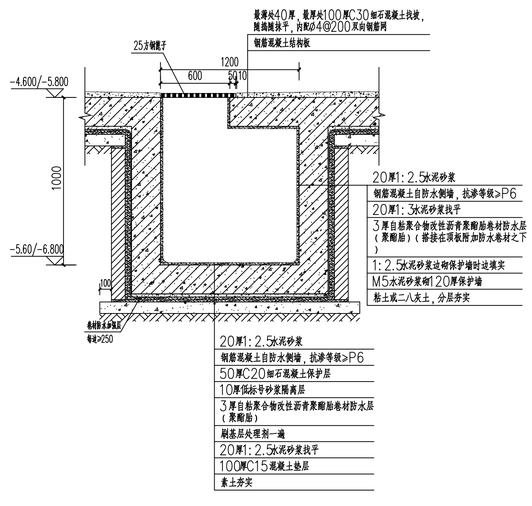

⑨ 集水井大样图 1:25

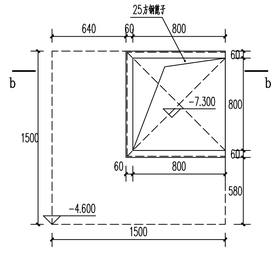

消防电梯集水井平面图 1:25

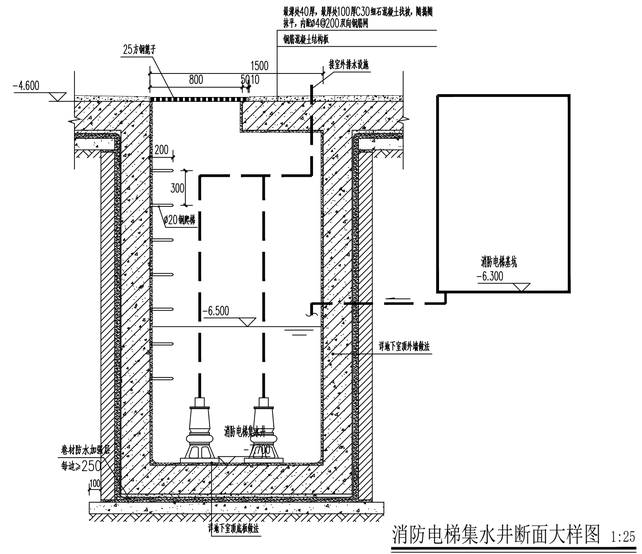

消防电梯集水井断面大样图 1:25

⑩ 消防电梯集水井大样图 1:25

建设单位/CLIENT:

麻阳苗族自治县远桥房地产开发有限公司

项目名称/PROJECT:

远程国际

子项目名称/SUB-PROJECT:

远程国际

区位图/REGIONAL LOCATION MAP :

广东建筑艺术设计院有限公司
GUANGDONG ARCHITECTURAL ARTISTIC DESIGN INSTITUTE CO.,LTD
■ 建筑工程设计：甲级 ■ 风景园林设计：乙级
■ 城乡规划设计：乙级 ■ 市政设计：乙级

图纸名称/TITLE:

节点大样图二

项目名称/PROJECT:

远程国际

设计 DESIGNED	古新辉	
校对 CHECKED	吴新红	
专业负责人 CHIEF	吴志刚	
项目负责人 PROJECT CHIEF	吴志刚	
审核 IDENTIFIED	黄履优	
审定 APPROVED	李 坚	

业务号/JOB NO.

设计阶段/STATUS: 施工图

专业/DISCIPLINE: 建施

比例/SCALE:	1：100	规格/SIZE:	A1

出图日期/DATE: 2021.06

图号/DRAWING NO. JS-41

版次 NO.	修改内容 DESCRIPTION	日期 DATE

条形码/BARCODE:

版权所有，不得复制、套用。
ALL RIGHTS RESERVED,DON'T COPIED,REPRODUCED.