
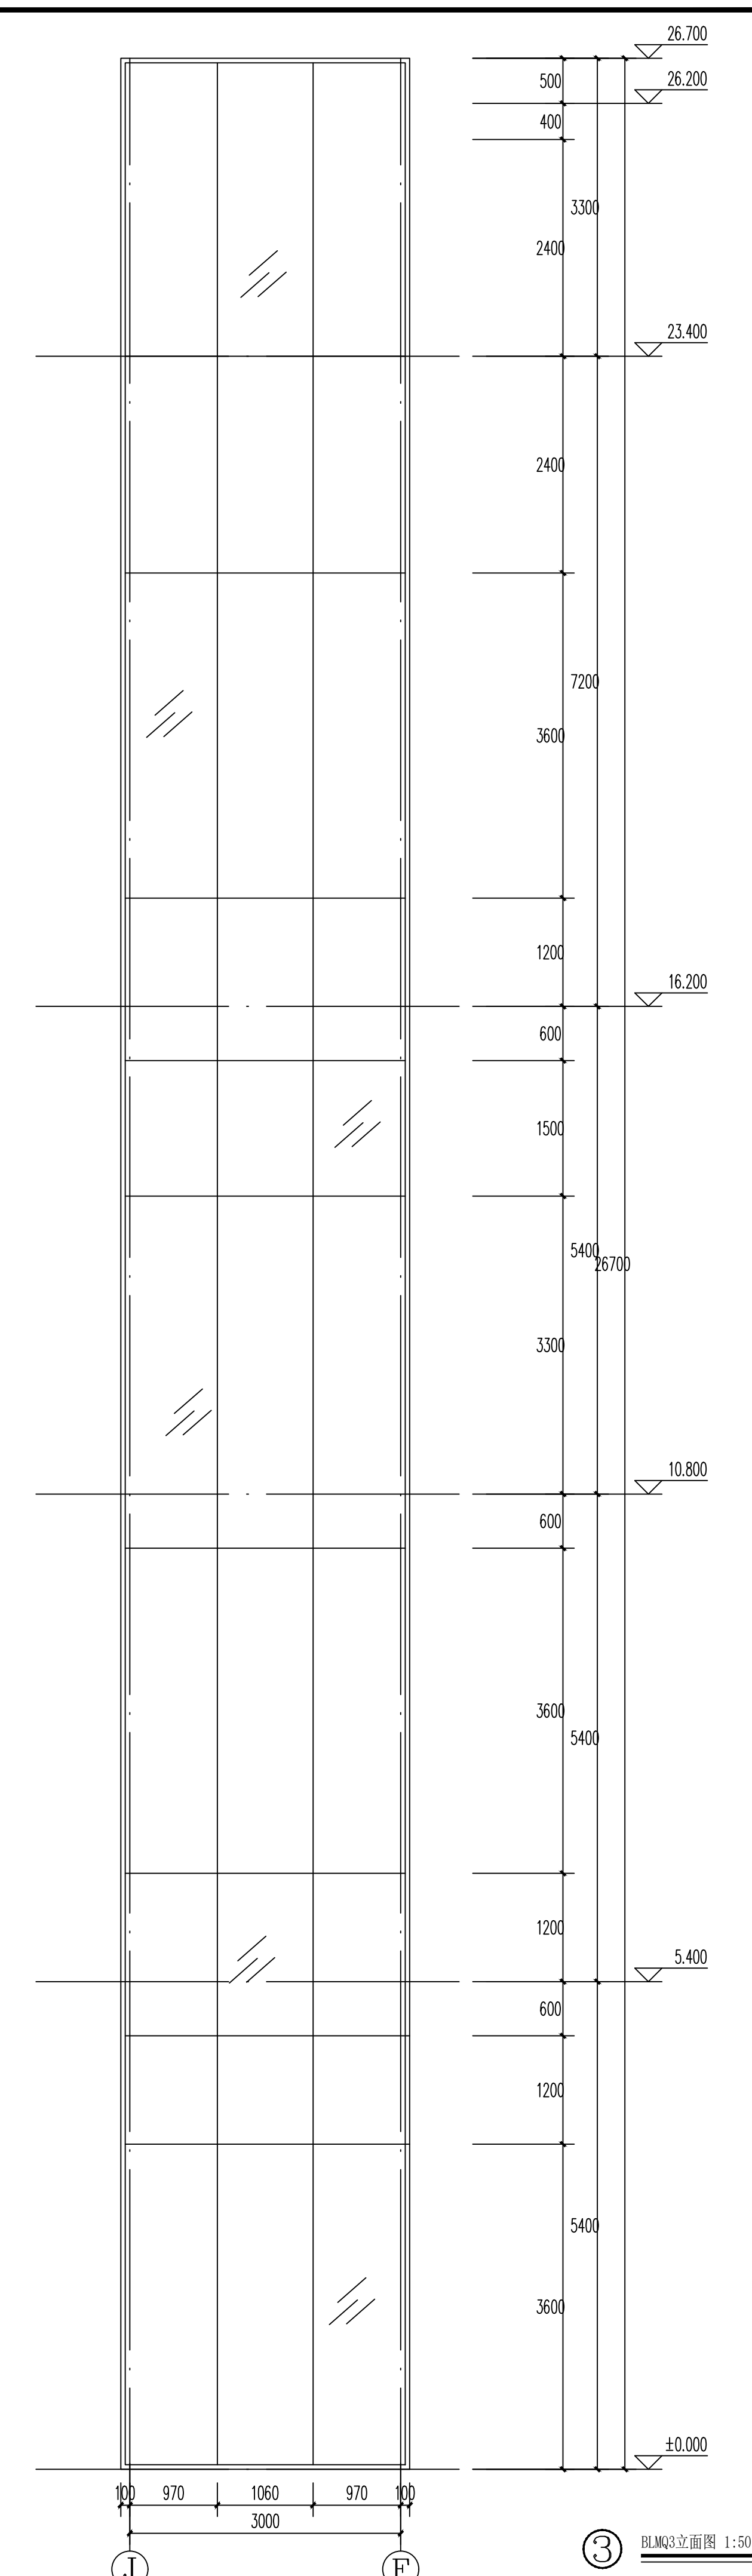
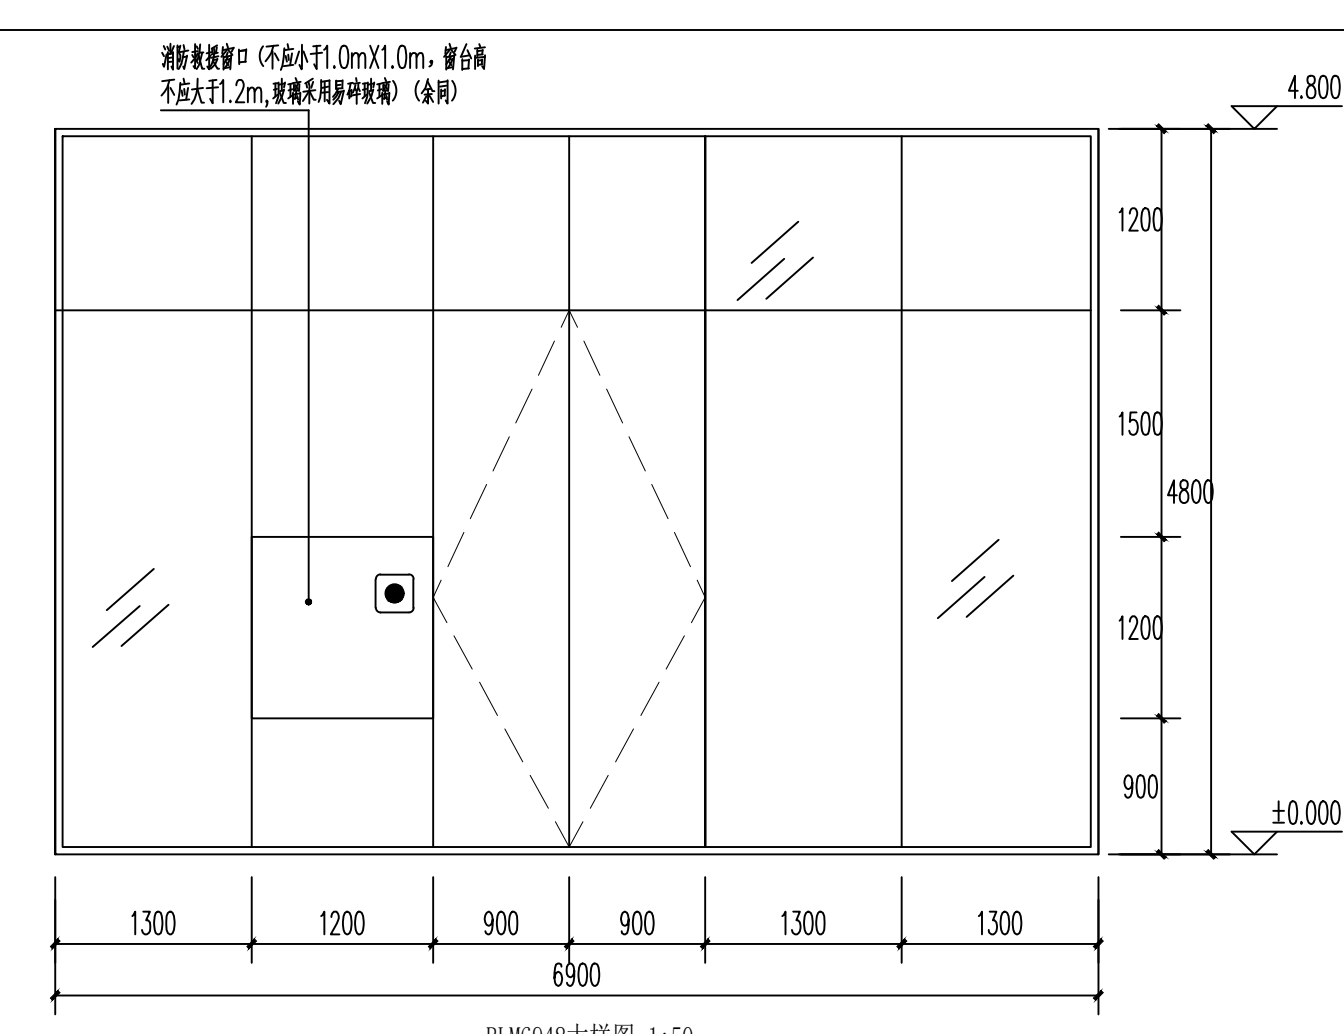
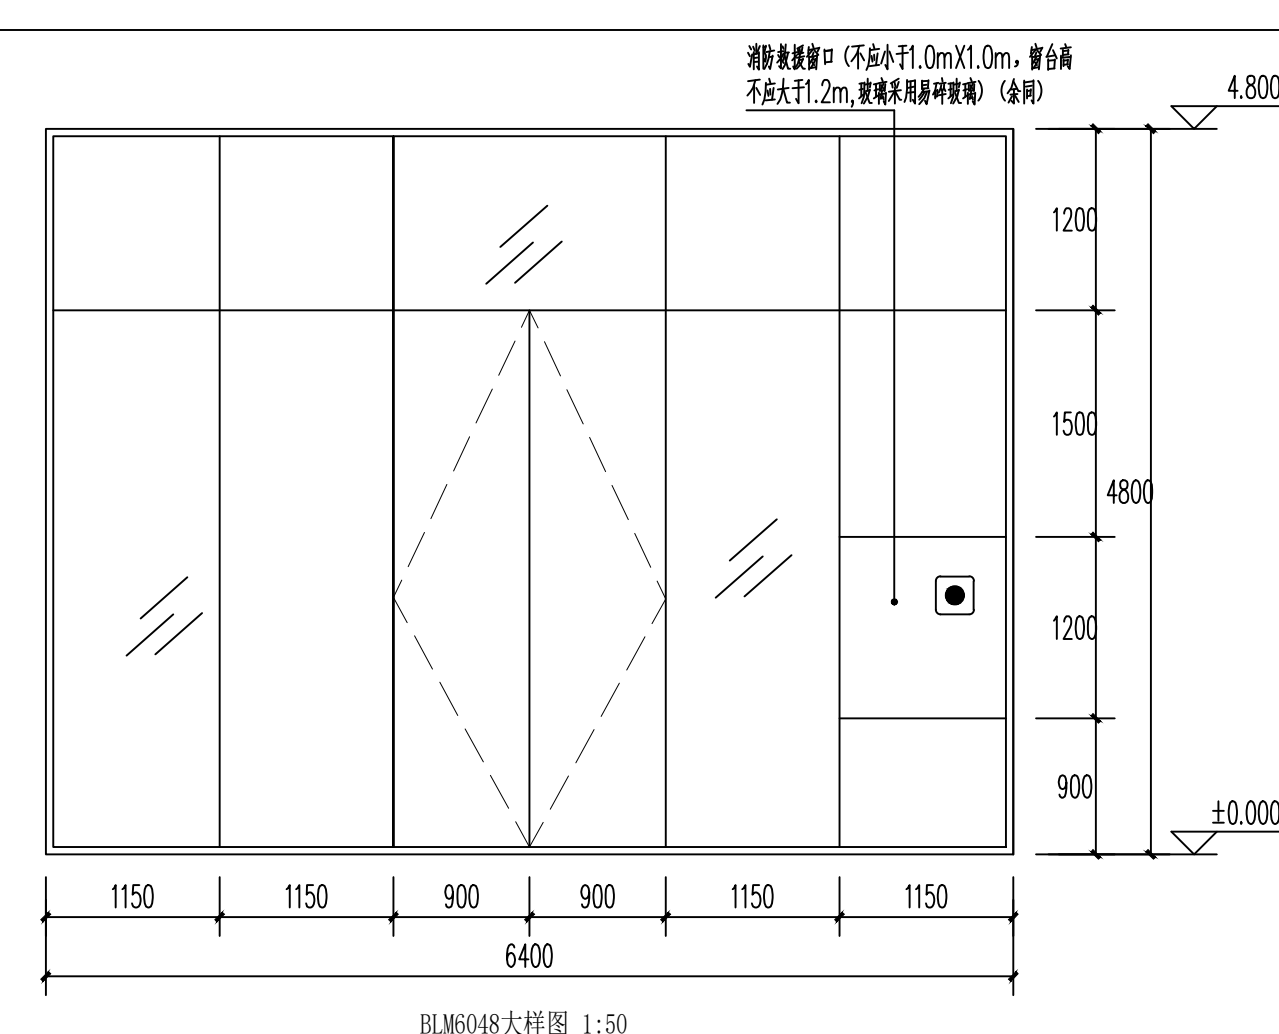
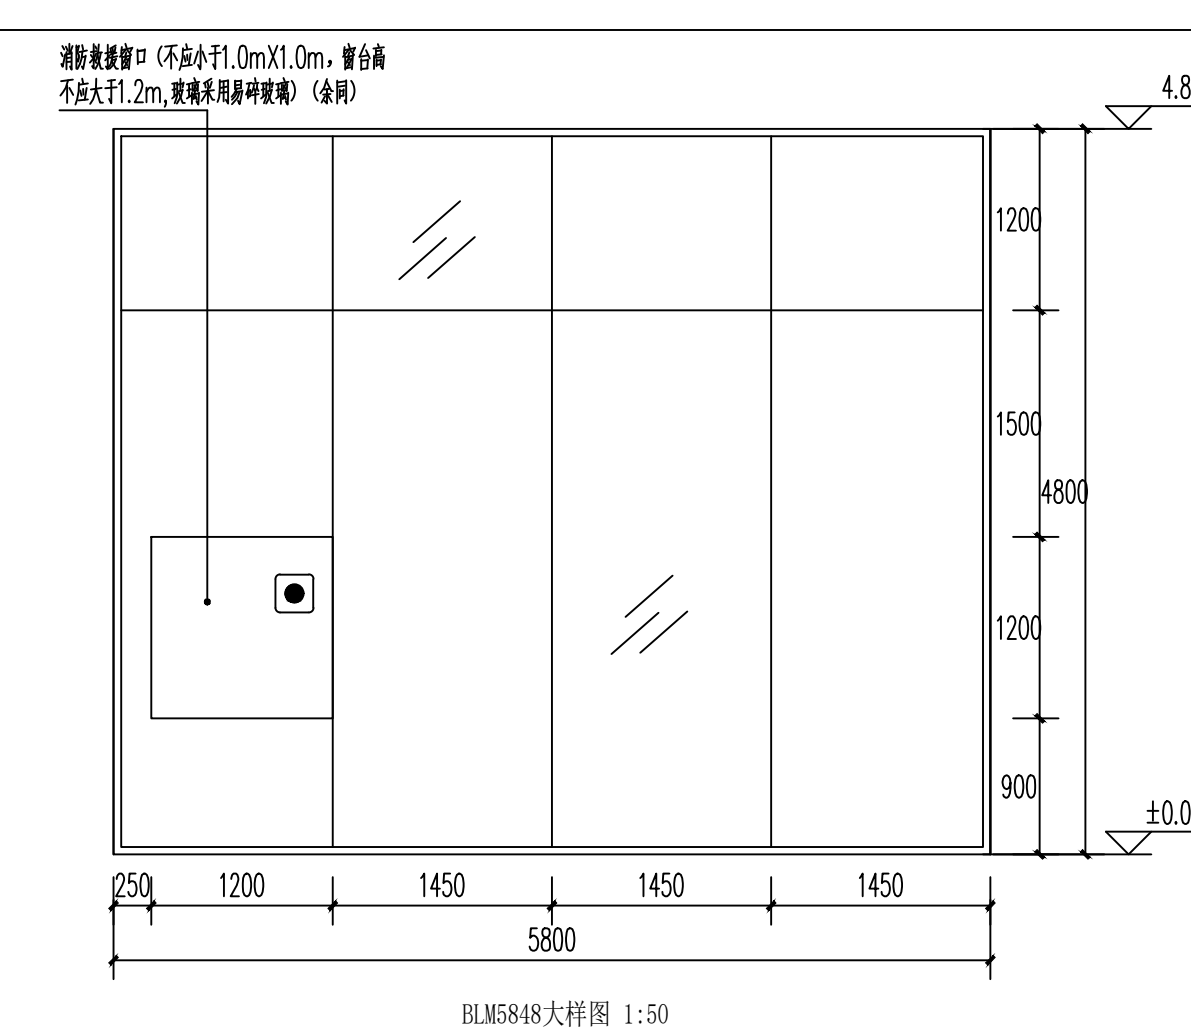
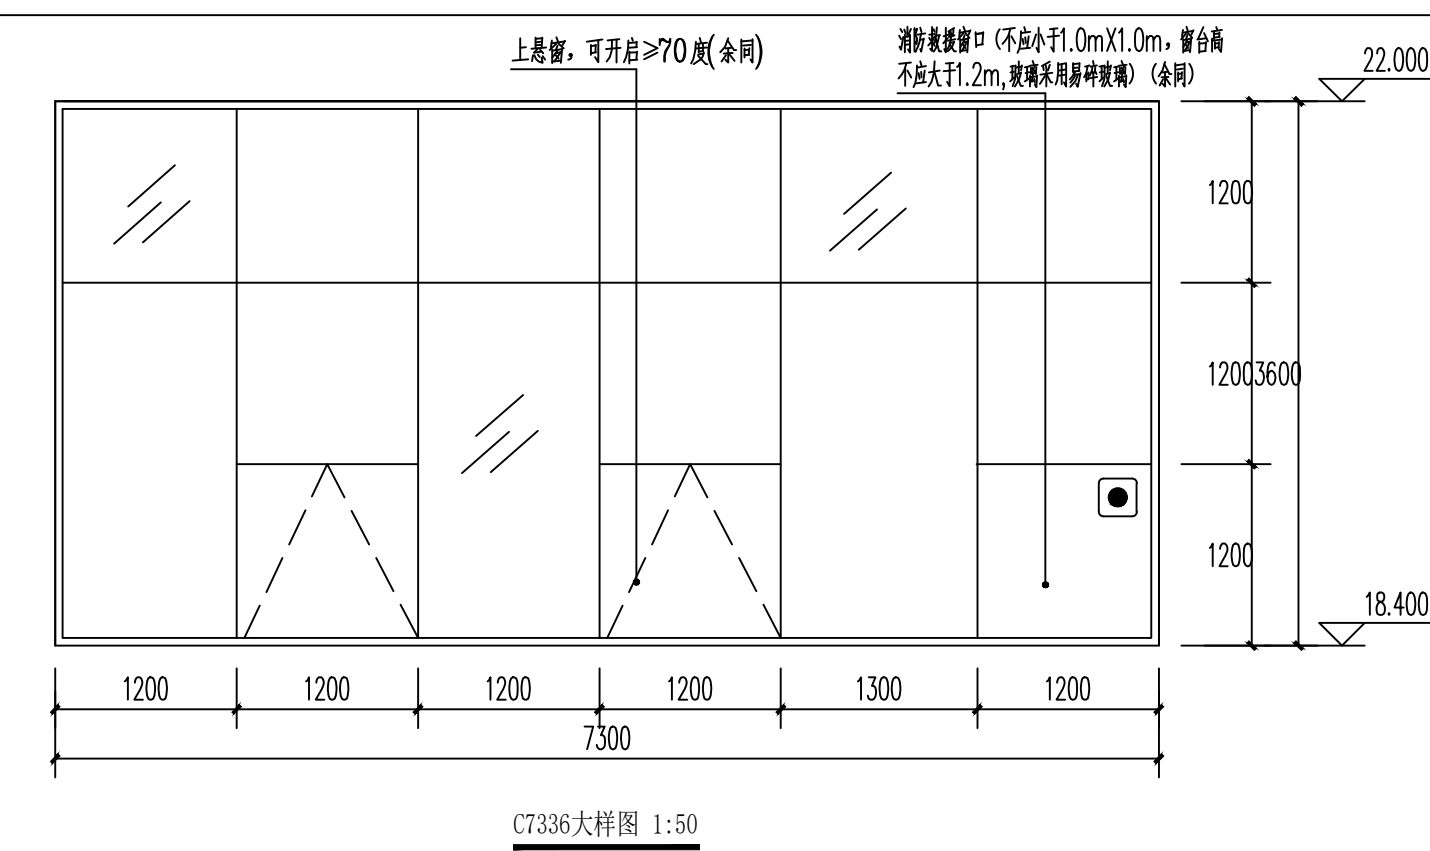
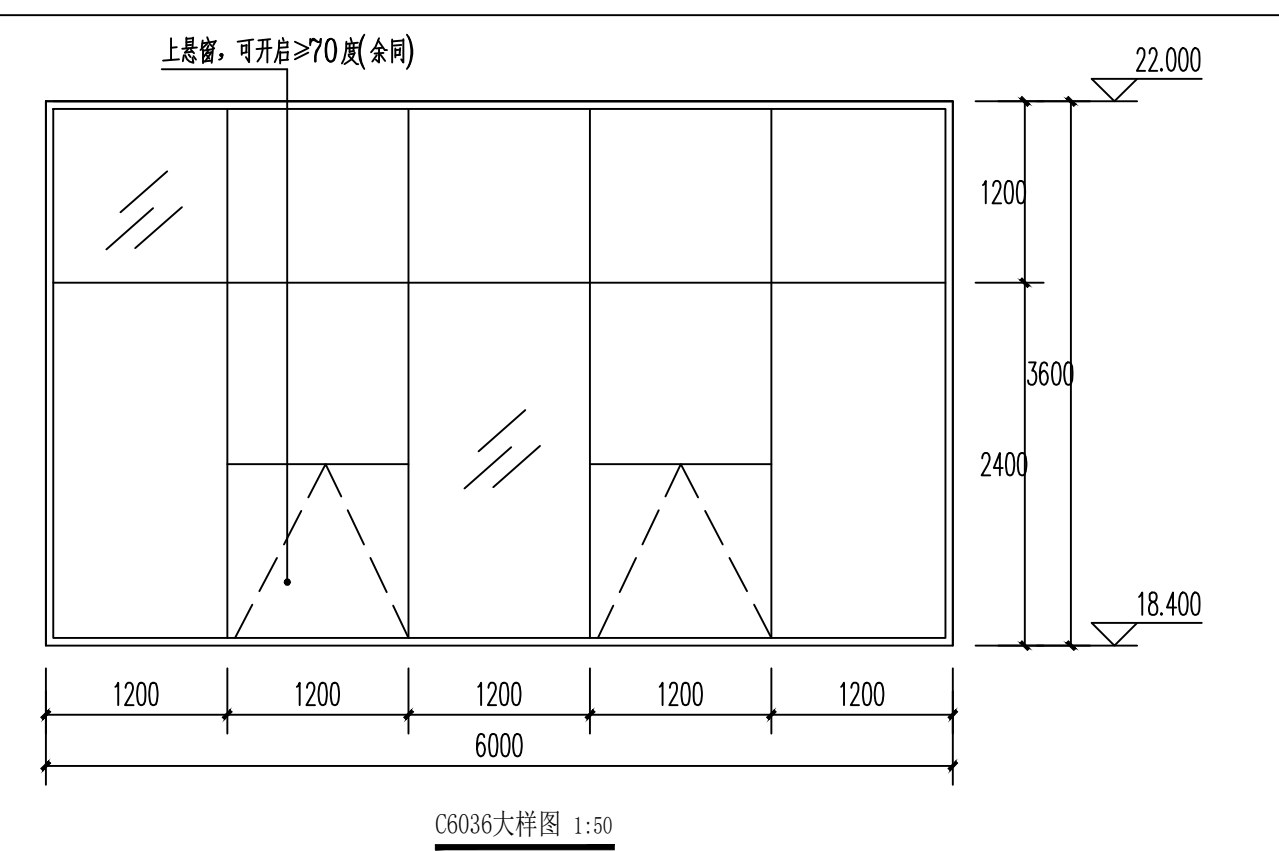
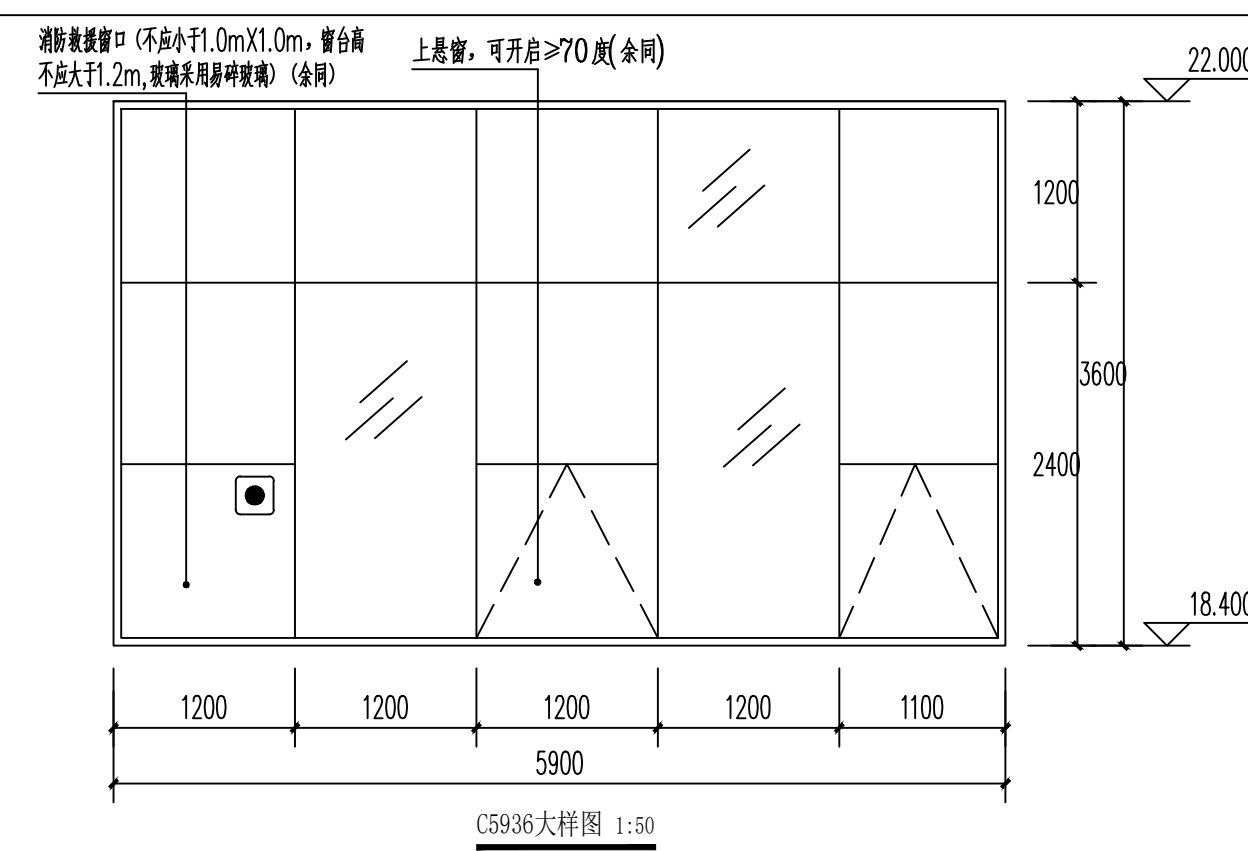
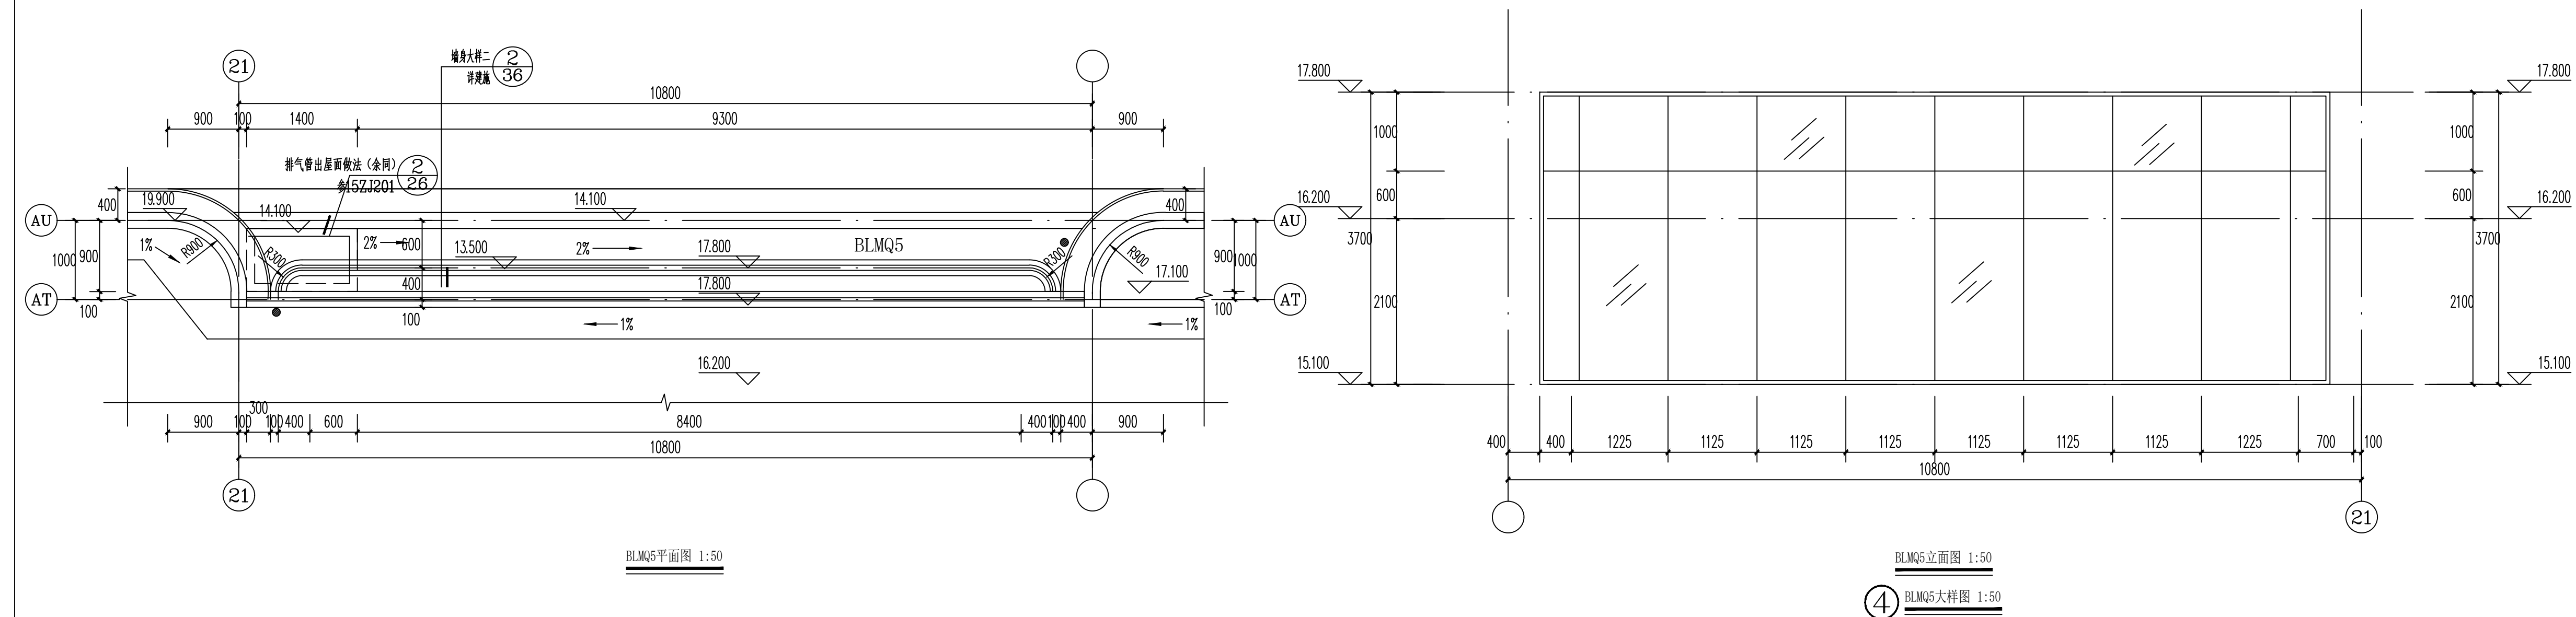
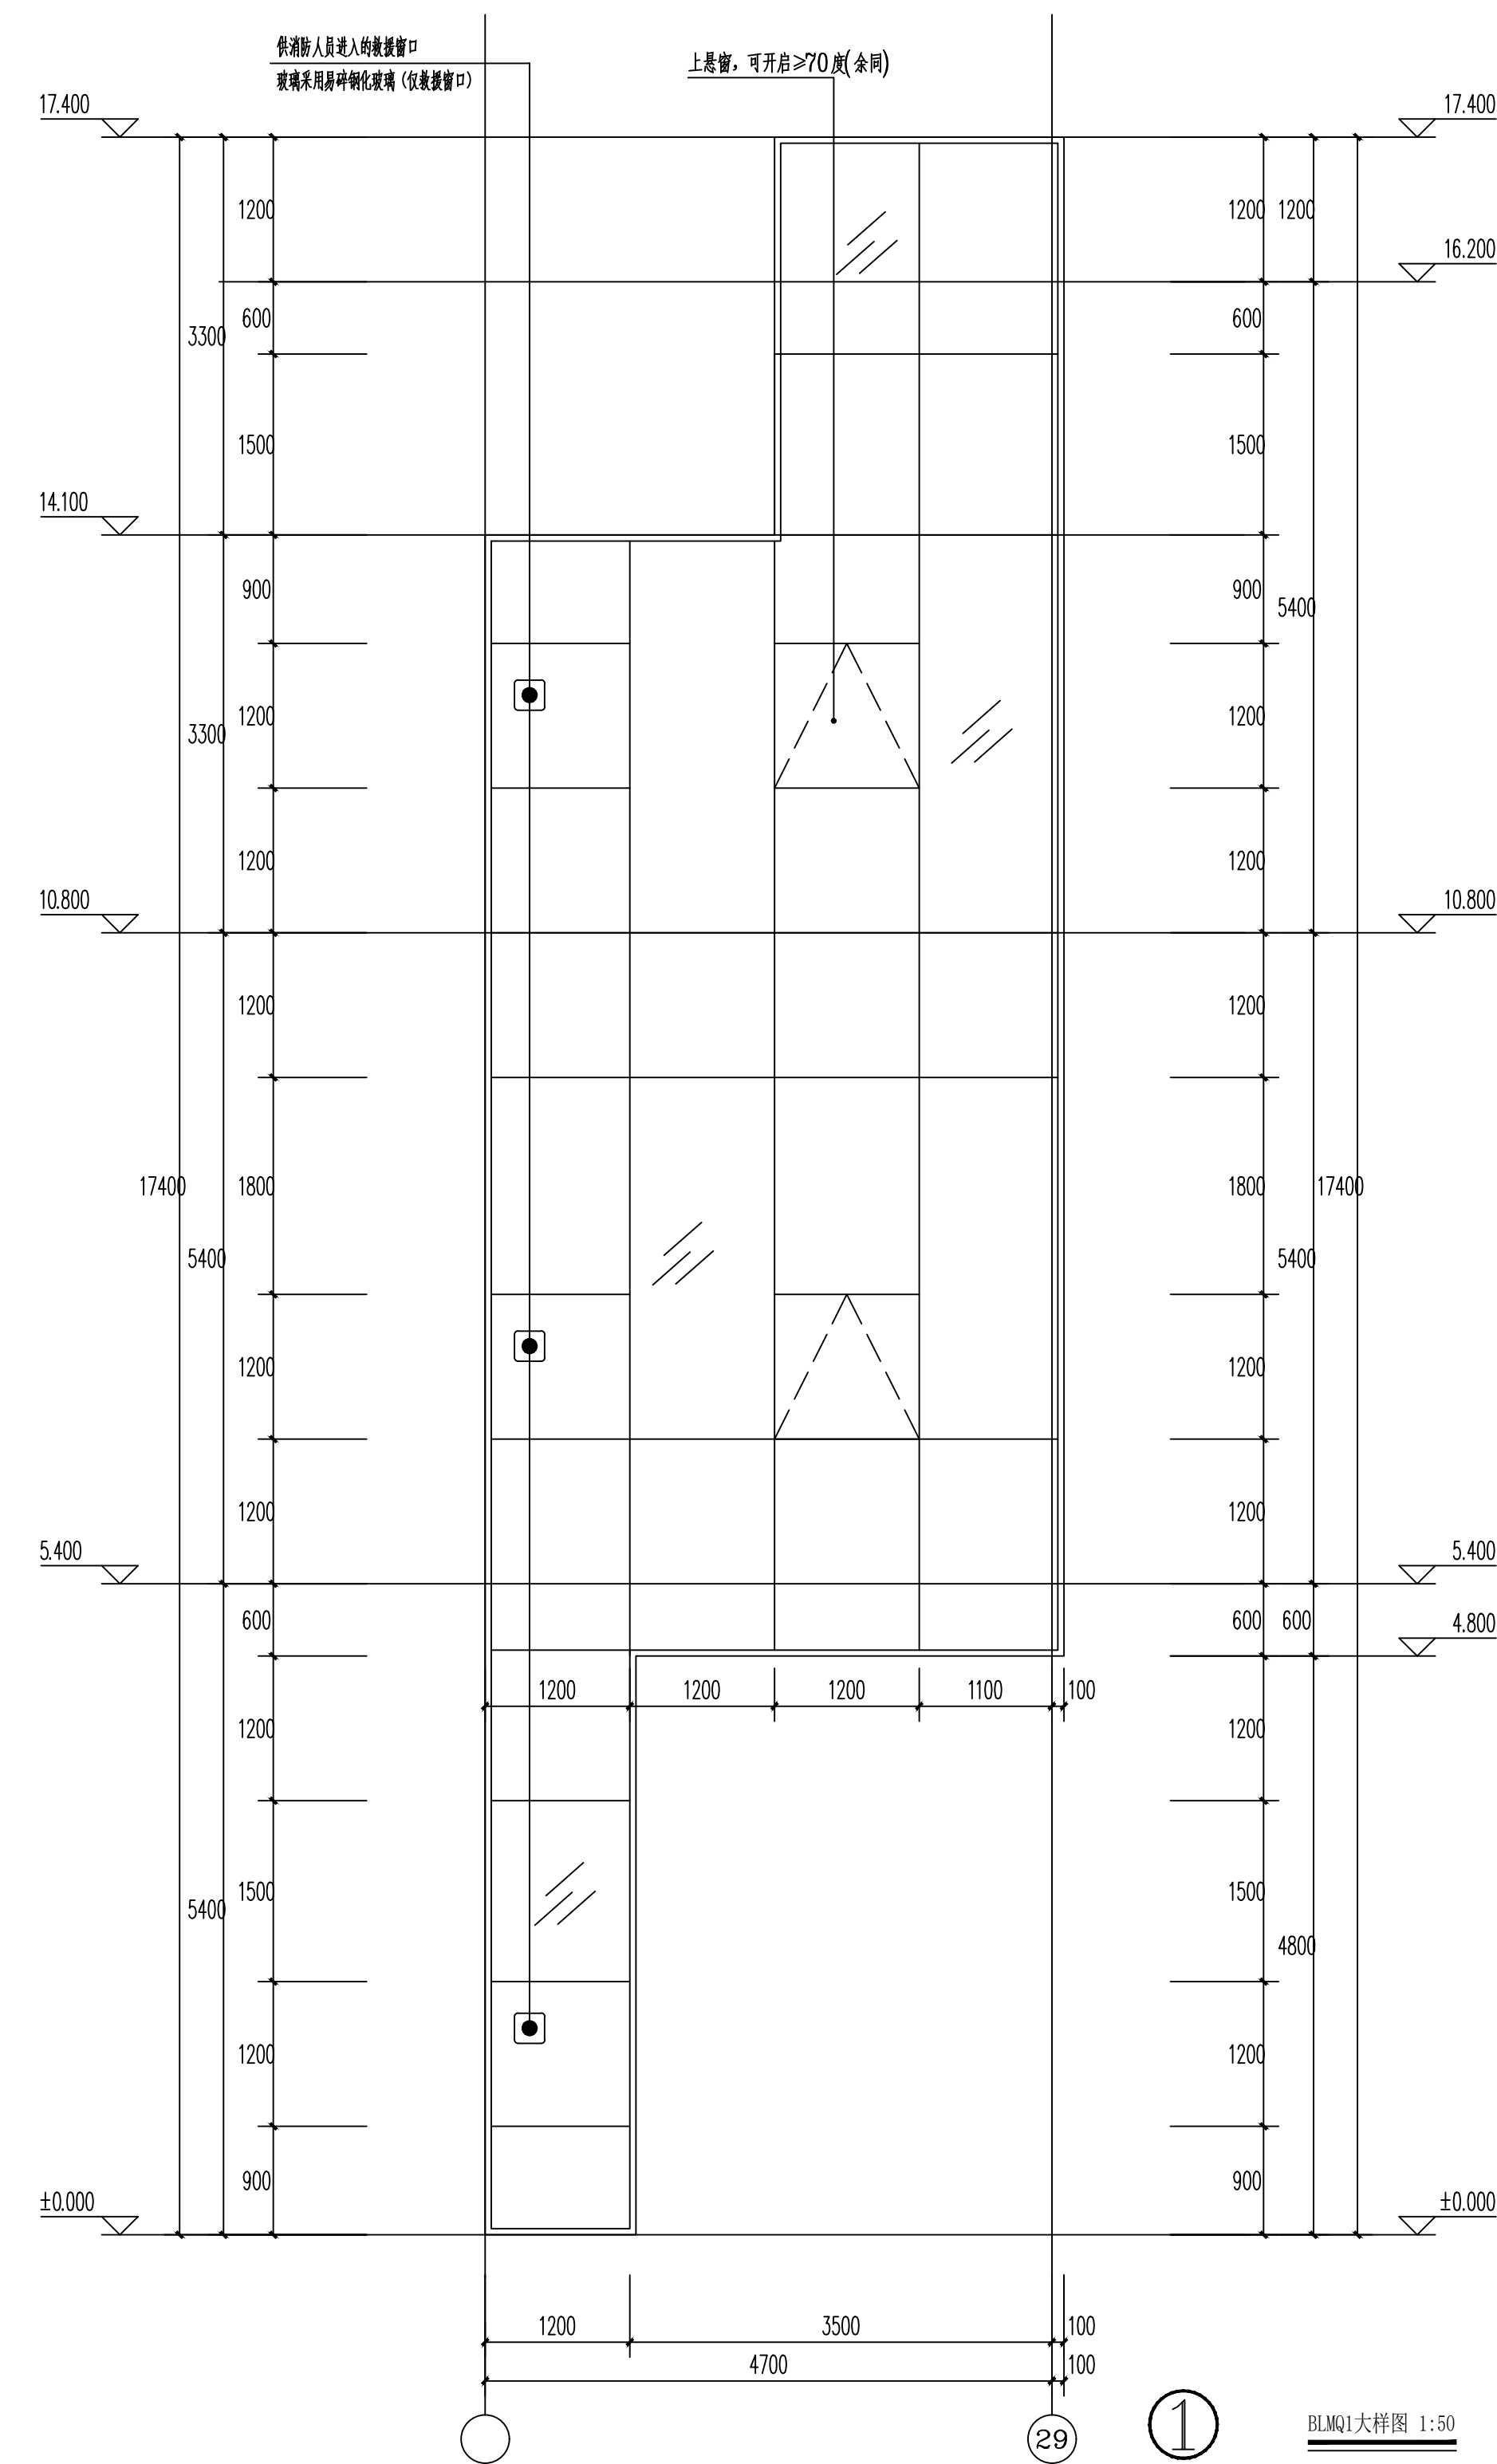
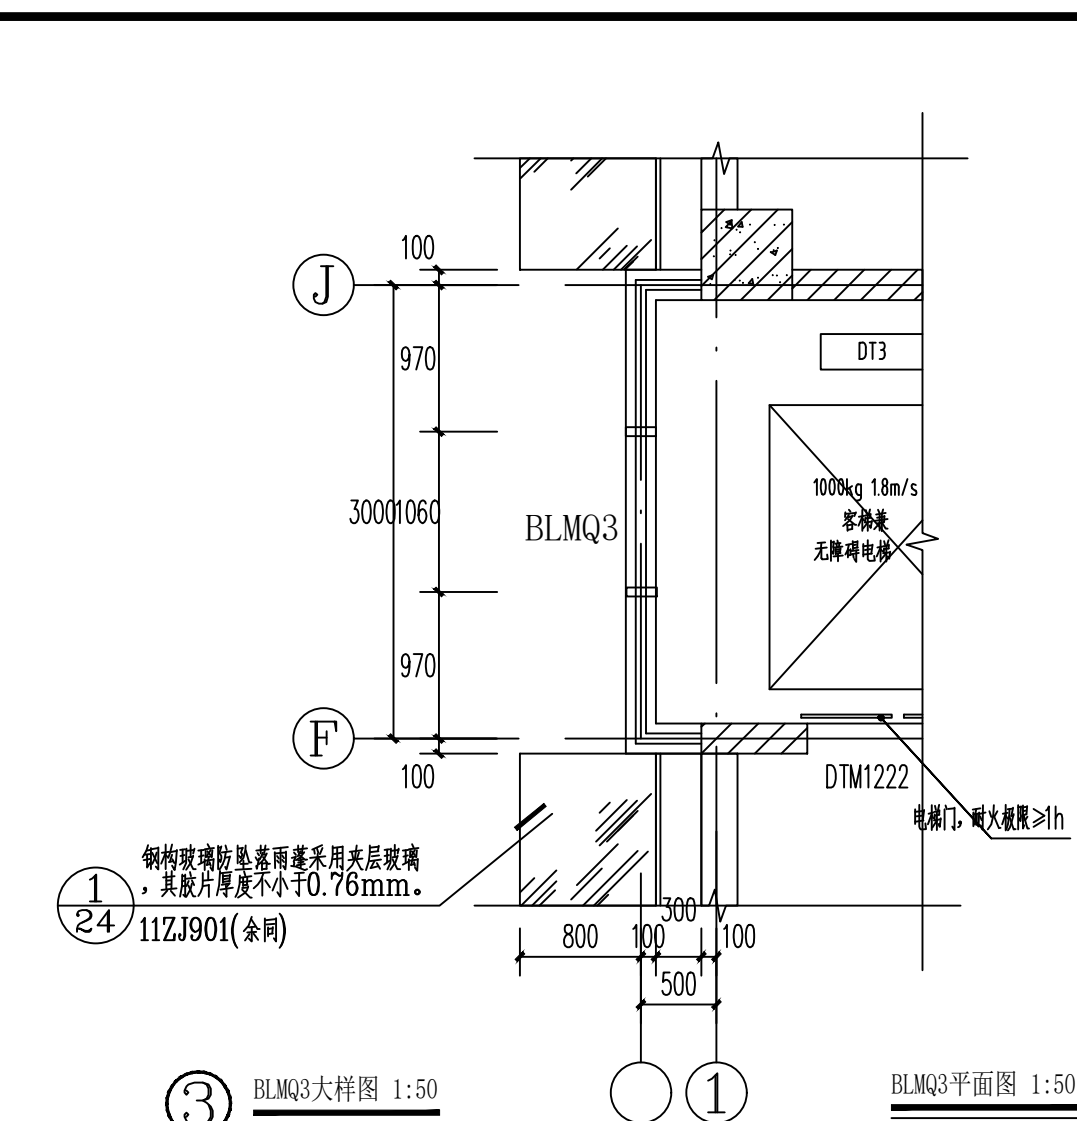


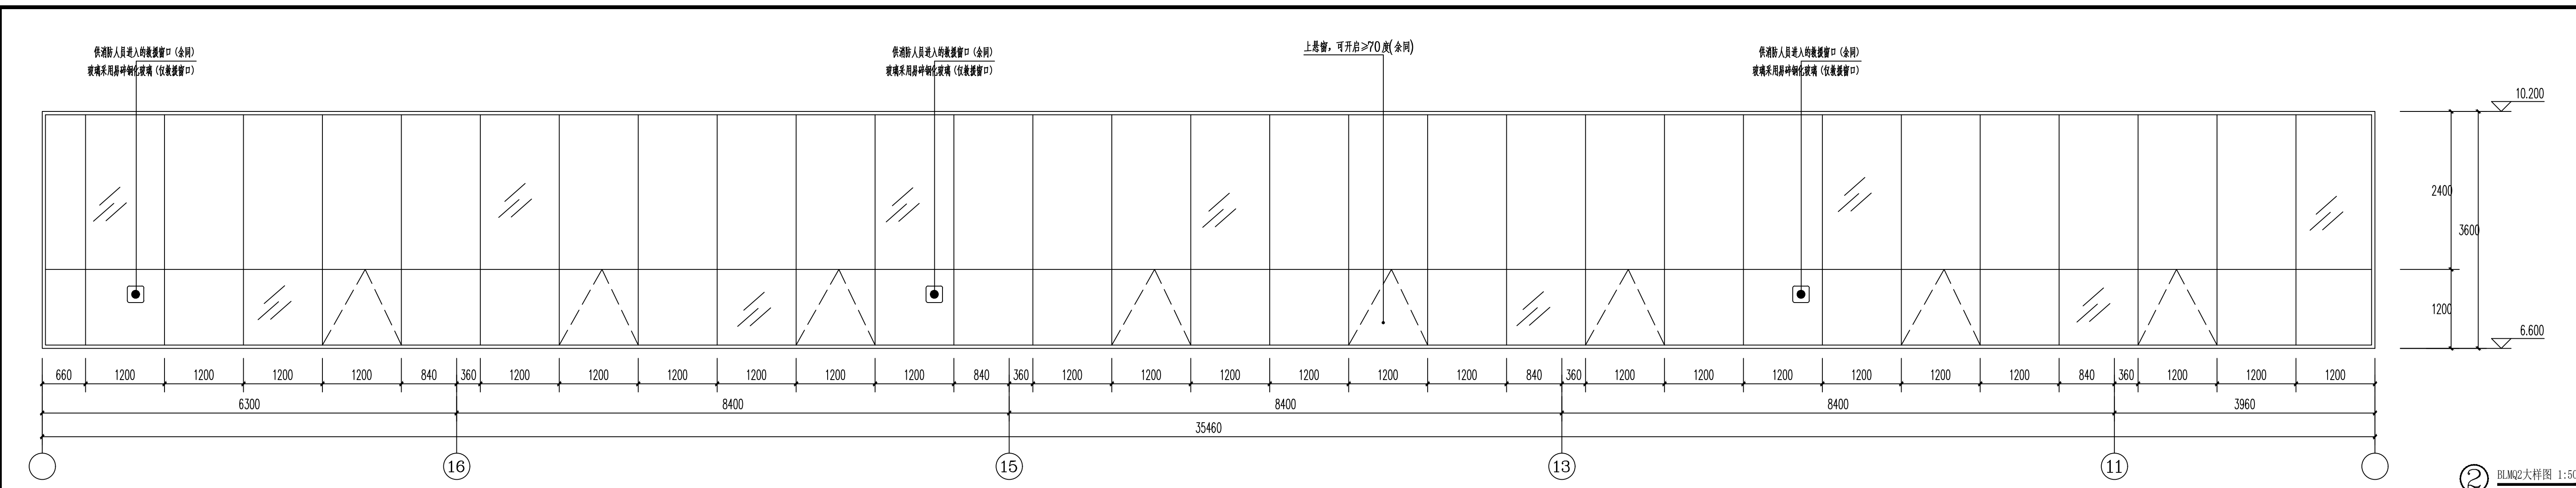

建设单位/CLIENT:

麻阳苗族自治县远桥房地产开发有限公司


项目名称/PROJECT:

远程国际

子项目名称/SUB-PROJECT:

远程国际

区位图/REGIONAL LOCATION MAP :

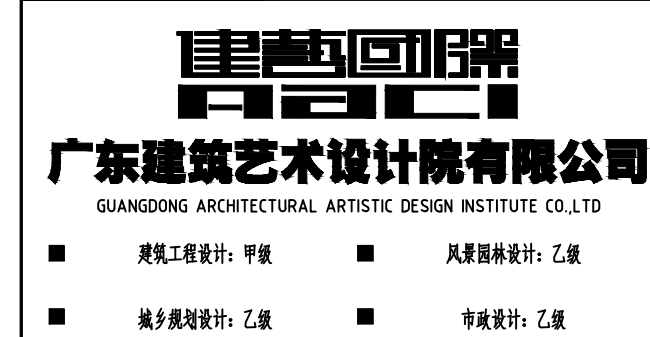

图纸名称/TITLE:

玻璃幕墙大样图一

项目名称/PROJECT:

远程国际

设计 DESIGNED	古新辉	古新辉
校对 CHECKED	吴新红	吴新红
专业负责人 CHIEF	吴志刚	吴志刚
项目负责人 PROJECT CHIEF	吴志刚	吴志刚
审核 IDENTIFIED	黄履优	黄履优
审定 APPROVED	李 坚	李 坚

业务号/JOB NO.

设计阶段/STATUS: 施工图

专业/DISCIPLINE: 建施

比例/ SCALE:	1: 100	规格/ SIZE:	A1
---------------	--------	--------------	----

出图日期/DATE: 2021.06

图号/DRAWING NO. JS-43

版次 NO.	修改内容 DESCRIPTION	日期 DATE

条形码/BARCODE:

版权所有，不得复制、套用。
ALL RIGHTS RESERVED, DON'T COPIED, REPRODUCED.