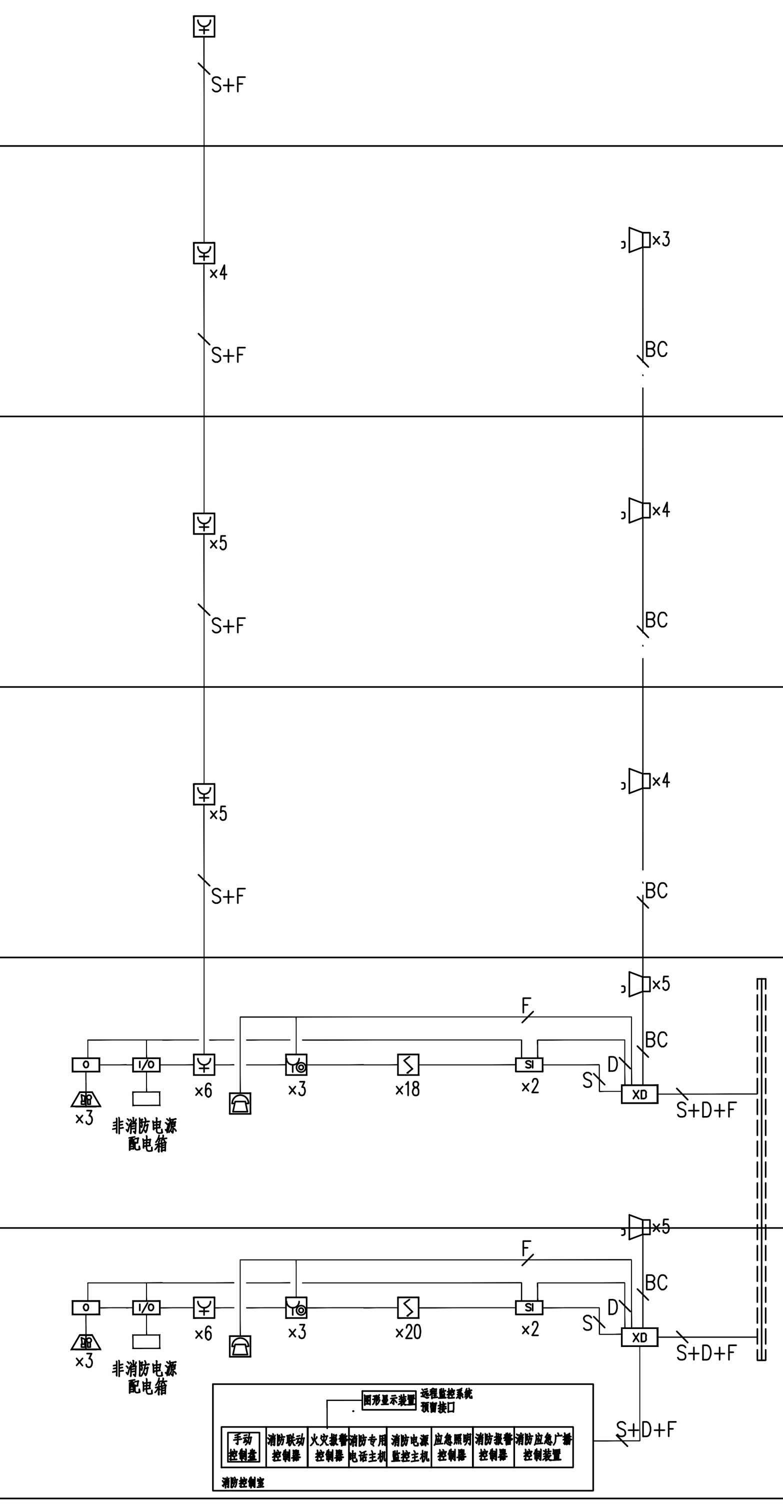

消防报警系统图

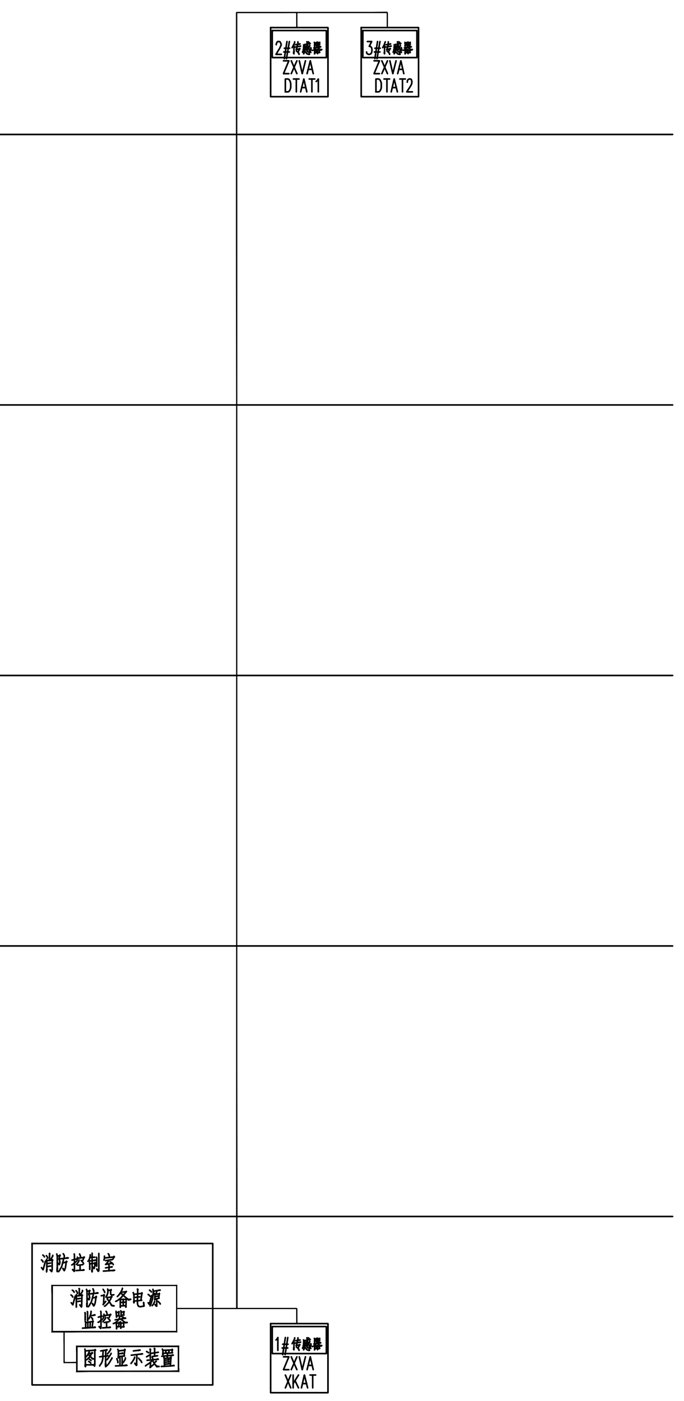

消防设备电源监控系统示意图

强电竖向图

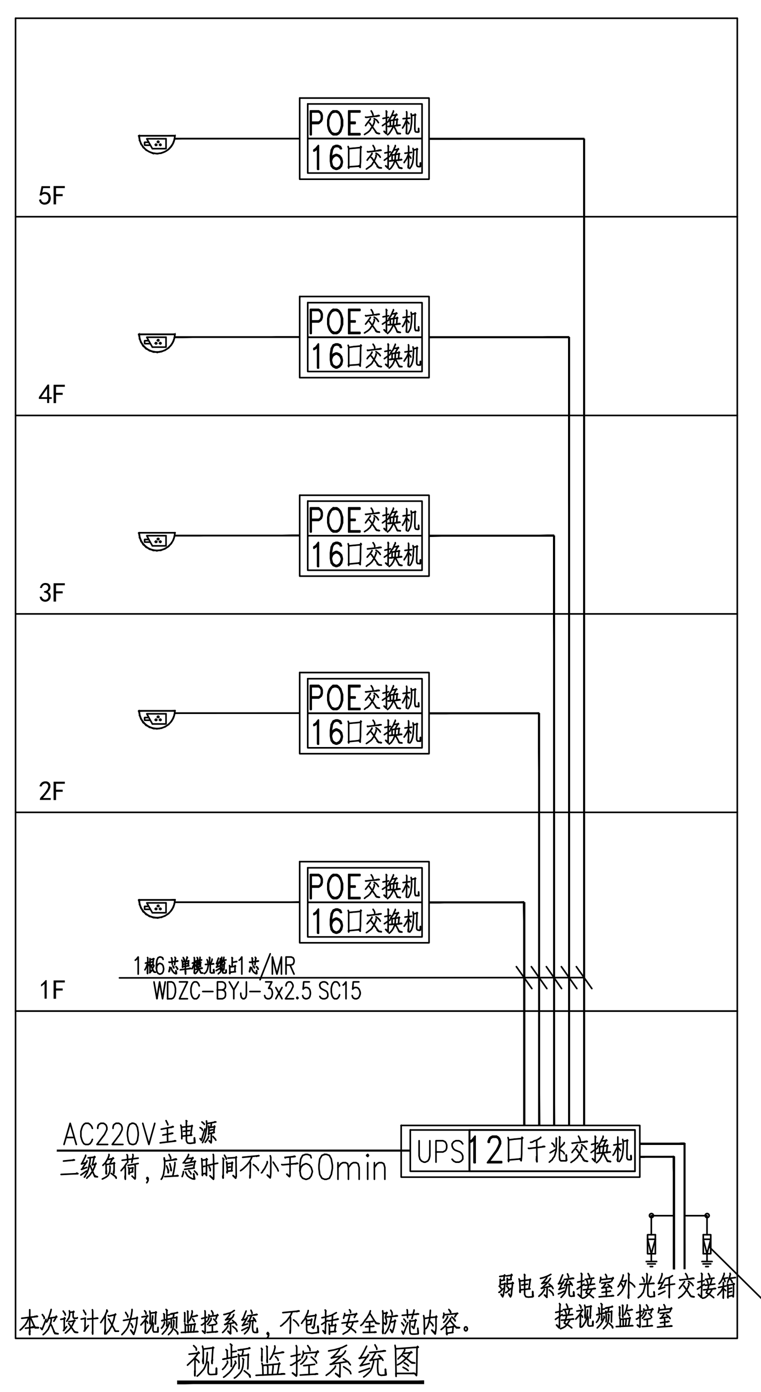

视频监控系统图

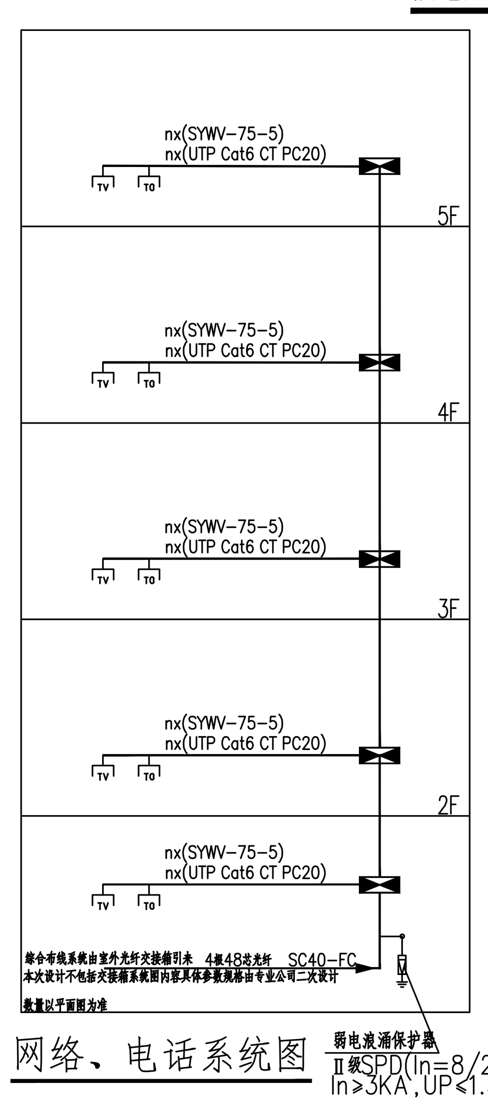

网络、电话系统图

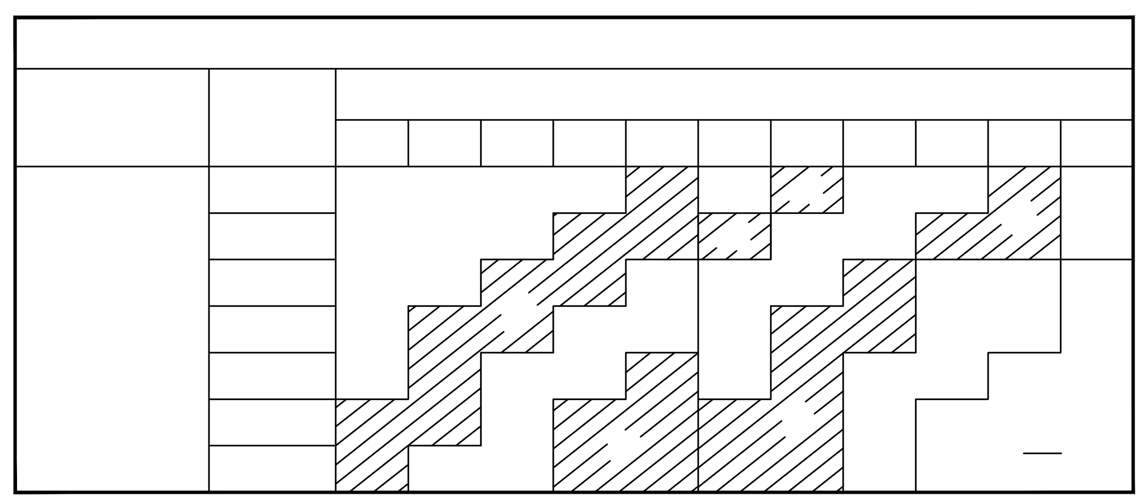

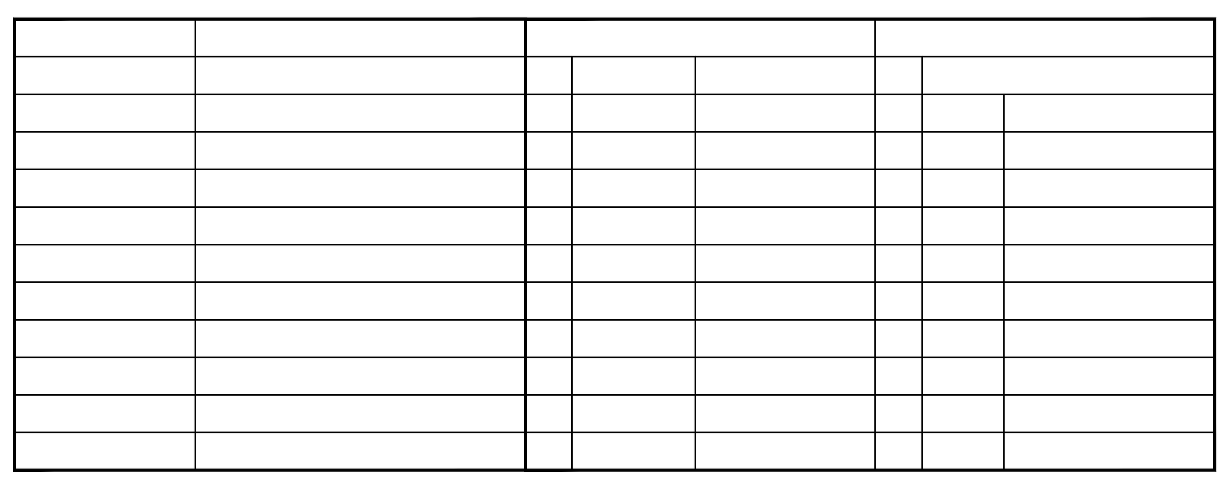

施工危大工程设计专篇

按建设部37号文、建质办2018131号文及我院统一要求，"危险性较大的分部分项工程设计单位需要在设计文件中注明涉及伟大工程的重点部位和缓解，提出保障工程周边环境安全盒工程施工安全的意见，必要时进行专项设计。"本工程属于危险性较大的的分部分项工程。电气施工及安装时应满足下列要求·

（一）、施工临时用电工程应满足《施工现场临时用电安全技术规范》C46-2005的要求。在施工现场安装的机电要保持良好的技术状态，严禁带"病"运转。

（二）、在带电设备附近搭、拆脚手架时，宜停电作业。在外电架空线路附近作业时。脚手架外侧边缘与外电架空线路的边线之间最

小安全操作距离不得小于《 施工现场临时用电安全技术规范》要求。了做好脚手架的接地，接地极可用三根L50x5mm长2500mm的角钢，埋入地下再用—4 扁钢引出与脚手架连接。4.采用起重机械进行安装的工程，起重机司机及信号指挥人员应经专业培训、考核合格并取得有关部门颁发的操作证后，方可上岗操作。

5建筑拆除过程中需用照明和电动机械时 必须另设专用配电线路，严禁使用被拆除建筑中的电气线路

（三）、现场施工临时用电及带电设备

1、施工单位电工必须经过专业培训持证上岗，非电工人员不得独立从事电工作业，禁止在施工现场和驻地私拉乱接生产生活用电。

2、现场施工用低压设备及线路应按施工及有关电气安全技术规程安装和架设。场内架设电线应绝缘良好，临时线路必须用绝缘物支撑，严禁将电线缠绕在钢筋、树木、脚手架上。

3、施工现场用电，各种电器设备须配专用开关，室外使用的开关，插座应外加防水箱并加锁，在操作处加设绝缘垫层。

4、在三相四线制中性接点接地供电系中，应采用tn-s接地系统，电器设备的金属外壳应接零保护；在非三相四线供电系统中，电气设备外壳应接地保护，其接地电阻应大于4欧姆，并不得在同一供电系统上有的接地、有的接零。

5、各种电气设备的检查维修，一般应停电作业；如必须带电作业时应有可靠的安全措施并派专人监护。

6、工地安装现场变压器必须符合电业部门的要求，并有专人管理，施工用电要尽量保持三相平衡。非电工人员严禁接近带电设备。

7、施工现场变配电设备处，必须配有灭火器材和高压安全用具，非电工人员严禁接近带电设备。

8、使用高温灯具要防止失火，其与易燃物的距离不得小于lm，一般电灯泡距易燃物不得小于50cm。

9、移动式电气机具设备应用橡胶电缆线供电，并经常注意理顺；跨越道路时，应埋地下或做穿管保护；手持式电动工具应设置有效的防漏保护器。

10、施工工地用于照明的灯具不能采用白炽灯、碘钨灯、卤素灯等非节能光源，不得用于建设工地的生产、办公、生活等区域的照明，应采用LED、节能灯。

11、电气设备检修应在切断电源，设好防护后进行，并在开关处设置警示标牌，工作完成后方可拆除；如需做送电试验，必须认真检查，并与项目部各施工部门联系后方可进行。

注：本设计预留管线，由甲方另委托专业设备公司进行二次设计，施工前征得有关部门的认可。

2022年版
版权所有，不得复制、套用。
ALL RIGHTS RESERVED,DON'T COPIED,REPRODUCED.

广东建筑艺术设计院有限公司
GUANGDONG ARCHITECTURAL ARTISTIC DESIGN INSTITUTE CO.,LTD
■建筑行业（建筑工程）甲级 A244004516
■城乡规划编制甲级 ■风景园林工程设计专项乙级
■市政行业道路工程乙级 ■市政行业排水工程乙级
■环境工程专项水污染防治工程乙级 ■公路行业(公路)乙级
地址:广州市天河区黄埔大道中309号自编3-09A
电话：(020)38031603 传真：(020)38031690

会签栏 COUNTER SIGNATURE

建筑 ARCHI.		电气 ELEC.	
结构 STRUCT.		暖通 HVAC.	
给排水 PLUMBING			

签章区 STAMP AREA

版次 NO.	修改内容 DESCRIPTION	日期 DATE

建设单位 CLIENT：湖南利农五倍子产业发展有限公司

项目名称 PROJECT：没食子酸丙脂技改厂房与研发综合楼及职工宿舍楼建设项目

子项目名称 SUB-PROJECT：2#综合楼

图纸名称 TITLE：竖向图

制图 DRAWING BY	唐博	(签名)
设计 DESIGNED BY	唐博	(签名)
校对 CHECKED BY	马欣凡	(签名)
专业负责 SPECIALTY CHIEF	邱继国	邱继国
项目负责 PROJECT CHIEF	吴志刚	吴志刚
审核 EXAMINED BY	邱继国	邱继国
审定 APPROVED BY	李坚	(签名)

图号 DRAWING NO. DS-05

业务号 JOB NO.

出图日期 DATE 2023.04

专业 DISCIPLINE	电气	设计阶段 STAGE	施工图
比例 SCALE	1:100	规格 SIZE	

条形码,二维码 BARCODE,QR CODE